

ÎLOT A2 - IMMEUBLES DE LOGEMENTS  
rue Mathieu Dussurgey - 69190 SAINT FONS  
PARC LYON SUD - CONCERTO

Les entreprises réalisant les travaux devront tenir compte des derniers plans architecte lors de la réalisation des travaux  
Les plans du be MATTE ne doivent servir qu'au corps d'état concerné et doivent être des plans d'exécution.

ARCHITECTE(S): ARCHIGROUP  
BET STRUCTURE: BET MATTE  
BET FLUIDES: ITEE  
ECONOMISTE: CABINET TROMPILLE  
BUREAU DE CONTROLE: SOCOTEC

M.O. Délégué: .  
M.O.: BOUYGUES IMMOBILIER  
CSPS: .  
M.O.E.: .  
ENTREPRISE(S): FONTANEL

BÂTIMENT C  
FONDATIONS  
ARMATURES

DOE

| INDICE | DATE | MODIFICATIONS |
|--------|------|---------------|
|--------|------|---------------|

|   |            |                     |
|---|------------|---------------------|
| A | 04/02/2013 | Maj fosse ascenseur |
|   |            |                     |
|   |            |                     |
Aciers HA (T) FeE500  
Aciers Doux (Ø) FeE 235  
Aciers TS FeE 500  
Béton fc28 >= 25MPa  
Enrobage = 3 cm

PLAN N°  
C 02 A

DATE : 24/01/2013

**MATTÉ**

BUREAU D'ÉTUDES  
STRUCTURES ET FLUIDES

119 BOULEVARD STALINGRAD 69100 VILLEURBANNE

Tél. 04 72 44 02 87 Fax 04 72 44 26 59

E-mail : bet@matte.fr


Dessiné par : C. COLLOT

Contrôlé par : P. LIN

Ech : 1/50


Affaire N°  
S.11.08.071

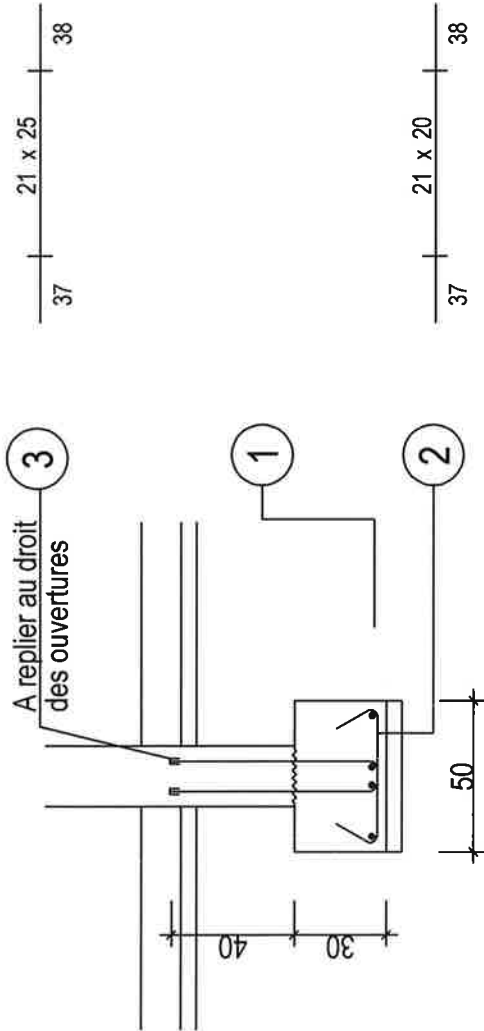


| AFF: S.13.12.119                                          | Bât: C    | LA MULATIERE-69350 LaMulatiere<br>CREATION de LOGEMENTS                           | FONDATIONS au -3                                                                              | Plan n° C 02 | Page: 4 |
|-----------------------------------------------------------|-----------|-----------------------------------------------------------------------------------|-----------------------------------------------------------------------------------------------|--------------|---------|
| <div>SF1</div> <div>Nombre: 9</div> <div>Rec: 50 cm</div> |           |                                                                                   | <div></div> |              |         |
| 1                                                         | 4 HA 8 x  | 600                                                                               |                                                                                               |              |         |
| 2                                                         | 22 HA 8 x |  |                                                                                               |              |         |
| 3                                                         | 22 HA 8 x |  |                                                                                               |              |         |
| 4                                                         |           |                                                                                   |                                                                                               |              |         |
| 5                                                         |           |                                                                                   |                                                                                               |              |         |
| 6                                                         |           |                                                                                   |                                                                                               |              |         |
| 7                                                         |           |                                                                                   |                                                                                               |              |         |
| 8                                                         |           |                                                                                   |                                                                                               |              |         |
| 9                                                         |           |                                                                                   |                                                                                               |              |         |
| 10                                                        |           |                                                                                   |                                                                                               |              |         |
| 11                                                        |           |                                                                                   |                                                                                               |              |         |
| 12                                                        |           |                                                                                   |                                                                                               |              |         |
| 13                                                        |           |                                                                                   |                                                                                               |              |         |
| 14                                                        |           |                                                                                   |                                                                                               |              |         |
| 15                                                        |           |                                                                                   |                                                                                               |              |         |

|                                     |  |        |                                                          |  |                  |    |              |  |         |  |
|-------------------------------------|--|--------|----------------------------------------------------------|--|------------------|----|--------------|--|---------|--|
| AFF: S.13.12.119                    |  | Bât: C | LA MULATIERE-69350 La Mulatiere<br>CREATION de LOGEMENTS |  | FONDATIONS au -3 |    | Plan n° C 02 |  | Page: 5 |  |
| <div>ANGLES SEMELLES FILANTES</div> |  |        |                                                          |  |                  |    |              |  |         |  |
| ①                                   |  |        |                                                          |  | 1 HA 8 x         | 70 | 70           |  |         |  |
| ②                                   |  |        |                                                          |  | 2X1 HA 8 x       | 70 | 100          |  |         |  |
| ③                                   |  |        |                                                          |  |                  |    |              |  |         |  |
| ④                                   |  |        |                                                          |  |                  |    |              |  |         |  |
Nombre: ~~4~~ 6

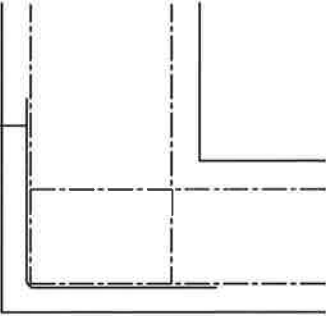



Nombre: ~~2~~ 4

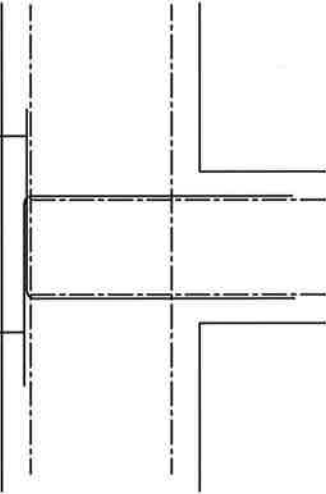

ATTENTES POTEAUX DANS SEMELLES

18x50


Nb: 2

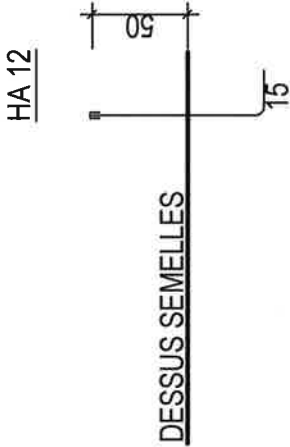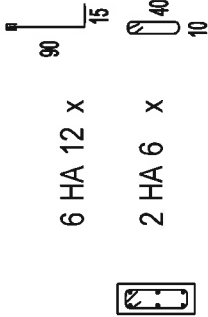

ANGLES et ABOUTS VOILES et OUVERTURES


Nb: 22



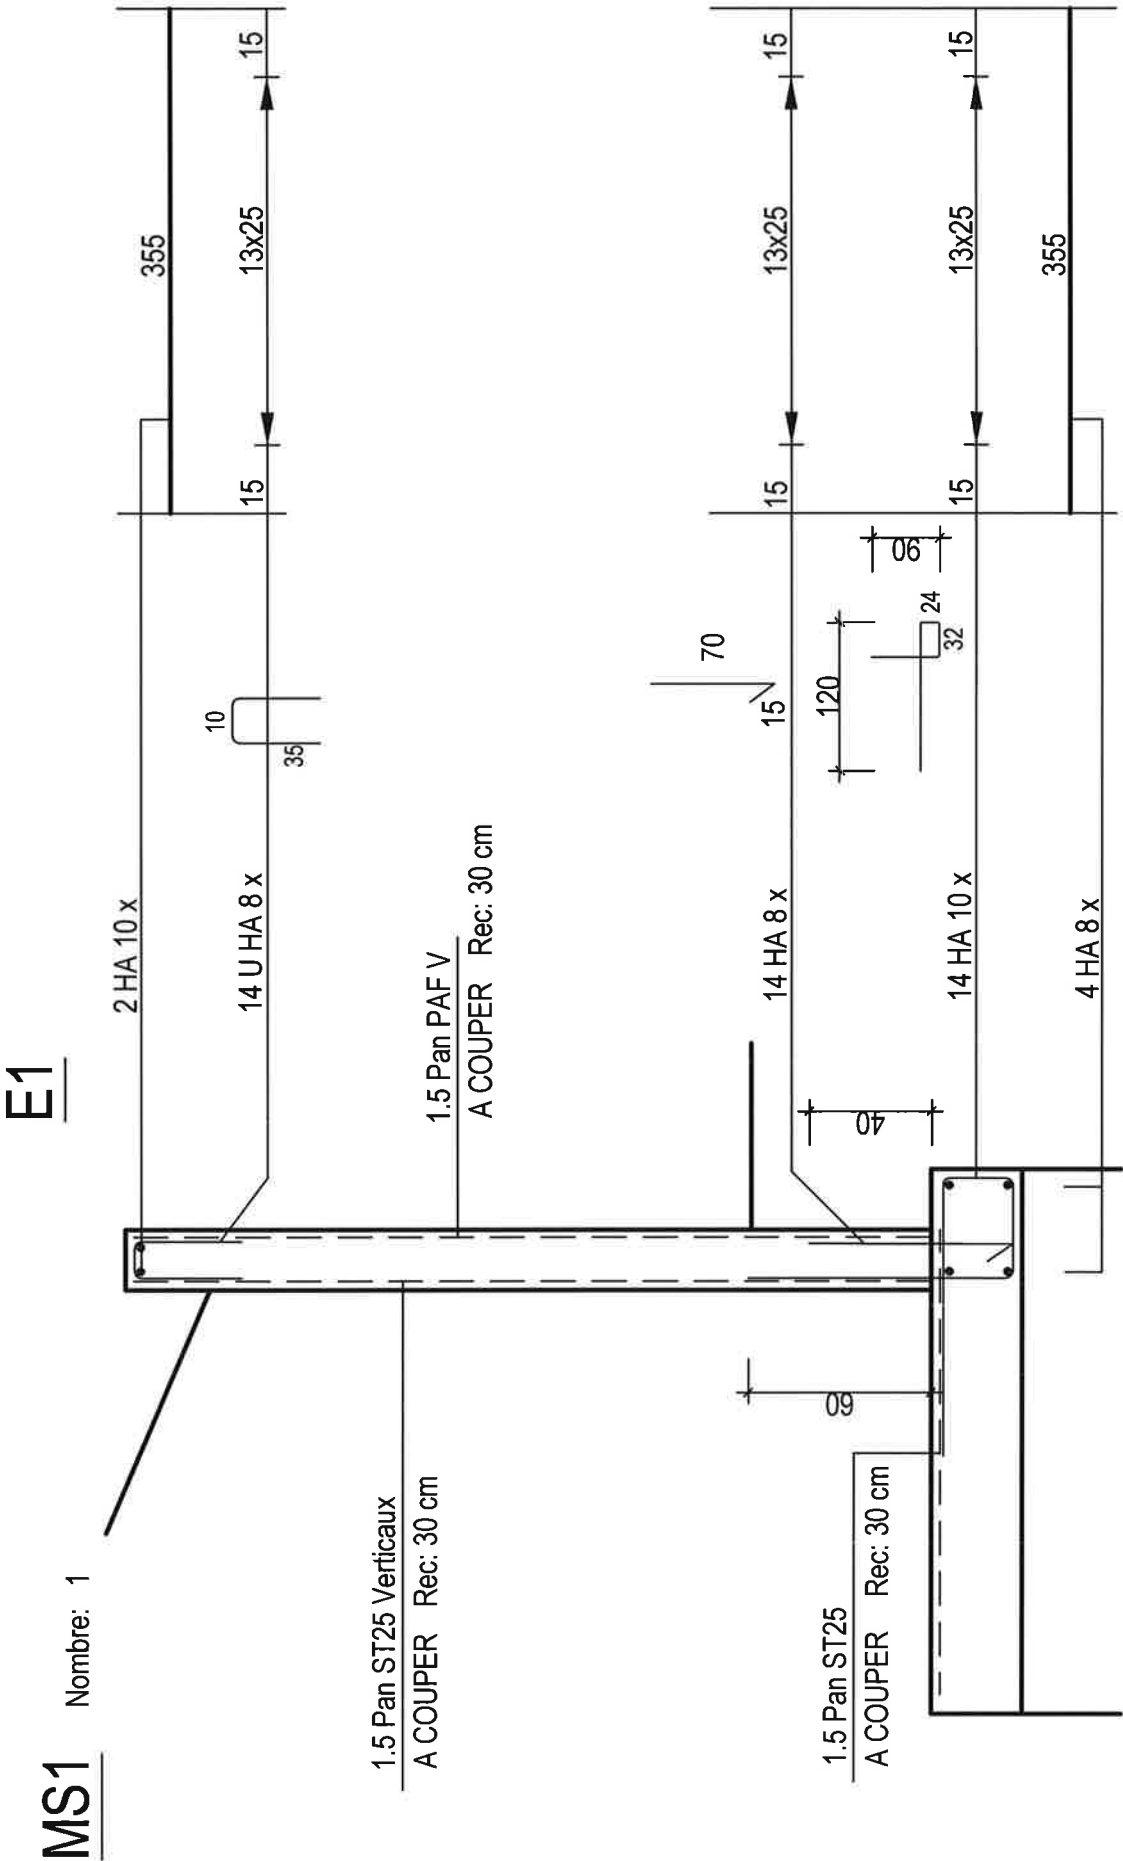

DALLAGE

JOINTS SCIÉS

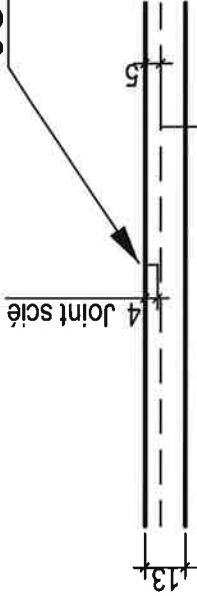



Pan ST10 480X240

Rec: 30 cm MINI

Nb: 14 Env. (Nb: INDICATIF A CONFIRMER PAR LE DALLAGISTE)

- Date 12/04/15 - 10 étages -  
Section : 50 x 50ht

**Fc28= 25 MPa Fe= 500 MPa Fissuration peu préjudiciable**

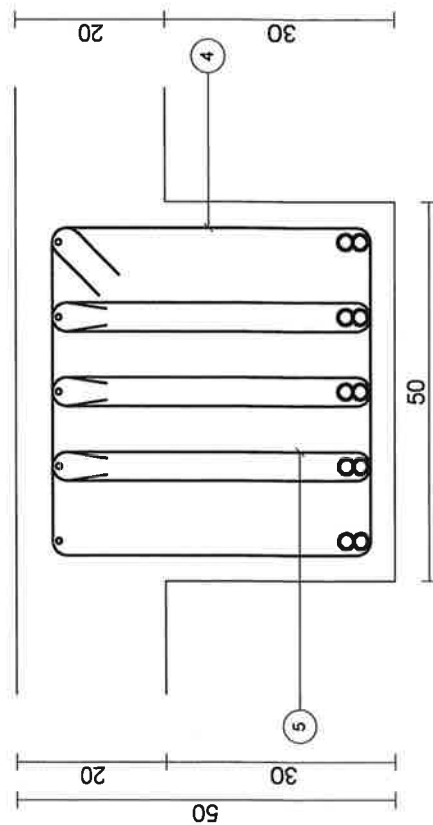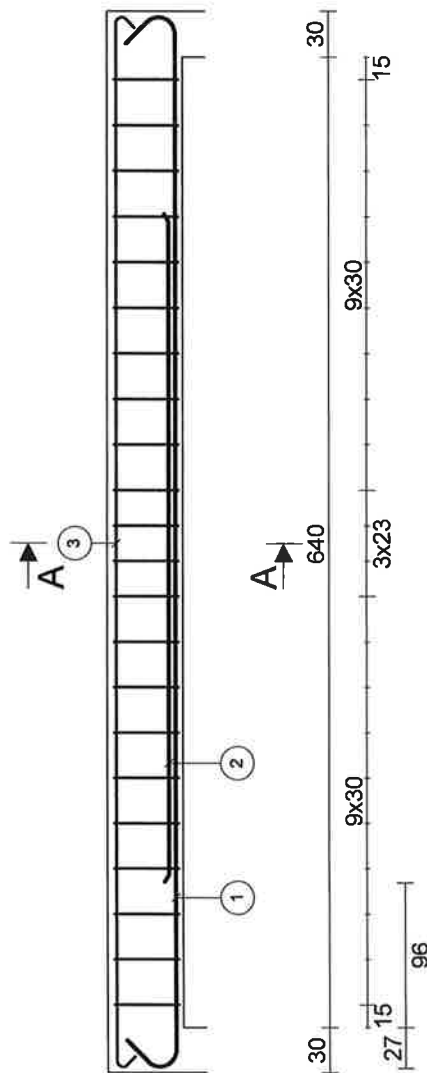

| Barre                              |       | Lg         | Forme                                                                            |
|------------------------------------|-------|------------|----------------------------------------------------------------------------------|
| 1                                  | 5HA20 | 762        |  |
| 2                                  | 5HA20 | 442        | 442                                                                              |
| 3                                  | 5HA8  | 719        |  |
| 4                                  | 22HA8 | 189        |  |
| 5                                  | 66HA8 | 104        |  |
| <p>602</p> <p>da Par Phiere 91</p> |       |            |                                                                                  |
|                                    |       |            |                                                                                  |
| Barre                              |       | Lg/Poids   |                                                                                  |
| HA8                                |       | 146.3/57.8 |                                                                                  |
| HA20                               |       | 60.2/148.4 |                                                                                  |

CO2  
da Ferrière 9/