




COUPE D
Ech: 1/25

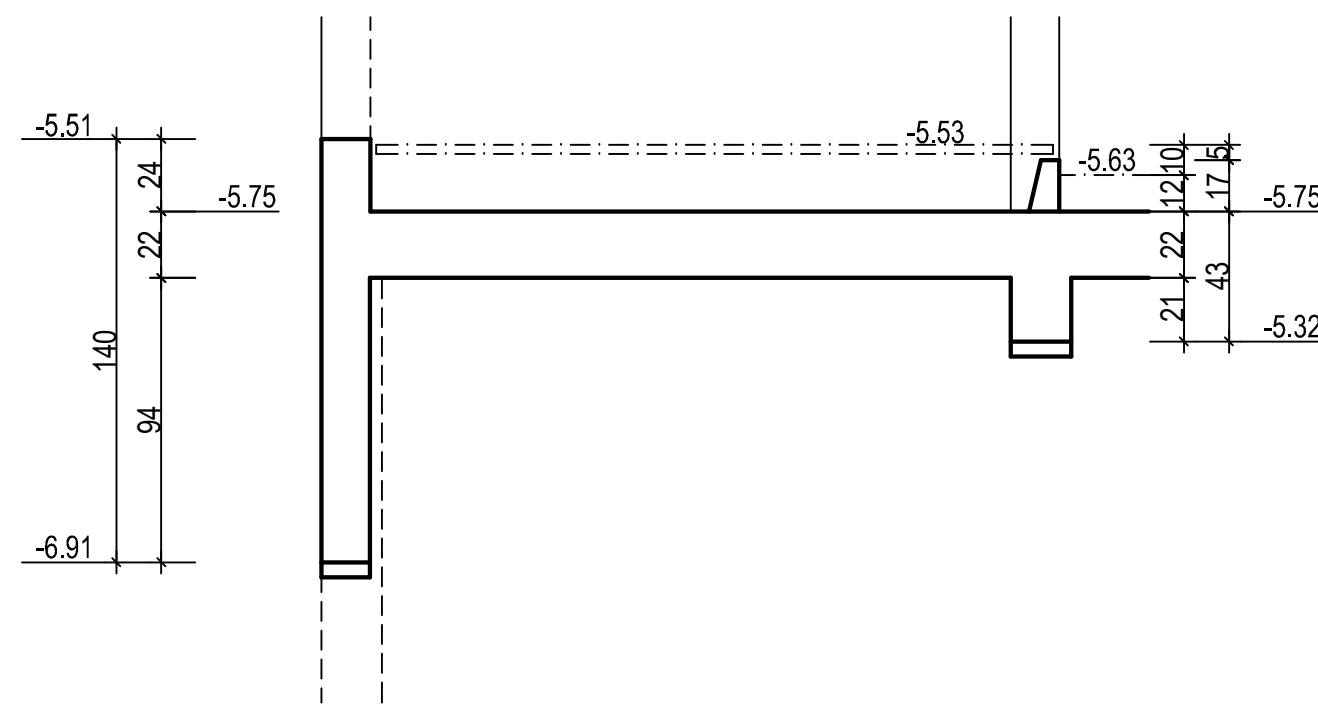


COUPE A
Ech: 1/25

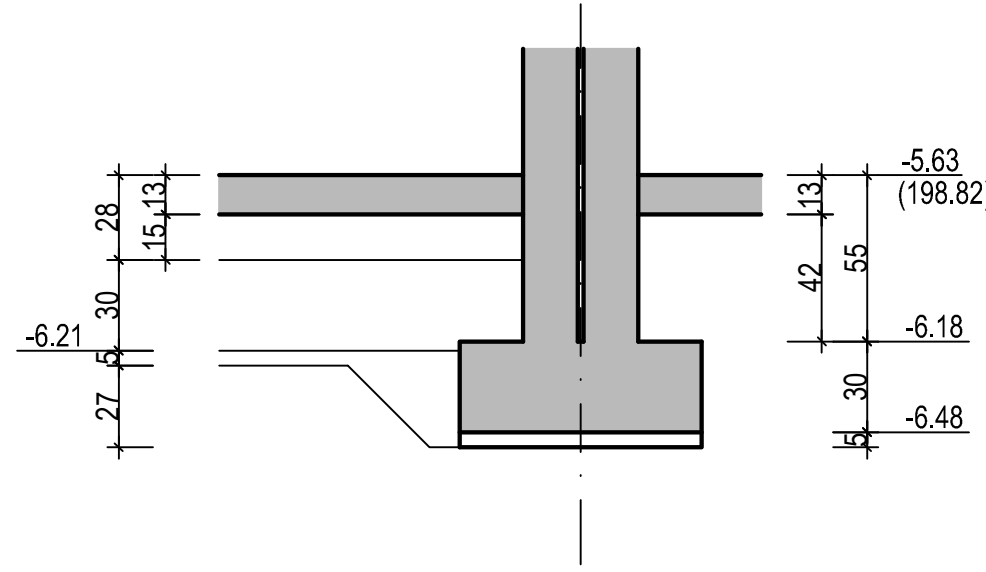

COUPE B
Ech: 1/25

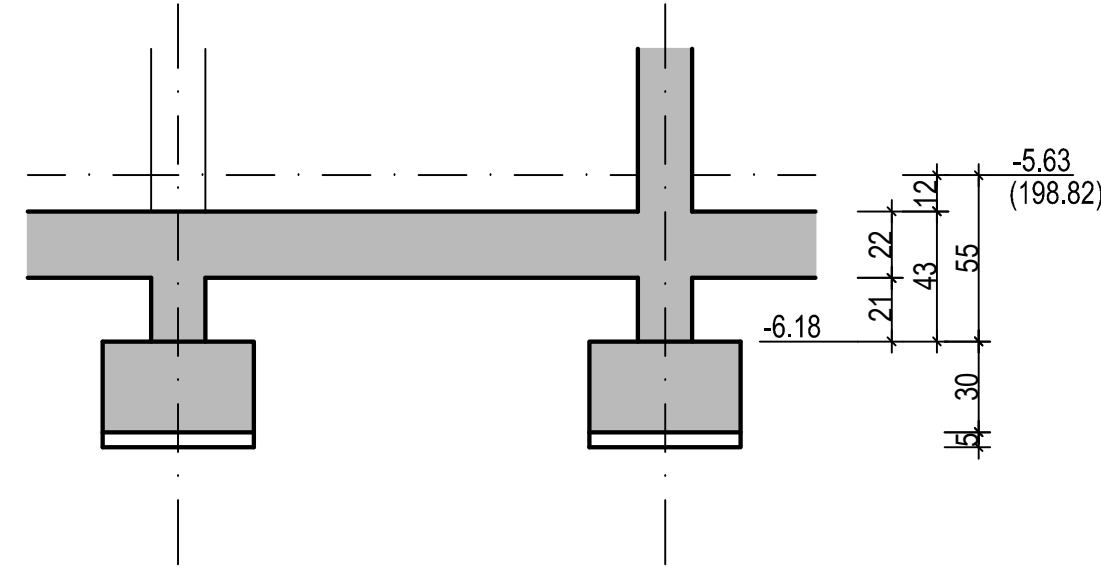


COUPE C
Ech: 1/25

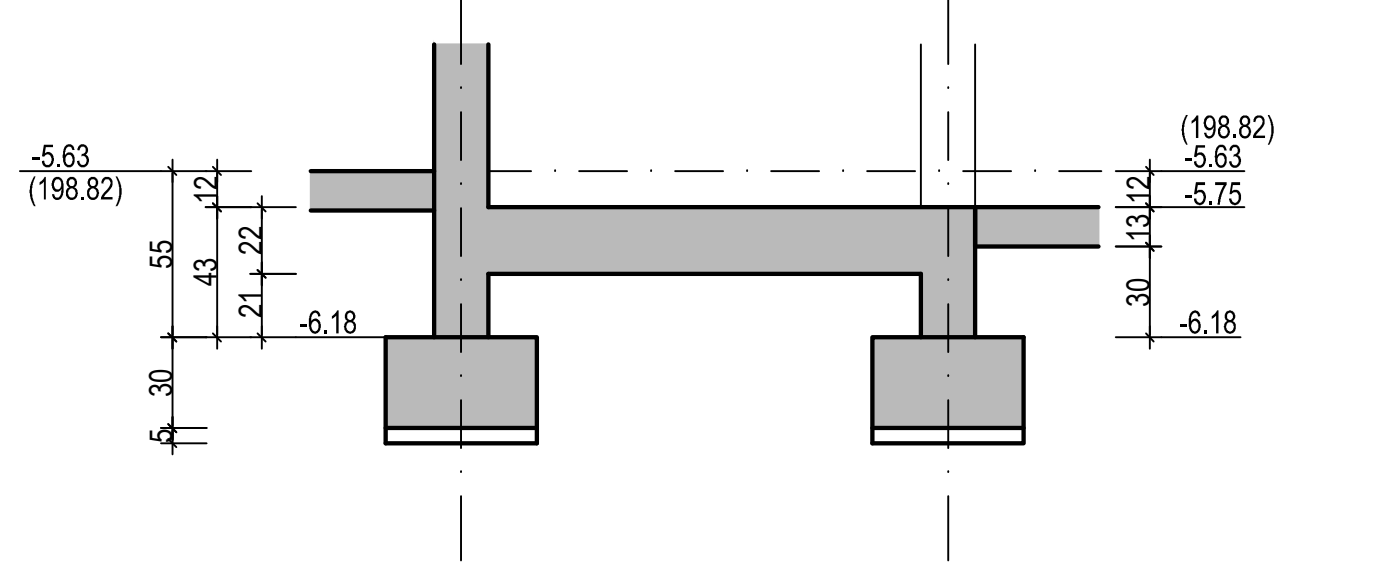


COUPES TYPES SEMELLES FILANTES
Ech: 1/25

RIVES

COUPE SUR DALLE

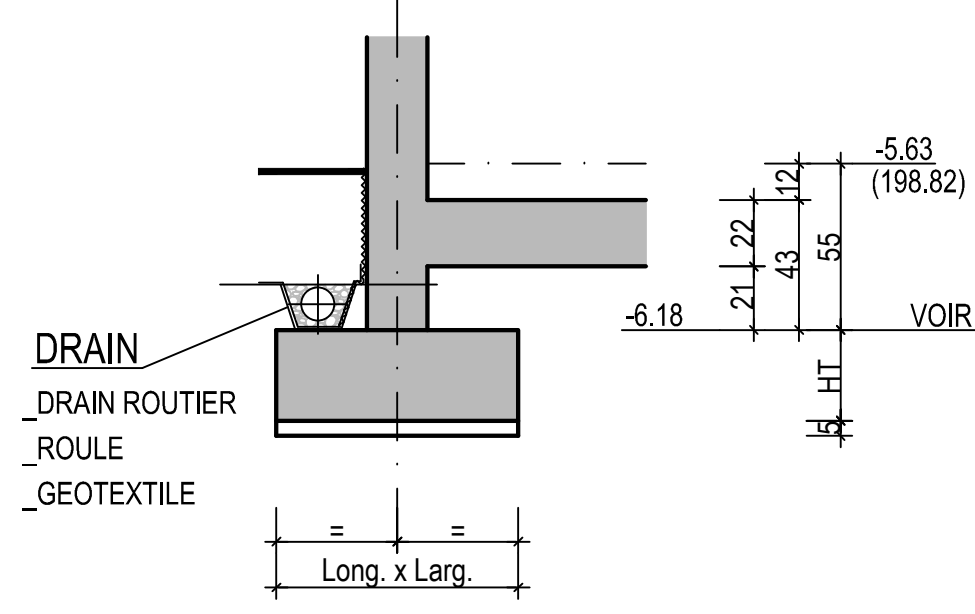


COUPE SUR DALLAGE

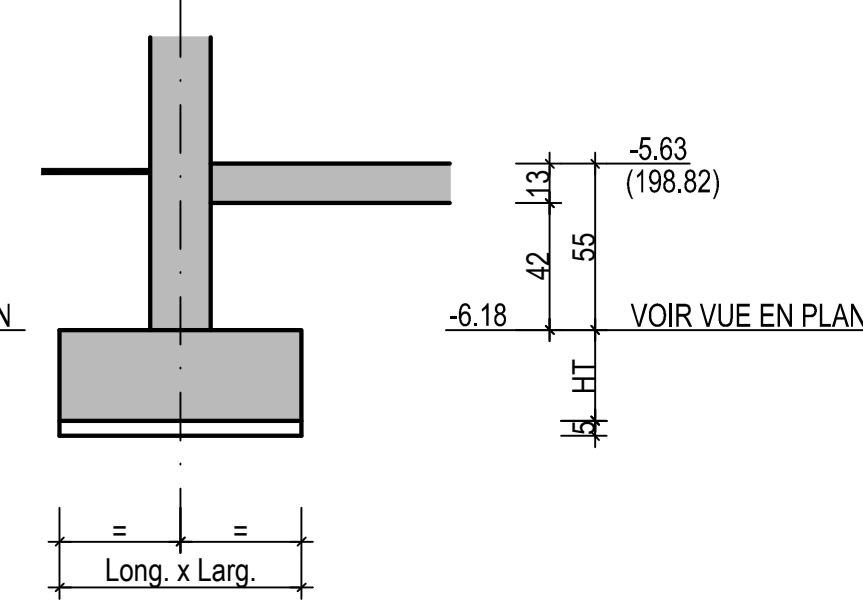

INTERIEURES

COUPE SUR DALLE

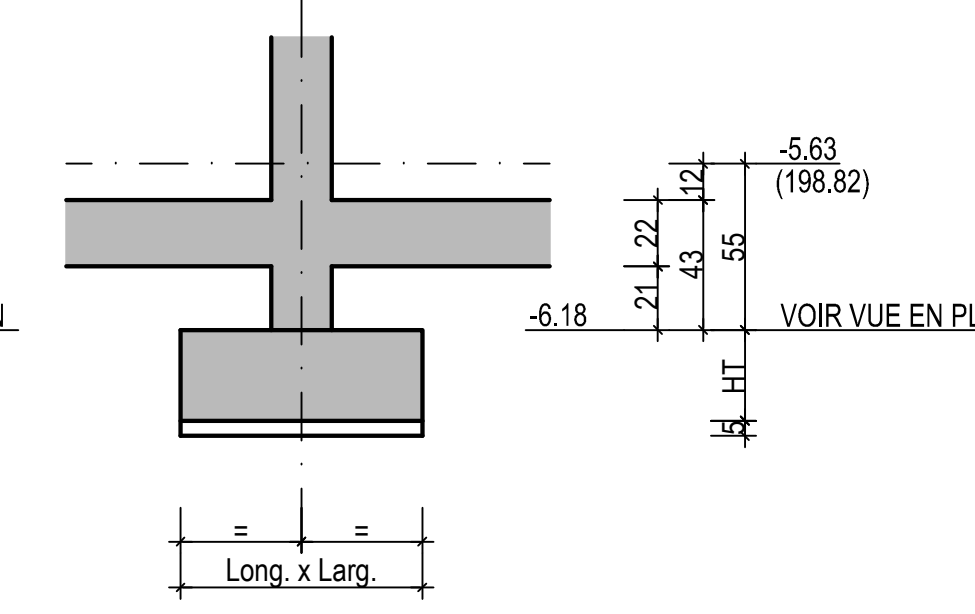

COUPE SUR DALLAGE

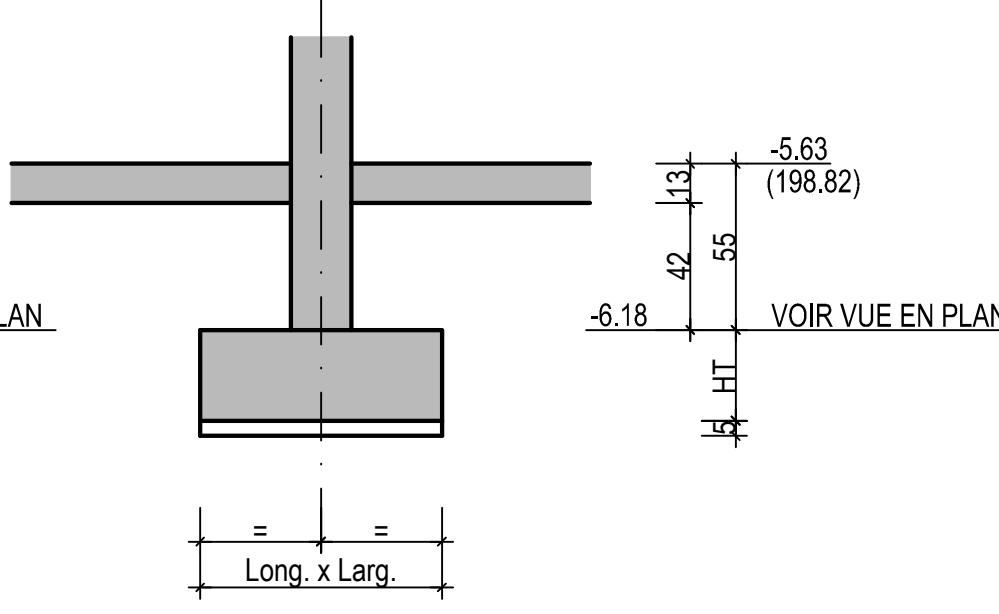



TABLEAU SEMELLES FILANTES

Repère	Larg.	HT
SF 50	50	30
SF 60		
SF 70		
SF 80	80	30


VUE EN PLAN
Ech: 1/50

- 1 FINI: -5.63=198.82
DALLAGE Epr: 13 cm
DESSUS BRUT: -5.63
RESERVE: 0 cm
Voir pente dans local vélo
- 2 FINI: -5.63=198.82
DALLE BA Epr: 22 cm
DESSUS BRUT: -5.75
RESERVE: 12 cm
- 3 FINI: -5.53=198.92
DALLE BA Epr: 22 cm
DESSUS BRUT: -5.75
RESERVE: 22 cm
Bois sur plots
- 4 FINI: -5.53=198.92
DALLAGE Epr: 13 cm
DESSUS BRUT: -5.75
RESERVE: 12 cm
- 5 FINI: -5.65=198.80
DALLE BA Epr: 22 à 19 cm
DESSUS BRUT: -5.75 à -5.78
RESERVE: 10 à 13 cm


FONDATEURS VOIR PLAN N° C01

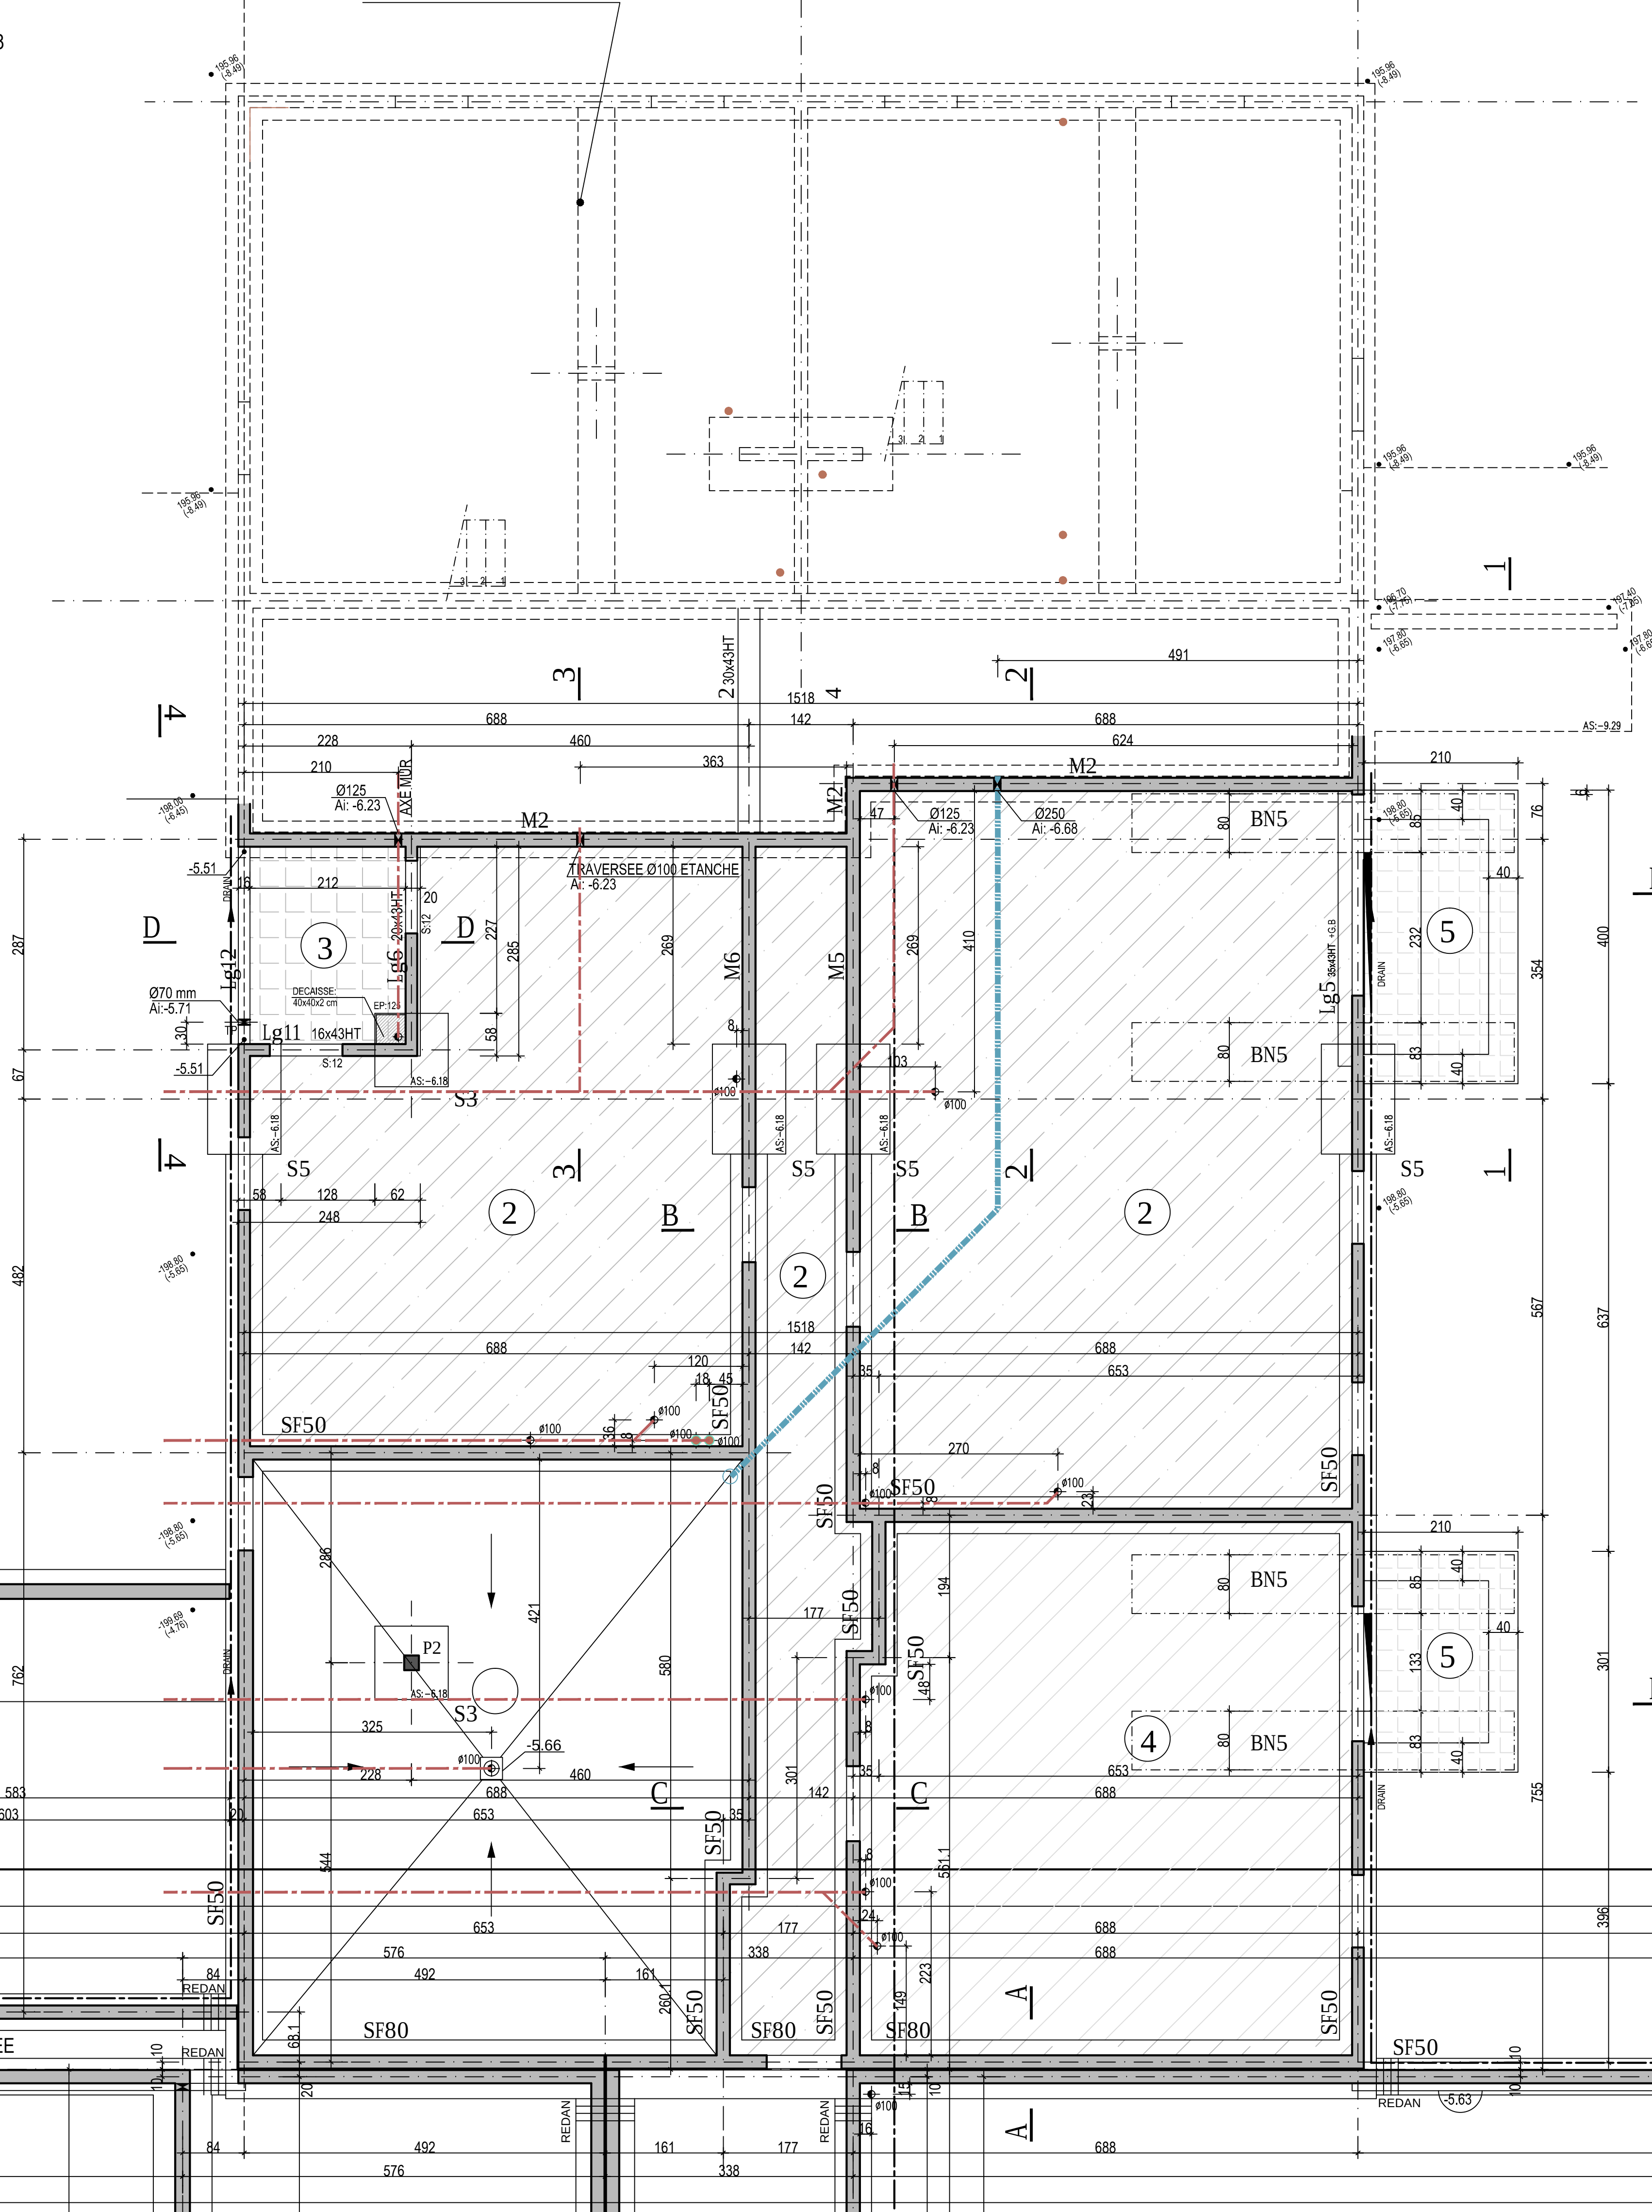


COUPE 4
Ech: 1/50

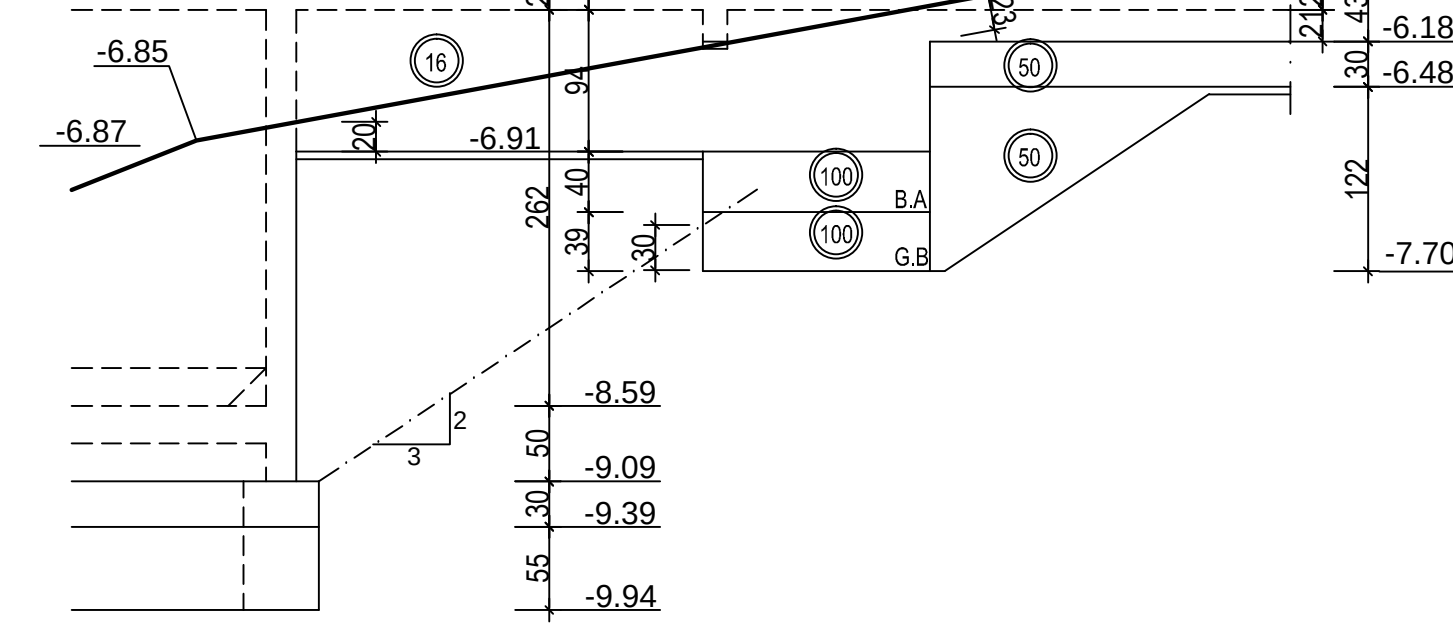


COUPE 3
Ech: 1/50

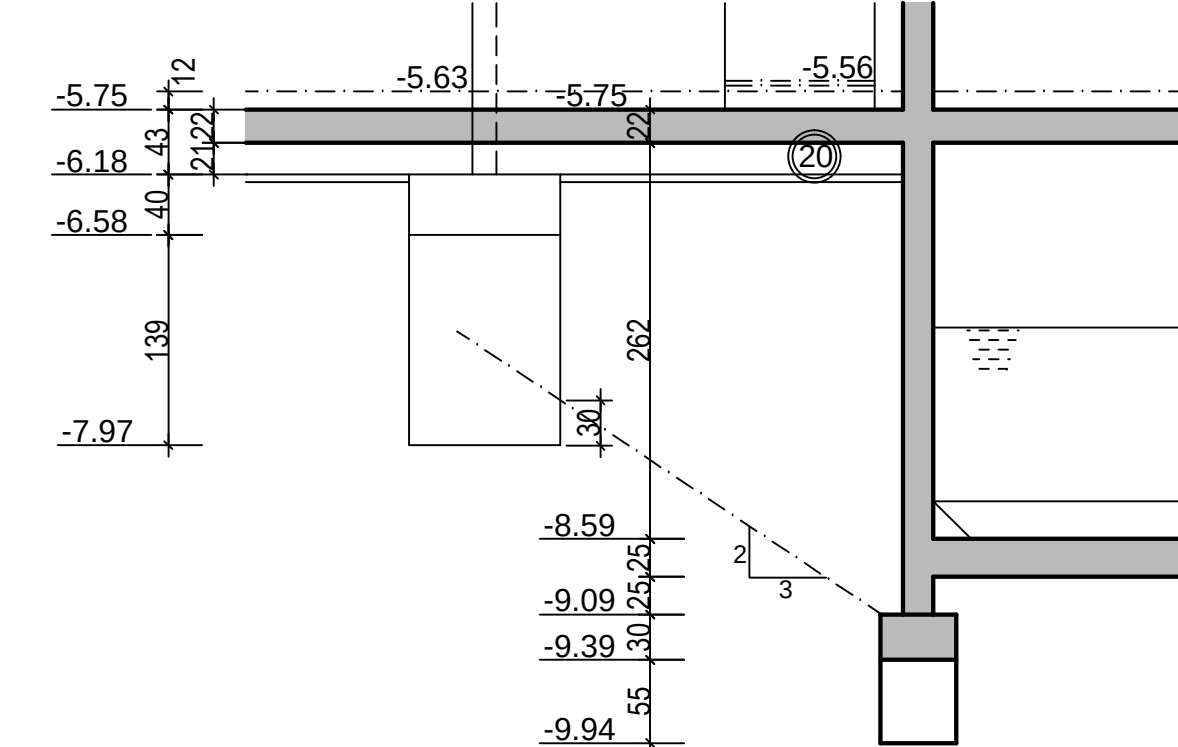

COUPE 2
Ech: 1/50

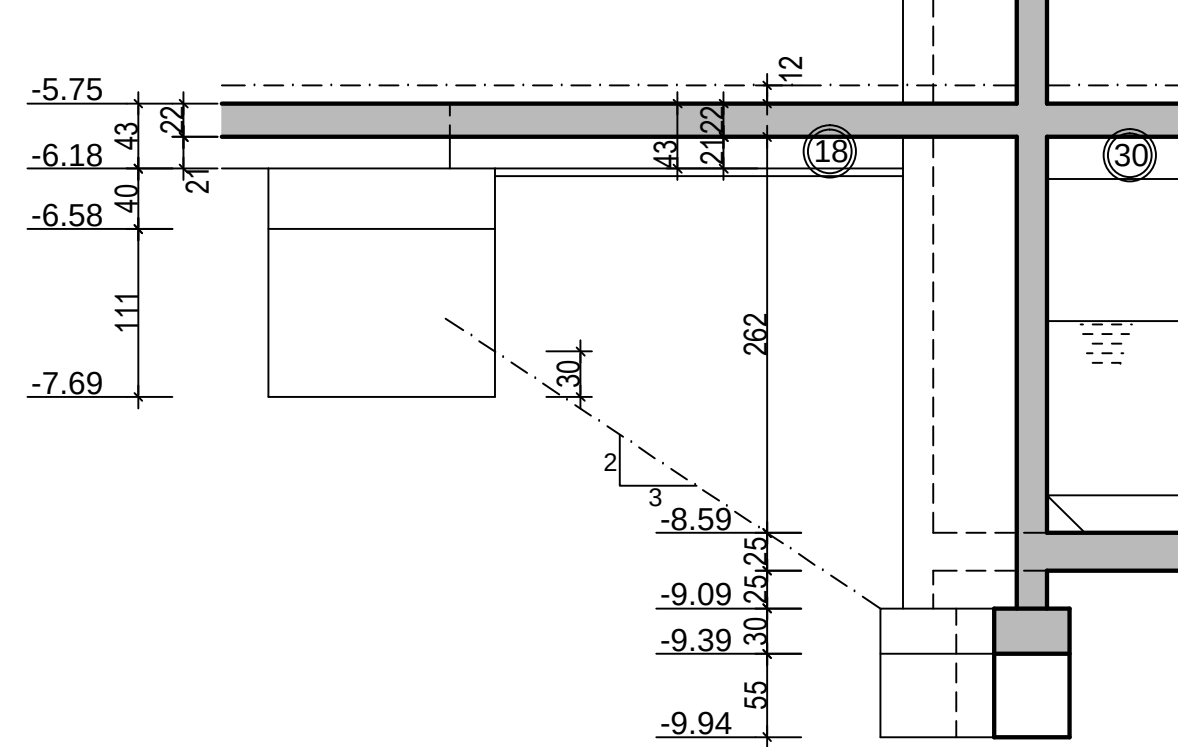


COUPE 1
Ech: 1/50

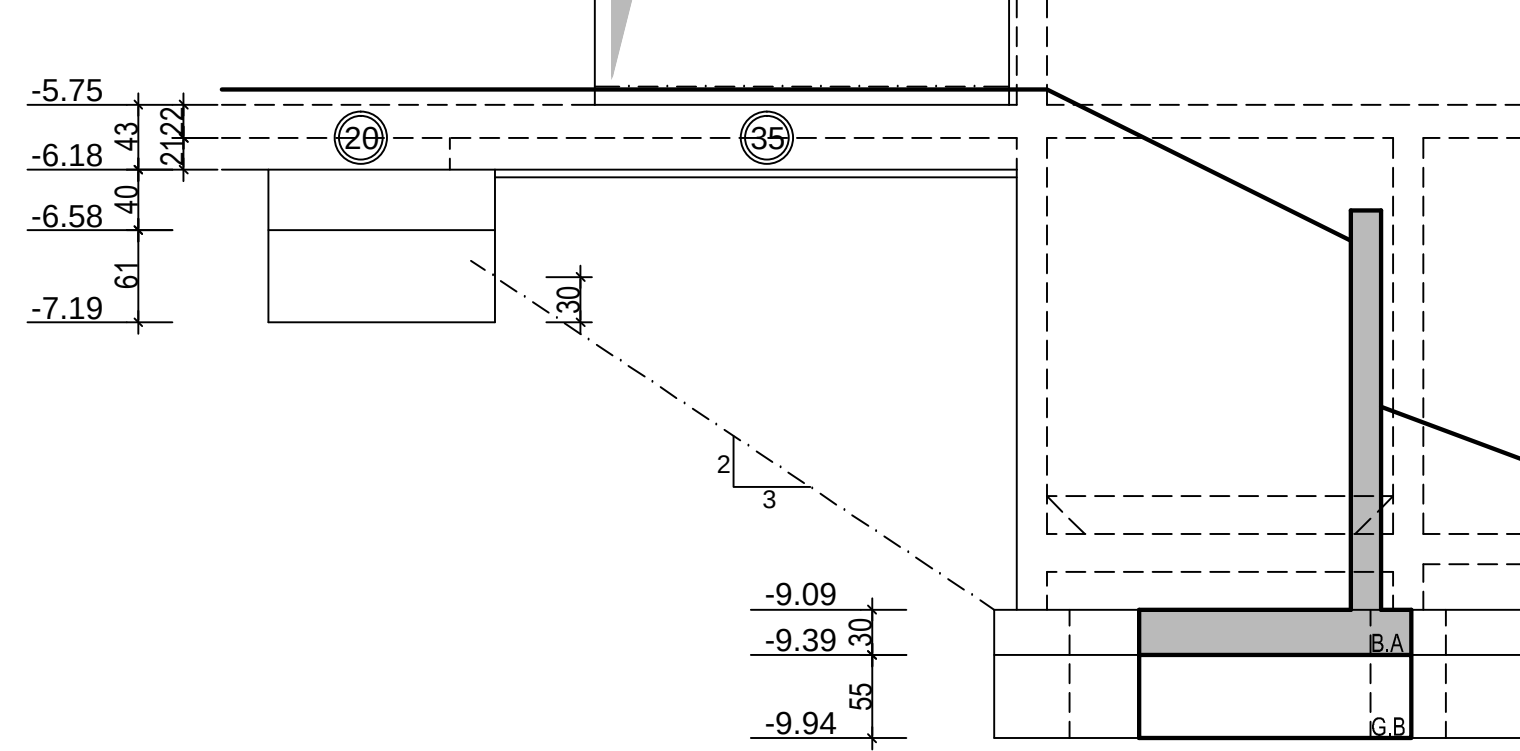

COUPES TYPES SEMELLES ISOLEES
Ech: 1/25

COUPE SUR DALLE

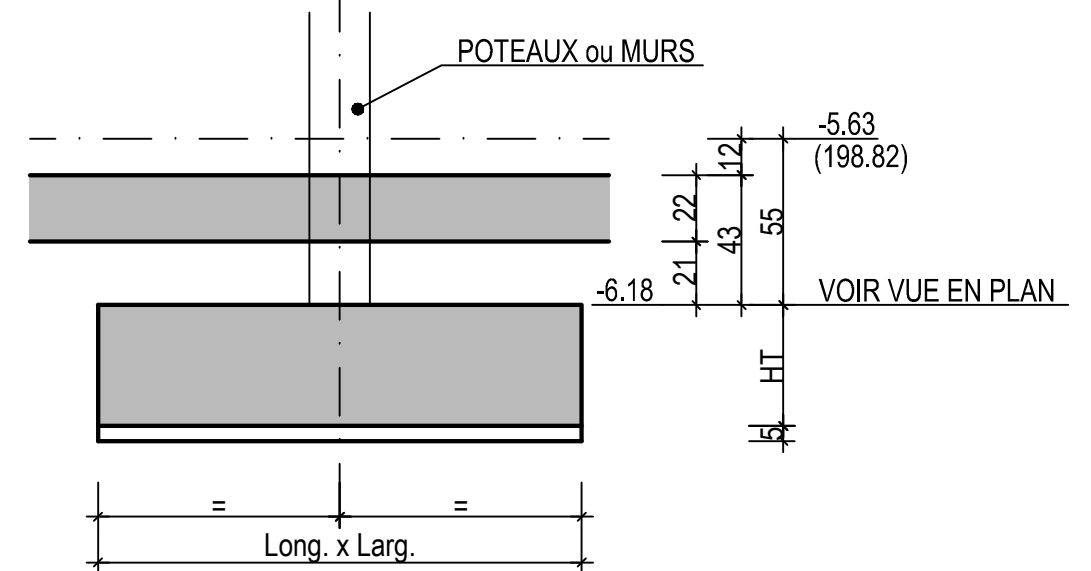

COUPE SUR DALLAGE


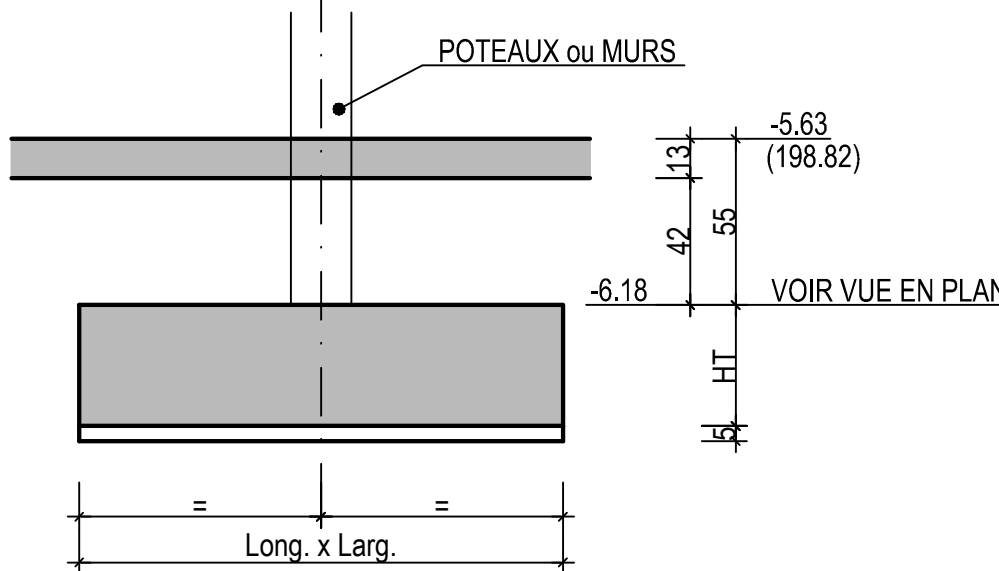


TABLEAU SEMELLES ISOLEES

Repère	Long. x Larg.	HT
S1	100 x 150	40
S2	80 x 400	30
S3	100 x 100	40
S4	80x 450	30
S5	100 x 150	40

COUPE E
Ech: 1/50

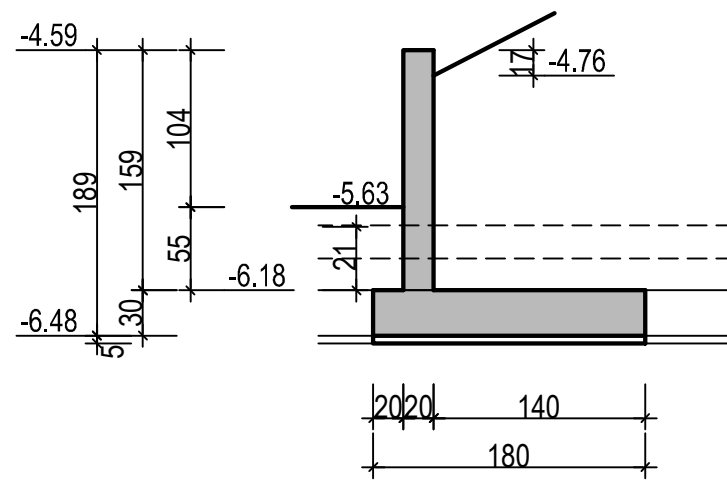

±0.00 = 204.45 = NIVEAU FINI du REZ de CHAUSSEE Bât: C

NOAHO

Chemin de Fontanière - 69350 La Mulatière

Création de logements

Les entreprises réalisant les travaux devront tenir compte des derniers plans architecturaux lors de la réalisation des travaux.
Les plans du bureau MATTÉ ne doivent servir qu'au corps d'état concerné et doivent être des plans d'exécution.

ARCHITECTES:	Atelier DTS	MO DELEGUE:	PSO Ingénierie
BET STRUCTURE:	MATTE SAS	MO:	CSPS
BET FLUIDES:	PRELEM	SUD EST COORDINATION	OPC
ECONOMISTE:	EXECO		
BUREAU DE CONTROLE:	Bureau VERITAS	ENTREPRISES:	Fontanel pbc

Bât: C Aile EST
FONDATEURS au -2
Coffrage

INCE	DATE	MODIFICATIONS
A	17/08/2015	AJOUTE COUPE E et RESEAUX SOUS DALLAGE

MATTÉ
BUREAU D'ETUDES
STRUCTURES ET FLUIDES
119 BOULEVARD DU MARSHALL GENERAL DE GAULLE
74 04 72 44 02 87 Fax 04 72 44 26 99
E-mail: matte@matte.fr

DOE
Contrainte de sol: 8 bars ELS
Aciers HA (T) F4E500
Aciers Doux (B) F4E235
Aciers TS F4E 500
30cm k28 > 20MPa
Enrobage = 3cm

PLAN N°
C03 A
DATE: 12/05/2015

Affaire N°
13.12.119