

NOAHO

Chemin de Fontanière - 69350 La Mulatière

Création de logements

Les entreprises réalisant les travaux devront tenir compte des derniers plans architecte lors de la réalisation des travaux
Les plans du be MATTE ne doivent servir qu'au corps d'état concerné et doivent être des plans d'exécution.

ARCHITECTE(S):	Atelier D'IS	MO DELEGUE:	
BET STRUCTURE:	MATTE SAS	MOE:	PSO Ingénierie
BET FLUIDES:	PRELEM	CSPS:	SUD EST COORDINATION
ECONOMISTE:	EXECO	OPC:	
BUREAU DE CONTROLE:	Bureau VERITAS	ENTREPRISE(S):	Fontanel-pbc

Bât: C Ailes EST et OUEST
FONDATIONS au -2
Armatures

INDICE	DATE	MODIFICATIONS
A	16/06/2015	AJOUTE PAGE 9bis

MATTÉ
BUREAU D'ÉTUDES
STRUCTURES ET FLUIDES

119 BOULEVARD STALINGRAD 69100 VILLEURBANNE

Tél. 04 72 44 02 87 Fax 04 72 44 26 59

E-mail : bet@matte.fr

Dessiné par : J.BO

Contrôlé par : P.LIN

Echelle : 1/50°

DOE

Contrainte de sol: 8 bars ELS

Aciers HA (T) FeE500

Aciers Doux (Ø) FeE 235

Aciers TS FeE 500



Béton fc28 >= 25MPa

Enrobage = 3 cm

PLAN N°
C05 A

DATE : 11/05/2015

Affaire N°
13.12.119

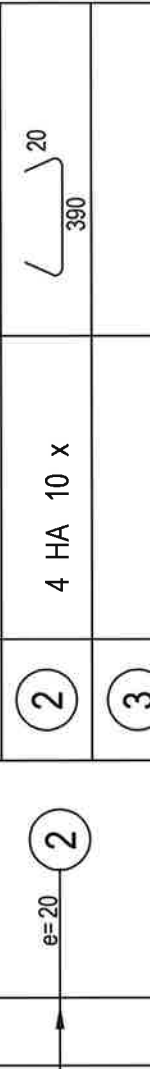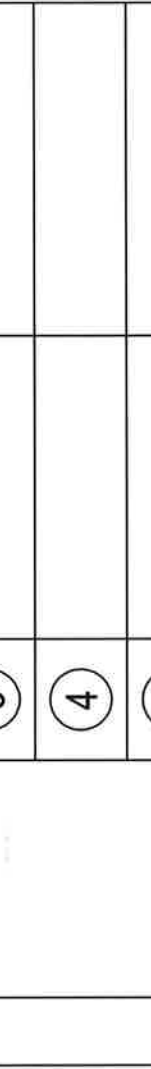AFF: S.13.12.119	Bât: C	LA MULATIERE-69350 La Mulatiere CREATION de LOGEMENTS	FONDATIONS au -2	Plan n° C 05	Page: 2
S2 Nombre: 9 80X400x40ht  				① 20 HA 8 x	
				② 4 HA 10 x	
				③	
				④	
				⑤	
				⑥	
				⑦	
				⑧	
				⑨	
				⑩ 20 HA 8 x	
				⑪	
				⑫	
				⑬	
				⑭	
				⑮	



AFF: S.13.12.119	Bât: C	LA MULATIERE-69350 LaMulatiere CREATION de LOGEMENTS	FONDATIONS au -2	Plan n° C 05	Page: 4
S4 80X450x40ht					

AFF: S.13.12.119	Bât: C	LA MULATIERE-69350 LaMulatiere CREATION de LOGEMENTS	FONDATIONS au -2	Plan n° C 05	Page: 5
S5 Nombre: 4 100X150x40ht		VOIR ATTENTES POTEAUX 40 150 100 e=25 2 1			
					①
					②
					③
					④
					⑤
					⑥
					⑦
					⑧
					⑨
					⑩
					⑪
					⑫
					⑬
					⑭
					⑮
			6 HA 12 x		
			4 HA 12 x		

AFF: S.13.12.119	Bât: C	LA MULATIERE-69350 LaMulatiere CREATION de LOGEMENTS	FONDATIONS au -2	Plan	n° C 05	Page: 6
SF50 Nombre: 32 Rec: 50 cm				①	4 HA 8 x	600
				②	22 HA 8 x	
				③	22 HA 8 x	
				④		
				⑤		
				⑥		
				⑦		
				⑧		
				⑨		
				⑩		
				⑪		
				⑫		
				⑬		
				⑭		
				⑮		


AFF: S.13.12.119	Bât: C	LA MULATIERE-69350 LaMulatiere CREATION de LOGEMENTS	FONDATIONS au -2	Plan n° C 05	Page: 7	
SF80 Nombre: 6 Rec: 50 cm			A replier au droit des ouvertures 21 x 25 37 38 80 40 21 x 25 37 38	①	6 HA 8 x	600
				②	28 HA 8 x	
				③	28 HA 8 x	
				④		
				⑤		
				⑥		
				⑦		
				⑧		
				⑨		
				⑩		
				⑪		
				⑫		
				⑬		
				⑭		
				⑮		

AFF: S.13.12.119	Bât: C	LA MULATIERE-69350 LaMulatiere CREATION de LOGEMENTS	FONDATIONS au -2	Plan n° C05	Page: 8
SF80 Nombre: 6 Rec: 50 cm					
①	6 HA 8 x	600			
②	22 HA 8 x				
③	2x22 HA 8 x				
④					
⑤					
⑥					
⑦					
⑧					
⑨					
⑩					
⑪					
⑫					
⑬					
⑭					
⑮					

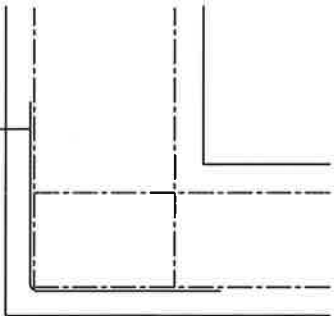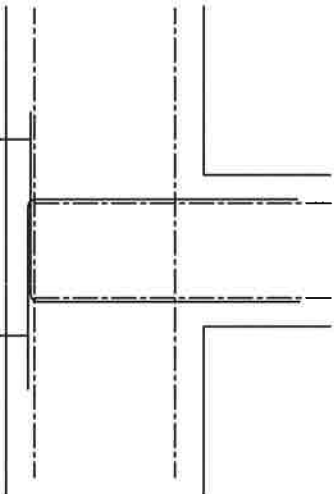AFF: S.13.12.119	Bât: C	LA MULATIERE-69350 La Mulatiere CREATION de LOGEMENTS	FONDATIONS au -2	Plan n° C 02	Page: 9	
ANGLES SEMELLES FILANTES Nombre: 20 1  Nombre: 14 2 2  <tr><td>1</td><td>1 HA 8 x</td><td>70</td><td>70</td></tr> <tr><td>2</td><td>2X1 HA 8 x</td><td>70</td><td>100</td></tr> <tr><td>3</td><td></td><td></td><td></td></tr> <tr><td>4</td><td></td><td></td><td></td></tr> <tr><td>5</td><td></td><td></td><td></td></tr> <tr><td>6</td><td></td><td></td><td></td></tr> <tr><td>7</td><td></td><td></td><td></td></tr> <tr><td>8</td><td></td><td></td><td></td></tr> <tr><td>9</td><td></td><td></td><td></td></tr> <tr><td>10</td><td></td><td></td><td></td></tr> <tr><td>11</td><td></td><td></td><td></td></tr> <tr><td>12</td><td></td><td></td><td></td></tr> <tr><td>13</td><td></td><td></td><td></td></tr> <tr><td>14</td><td></td><td></td><td></td></tr> <tr><td>15</td><td></td><td></td><td></td></tr>				1	1 HA 8 x	70	70	2	2X1 HA 8 x	70	100	3				4				5				6				7				8				9				10				11				12				13				14				15			
				1	1 HA 8 x	70	70	
				2	2X1 HA 8 x	70	100	
				3	
				4	
				5	
				6	
				7	
				8	
				9	
				10	
				11	
				12	
				13	
				14	
15	

AFF: S.13.12.119	Bât: C	LA MULATIERE-69350 LaMulatiere CREATION de LOGEMENTS	FONDATIONS au -2	Plan n° C 05	Page: 9bis
SFe50 Nombre: 6 Rec: 50 cm					
①	4 HA 8 x				600
②	22 HA 8 x				80 42 20
③	22 HA 8 x				10 80
④					
⑤					
⑥					
⑦					
⑧					
⑨					
⑩					
⑪					
⑫					
⑬					
⑭					
⑮					

ATTENTES POTEAUX DANS SEMELLES

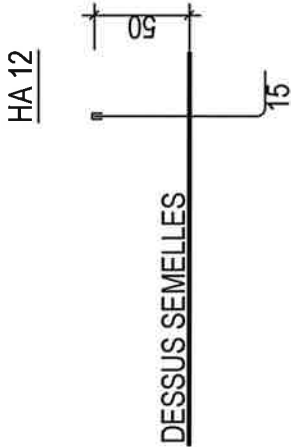


20x20


Nb: 1

20x80

Nb: 7

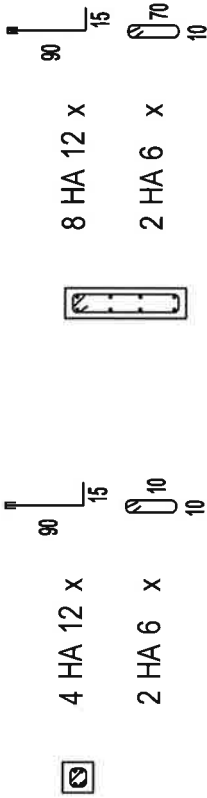


ANGLES et ABOUTS VOILES et OUVERTURES

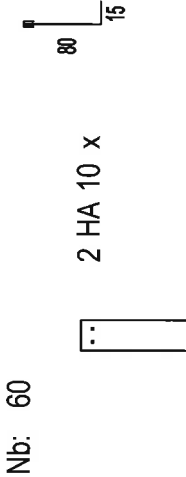

MS2


Nombre: 1

E2

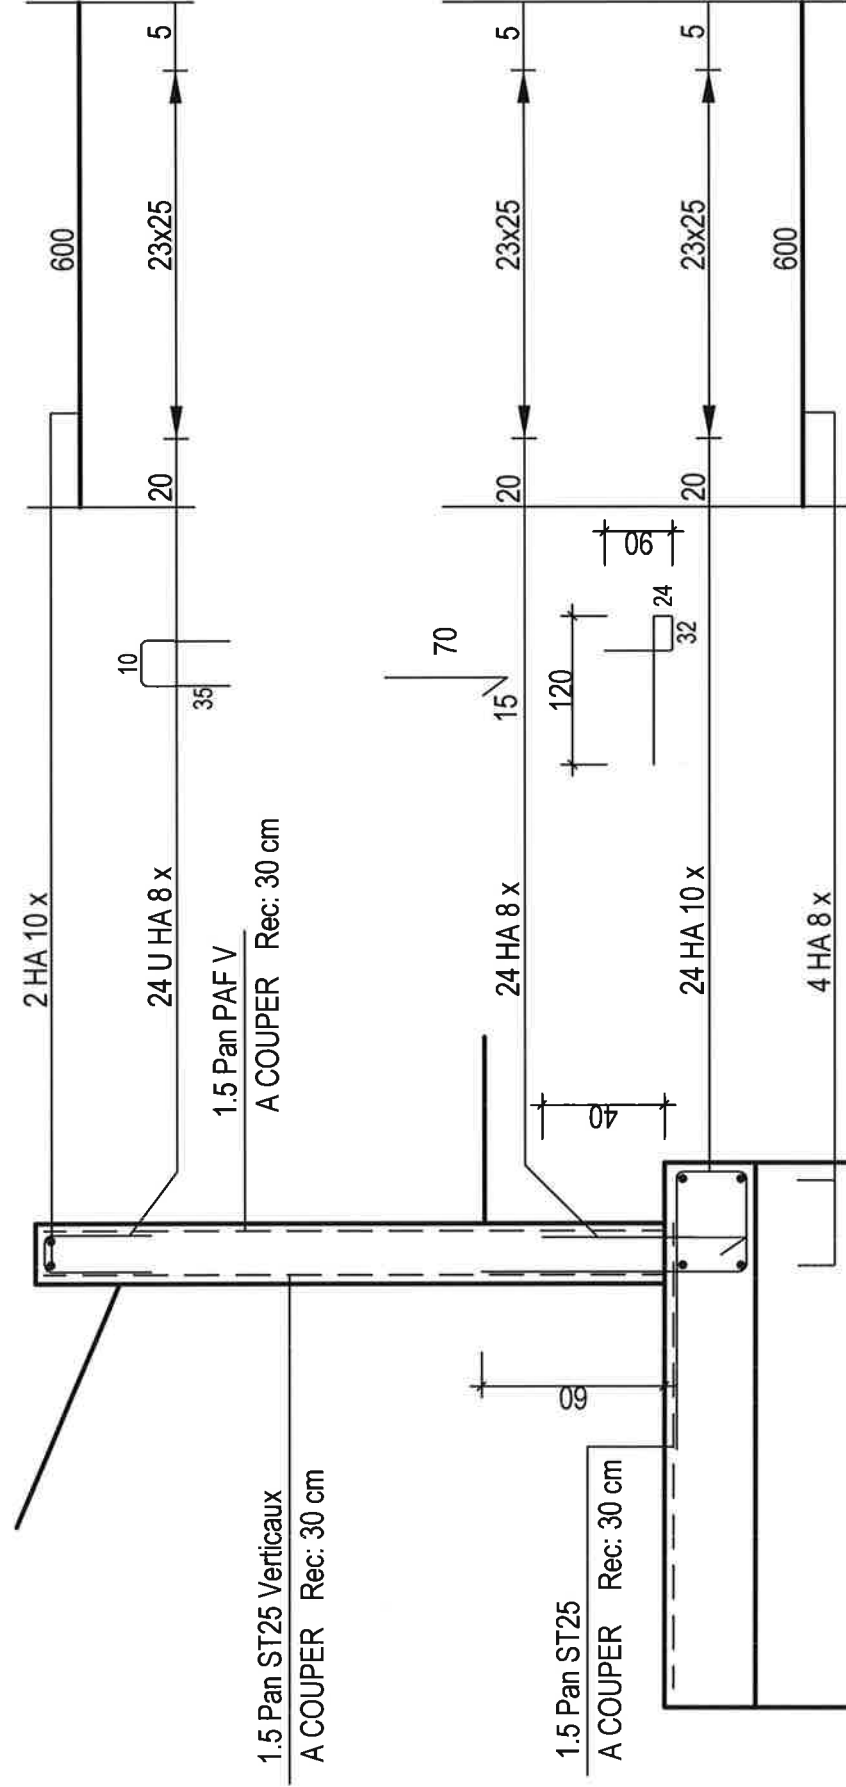


FOSSE ASCENSEUR

1 Pièce

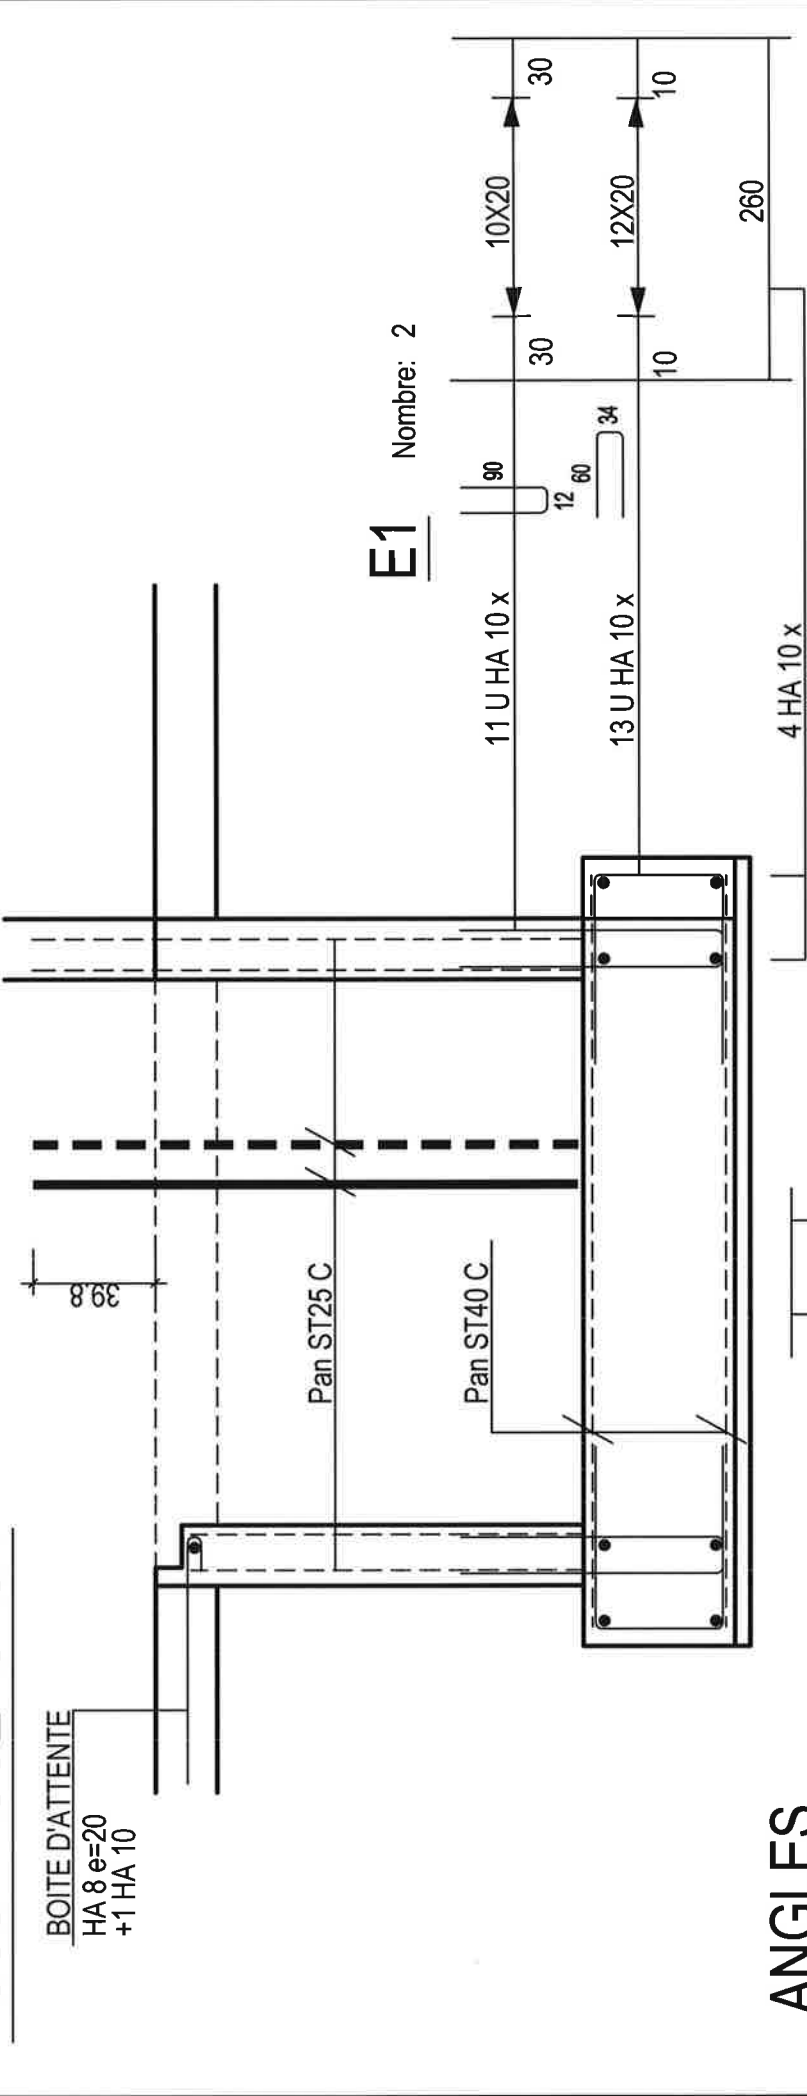


ANGLES

(VALABLE 4 fois)

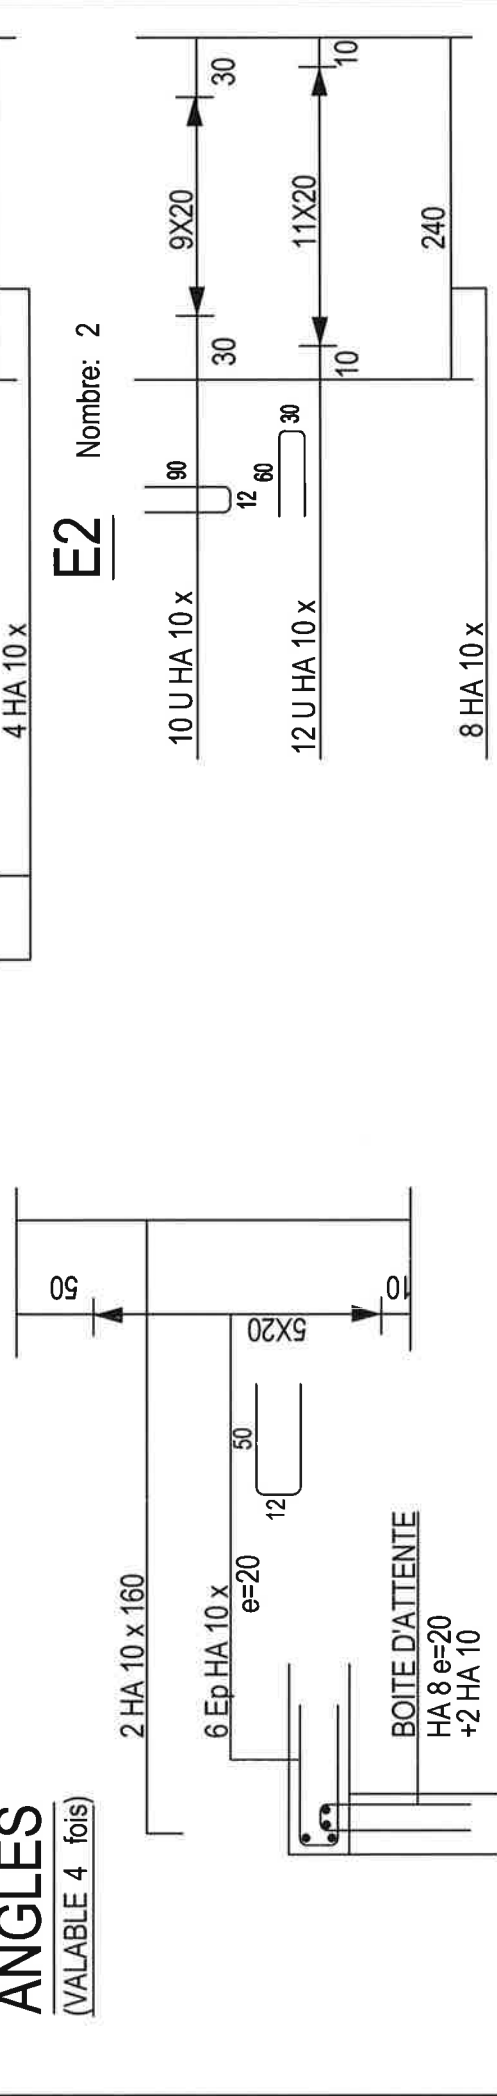

DALLAGE

JOINTS SCIÉS

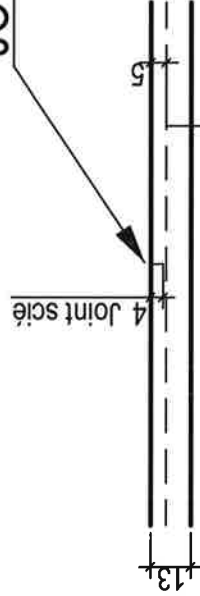

Pan ST10 480X240

Rec: 30 cm MINI

Nb: 100 Env. (Nb: INDICATIF A CONFIRMER PAR LE DALLAGISTE)

