
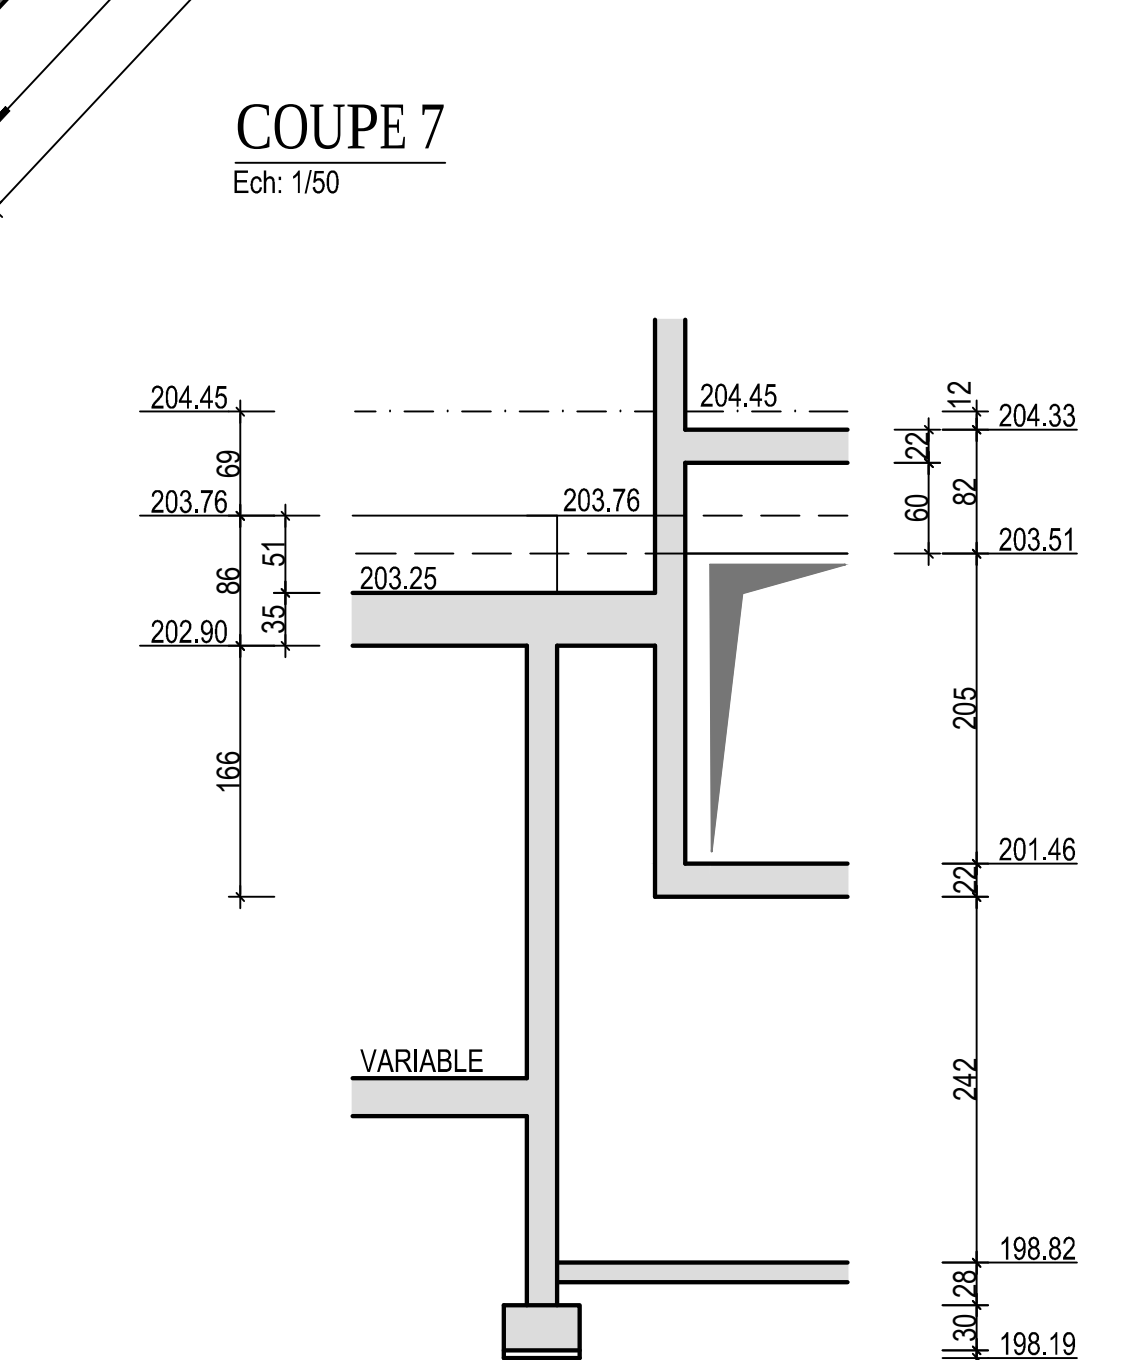
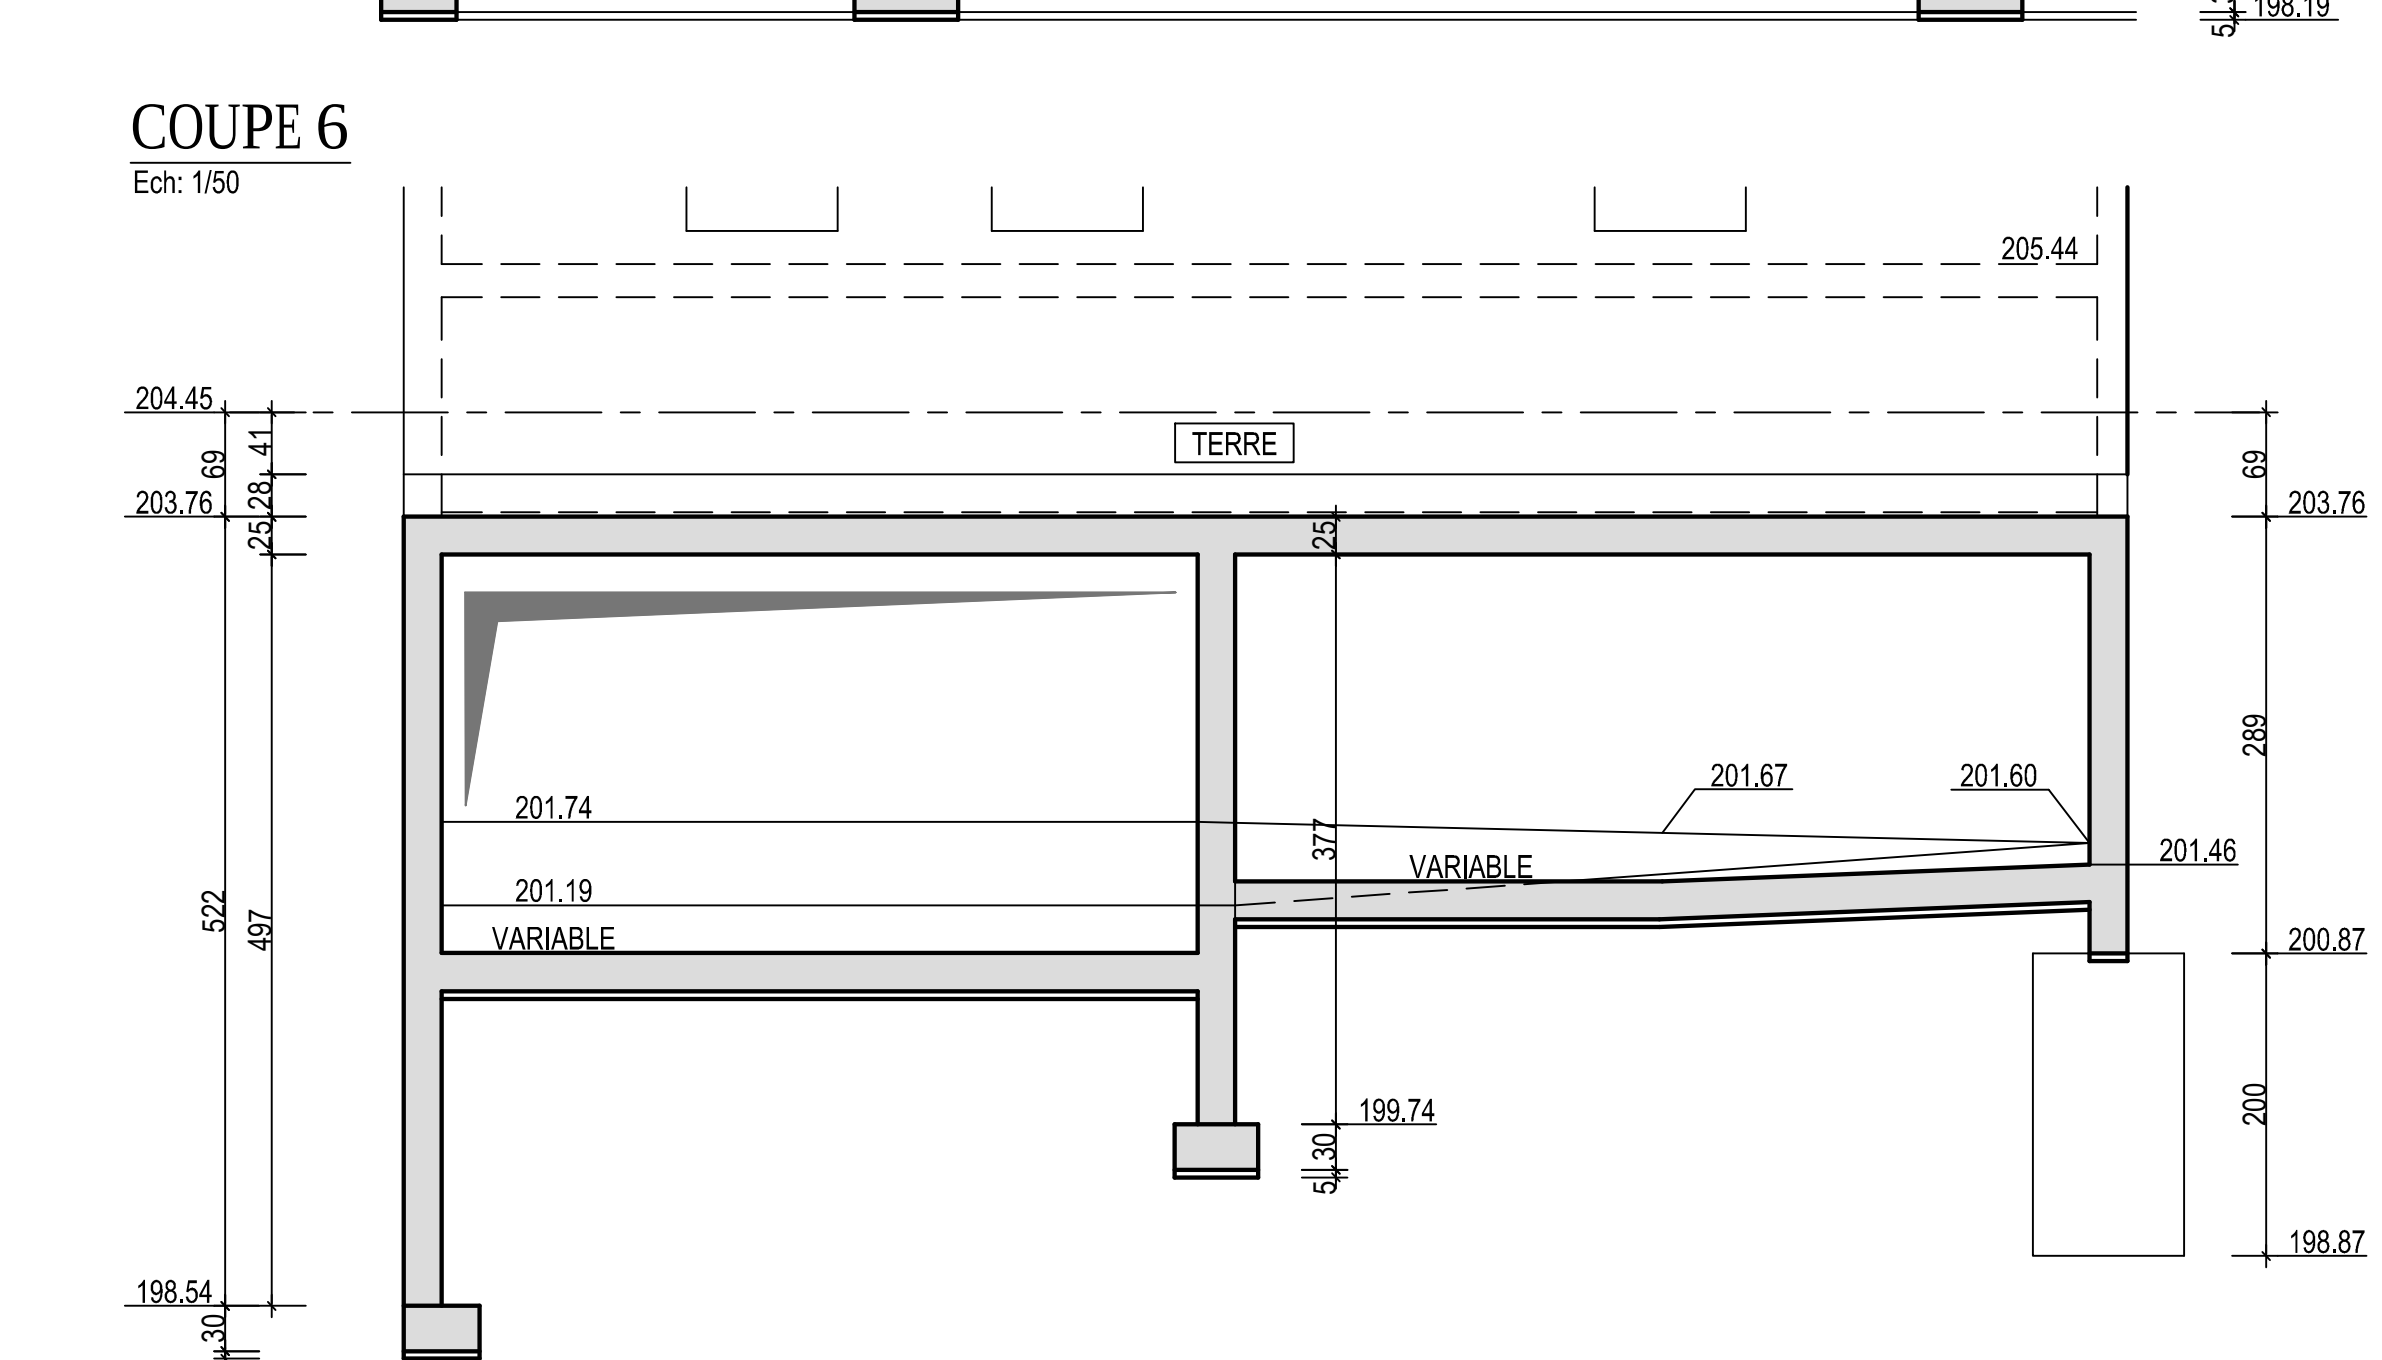
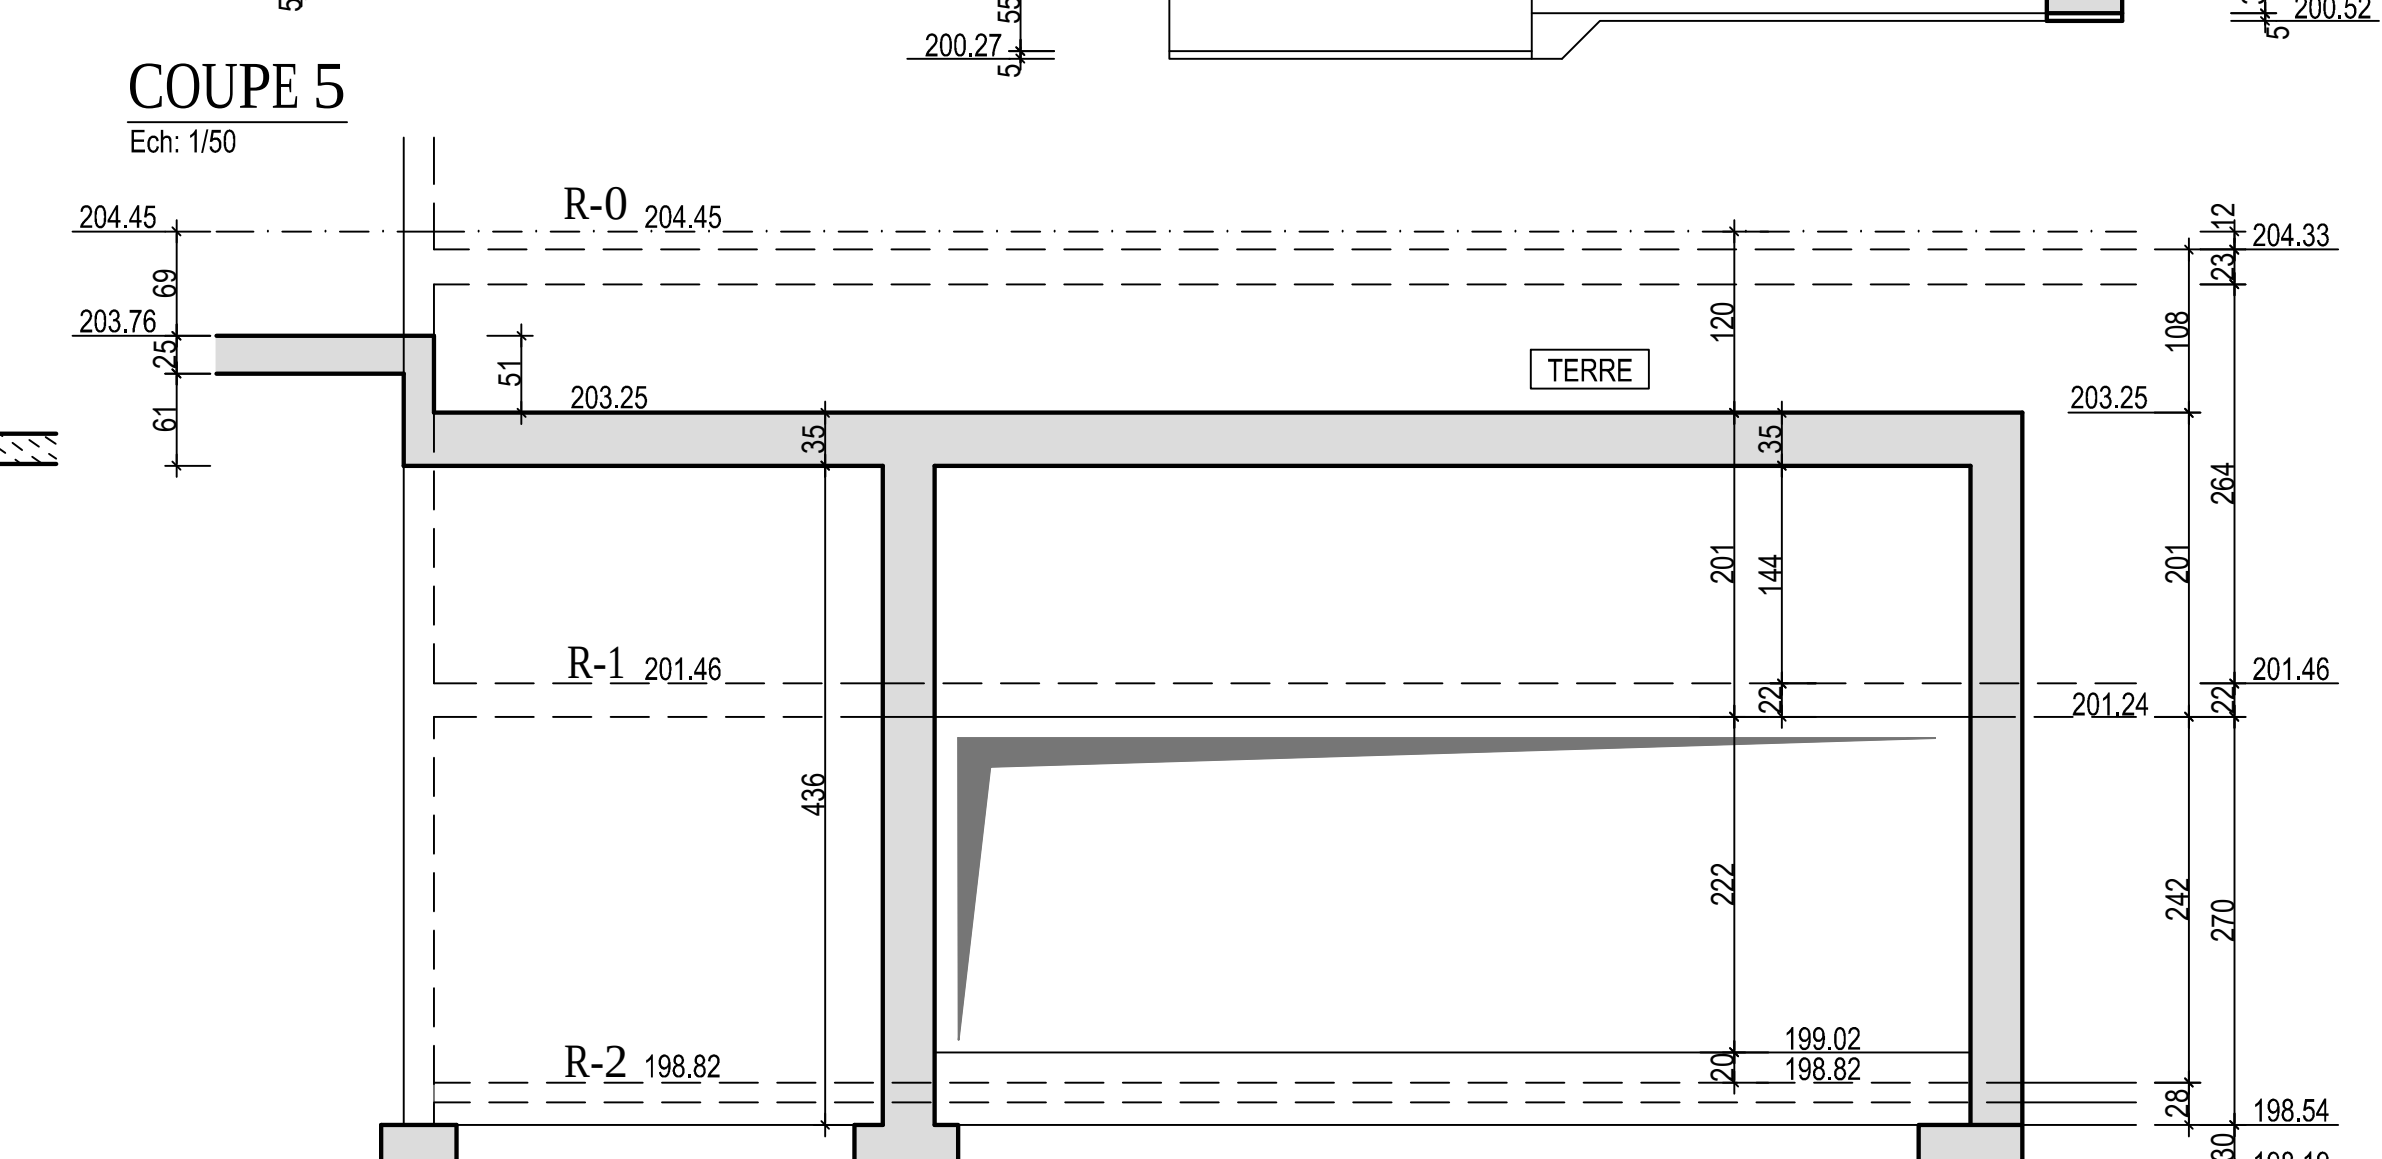
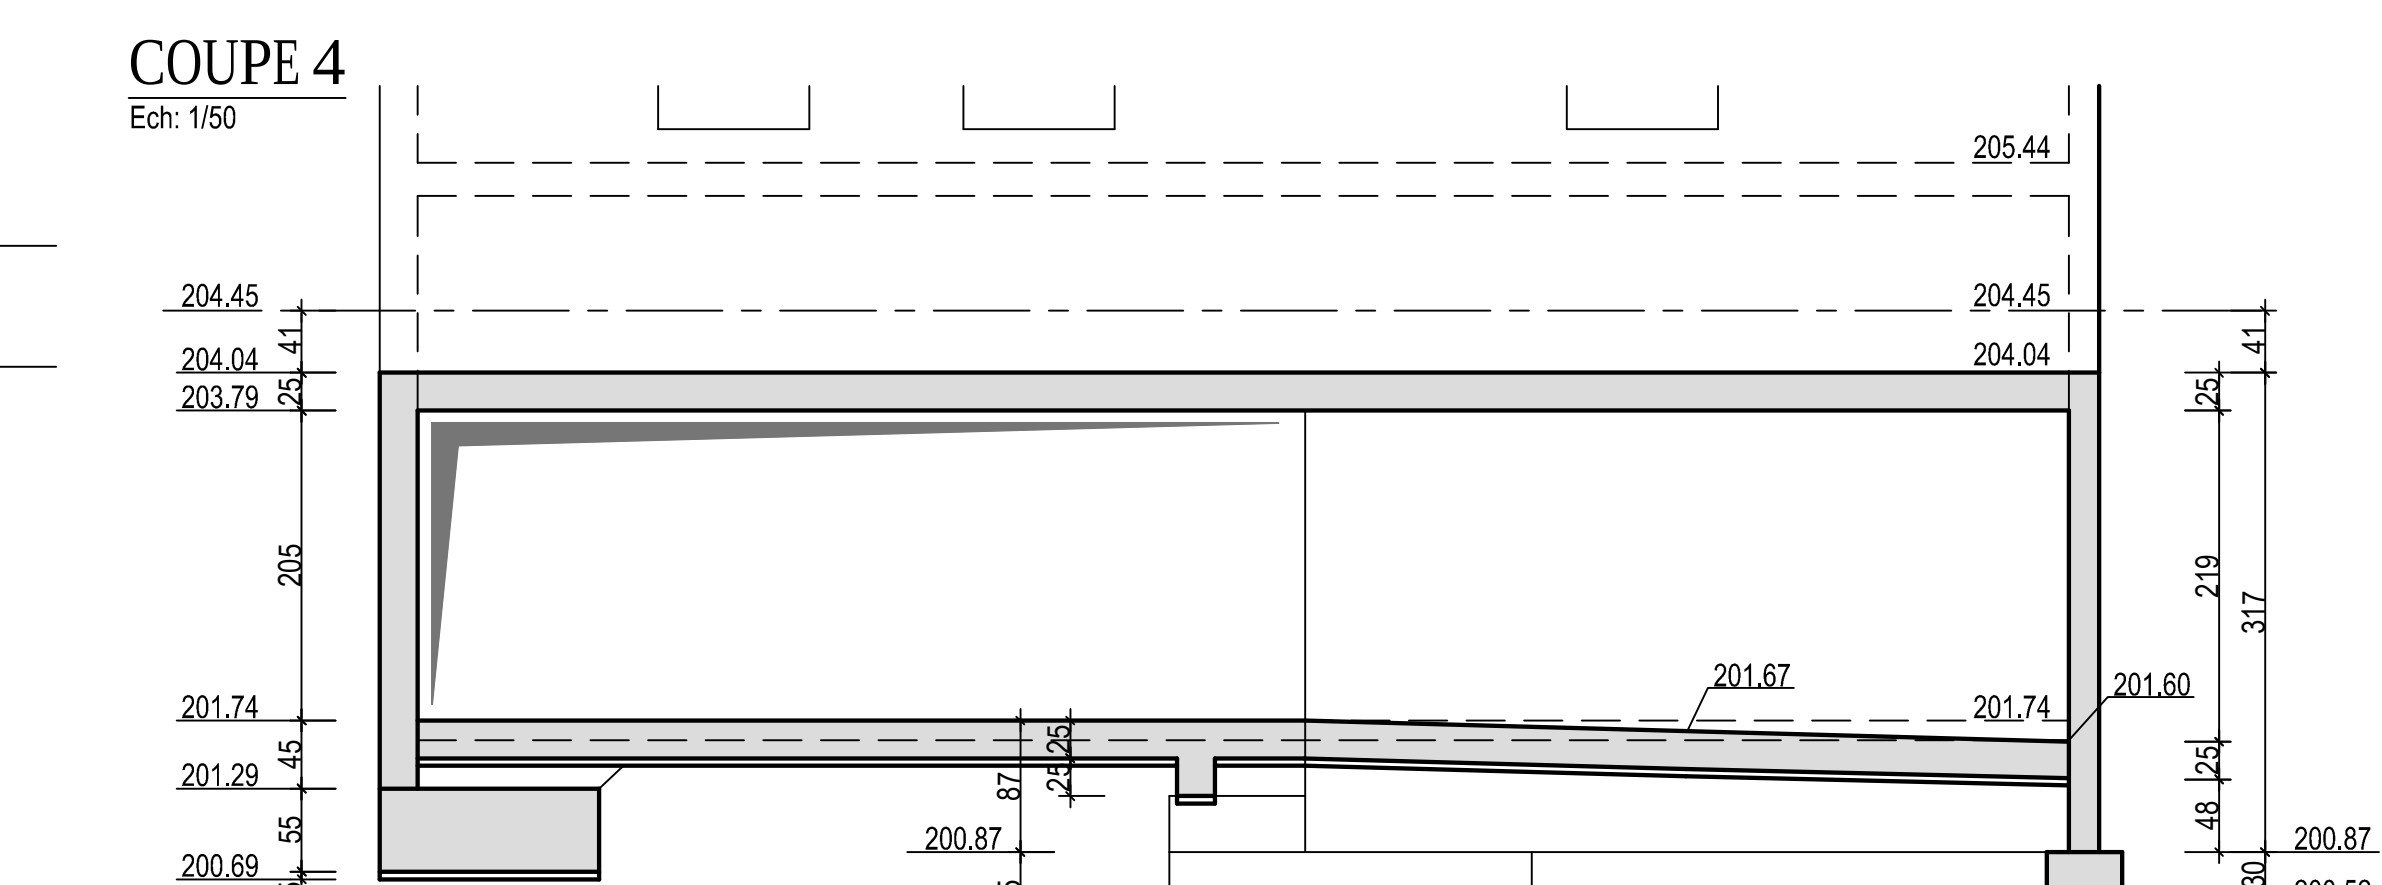
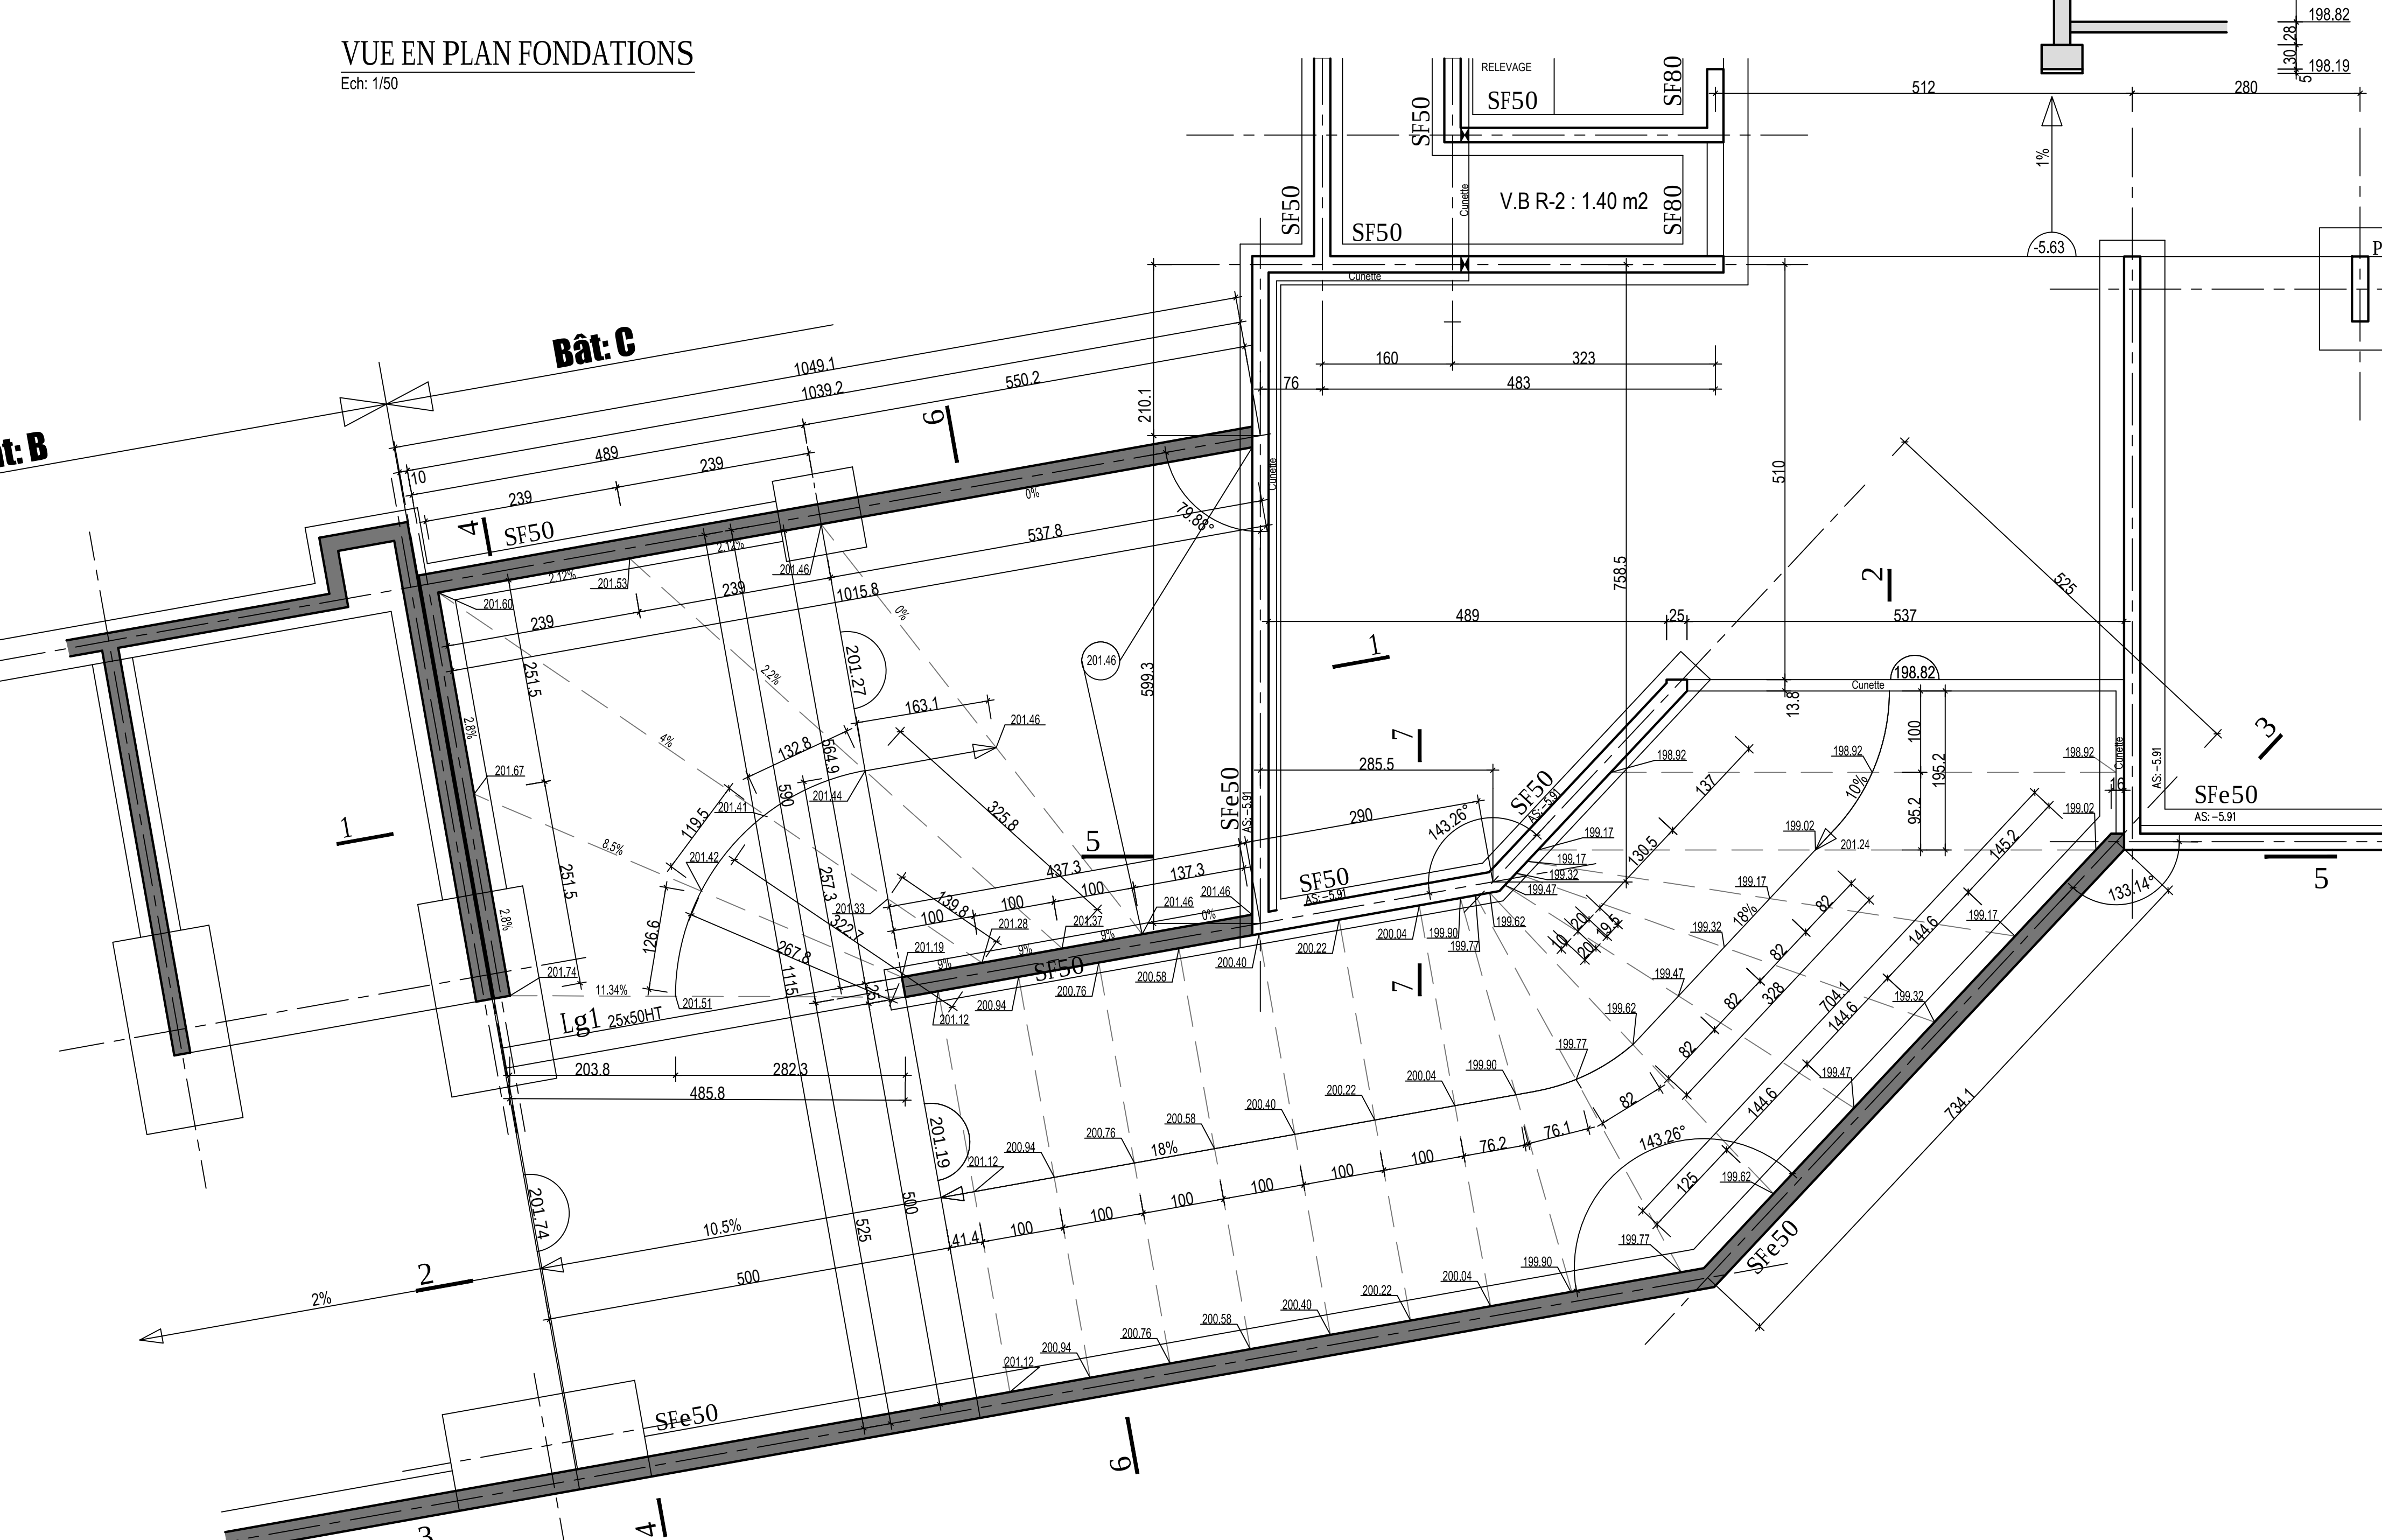
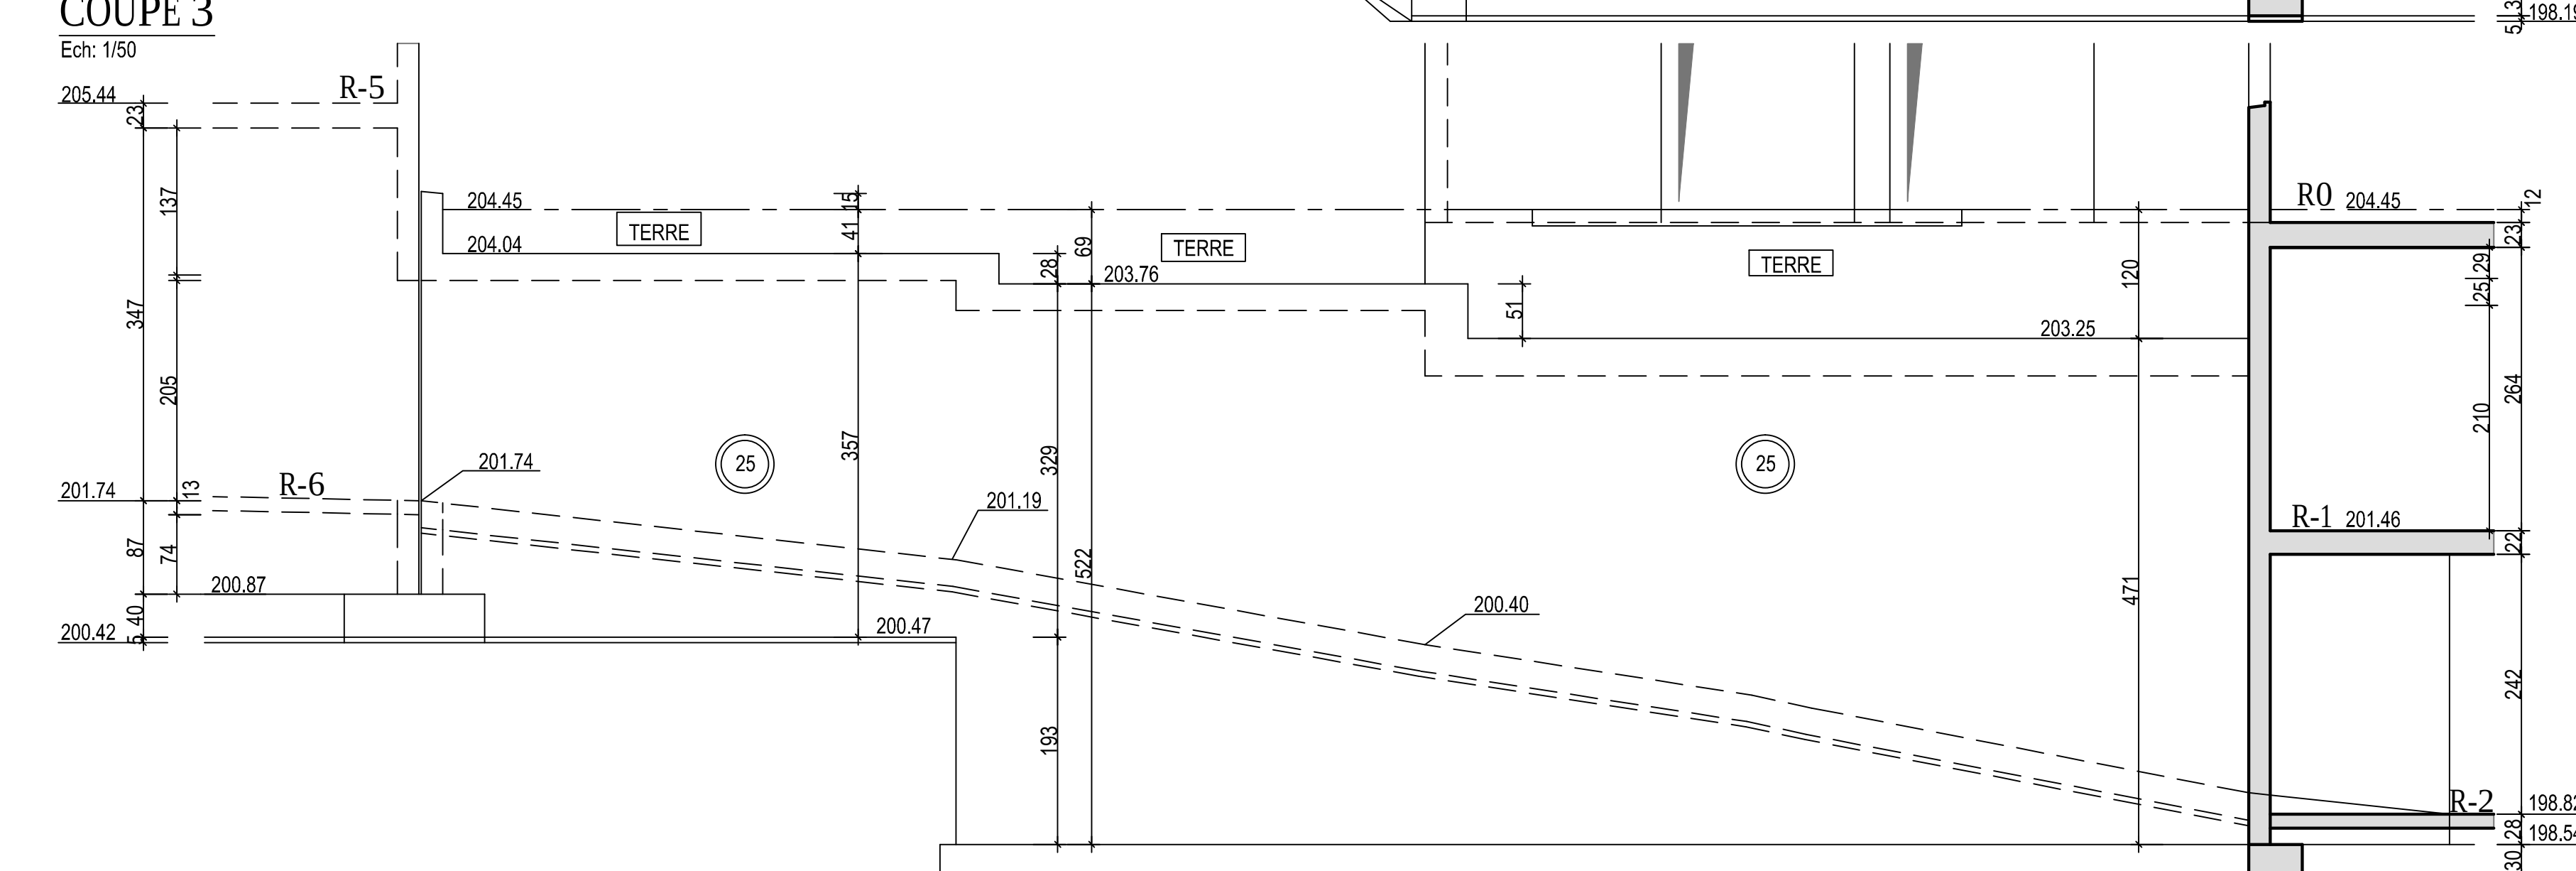
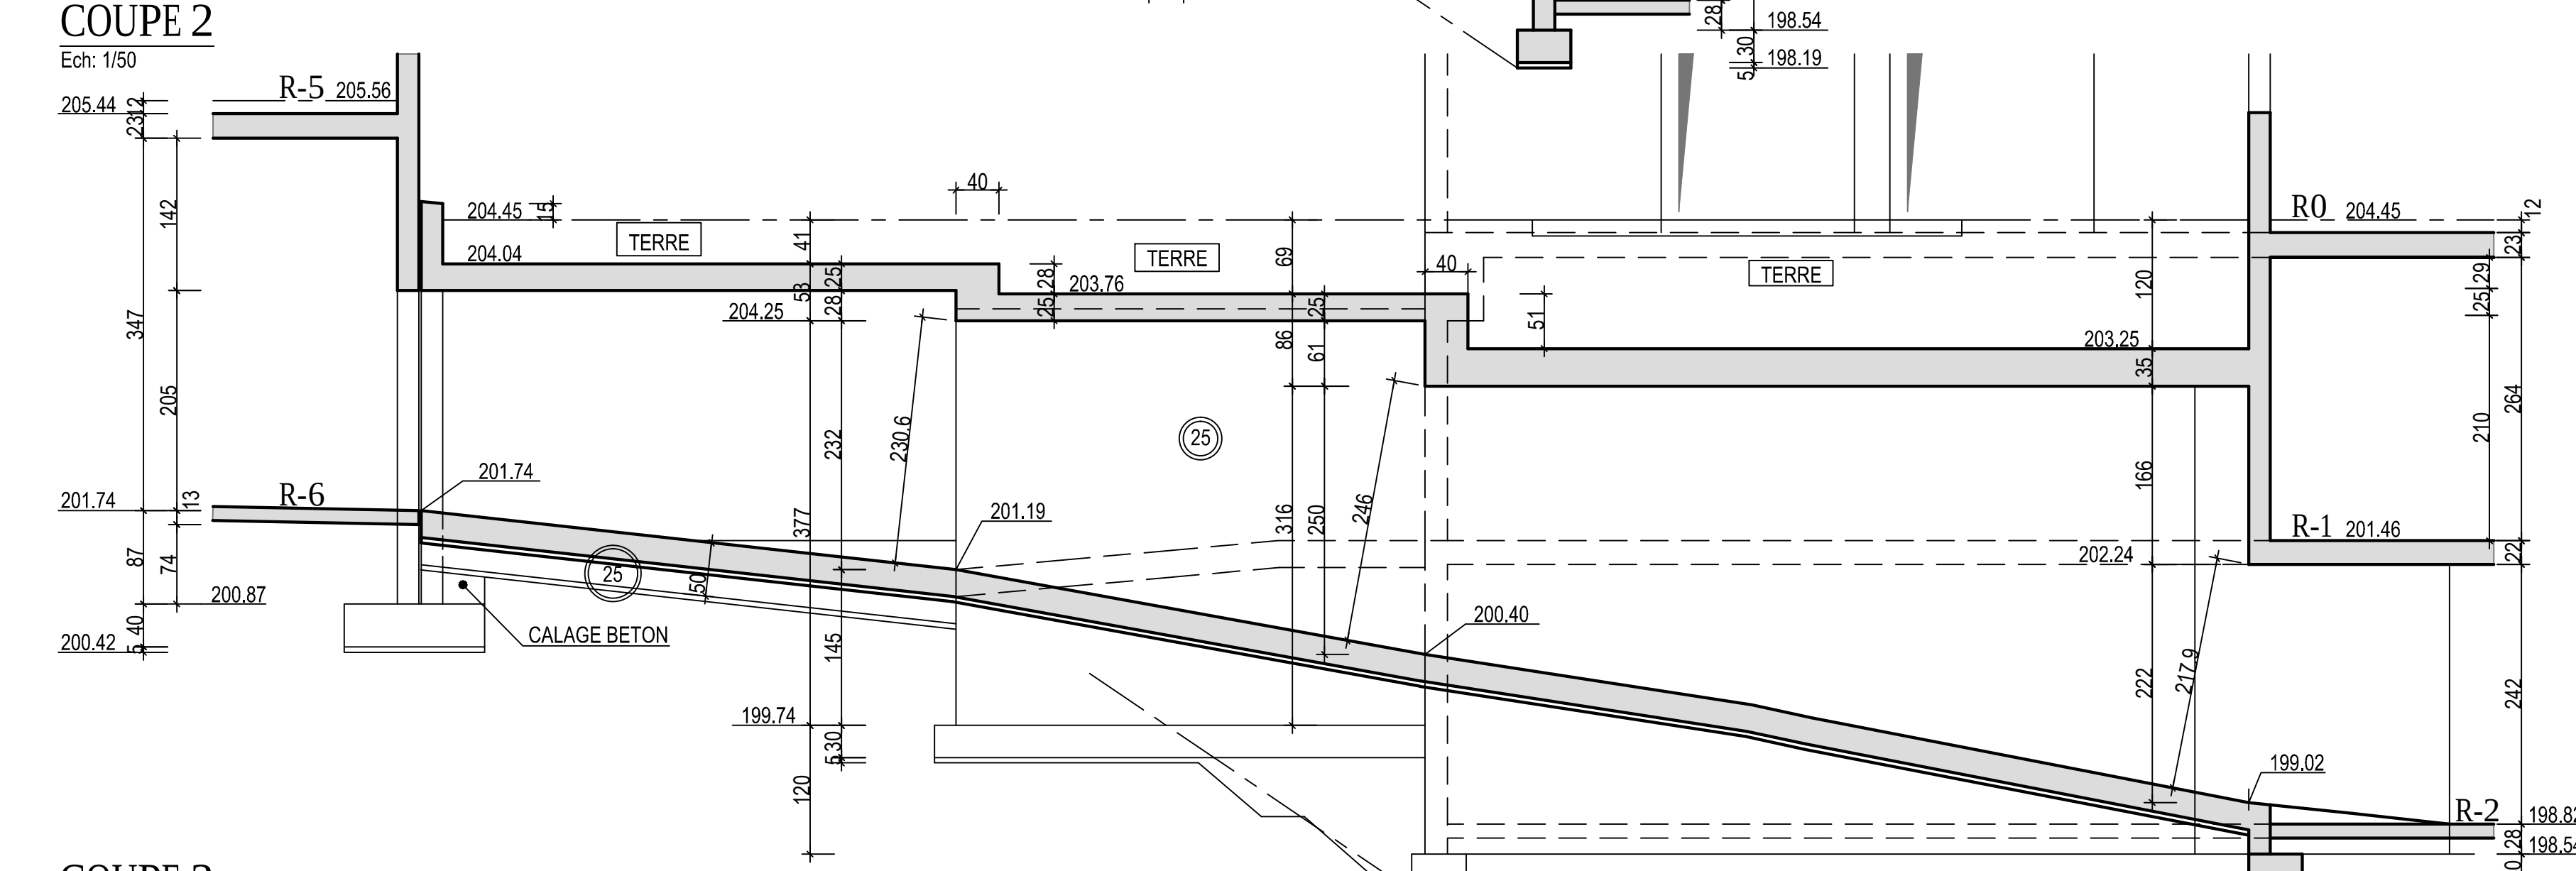
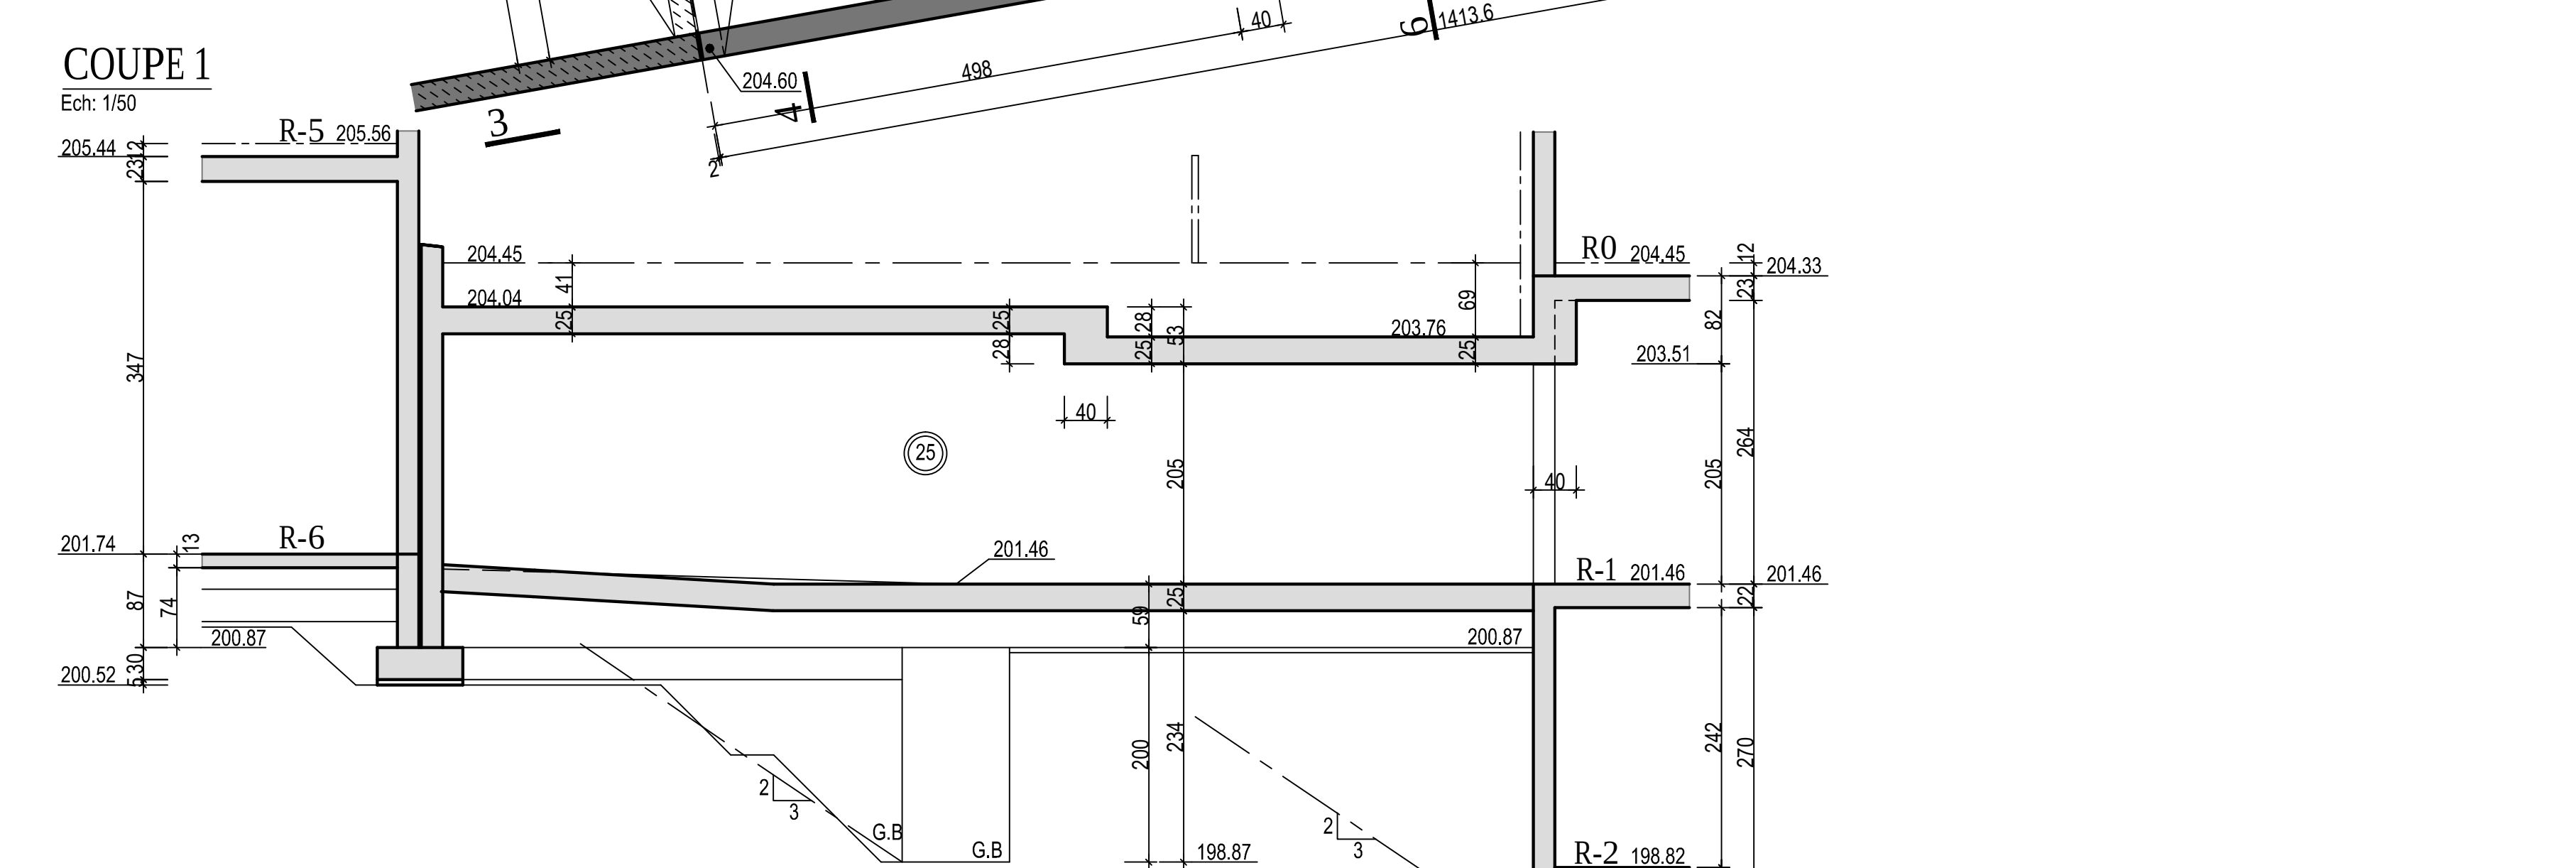
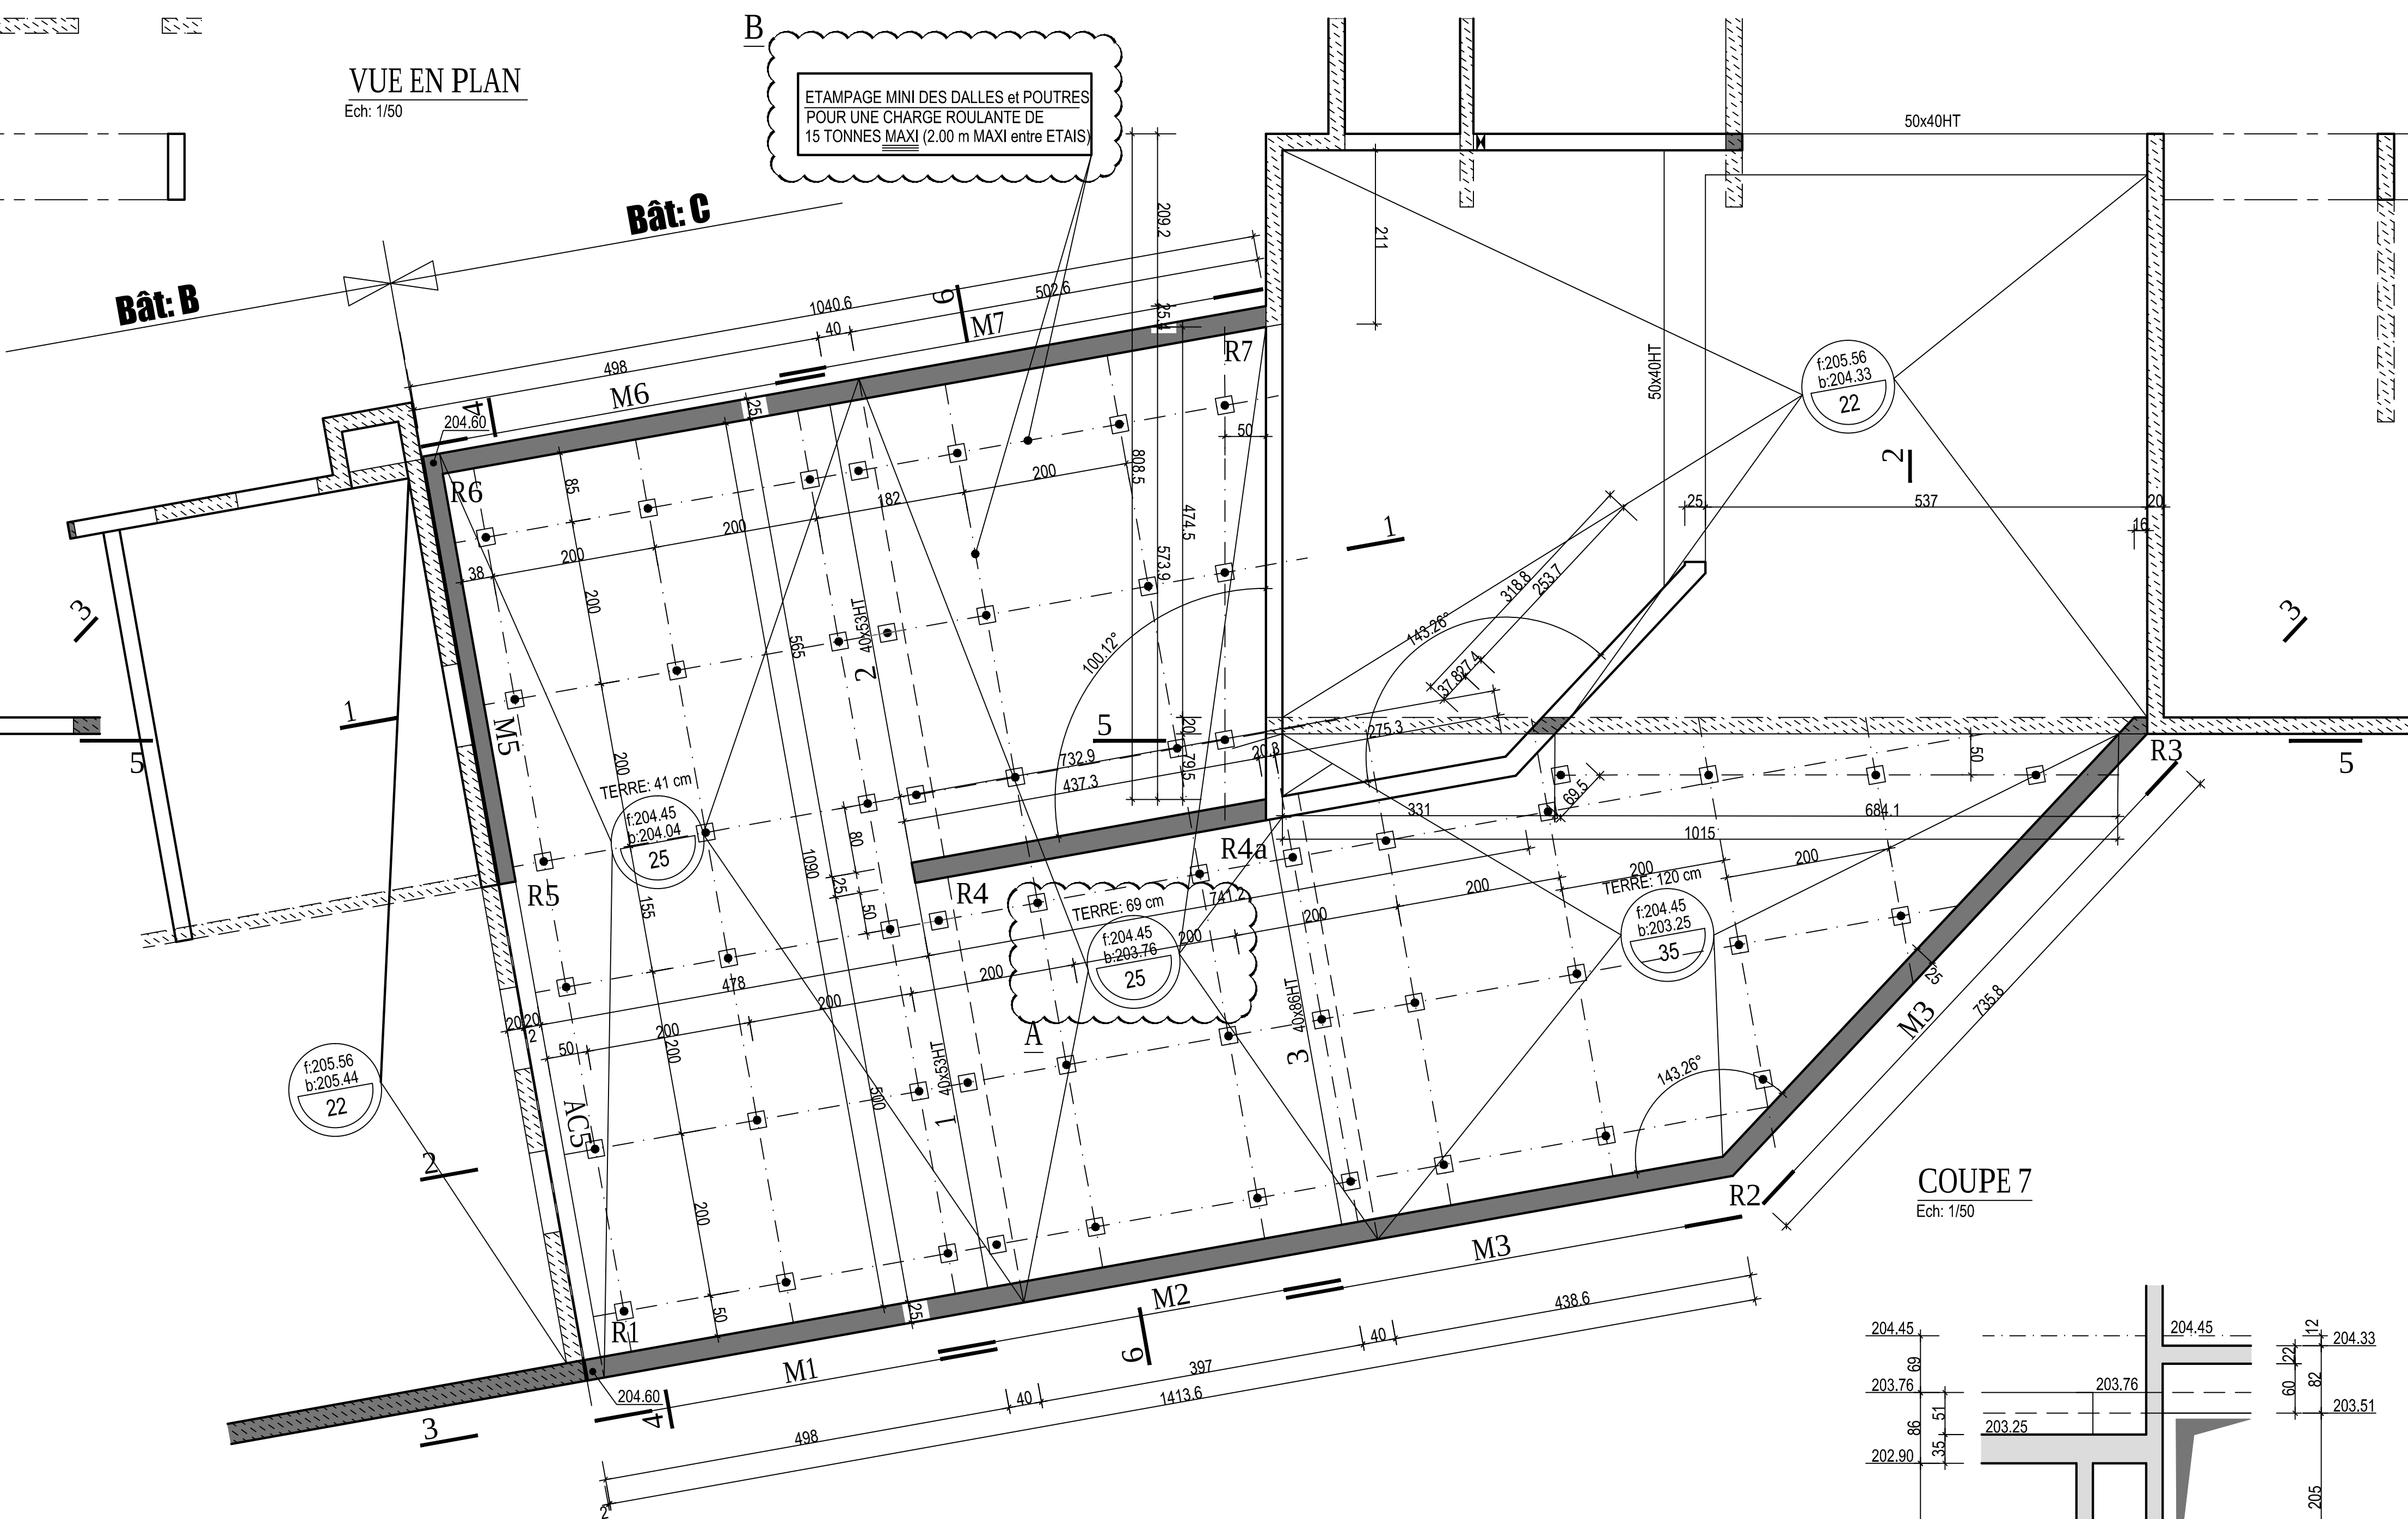


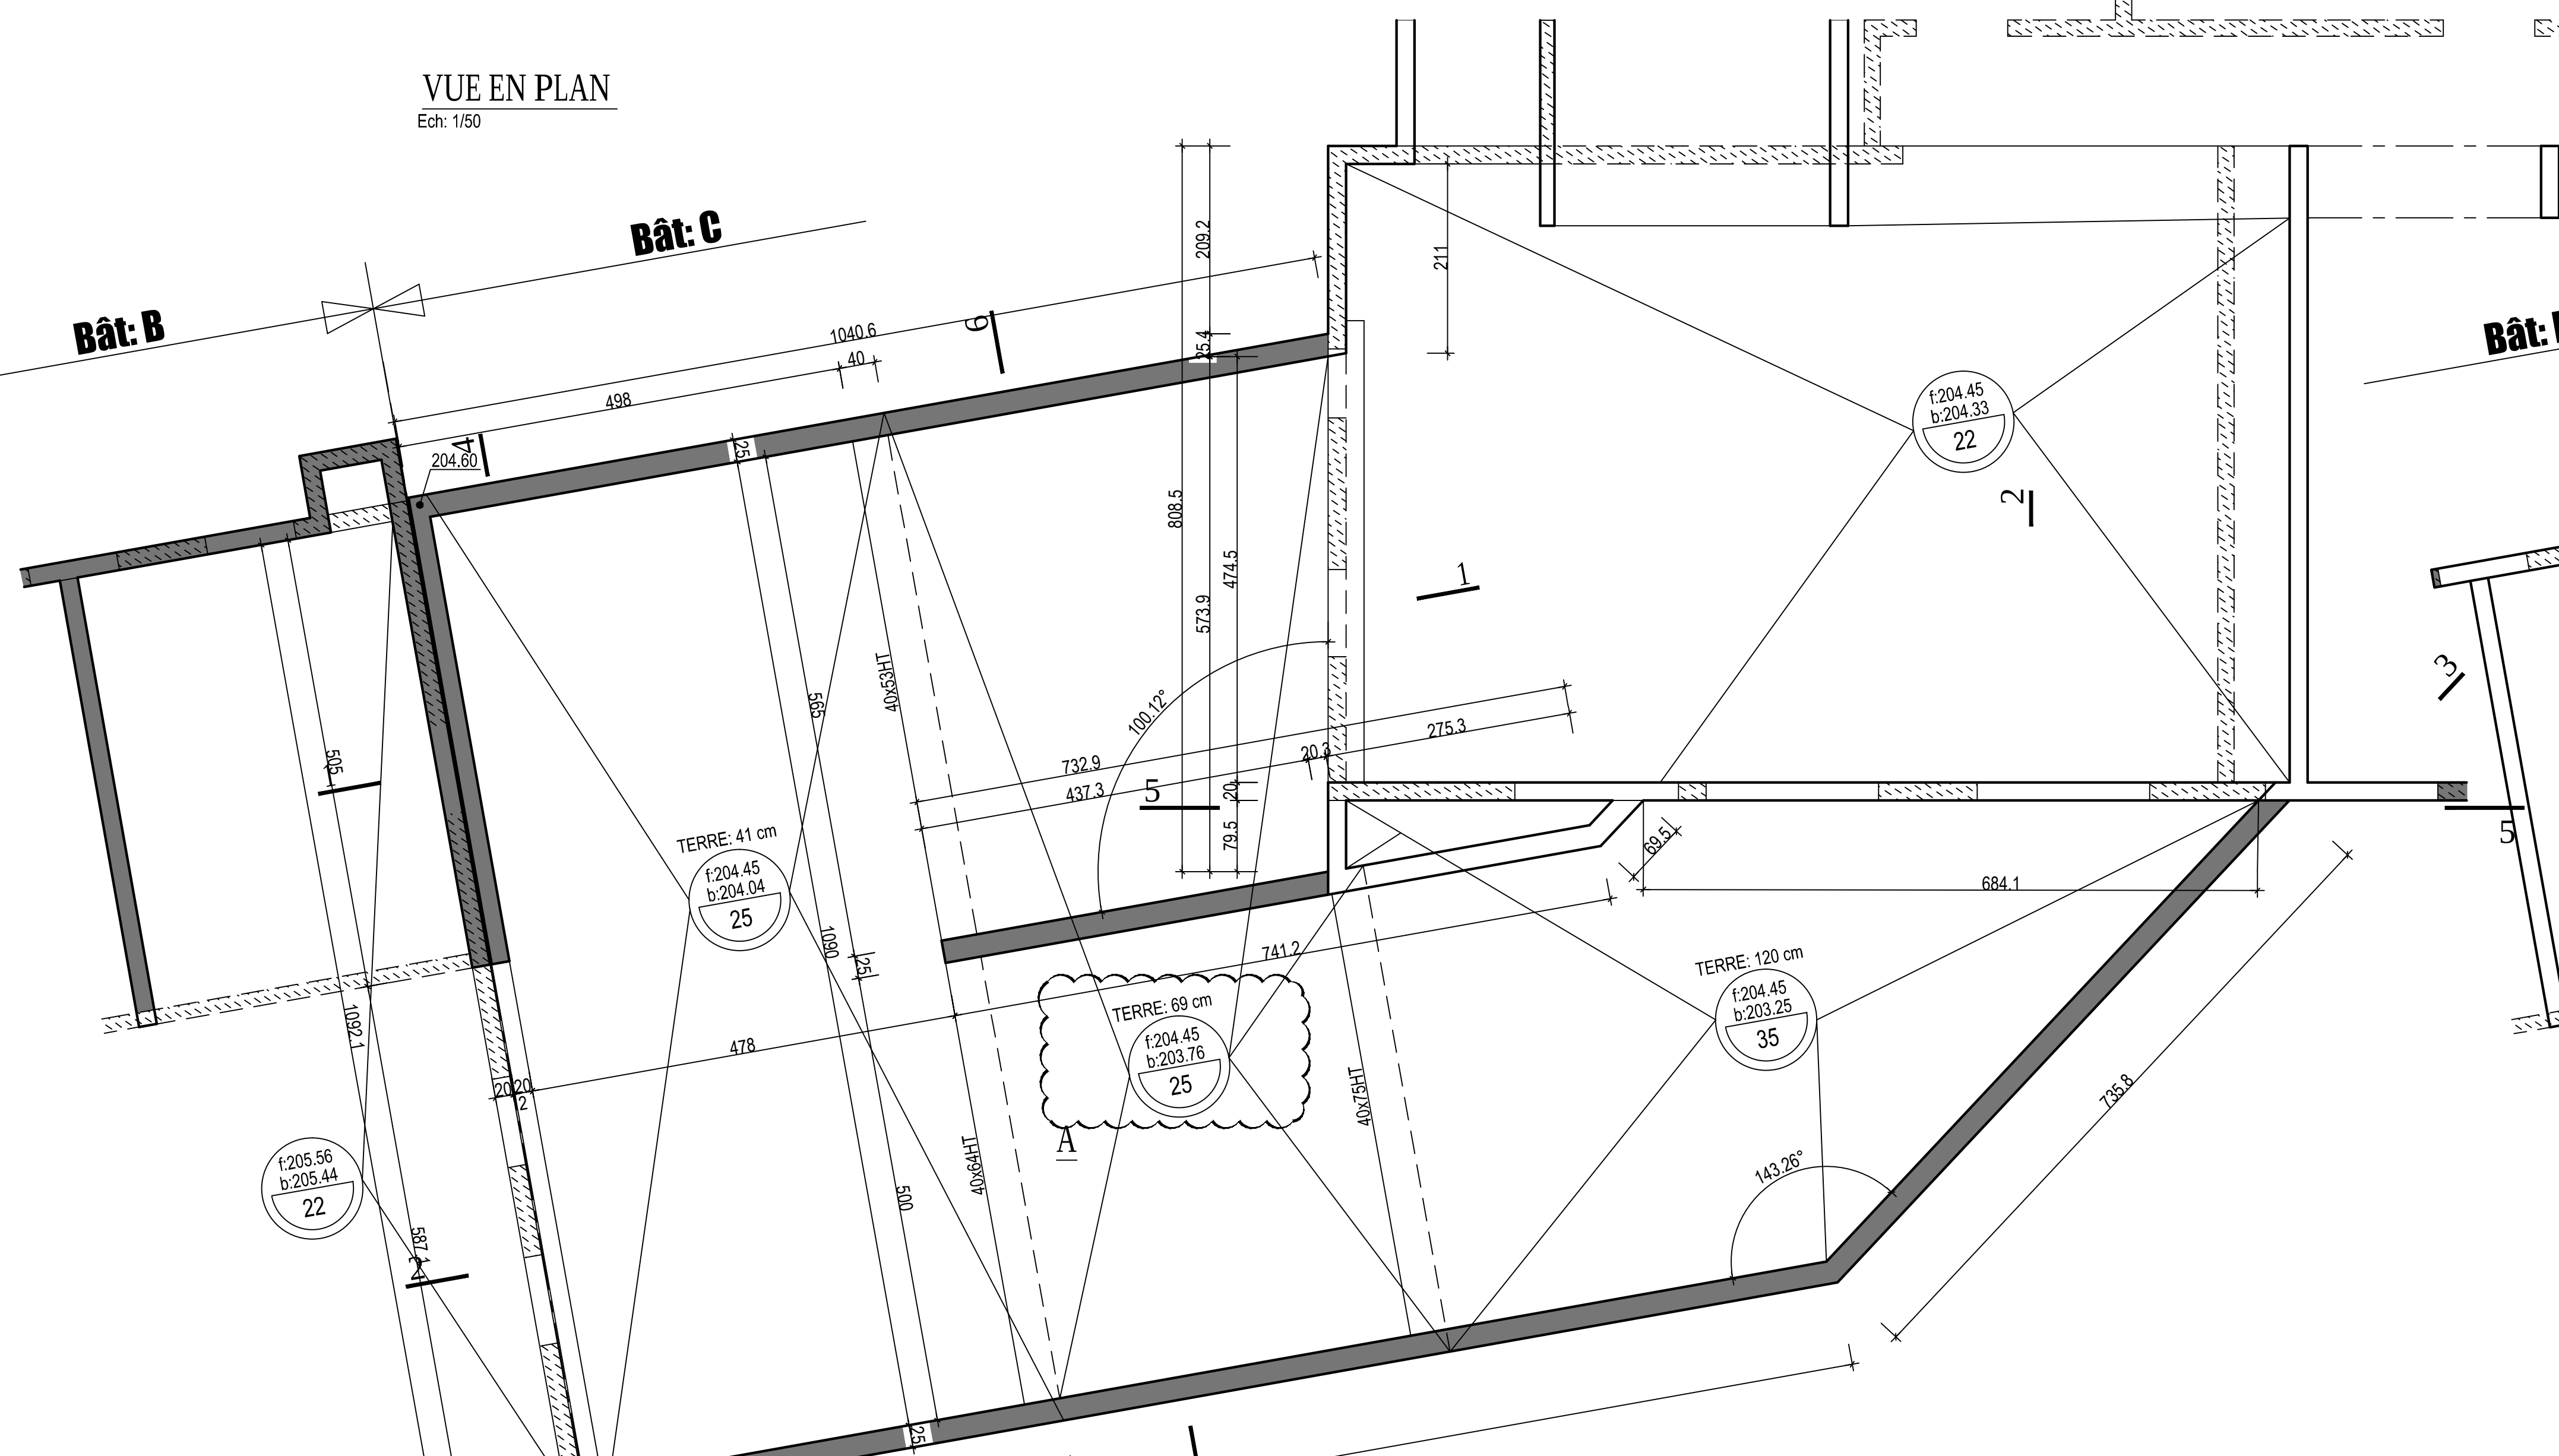

±0.00 = 204.45 = NIVEAU FINI du REZ de CHAUSSEE Bât: C

NOHAO

Chemin de Fontanière-69350 La Mulatière

Création de logements

ARCHITECTES: Atelier DTS

BET STRUCTURE: BET MATTE

BET FLUIDES: PRELEM

ECONOMISTE: EXECO

BUREAU DE CONTRÔLE: VERITAS

M.O. Délégue: M.O.E.

M.O.E.: PSO ingénierie

SUD EST COORDINATION

Fontanel-gbc

Bât: B et C

RAMPE entre B et C du -6 au -2,-1

Coffrage

INDICE

INDICE	DATE	MODIFICATIONS
A	12/02/2016	MODIFIE NIVEAU DALLE SUIVANT A AJOUTE REPERAGE
B	18/02/2016	AJOUTE CHARGE ROULANTE

MATTÉ

BUREAU D'ETUDES

STRUCTURES ET FLUIDES

119 BOULEVARD STALINISME 69100 VILLEURBANNE

Tel: 04 72 44 12 87 Fax: 04 72 44 26 99

E-mail: bet@matté.fr

DOE

Asiers HA (T) Fe500

Asiers Dour (D) Fe235

Asiers TS Fe500

Biton C28 = 28MPa

Enrobage = 3 cm

PLAN N° C06 B

DATE: 07-07-2015

Desiné par: J.BONDETTI

Corrigé par: P.LIN

Ech:

Affaire N° S.13.12.119