

NOAHO

Chemin de Fontanière - 69350 La Mulatière

Création de logements

Les entreprises réalisant les travaux devront tenir compte des derniers plans architecte lors de la réalisation des travaux
Les plans du be MATTE ne doivent servir qu'au corps d'état concerné et doivent être des plans d'exécution.

ARCHITECTE(S):	Atelier D'IS	MO DELEGUE:	
BET STRUCTURE:	MATTE SAS	MOE:	PSO Ingénierie
BET FLUIDES:	PRELEM	CSPS:	SUD EST COORDINATION
ECONOMISTE:	EXECO	OPC:	
BUREAU DE CONTROLE:	Bureau VERITAS	ENTREPRISE(S):	Fontanel-pbc

Bât: C
BA au -3
DALLE BASSE du -3

DOE

Contrainte de sol: bars ELS

Aciers HA (T) FeE500

Aciers Doux (Ø) FeE 235

Aciers TS FeE 500

Béton fc28 >= 25MPa

Enrobage = 3 cm

PLAN N°
C07 A

DATE : 09/05/2015

MATTÉ

BUREAU D'ÉTUDES
STRUCTURES ET FLUIDES

119 BOULEVARD STALINGRAD 69100 VILLEURBANNE

Tél. 04 72 44 02 87 Fax 04 72 44 26 59

E-mail : bet@matte.fr



Dessiné par : J.BO



Contrôlé par : P.LIN



Echelle : 1/50°

Affaire N°

13.12.119

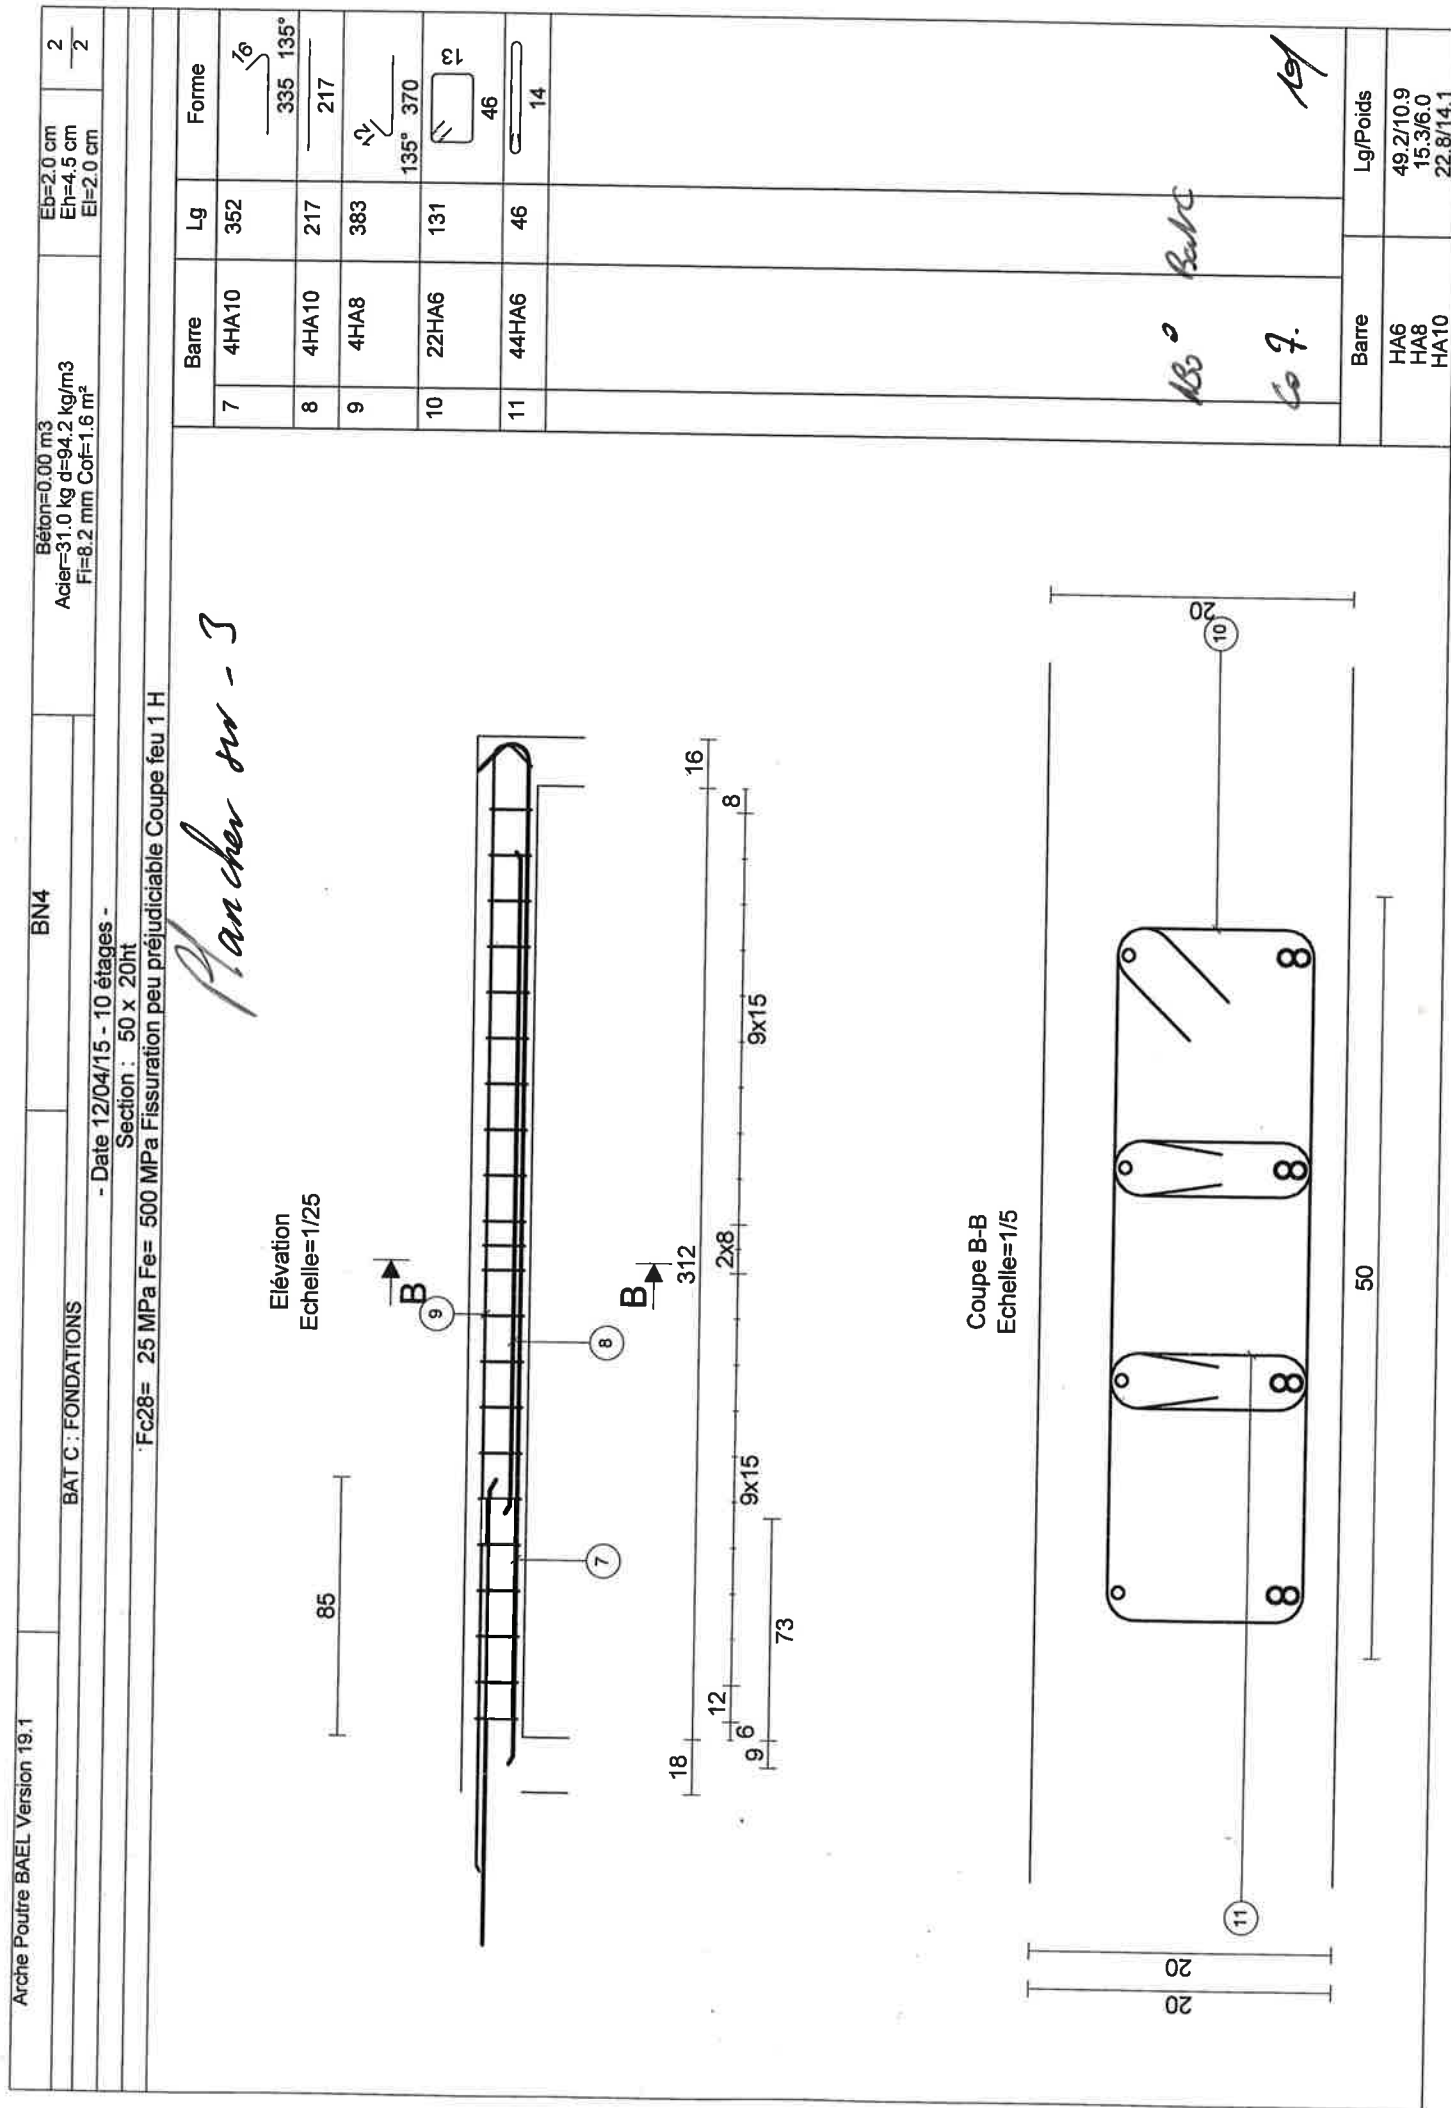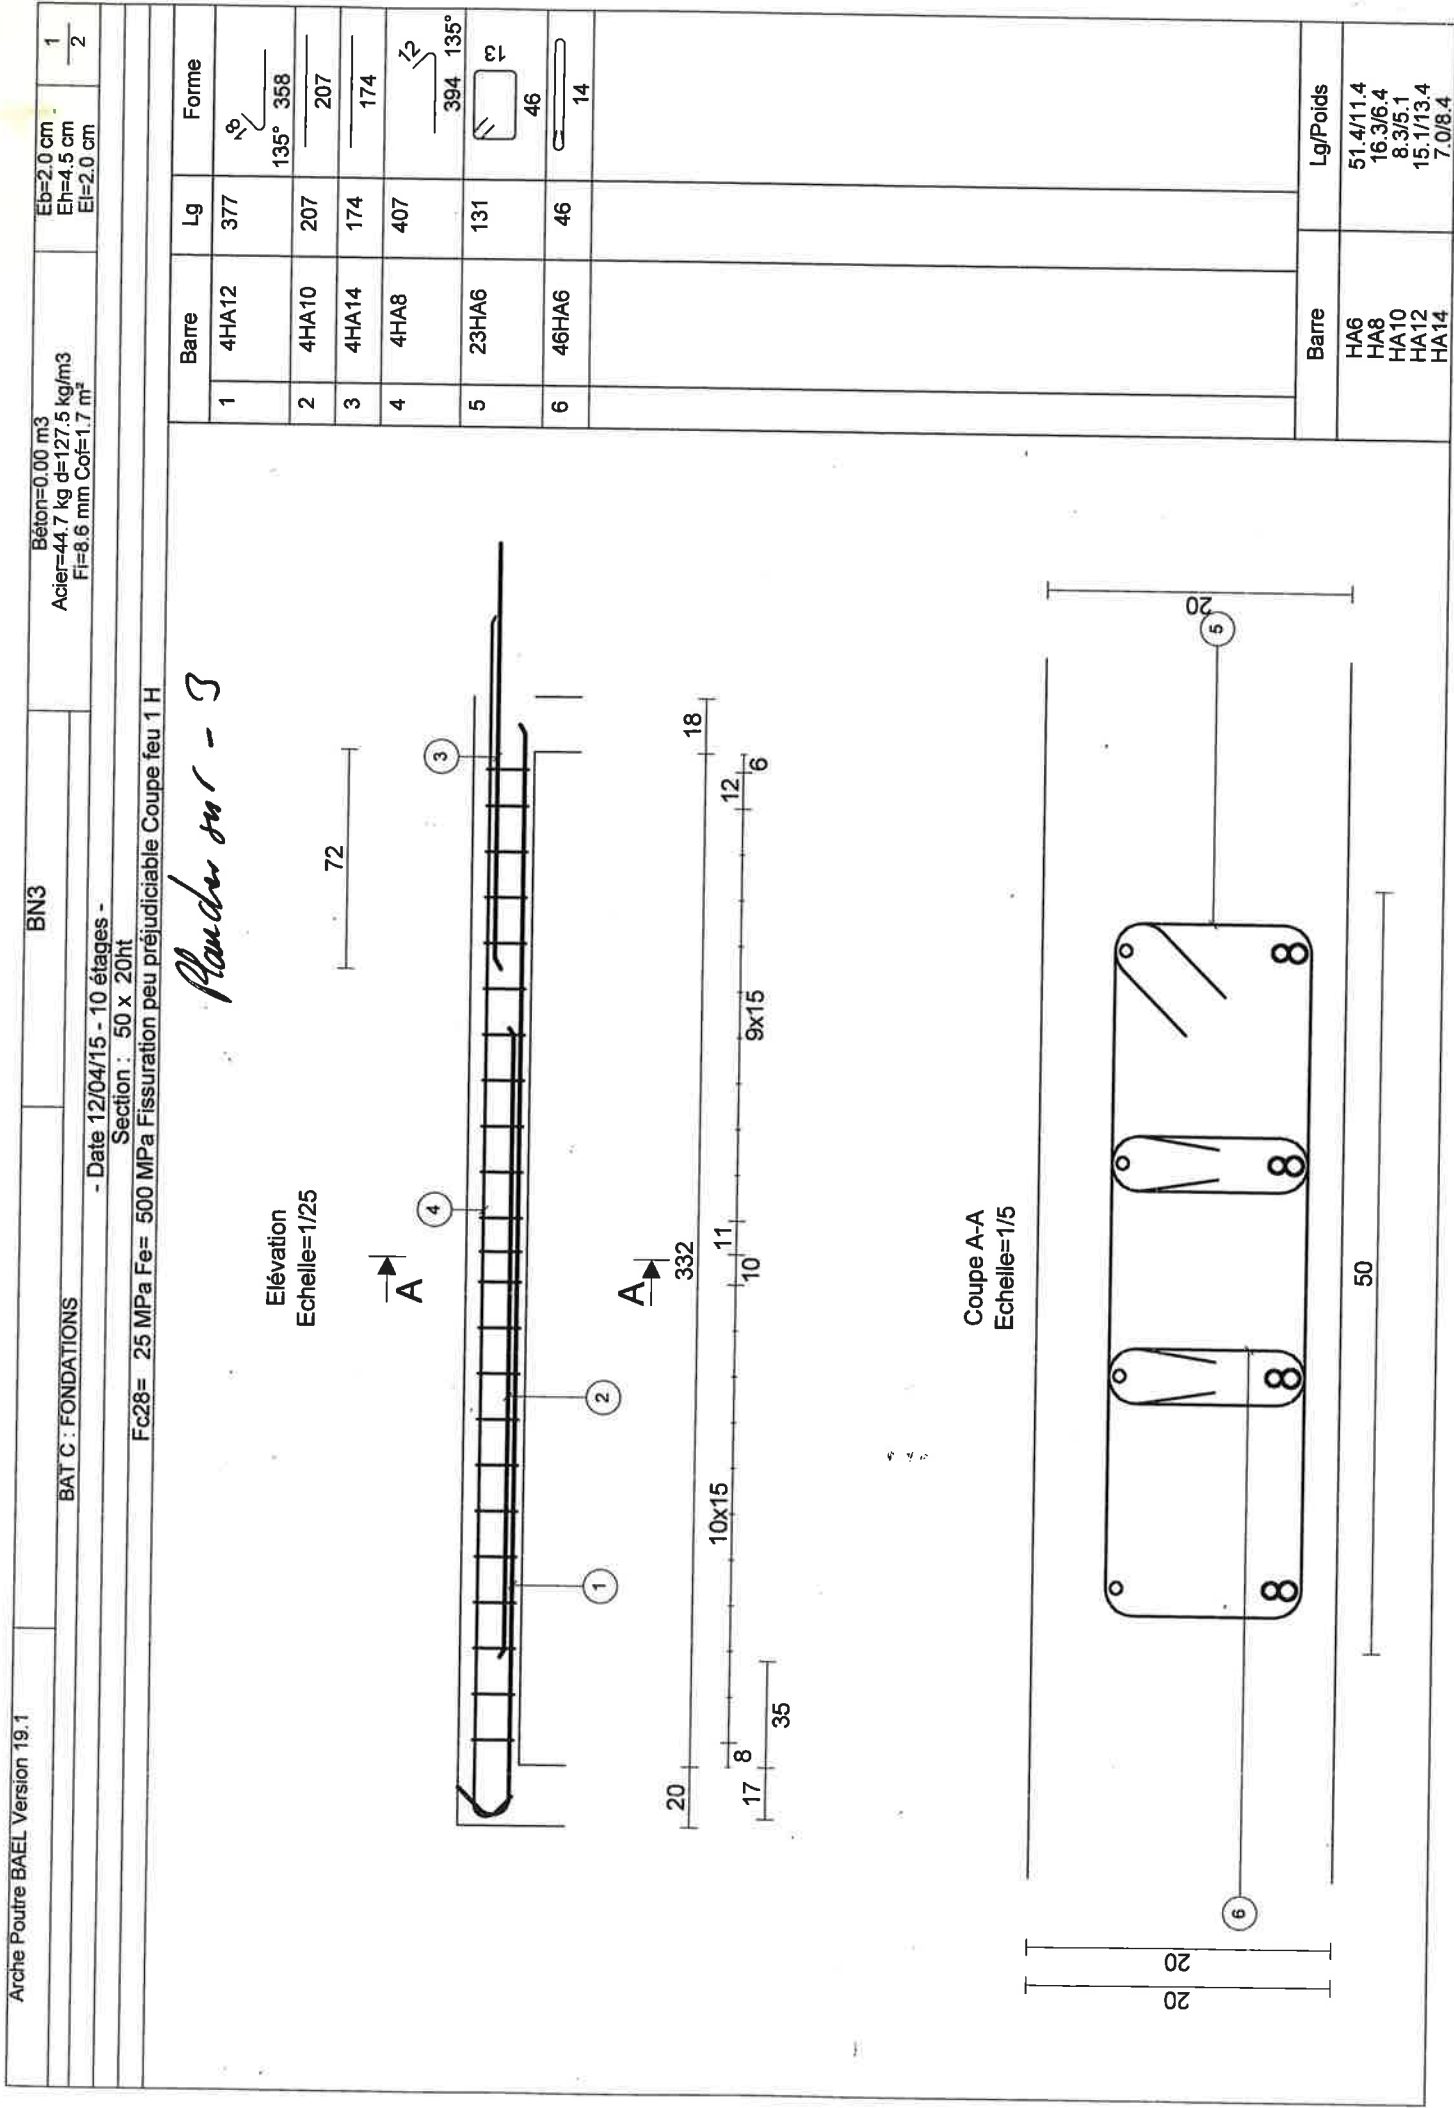

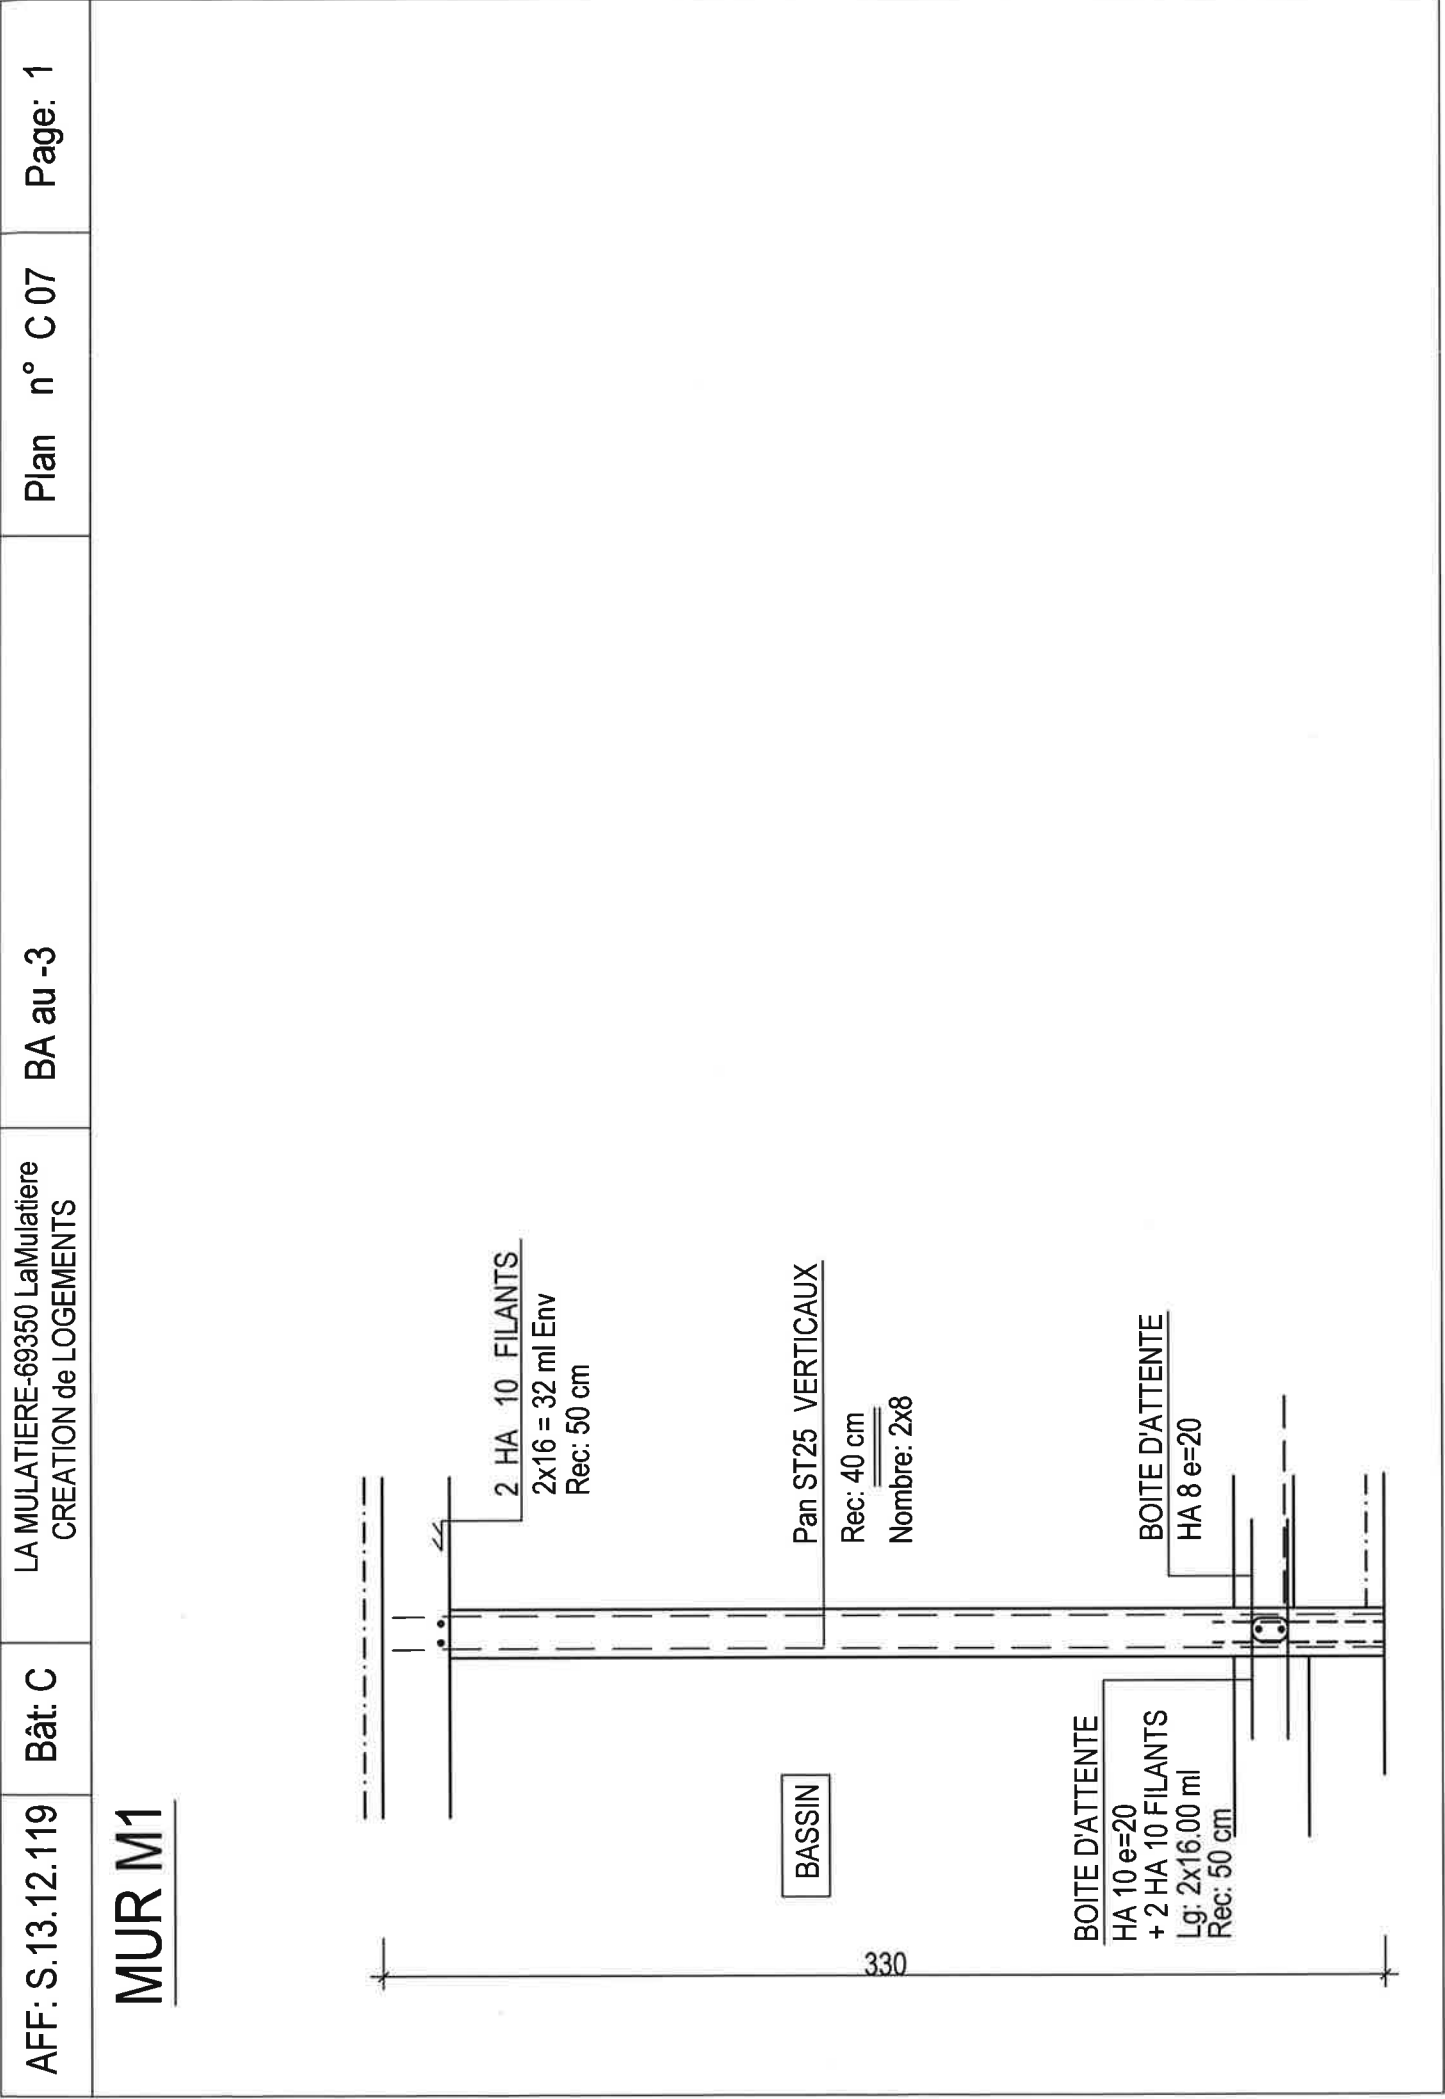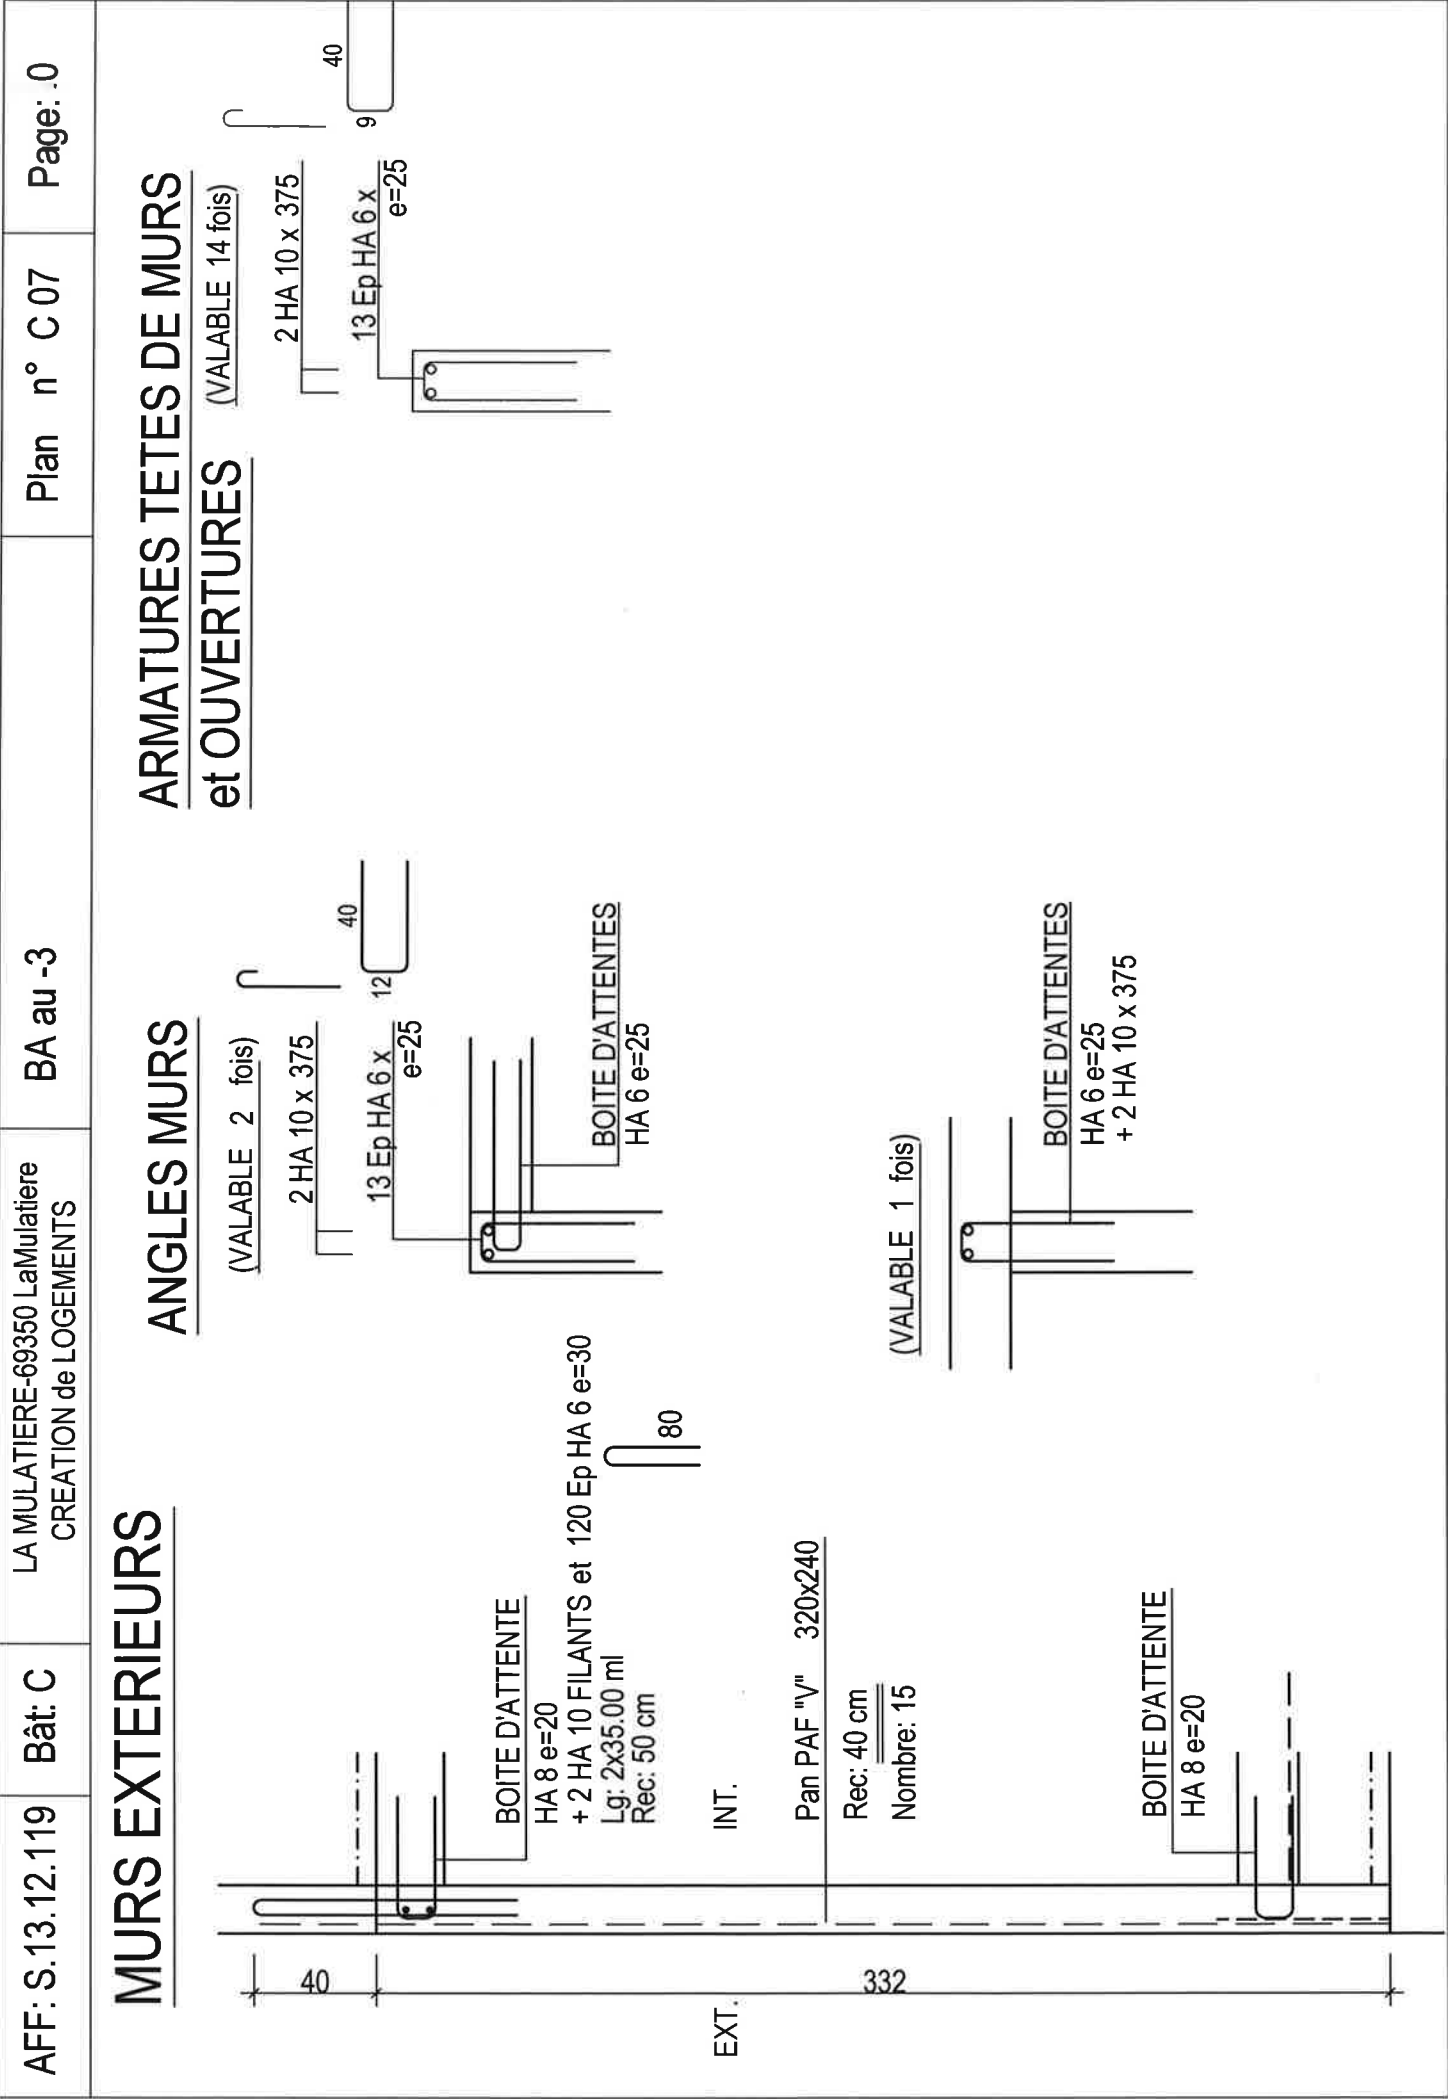


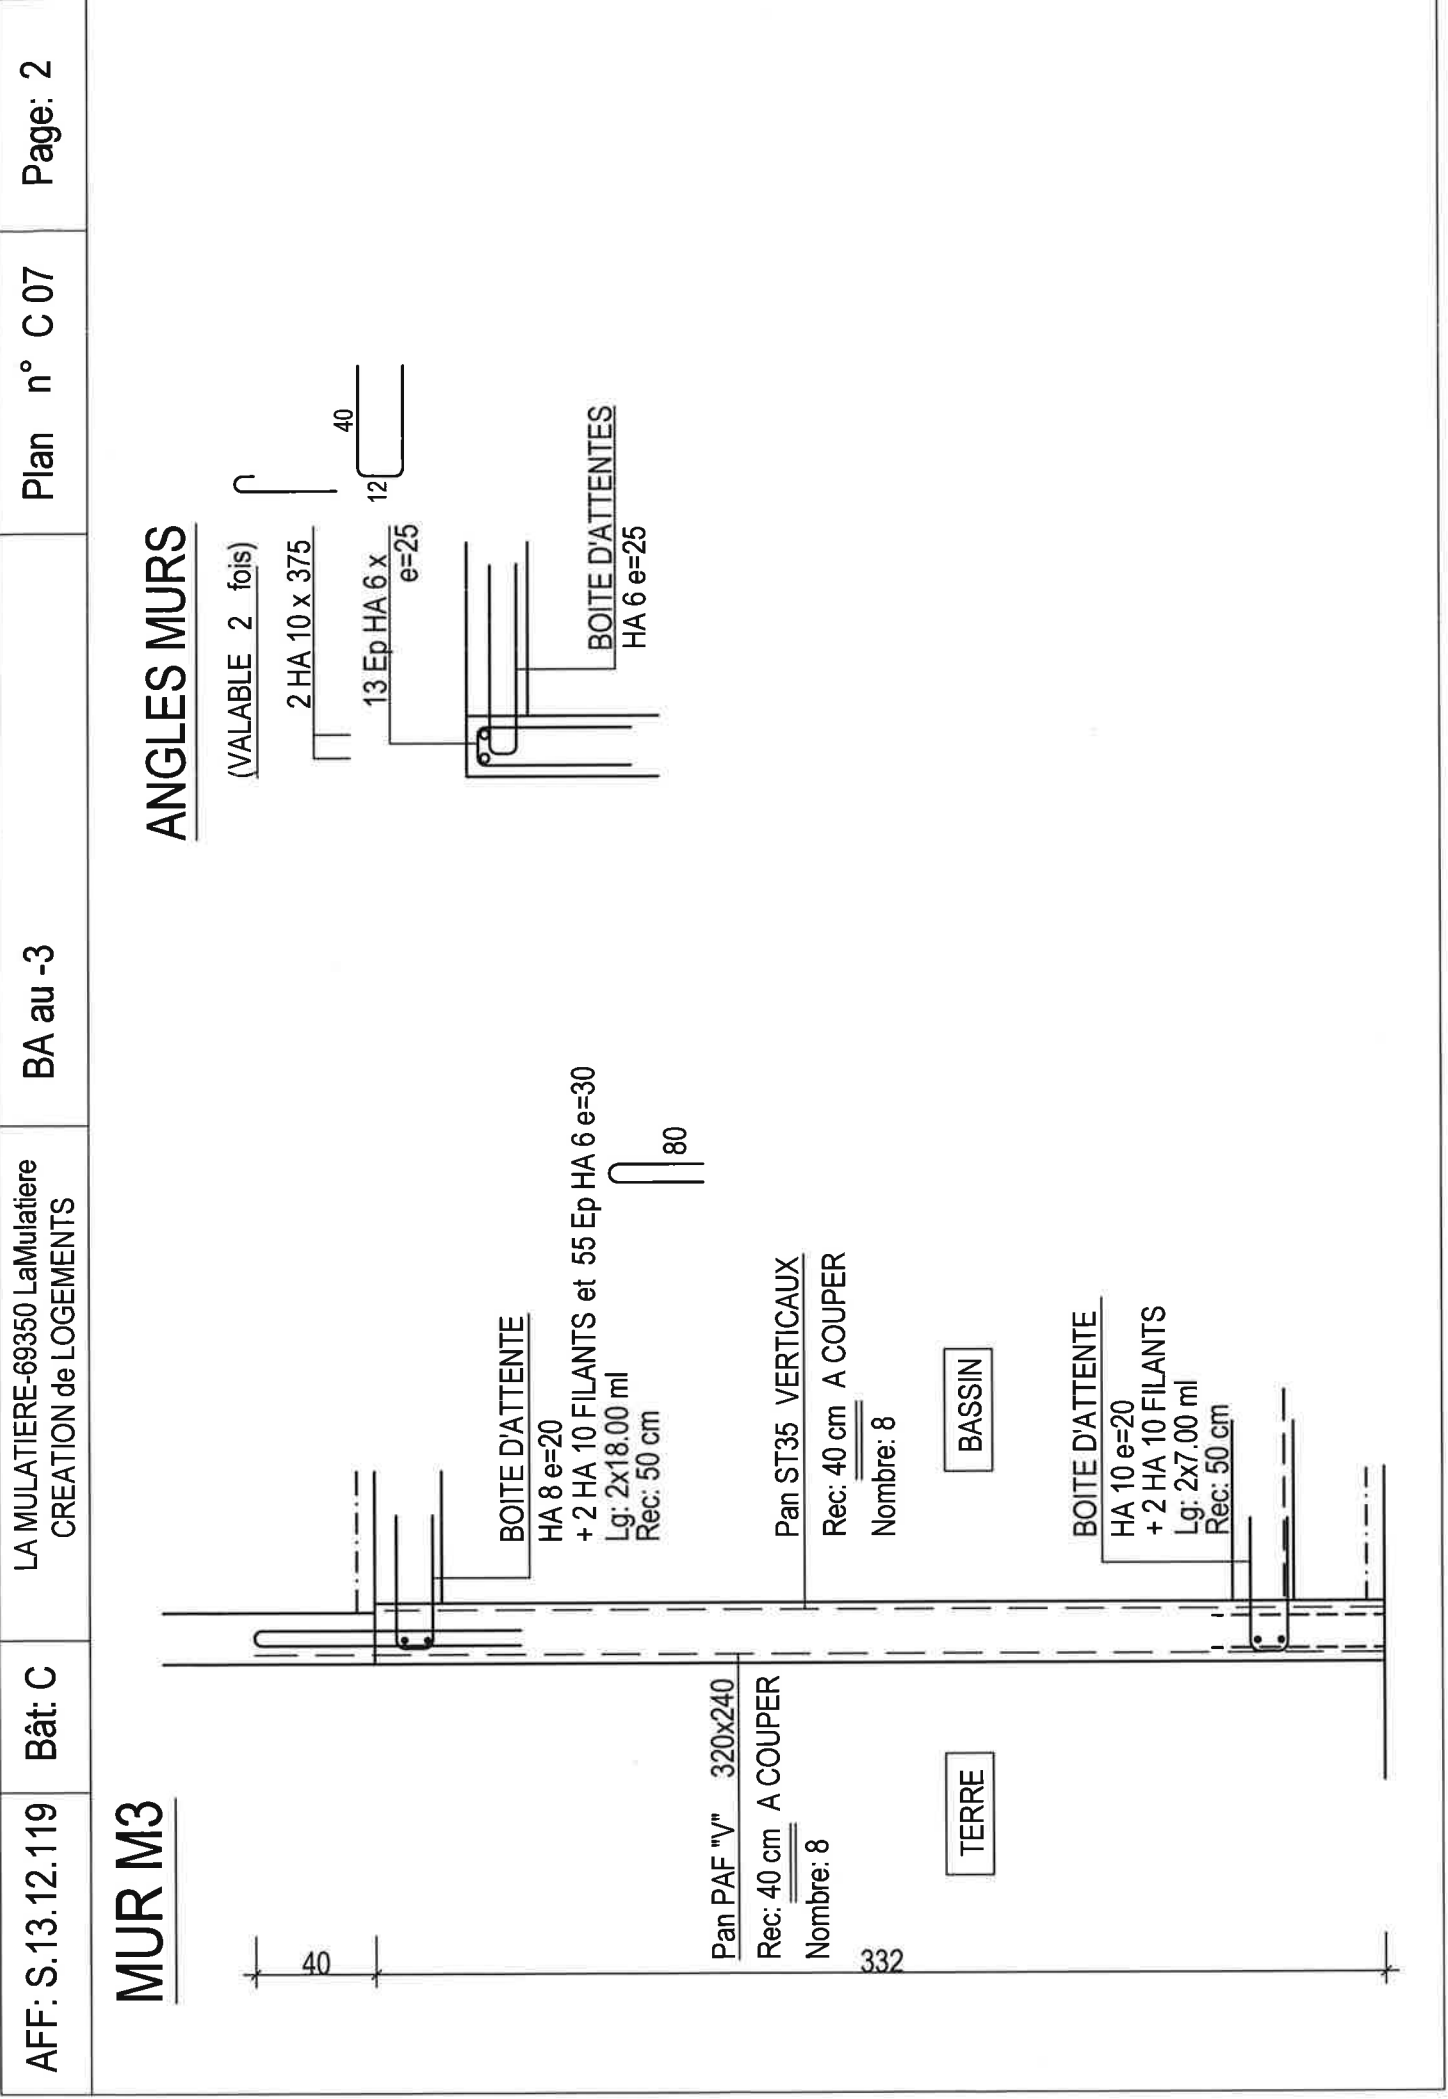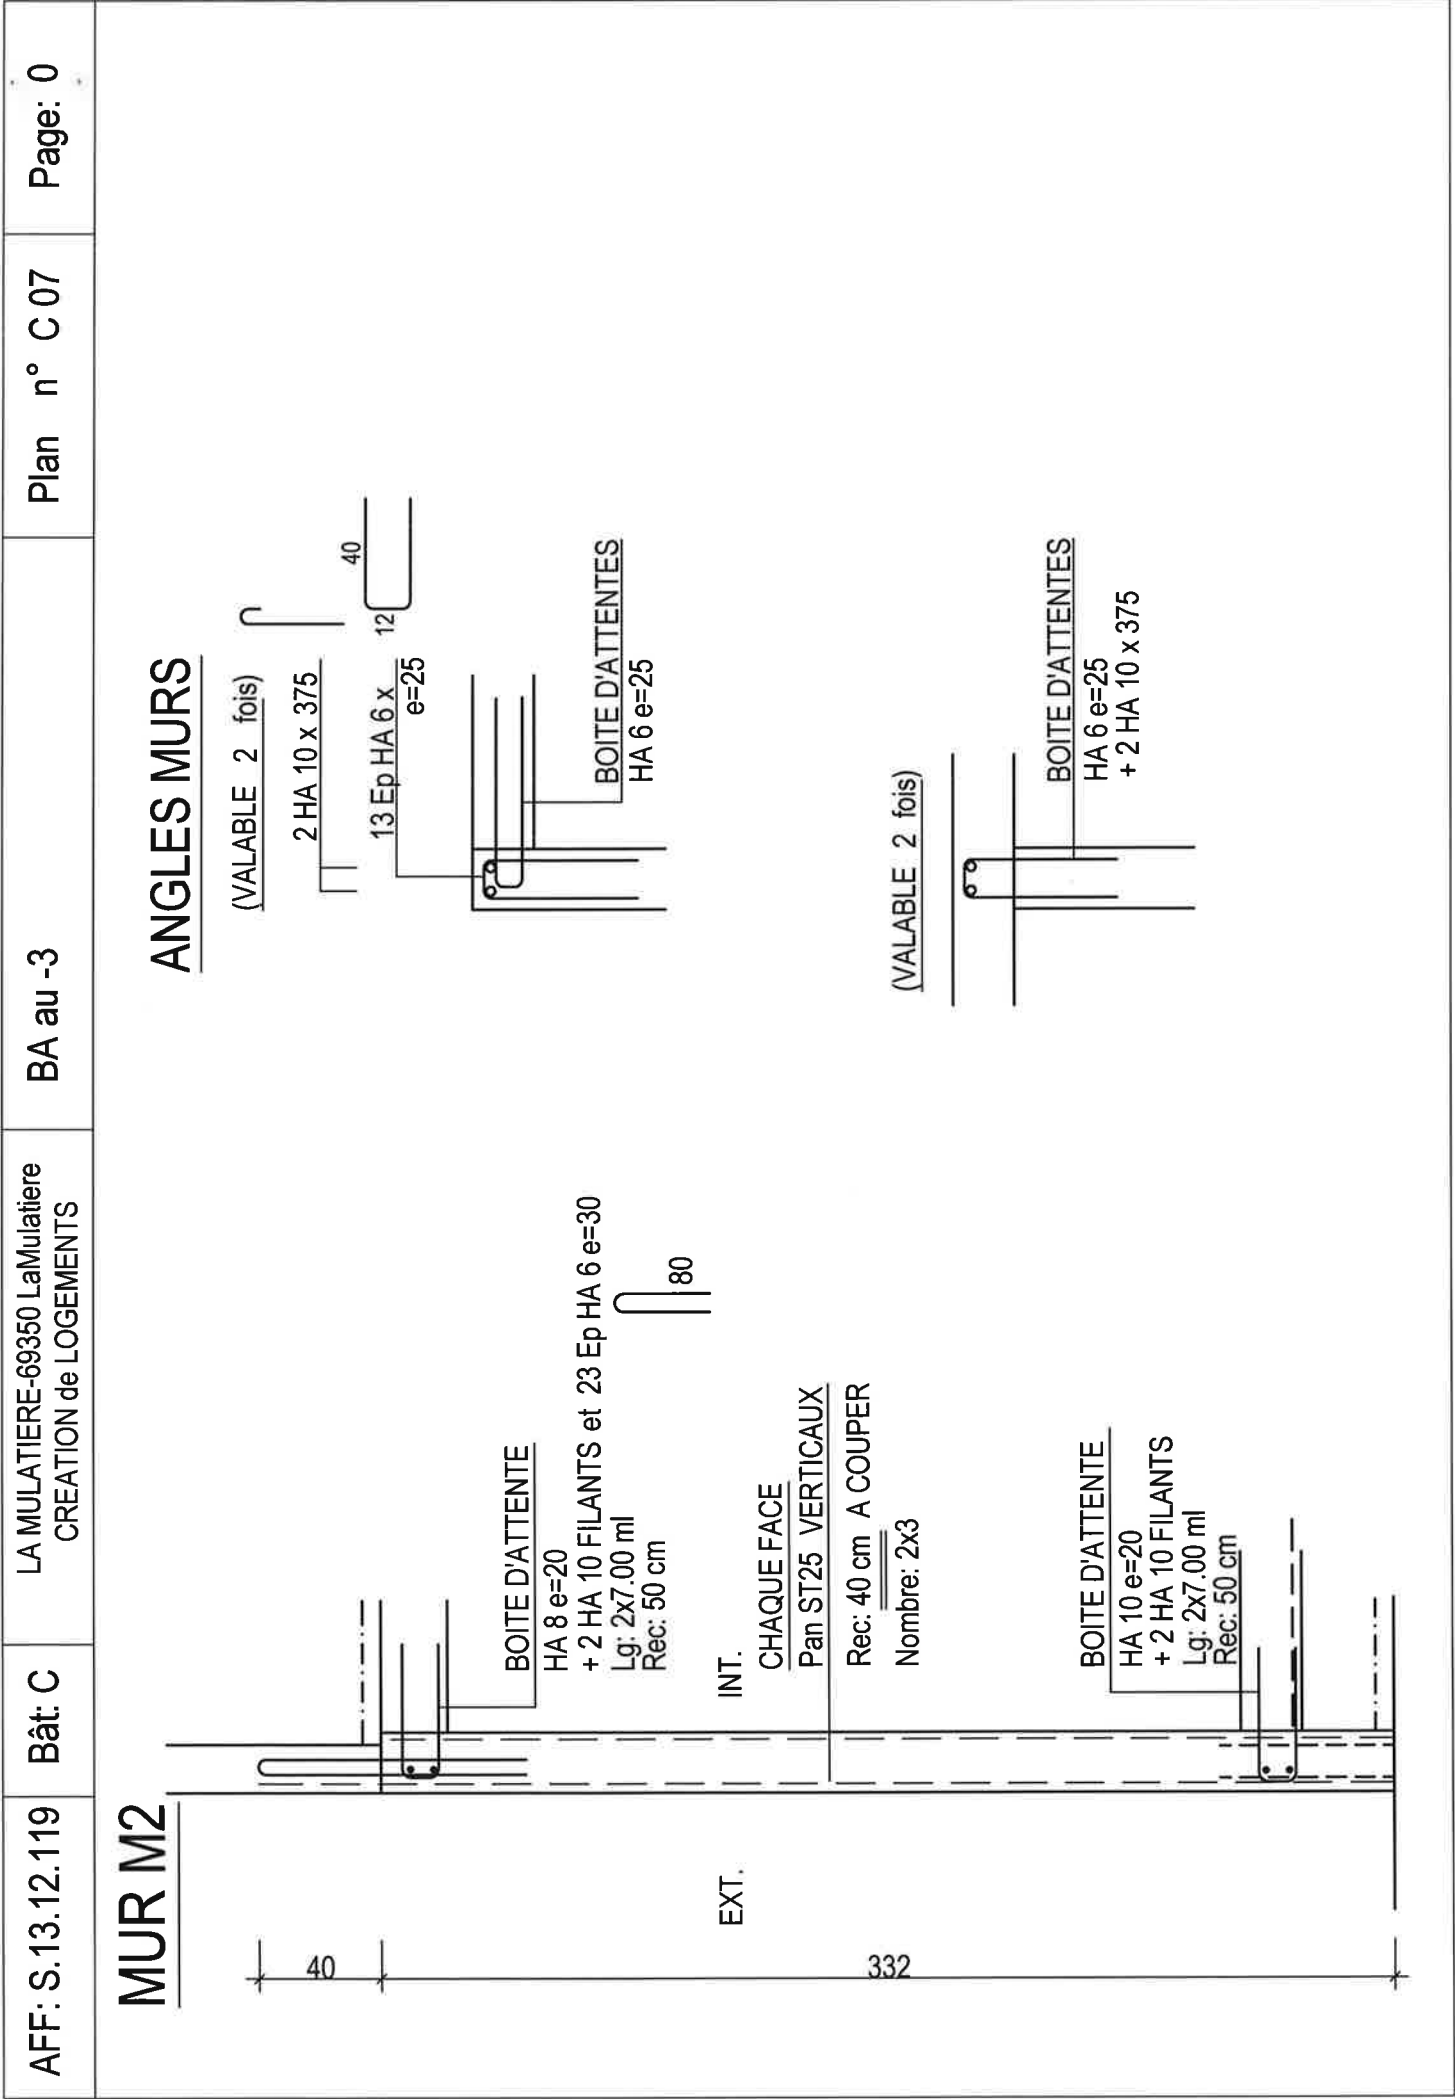

MUR M4


E4a Nombre: 1

Nombre: 1

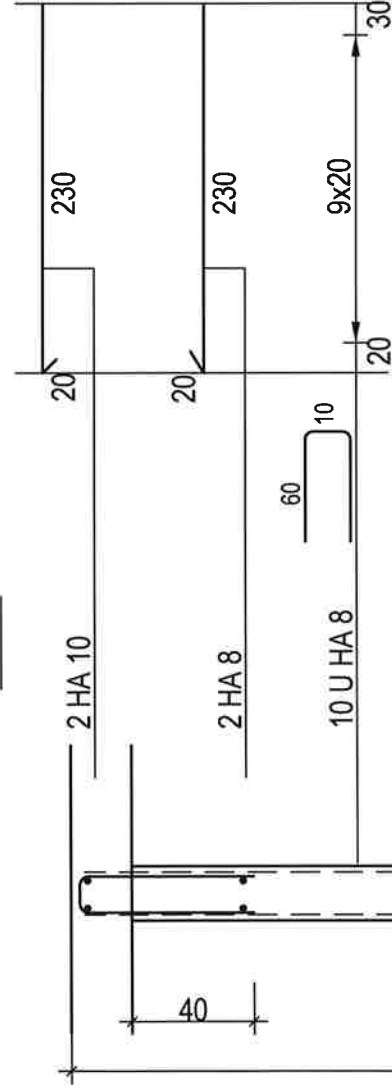

CHAQUE FACE
Pan ST15C A COUPER

Rec: 40 cm
Nombre: 2x1

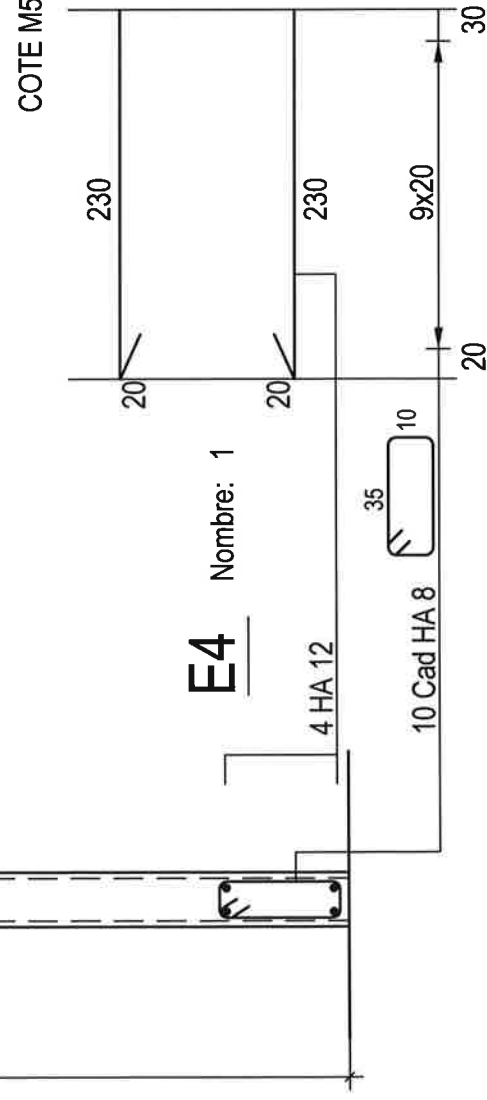

E4 Nombre: 1


Nombre: 1

4 HA 12




E5a Nombre: 1

Nombre: 1

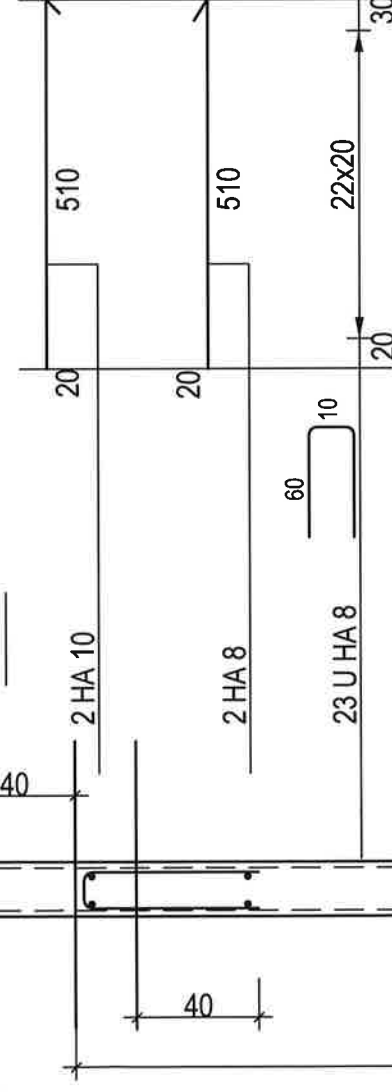

CHAQUE FACE
Pan ST15C A COUPER


Rec: 40 cm
Nombre: 2x2.5

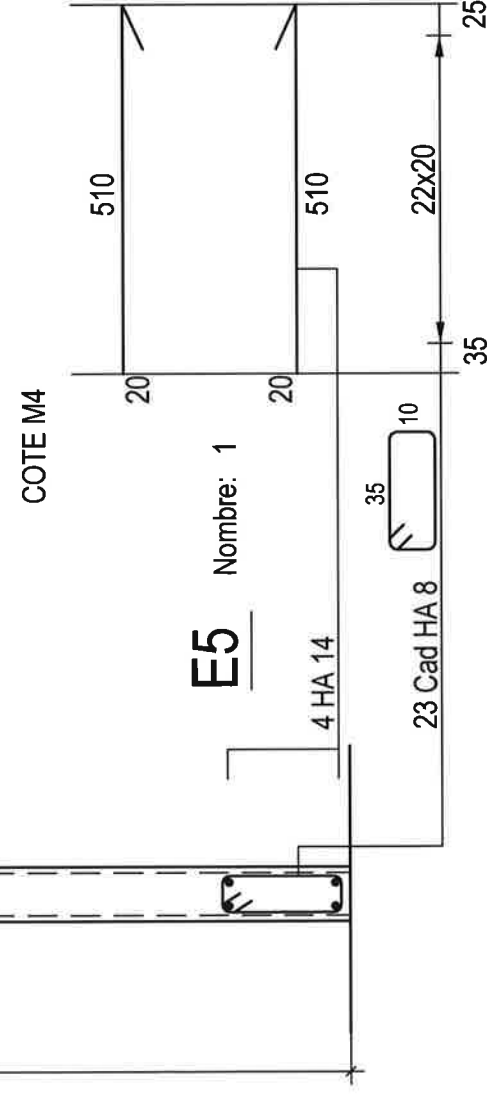


E5




Nombre: _____

4 HA 14

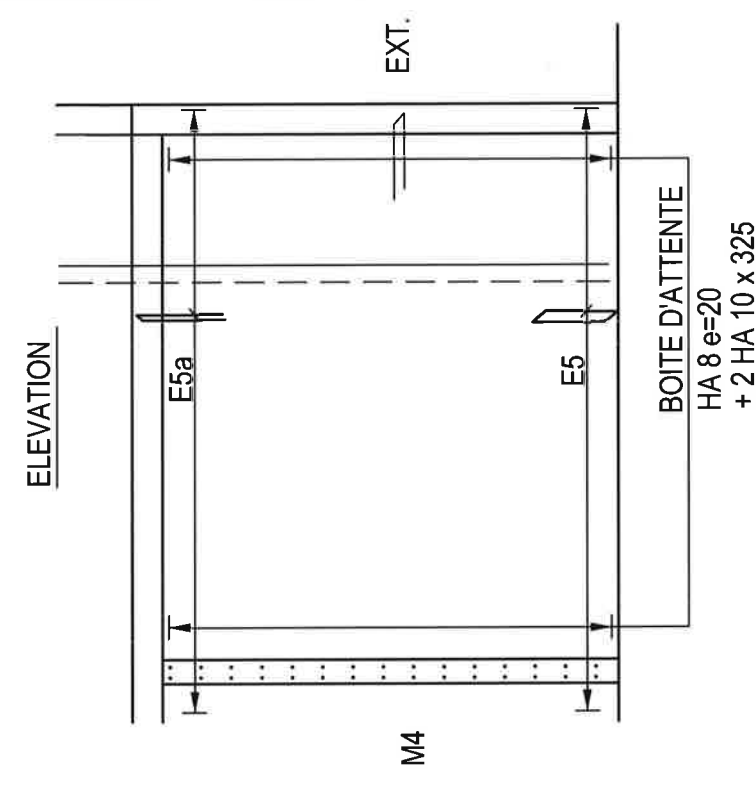


BOITE D'ATTENTE
HA 8 e=20
+ 2 HA 10 x 325

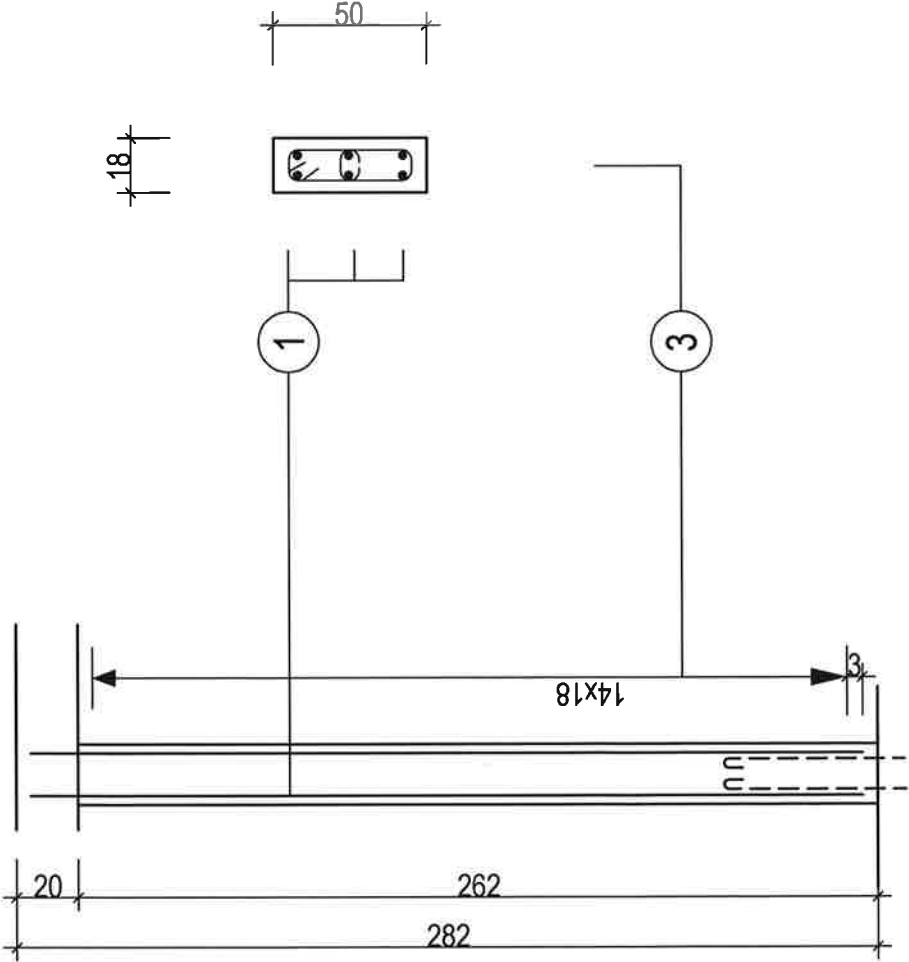
AFF: S.13.12.119	Bât: C	LA MULATIERE-69350 LaMulatiere CREATION de LOGEMENTS	BA au -3	Plan n° C 07	Page: 0
P1 Nombre: 2 18x50 					
1	6 HA 12 x				270
2					
3	15 HA 6 x				44 12
4	15 HA 6 x				12
5					
6					
7					
8					
9					
10					
11					
12					
13					
14					
15					

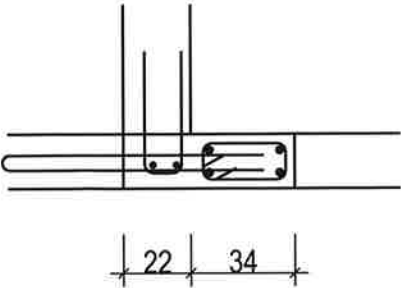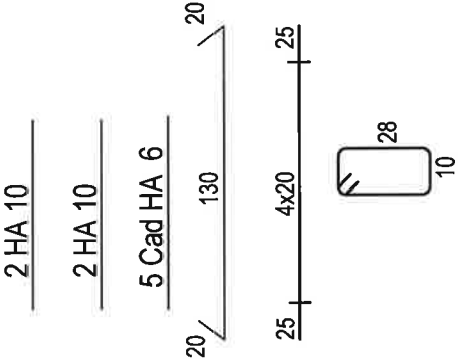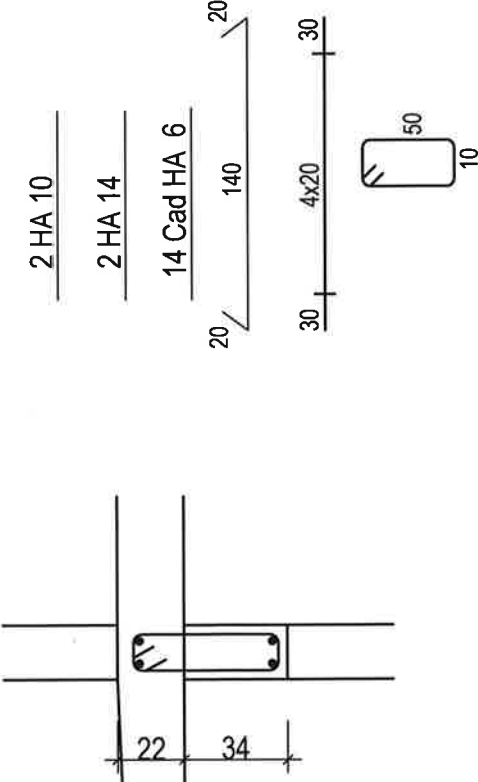AFF: S.13.12.119	Bât: C	LA MULATIERE-69350 LaMulatiere CREATION de LOGEMENTS	BA au -3	Plan n° C 07	Page: 4
LINTEAUX L1 Nombre: 2 PORTEE: 97 					
L3 Nombre: 1 PORTEE: 90 					
L2 Nombre: 4 PORTEE: 97 					


ARMATURES DALLE BASSE du -3
NAPPE INFERIEURE

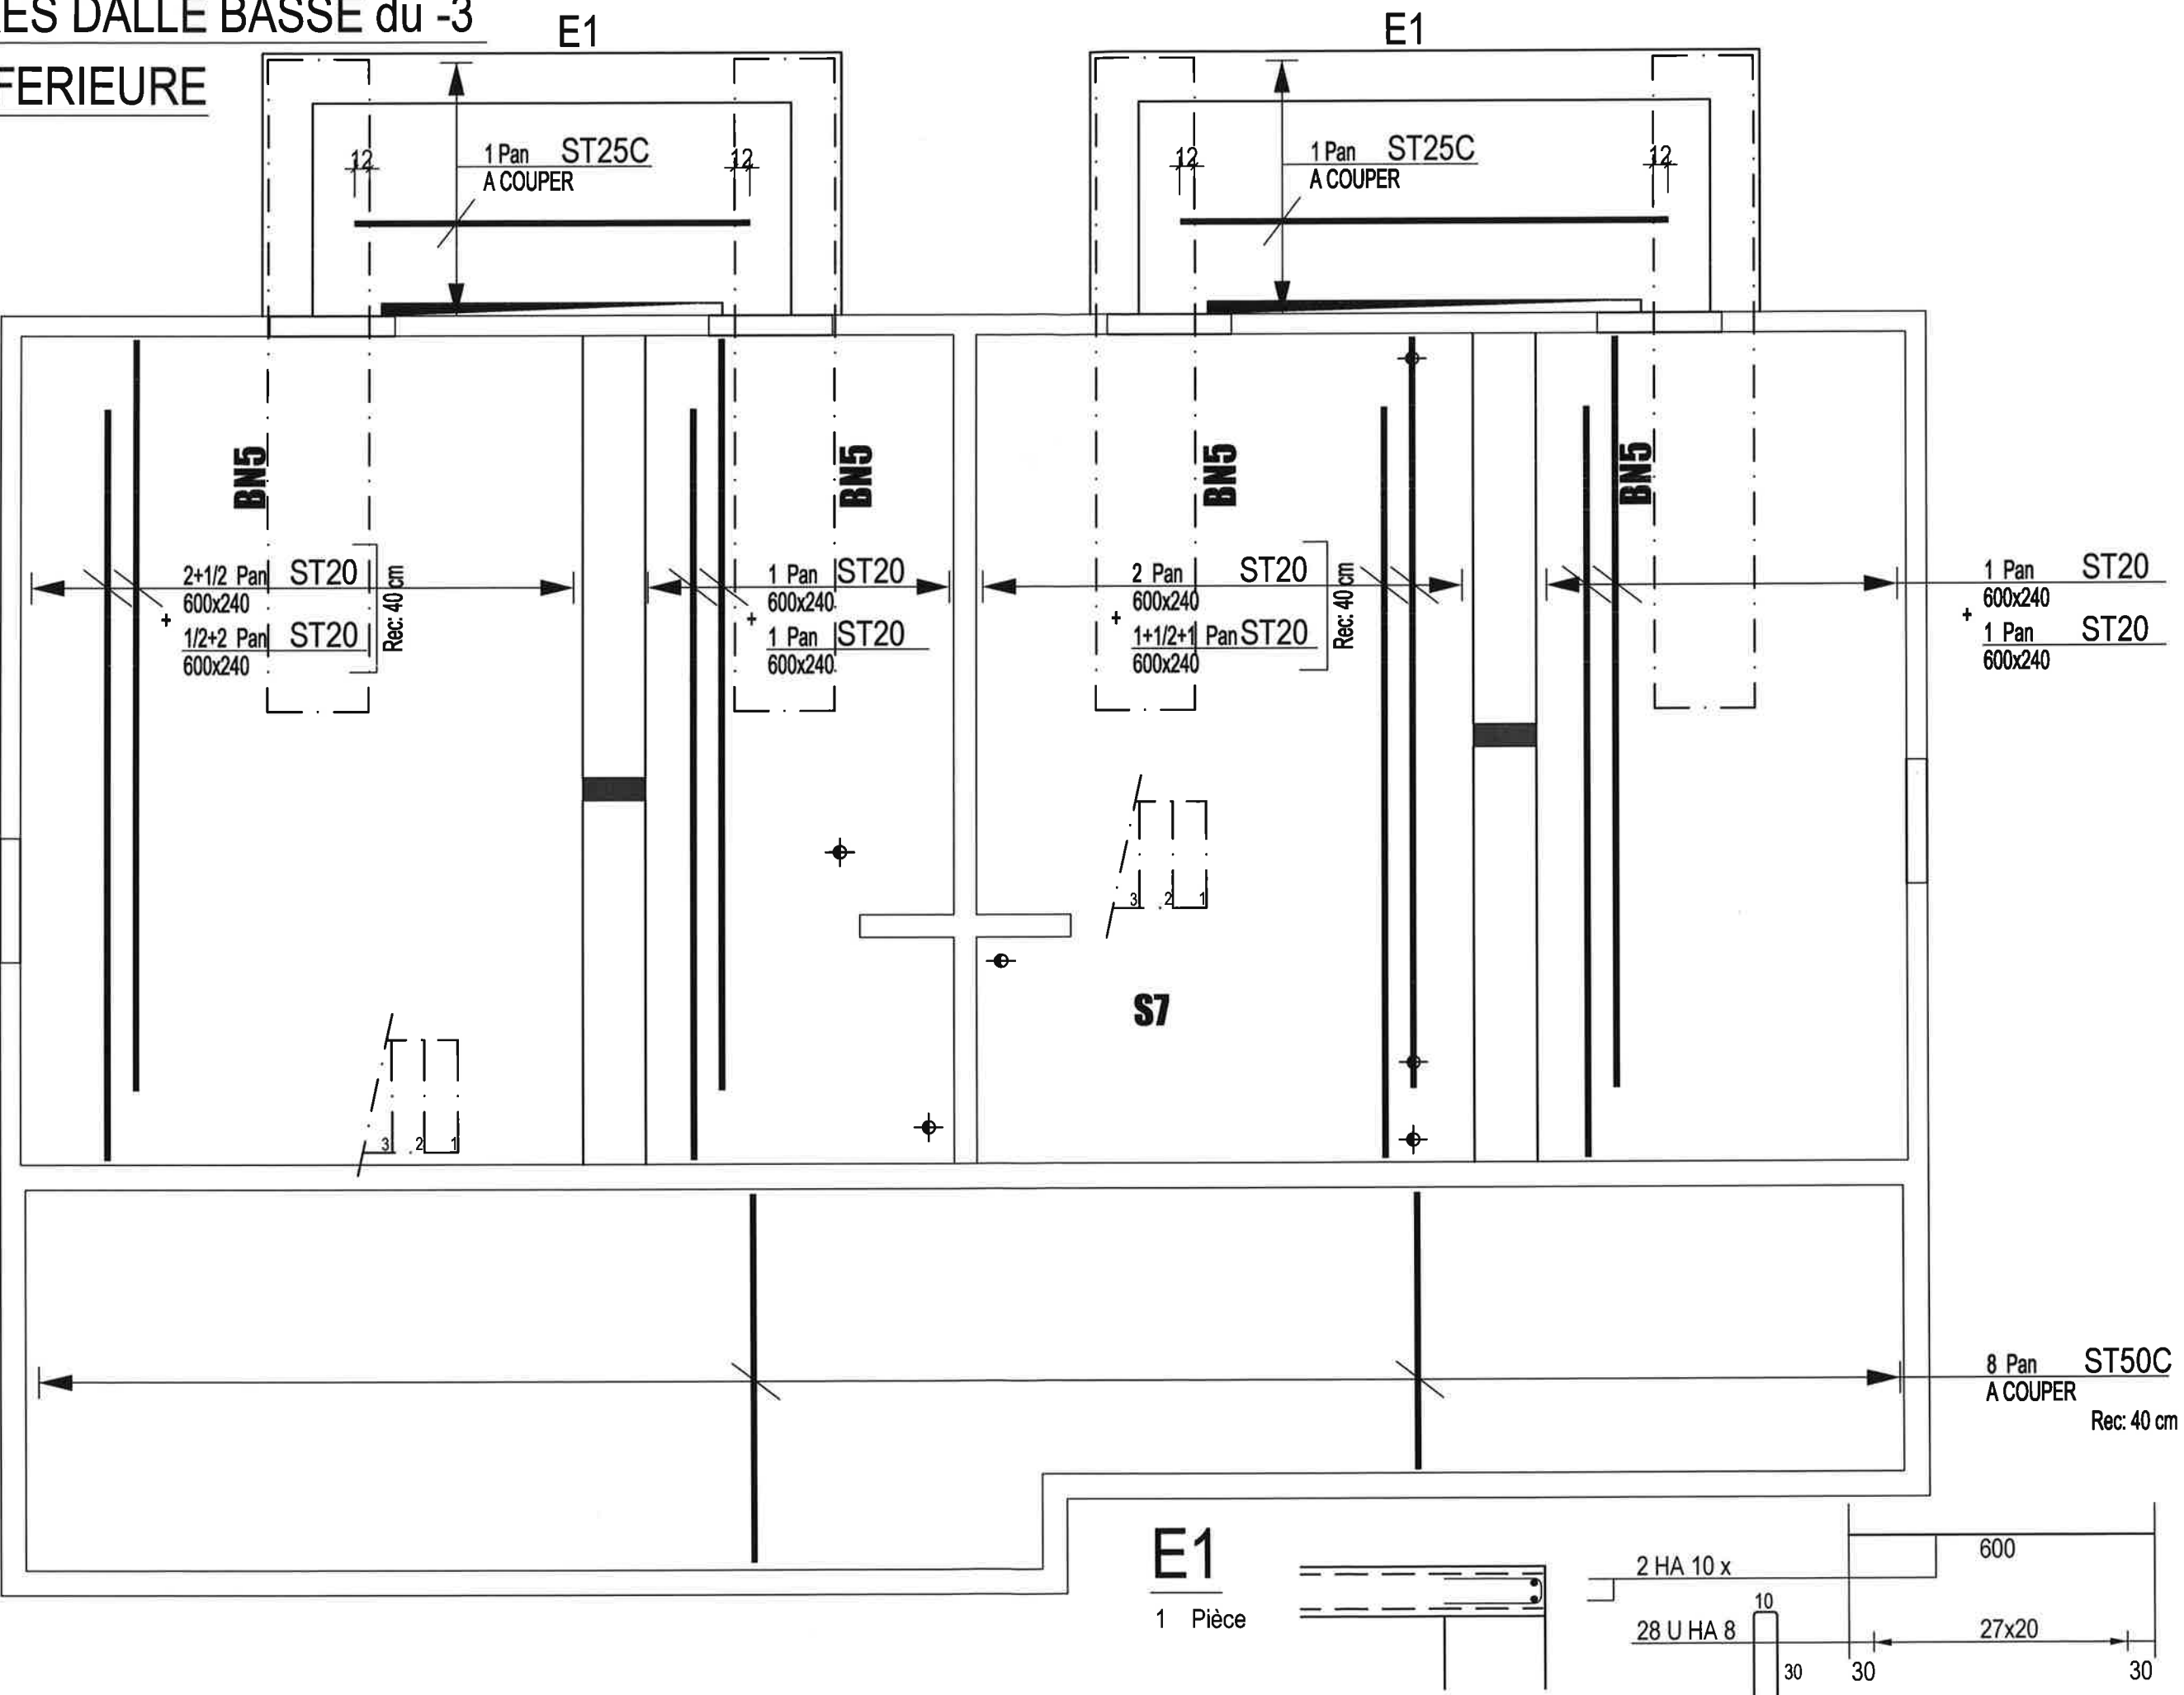


ARMATURES DALLE BASSE du -3

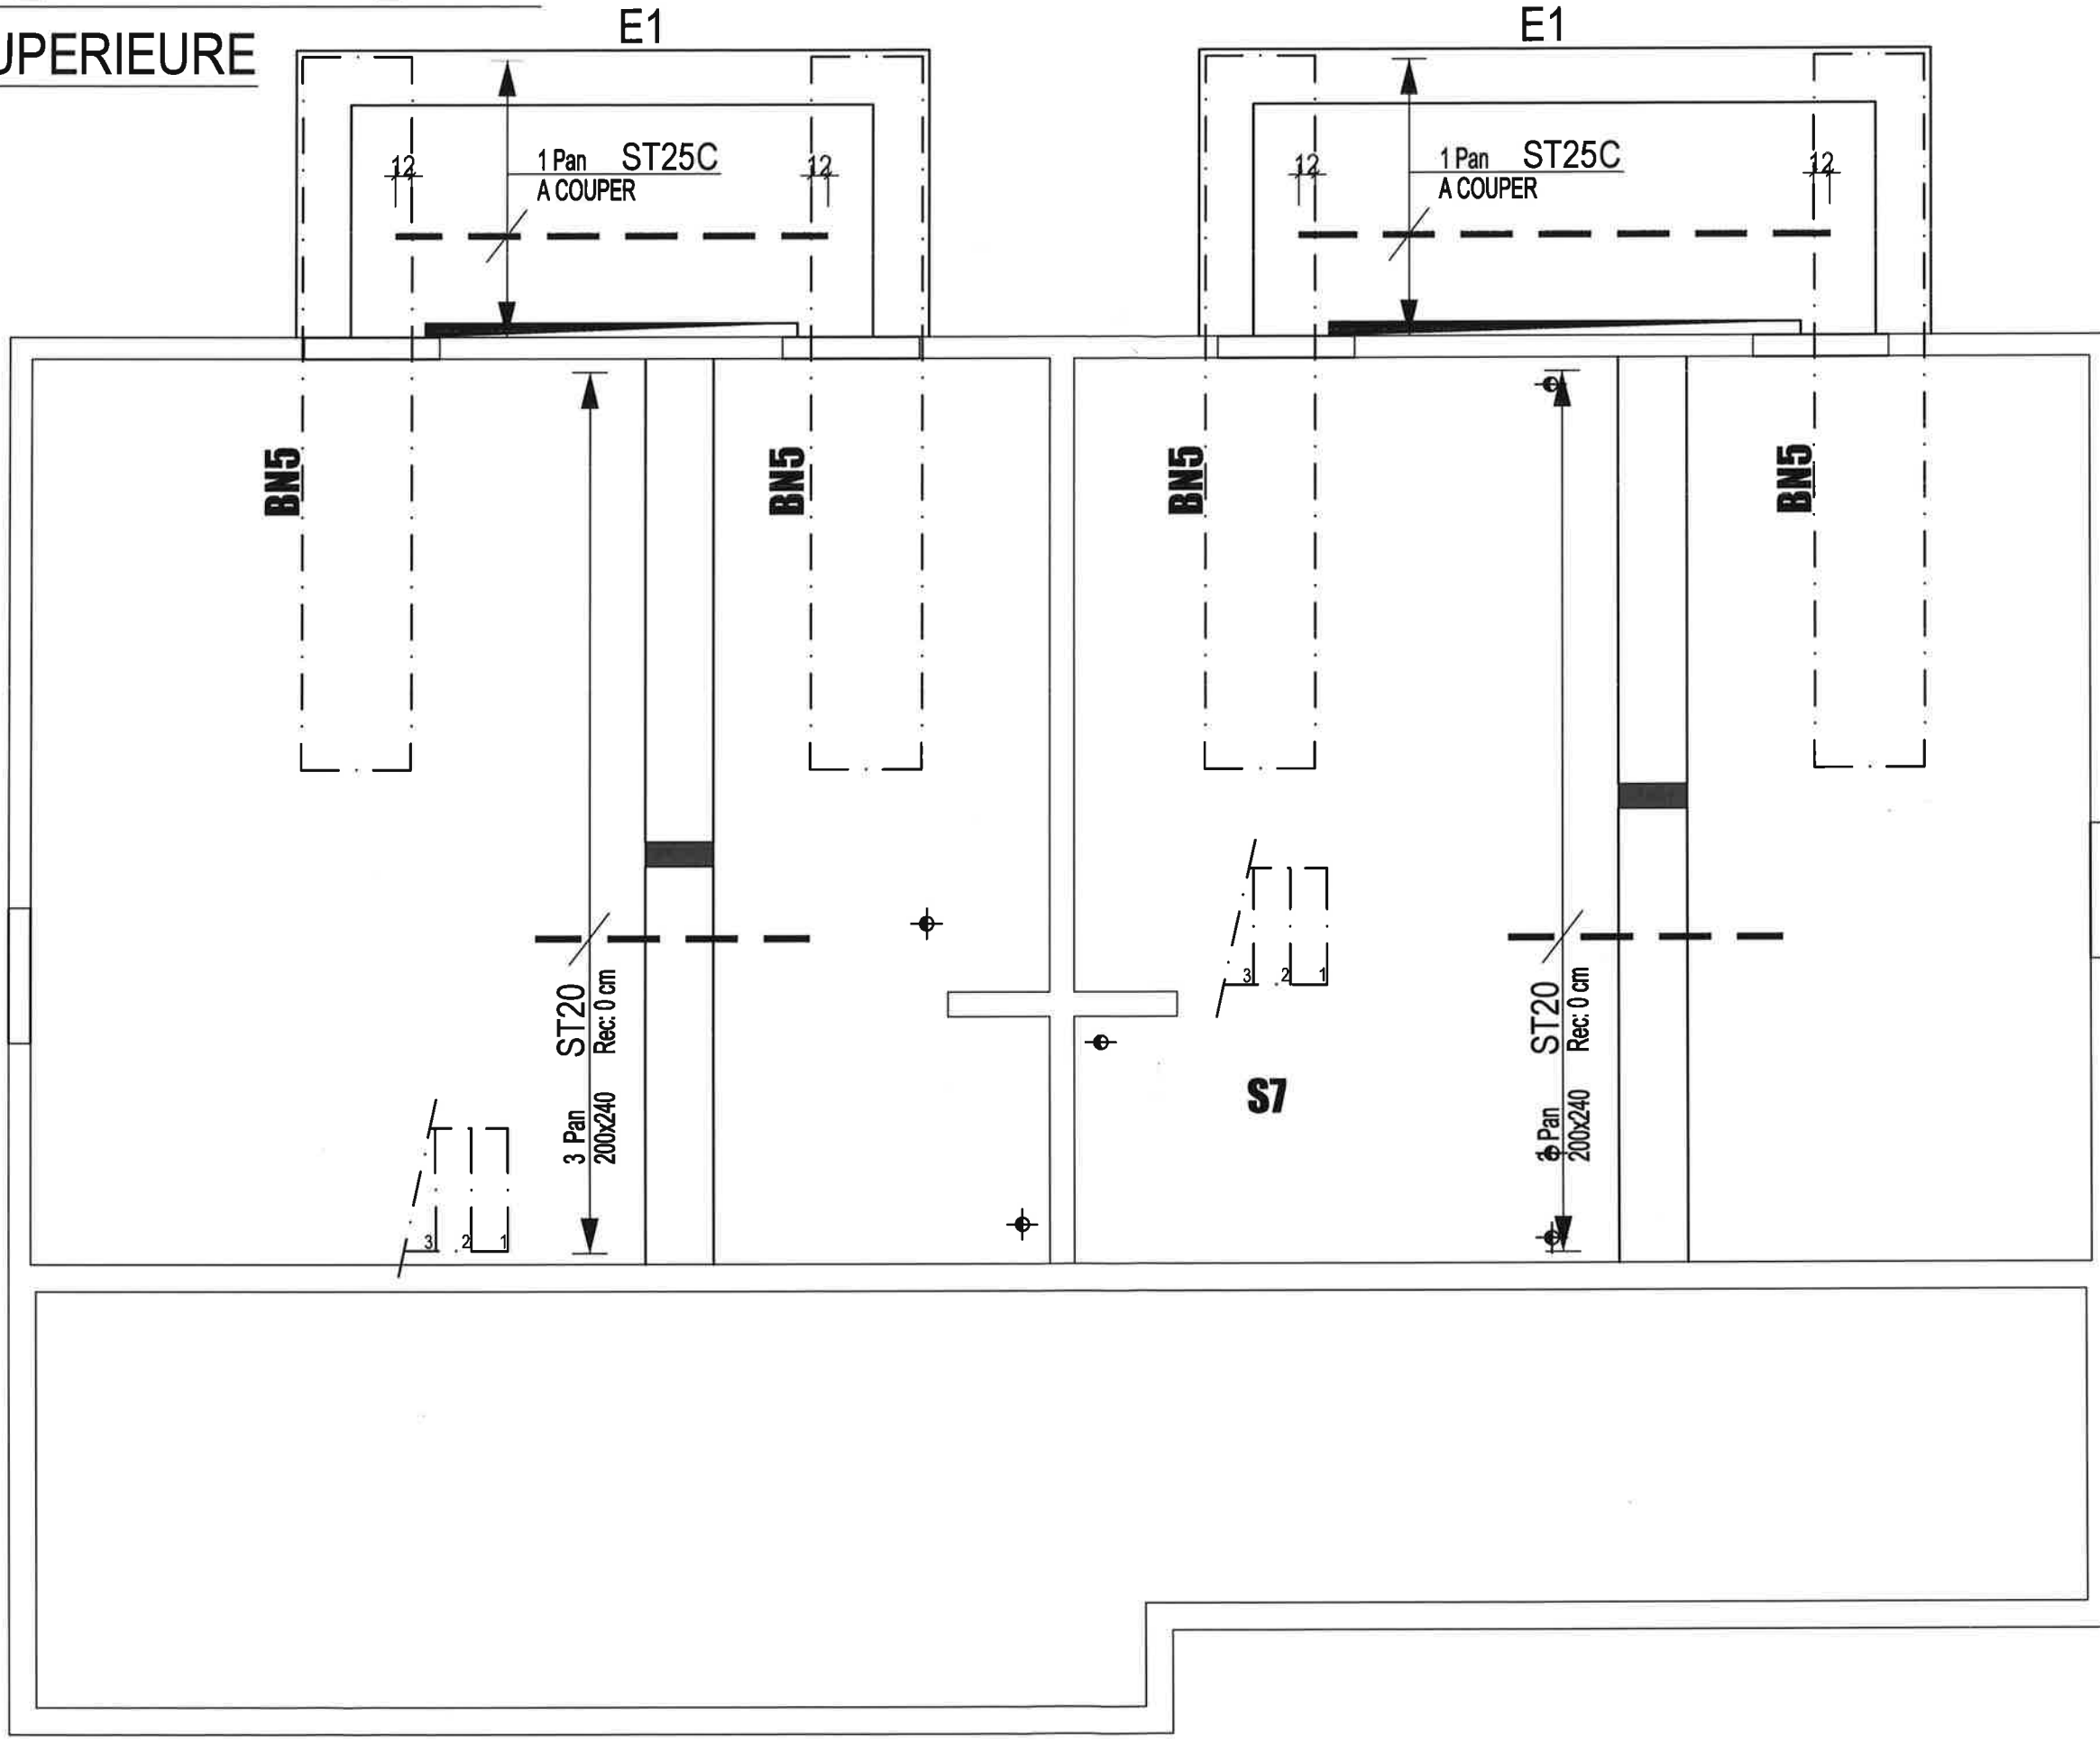

SS-3	BN 5	X4	Béton=0.88 m ³ Acier=84.8 kg d=96.4 kg/m ³ Fi=111.6 mm Cof=6.1 m ²	Ed=2.5 cm Eh=4.0 cm El=3.0 cm	1 2
- Date 18/03/15 - 10 étages -					
Section : 80 x 20ht					
fck= 25 MPa fyk= 500 MPa					

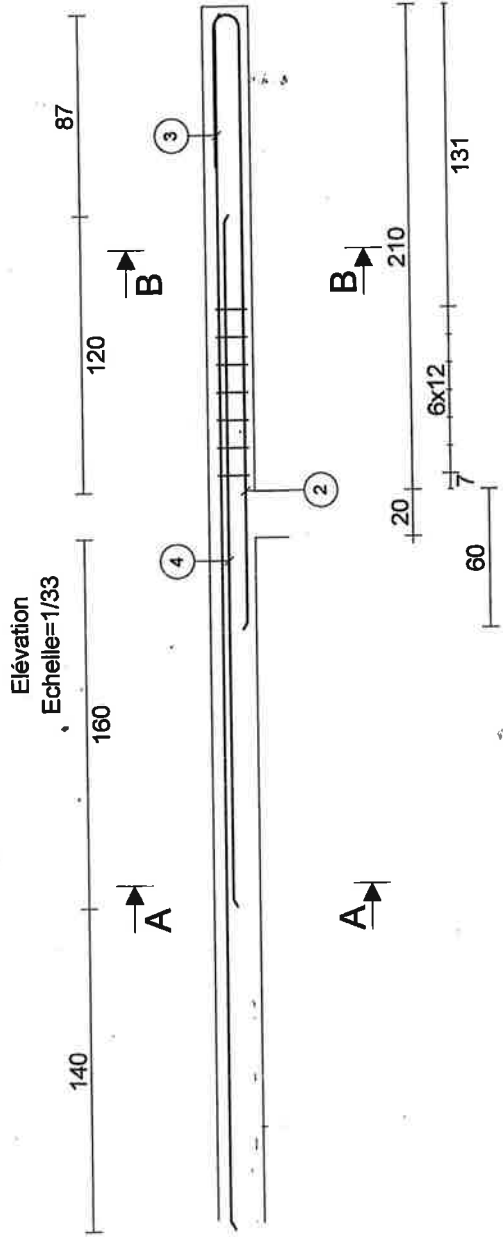


Coupe B-B
Echelle=1/10

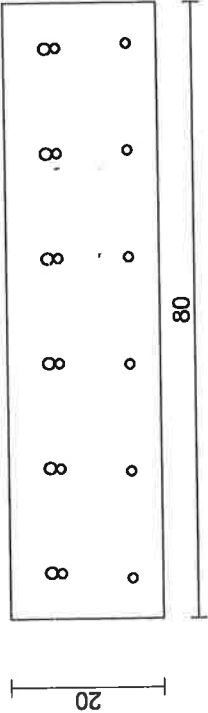

titre EC2 Version 2013

Pouches - 5

Elévation
Echelle=1/20

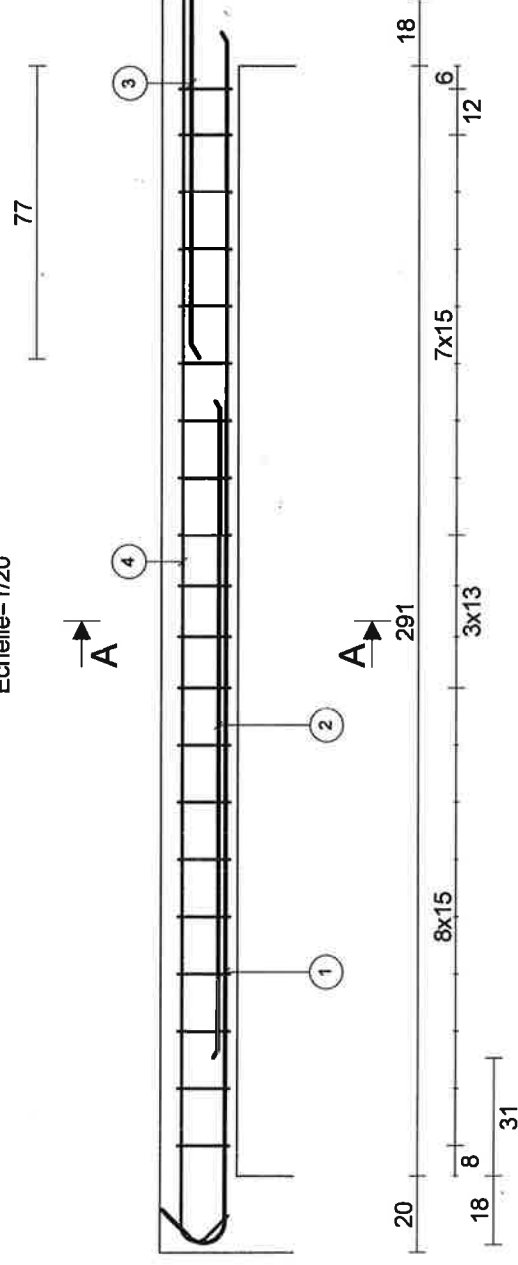


Coupe A-A
Echelle=1/5

Barre	Lg	Forme
1 4HA10	335	
2 4HA8	172	
3 4HA14	192	
4 4HA8	366	
5 20HA6	131	
6 40HA6	46	

Barre	Lg/Poids
HA6	44.7/9.9
HA8	21.5/8.5
HA10	13.4/8.3
HA14	7.7/9.3

Panchanow-3

Elévation
Echelle=1/25

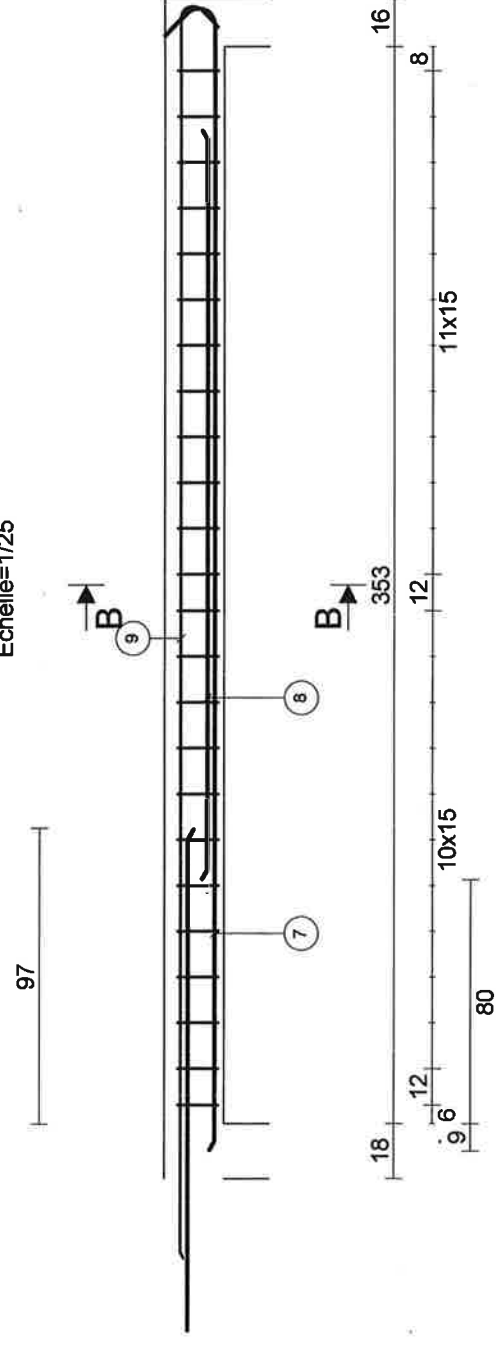

Coupe B-B
Echelle=1/5

Barre	Lg	Forme
7 4HA12	394	
8 4HA12	246	
9 4HA8	424	
10 24HA6	131	
11 48HA6	46	

Barre	Lg/Poids
HA6	53.6/11.9
HA8	16.9/6.7
HA12	25.6/22.7