

VUE EN PLAN

Ech: 1/50

DALLES



FINI: -2.99=-201.46
DALLE BA Epr: 22 cm
DESSUS BRUT: -2.99 + PENTE
RESERVE: 0 cm



FINI: -2.99=-201.46 + PENTE
DALLE BA Epr: 22 cm à 17 cm SOUS CUNETTE
DESSUS BRUT: -2.99 + PENTE
RESERVE: 0 cm + PENTE
VOIR VUE PLAN


VOIR PLAN N° C06

MUR PLISSE A CONFIRMER
SUIVANT NIVEAU du TERRAIN
(Voir FACADE EST archi)

NIVEAU DALLE A CONFIRMER
SUIVANT NIVEAU du TERRAIN
(Voir FACADE EST)


COUPE A

Ech: 1/50

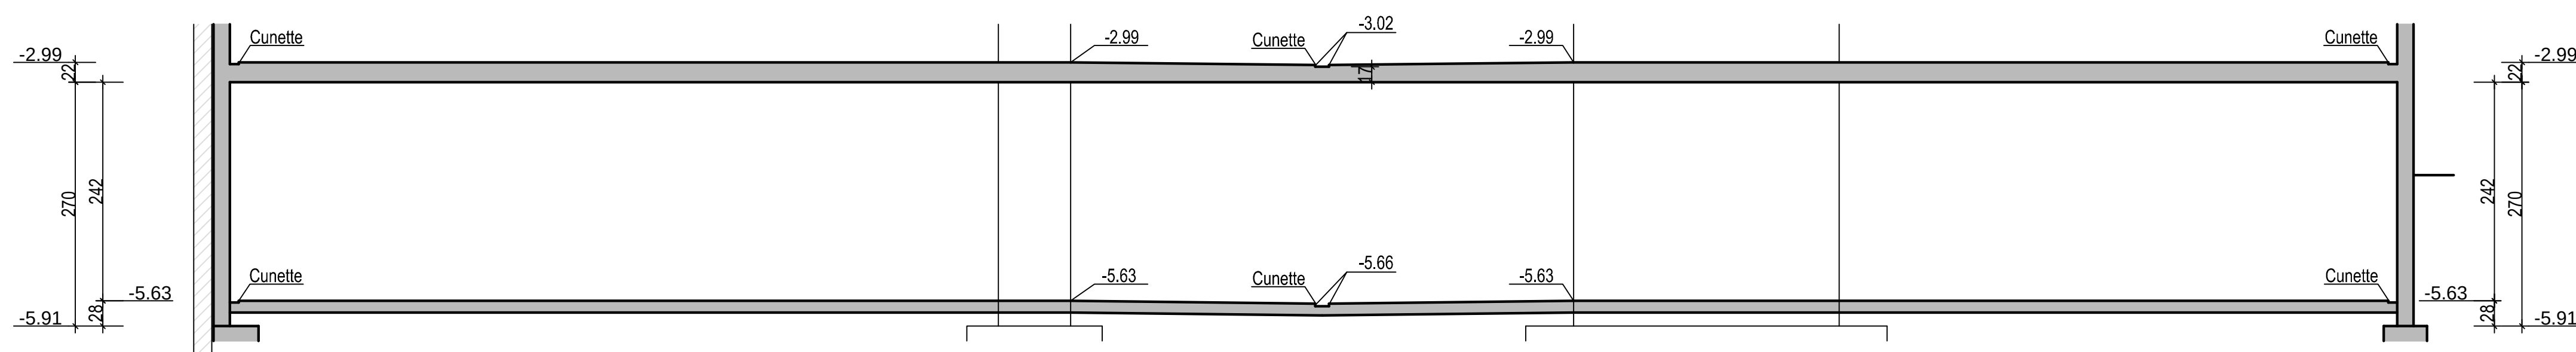


COUPE E

Ech: 1/50

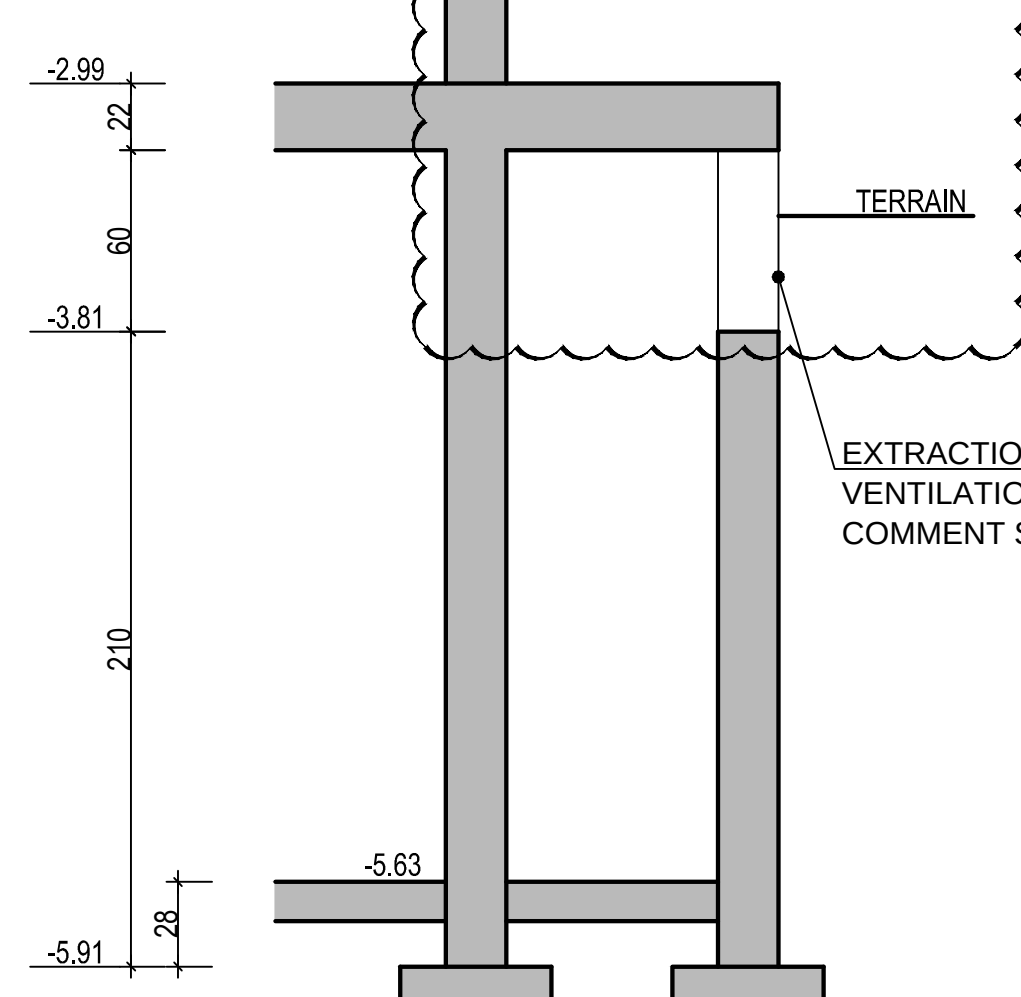


COUPE D

Ech: 1/50

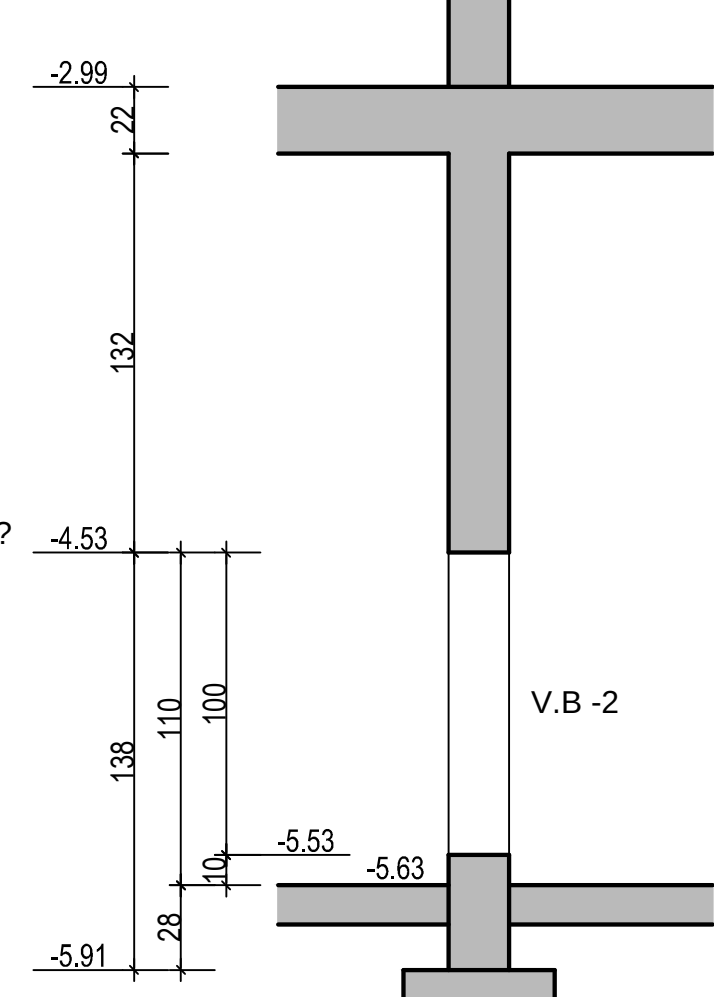


COUPE C

Ech: 1/50

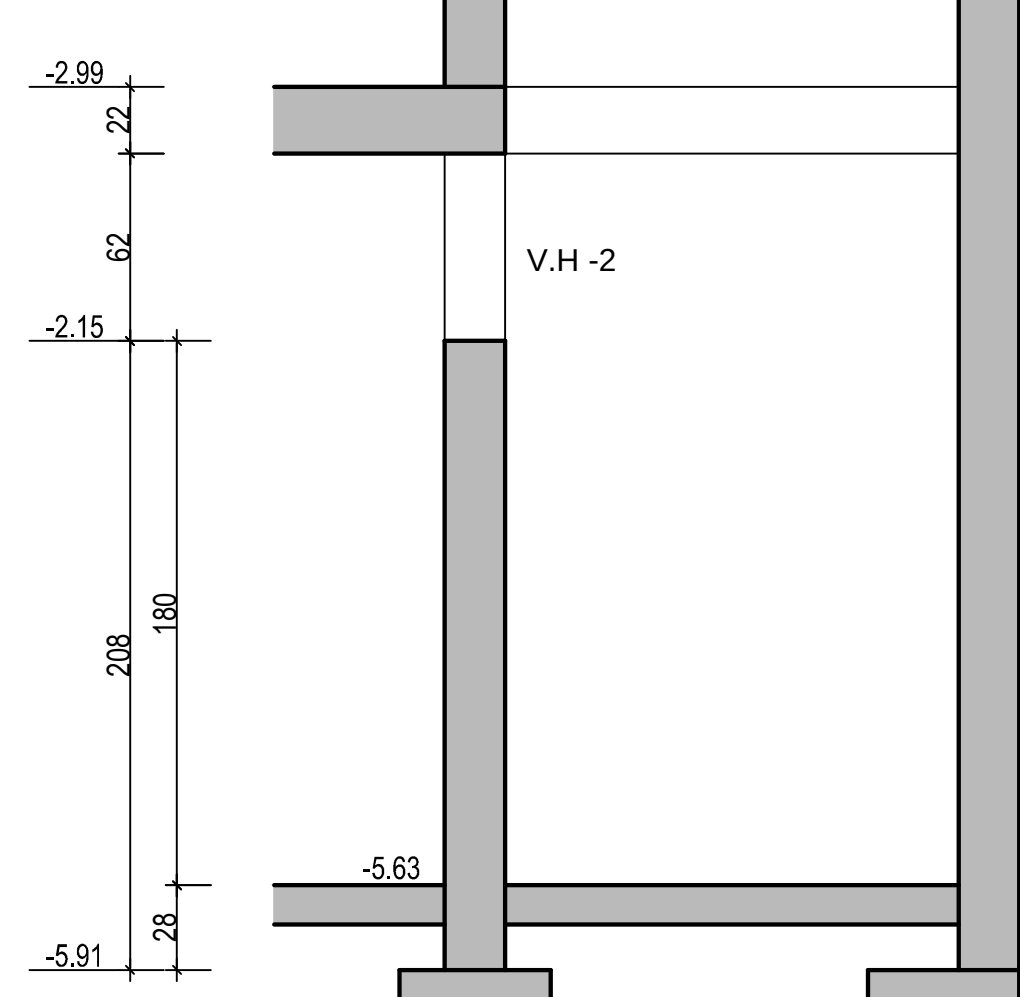

COUPE B

Ech: 1/50

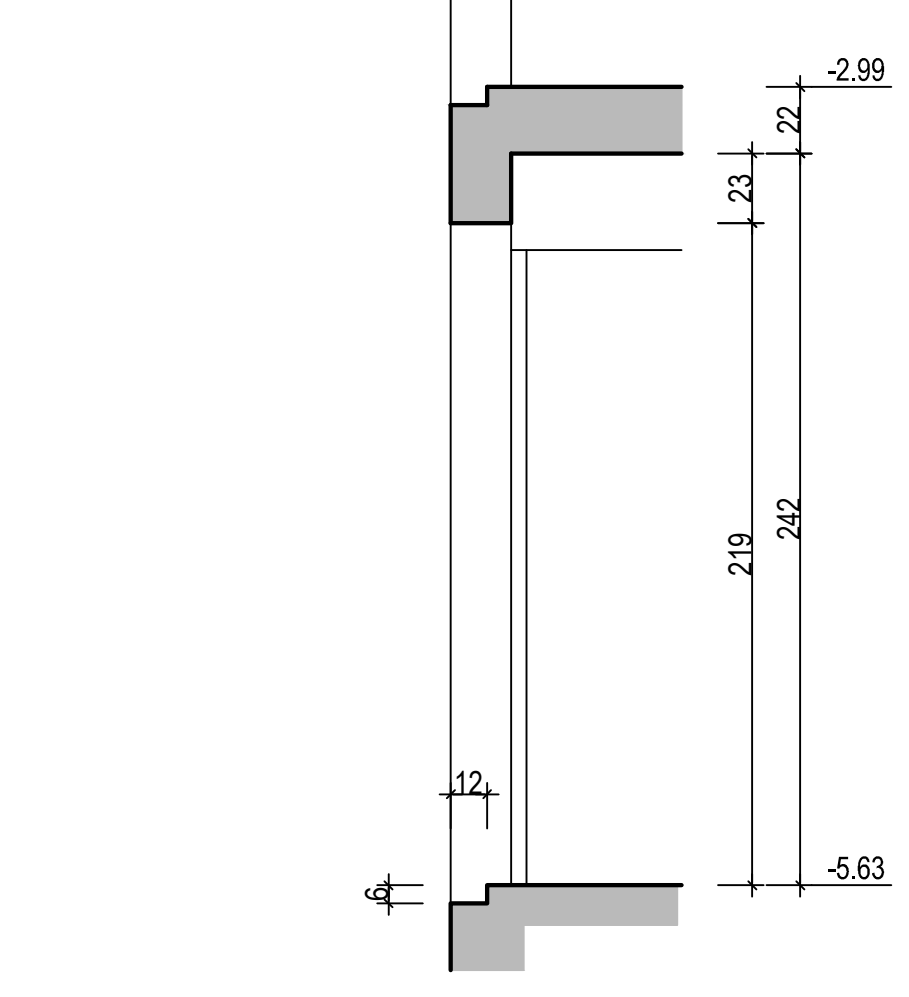

±0.00 = 204.45 = NIVEAU FINI du REZ de CHAUSSEE Bât: C

NOAHO

Chemin de Fontanière - 69350 La Mulatière

Création de logements

Les entreprises réalisant les travaux devront tenir compte des derniers plans architectes lors de la réalisation des travaux.
Les plans du bat MATTE ne doivent servir qu'au corps d'Etat concerné et doivent être des plans d'exécution.

ARCHITECTES: Atelier DTS
BET STRUCTURE: MATTE SAS
BET FLUIDES: PRELEM
ECONOMISTE: EXECO
BUREAU DE CONTROLE: Bureau VERITAS

MO DELEGUE: PSO Ingénierie
MSE: CSFS
SUD EST COORDINATION: OPC
ENTREPRISES: Fontanel pbc

Bât: C Aile OUEST

PLANCHER SUR -2

Coffrage

INDICE DATE MODIFICATIONS

A 30/06/2015 COMPLETE

MATTÉ

BUREAU D'ETUDES

STRUCTURES ET FLUIDES

119 BOULEVARD STALIN - 69100 VILLEURBANNE
Tél: 04 72 44 12 81 Fax: 04 72 44 26 99
E-mail: mat@matte.fr

DOE

Contrainte de sol: 8 bars EL5

Aciers HA (T) F4E500

Aciers Doux (B) F4E235

Aciers TS F4E 500

Béton C28 + 2MPa

Enrobage = 3 cm

PLAN N°

C08 A

DATE: 15/06/2015

Affaire N°

13.12.119