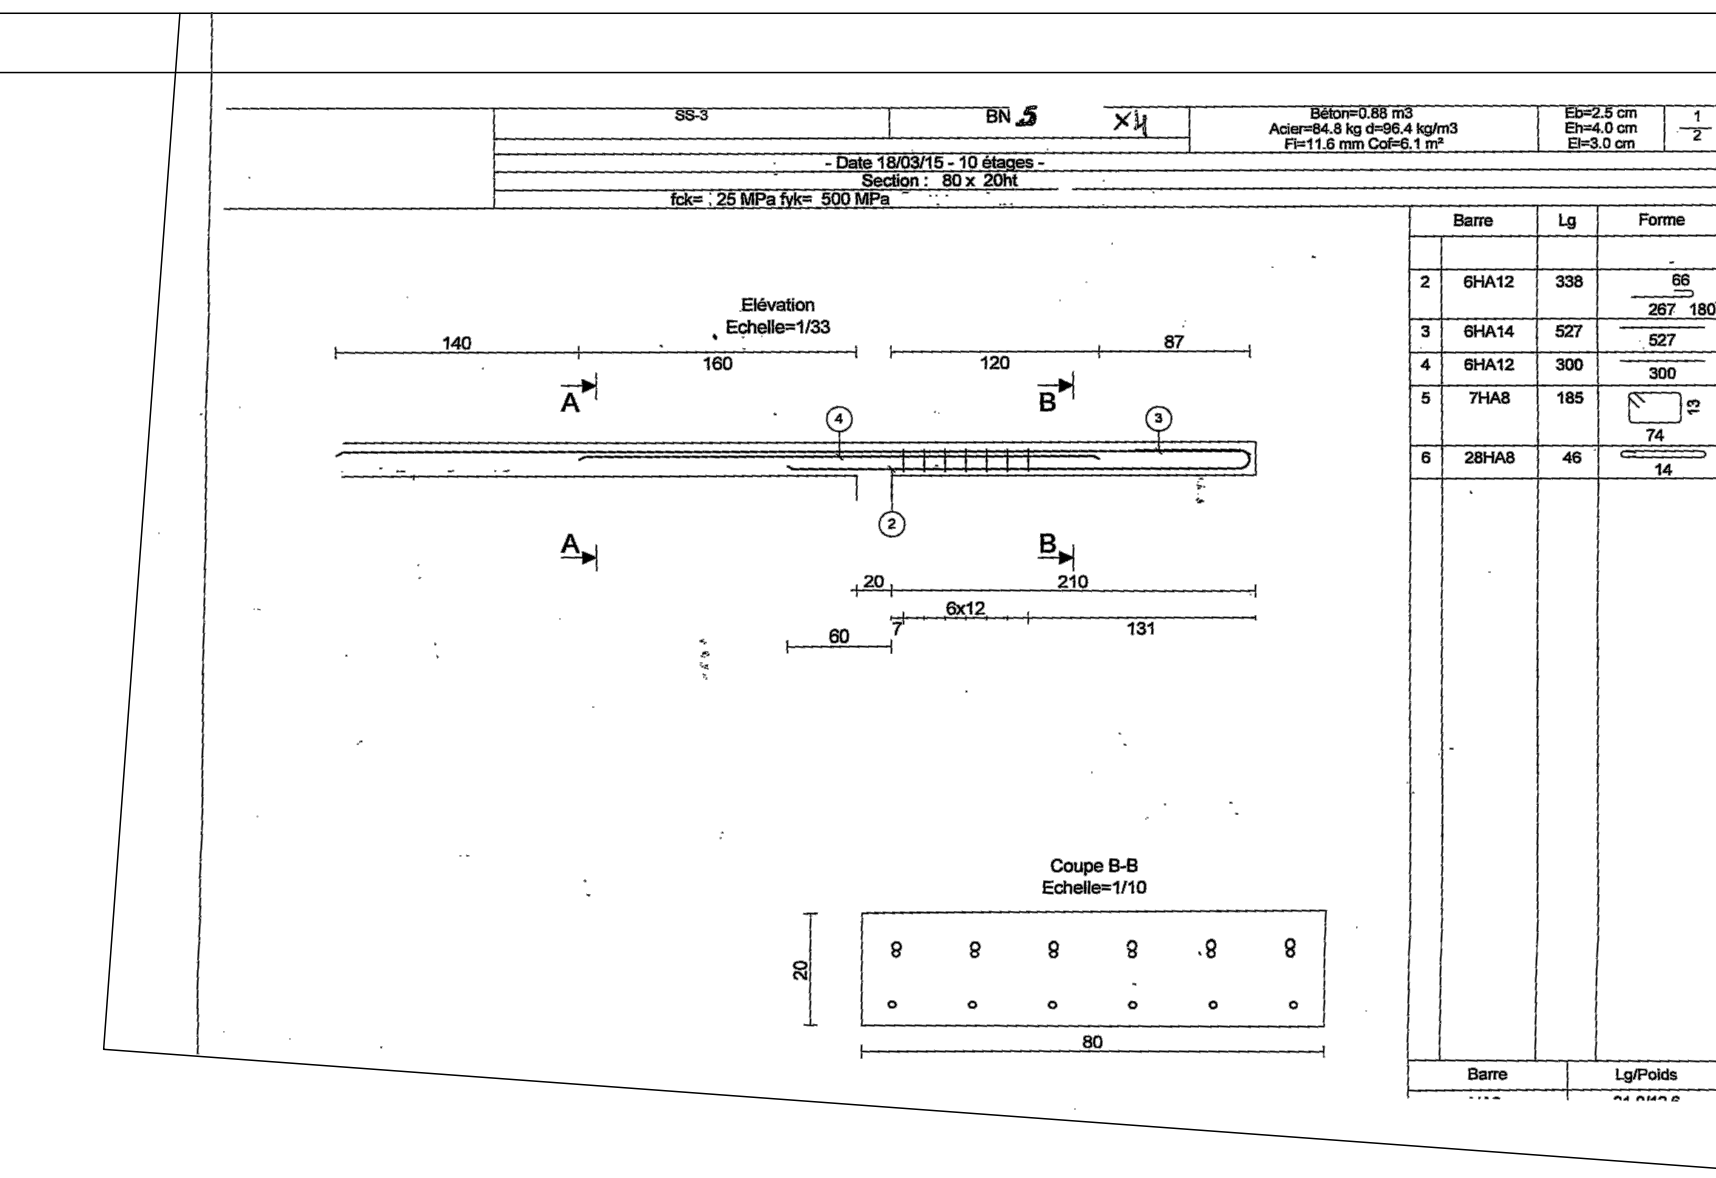
SS-3
BN 5
Béton=0.88 m3
Acier=84.8 kg d=96.4 kg/m3
Eb=2.5 cm
Eh=4.0 cm
El=3.0 cm
- Date 18/03/15 - 10 étages -
Section : 80 x 20ht
fck= 25 MPa fyk= 500 MPa
Elévation
Echelle=1/33
140
160
120
87
20
210
6x12
131
60
Coupe B-B
Echelle=1/10
80
20

Barre	Lg	Forme
2 6HA12	338	66 267 180°
3 6HA14	527	527
4 6HA12	300	300
5 7HA8	185	13 74
6 28HA8	46	14

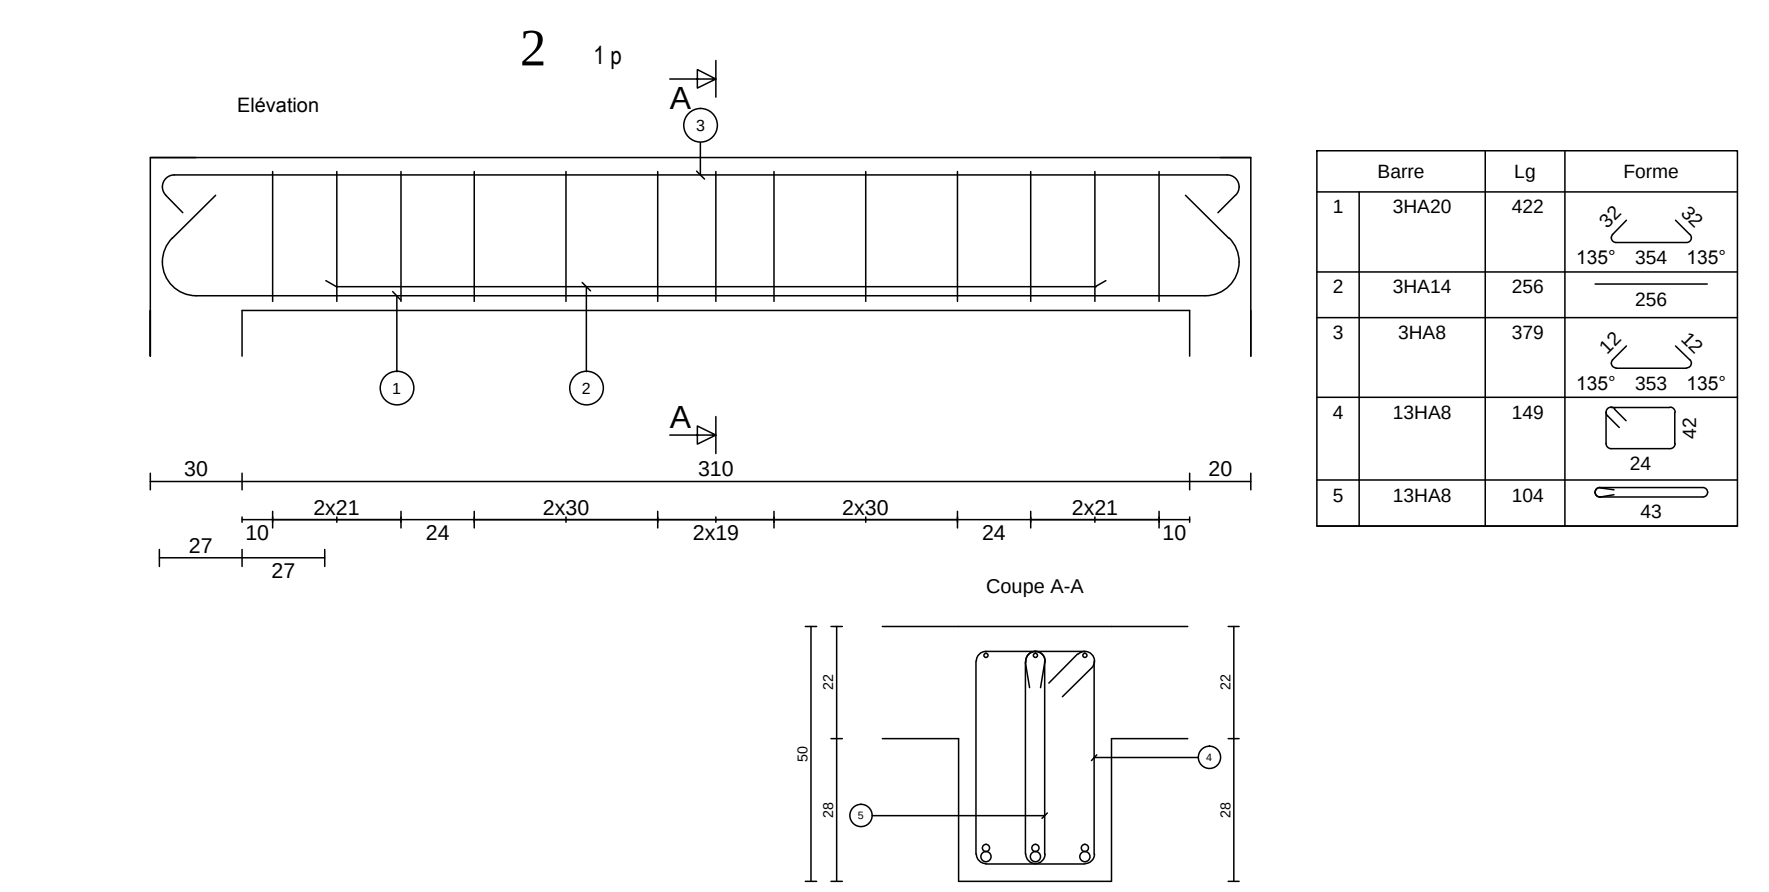
2 1 p
Elévation
A
30
310
20
2x21
2x30
2x30
2x21
10
24
2x19
24
10
27
27
Coupe A-A
30

	Barre	Lg	Forme
1	3HA20	422	32 135° 354 135° 32
2	3HA14	256	256
3	3HA8	379	12 135° 353 135° 12
4	13HA8	149	24 42
5	13HA8	104	43

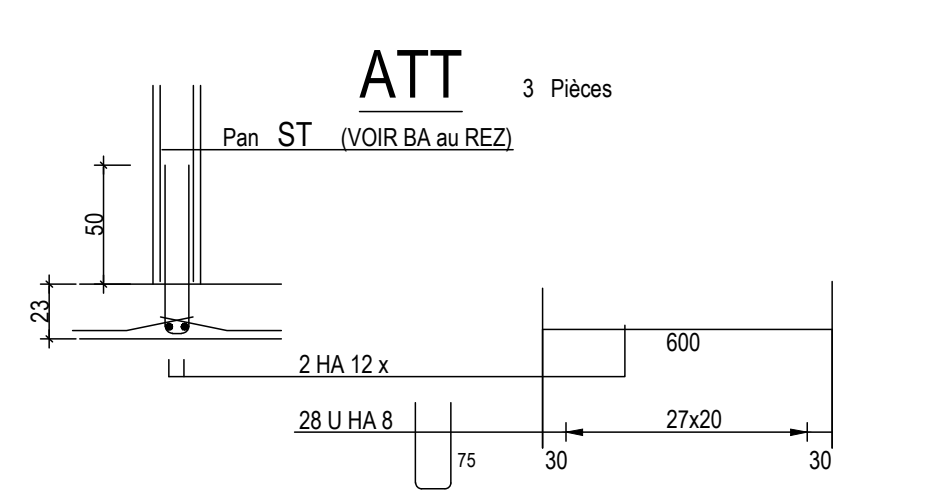
ATT 3 Pièces
Pan ST (VOIR BA au REZ)
50
23
2 HA 12 x
600
28 U HA 8
75
8
27x20
30
30

RECA. T.S.		
PAF 10	420x240	9
ST20	600x240	42
ST25	600x240	7
ST30	600x240	0
ST35	600x240	0
ST50	600x240	0
ST60	600x240	0
ST15C	400x240	0
ST25C	600x240	7
ST40C	600x240	0
ST50C	600x240	4
ST65C	600x240	4

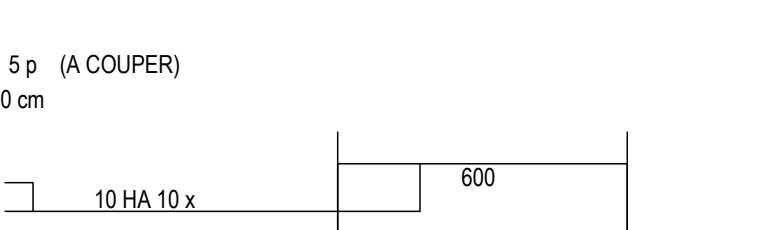
E1 5 p (A COUPER)
Rec: 50 cm
10 HA 10 x
600
28 Cad HA 6
35
10
27x20
30
30

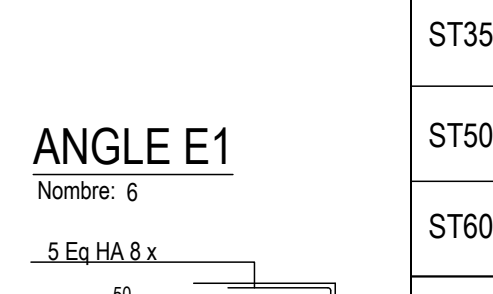
ANGLE E1
Nombre: 6
5 Eq HA 8 x
50
50

NAPPE SUPERIEURE

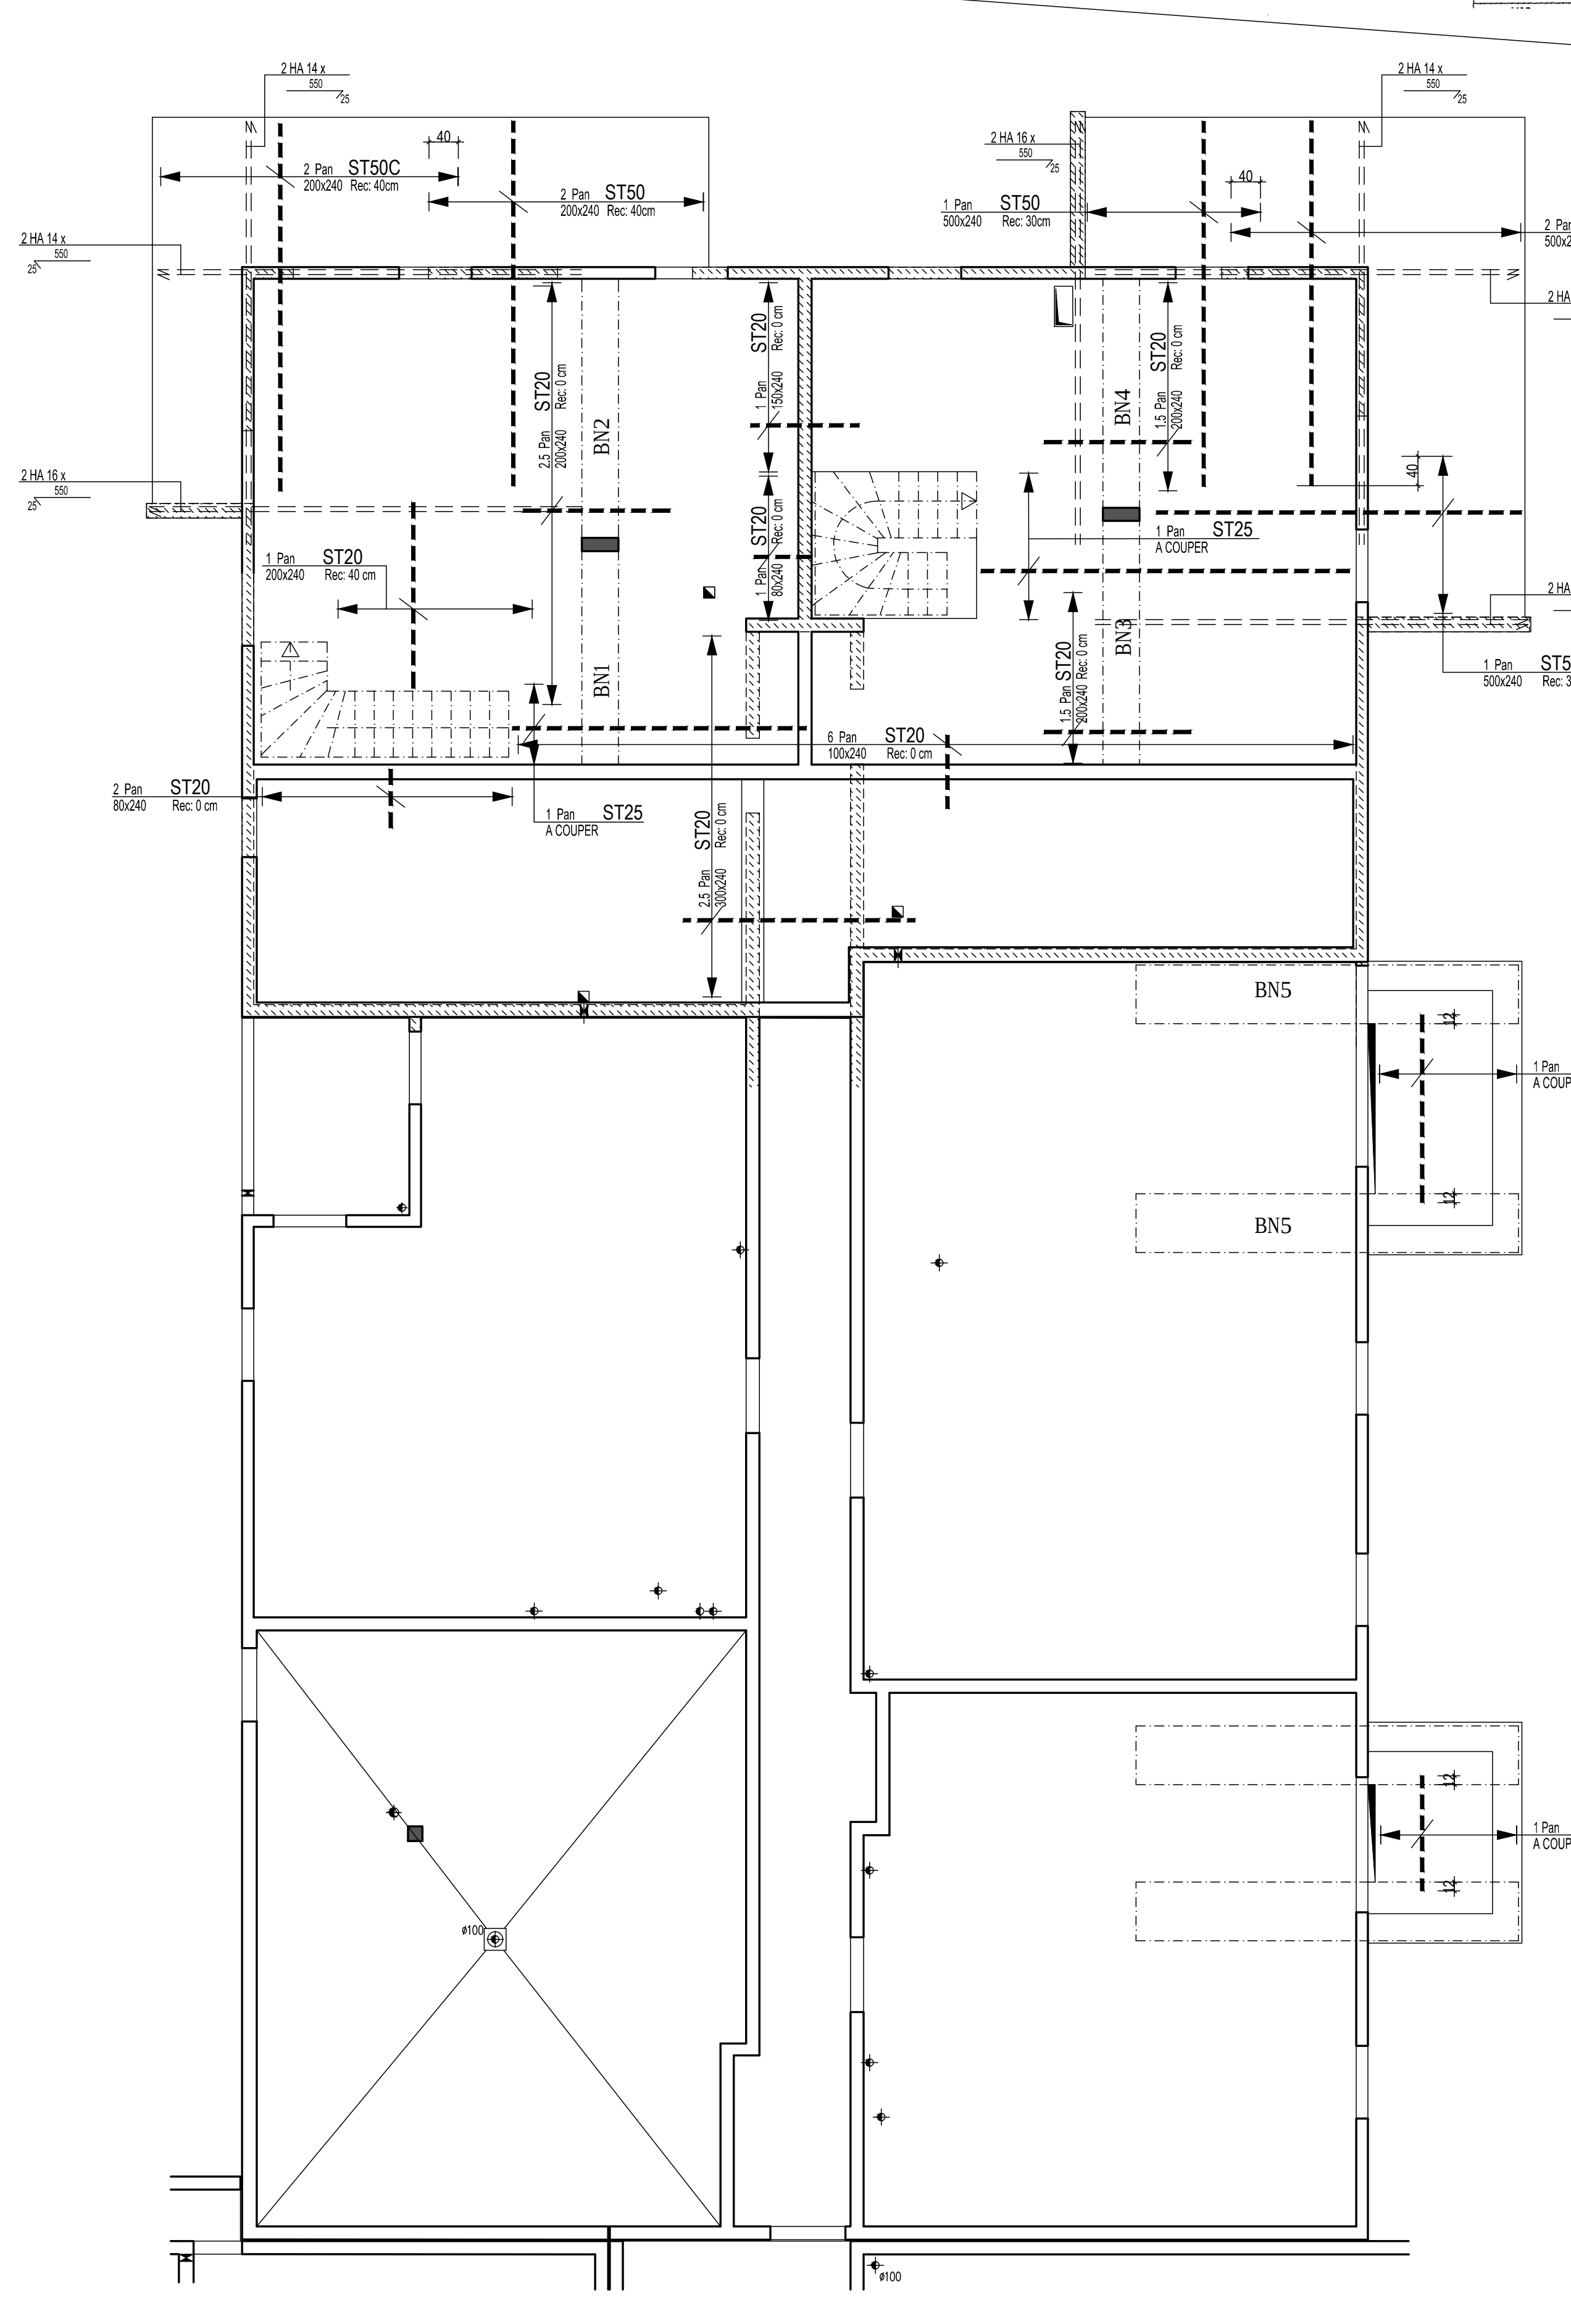
2 HA 14 x 550 25
2 Pan ST50C 200x240 Rec: 40cm
2 Pan ST50 200x240 Rec: 40cm
1 Pan ST50 500x240 Rec: 30cm
2 HA 16 x 550 25
2 Pan ST50C 500x240 Rec: 30cm
40
ST20 Rec: 0 cm
2.5 Pan 200x240
BN2
BN1
BN4
BN3
1 Pan 150x240
1 Pan 80x240
1.5 Pan 200x240
1 Pan ST20 200x240 Rec: 40 cm
1 Pan ST25 A COUPER
1.5 Pan ST20 200x240 Rec: 0 cm
1 Pan ST50 500x240 Rec: 30cm
6 Pan ST20 100x240 Rec: 0 cm
2 Pan ST20 80x240 Rec: 0 cm
2.5 Pan ST20 300x240 Rec: 0 cm
BN5
1 Pan ST25C A COUPER
ø100

NAPPE INFERIEURE

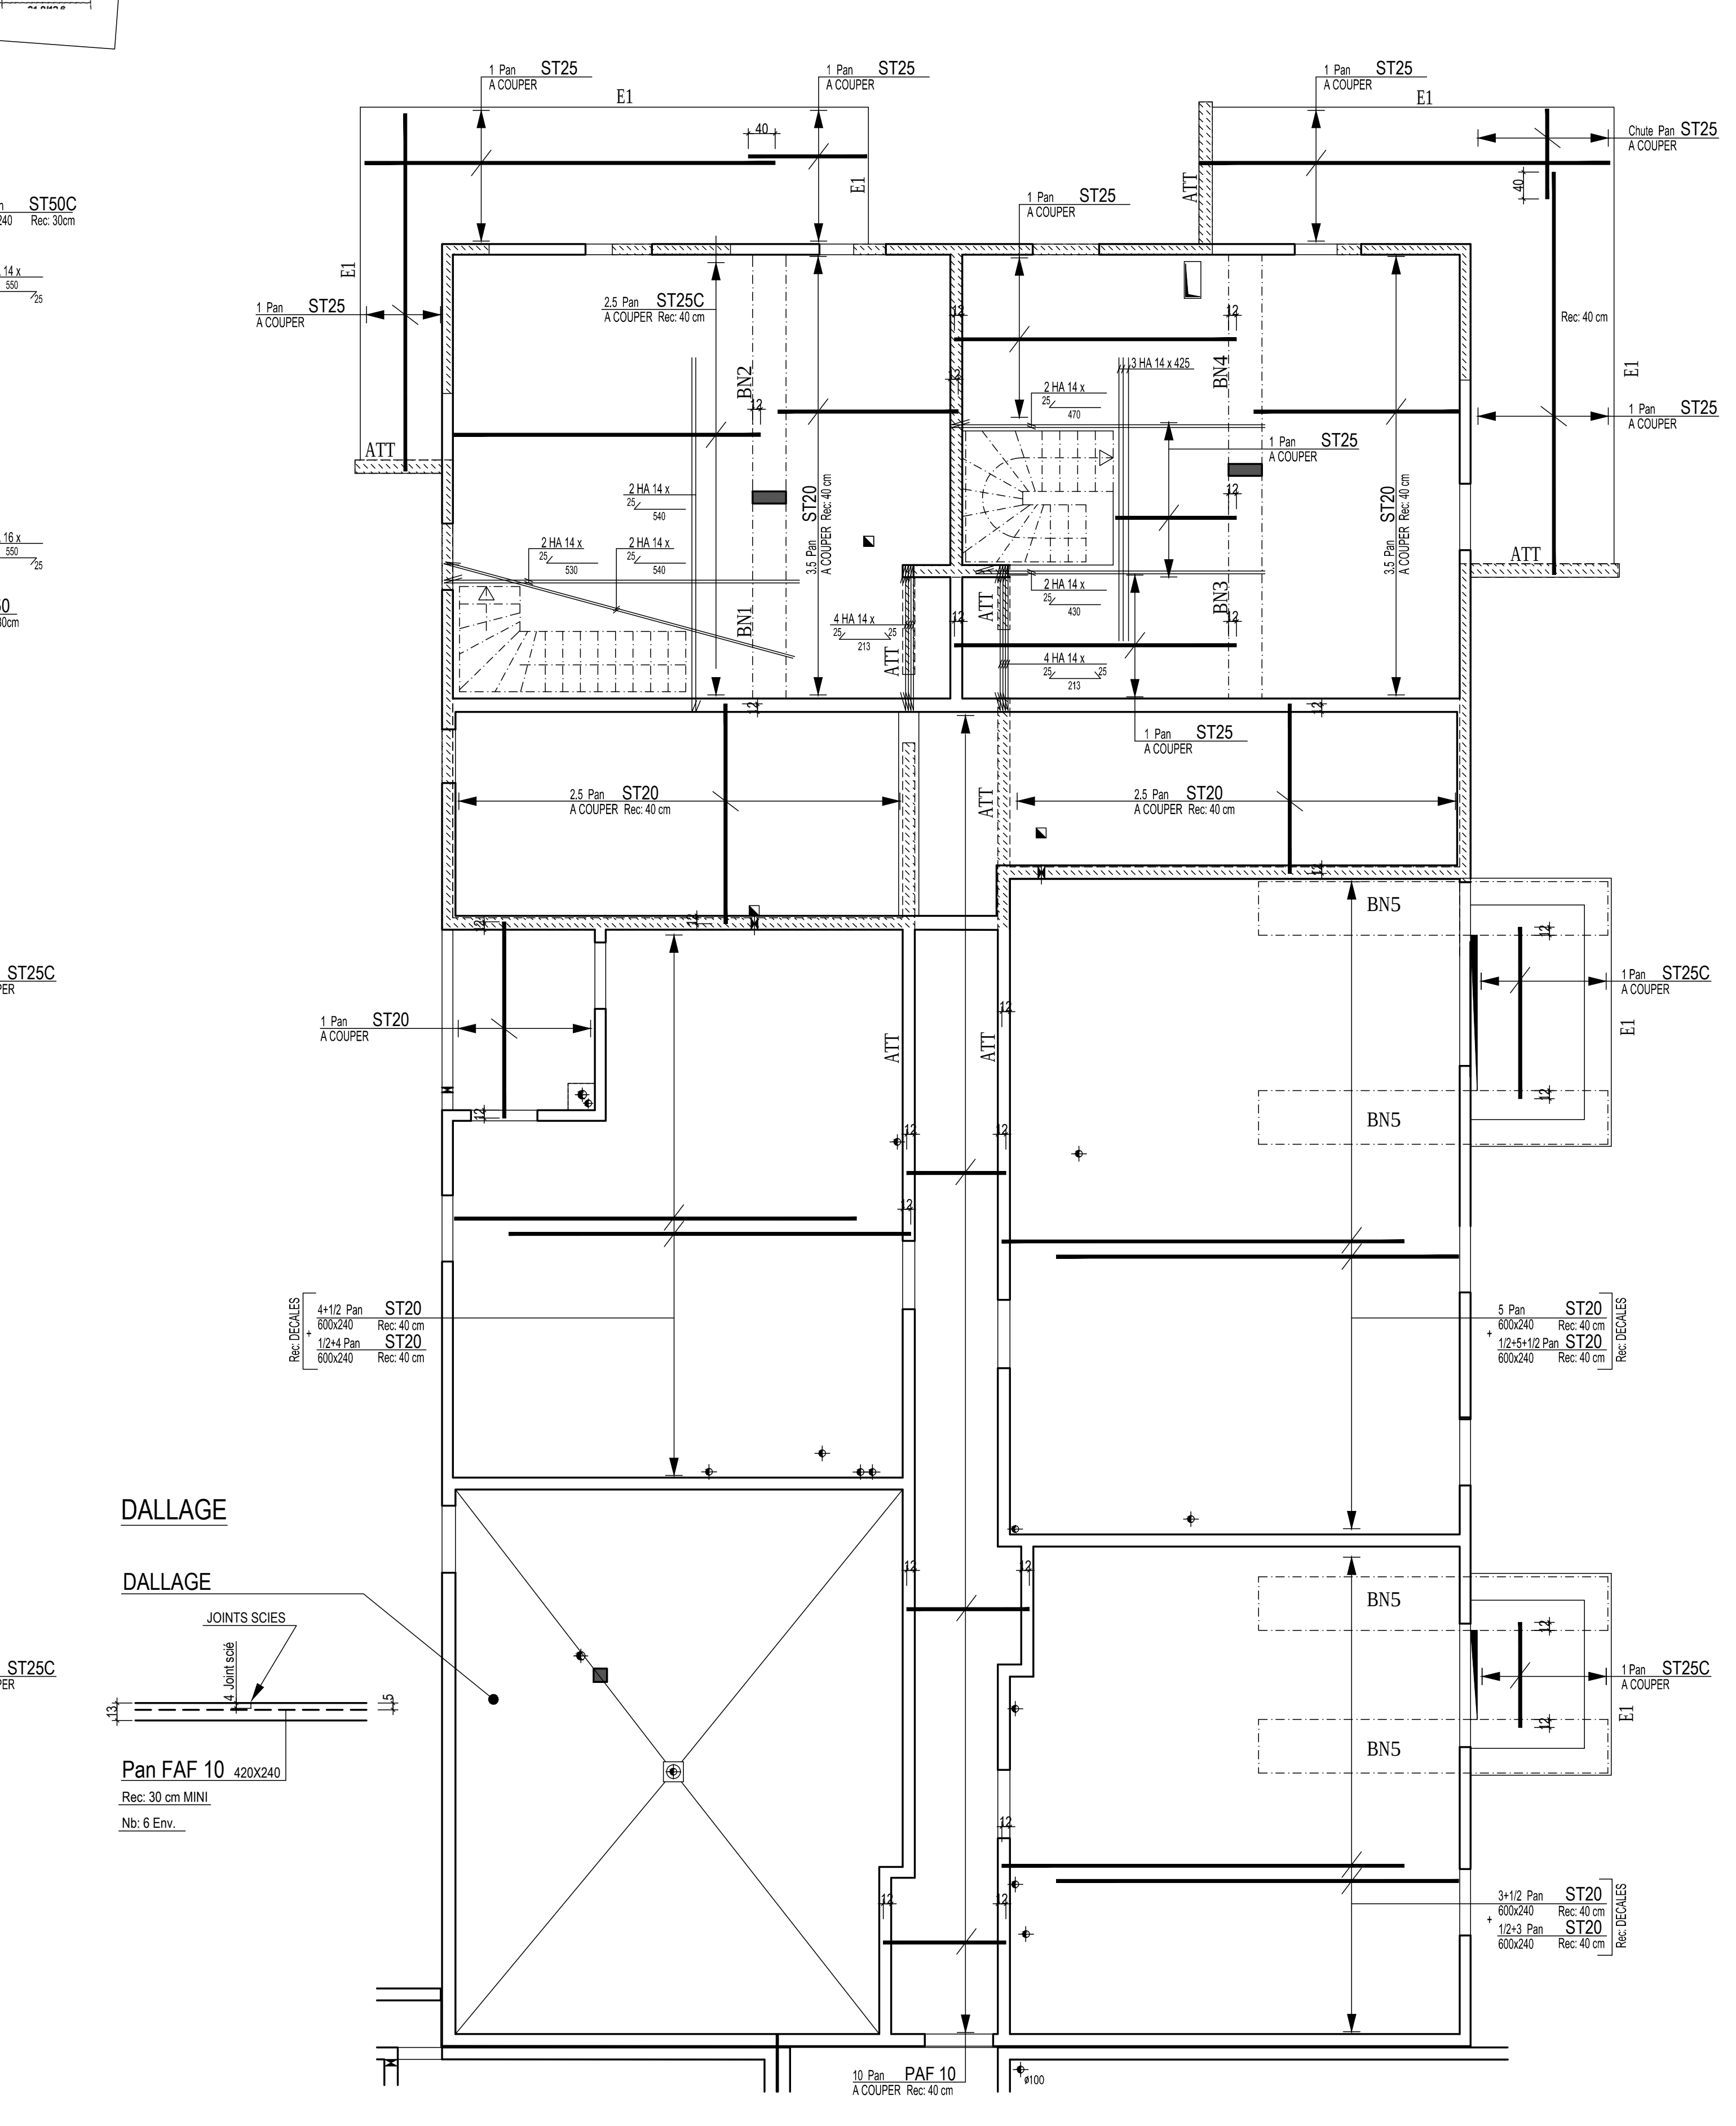
1 Pan ST25 A COUPER
E1
ATT
2.5 Pan ST25C A COUPER Rec: 40 cm
BN2
BN1
BN4
BN3
12
3 HA 14 x 425
2 HA 14 x 470
2 HA 14 x 540
2 HA 14 x 530
2 HA 14 x 430
4 HA 14 x 213
3.5 Pan ST20 A COUPER Rec: 40 cm
Chute Pan ST25 A COUPER
Rec: 40 cm
2.5 Pan ST20 A COUPER Rec: 40 cm
1 Pan ST20 A COUPER
4+1/2 Pan ST20 600x240 Rec: 40 cm
1/2+4 Pan ST20 600x240 Rec: 40 cm
Rec: DECALES
5 Pan ST20 600x240 Rec: 40 cm
1/2+5+1/2 Pan ST20 600x240 Rec: 40 cm
3+1/2 Pan ST20 600x240 Rec: 40 cm
1/2+3 Pan ST20 600x240 Rec: 40 cm
BN5
1 Pan ST25C A COUPER
10 Pan PAF 10 A COUPER Rec: 40 cm
ø100
DALLAGE
DALLAGE
JOINTS SCIES
4 Joint scié
13
5
Pan FAF 10 420X240
Rec: 30 cm MINI
Nb: 6 Env.

RENFORTS RESESERVATIONS JUSQU'A Ø200 mm

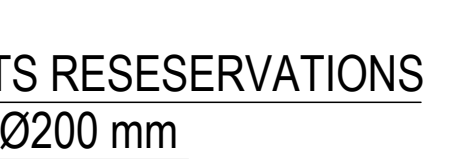

Principe de renfort aux droits des gaines:

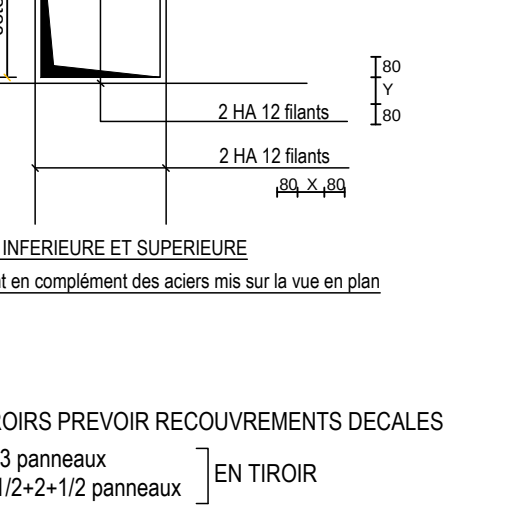
cote X
cote Y
2 HA 12 filants
2 HA 12 filants
80 Y 80
80 X 80

NAPPE INFERIEURE ET SUPERIEURE

NOTA: Ces renforts sont en complément des aciers mis sur la vue en plan

_PANNEAUX EN TIROIRS PREVOIR RECOUVREMENTS DECALES

EX: 1er Lit: 3 panneaux
2ème Lit: 1/2+2+1/2 panneaux] EN TIROIR

NOAHO

Chemin de Fontanière - 69350 La Mulatière

Création de logements

Les entreprises réalisant les travaux devront tenir compte des derniers plans architecte lors de la réalisation des travaux
Les plans du be MATTE ne doivent servir qu'au corps d'état concerné et doivent être des plans d'exécution.

ARCHITECTE(S): Atelier D'IS
BET STRUCTURE: MATTE SAS
BET FLUIDES: PRELEM
ECONOMISTE: EXECO
BUREAU DE CONTROLE: Bureau VERITAS
MO DELEGUE:
MOE: PSO Ingénierie
CSPS: SUD EST COORDINATION
OPC:
ENTREPRISE(S): Fontanel-pbc

Bât: C Aile EST
Dalle basse au -3 et Plancher sur -3
Armatures dalle

DOE

Contrainte de sol: 8 bars ELS
Aciers HA (T) FeE500
Aciers Doux (Ø) FeE 235
Aciers TS FeE 500
Béton fc28 >= 25MPa
Enrobage = 3 cm

INDICE	DATE	MODIFICATIONS
A		

PLAN N°
C11 0
DATE : 17/05/2015

MATTÉ
BUREAU D'ÉTUDES
STRUCTURES ET FLUIDES
119 BOULEVARD STALINGRAD 69100 VILLEURBANNE
Tél. 04 72 44 02 87 Fax 04 72 44 26 59
E-mail : bet@matte.fr

Dessiné par : J.BO
Contrôlé par : P.LIN
Echelle : 1/50°

Affaire N°
13.12.119