
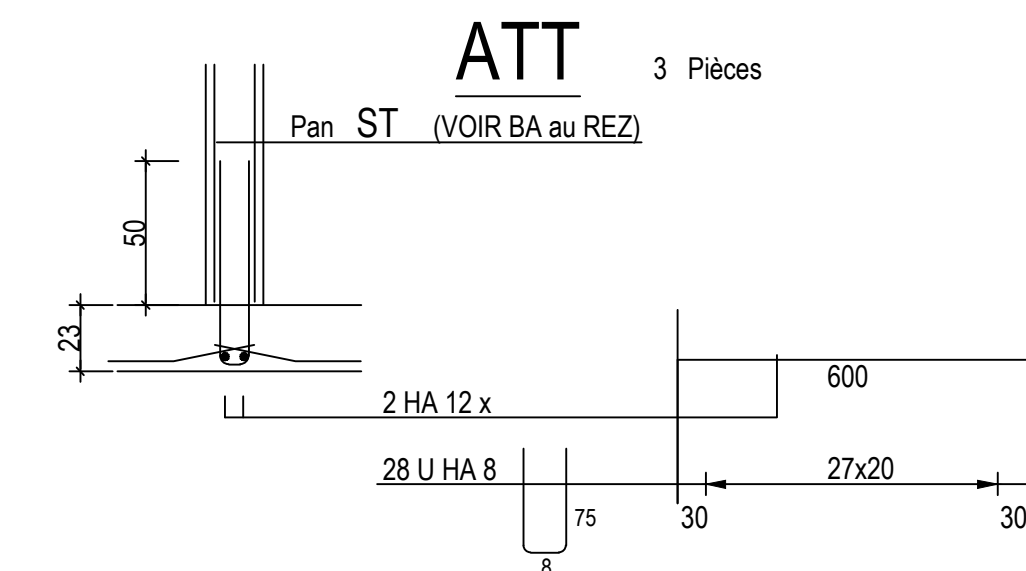


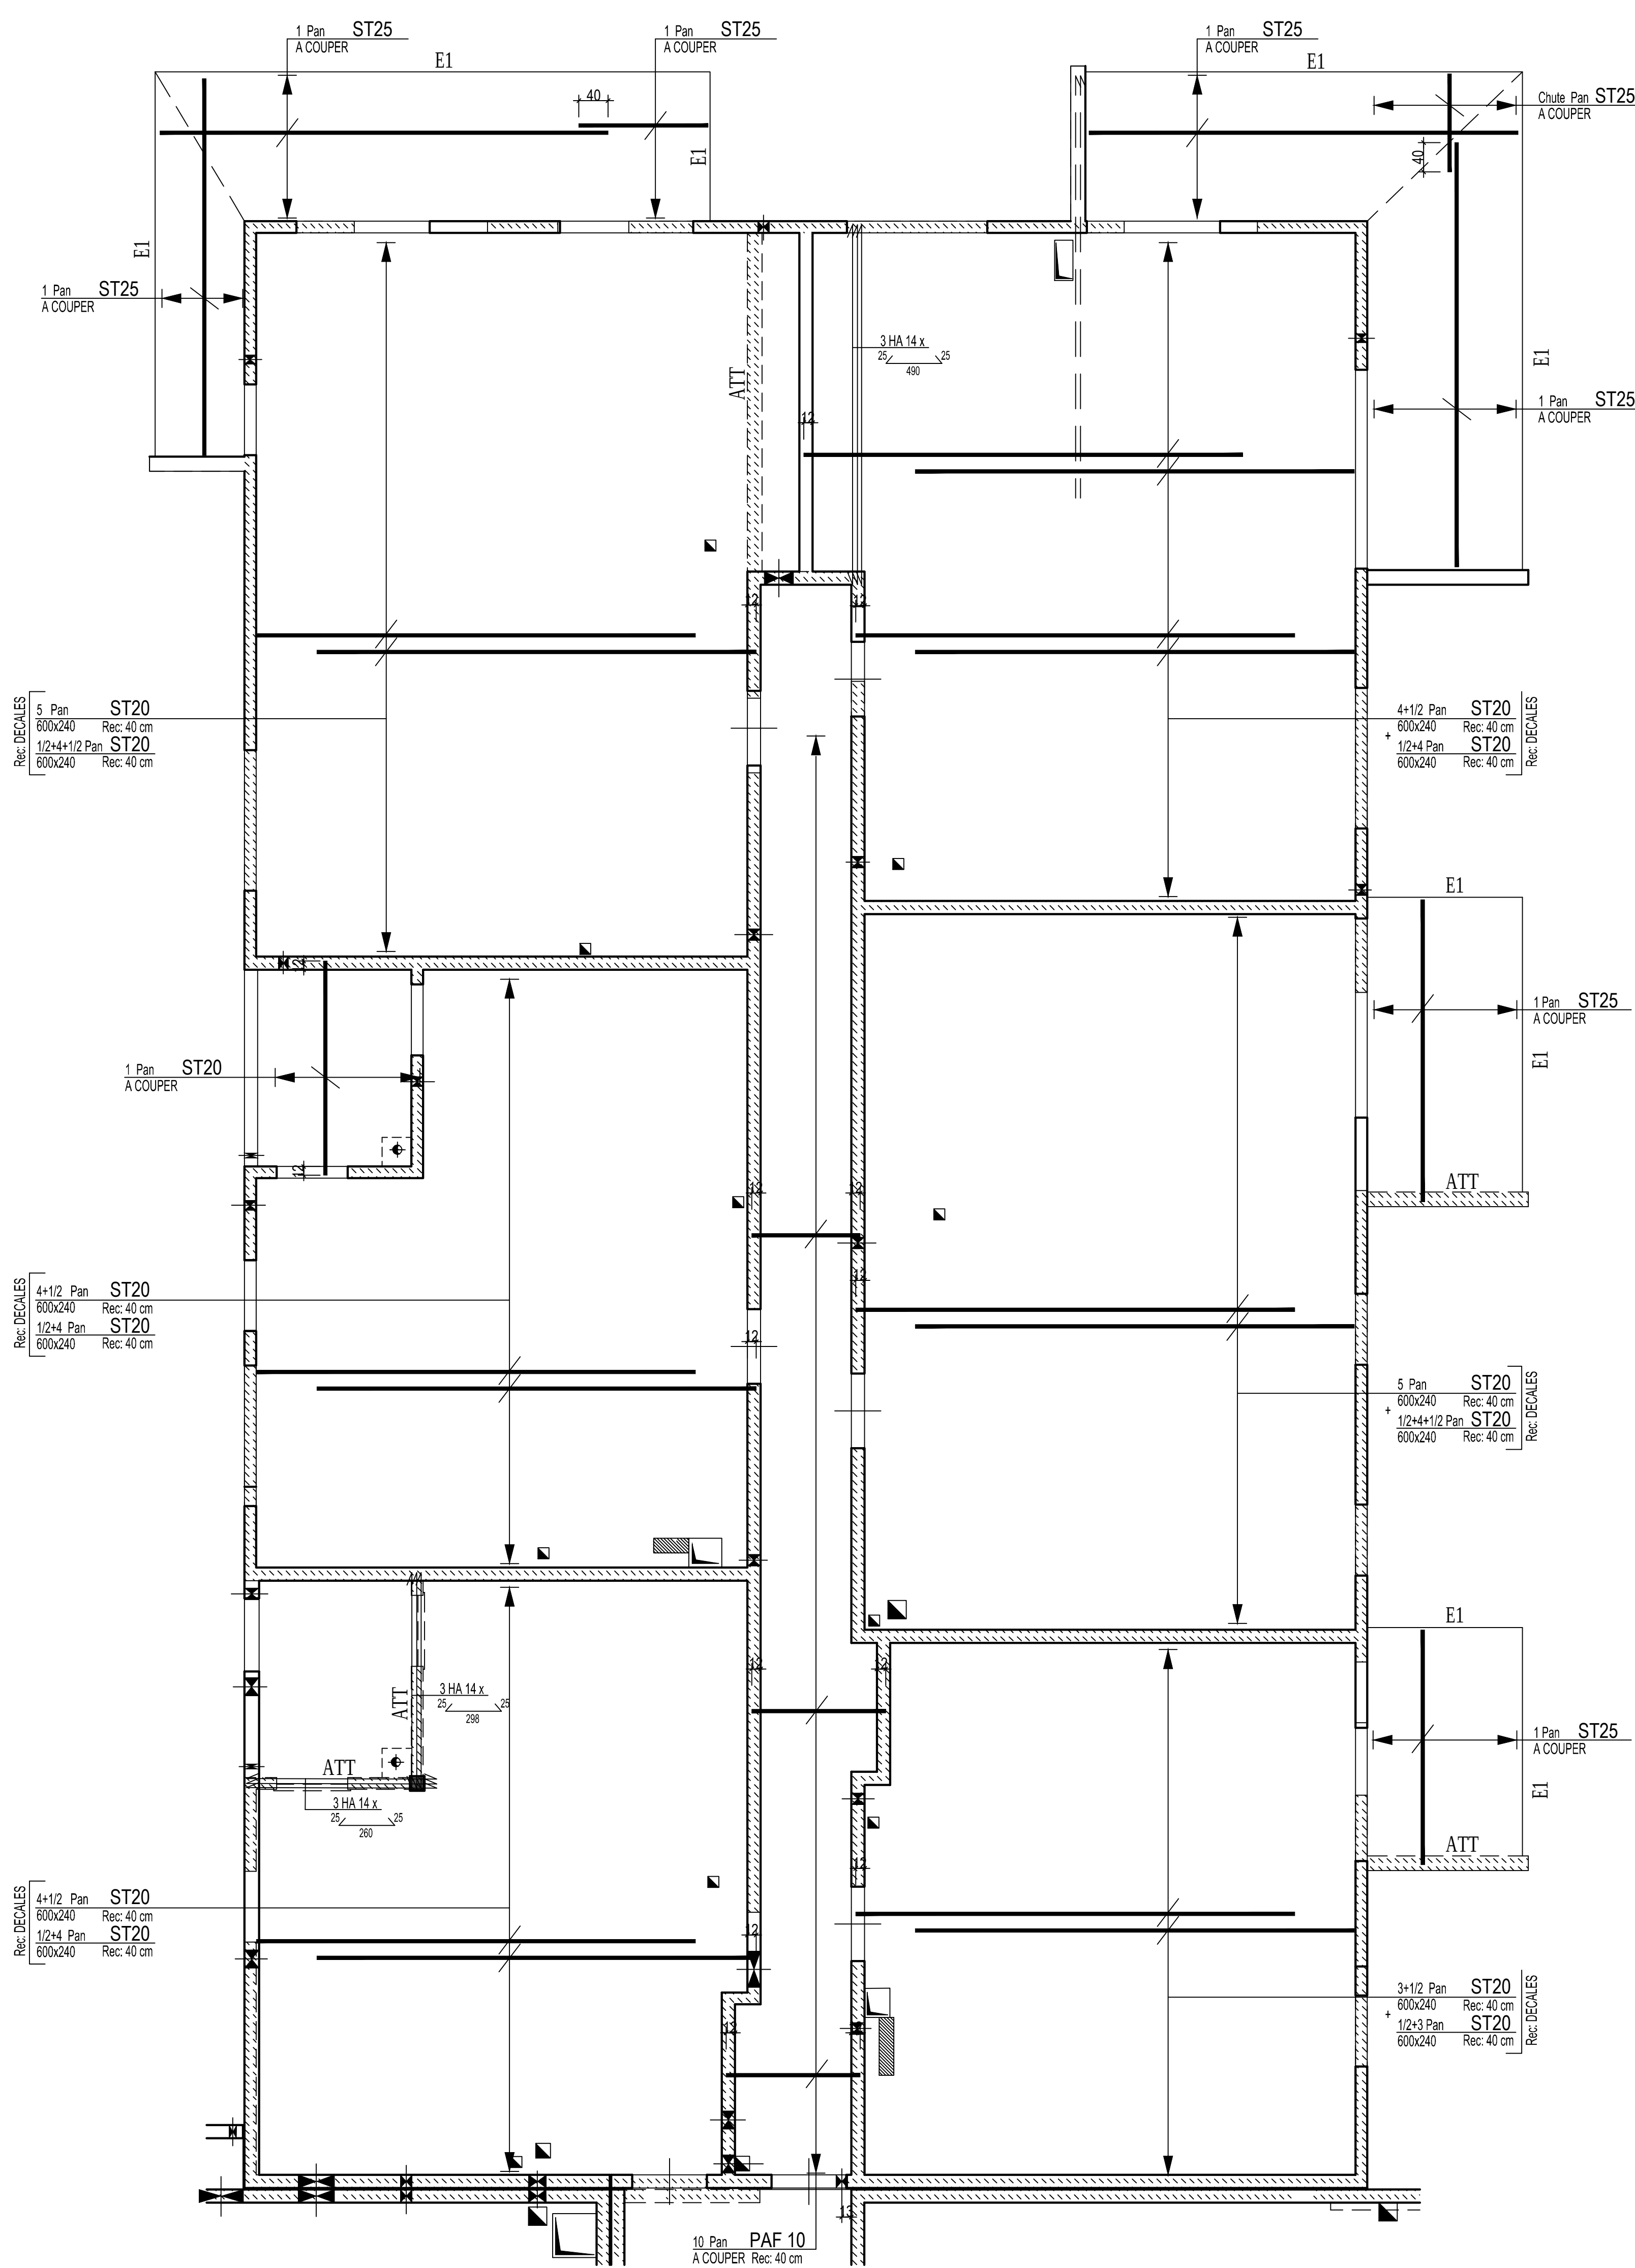

ATT 3 Pièces
(VOIR BA au REZ)

3 Pièces

Pan ST (VOIR BA au REZ

E1 7 p (A COUPER)
Rec: 50 cm

Rec: 50 c


Rec: 50 c

ANGLE E1


Nombre: 5

RECA T.S.		
PAF 10	420x240	3
ST20	600x240	65
ST25	600x240	8
ST30	600x240	0
ST35	600x240	0
ST50	600x240	8
ST60	600x240	0
ST15C	400x240	0
ST25C	600x240	0
ST40C	600x240	0
ST50C	600x240	4
ST65C	600x240	0

RENFORTS RESESERVATIONS
JUSQU'A Ø200 mm

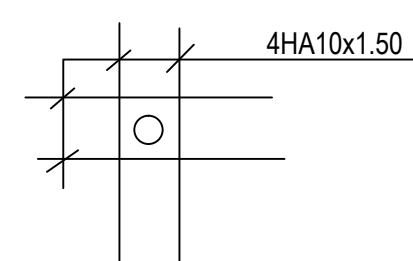

Principe de renfort aux droits des gaines:

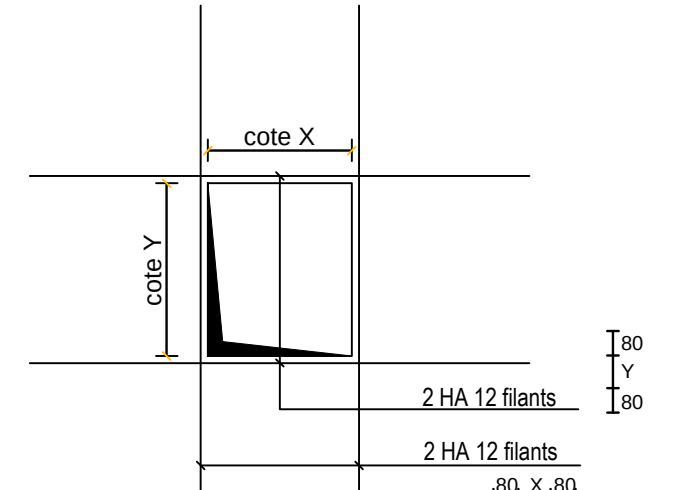

NAPPE INFÉRIEURE ET SUPÉRIEURE
NOTA: Ces renforts sont en complément des aciers mis sur la vue en plan

_PANNEAUX EN TIROIRS PREVOIR RECOUVREMENTS DECALES

EX: 1er Lit: 3 panneaux
2ème Lit: 1/2 + 2 + 1/2 panneaux

2ème Lit: 1/2+2+1/2 panneaux] en tôle

NOAHO

Chemin de Fontanière - 69350 La Mulatière

Création de logements

Les entreprises réalisant les travaux devront tenir compte des derniers plans architecte lors de la réalisation des travaux.
Les plans du be MATTE ne doivent servir qu'au corps d'état concerné et doivent être des plans d'exécution.

ARCHITECTE(S):	Atelier D'IS	MO DELEGUE:	
BET STRUCTURE:	MATTE SAS	MCE:	PSO Ingénierie
BET FLUIDES:	PRELEM	CSPS:	SUD EST COORDINATION
ECONOMISTE:	EXECO	OPC:	
BUREAU DE CONTROLE:	Bureau VERITAS	ENTREPRISE(S):	Fontanel-pbc

Bât: C Aile

Plancher sur -2
Armatures dalle

INDICE	DATE	MODIFICATO
A		

MATTÉ
BUREAU D'ÉTUDES

STRUCTURES ET FLUIDES
119 BOULEVARD STALINGRAD 89100 VILLEURBANNE
Tél. 04 72 44 02 87 Fax 04 72 44 26 59
E-mail : bat@brest.fr

MO DEPOSE:
MCE: PSO Ingénierie
CSPS: SUD EST COORDINATION
OPC:
ENTREPRISE(S): Fontanel-pbc

DO

CONTRA

PLAN N°
C12 0
DATE : 18/05/20

Dessiné par : J.BO
Contrôlé par : P.LIN

Echelle : 1/50°