



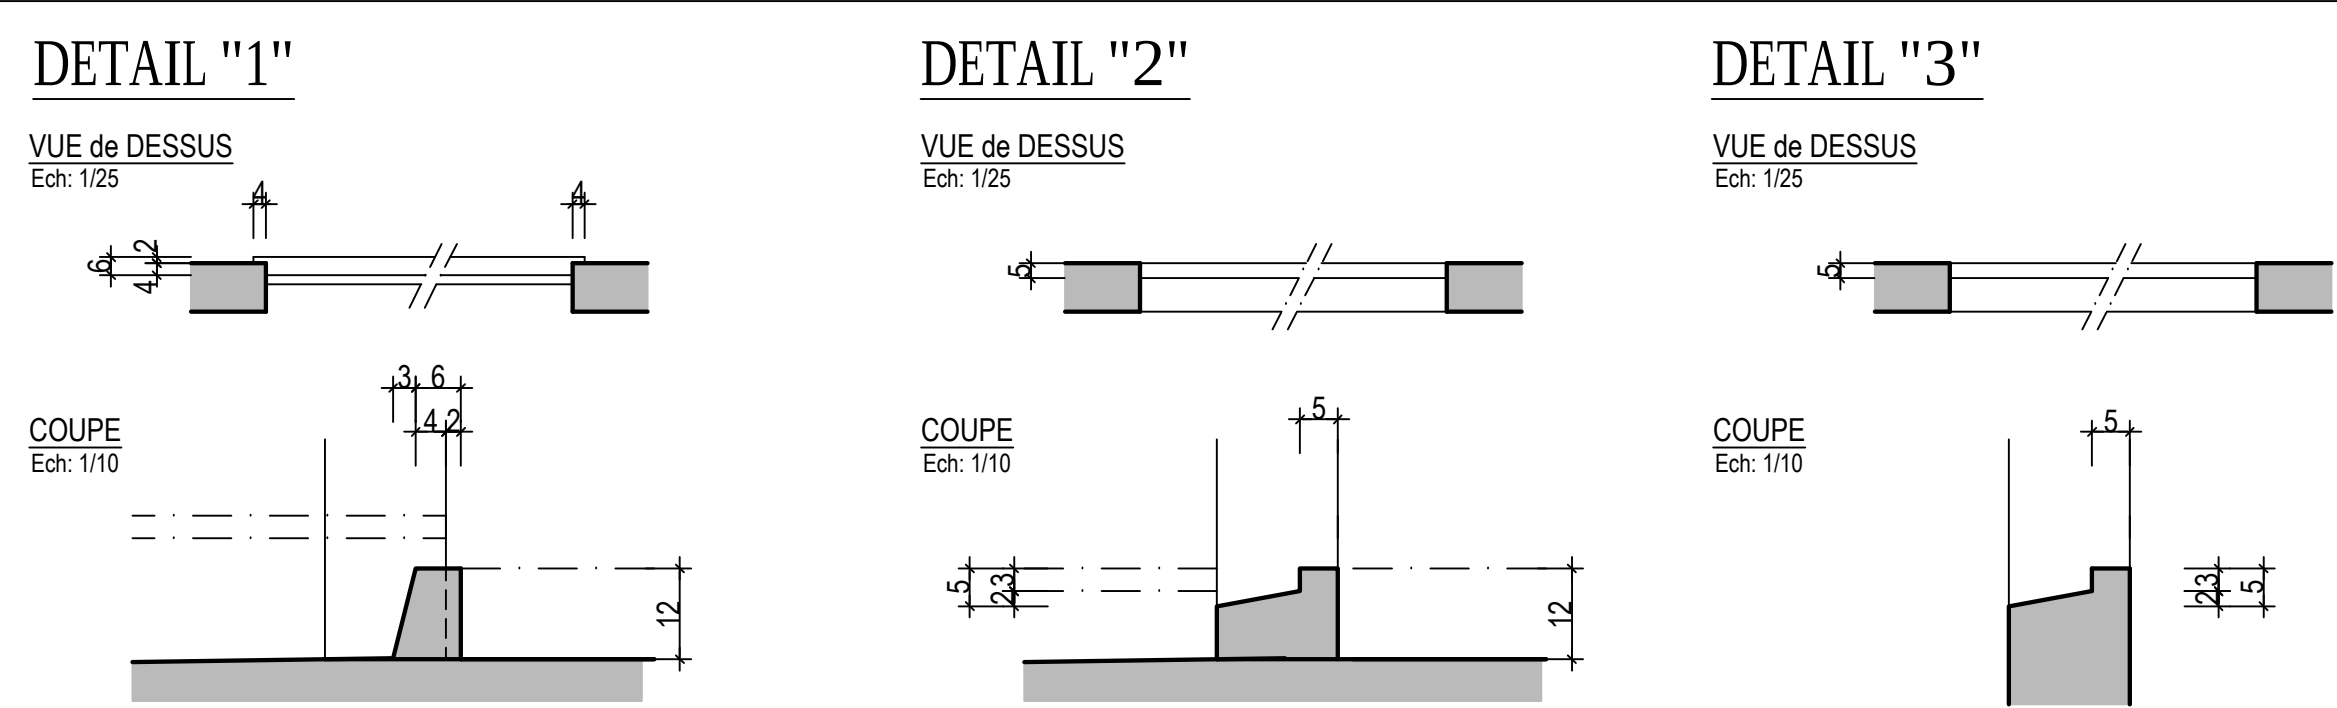

VUE EN PLAN FONDATIONS

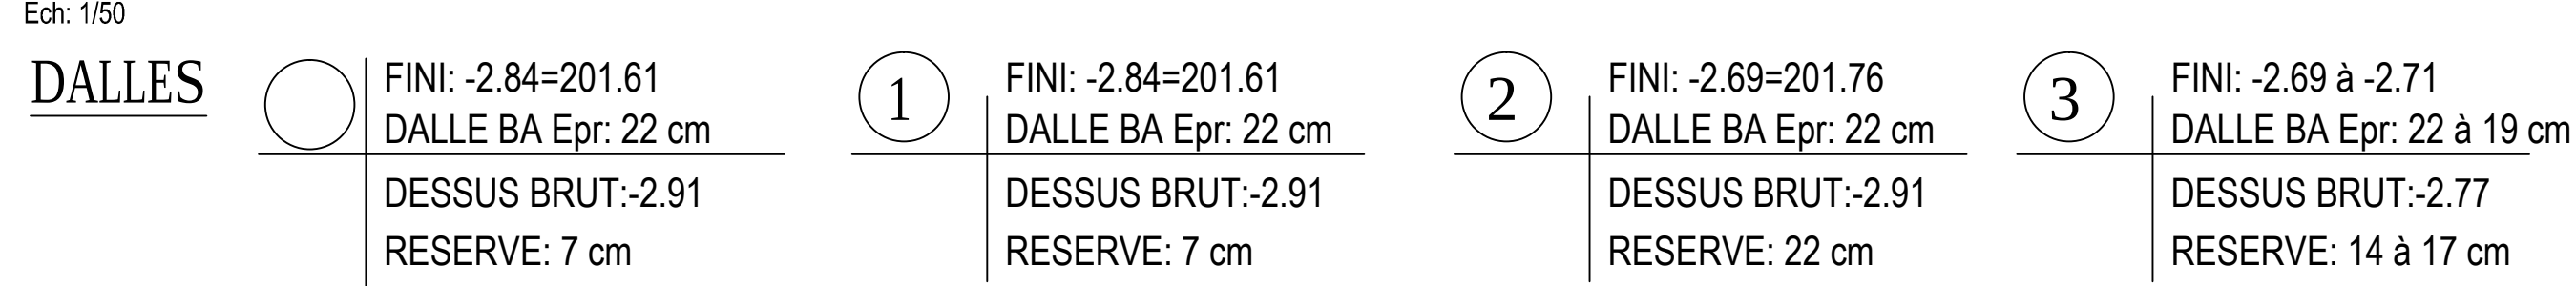

DETAIL "A"

Ech: 1/25

PAREMENT de FINITION

PAREMENT PLISSE

1300 Ent. MUR PAREMENT ASPECT PLISSE

1300 Ent. MUR PAREMENT ASPECT PLISSE

COUPE A

Ech: 1/25

COUPE B

Ech: 1/25

COUPE C

Ech: 1/25

COUPE D

Ech: 1/25

COUPE E

Ech: 1/25

COUPE F

Ech: 1/25

COUPE G

Ech: 1/25

COUPE H

Ech: 1/25

COUPE J

Ech: 1/25

COUPE K

Ech: 1/25

COUPE L

Ech: 1/25

COUPE M

Ech: 1/25

COUPE N

Ech: 1/25

COUPE P

Ech: 1/25

COUPE LINTEAUX INTERIEURS

Ech: 1/25

NOAHO

Chemin de Fontanière - 69350 La Mulatière

Création de logements

Les entreprises réalisant les travaux devront tenir compte des derniers plans architecturaux lors de la réalisation des travaux. Les plans du BAT MATTE ne doivent servir qu'à titre consultatif et doivent être en accord avec les plans d'exécution.

ARCHITECTES: Atelier DTS
BET STRUCTURE: MATTE SAS
BET FLUIDES: PRELEM
ECONOMISTE: EXECO
BUREAU DE CONTROLE: Bureau VERITAS

MO DELEGUE: PSD Ingénierie
MODE: CSFS
SUD EST COORDINATION: OPC
ENTREPRISES: Fontanel pbc

Bât: C Aile EST
PLANCHER SUR -2
Coffrage

INCDCE	DATE	MODIFICATIONS
A	19/06/2015	AJOUTE OUVERTURE SUIVANT A
B	26/06/2015	Ajoute reperage et mise à jour hauteurs ouvertures
C	02-07-2015	Ajoute réservations ELECTRICITE

MATTÉ
BUREAU D'ETUDES
STRUCTURES ET FLUIDES
119 BOULEVARD PAUL MONTAUDO 69100 VILLEURBANNE
Tél. 04 72 44 50 91 Fax 04 72 44 26 99
E-mail: mat@matte.fr

DOE

Contrainte de voir 8 dans ELS

Aciers HA (T) F4E500

Aciers Doux (B) F4E235

Aciers TS F4E 500

30cm L28 -> 20kPa

Enrèlage = 1cm

PLAN N°

C13 C

DATE : 16/06/2015

Affaire N°

13.12.119