

NOAHO

Chemin de Fontanière - 69350 La Mulatière

Création de logements

Les entreprises réalisant les travaux devront tenir compte des derniers plans architecte lors de la réalisation des travaux
Les plans du be MATTE ne doivent servir qu'au corps d'état concerné et doivent être des plans d'exécution.

ARCHITECTE(S): Atelier D'IS
BET STRUCTURE: MATTE SAS
BET FLUIDES: PRELEM
ECONOMISTE: EXECO
BUREAU DE CONTROLE: Bureau VERITAS

MO DELEGUE:
MOE: PSO Ingénierie
CSPS: SUD EST COORDINATION
OPC:
ENTREPRISE(S): Fontanel-pbc

Bât: C Aile EST
BA au -2

INDICE	DATE	MODIFICATIONS
A		

MATTÉ
BUREAU D'ÉTUDES
STRUCTURES ET FLUIDES

119 BOULEVARD STALINGRAD 69100 VILLEURBANNE
Tél. 04 72 44 02 87 Fax 04 72 44 26 59
E-mail : bet@matte.fr

Dessiné par : J.BO
Contrôlé par : P.LIN
Echelle : 1/50°

DOE

Contrainte de sol: 8 bars ELS

Aciers HA (T) FeE500
Aciers Doux (Ø) FeE 235
Aciers TS FeE 500
Béton fc28 >= 25MPa
Enrobage = 3 cm

PLAN N°
C14 0




DATE : 17/05/2015

Affaire N°
13.12.119

MURS EXTERIEURS

ANGLES MURS

ARMATURES TETES DE MURS
et OUVERTURES

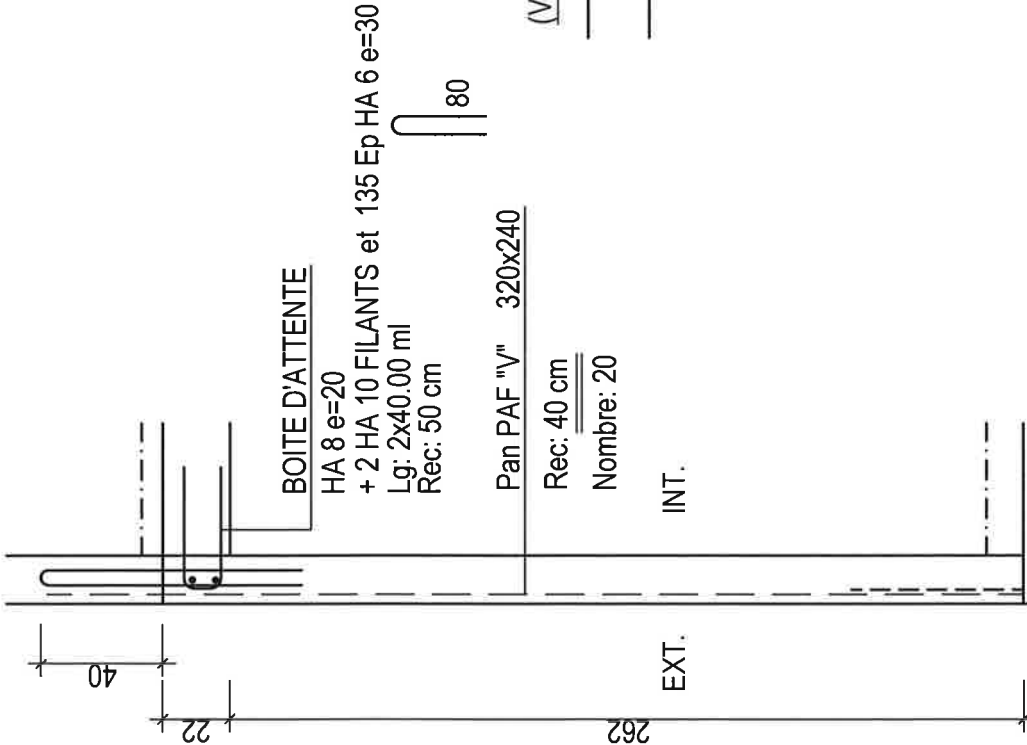
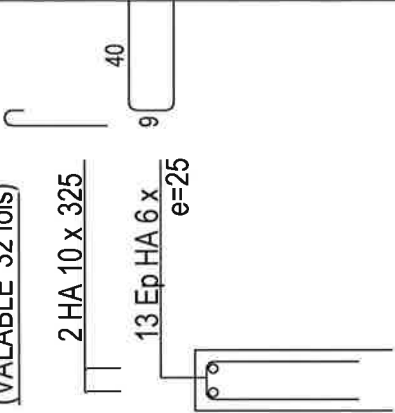
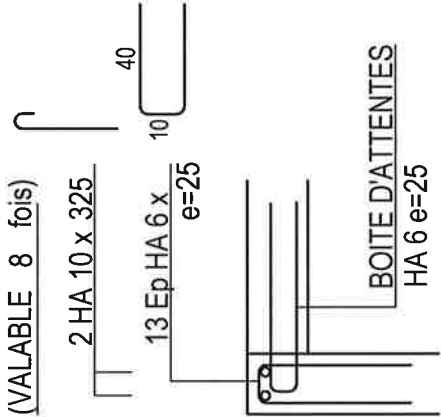


M1



ANGLES MURS

ARMATURES TETES DE MURS
et OUVERTURES

(VALABLE 1 fois)

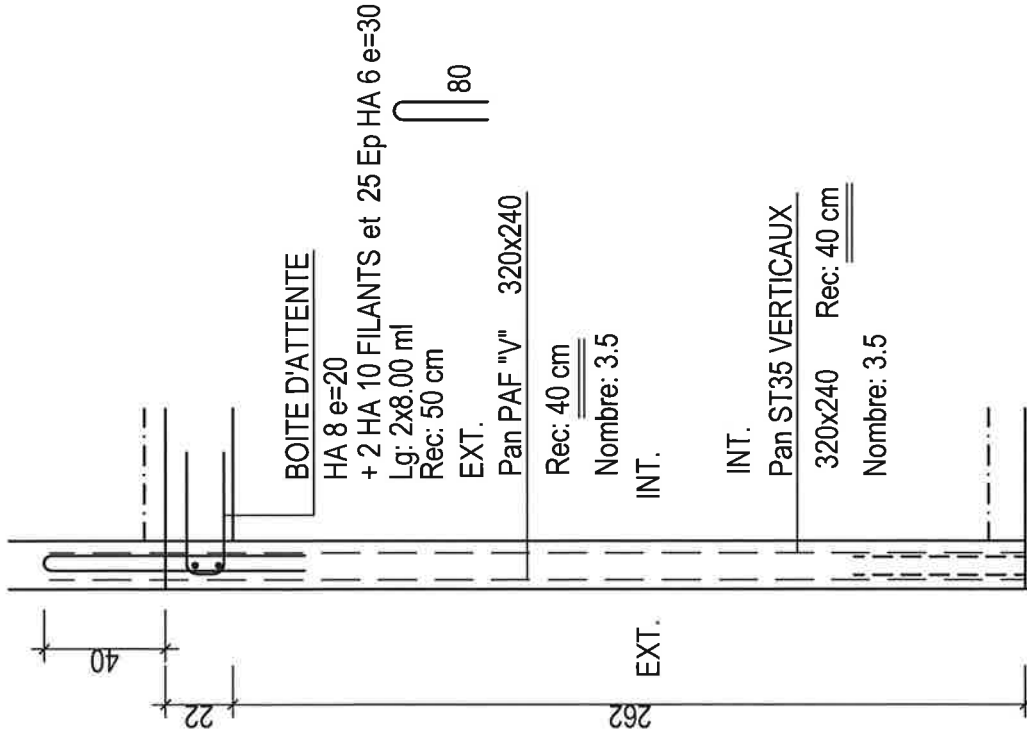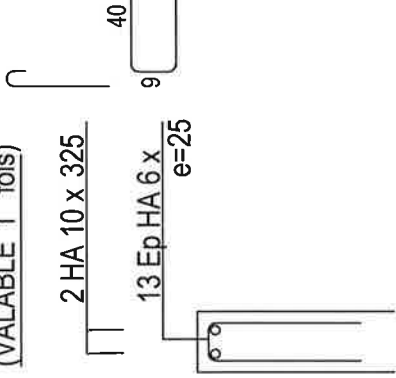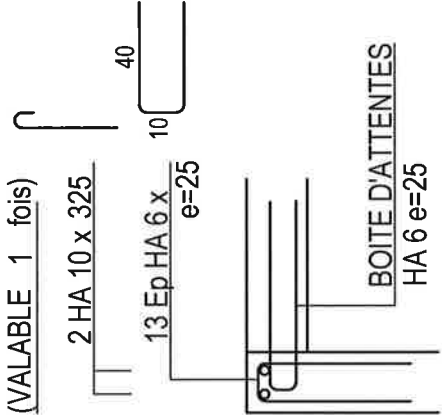

POUTRE VOILE : PV1

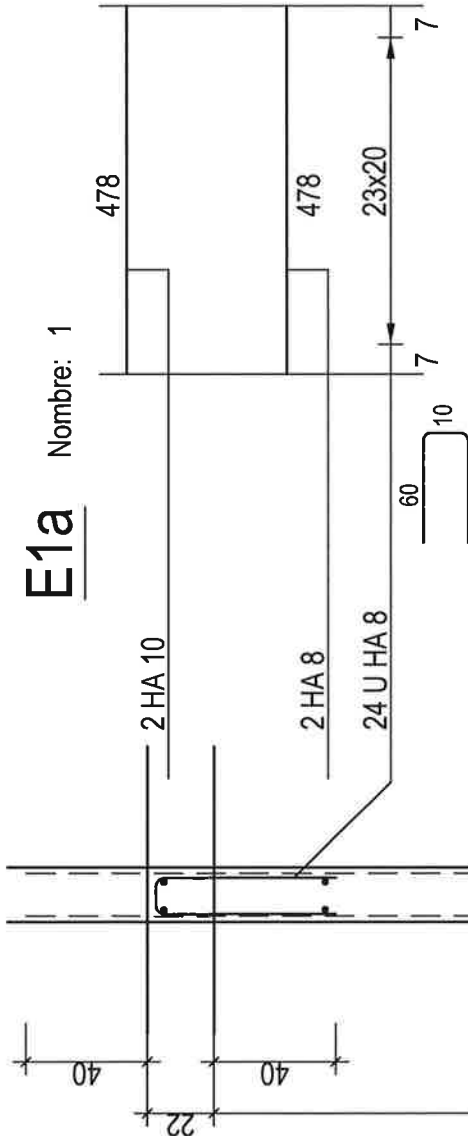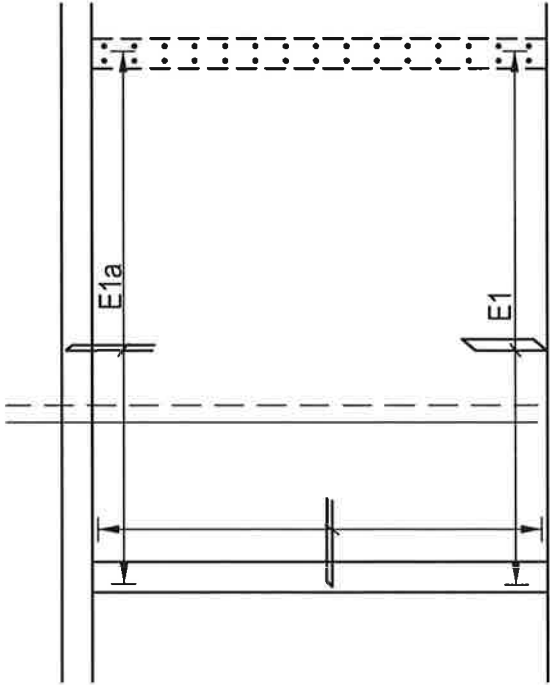


CHAQUE FACE


Pan ST25C A COUPER

Rec: 40 cm


Nombre: 2x2.5

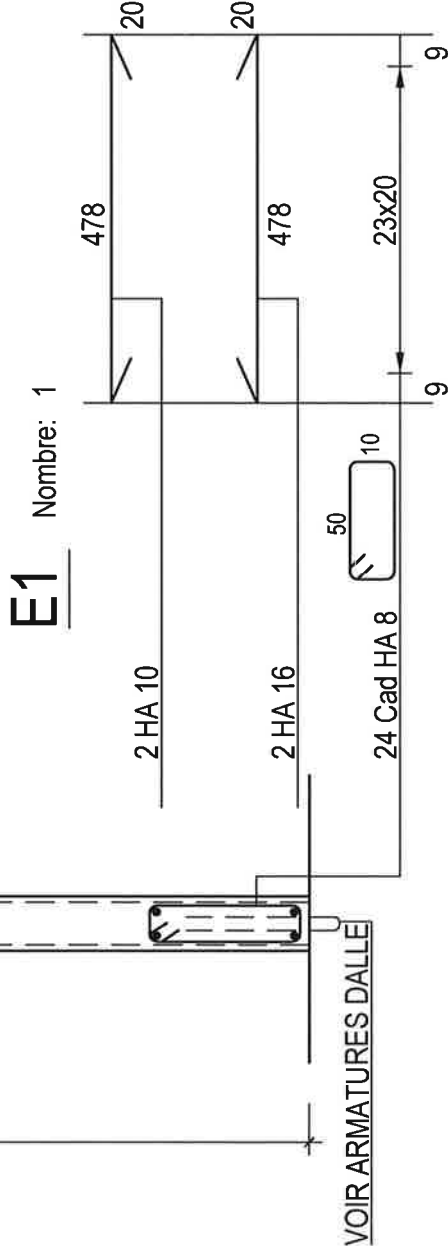


POUTRE VOILE : PV2

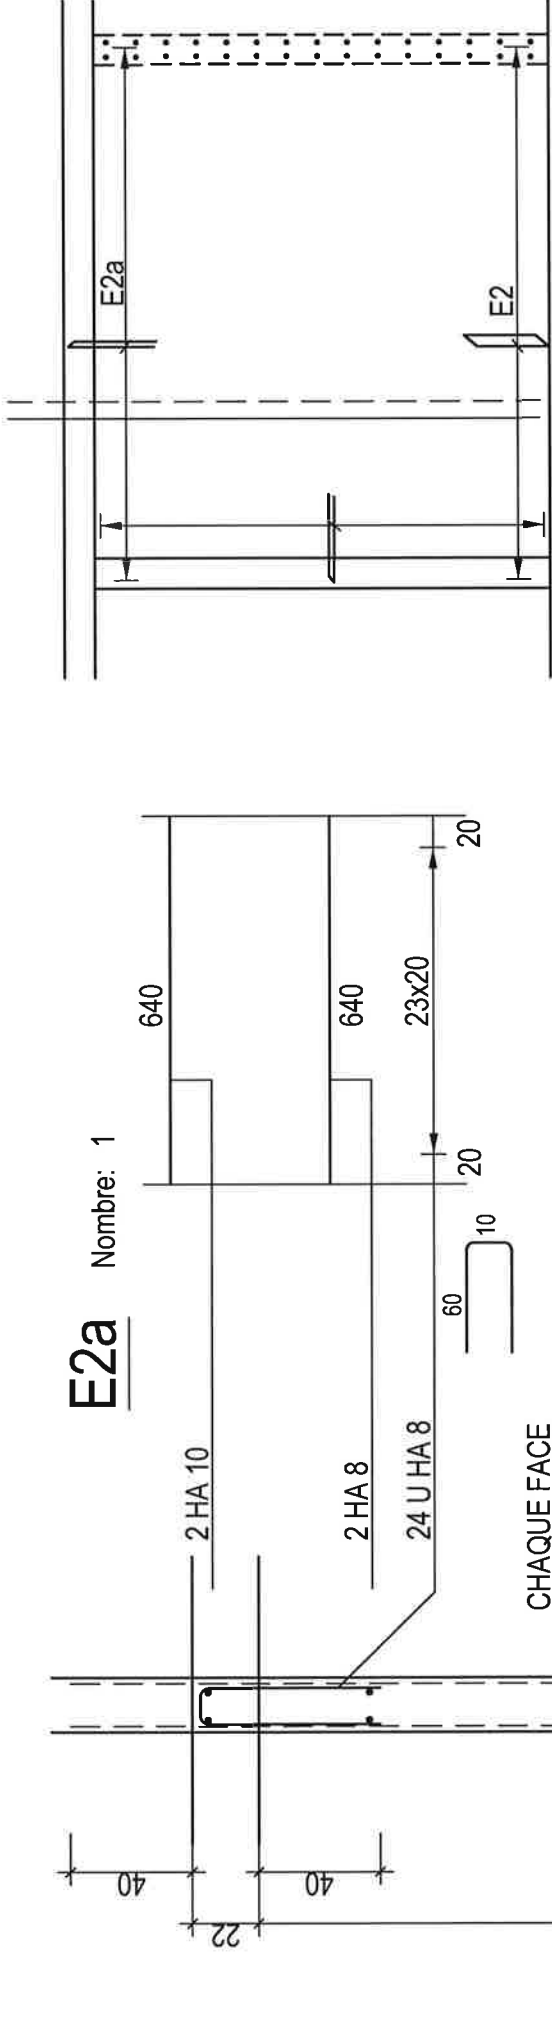

POUTRE VOILE : PV3

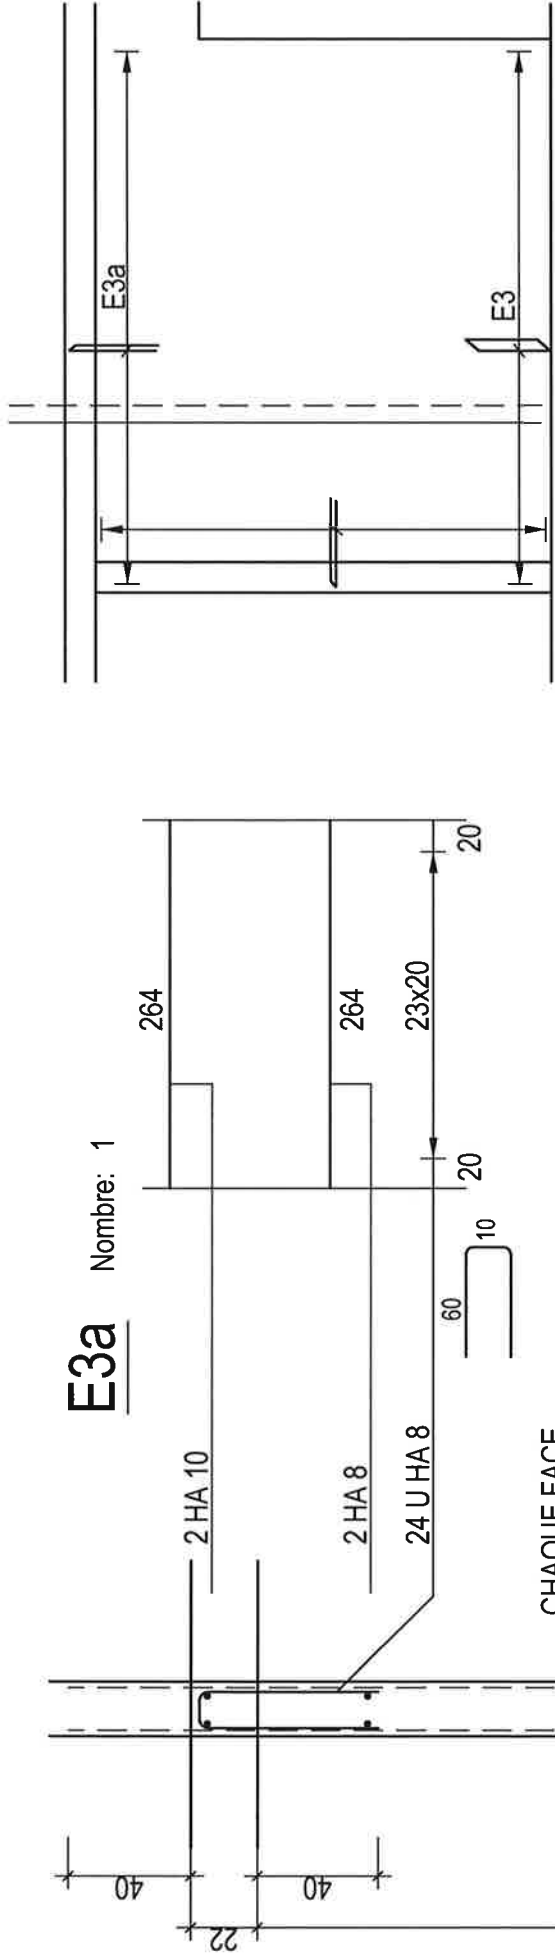



CHAQUE FACE
Pan ST25C A COUPER
Rec: 40 cm
Nombre: 2x1

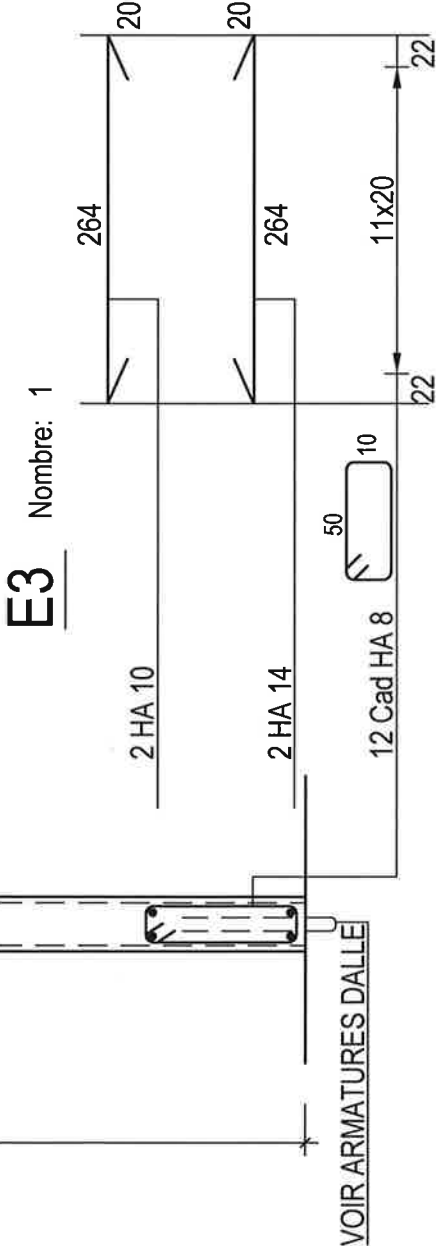

VOIR ARMATURES DALLE


ELEVATION

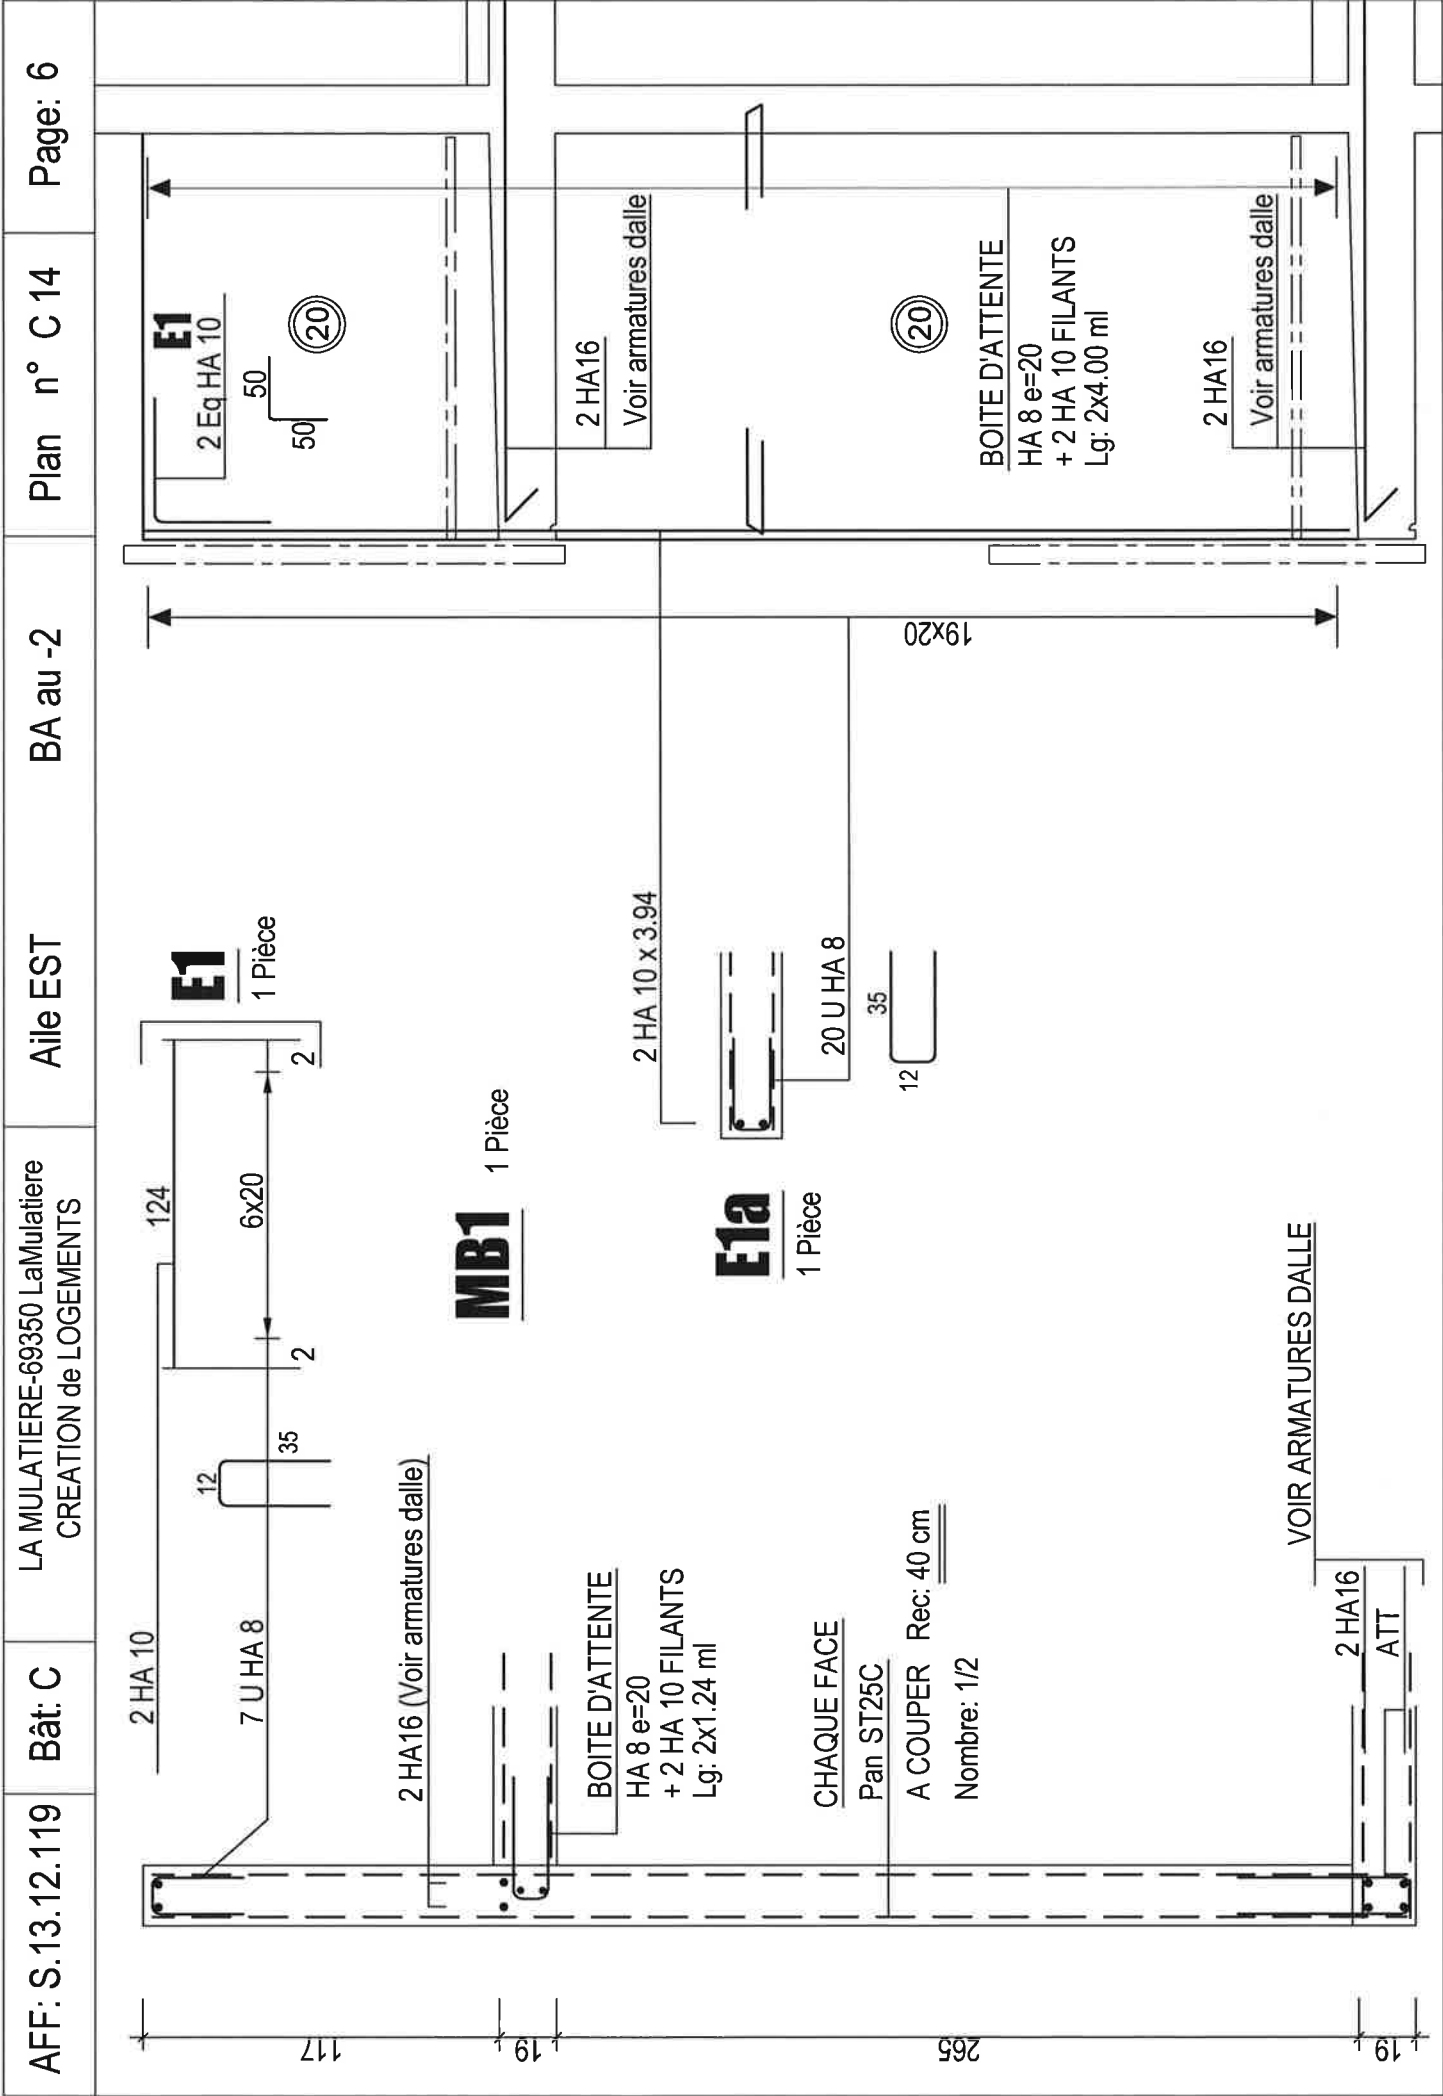

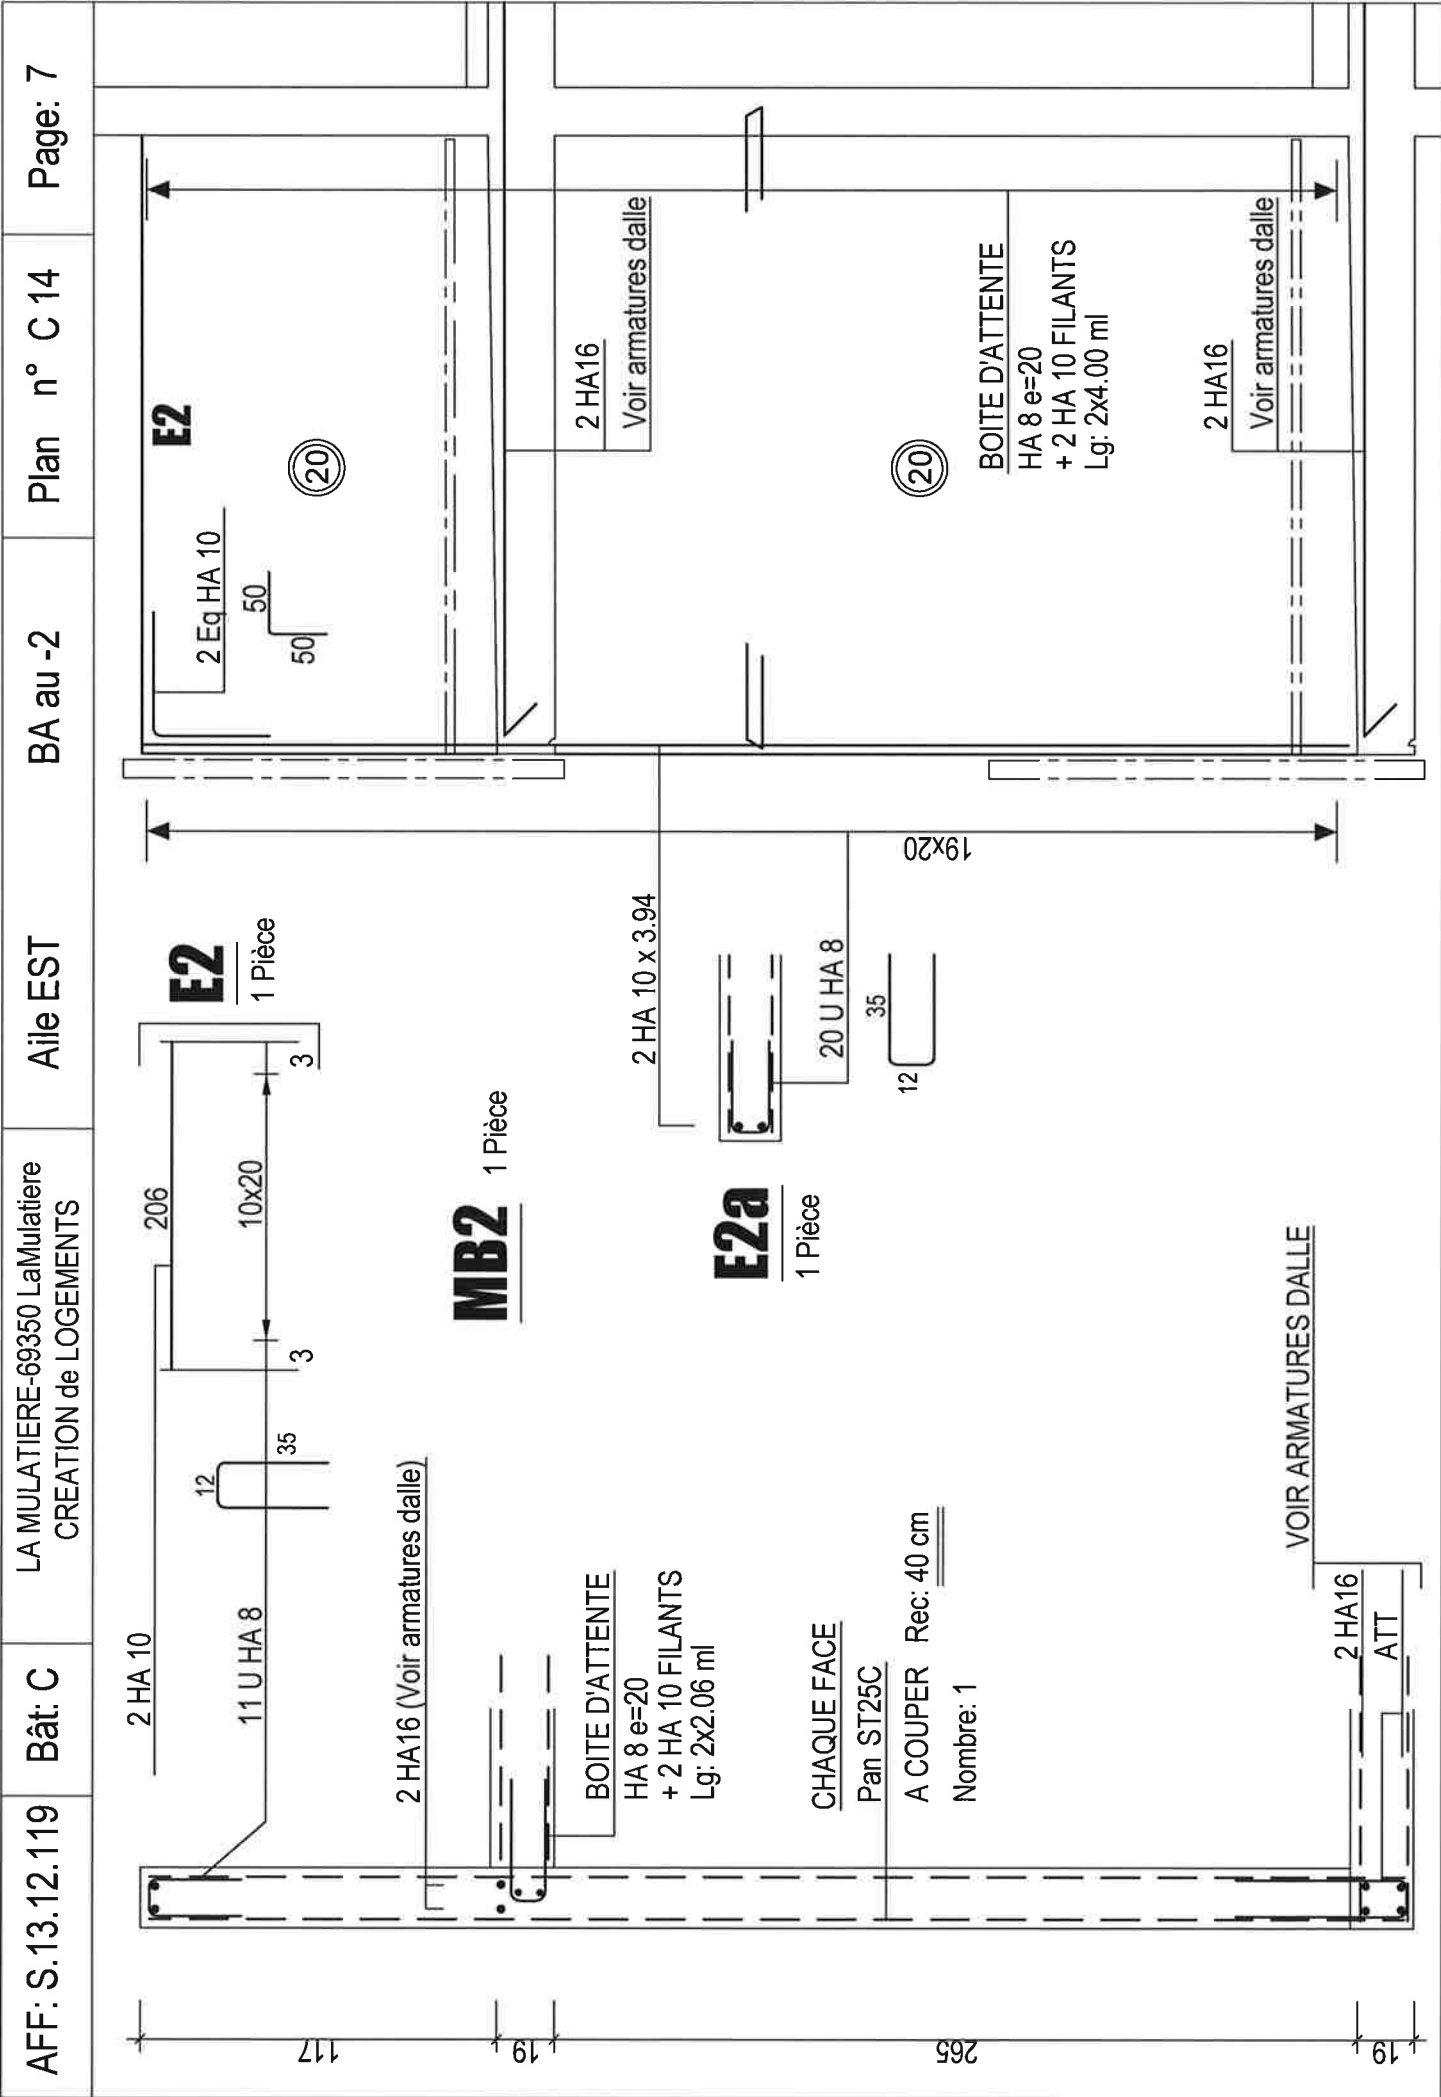


MURS INTERIEURS AVEC CONTINUITE


75.00 ml Env:

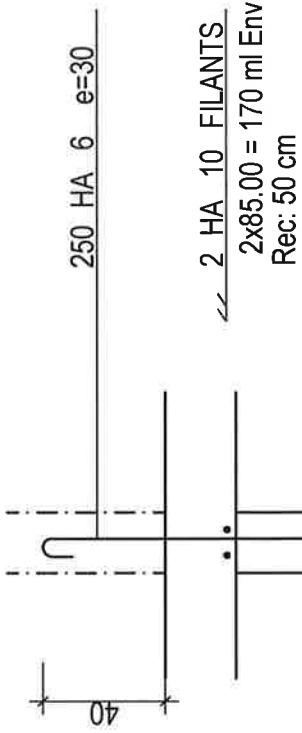


ARMATURES TETES DE MURS

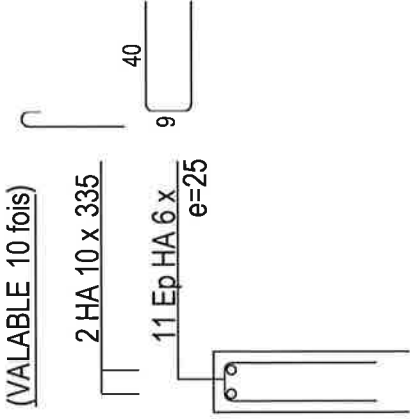


ANGLES MURS

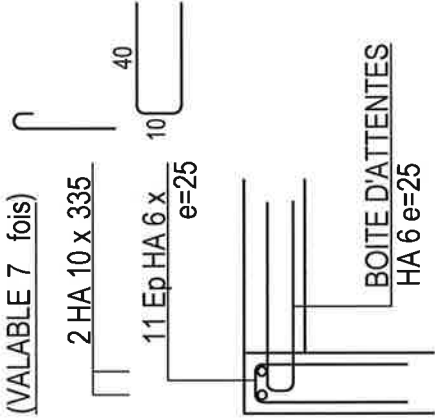



(VALABLE 7 fois)

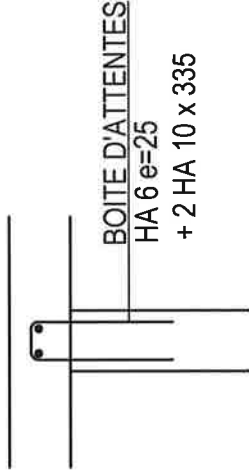

MURS INTERIEURS SANS CONTINUITE

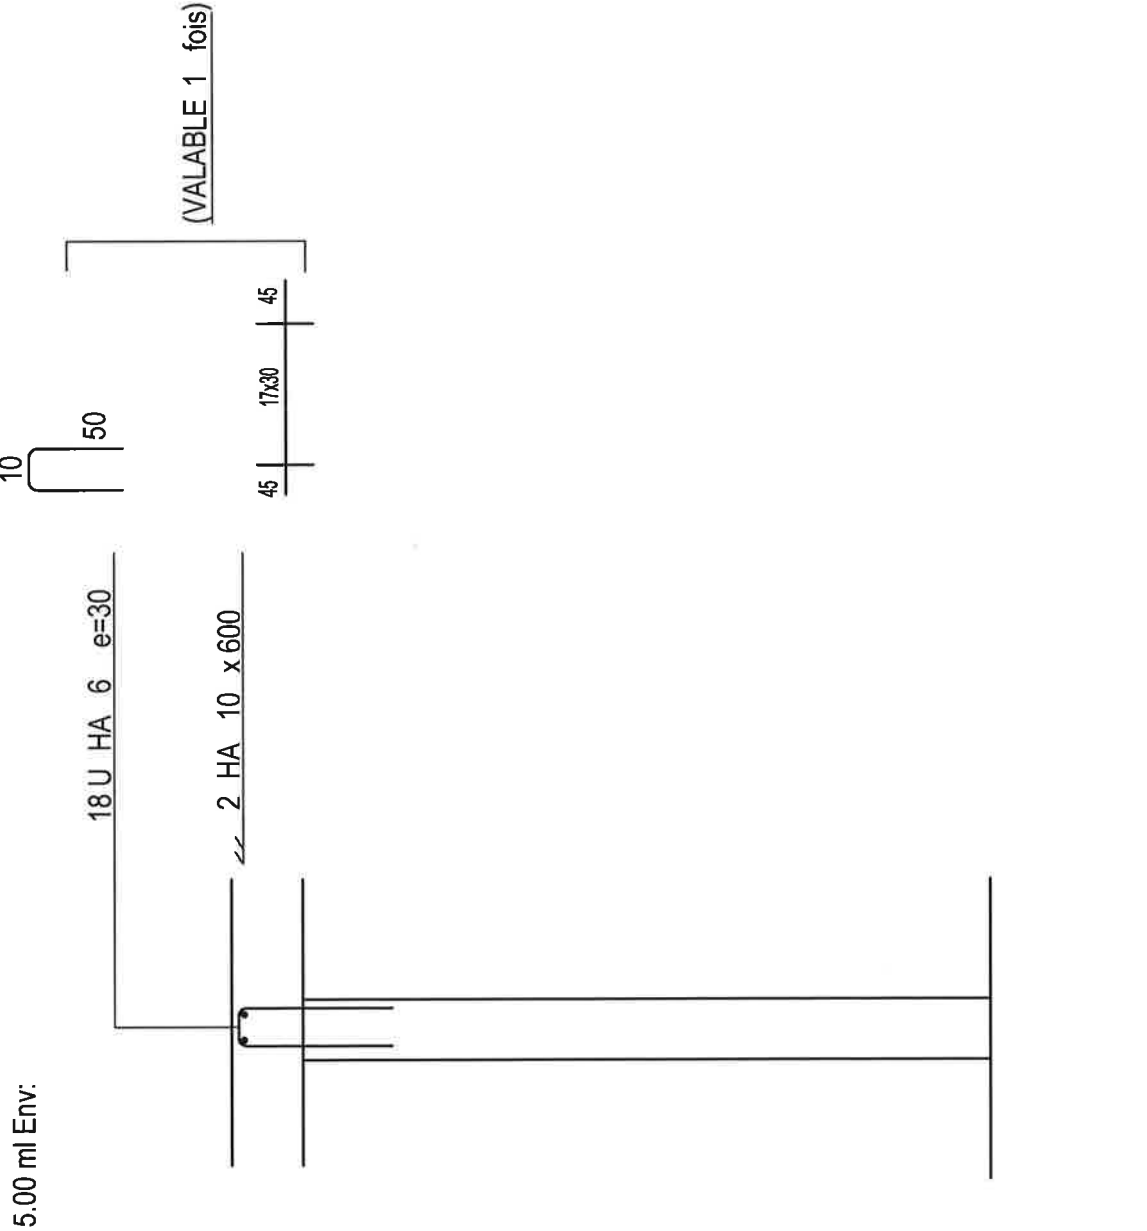


LINTEAUX INT.

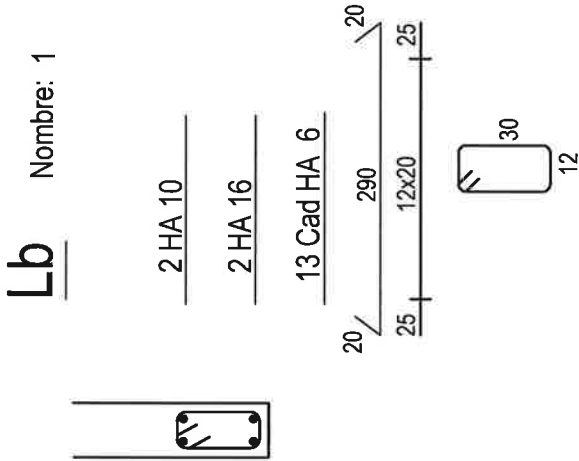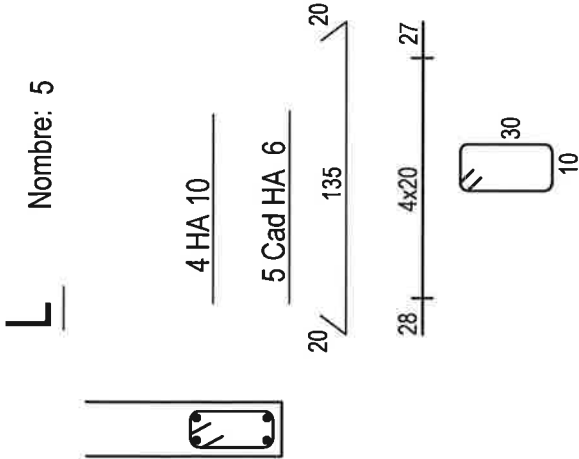

LINTEAUX EXT.





L1 Nombre: 5
PORTEE: 97

L3 Nombre: 4
PORTEE: 192

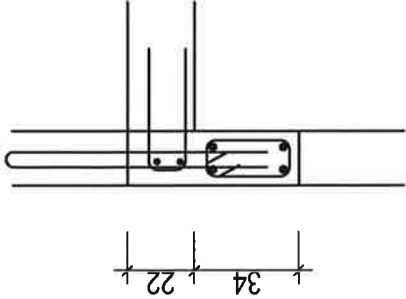


- 2 HA 10
- 2 HA 10
- 5 Cad HA 6

- 2 HA 10
- 2 HA 14
- 10 Cad HA 6

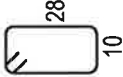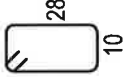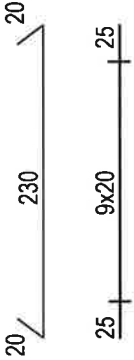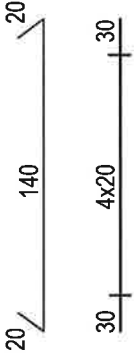





L2 Nombre: 4
PORTEE: 182

L4 Nombre: 2
PORTEE: 272

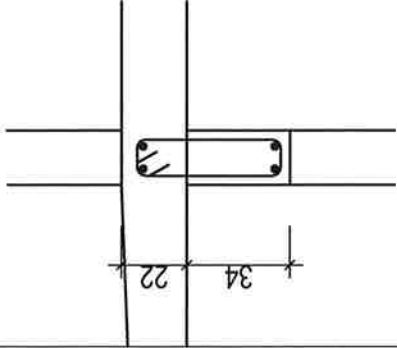

- 2 HA 10
- 2 HA 16
- 13 Cad HA 6

- 2 HA 10
- 2 HA 16
- 2 HA 16
- 18 Cad HA 6

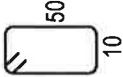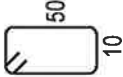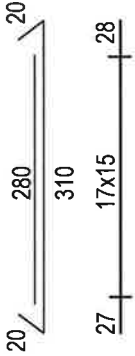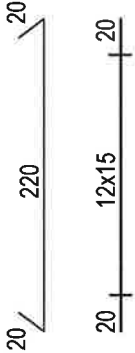

LINTEAUX

