


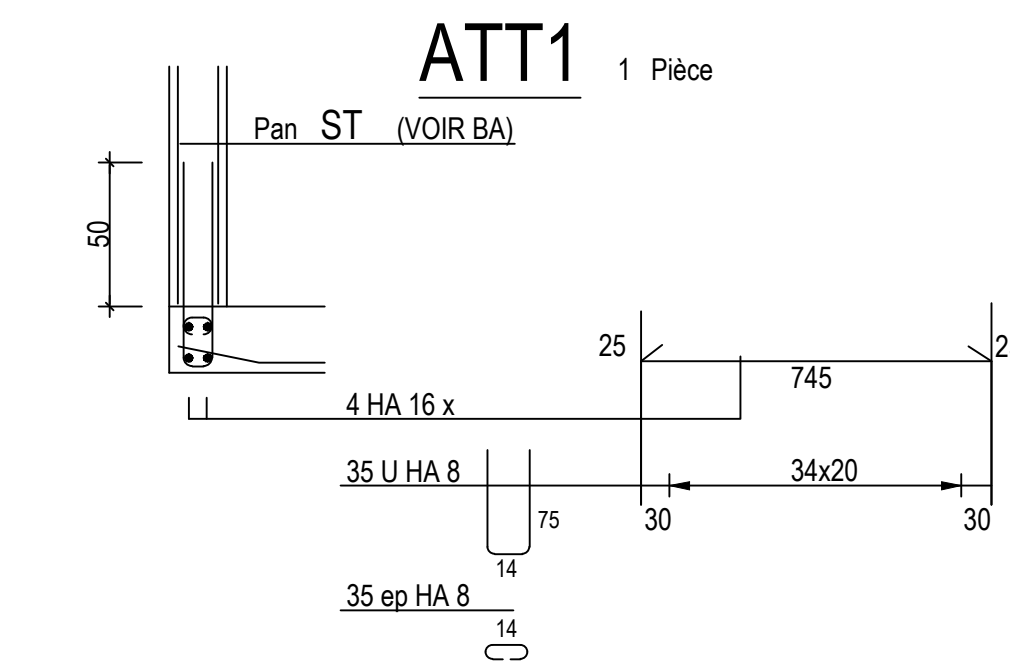
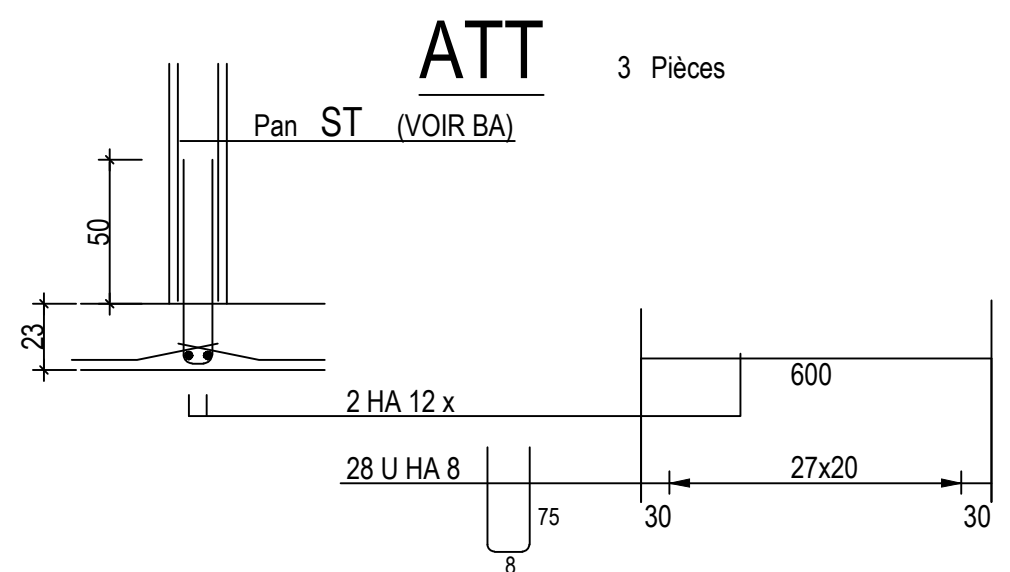


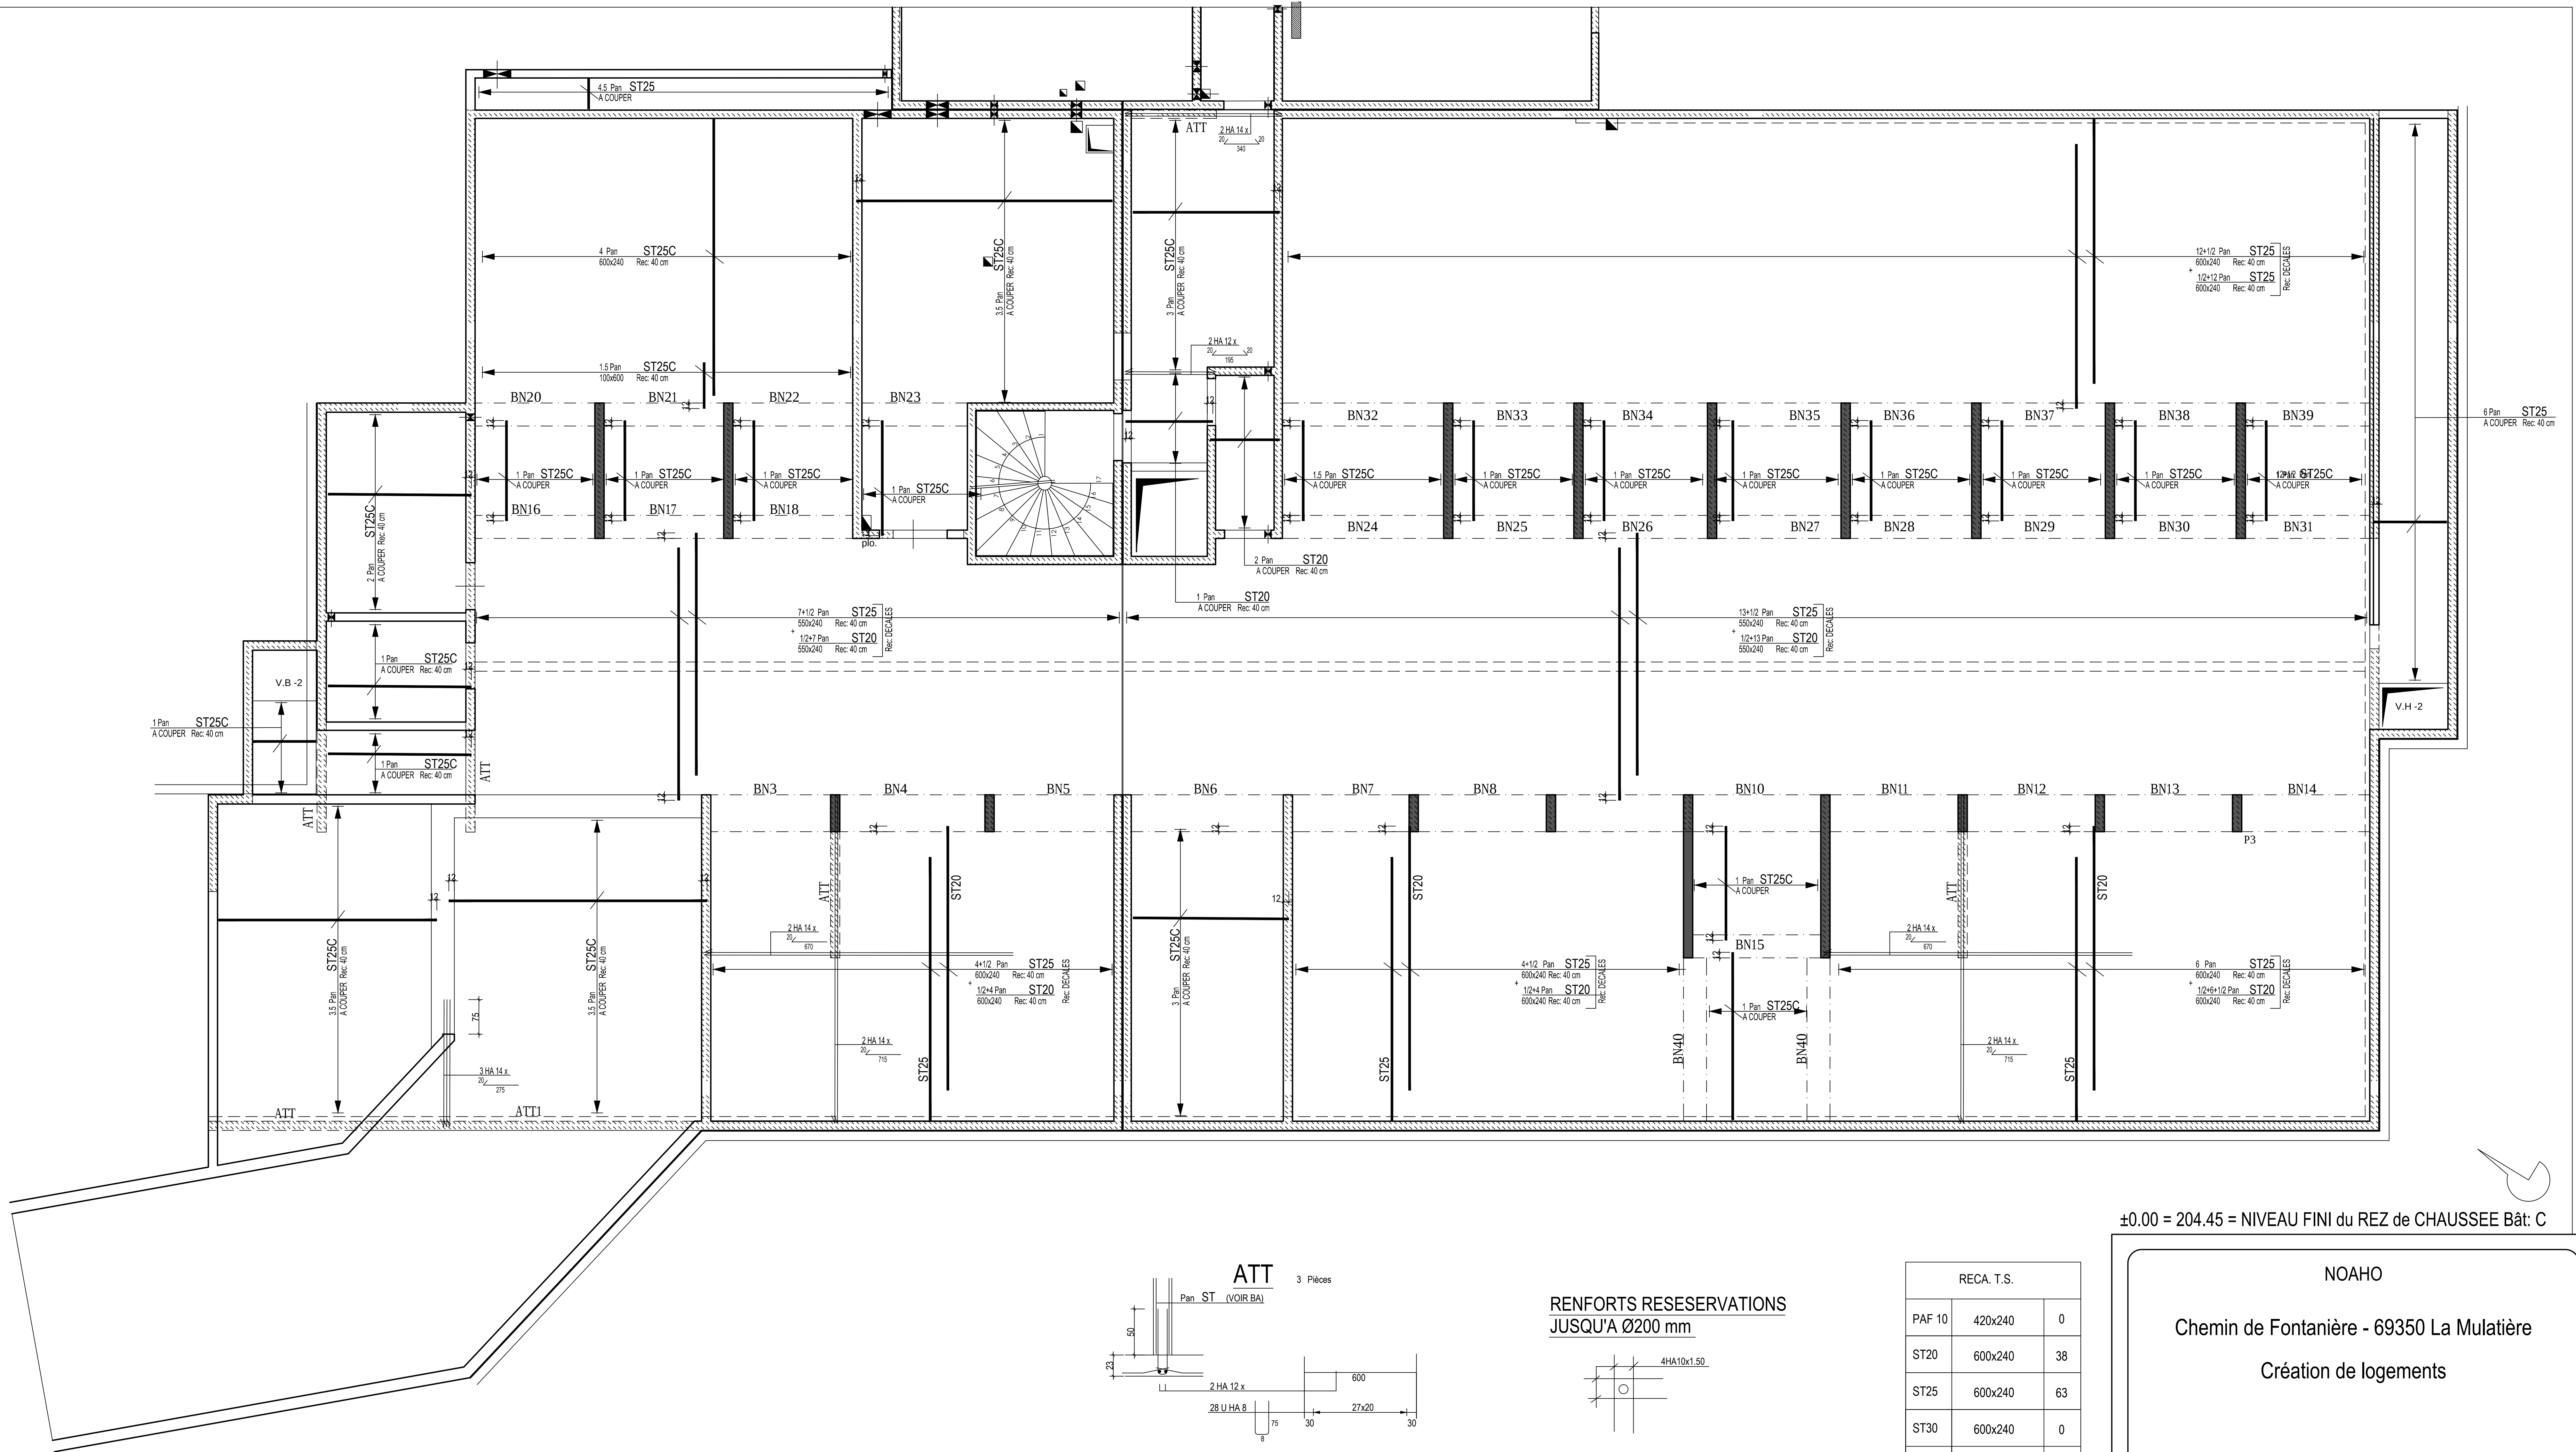

RENFORTS RESESERVATIONS  
JUSQU'A Ø200 mm

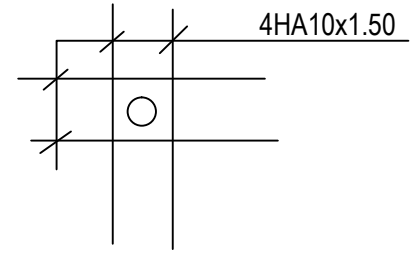

Principe de renfort aux droits des gaines:

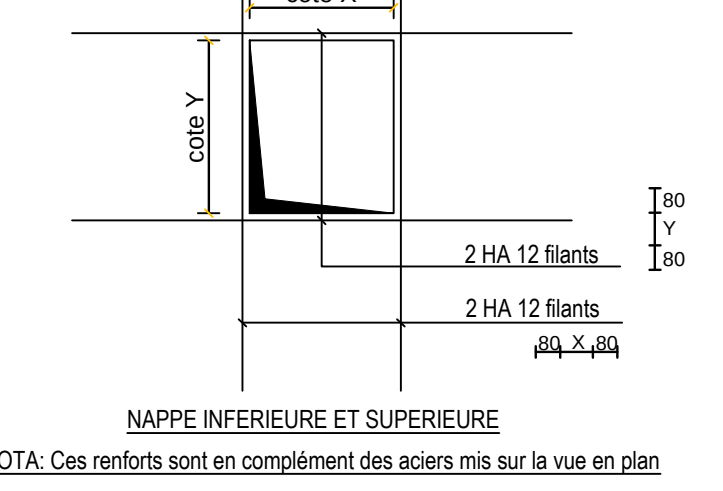

NOTA: Ces renforts sont en complément des aciers mis sur le vuie en plan

| RECA. T.S. |         |    |
|------------|---------|----|
| PAF 10     | 420x240 | 0  |
| ST20       | 600x240 | 38 |
| ST25       | 600x240 | 63 |
| ST30       | 600x240 | 0  |
| ST35       | 600x240 | 0  |
| ST50       | 600x240 | 0  |
| ST60       | 600x240 | 0  |
| ST15C      | 400x240 | 0  |
| ST25C      | 600x240 | 40 |
| ST40C      | 600x240 | 0  |
| ST50C      | 600x240 | 0  |
| ST65C      | 600x240 | 0  |

±0.00 = 204.45 = NIVEAU FINI du REZ de CHAUSSEE Bât: C

NOAHO

Chemin de Fontanière - 69350 La Mulatière

Création de logements

Les entreprises réalisant les travaux doivent tenir compte des données plans architectes lors de la réalisation des travaux

Les plans du Bât: C ont été revus et approuvés par le Bât: C

ARCHITECTES: Atelier D'S

SET STRUCTURE: MATTE SAS

ECONOMISTE: PRELEM

BUREAU DE CONTRÔLE: EXECO

MO DELEGUE: PSD Ingénierie

CSFR: SUD EST COORDINATION

OPC: Bureau VERITAS

ENTREPRISES: Fontanel pbc

Bât: C Aile OUEST

PLANCHER SUR -2

Armatures dalle INFÉRIEURE

DOE

Contrainte de sol: 8 bars EL5

Aciers HA (T) F4E600

Aciers Dux (D) F4E 235

Aciers TS F4E 500

Barres 12x12x20x20

Emboilage 3 cm

PLAN N° C15\_0

DATE: 19/06/2015

MATTÉ

BUREAU D'ETUDES

STRUCTURES ET FLUIDES

119 BOULEVARD STALINGRAD 69100 VILLEURBANNE

Tel: 04 72 44 12 87 Fax: 04 72 44 12 88

E-mail: mat@matte.fr

Dessiné par: J.B.O

Contrôle par: S.B.

Echelle: 1/50

Affaire N° 13.12.119