


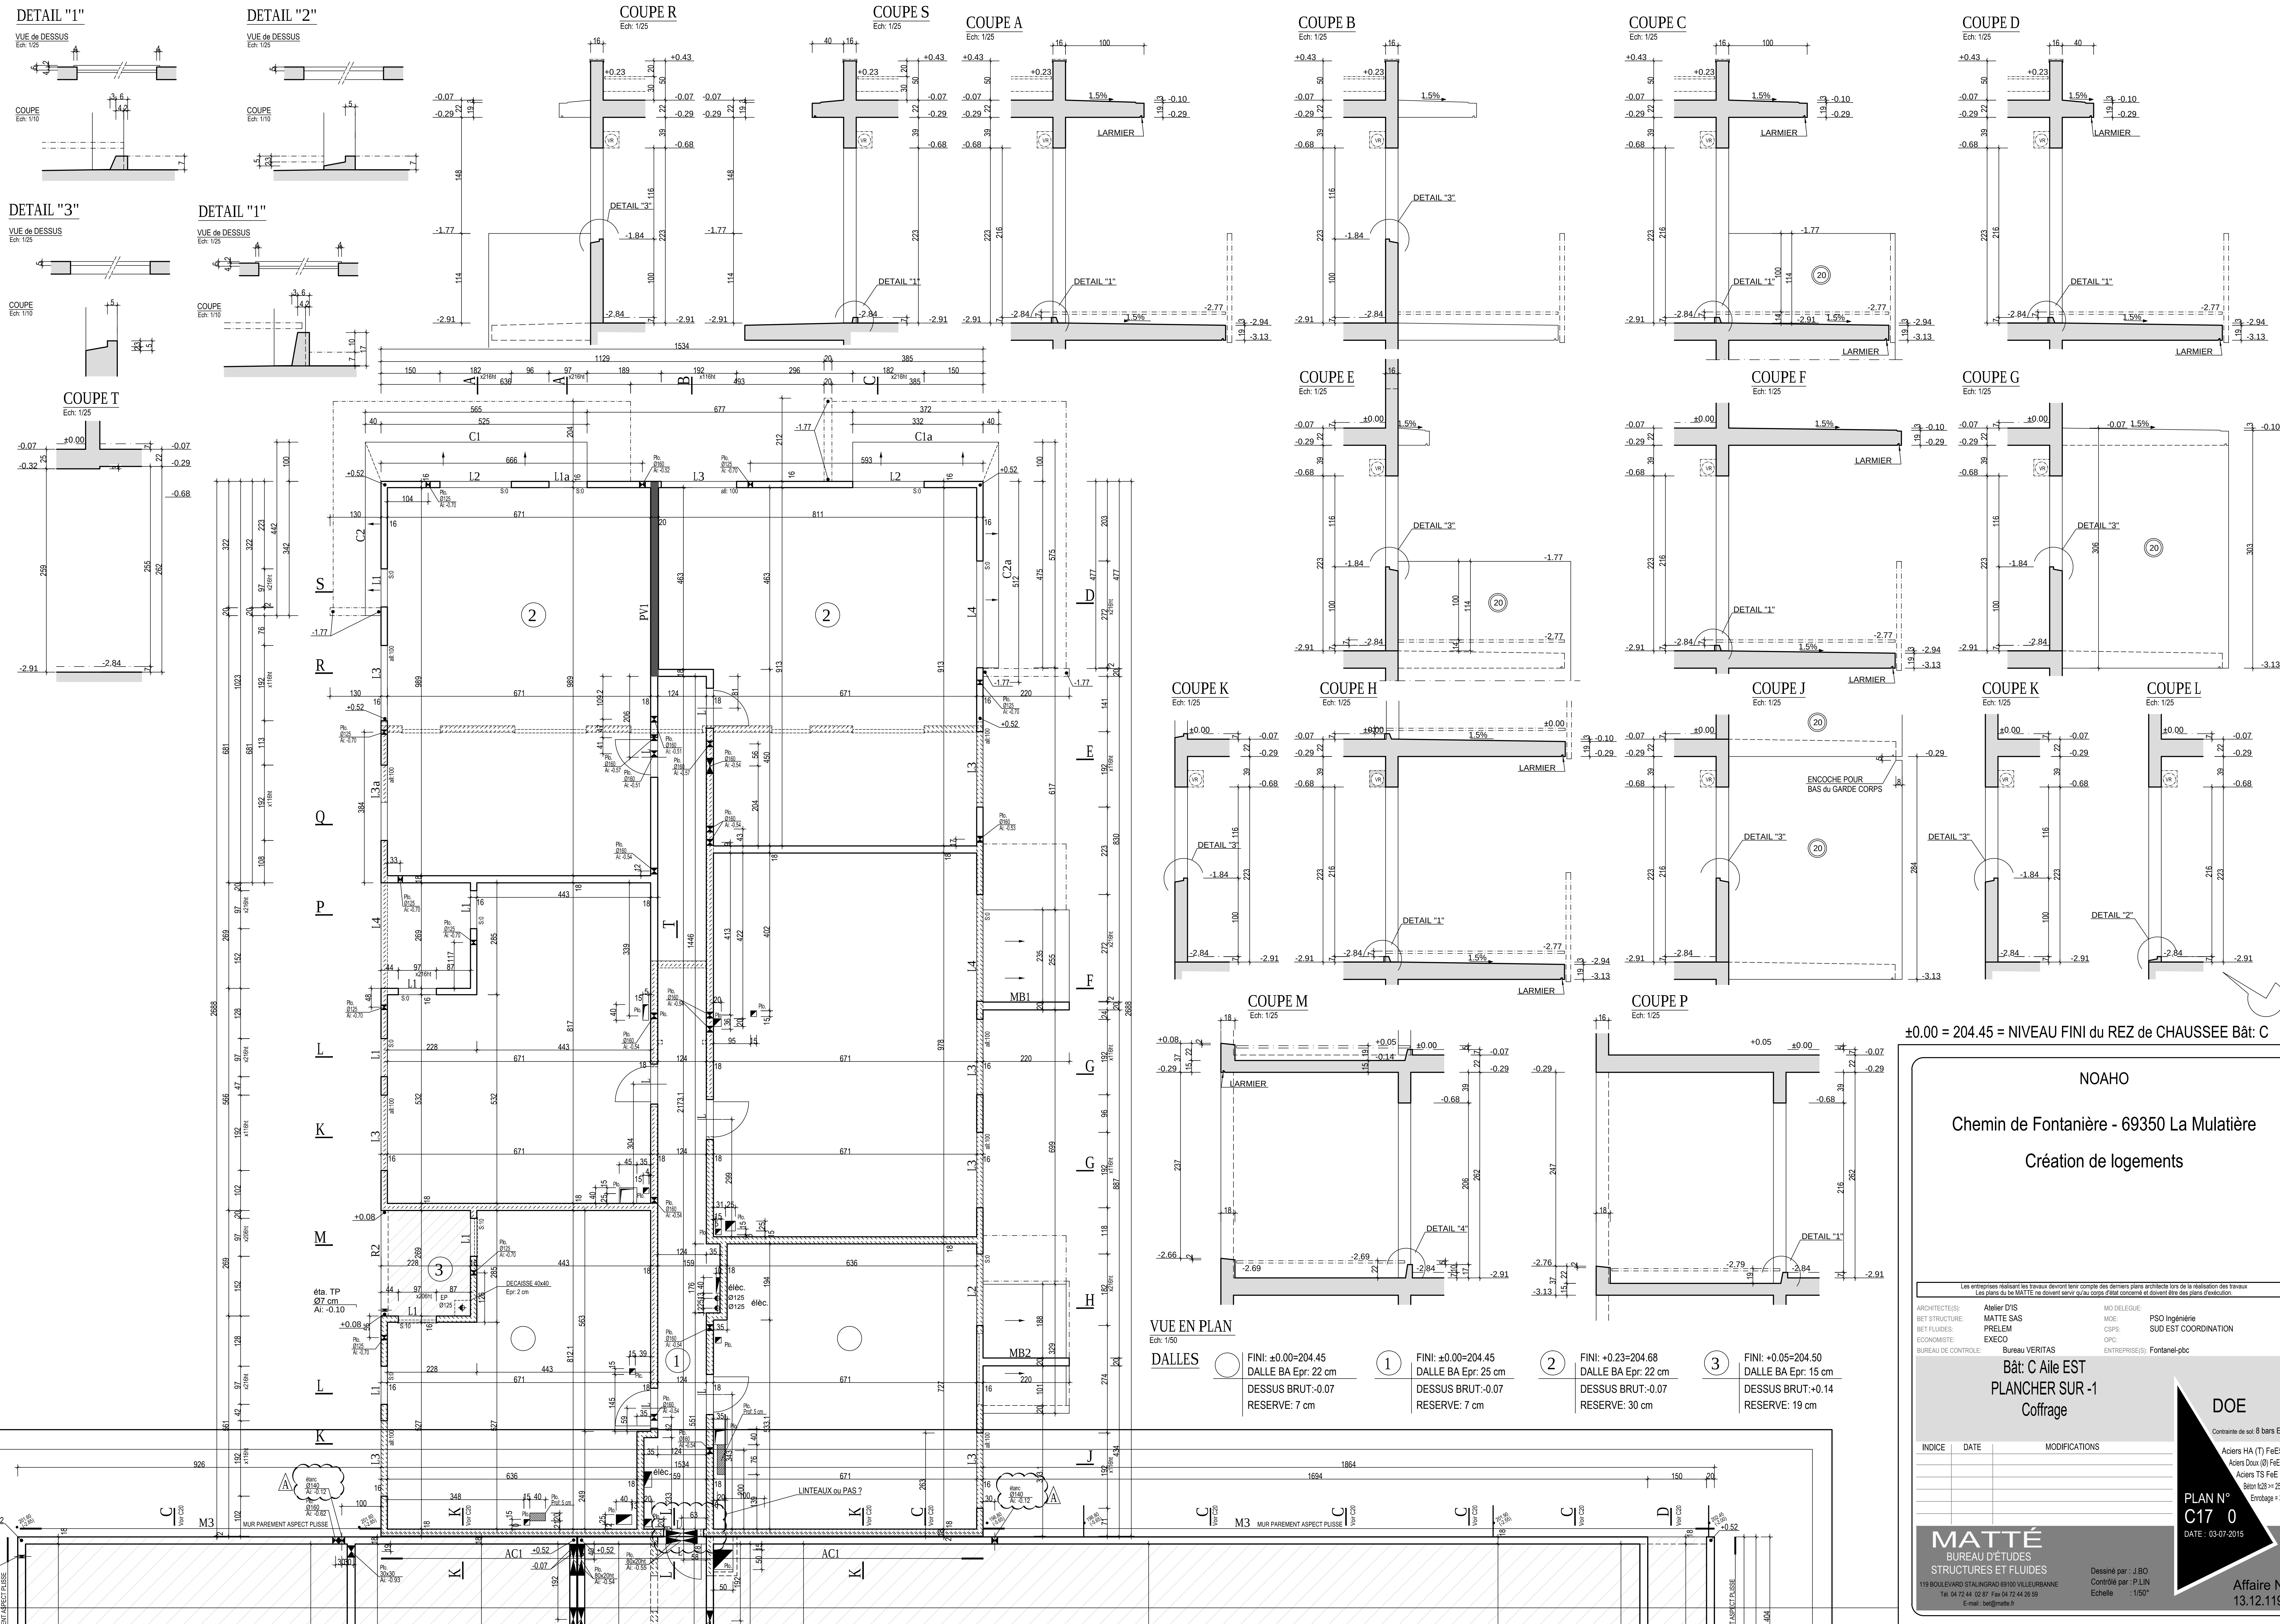

±0.00 = 204.45 = NIVEAU FINI du REZ de CHAUSSEE Bât C

NOAHO

Chemin de Fontanière - 69350 La Mulatière

Création de logements

ARCHITECTES: Atelier D1S

BET STRUCTURE: MATTE SAS

BET FLUIDES: PRELEM

ECONOMISTE: EXECO

BUREAU DE CONTROLE: Bureau VERITAS

MO DELEGUE: PSO Ingénierie

MOE: CSRS

MOF: SUD EST COORDINATION

ENTREPRISES: Fontanel-gbc

Bât C Aile EST

PLANCHER SUR-1

Coffrage

DOE

Contrainte de sol: 8 bars ELS

Aciers HA (T) FdE500

Aciers Dux (D) FdE235

Aciers TS FdE500

Béton f28 >= 25MPa

Enrobage = 3 cm

PLAN N° C17 0

DATE: 03-07-2015

MATTÉ

BUREAU D'ETUDES

STRUCTURES ET FLUIDES

119 BOULEVARD STALINGRAD 69100 VILLEURBANNE

Tel: 04 72 44 12 87 Fax: 04 72 44 26 59

E-mail: s@matte.fr

Dessiné par: J.B.O.

Contrôlé par: J.P.L.N.

Echelle: 1/150'

Affaire N° 13.12.119