

NOAHO

Chemin de Fontanière - 69350 La Mulatière

Création de logements

Les entreprises réalisant les travaux devront tenir compte des derniers plans architecte lors de la réalisation des travaux
Les plans du be MATTE ne doivent servir qu'au corps d'état concerné et doivent être des plans d'exécution.

ARCHITECTE(S): Atelier D'IS
BET STRUCTURE: MATTE SAS
BET FLUIDES: PRELEM
ECONOMISTE: EXECO
BUREAU DE CONTROLE: Bureau VERITAS

MO DELEGUE:
MOE: PSO Ingénierie
CSPS: SUD EST COORDINATION
OPC:
ENTREPRISE(S): Fontanel-pbc

Bât: C Aile EST
BA au -1

DOE

Contrainte de sol:

Aciers HA (T) FeE500
Aciers Doux (Ø) FeE 235
Aciers TS FeE 500
Béton fc28 >= 25MPa
Enrobage = 3 cm

PLAN N°
C18 0

DATE : 03/07/2015

MATTÉ
BUREAU D'ÉTUDES
STRUCTURES ET FLUIDES

119 BOULEVARD STALINGRAD 69100 VILLEURBANNE
Tél. 04 72 44 02 87 Fax 04 72 44 26 59
E-mail : bet@matte.fr


Dessiné par : J.BO
Contrôlé par : P.LIN
Echelle : 1/50°

Affaire N°
13.12.119

MURS EXTERIEURS

35.00 ml Env.

ANGLES MURS

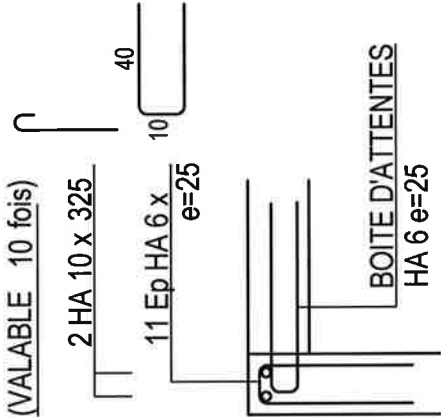

BOITE D'ATTENTE

HA 8 e=20
+ 2 HA 10 FILANTS et 120 Ep HA 6 e=30
Lg: 2x40.00 ml
Rec: 50 cm

Pan PAF "V" 320x240

Rec: 40 cm

Nombre: 18


EXT.

INT.

80

ARMATURES TETES DE MURS
et OUVERTURES


(VALABLE 44 fois)

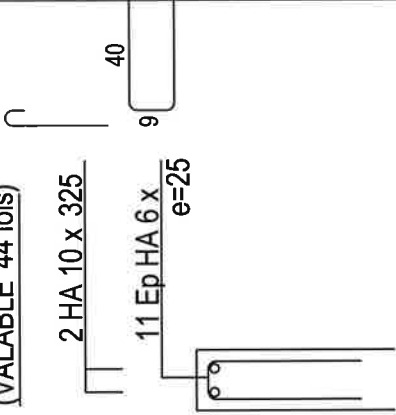

ARMATURES REJINGOT

(VALABLE 14 fois)

A COUPER SUIVANT OUVERTURES

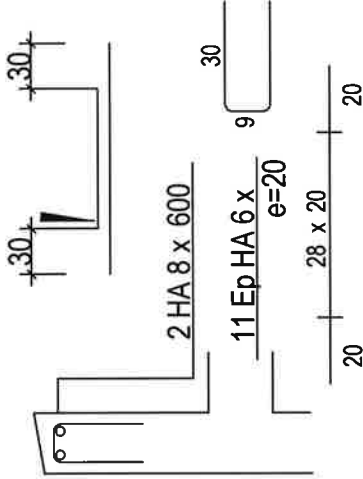


MURS M1


30.00 ml Env. AVEC CASQUETTES R1

Nombre: 6

SANS CASQUETTES

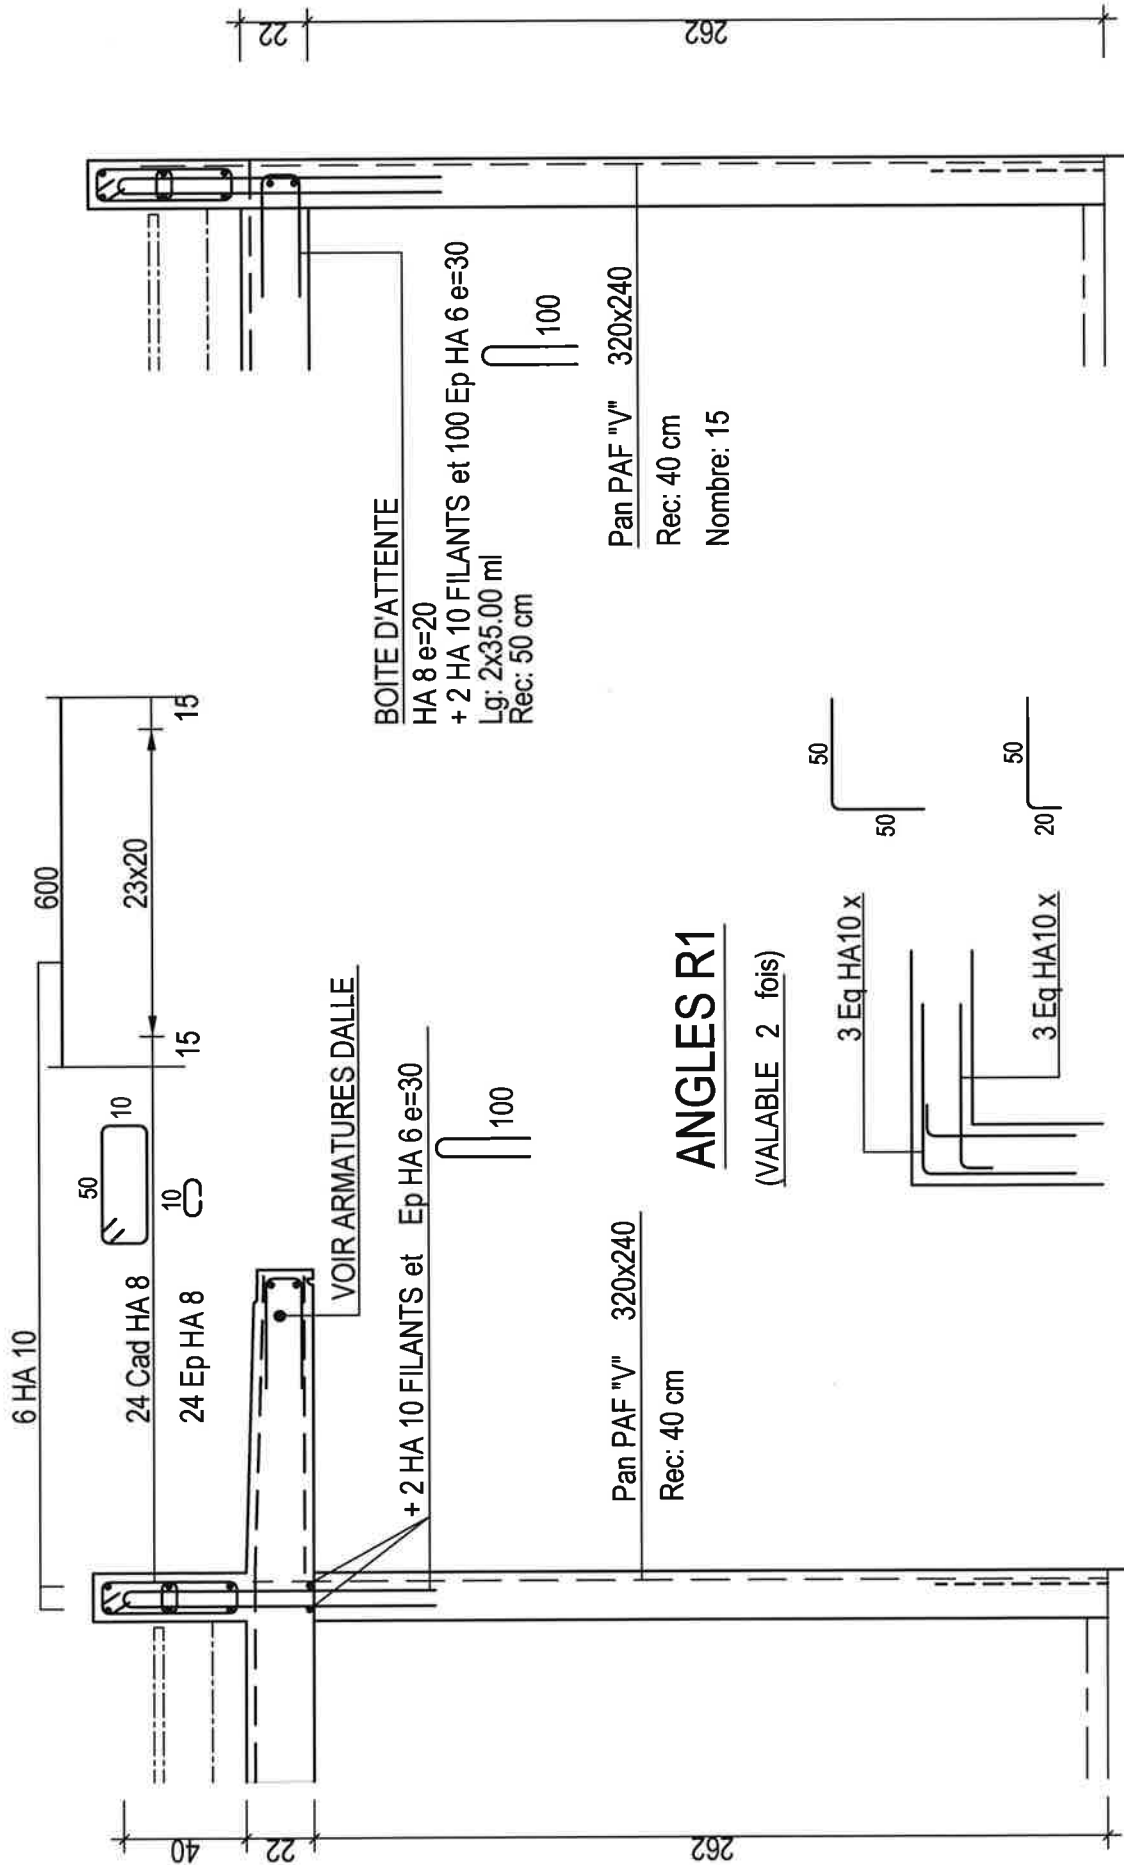

POUTRE VOILE : PV1

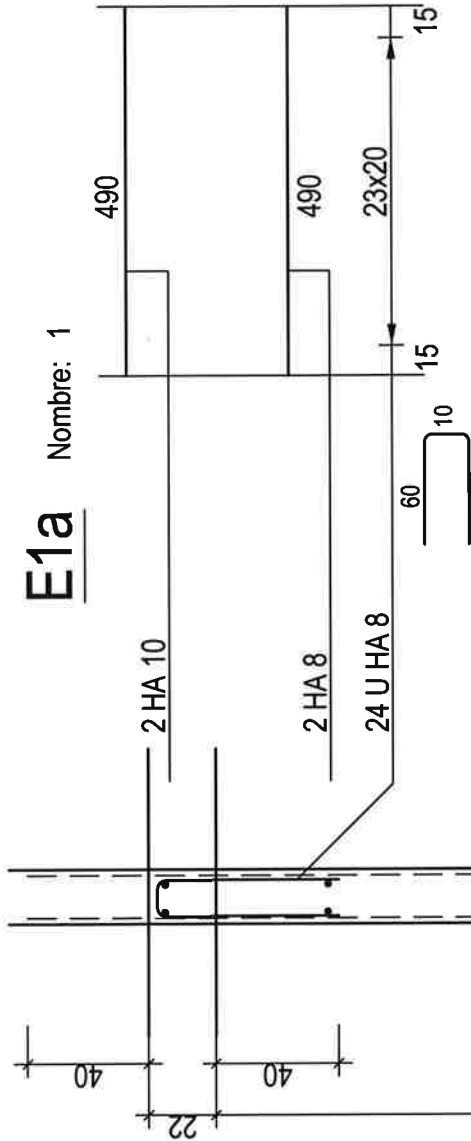


CHAQUE FACE

Pan ST25C A COUPER


Rec: 40 cm

Nombre: 2x2.5

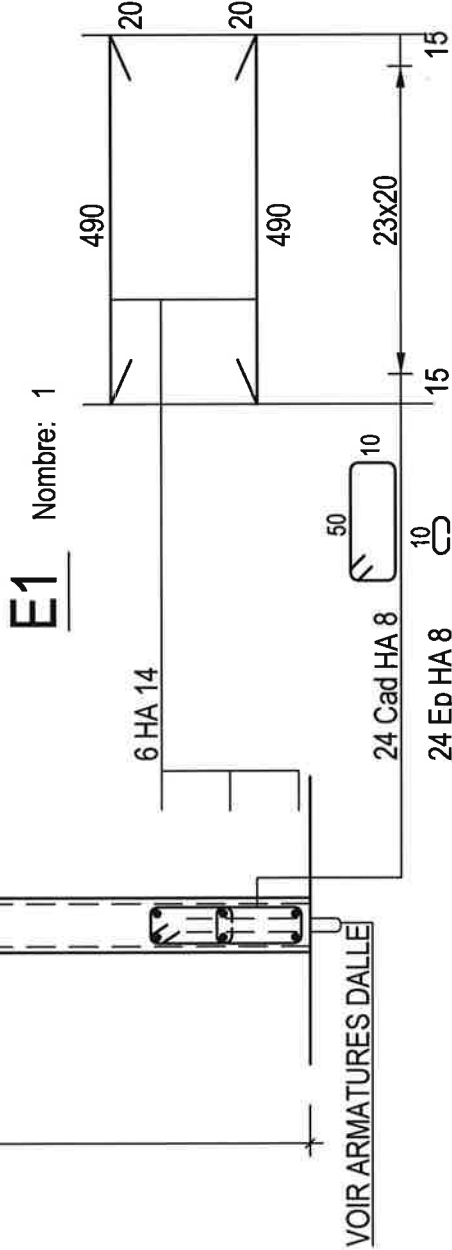


VOIR ARMATURES DALLE

ELEVATION

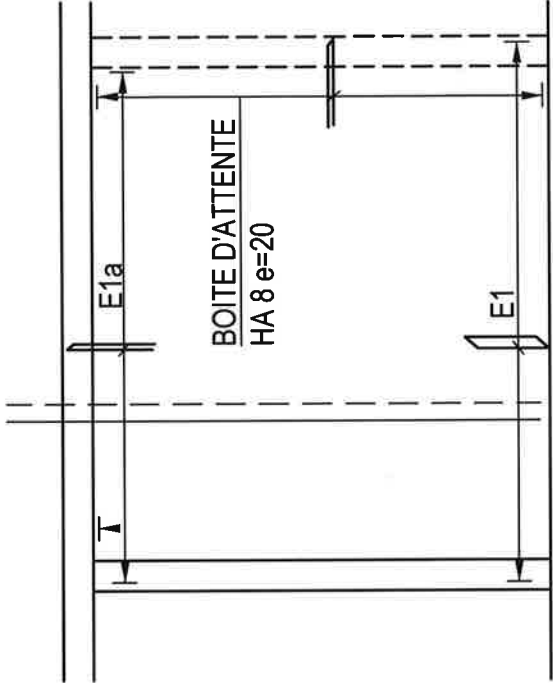


MURS INTERIEURS AVEC CONTINUITE


45.00 ml Env:

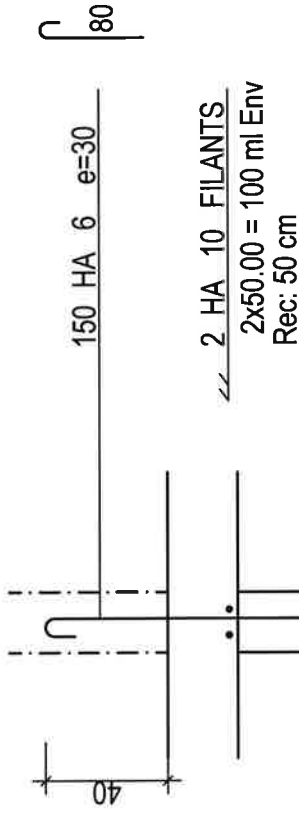

ANGLES MURS

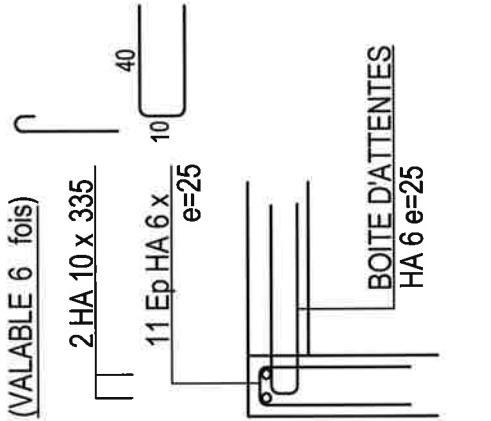


MURS INTERIEURS SANS CONTINUITE

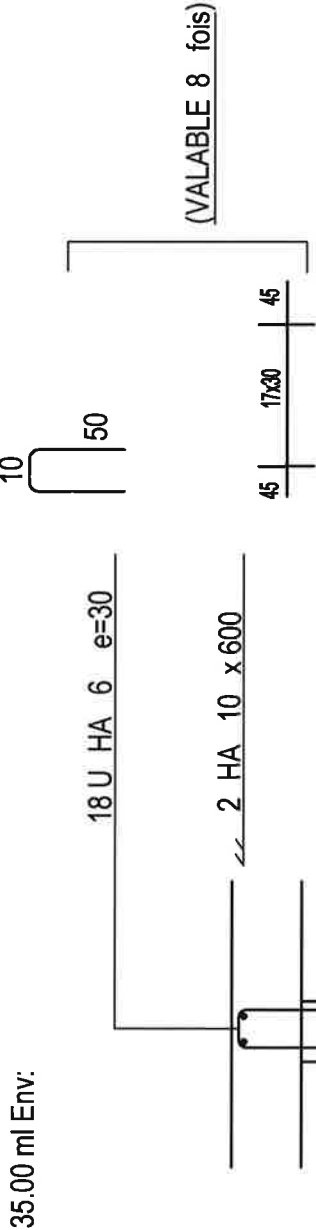

LINTEAUX INT.


L Nombre: 7

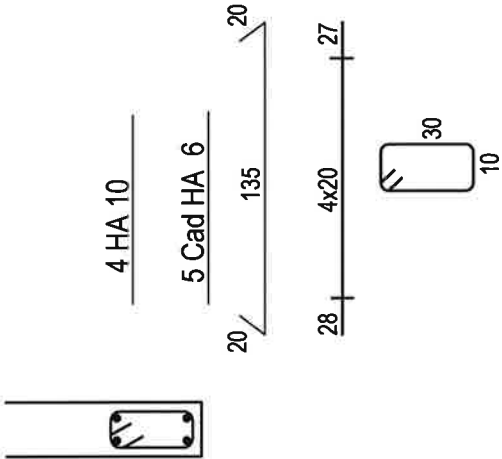

LINTEAUX EXT.



L1 Nombre: 6
PORTEE: 97

L3 Nombre: 8
PORTEE: 192

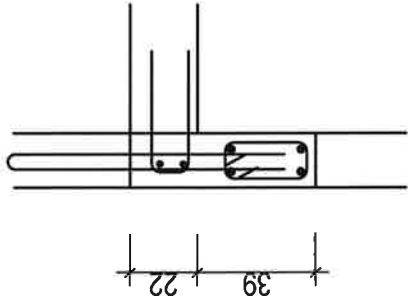



2 HA 10
2 HA 10

5 Cad HA 6

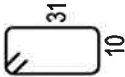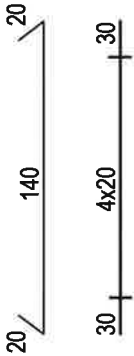


2 HA 10
2 HA 14

10 Cad HA 6

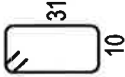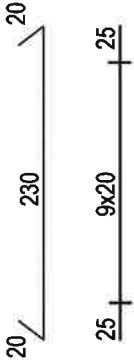

LINTEAUX EXT.



L1a Nombre: 2
PORTEE: 97

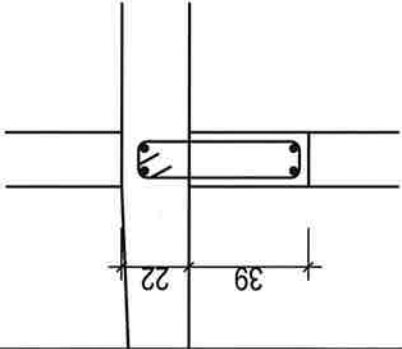

2 HA 10

2 HA 12

5 Cad HA 6

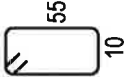
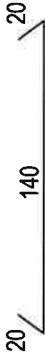


L2 Nombre: 3
PORTEE: 182

2 HA 10

2 HA 16

13 Cad HA 6

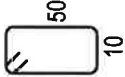
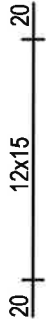


L3a Nombre: 1
PORTEE: 192

2 HA 10

2 HA 16

10 Cad HA 6

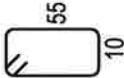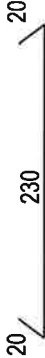

L4 Nombre: 2
PORTEE: 272

2 HA 10

2 HA 16

2 HA 16

18 Cad HA 6



