


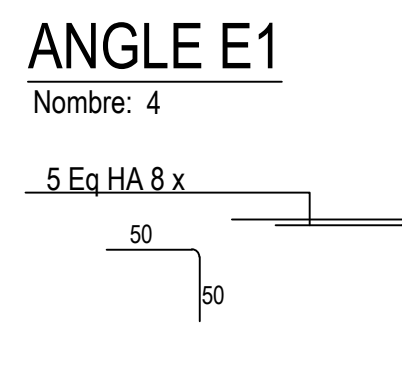
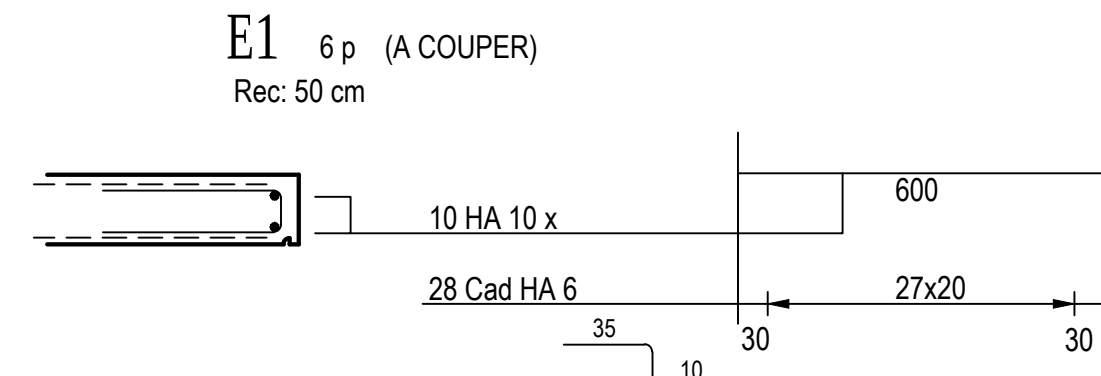
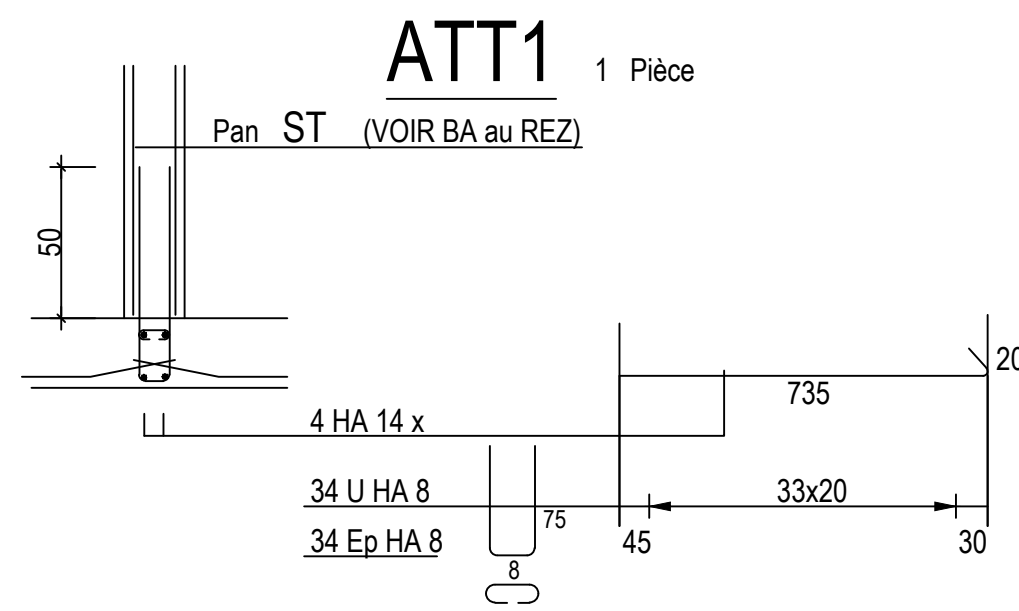
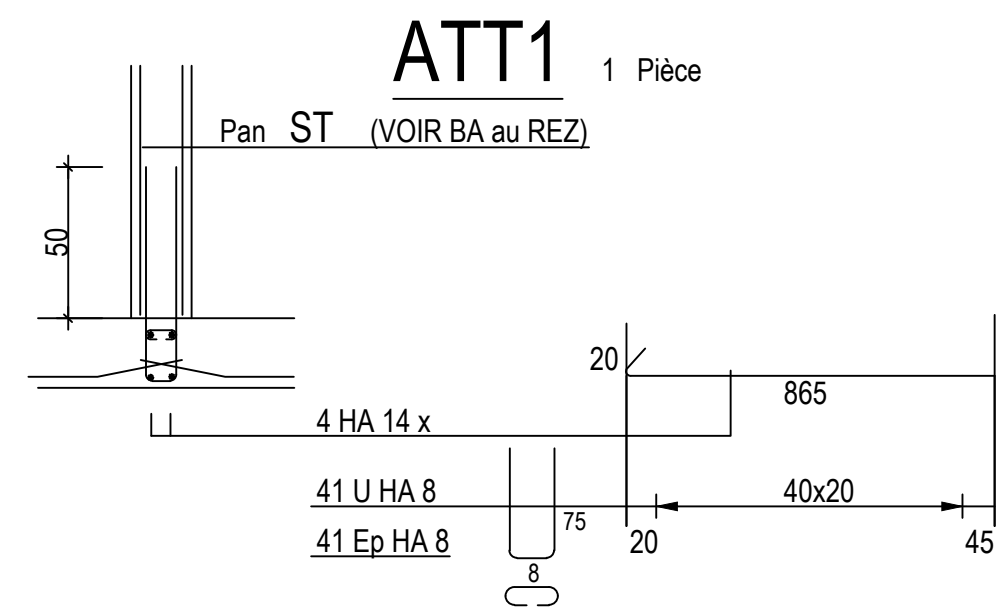


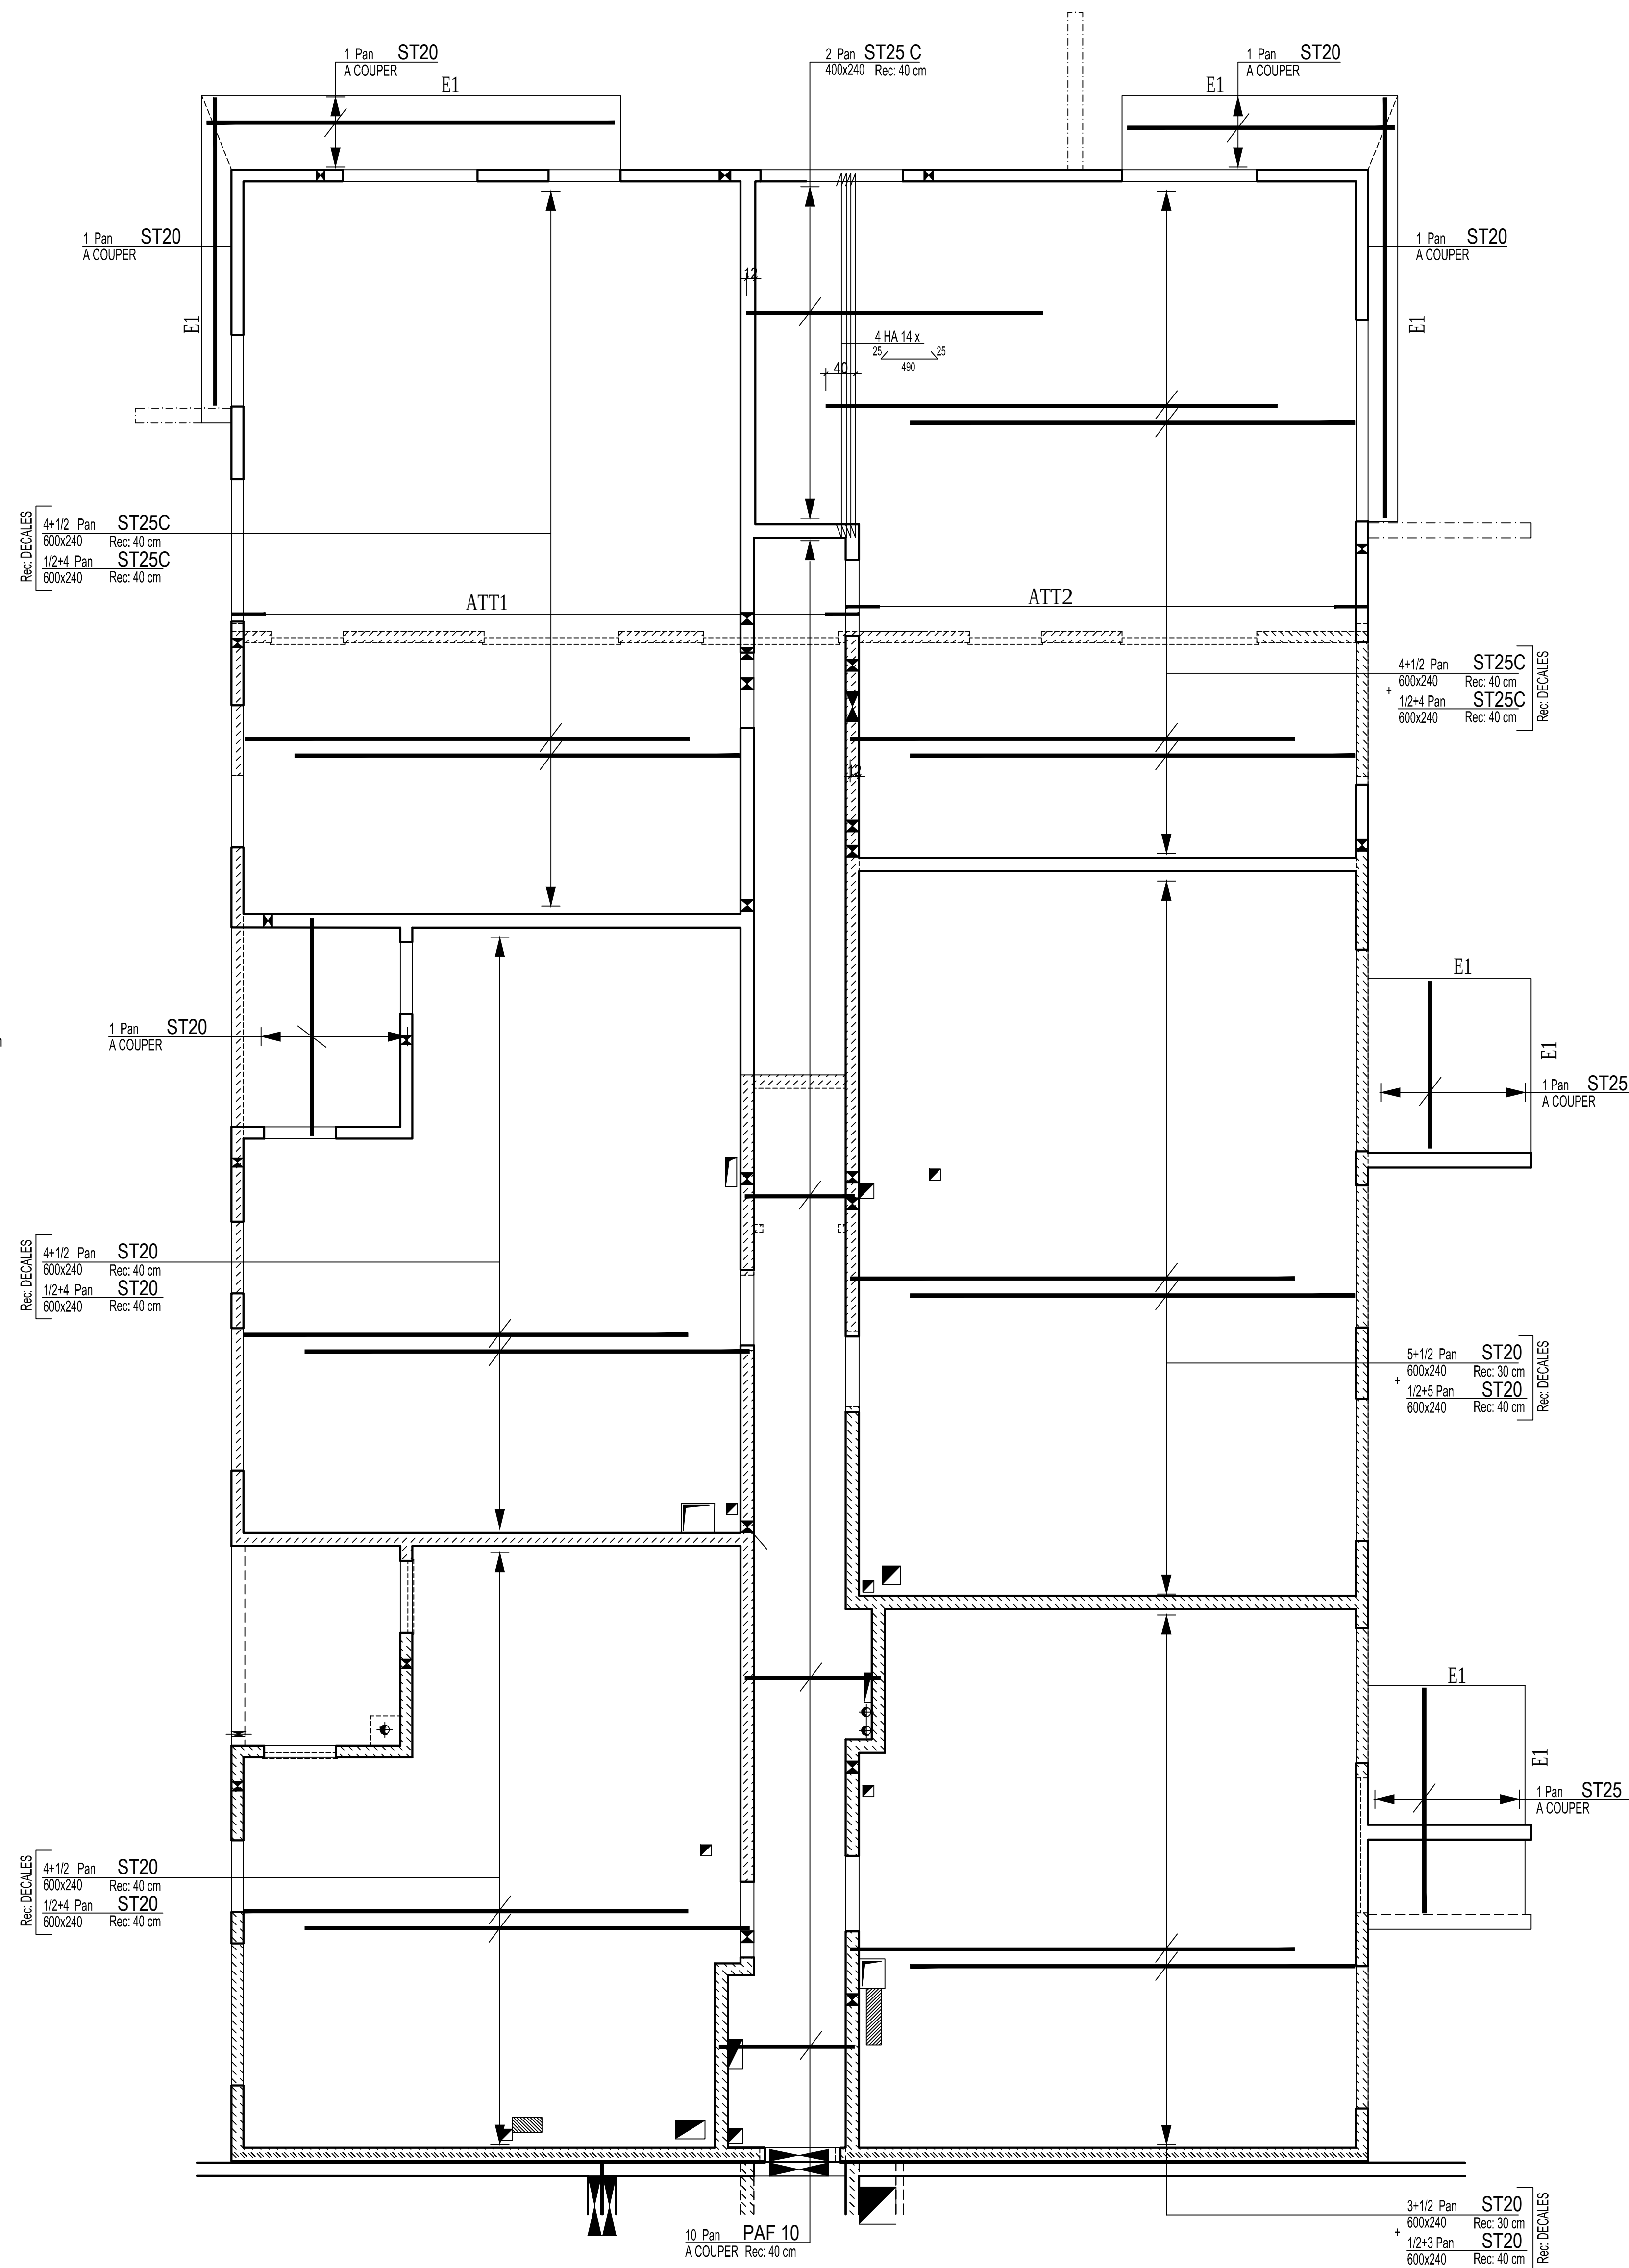


RECA. T.S.		
PAF 10	420x240	2
ST20	600x240	58
ST25	600x240	0
ST30	600x240	0
ST35	600x240	0
ST50	600x240	3
ST60	600x240	0
ST15C	400x240	2
ST25C	600x240	20
ST40C	600x240	0
ST50C	600x240	0
ST65C	600x240	0

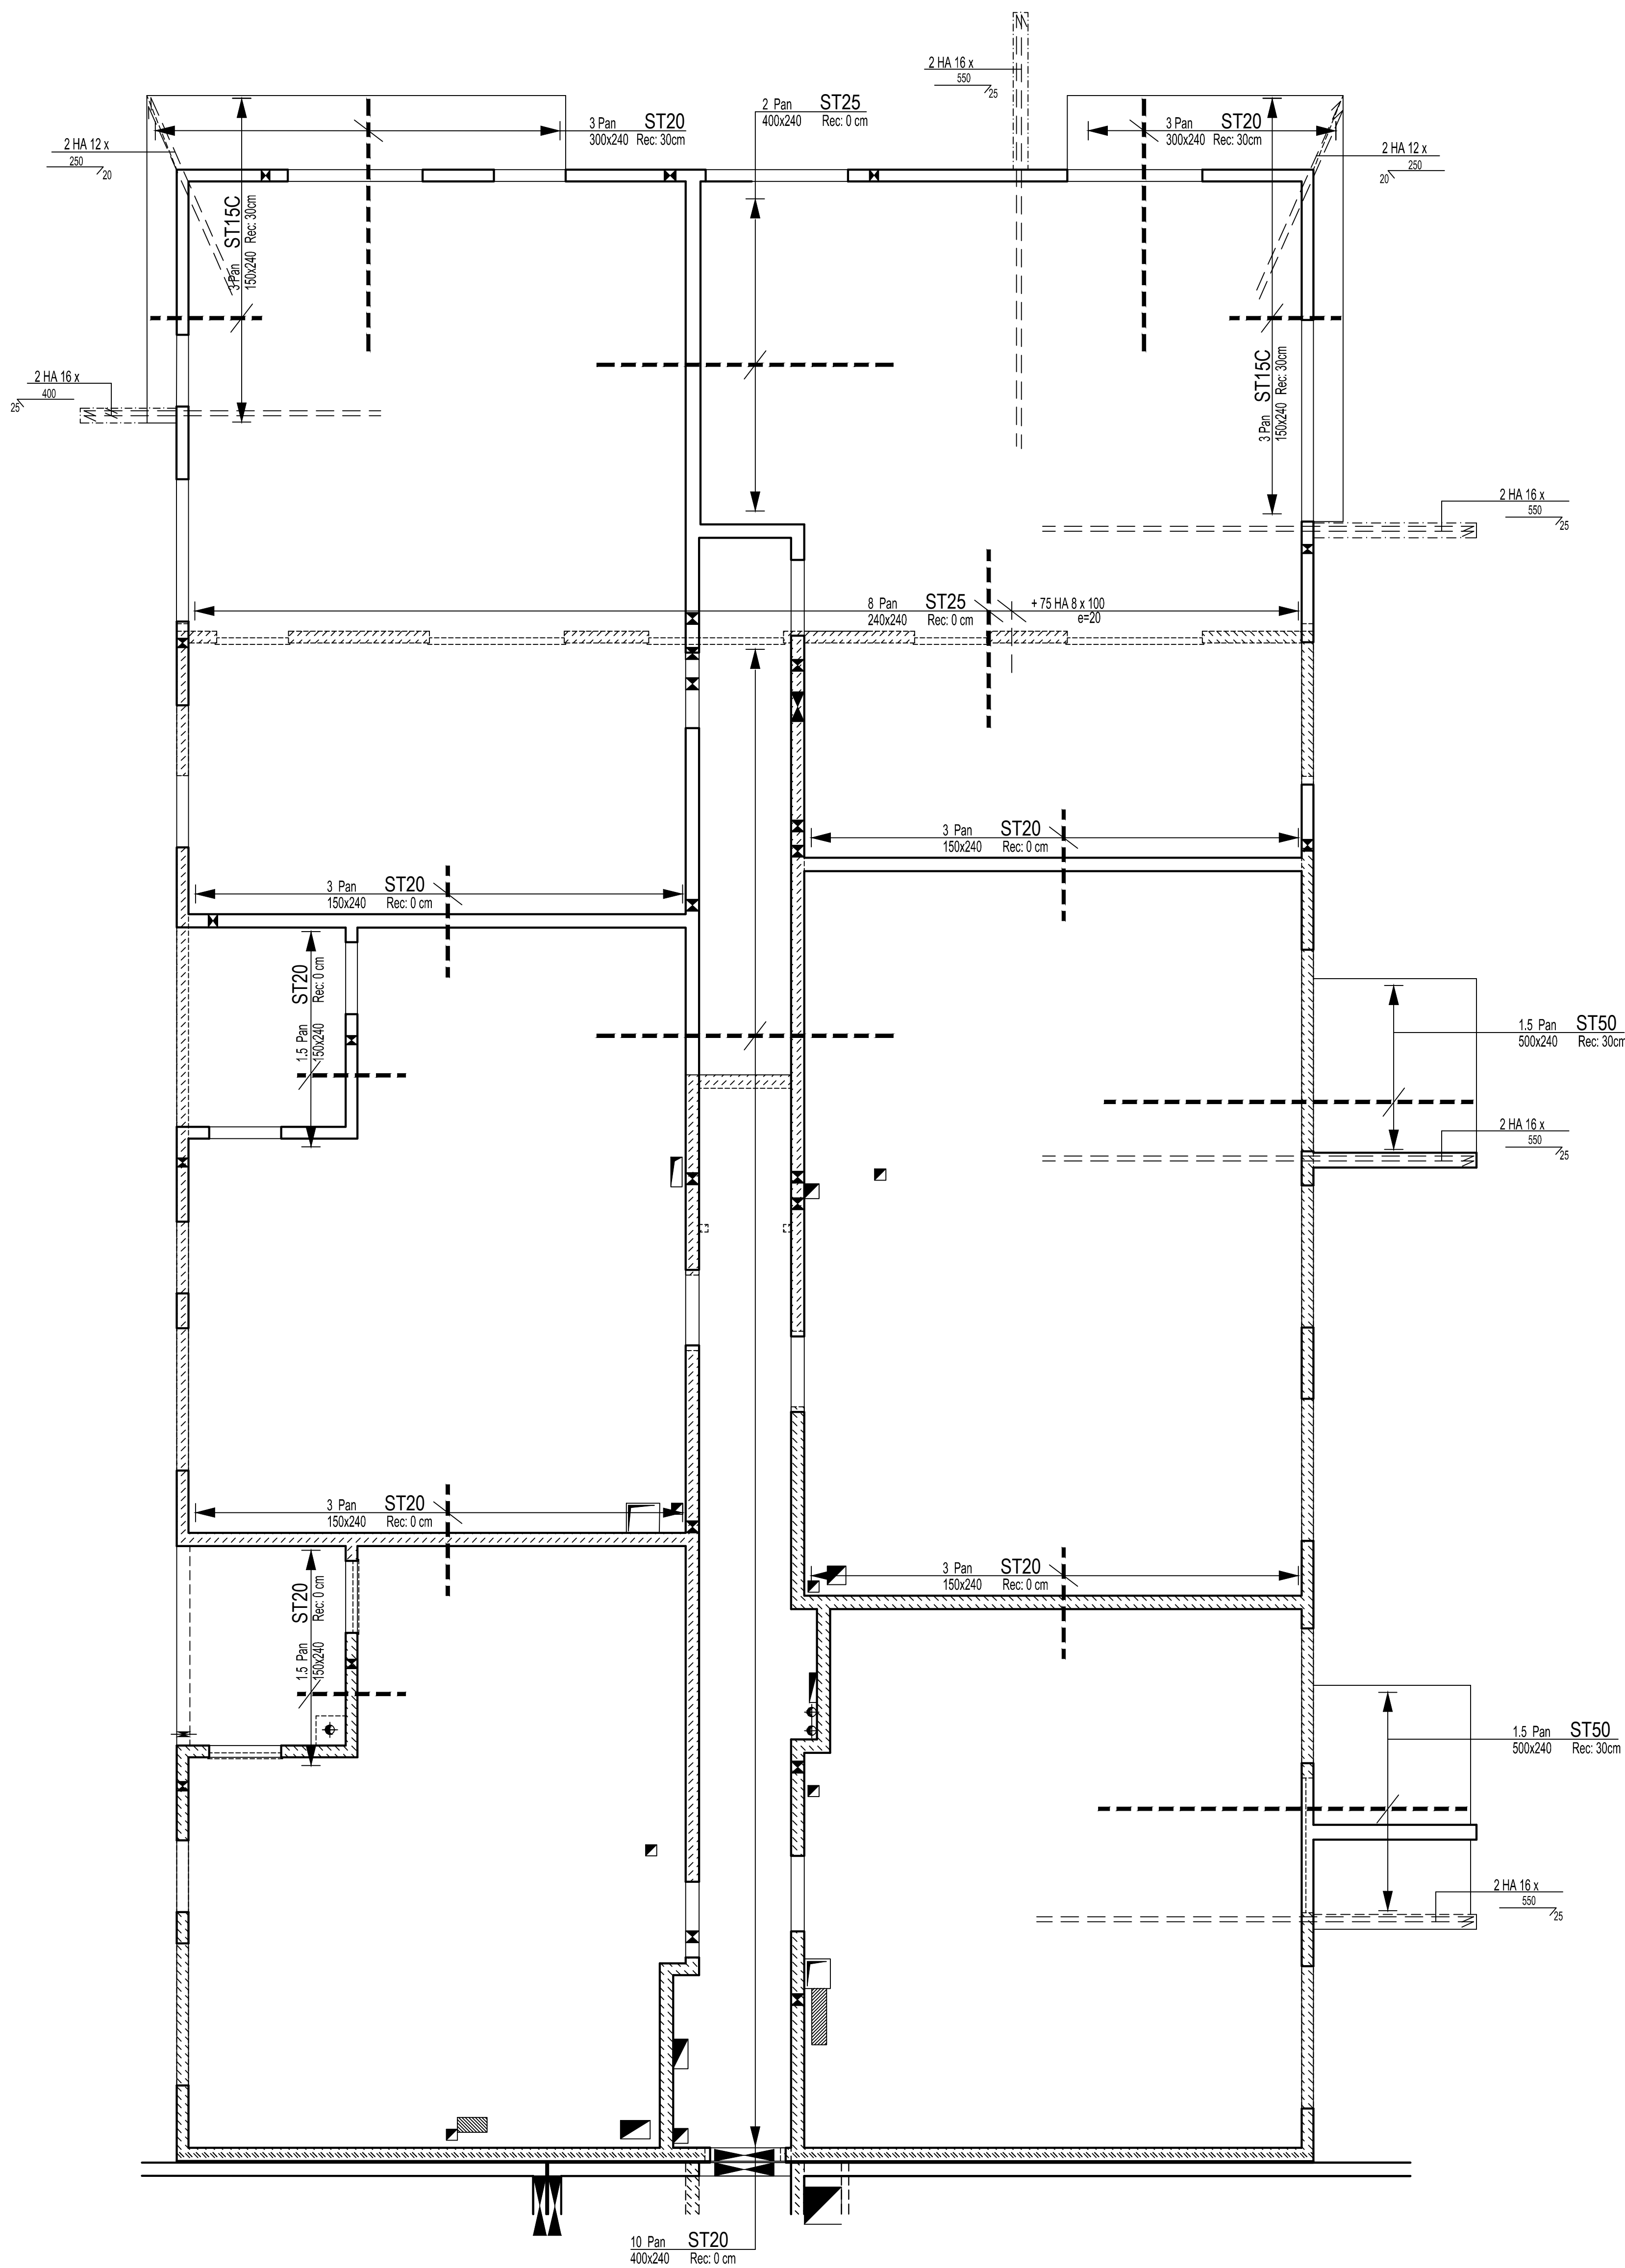

RENFORTS RESESERVATIONS JUSQU'A Ø200 mm

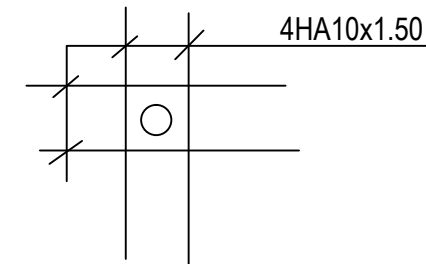

Principe de renfort aux droits des gaines:

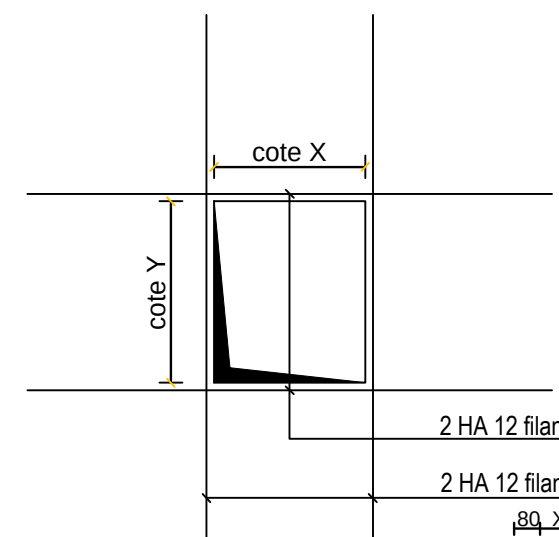

NAPPE INFÉRIEURE ET SUPÉRIEURE

NOTA: Ces renforts sont en complément des aciers mis sur la rue en plan

PANNEAUX EN TIROIRS PREVOIR RECouvreMENTS DECALES

EX: 1er Lit: 3 panneaux

2ème Lit: 1/2 x 1/2 panneaux

NOAHO

Chemin de Fontanière - 69350 La Mulatière

Création de logements

Bât: C Aile EST
PLANCHER SUR -1
ARMATURES DALLES

DOE

Contenance de sol: 8 bars EL5

Aciers HA (T) FcE500

Aciers Doux (D) FcE235

Aciers TS FcE 500

Béton k28 = 25MPa

Enrobage = 3 cm

PLAN N°
C19 0

DATE: 21-07-2015

MATTÉ
BUREAU D'ÉTUDES
STRUCTURES ET FLUIDES

Dessiné par: J.B.O.

Contrôlé par: P.LIN

Echelle: 1/150"

Affaire N°

13.12.119