




VUE EN PLAN FONDATIONS

Ech: 1/50

DALLES

- | | | | | | |
|--|--|--|--|--|---|
| ○ FINI: ±0.00=204.45
DALLE BA Epr: 37 cm
DESSUS BRUT:-0.12
RESERVE: 12 cm | ① FINI: +0.00=204.45
DALLE BA Epr: 23 cm
DESSUS BRUT:-0.12
RESERVE: 12 cm | ② FINI: +0.05=204.50
DALLE BA Epr: 23 cm
DESSUS BRUT:-0.12
RESERVE: 17 cm (TERRE) | ③ FINI: +0.37=204.82
DALLE BA Epr: 23 cm
DESSUS BRUT:-0.12
RESERVE: 49 cm (TERRE) | ④ FINI: +0.05=204.50
DALLE BA Epr: 35 cm
DESSUS BRUT:-0.69
RESERVE: 69 cm (TERRE) | ⑤ FINI: ±0.00=204.45
DALLE BA Epr: 35 cm
DESSUS BRUT:-1.20
RESERVE: 120 cm (TERRE) |
|--|--|--|--|--|---|

COUPE B

Ech: 1/25

COUPE A

Ech: 1/25

NOAHO

Chemin de Fontanière - 69350 La Mulatière

Création de logements

Les entreprises réalisant les travaux devront tenir compte des derniers plans architectes lors de la réalisation des travaux.
Les plans de la MATTE ne doivent servir qu'à titre d'information et ne doivent pas être utilisés pour la construction.

ARCHITECTES:	Atelier D'S	MO DELEGUE:	PSO Ingénierie
BET STRUCTURE:	MATTE SAS	MOE:	SUD EST COORDINATION
BET FLUIDES:	PRELEM	CSPS:	
ECONOMISTE:	EXECO	ENTREPRISES:	Fontanel gbc
BUREAU DE CONTROLE:	Bureau VERITAS		

Bât: C Aile OUEST
PLANCHER SUR -1
Coffrage

DOE
Contrainte de sol: 8 bars ELIS

INDICE	DATE	MODIFICATIONS
A	11/12/2015	AJOUTER RESERVATIONS SUIVANT A

MATTE
BUREAU D'ETUDES
STRUCTURES ET FLUIDES

Dessiné par : J.B.O
Contrôlé par : P.LIN
Echelle : 1/150

PLAN N°
C20 A
DATE : 23/05/2015

Affaire N°
13.12.119

Aciers HA (T) FeE500
Aciers Doux (D) FeE235
Aciers TS FeE 500
Béton f28 = 25MPa
Enrobage = 3 cm