

NOAHO

Chemin de Fontanière - 69350 La Mulatière

Création de logements

Les entreprises réalisant les travaux devront tenir compte des derniers plans architecte lors de la réalisation des travaux
Les plans du be MATTE ne doivent servir qu'au corps d'état concerné et doivent être des plans d'exécution.

ARCHITECTE(S): Atelier D'IS
BET STRUCTURE: MATTE SAS
BET FLUIDES: PRELEM
ECONOMISTE: EXECO
BUREAU DE CONTROLE: Bureau VERITAS

MO DELEGUE:
MOE: PSO Ingénierie
CSPS: SUD EST COORDINATION
OPC:
ENTREPRISE(S): Fontanel-pbc

Bât: C Aile OUEST
BA au -1

DOE

Contrainte de sol:

Aciers HA (T) FeE500
Aciers Doux (Ø) FeE 235
Aciers TS FeE 500
Béton fc28 >= 25MPa
Enrobage = 3 cm

PLAN N°
C21 0

DATE : 30/06/2015

MATTÉ
BUREAU D'ÉTUDES
STRUCTURES ET FLUIDES


119 BOULEVARD STALINGRAD 69100 VILLEURBANNE
Tél. 04 72 44 02 87 Fax 04 72 44 26 59
E-mail : bet@matte.fr

Dessiné par : J.BO
Contrôlé par : P.LIN
Echelle : 1/50°

Affaire N°
13.12.119

M1a

6.36 ml

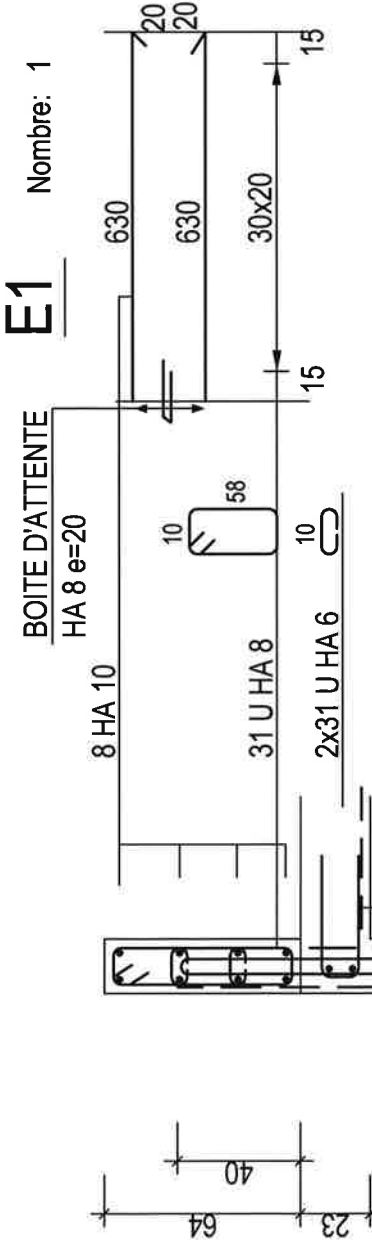

BOITE D'ATTENTE

HA 10 e=20
+ 2 HA 10 FILANTS et 22 Ep HA 6 e=30
Lg: 2x6.30 ml

80

INT.
Pan ST20 VERTICAUX

INT.
Rec: 40 cm 280X240
Nombre: 3

EXT.


EXT.

Pan PAF V VERTICAUX

Rec: 40 cm
Nombre: 3


ANGLES MURS

(VALABLE 1 fois)

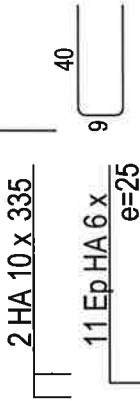


M2

12.00 ml Env:

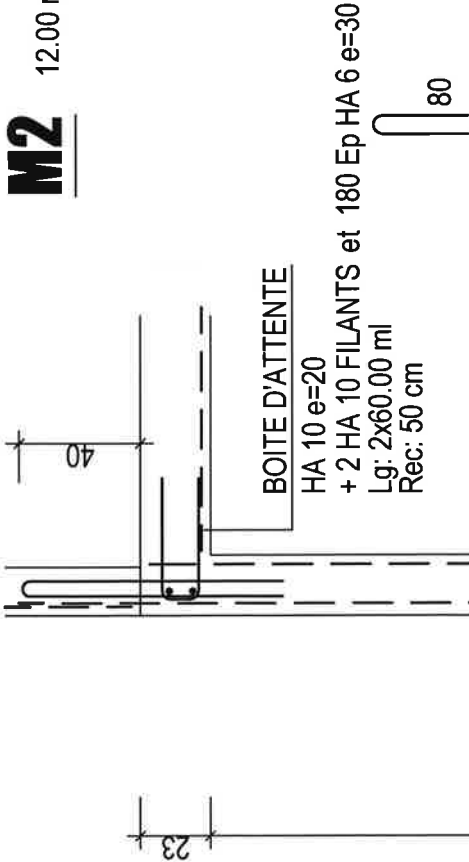


ANGLES MURS

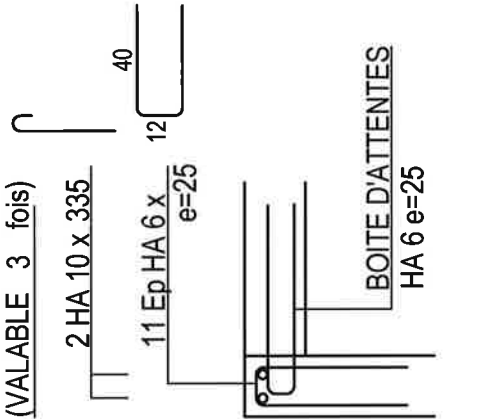


AFF: S.13.12.119	Bât: C	LA MULATIERE-69350 LaMulatiere CREATION de LOGEMENTS	BA au -1 Aile OUEST	Plan n° C 21	Page: 4
M2a E2a Nombre: 1 HAUT et BAS Pan ST15C Rec: 40 cm EXT. Pan PAF V VERTICAUX Rec: 40 cm BOITE D'ATTENTE HA 8 e=20 + 2 HA 10 FILANTS ±0.00 E2 Nombre: 1 BOITE D'ATTENTE HA 6 e=25 BOITE D'ATTENTE HA 8 e=20 + 2 HA 10 FILANTS et 12 Ep HA 6 e=30 Lg: 2x4.00 ml INT. Pan ST20 VERTICAUX Rec: 40 cm 280X240 Nombre: 1.5 EXT. EXT. Pan PAF V VERTICAUX Rec: 40 cm Nombre: 1.5					

M2b

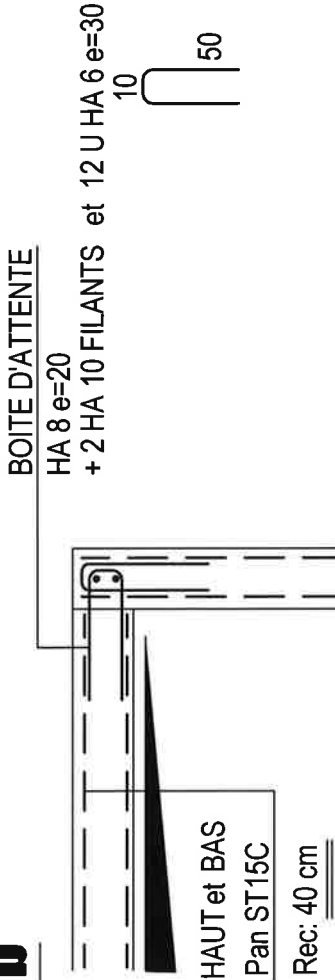

ANGLES MURS

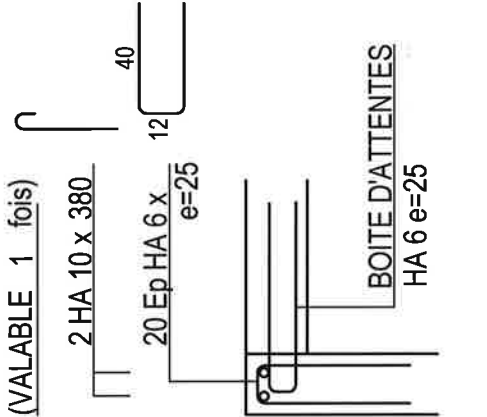


M3

28.00 ml Env.

E3

Nombre: 5

Rec: 50 cm

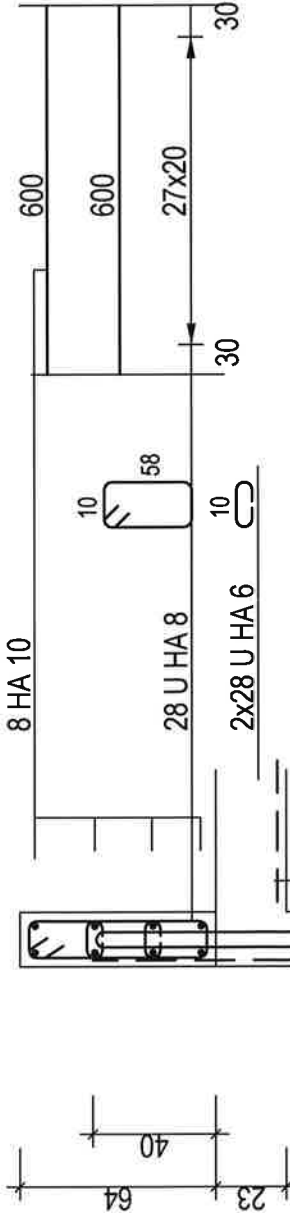

et 90 Ep HA 6 e=30

Lg: 2x30.00 ml

80

EXT.


INT.

Pan PAF V VERTICAUX

Rec: 40 cm


Nombre: 14

ANGLES MURS

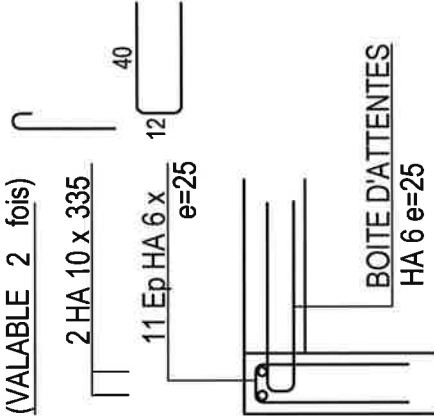

M3a

6.36 ml

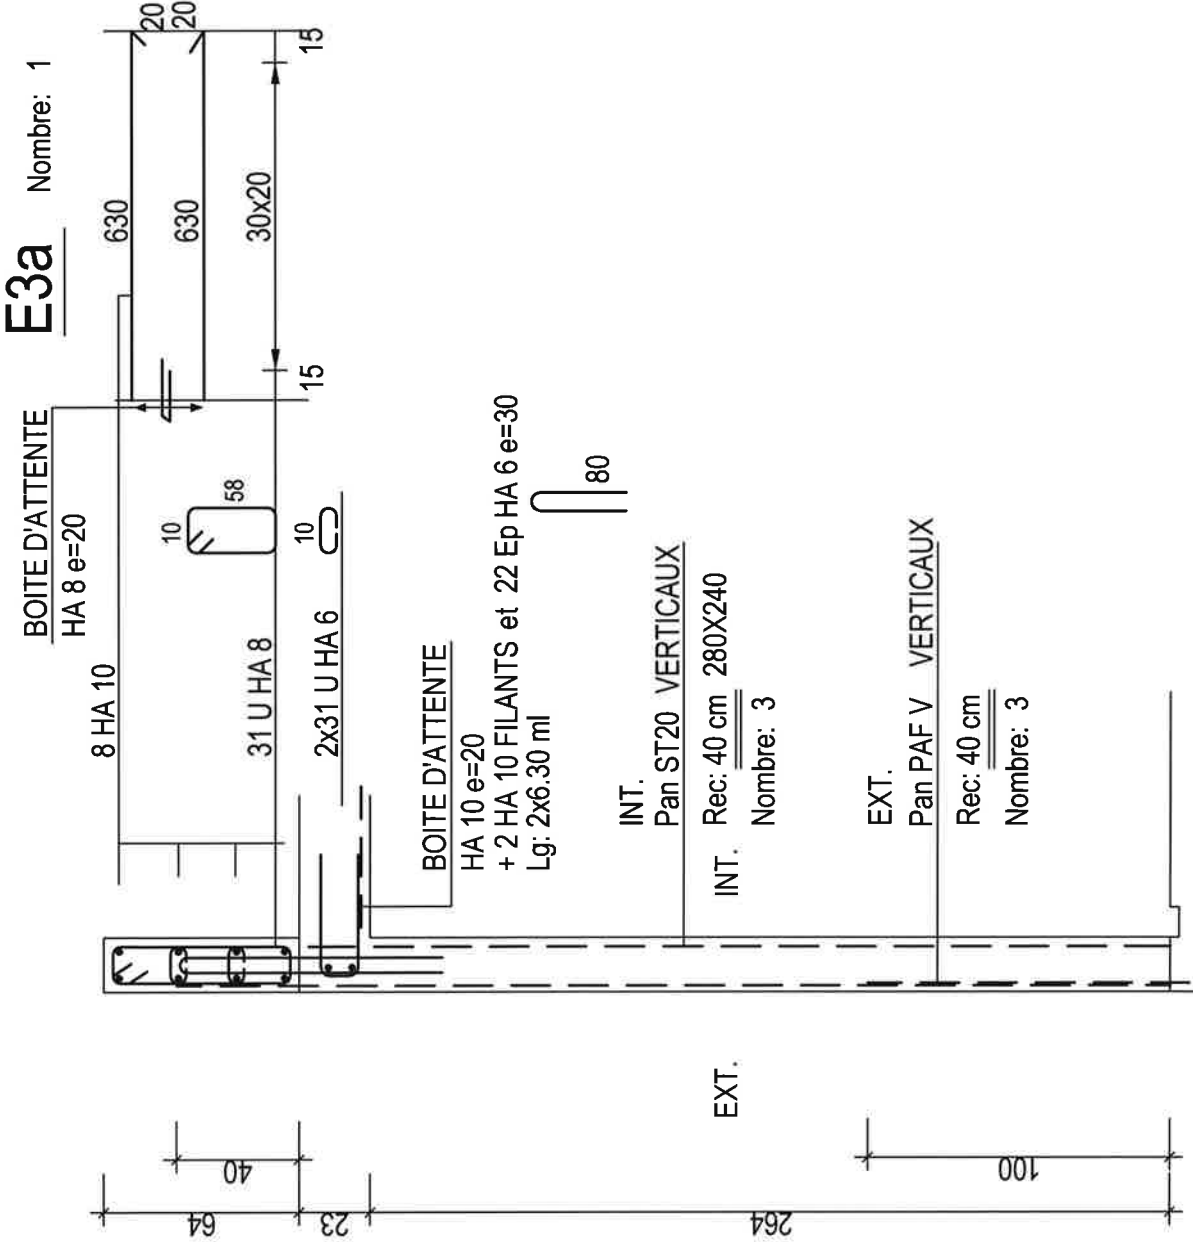


M5

Valable 3 fois

E5

Nombre: 3

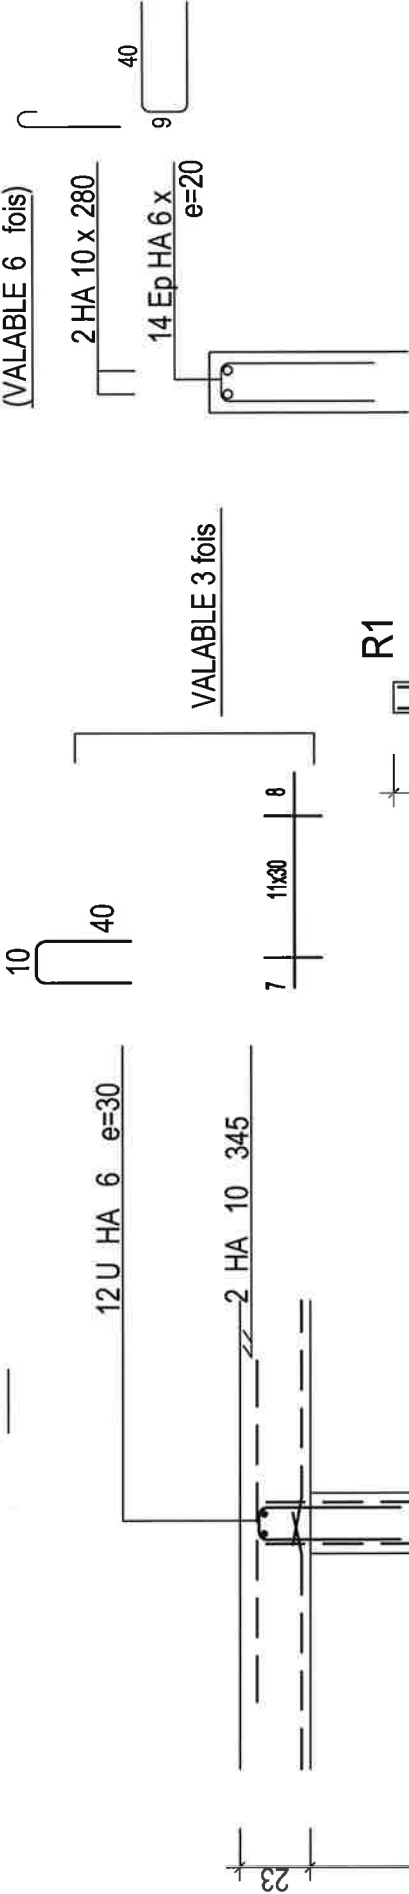

R1

R1

Chaque face


Pan ST20 VERTICAUX

Rec: 30 cm 2.80X240


Nombre: 2x2

MURS INTERIEURS AVEC CONTINUITE


30.00 ml Env:

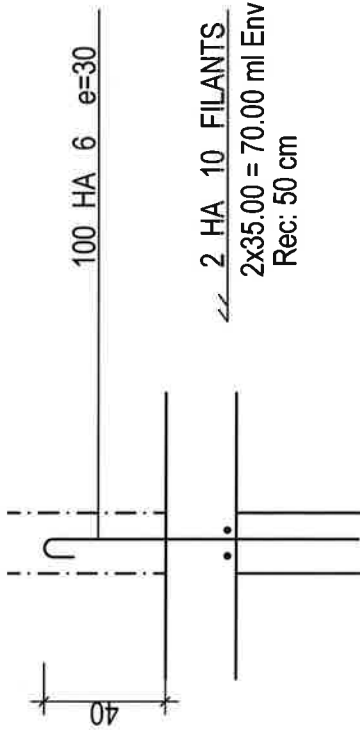


ARMATURES TETES DE MURS

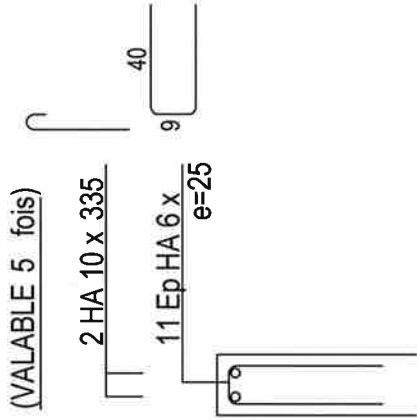

ANGLES MURS

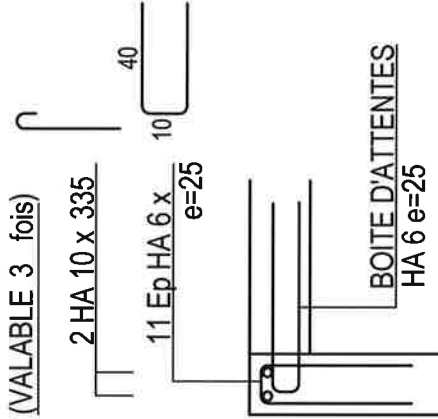


(VALABLE 1 fois)

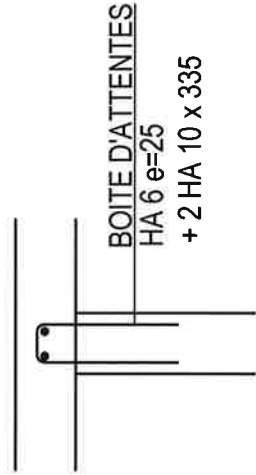


BOITE D'ATTENTES
HA 6 e=25
+ 2 HA 10 x 335

MURS INTERIEURS SANS CONTINUITE


55.00 ml Env:

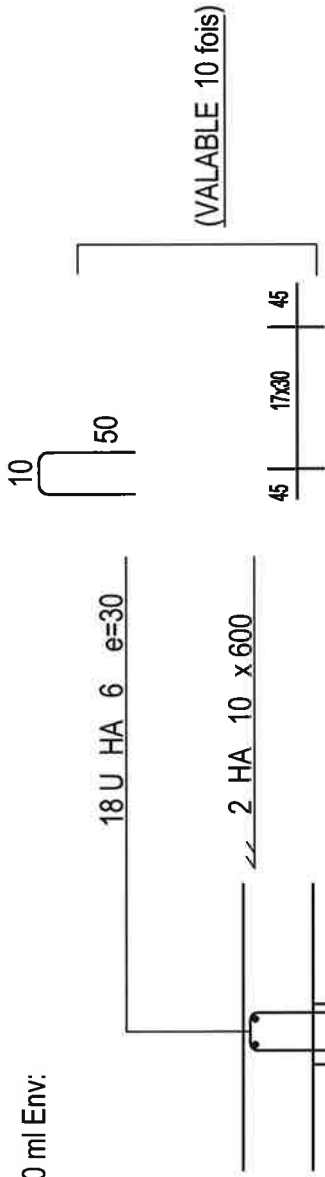


ARMATURES TETES DE MURS

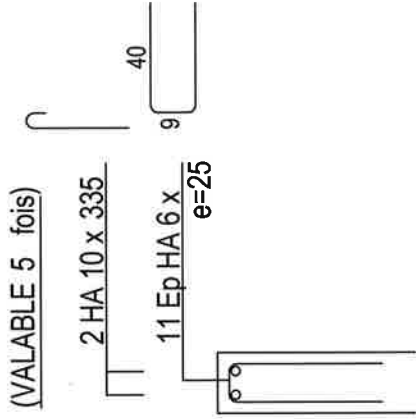


ANGLES MURS

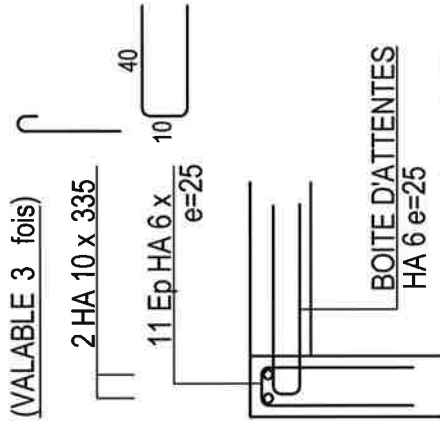

(VALABLE 1 fois)

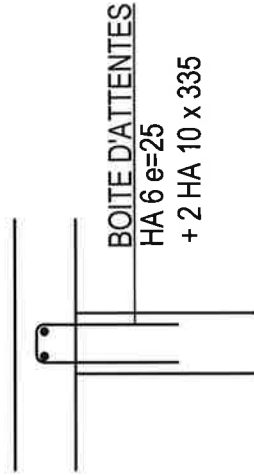

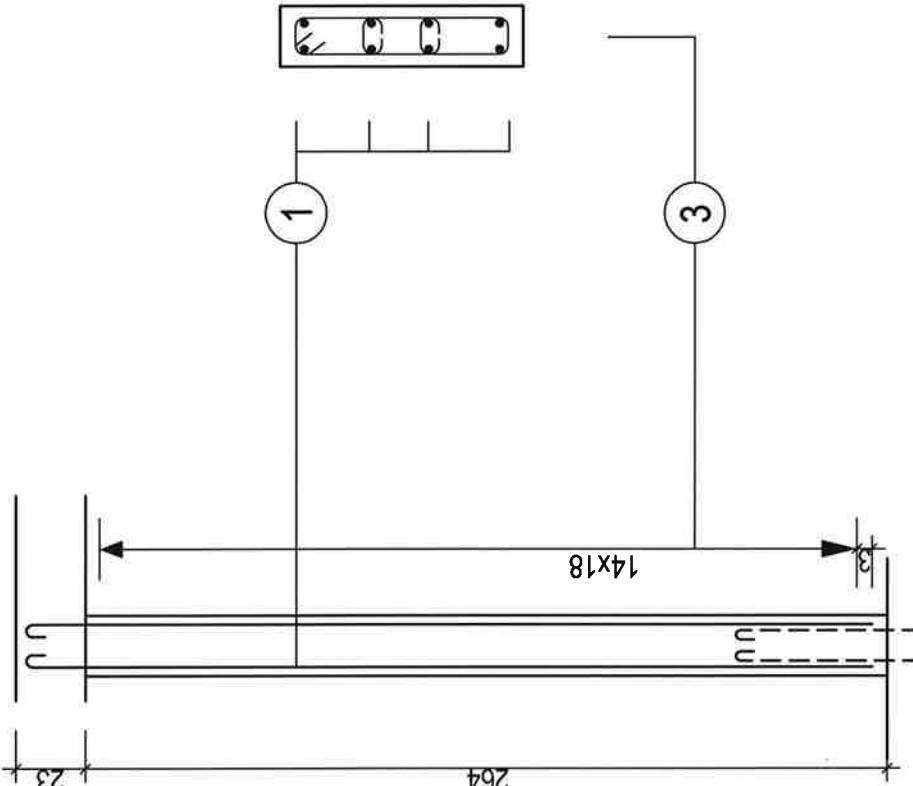AFF: S.13.12.119	Bât: C	LA MULATIERE-69350 LaMulatiere CREATION de LOGEMENTS	BA au -1 Aile OUEST	Plan n° C 21	Page: 13	
P3 Nombre: 6 20x80						
			①	8 HA 12 x	C 277	
			②			
			③	15 HA 6 x	74 14	
			④	2x15 HA 6 x	14	
			⑤			
			⑥			
			⑦			
			⑧			
			⑨			
			⑩			
			⑪			
			⑫			
			⑬			
			⑭			
			⑮			

