

NOAHO

Chemin de Fontanière - 69350 La Mulatière

Création de logements

Les entreprises réalisant les travaux devront tenir compte des derniers plans architecte lors de la réalisation des travaux
Les plans du be MATTE ne doivent servir qu'au corps d'état concerné et doivent être des plans d'exécution.

ARCHITECTE(S): Atelier D'IS
BET STRUCTURE: MATTE SAS
BET FLUIDES: PRELEM
ECONOMISTE: EXECO
BUREAU DE CONTROLE: Bureau VERITAS

MO DELEGUE:
MOE: PSO Ingénierie
CSPS: SUD EST COORDINATION
OPC:
ENTREPRISE(S): Fontanel-pbc

Bât: C Aile OUEST
PLANCHER sur -1
POUTRES et BN

DOE

Contrainte de sol:

Aciers HA (T) FeE500
Aciers Doux (Ø) FeE 235
Aciers TS FeE 500
Béton fc28 >= 25MPa
Enrobage = 3 cm

PLAN N°
C22 0


DATE : 30/06/2015


MATTÉ
BUREAU D'ÉTUDES
STRUCTURES ET FLUIDES


119 BOULEVARD STALINGRAD 69100 VILLEURBANNE
Tél. 04 72 44 02 87 Fax 04 72 44 26 59
E-mail : bet@matte.fr

Dessiné par : J.BO
Contrôlé par : P.LIN
Echelle : 1/50°

Affaire N°
13.12.119

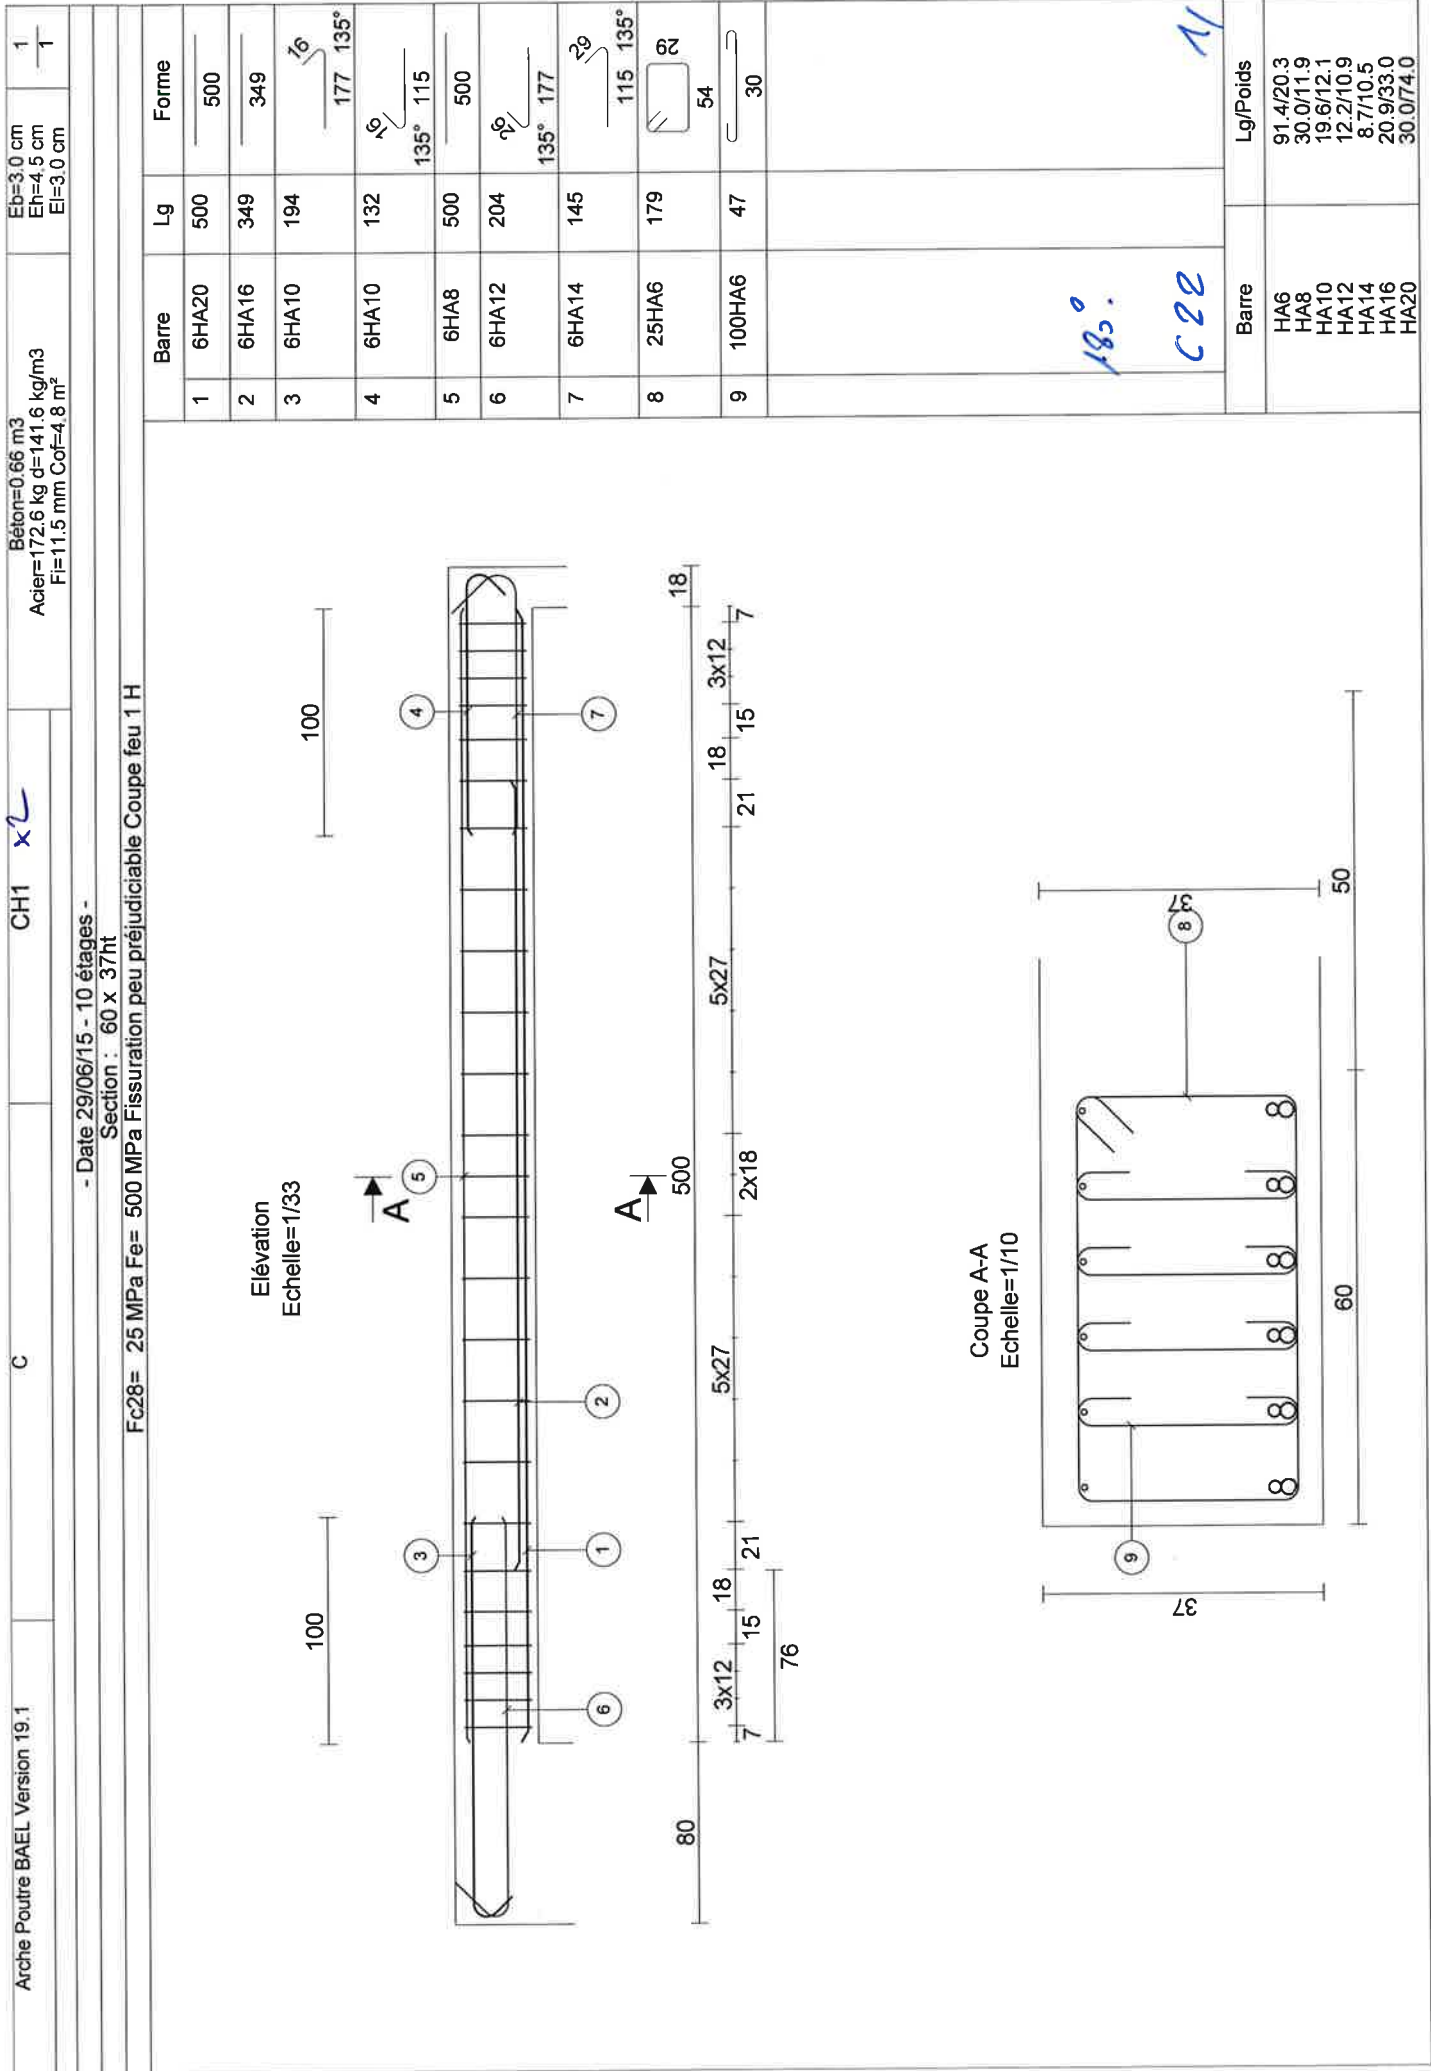

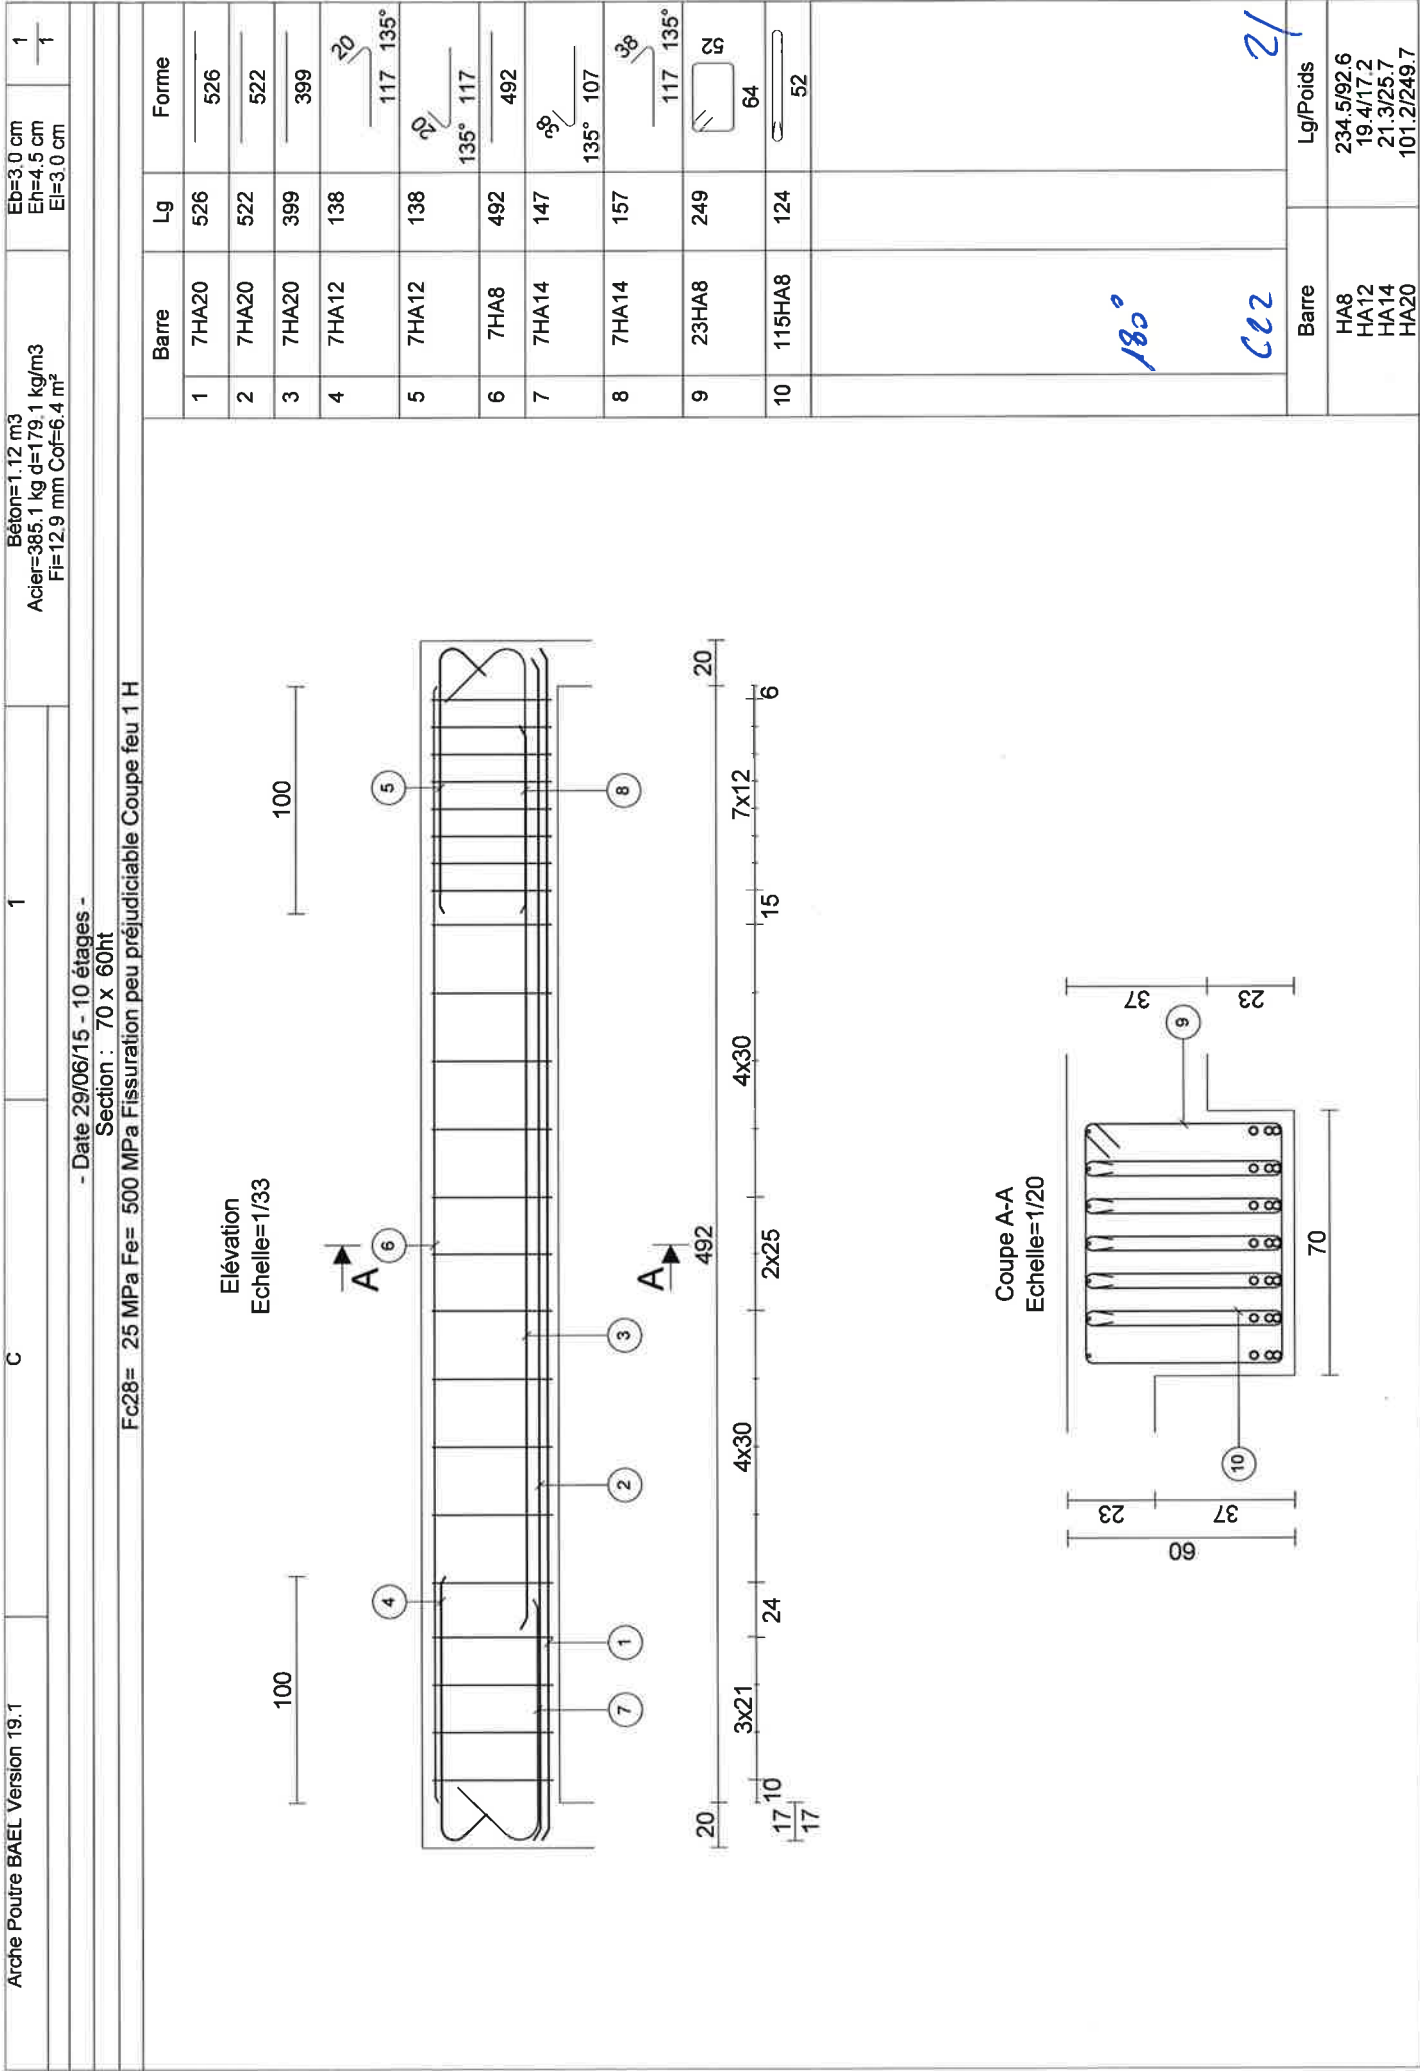


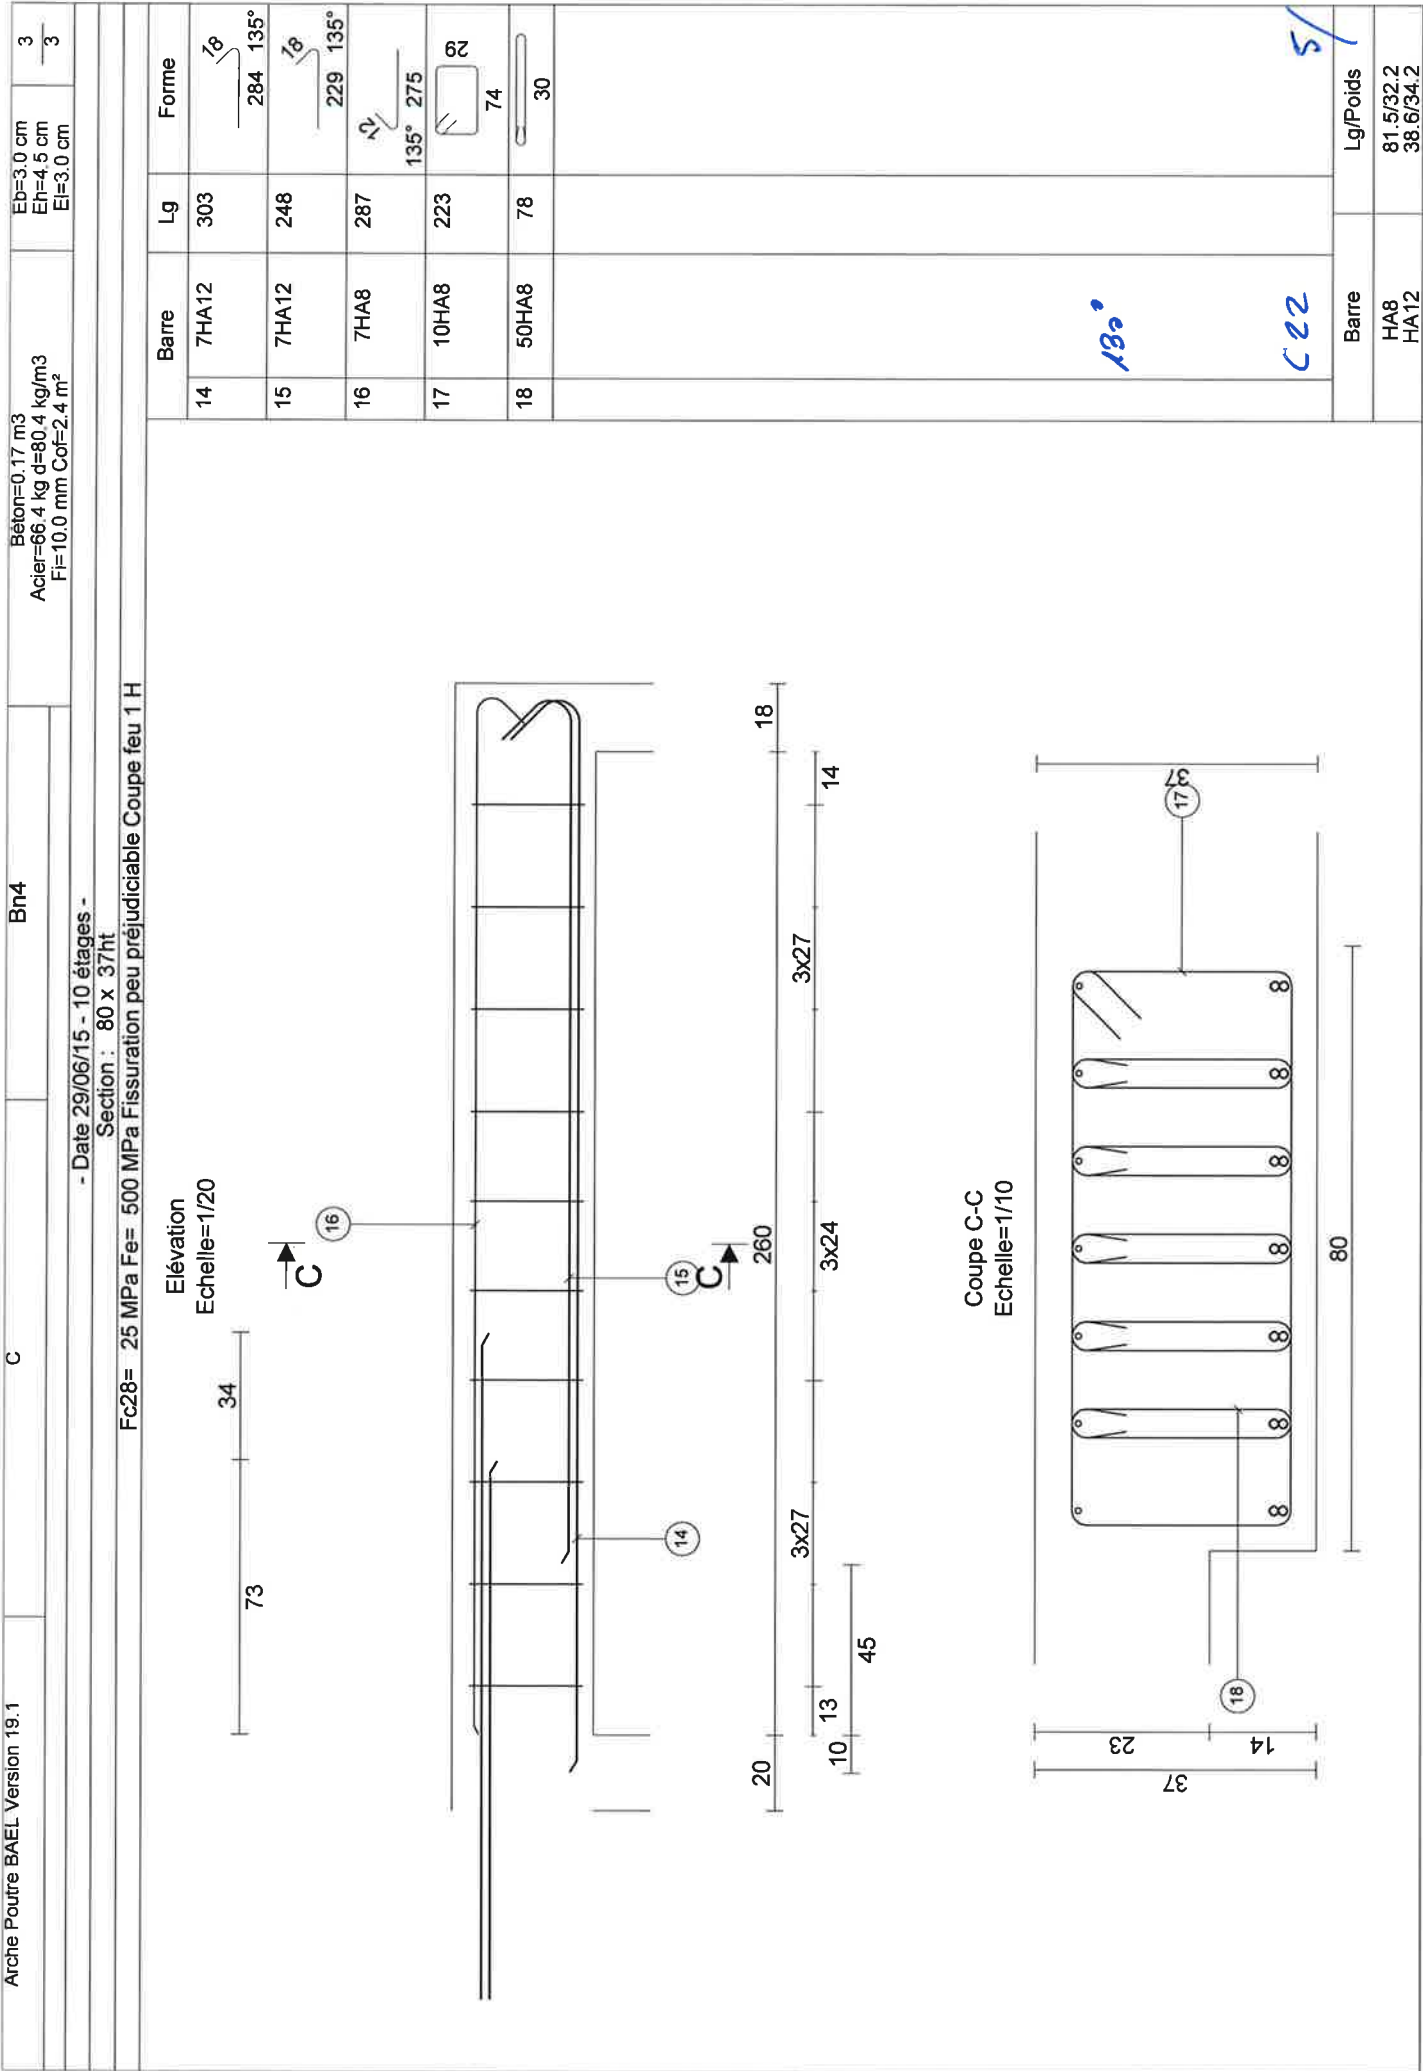


- Date 29/06/15 - 10 étages -


Section : 80 x 37ht


Fc28= 25 MPa Fe= 500 MPa Fissuration peu préjudiciable Coupe feu 1 H

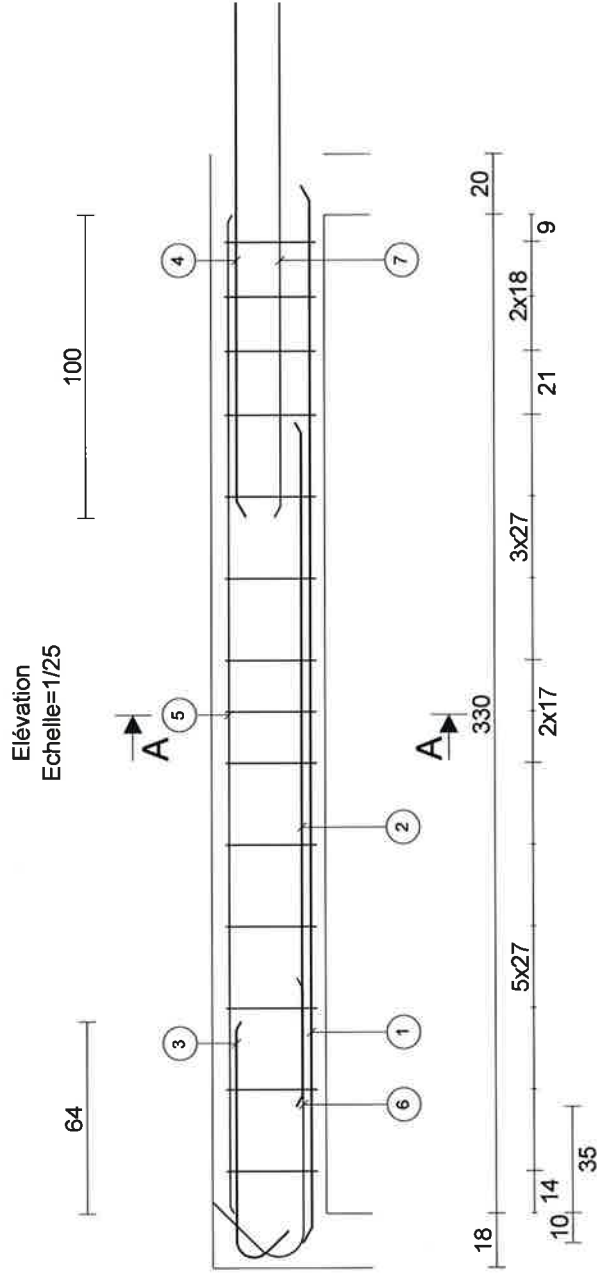
[illegible]


Arche Poutre BAEL Version 19.1	C	Bn6	Béton=0.16 m3 Acier=75.3 kg d=93.2 kg/m3 Fi=11.3 mm Cof=2.4 m²	2 9
- Date 29/06/15 - 10 étages - Section : 80 x 37ht				
Fc28= 25 MPa Fe= 500 MPa Fissuration peu préjudiciable Coupe feu 1 H				
Elévation Echelle=1/20				
Coupe B-B Echelle=1/10				
10	7HA10	273		273
11	7HA10	173		173
12	7HA12	200		200
13	7HA8	253		253
15	7HA12	200		200
16	10HA8	223		74 30
17	50HA8	78		
180°				
222				7/
Barre		Lg/Poids		
HA8		79.1/31.2		
HA10		31.2/19.3		
HA12		28.0/24.9		

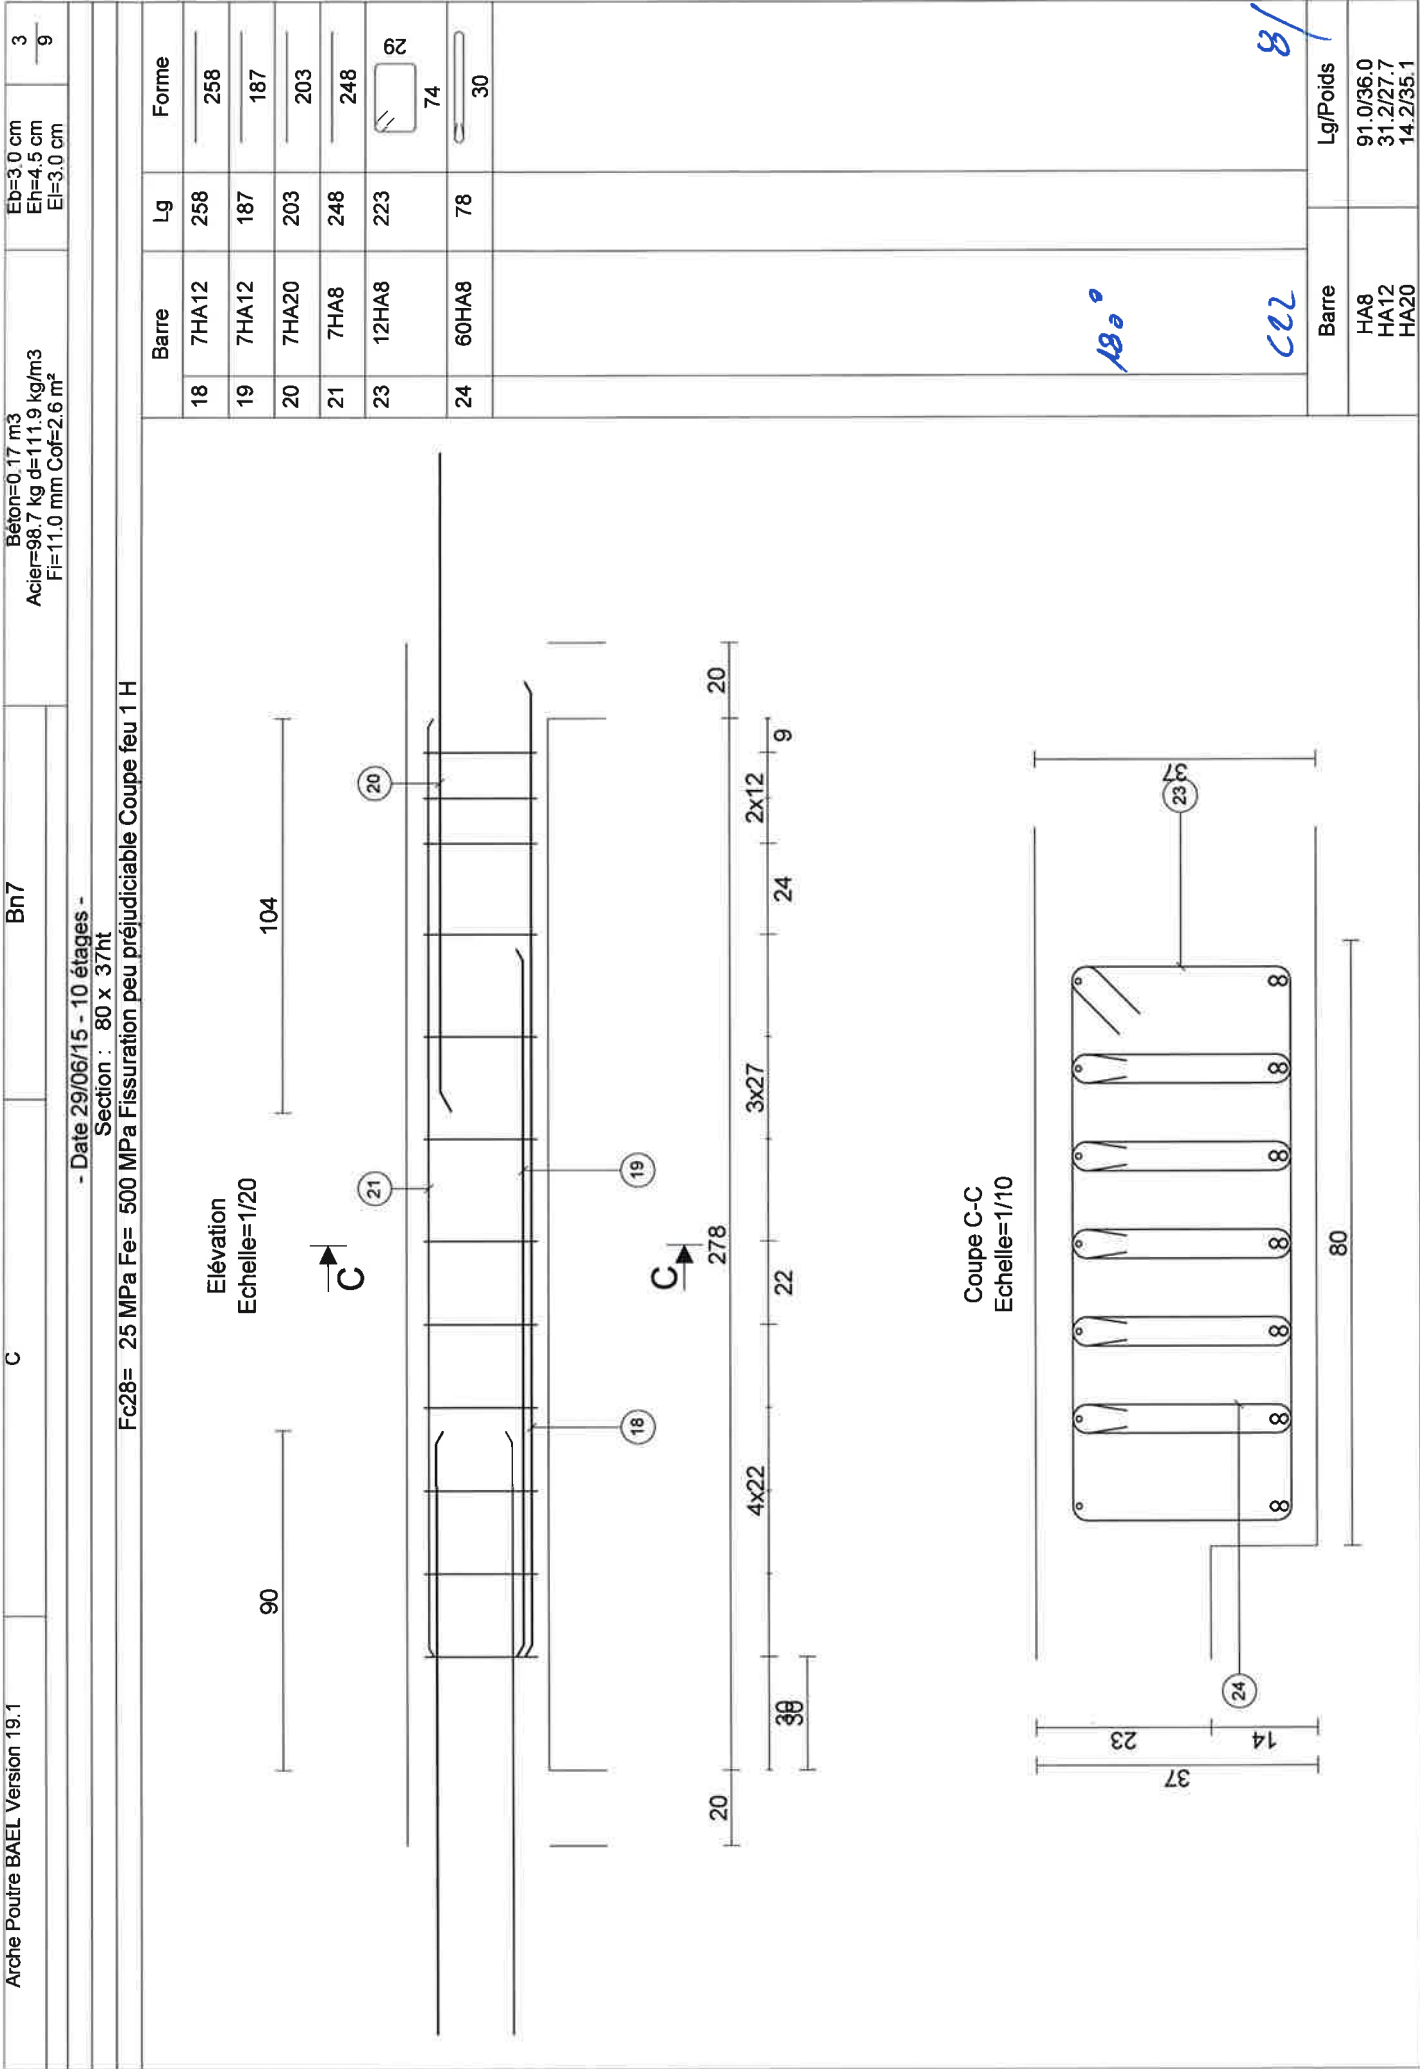


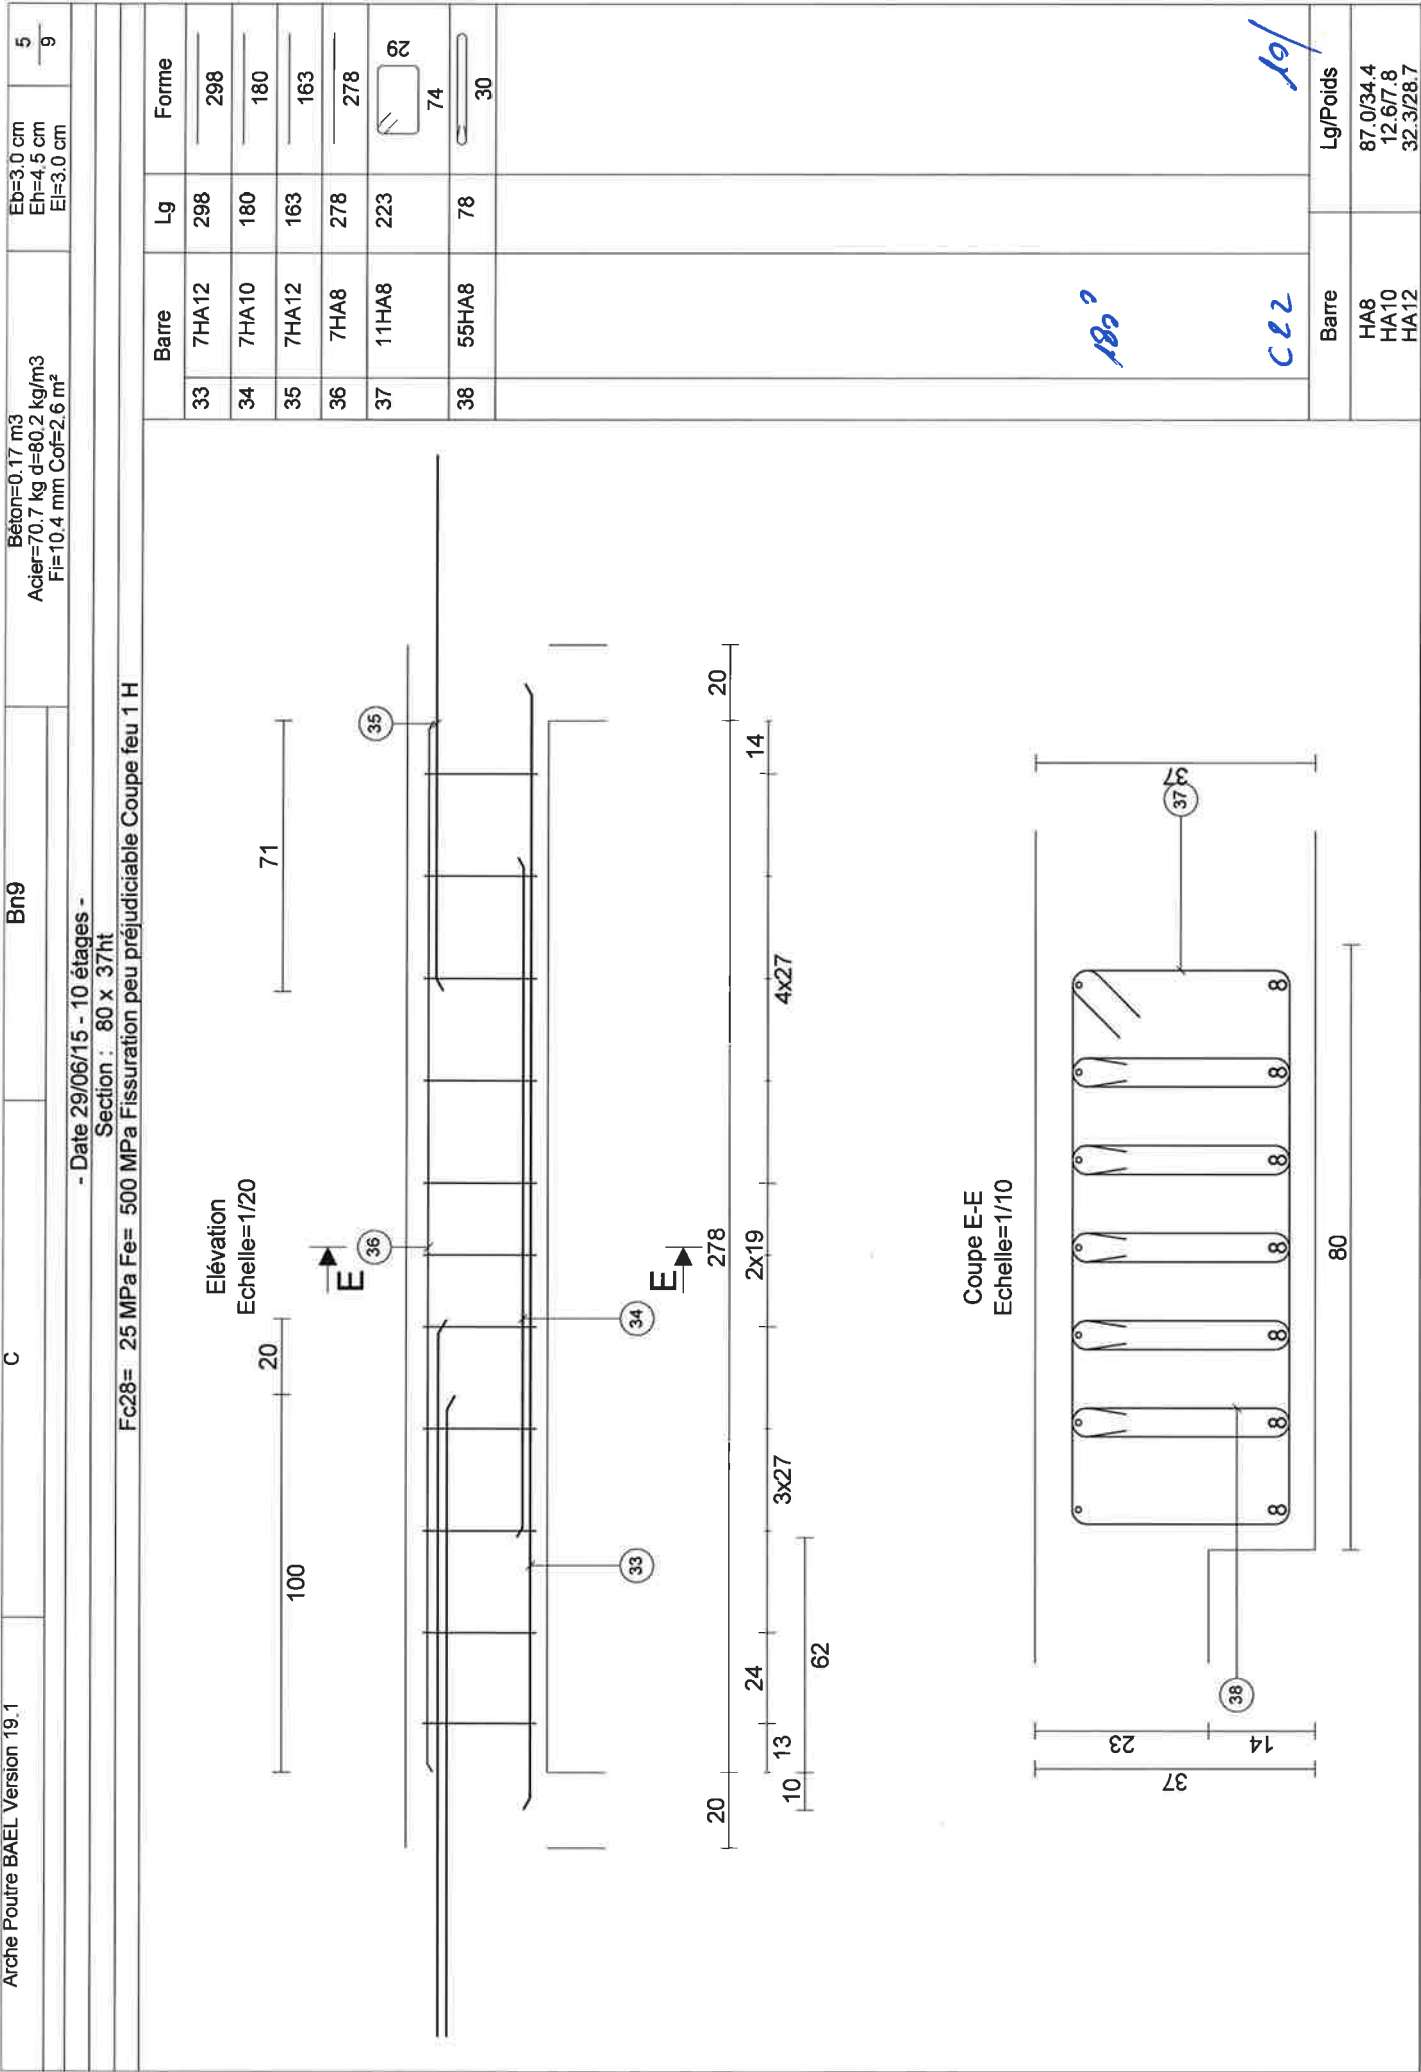

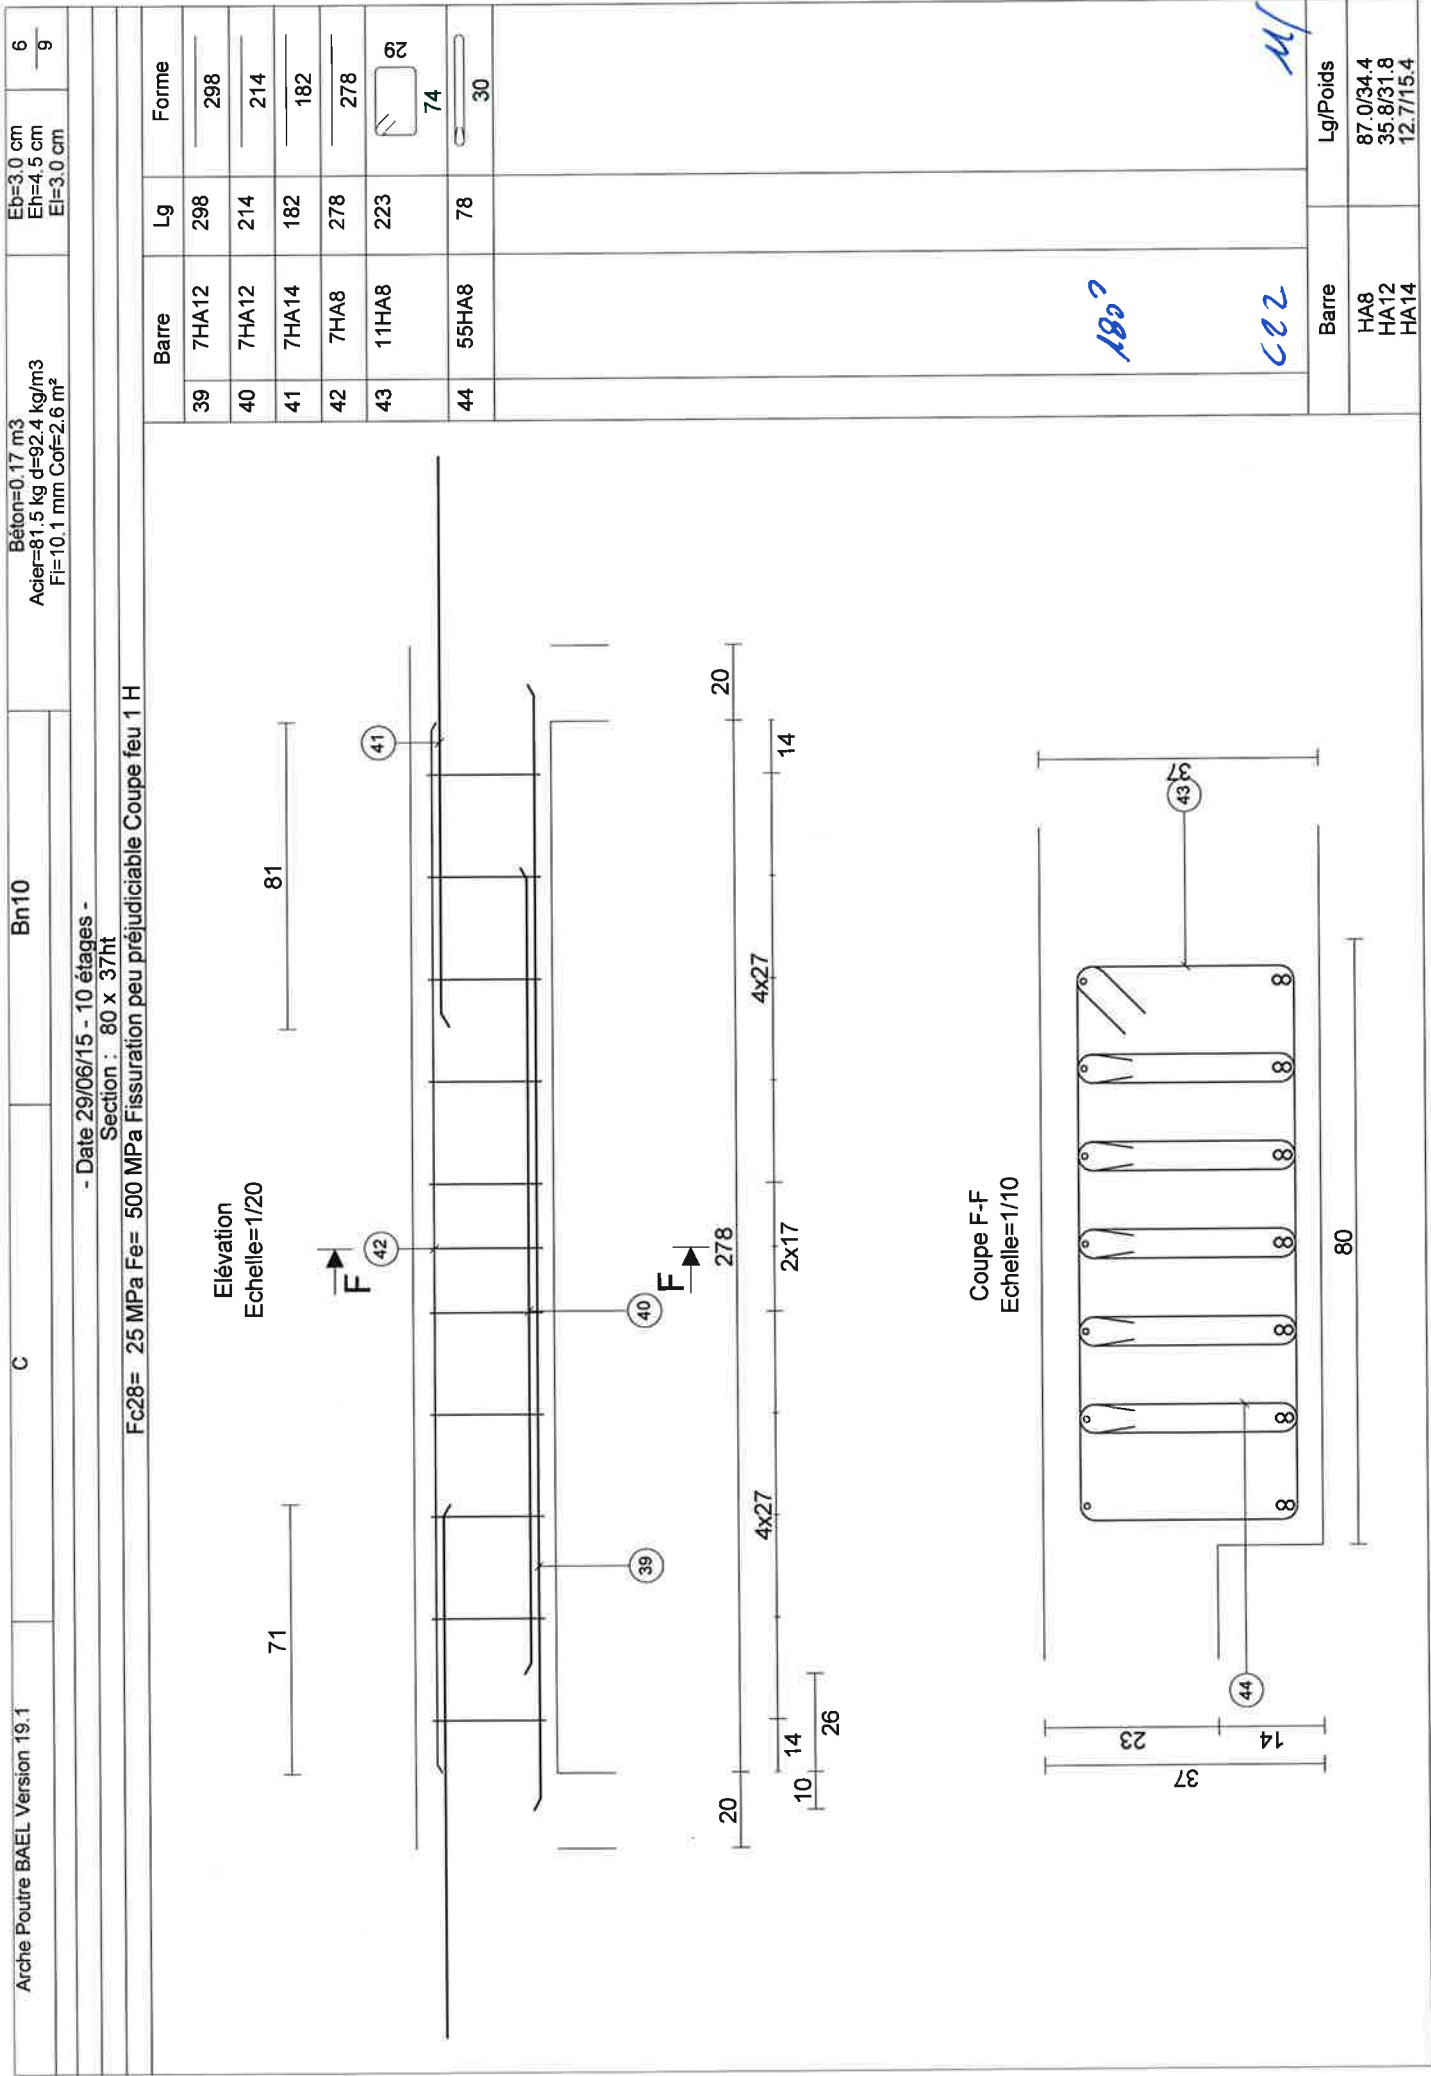

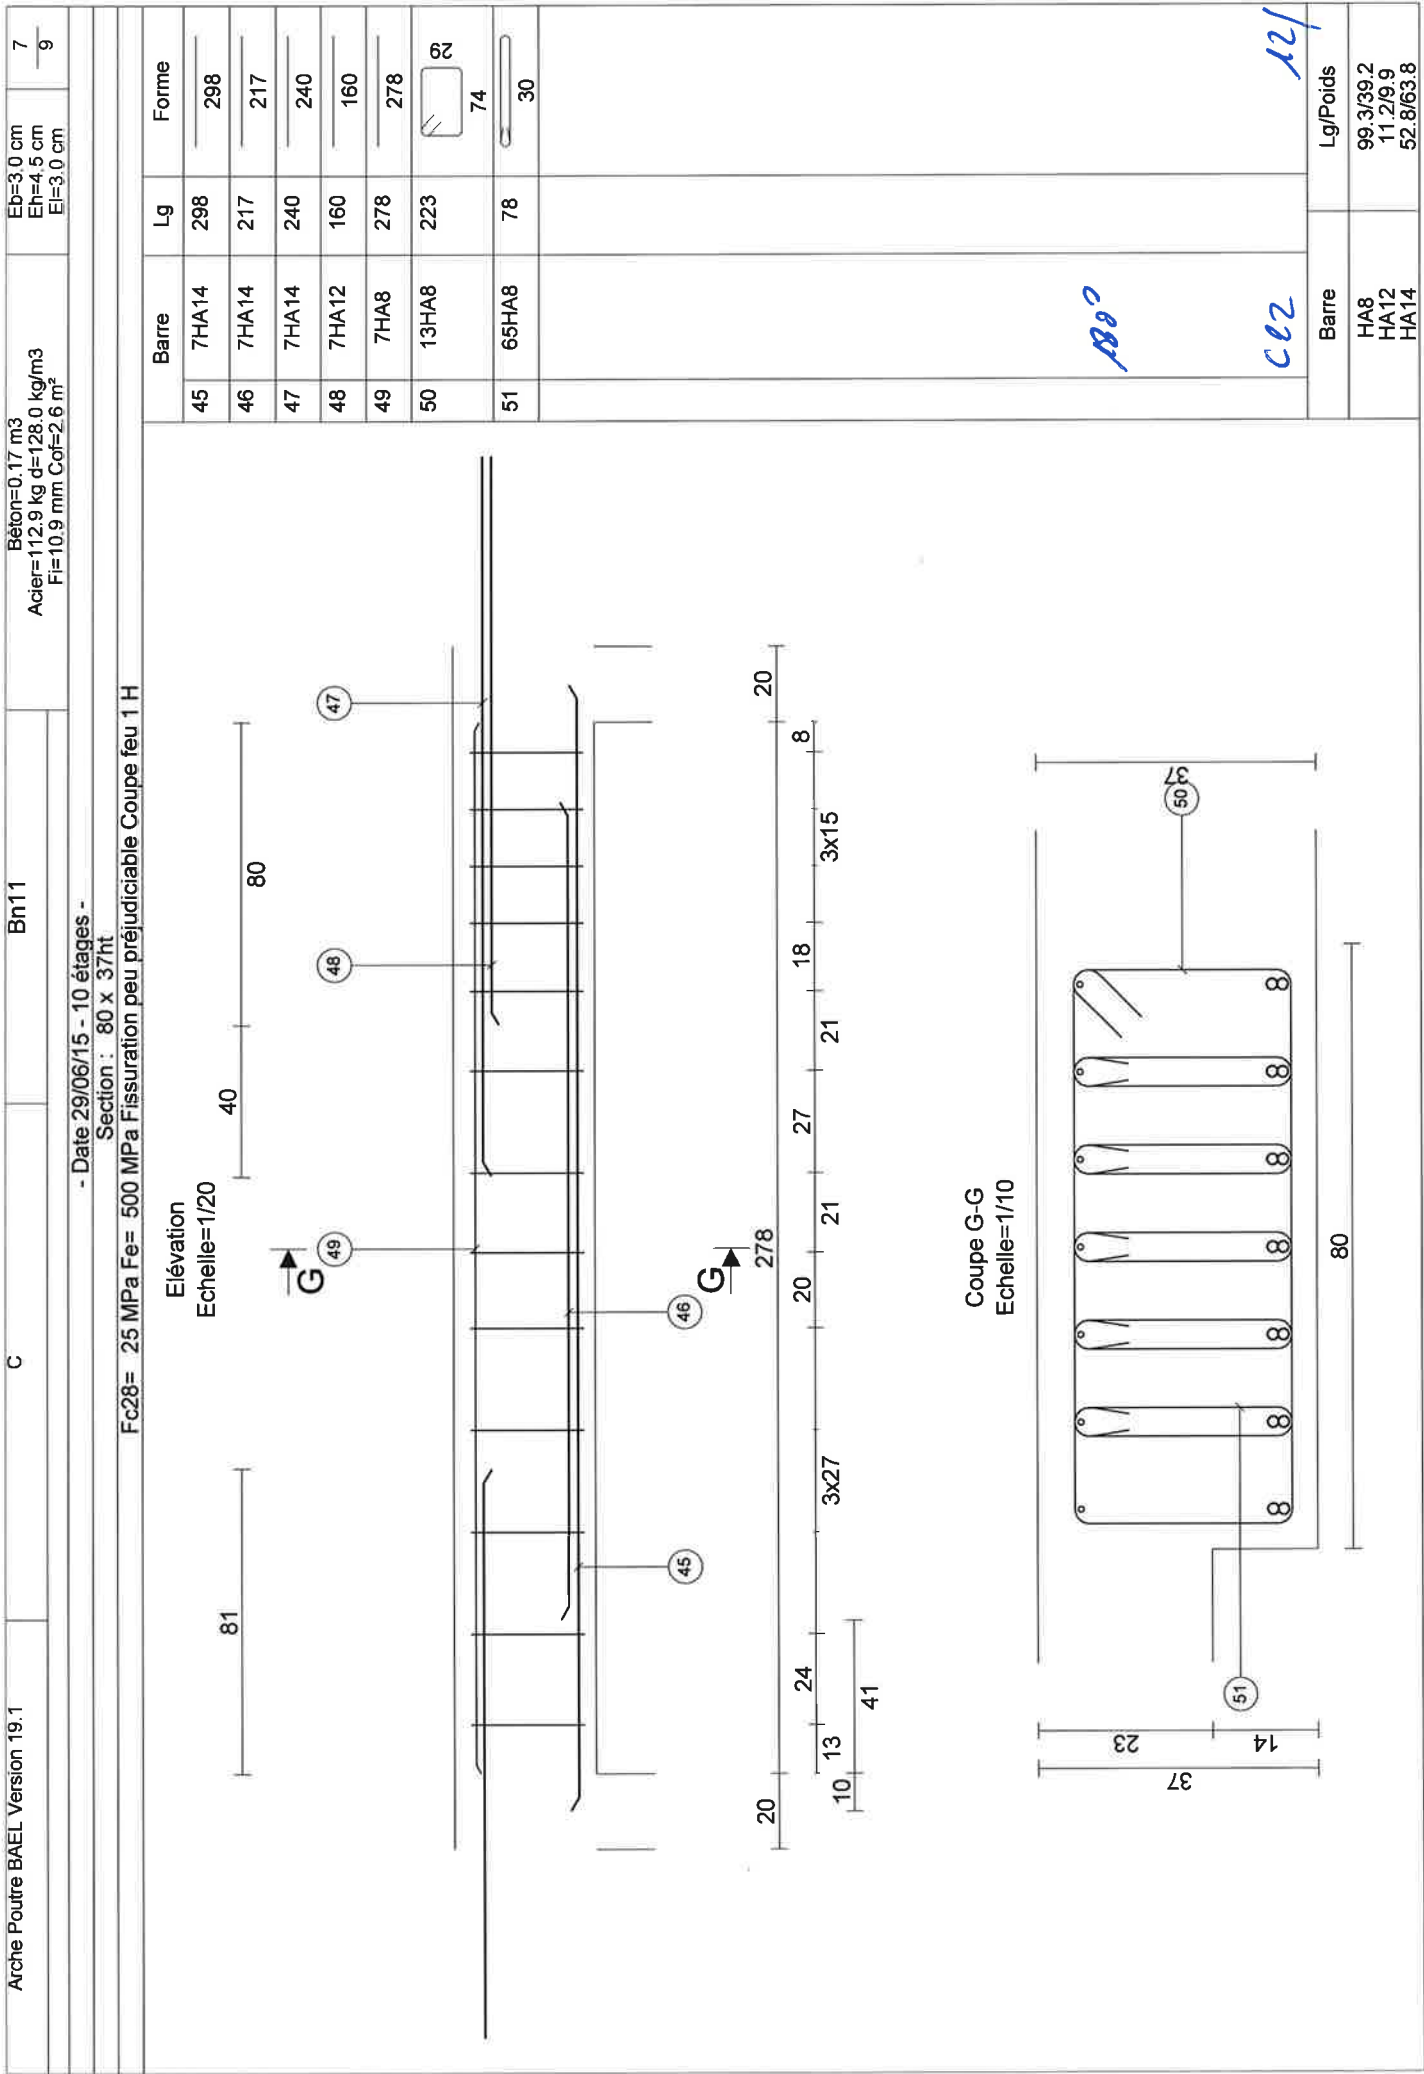



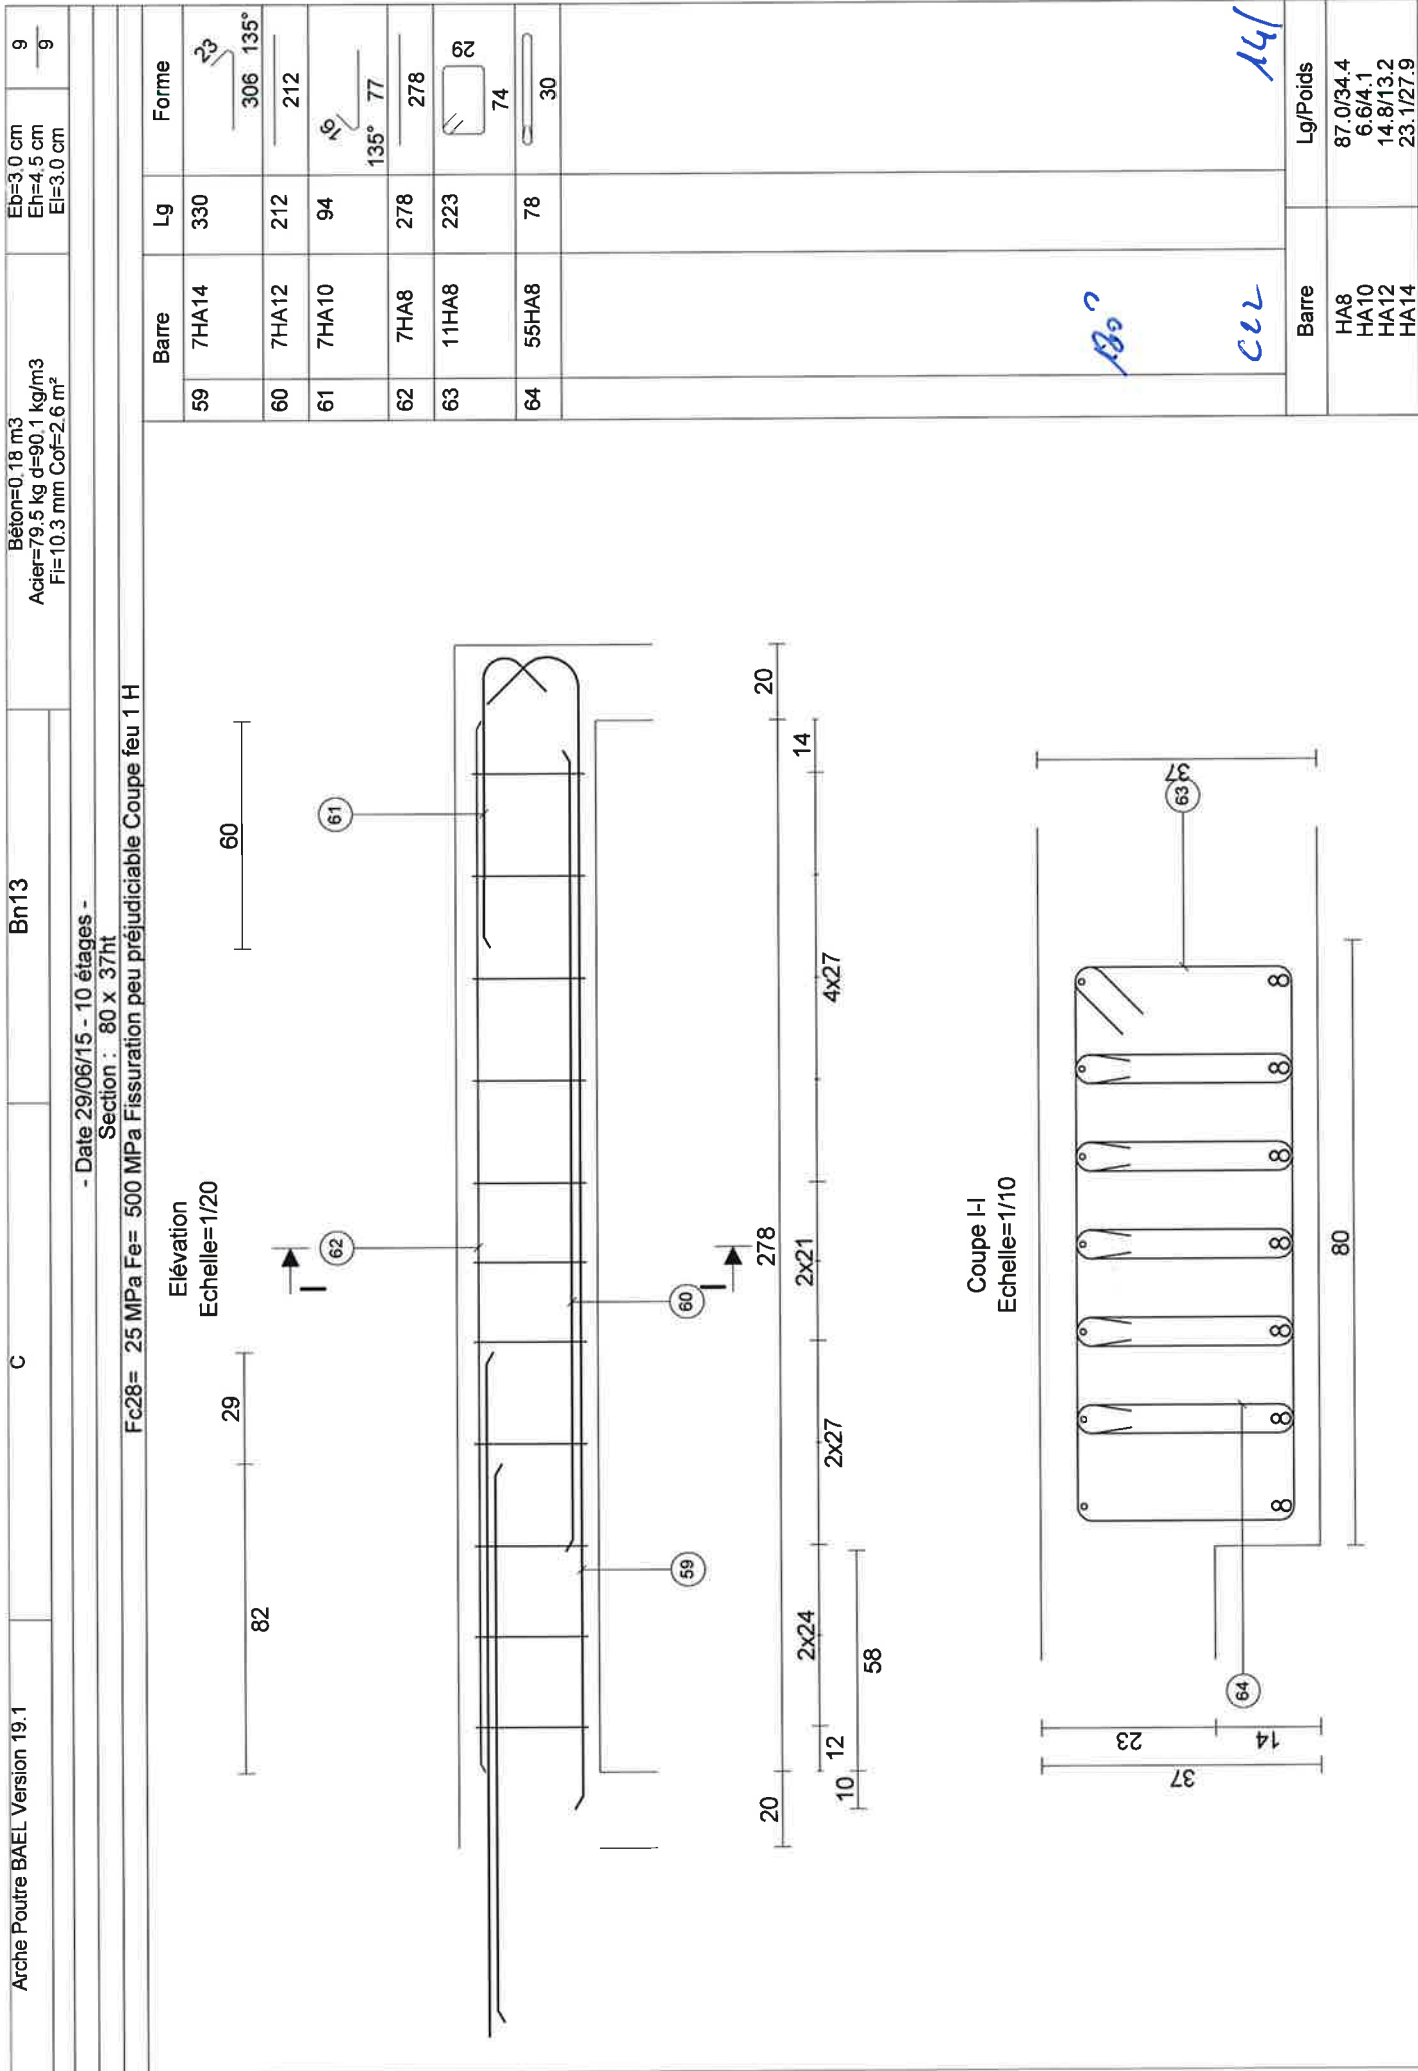


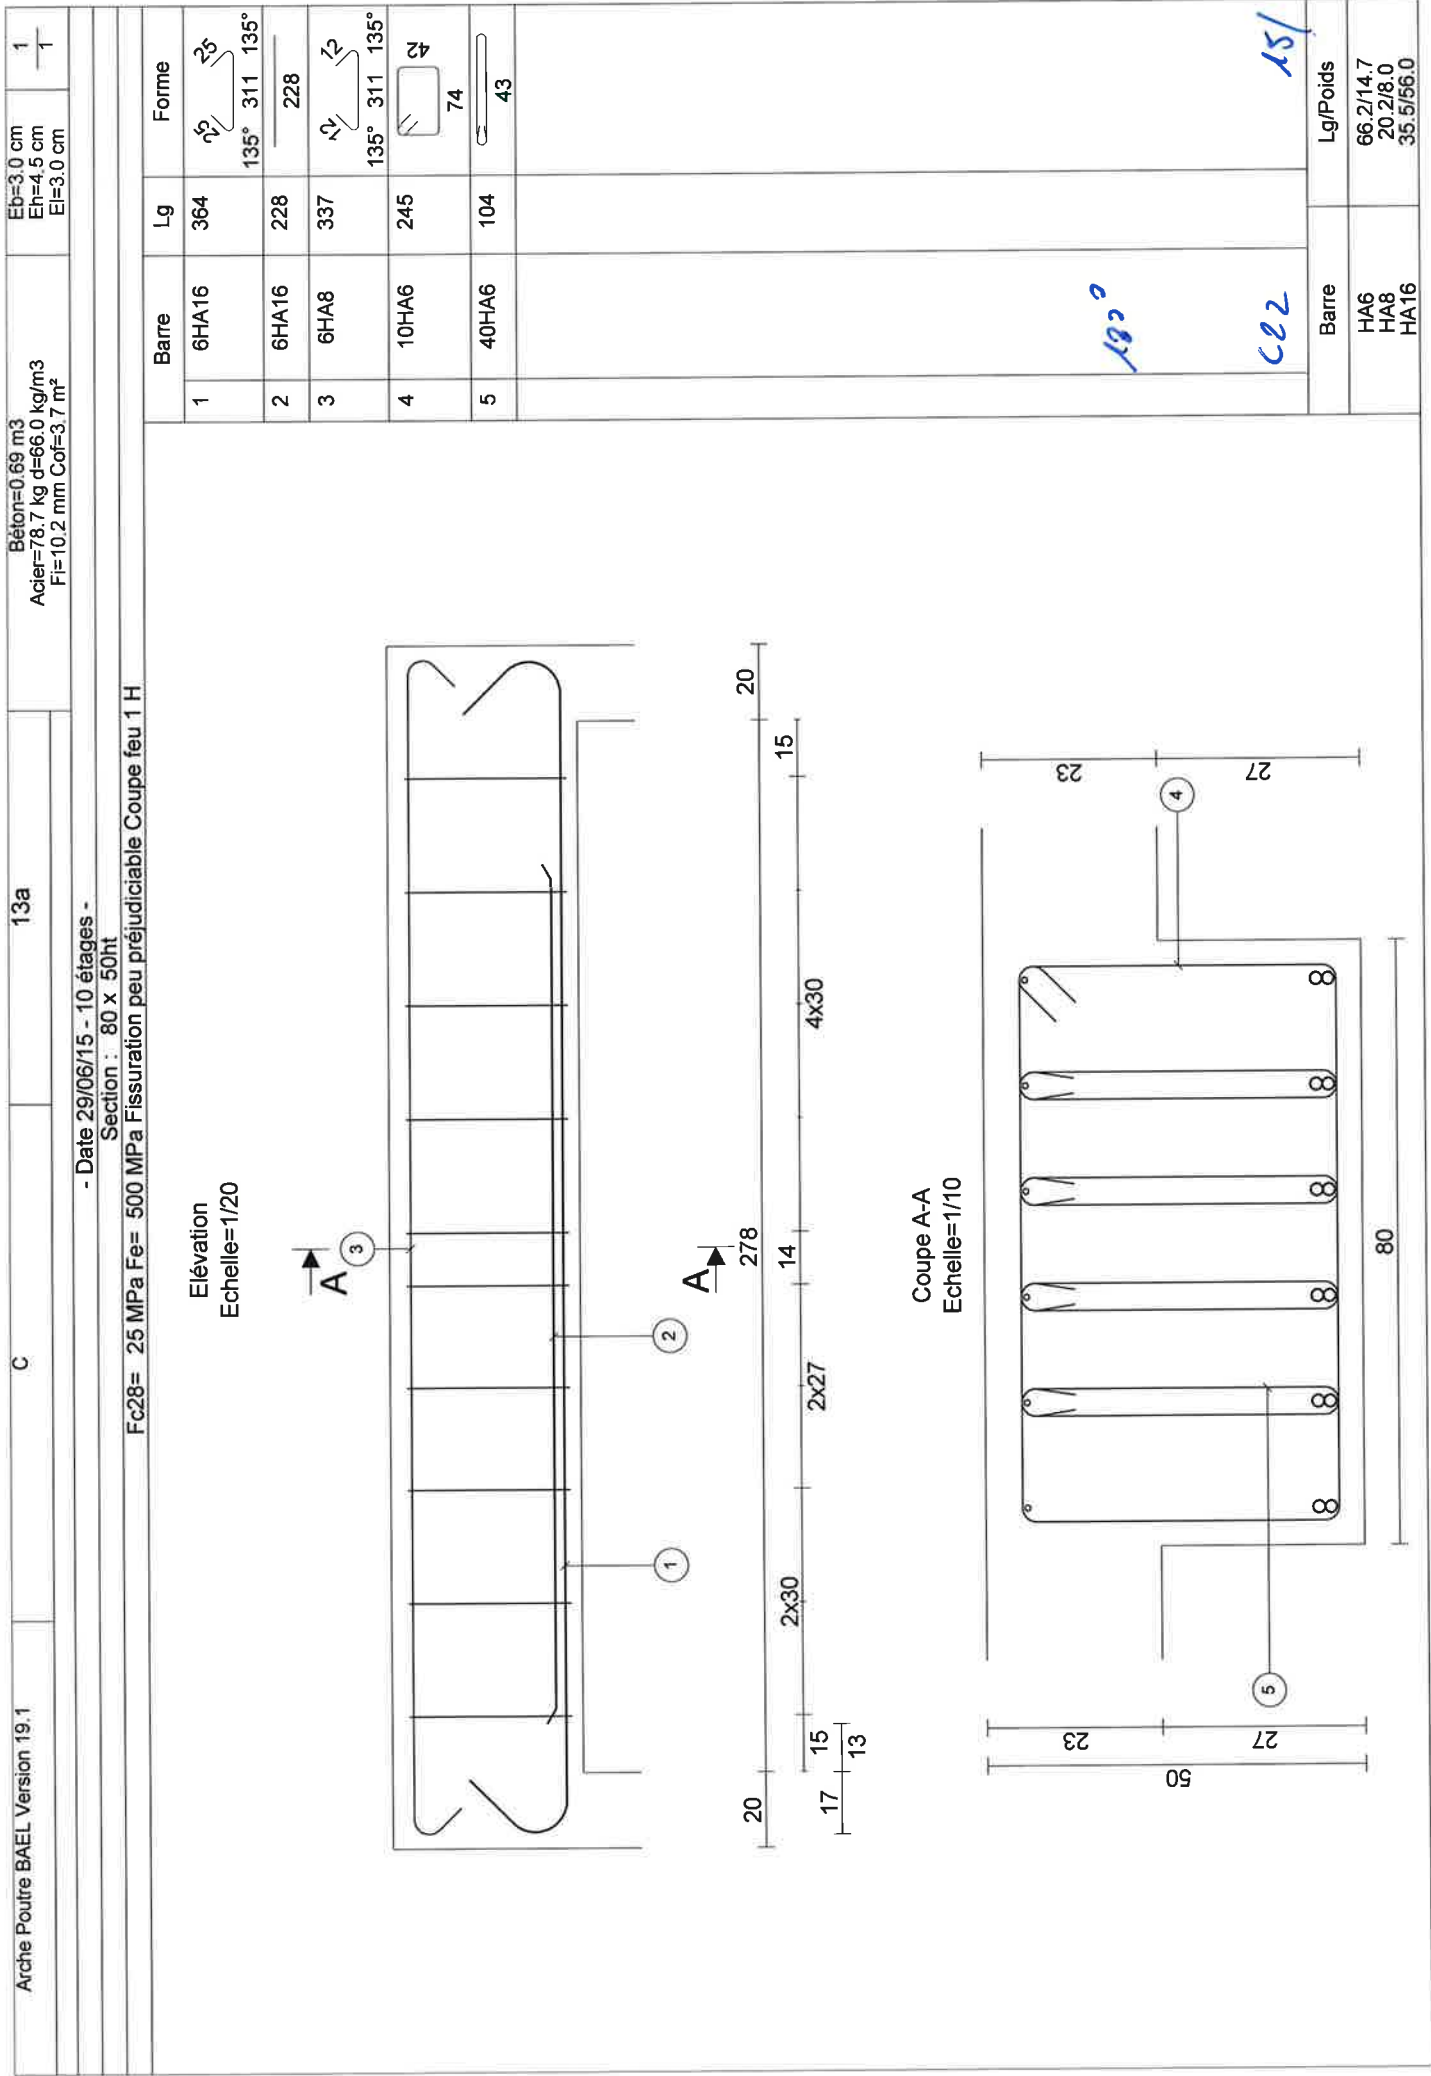



- Date 29/06/15 - 10 étages -

Section : 40 x 82ht

FC28= 25 MPa Fe= 500 MPa Fissuration peu préjudiciable Coupe feu 1 H

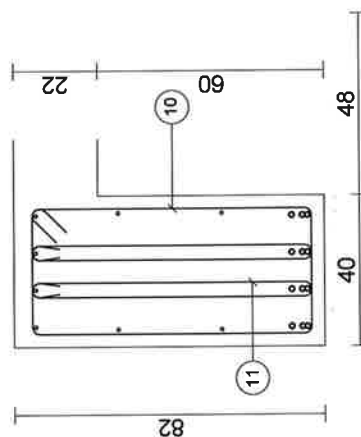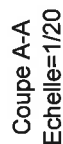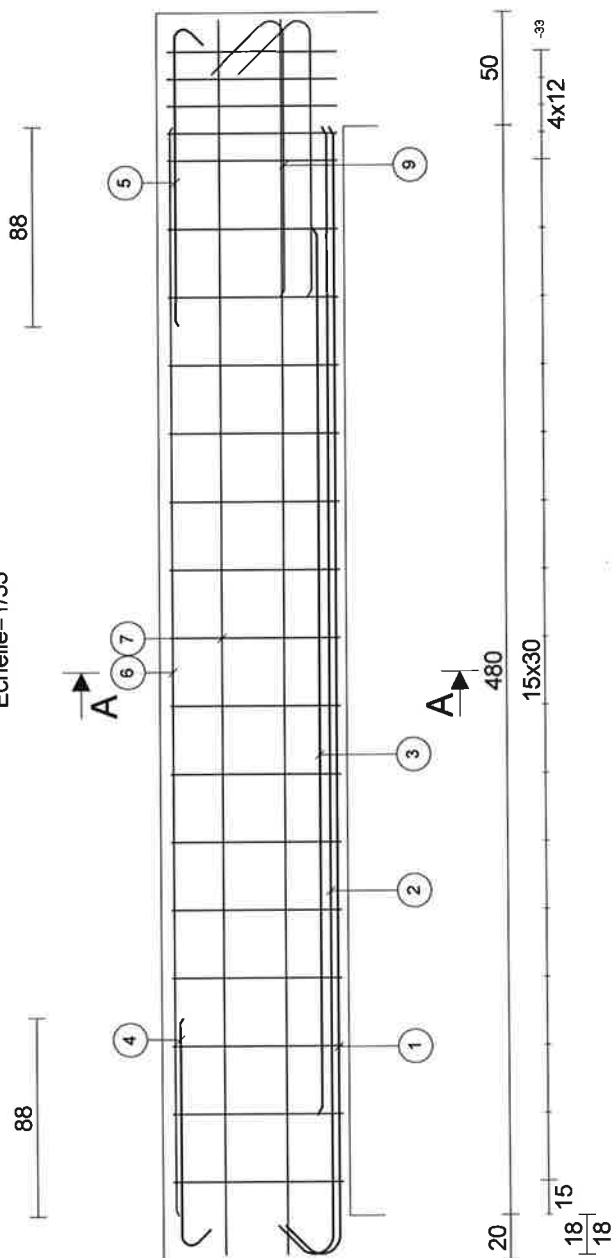

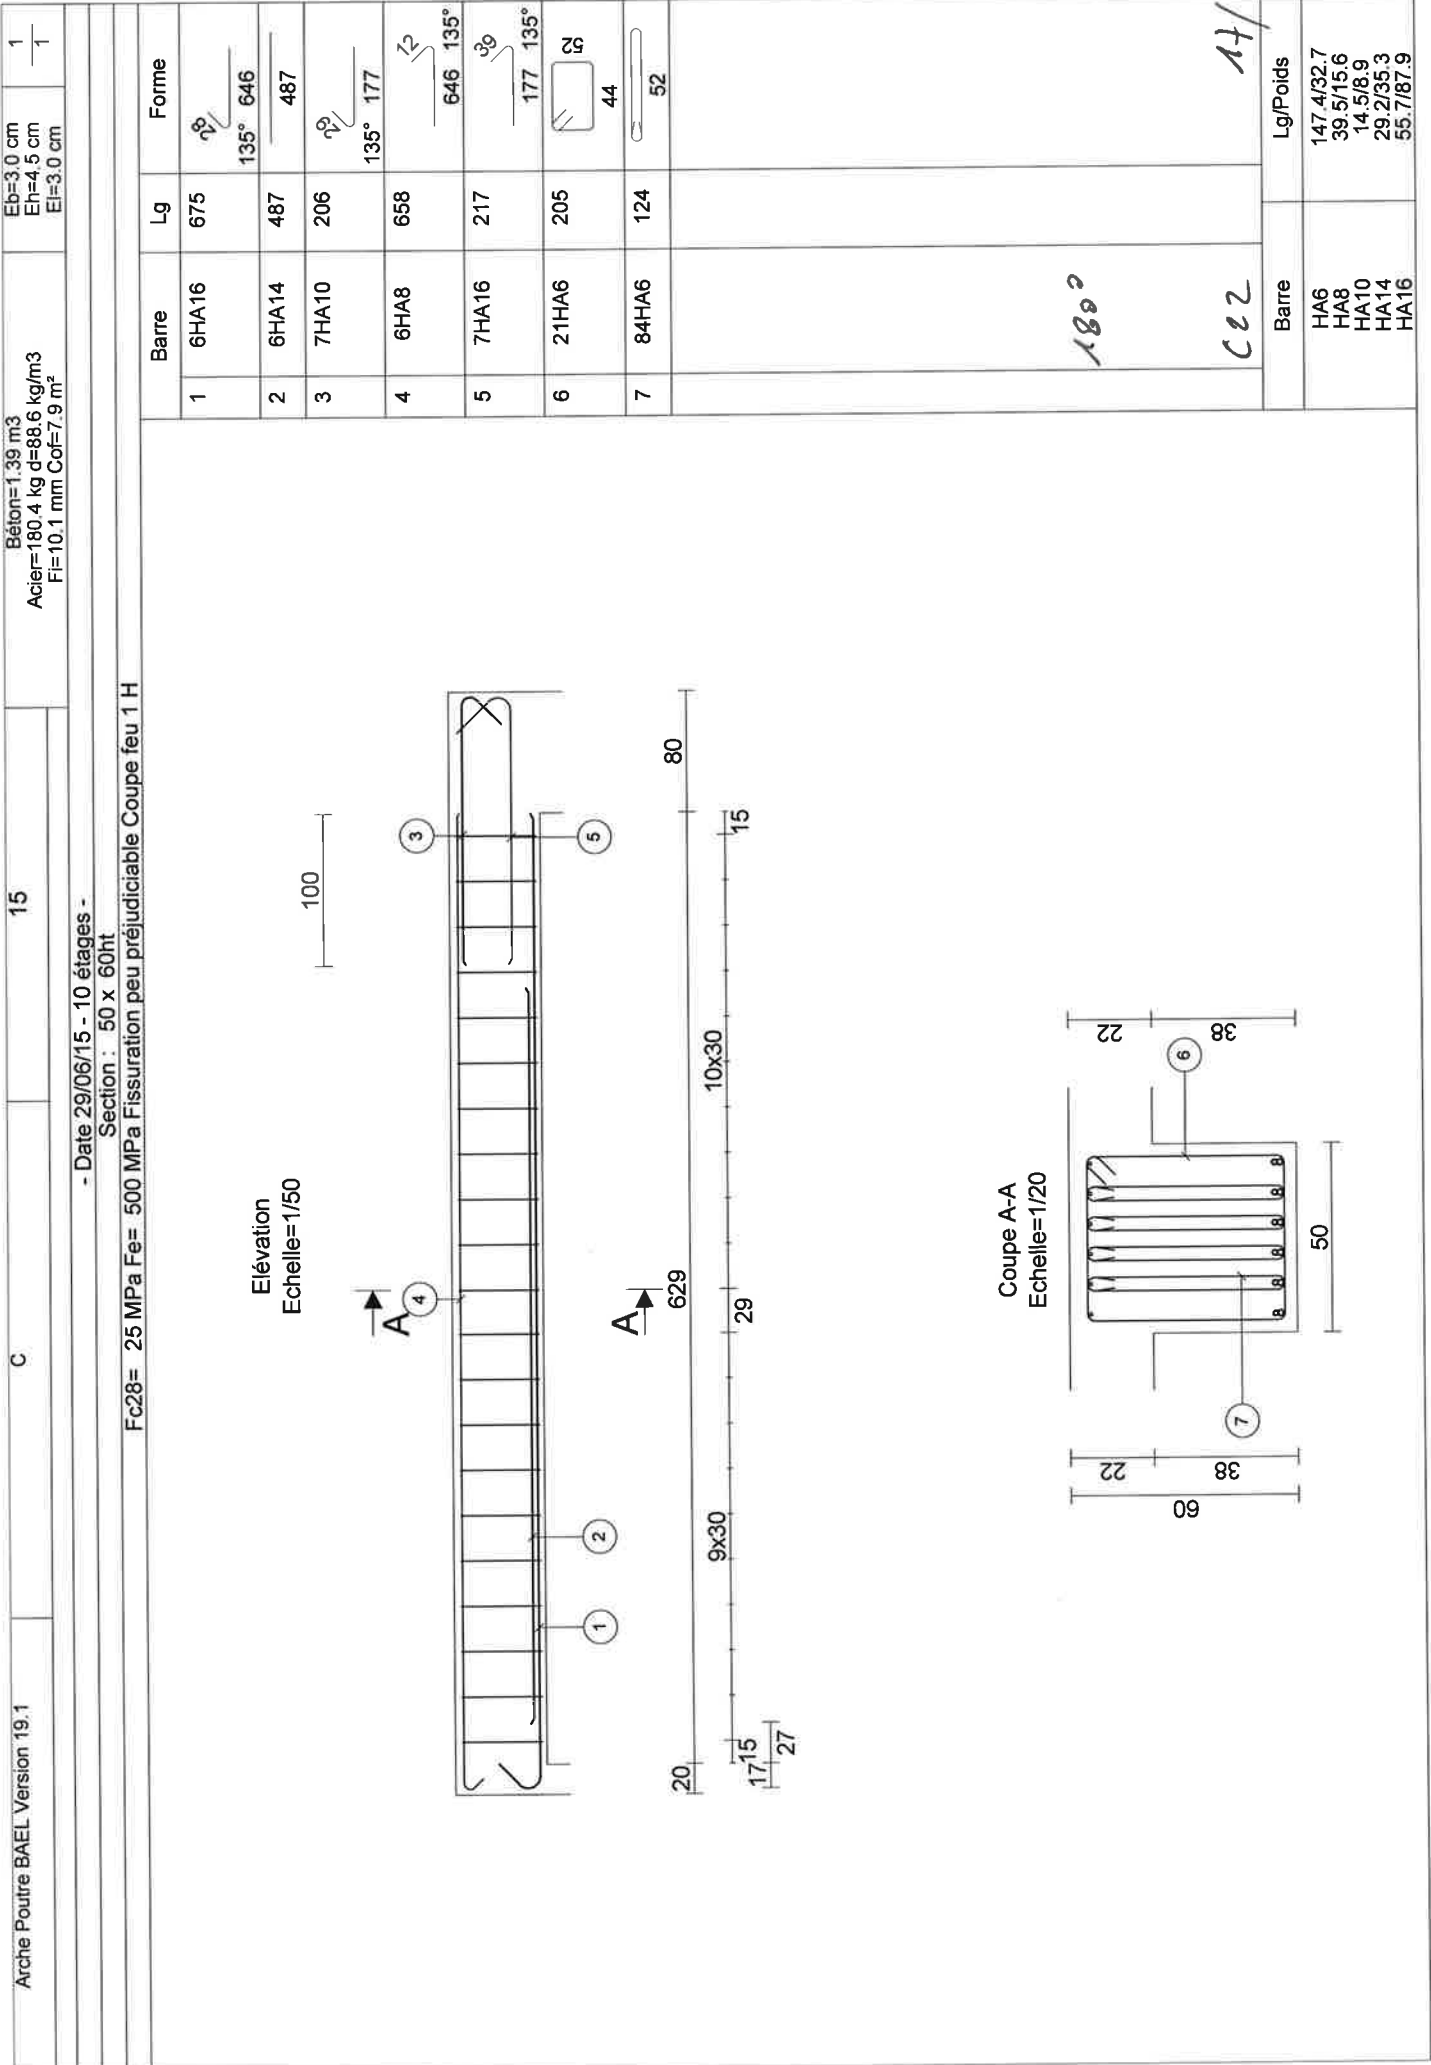

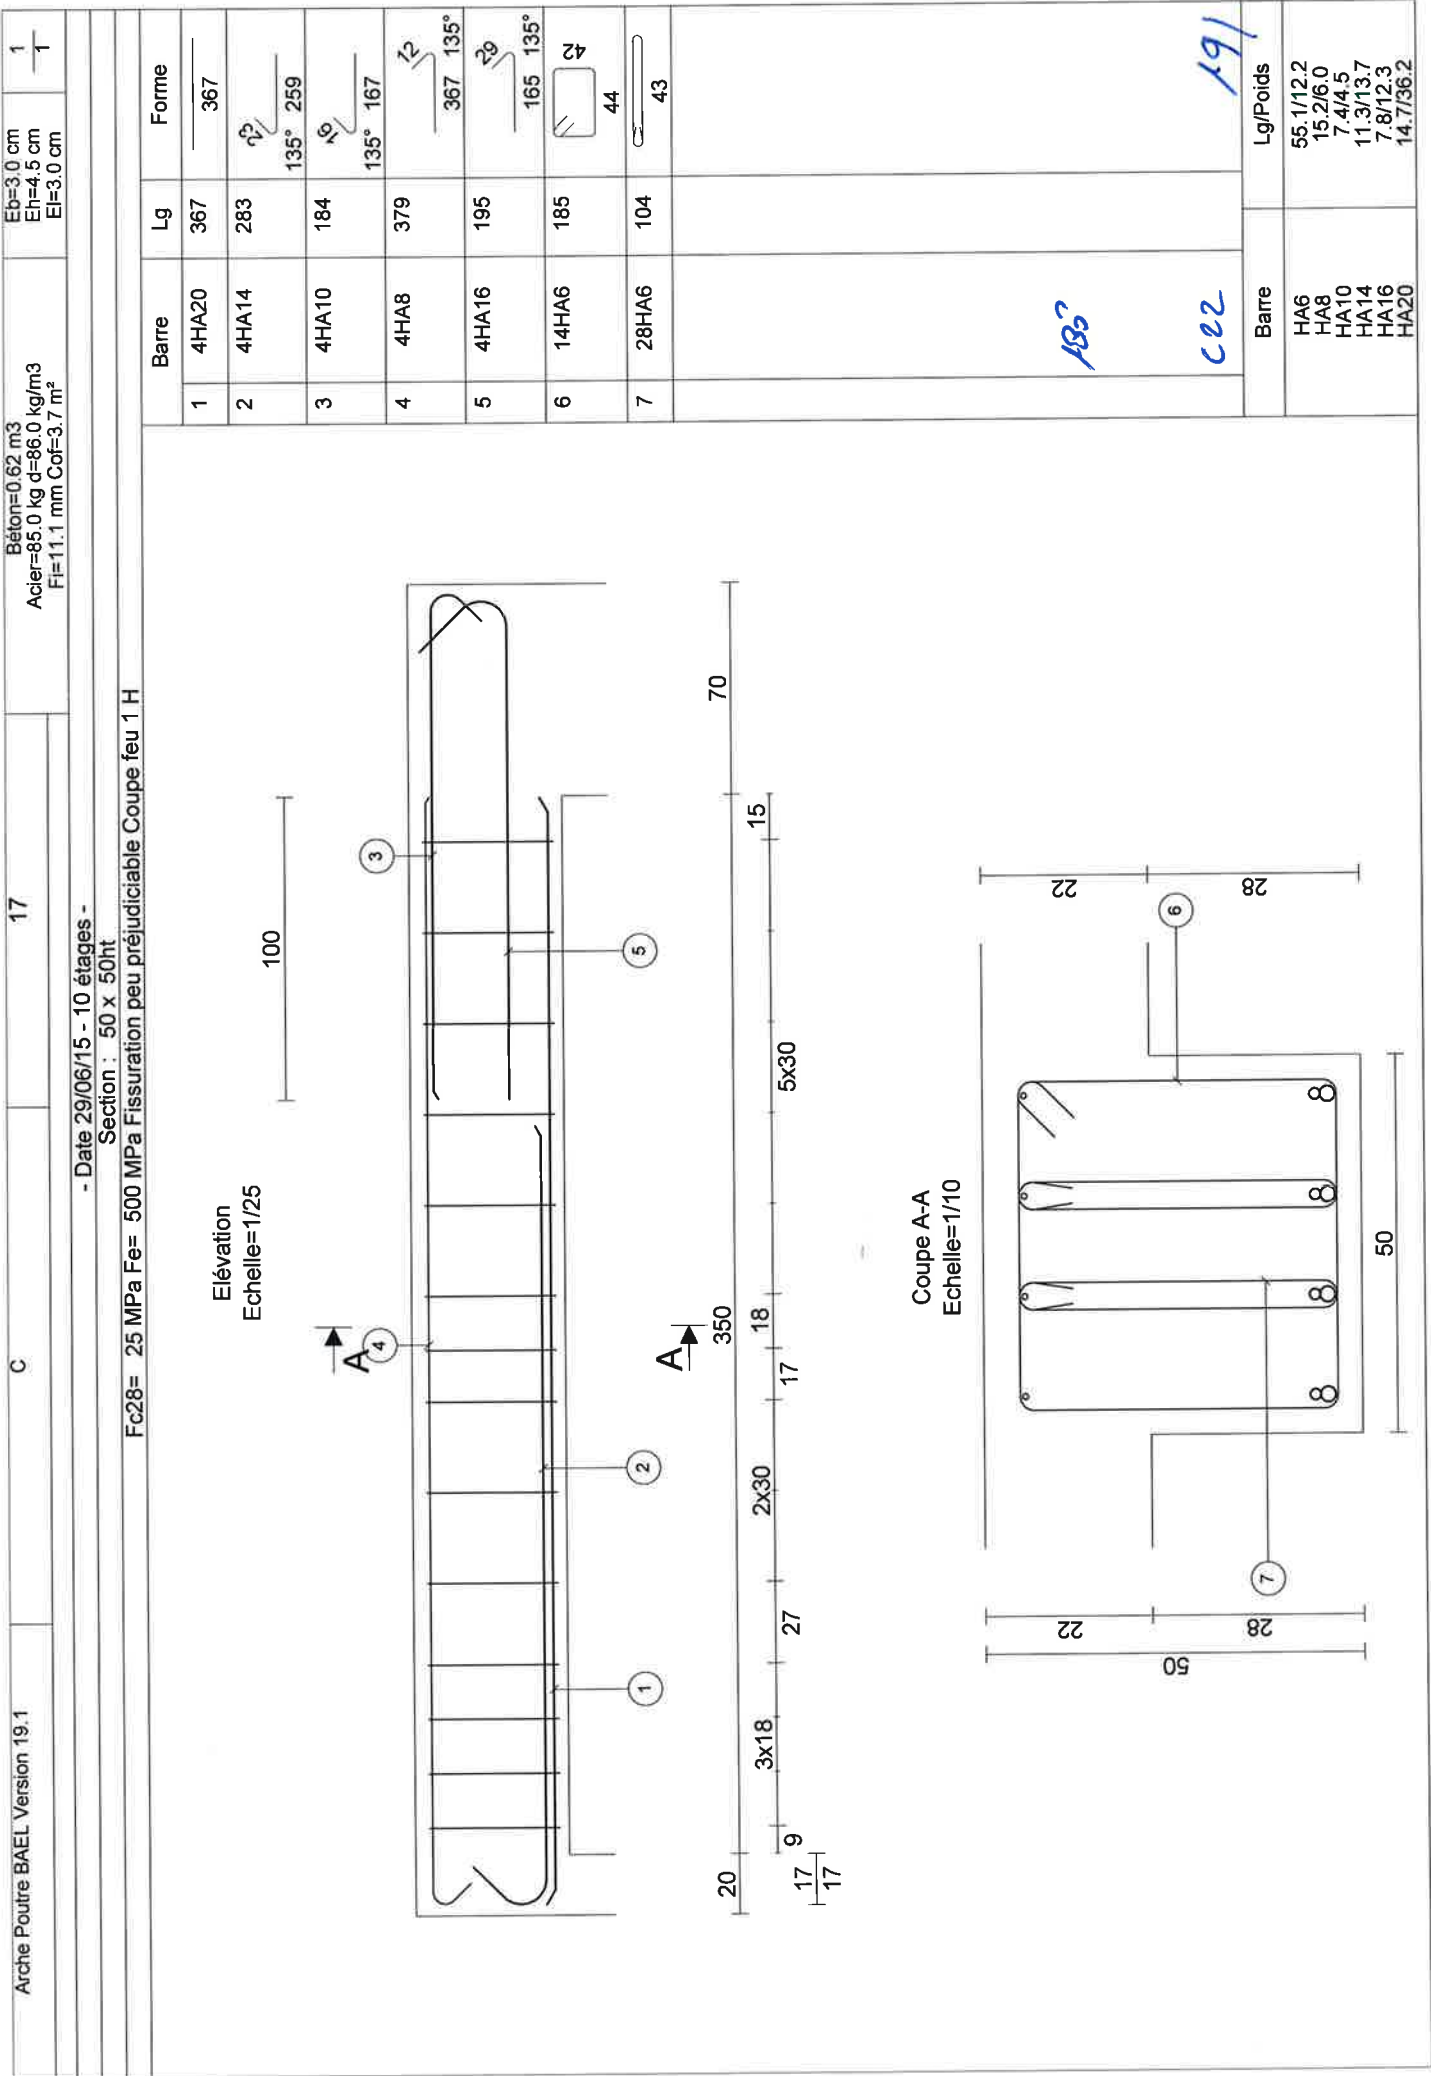


- Date 29/06/15 - 10 étages -

Section : 80 x 60ht


Fc28= 25 MPa Fe= 500 MPa Fissuration peu préjudiciable Coupe feu 1 H

Barre	Lg	Forme
1	646	646
2	509	509
3	190	135° 173
4	658	646 135°
5	200	175 135°
6	137	135° 97
7	265	74
8	124	52

Elévation
Echelle=1/50

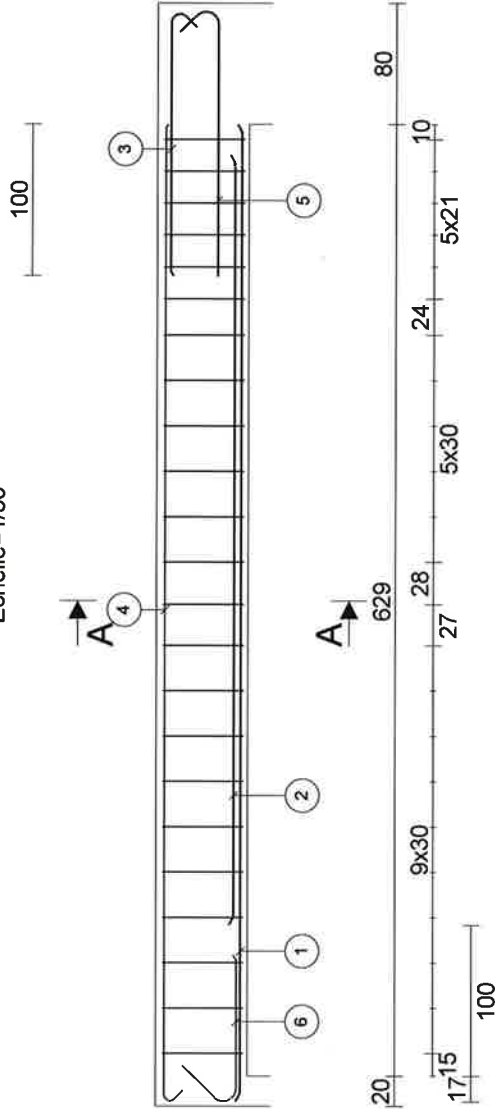


Coupe A-A
Echelle=1/20

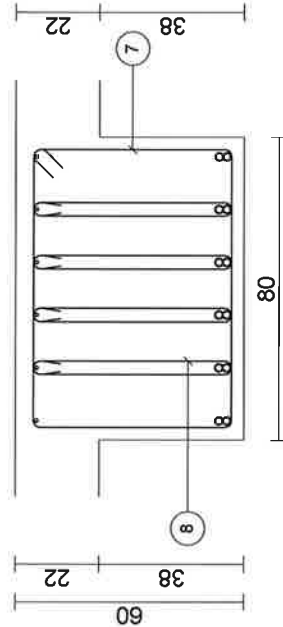


- Date 29/06/15 - 10 étages -

Section: 80 x 37ht

FC28= 25 MPa Fe= 500 MPa Fissuration peu préjudiciable Coupe feu 1 H


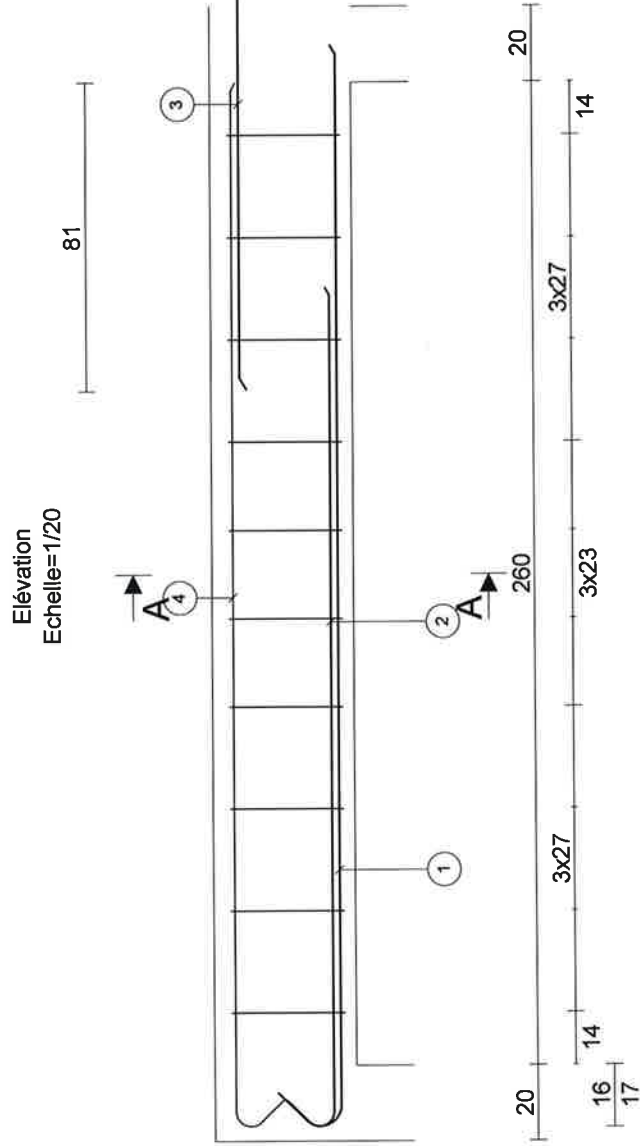


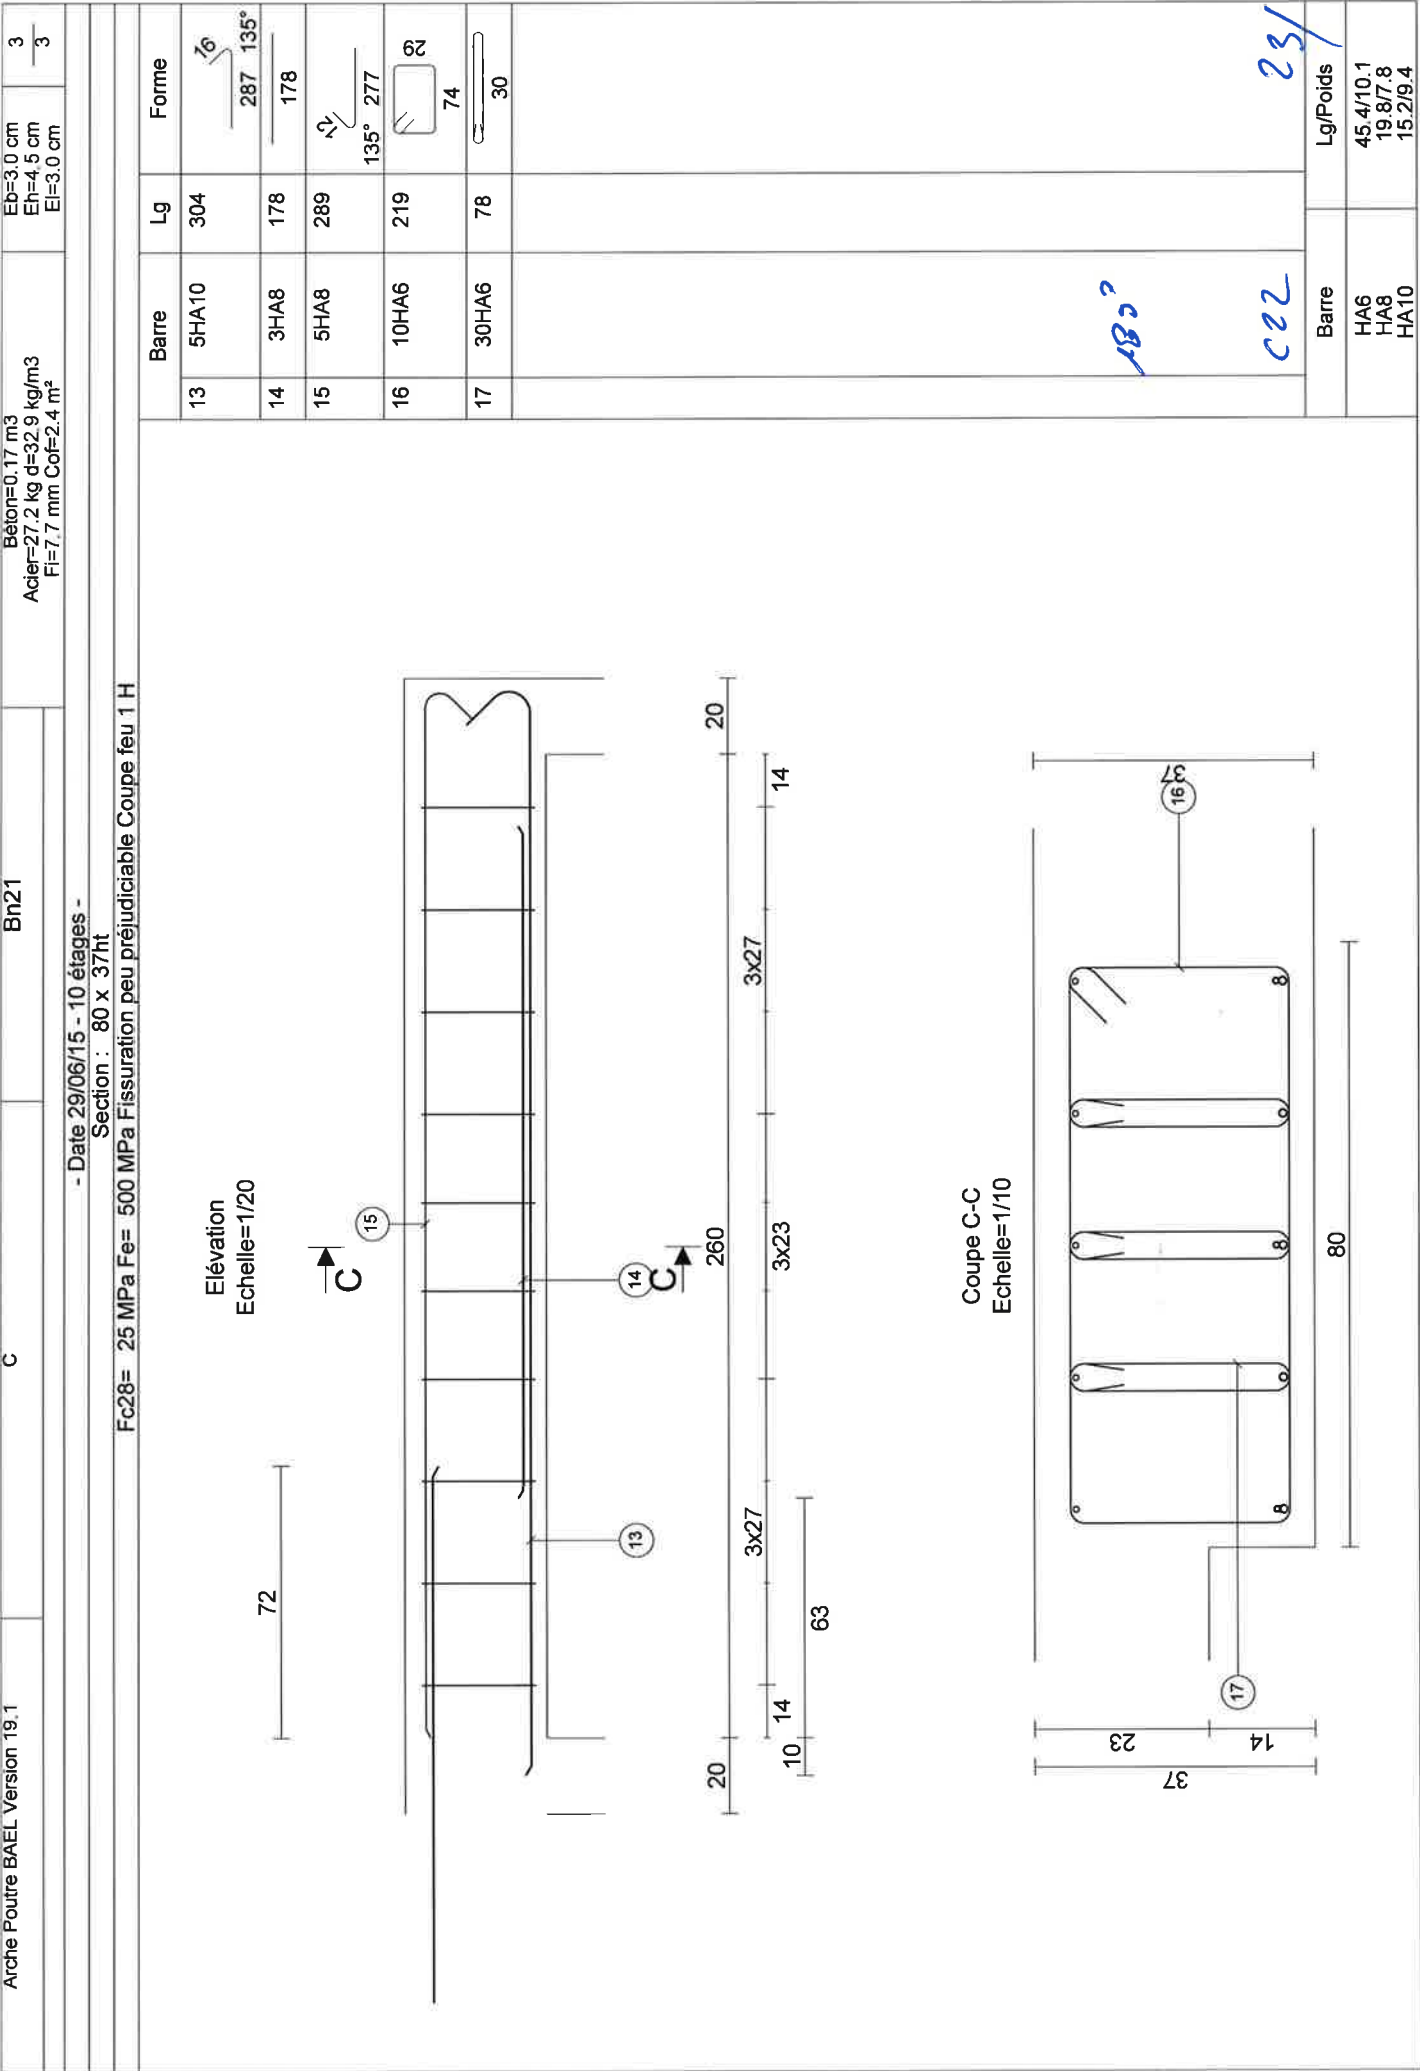



- Date 29/06/15 - 10 étages -


Section: 40 x 40ht


Fc28= 25 MPa Fe= 500 MPa Fissuration peu préjudiciable Coupe feu 1 H

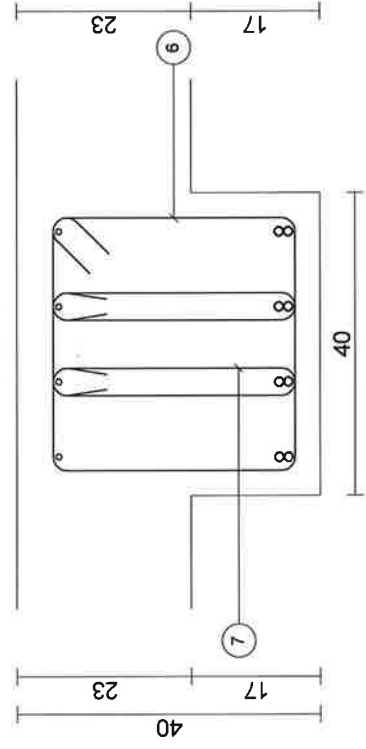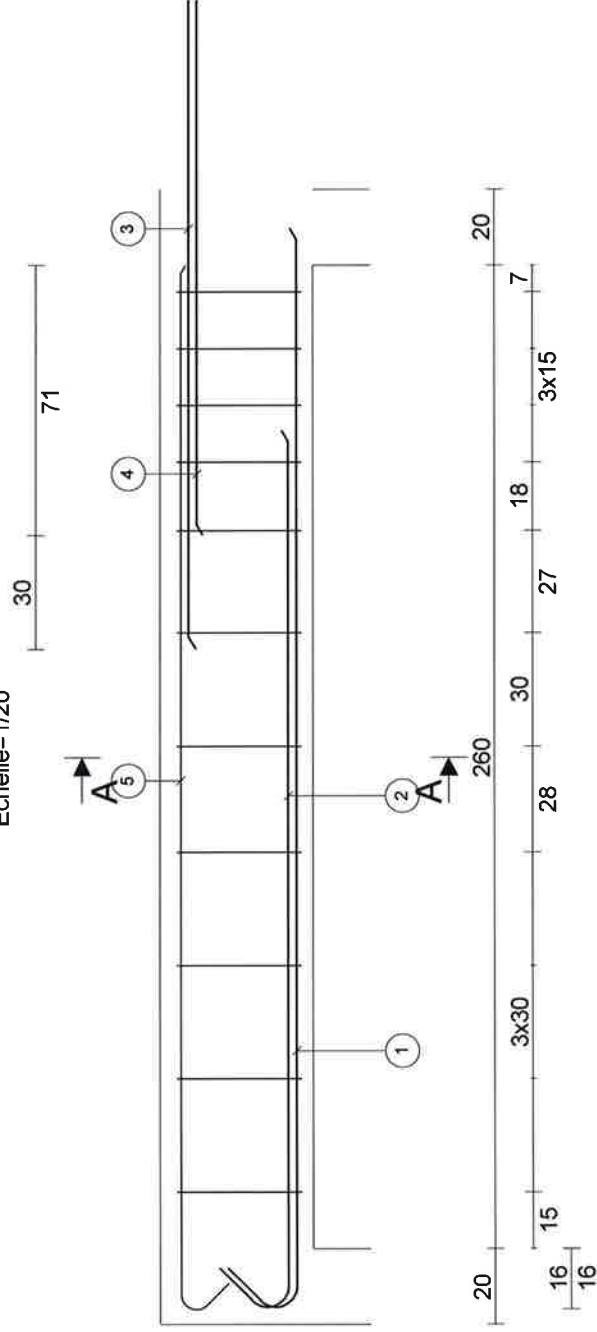
[illegible]

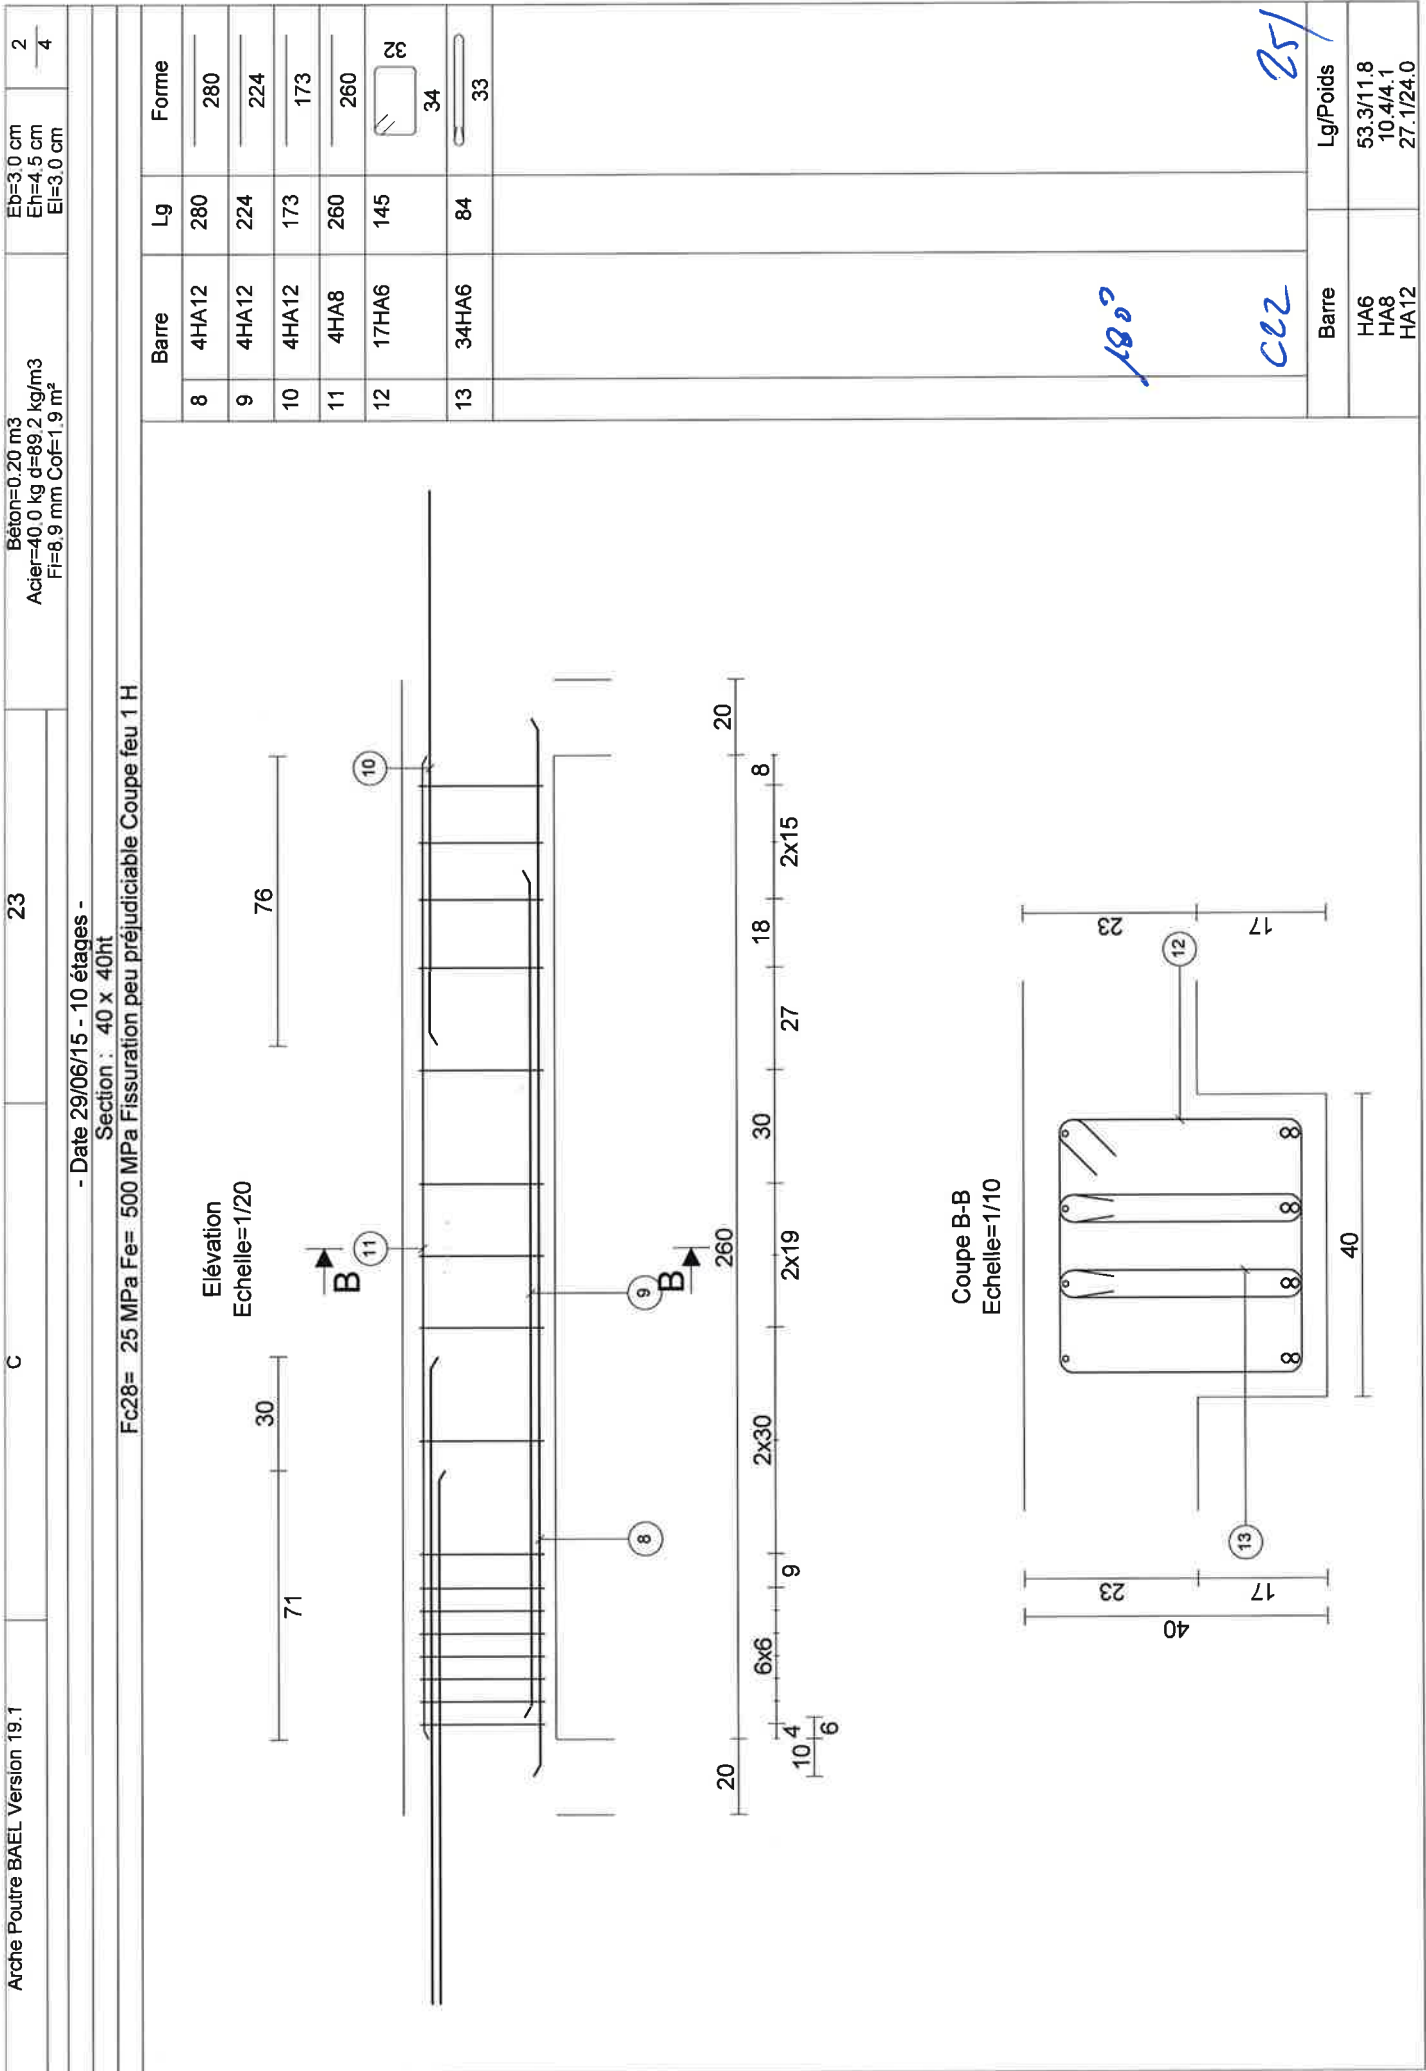


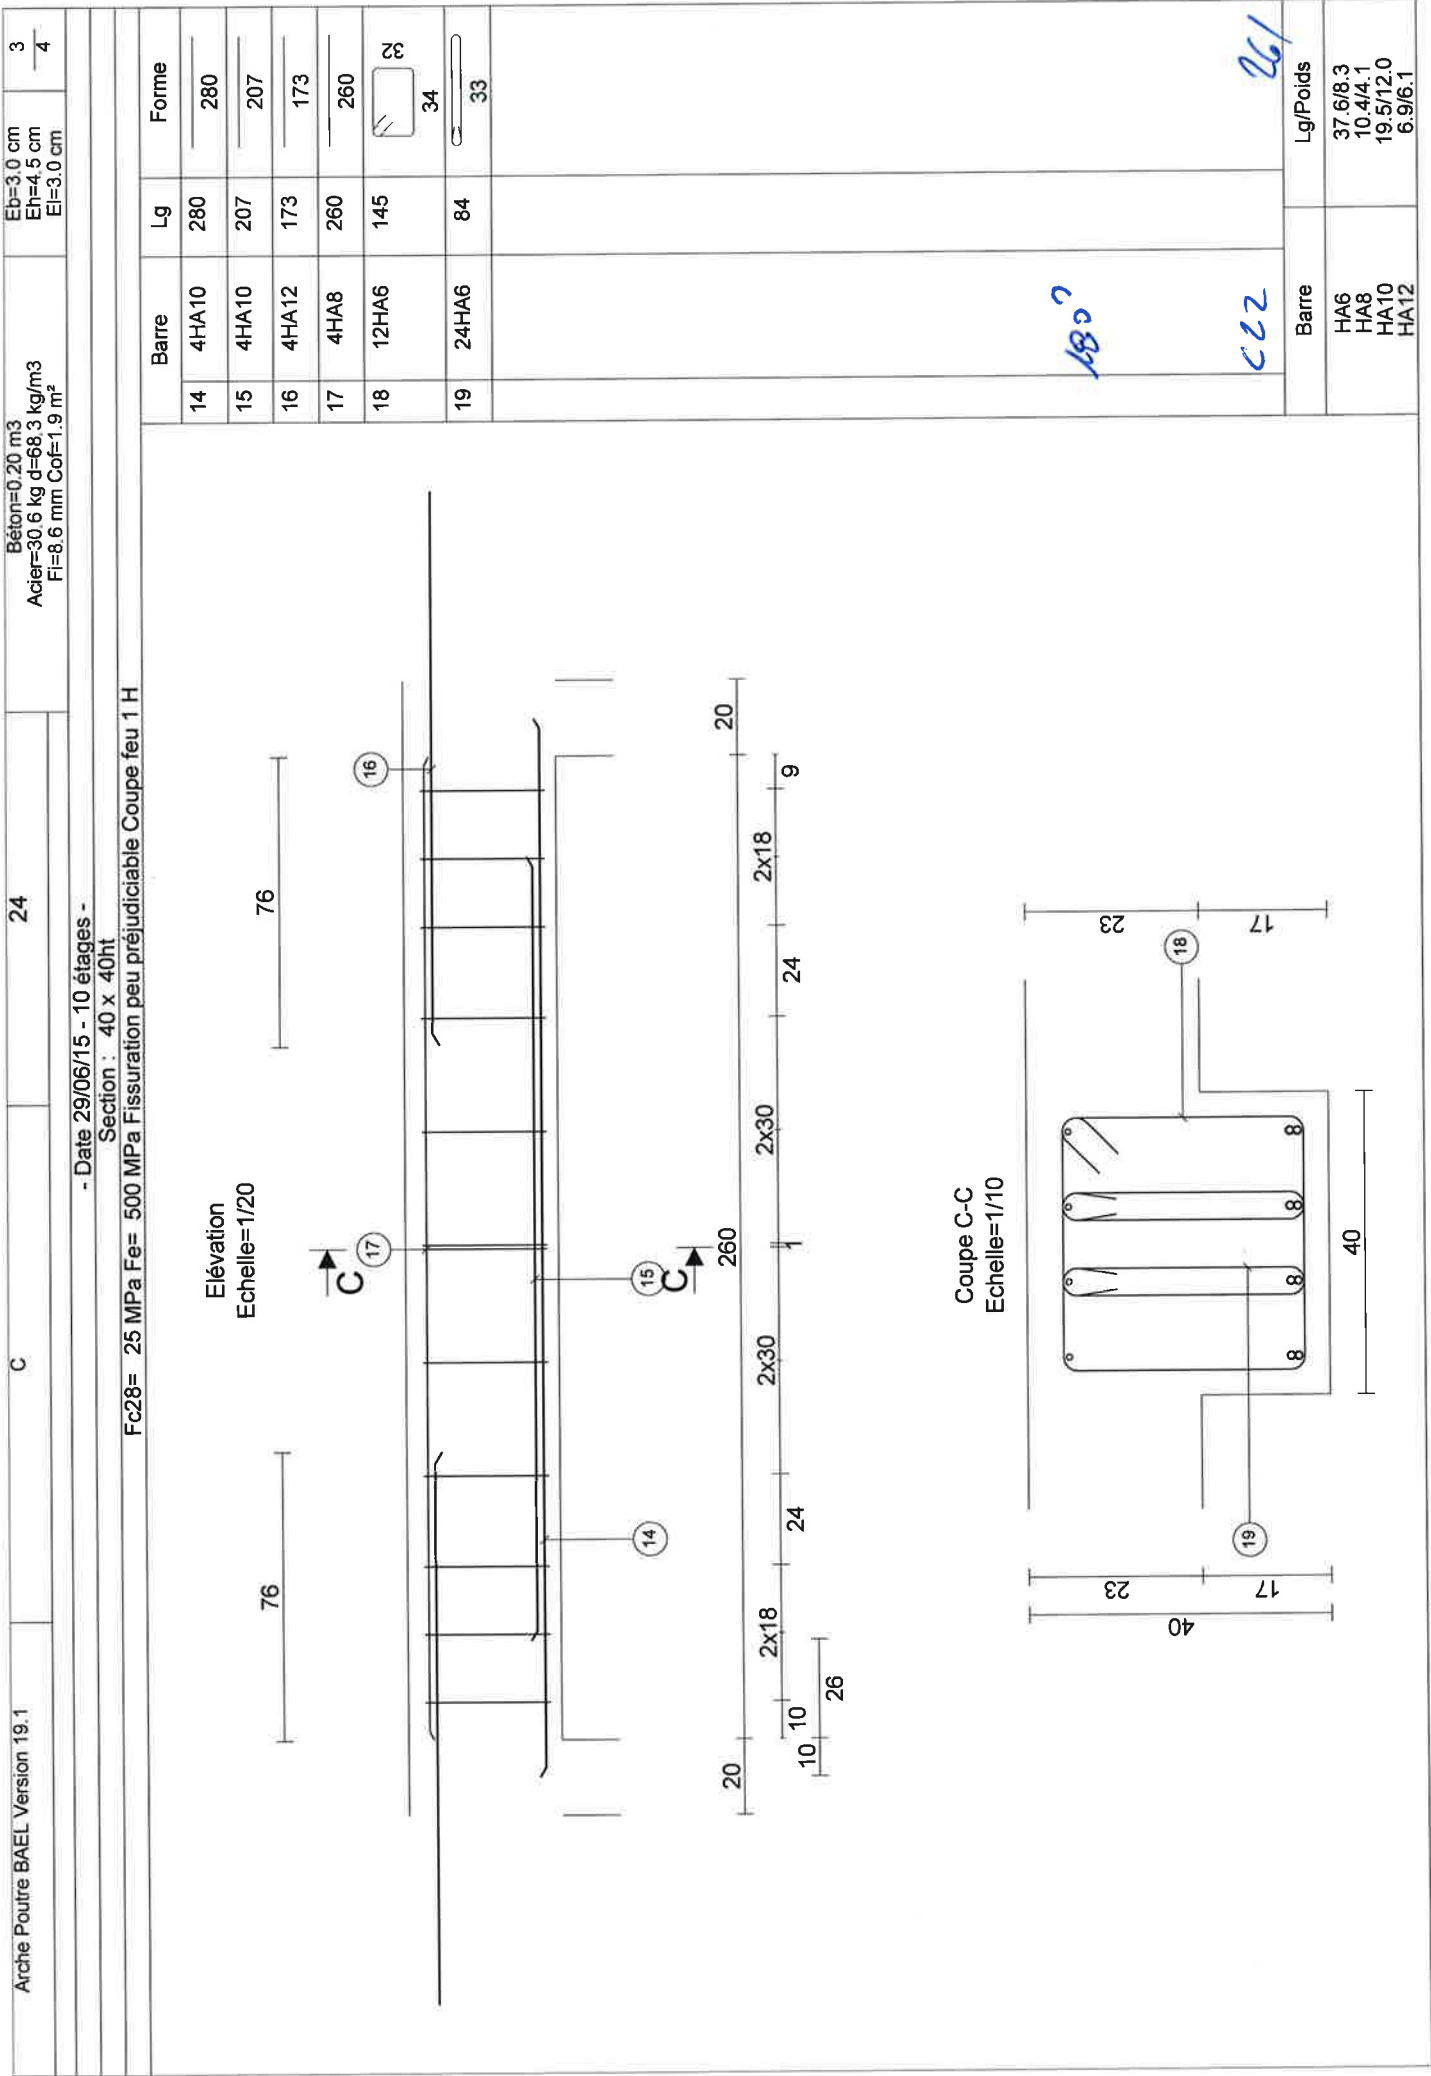


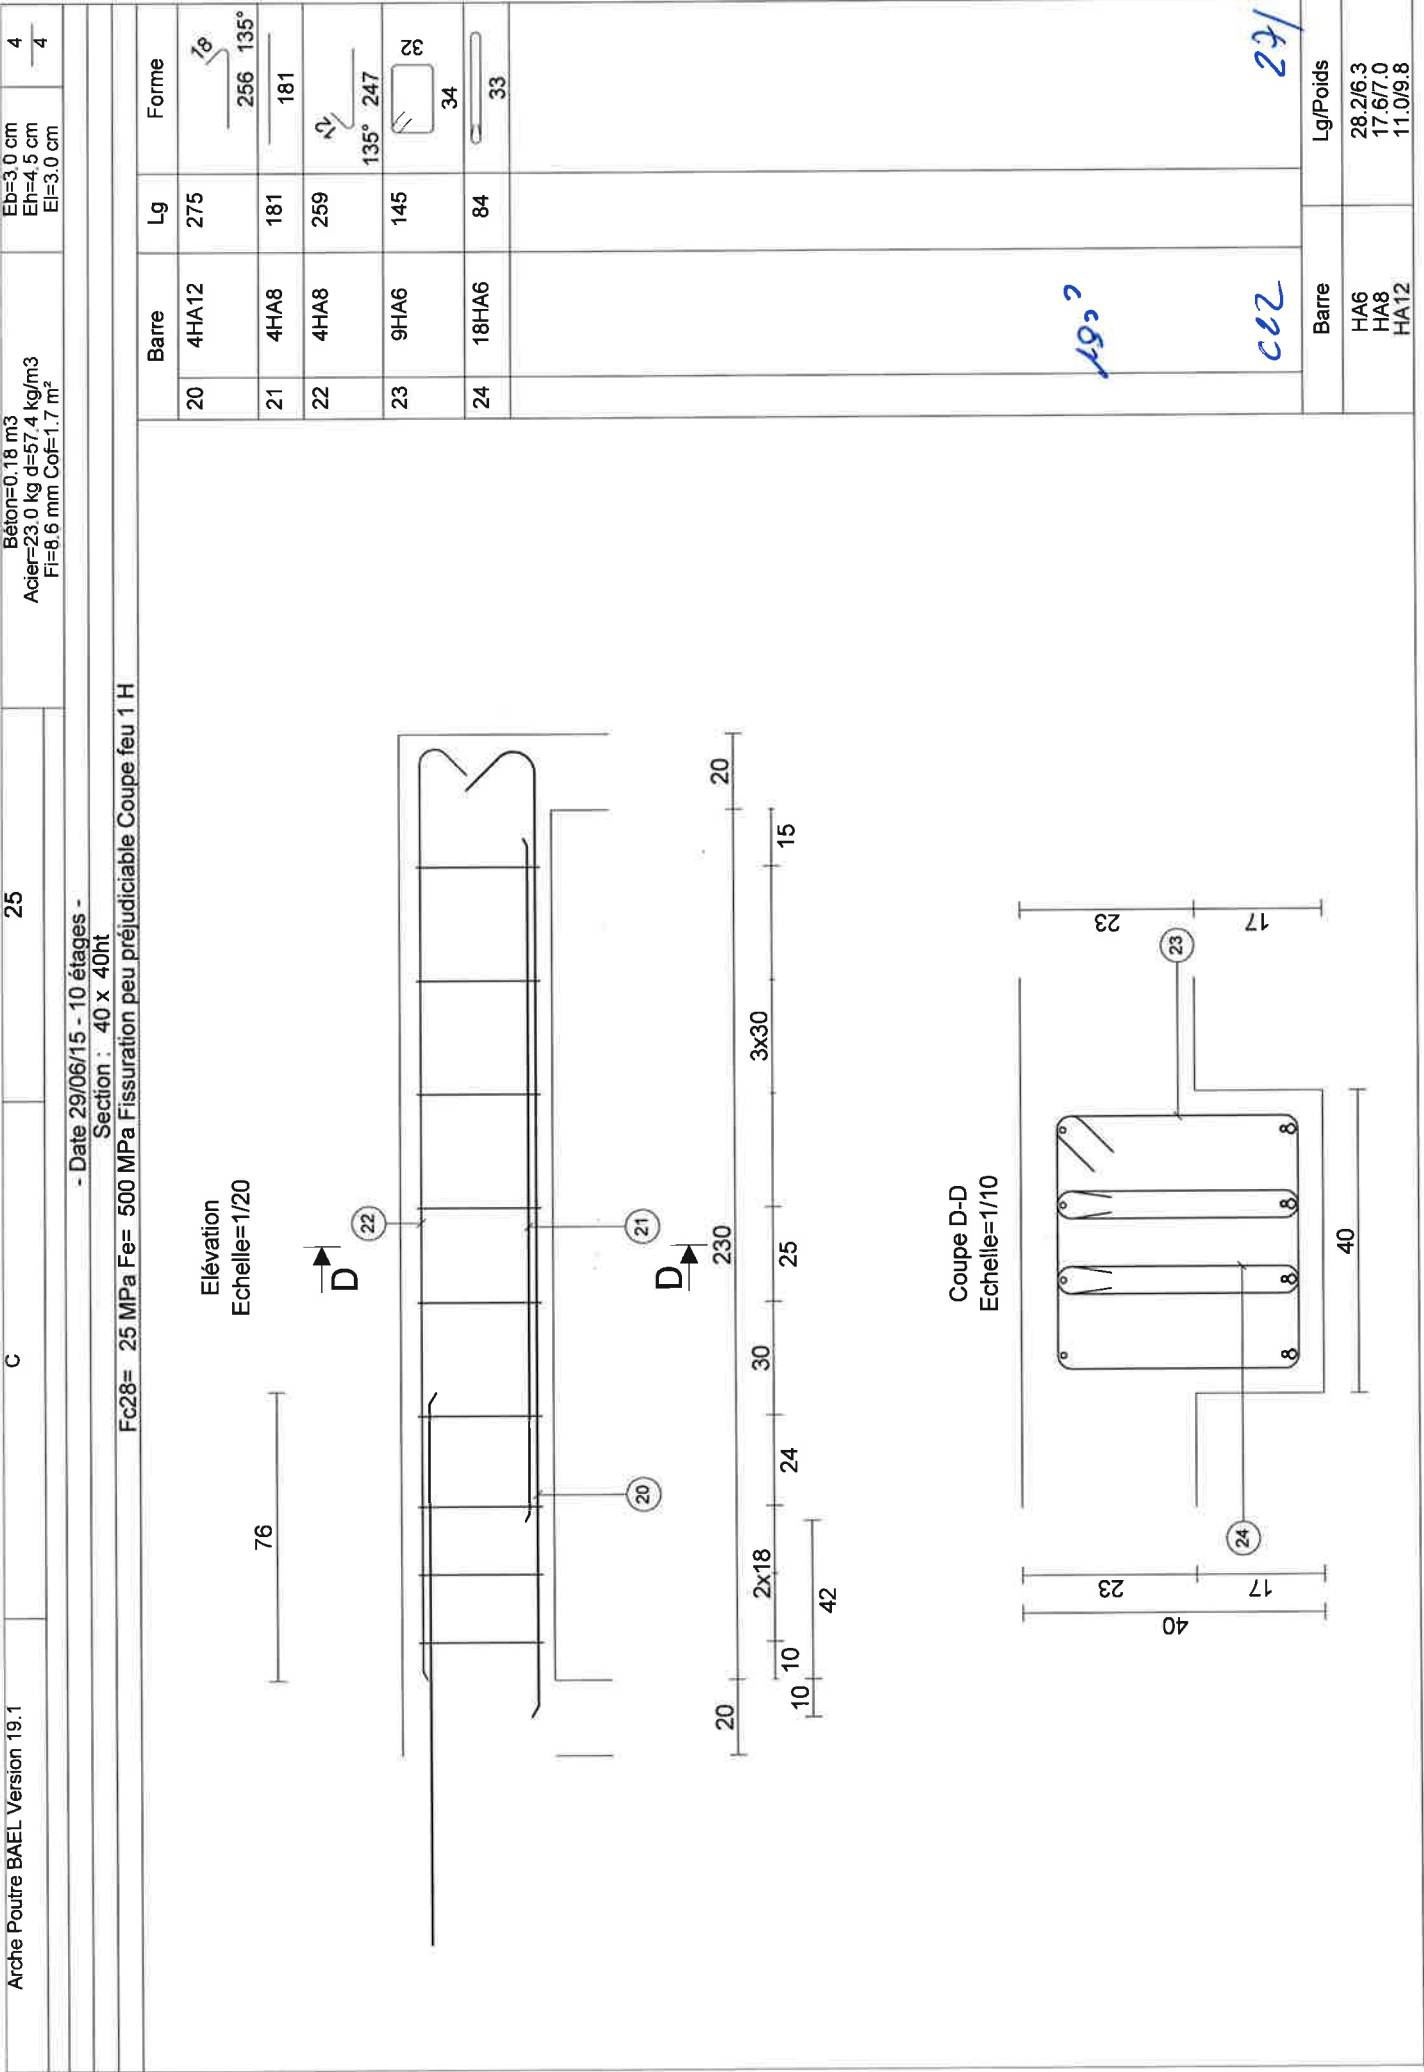

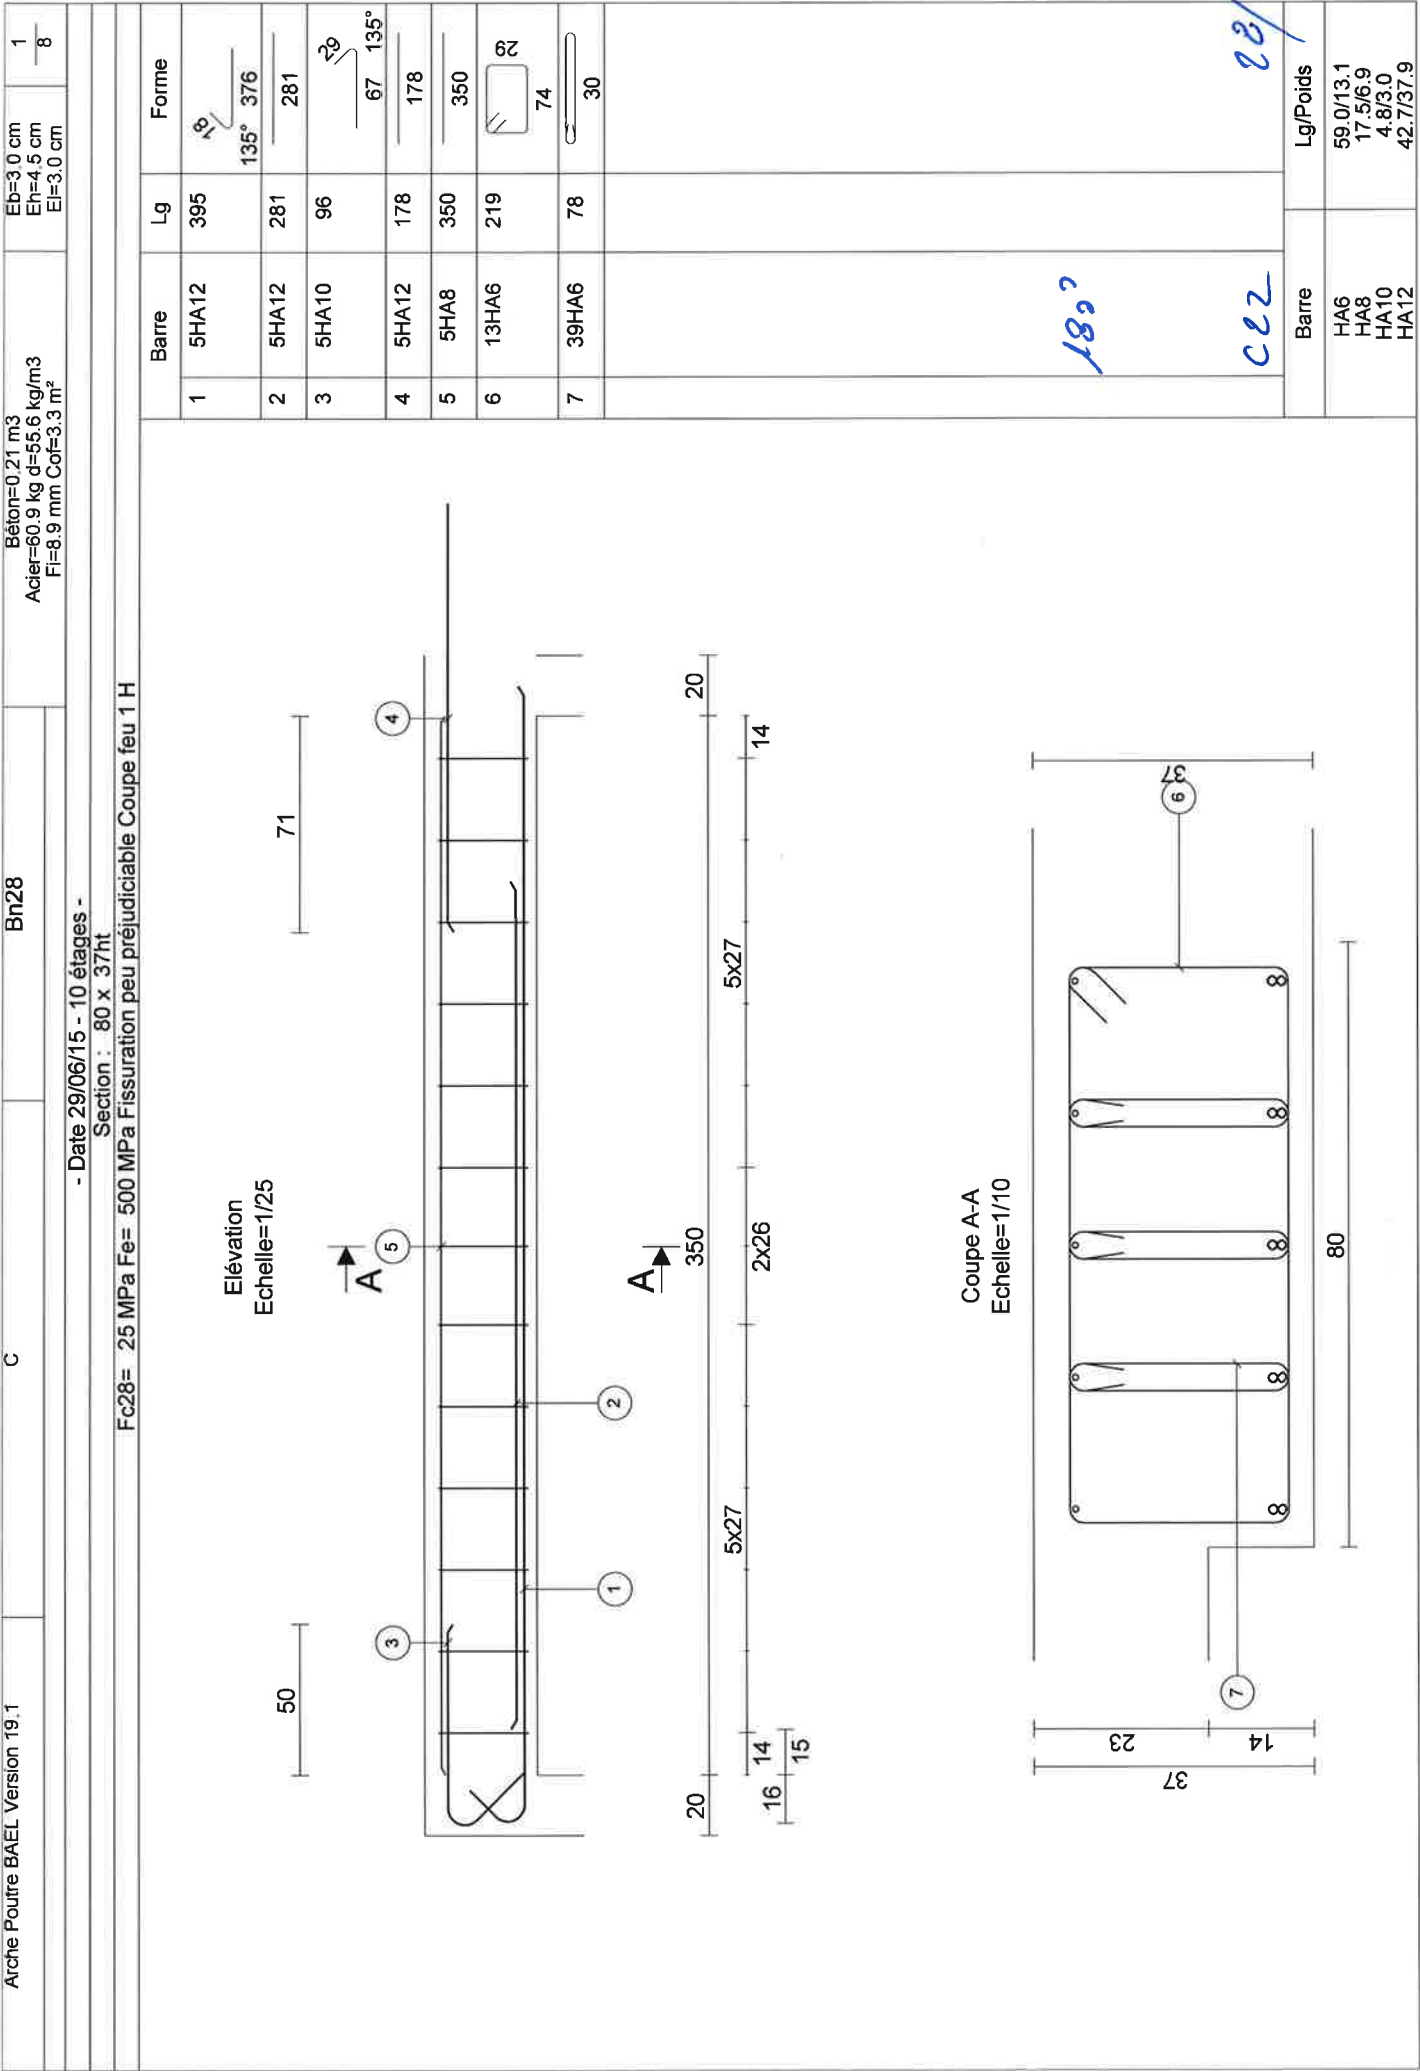

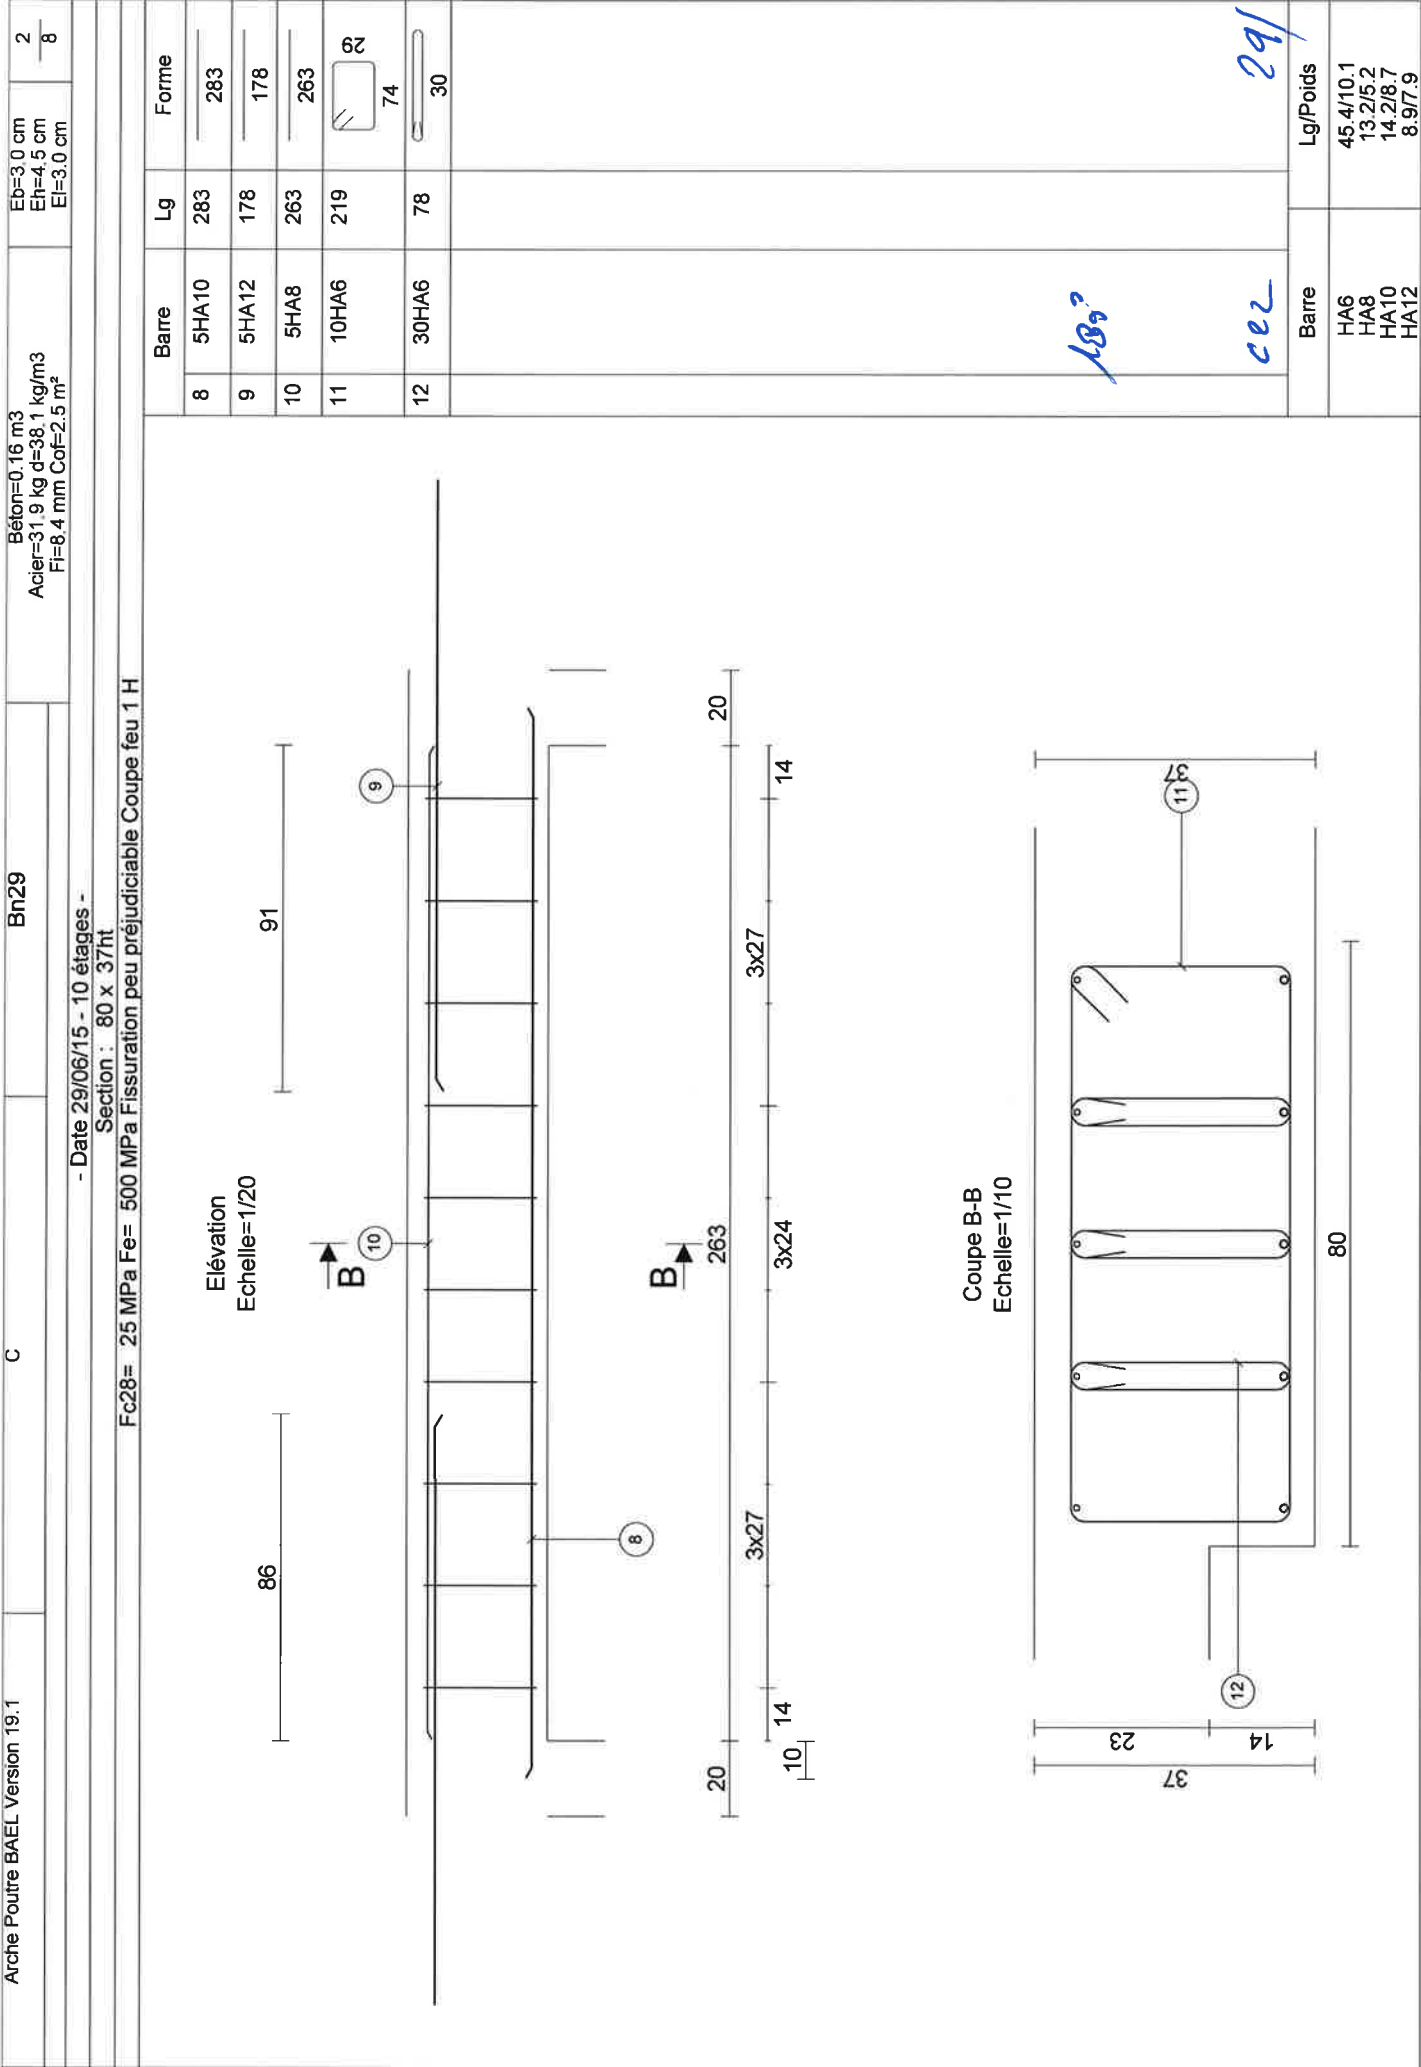


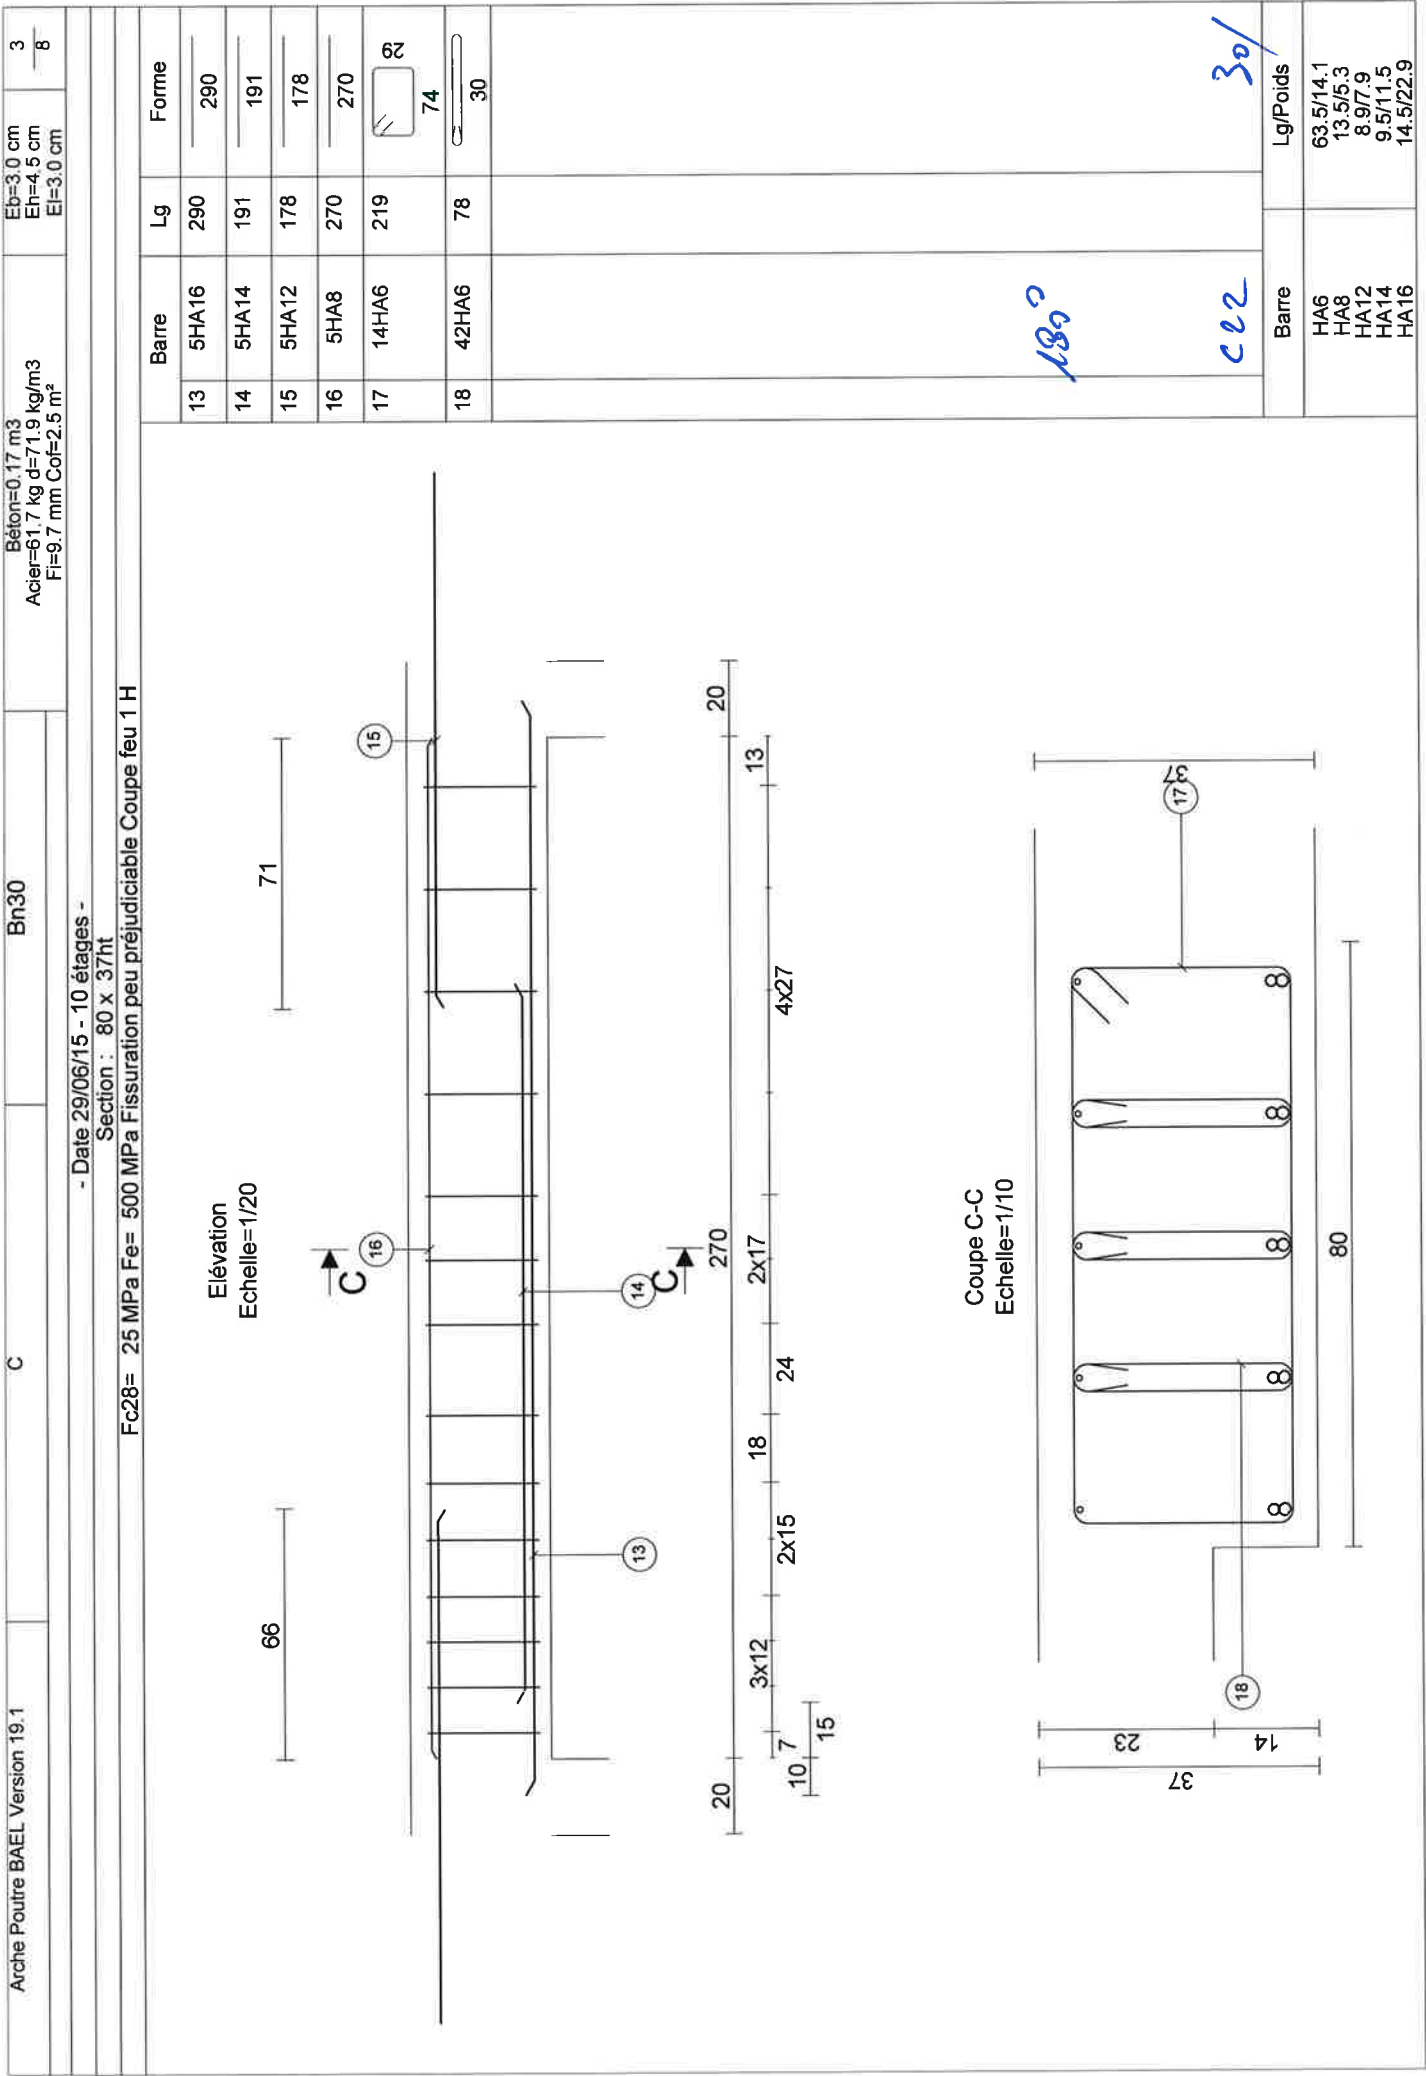


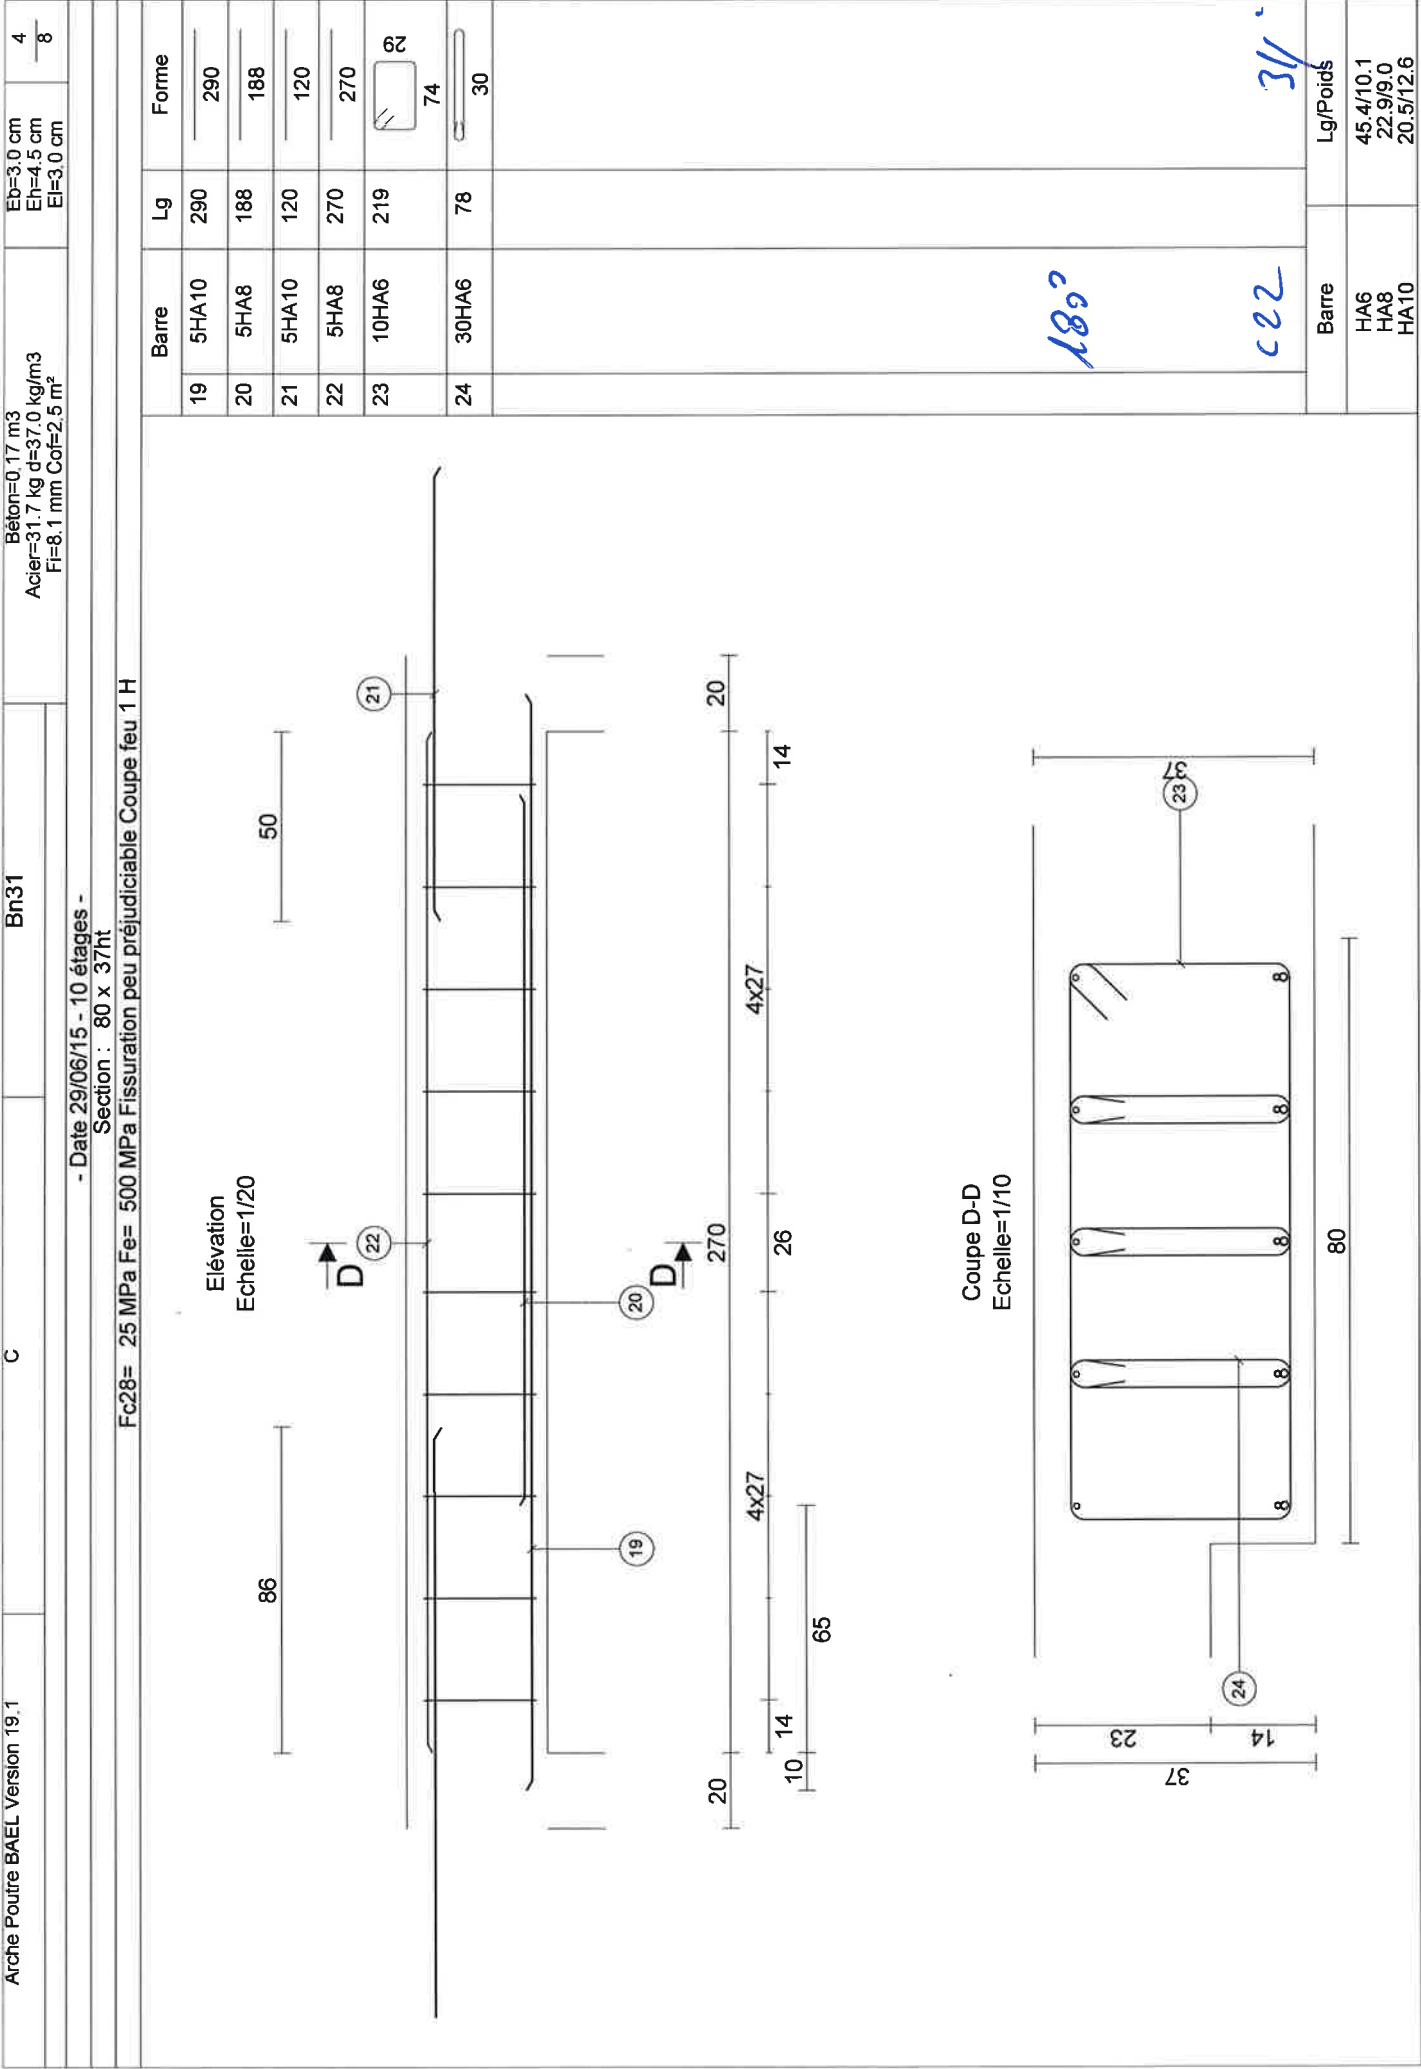



- Date 29/06/15 - 10 étages -


Section : 80 x 37ht


Section : 50 x 5 mm
Fc28= 25 MPa Fe= 500 MPa Fissuration peu préjudiciable Coupe feu 1 H

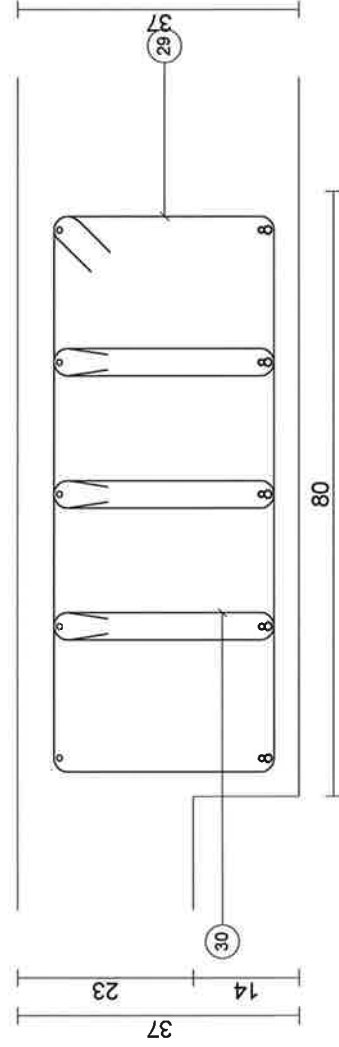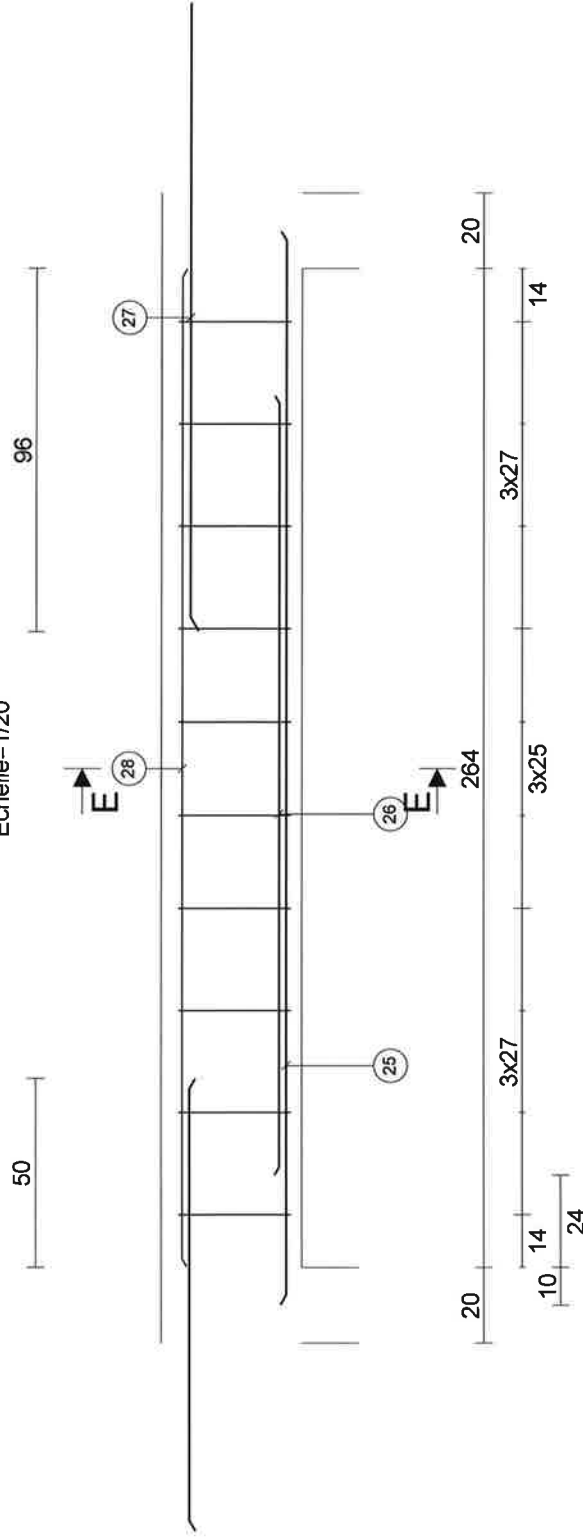
[illegible]

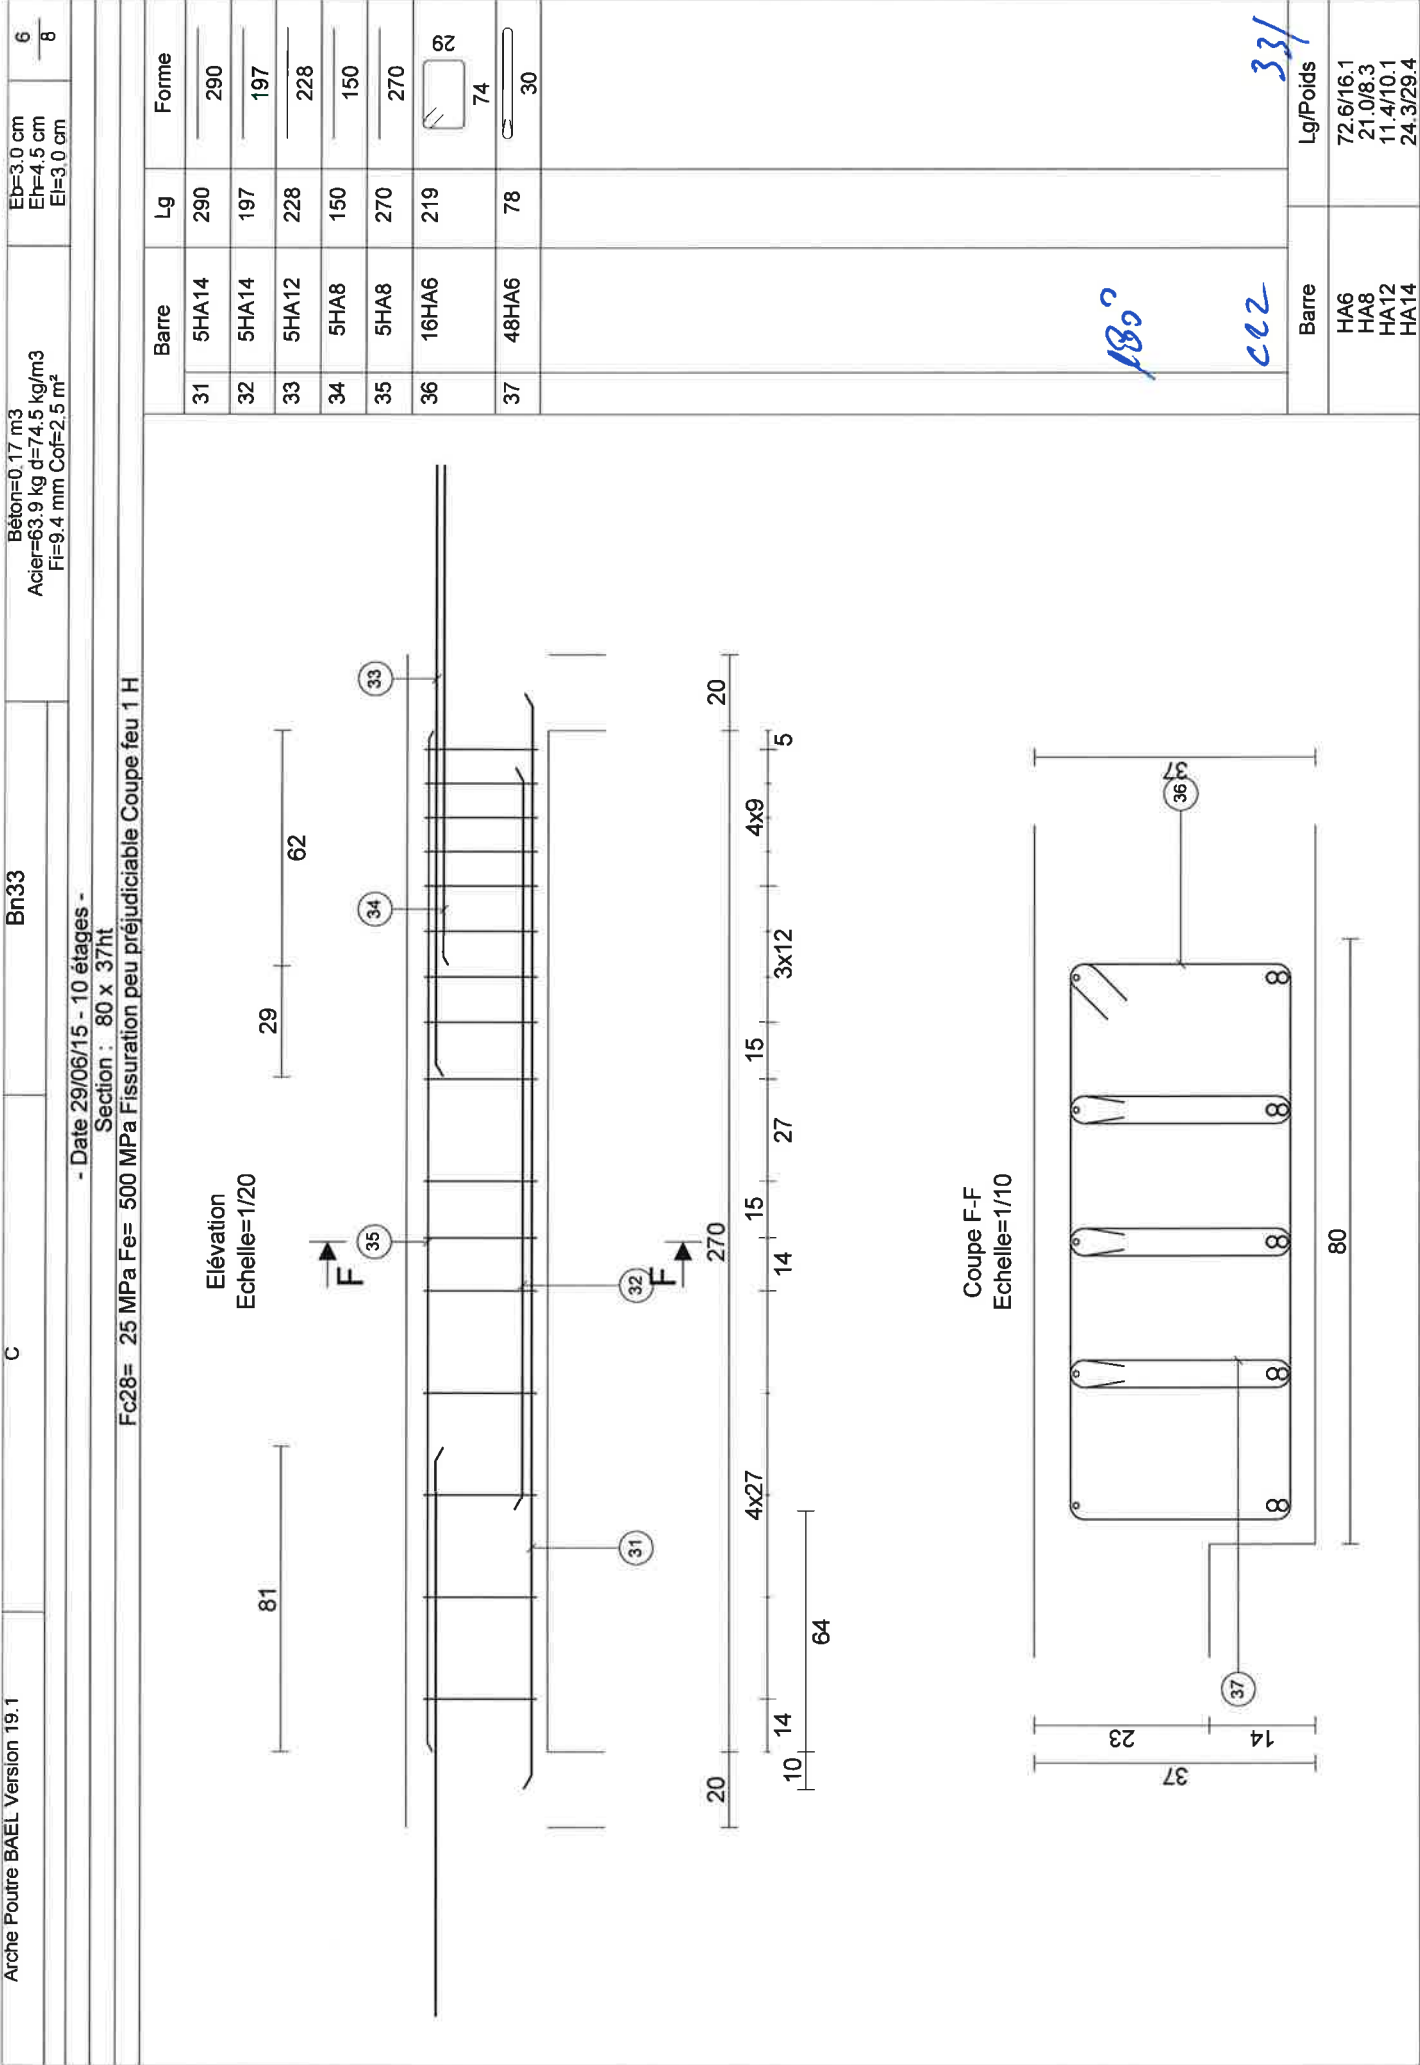


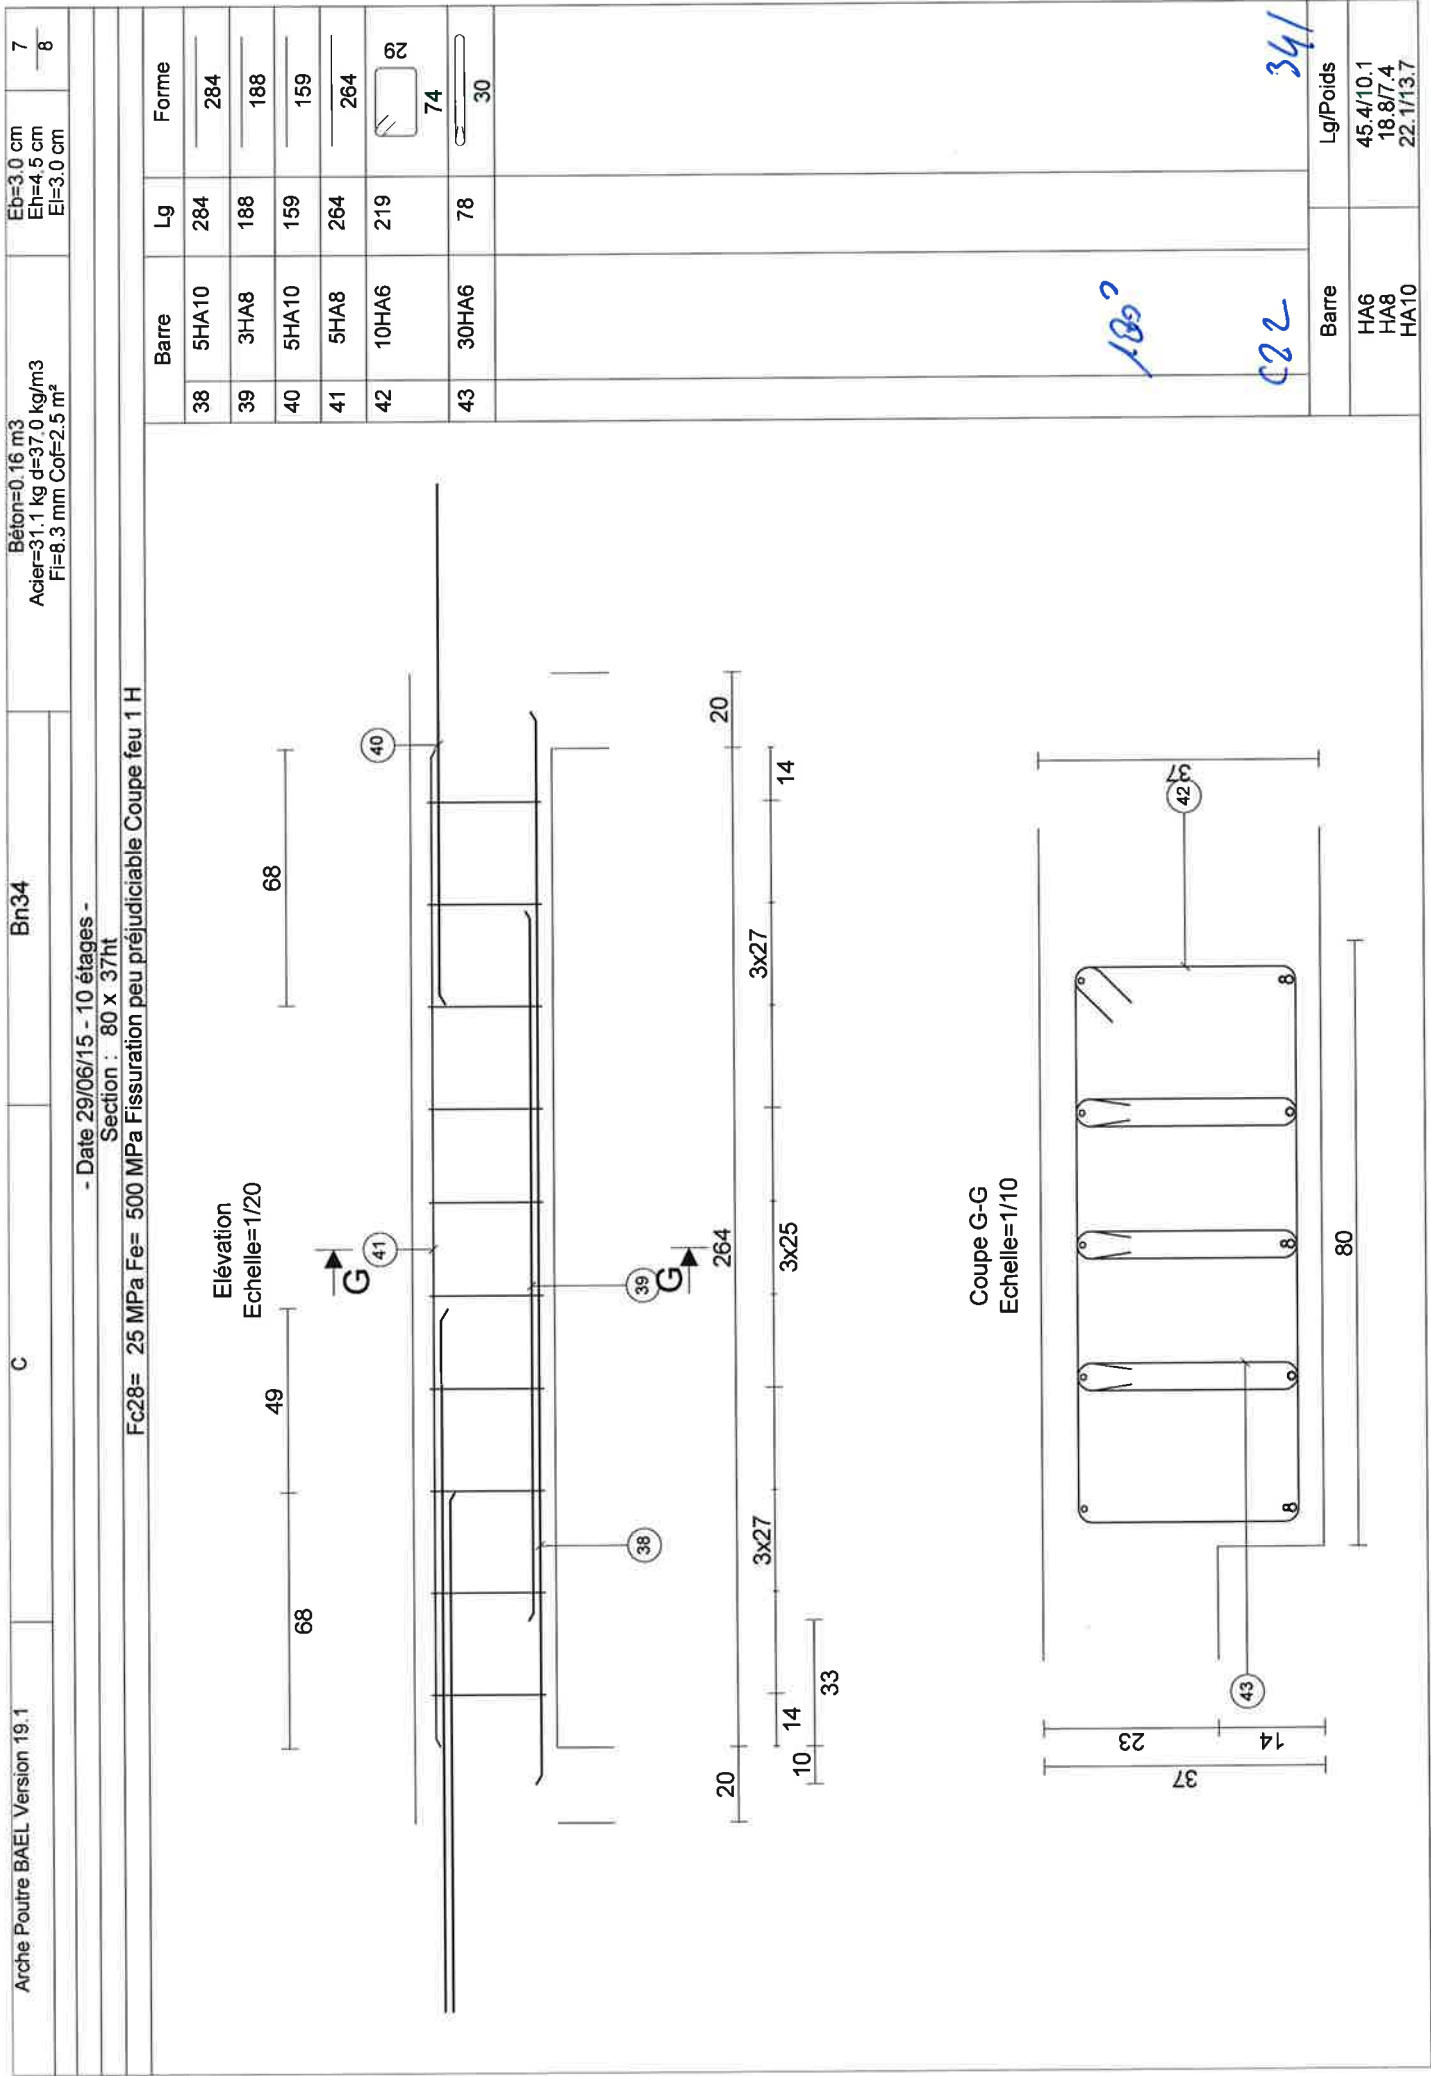


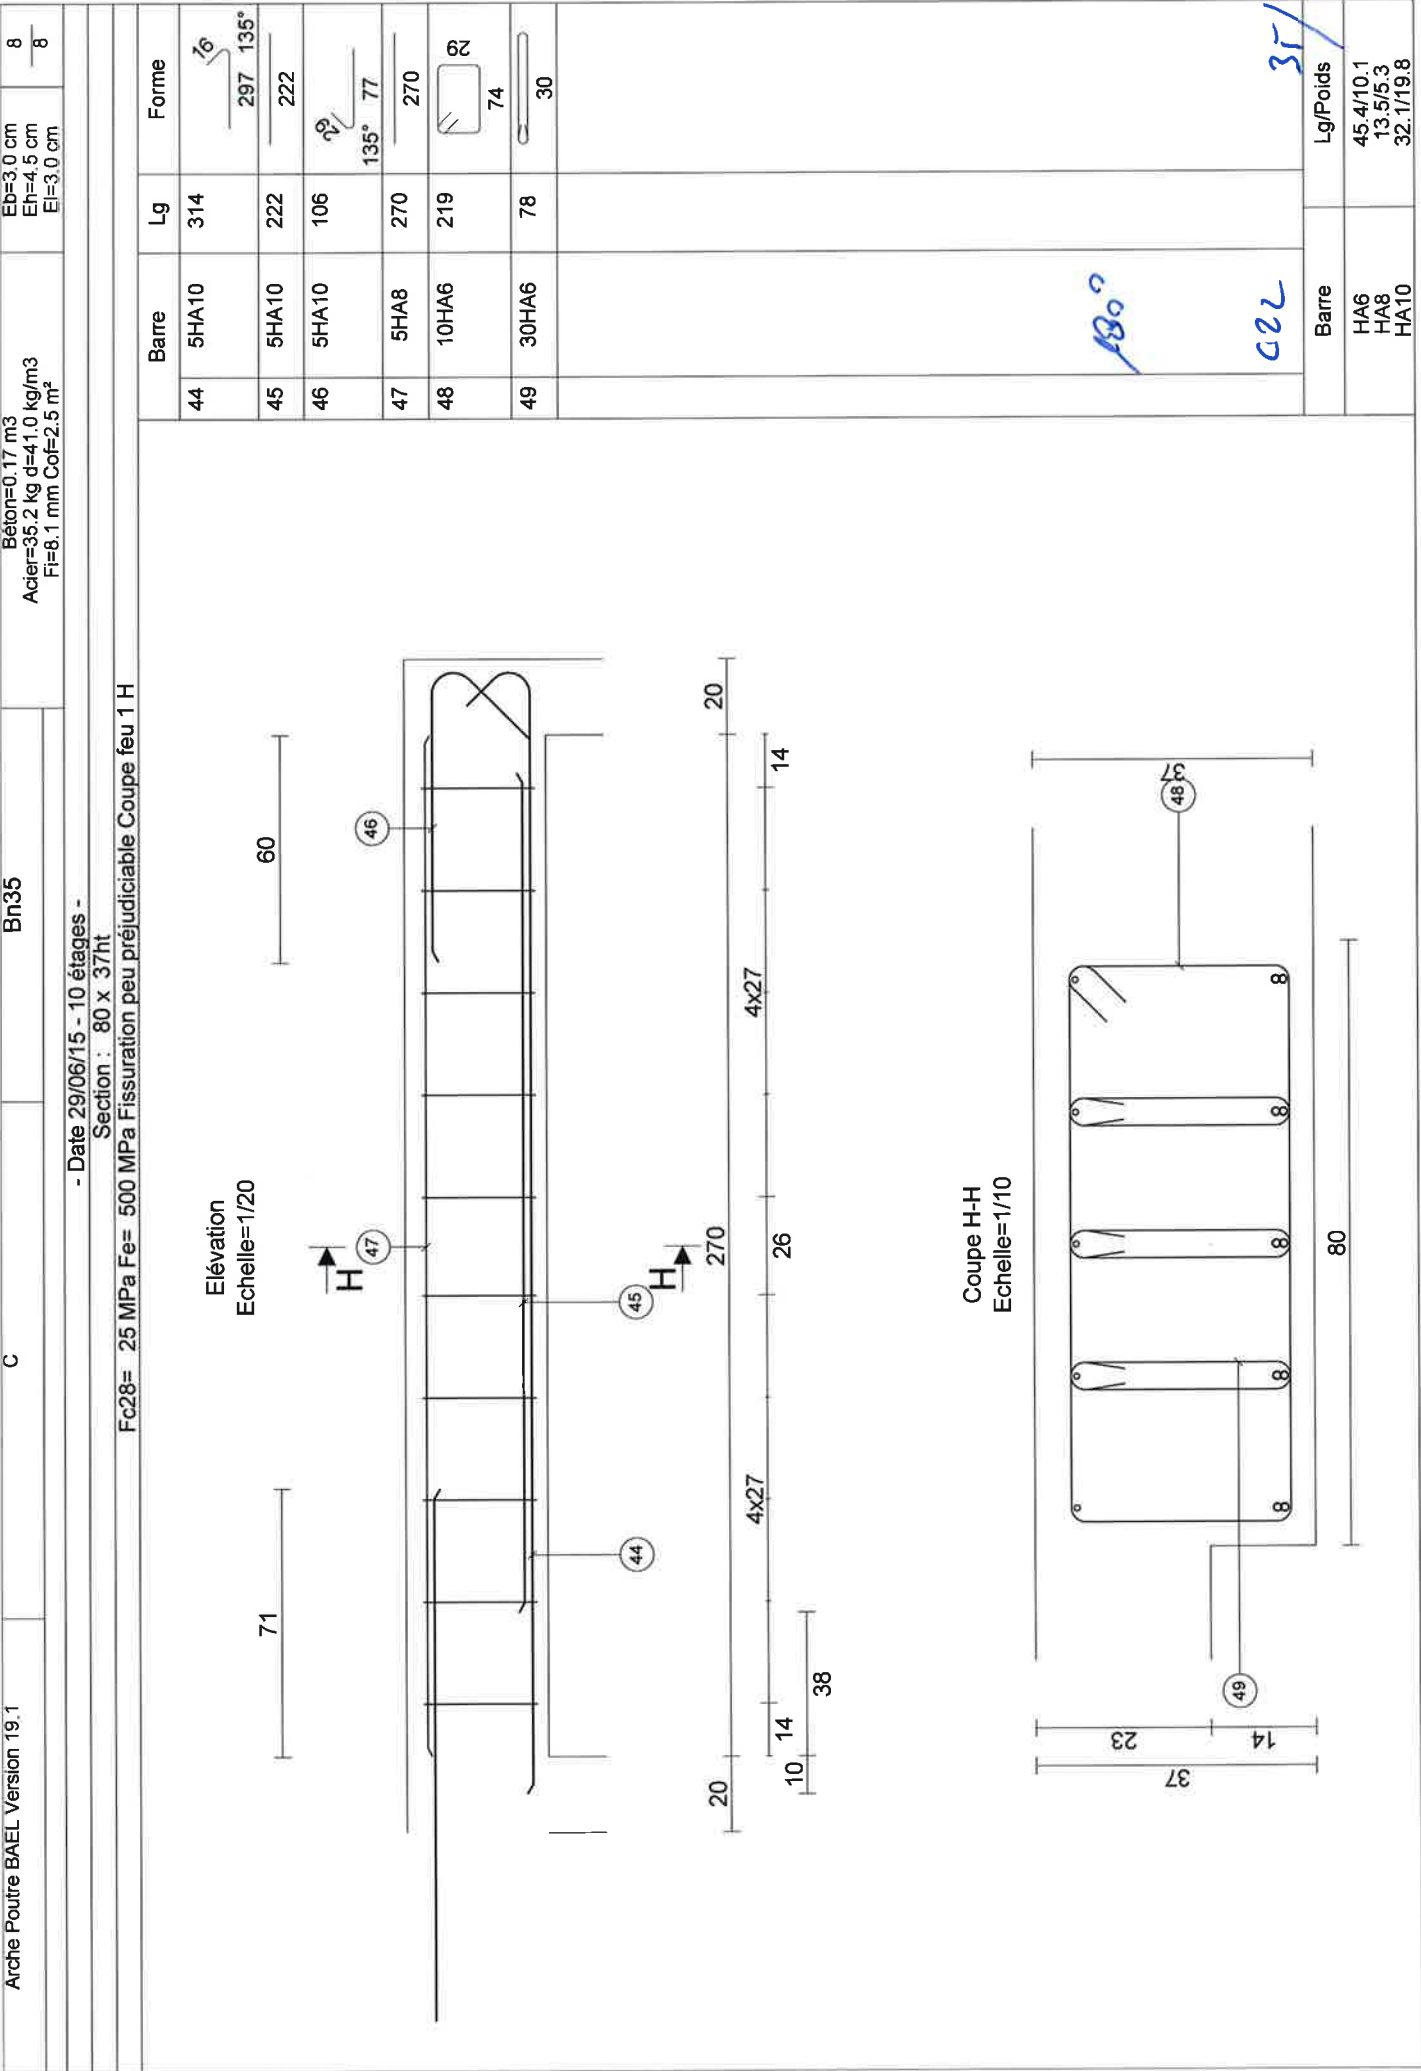


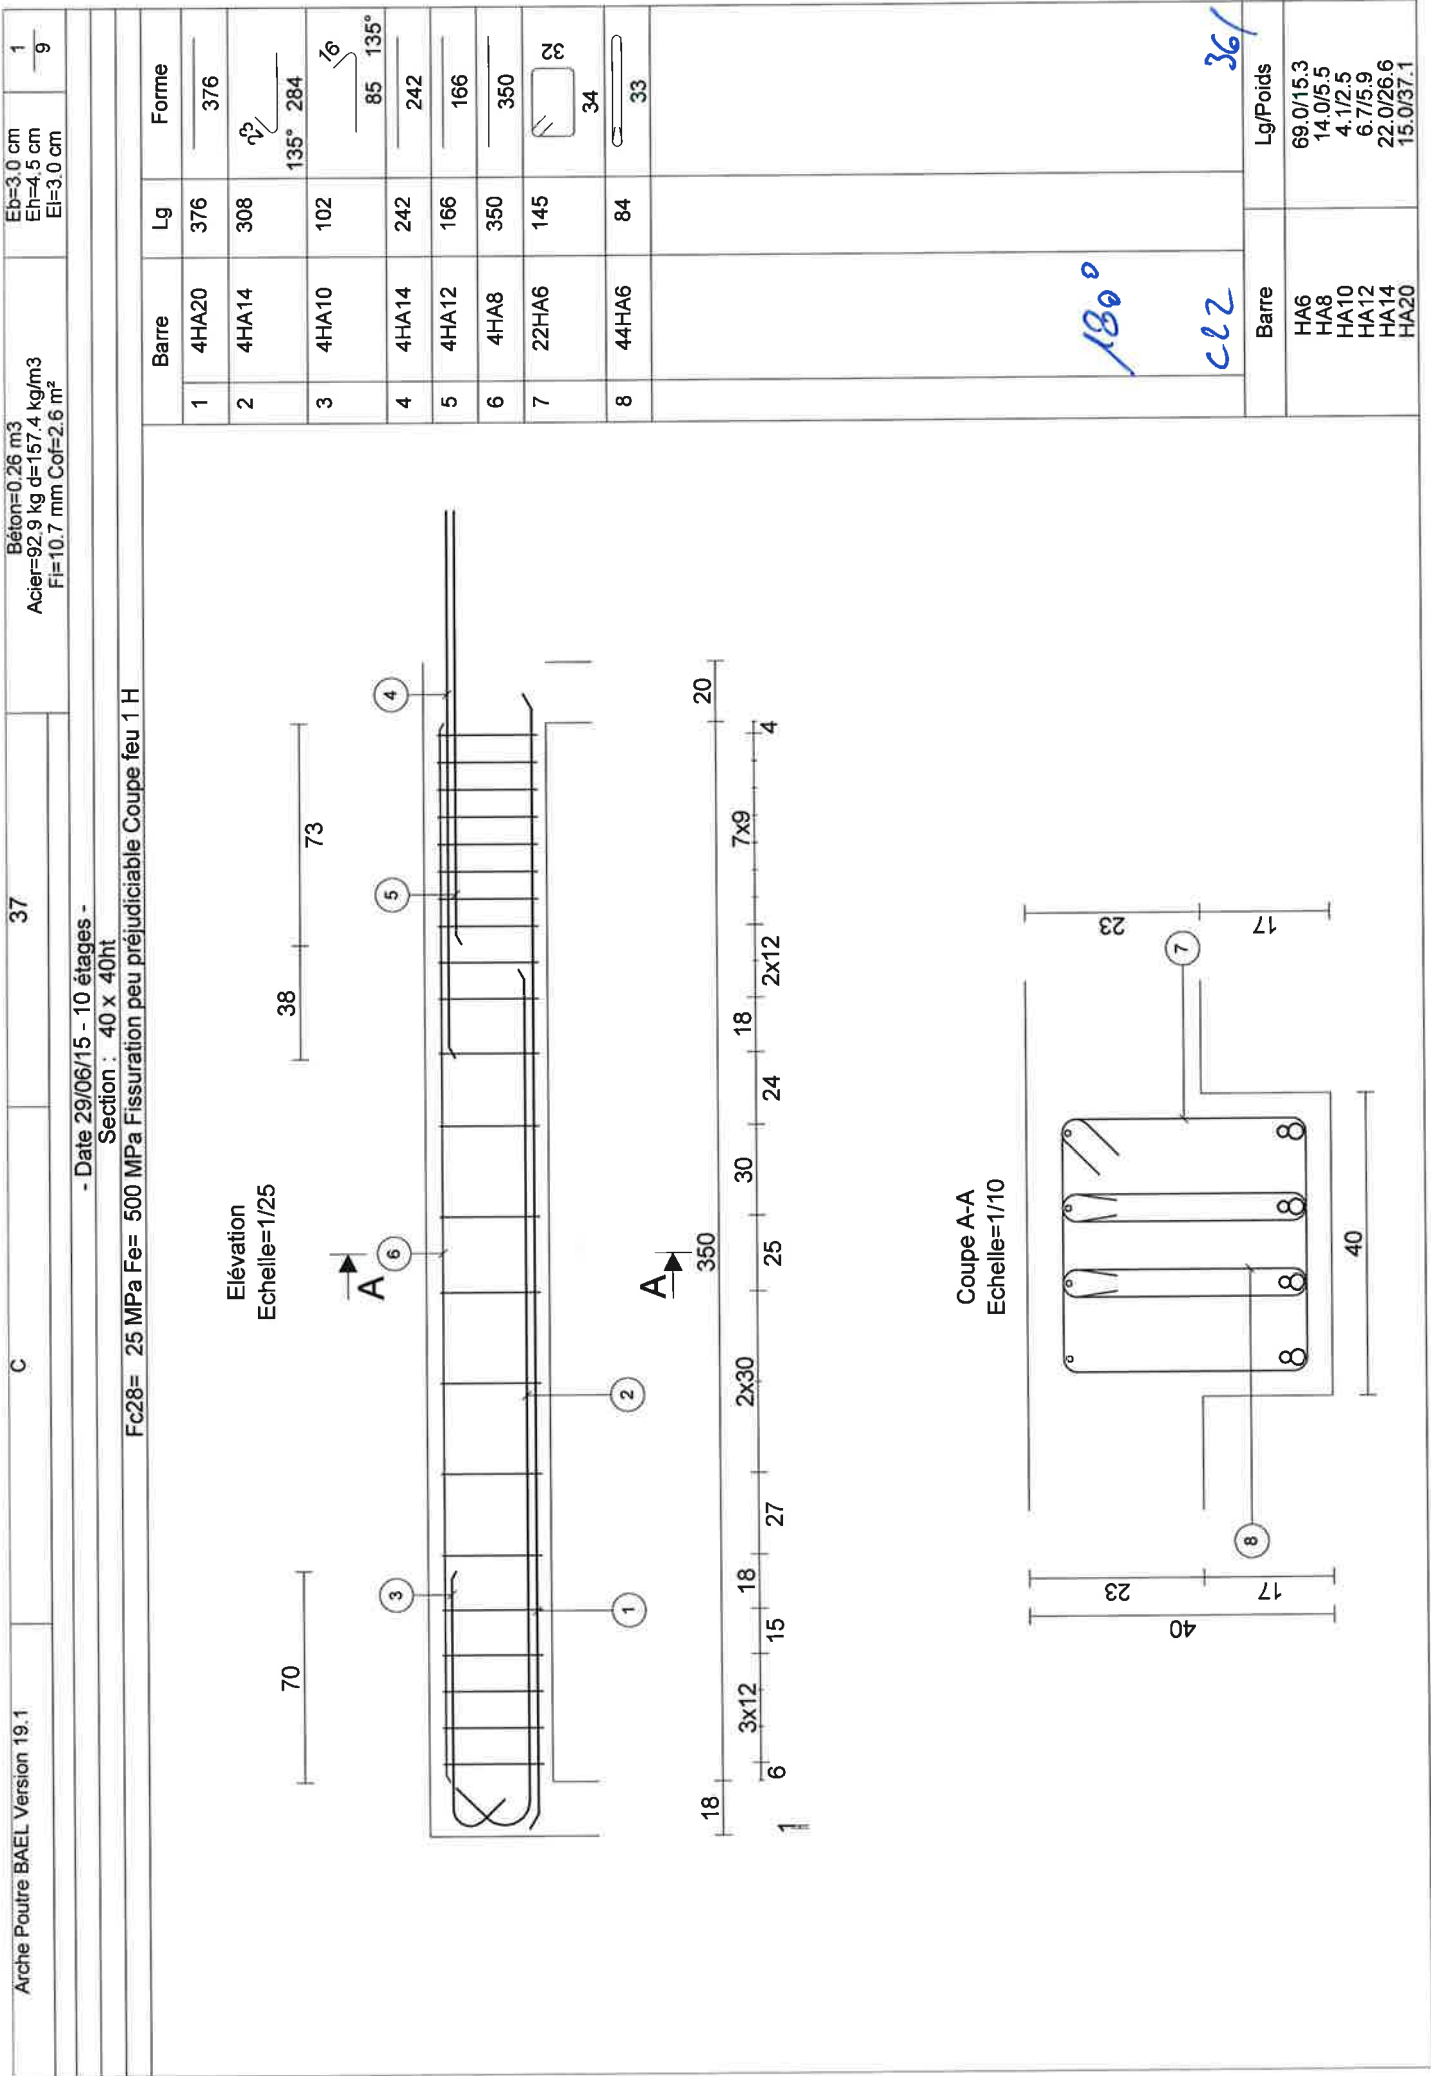


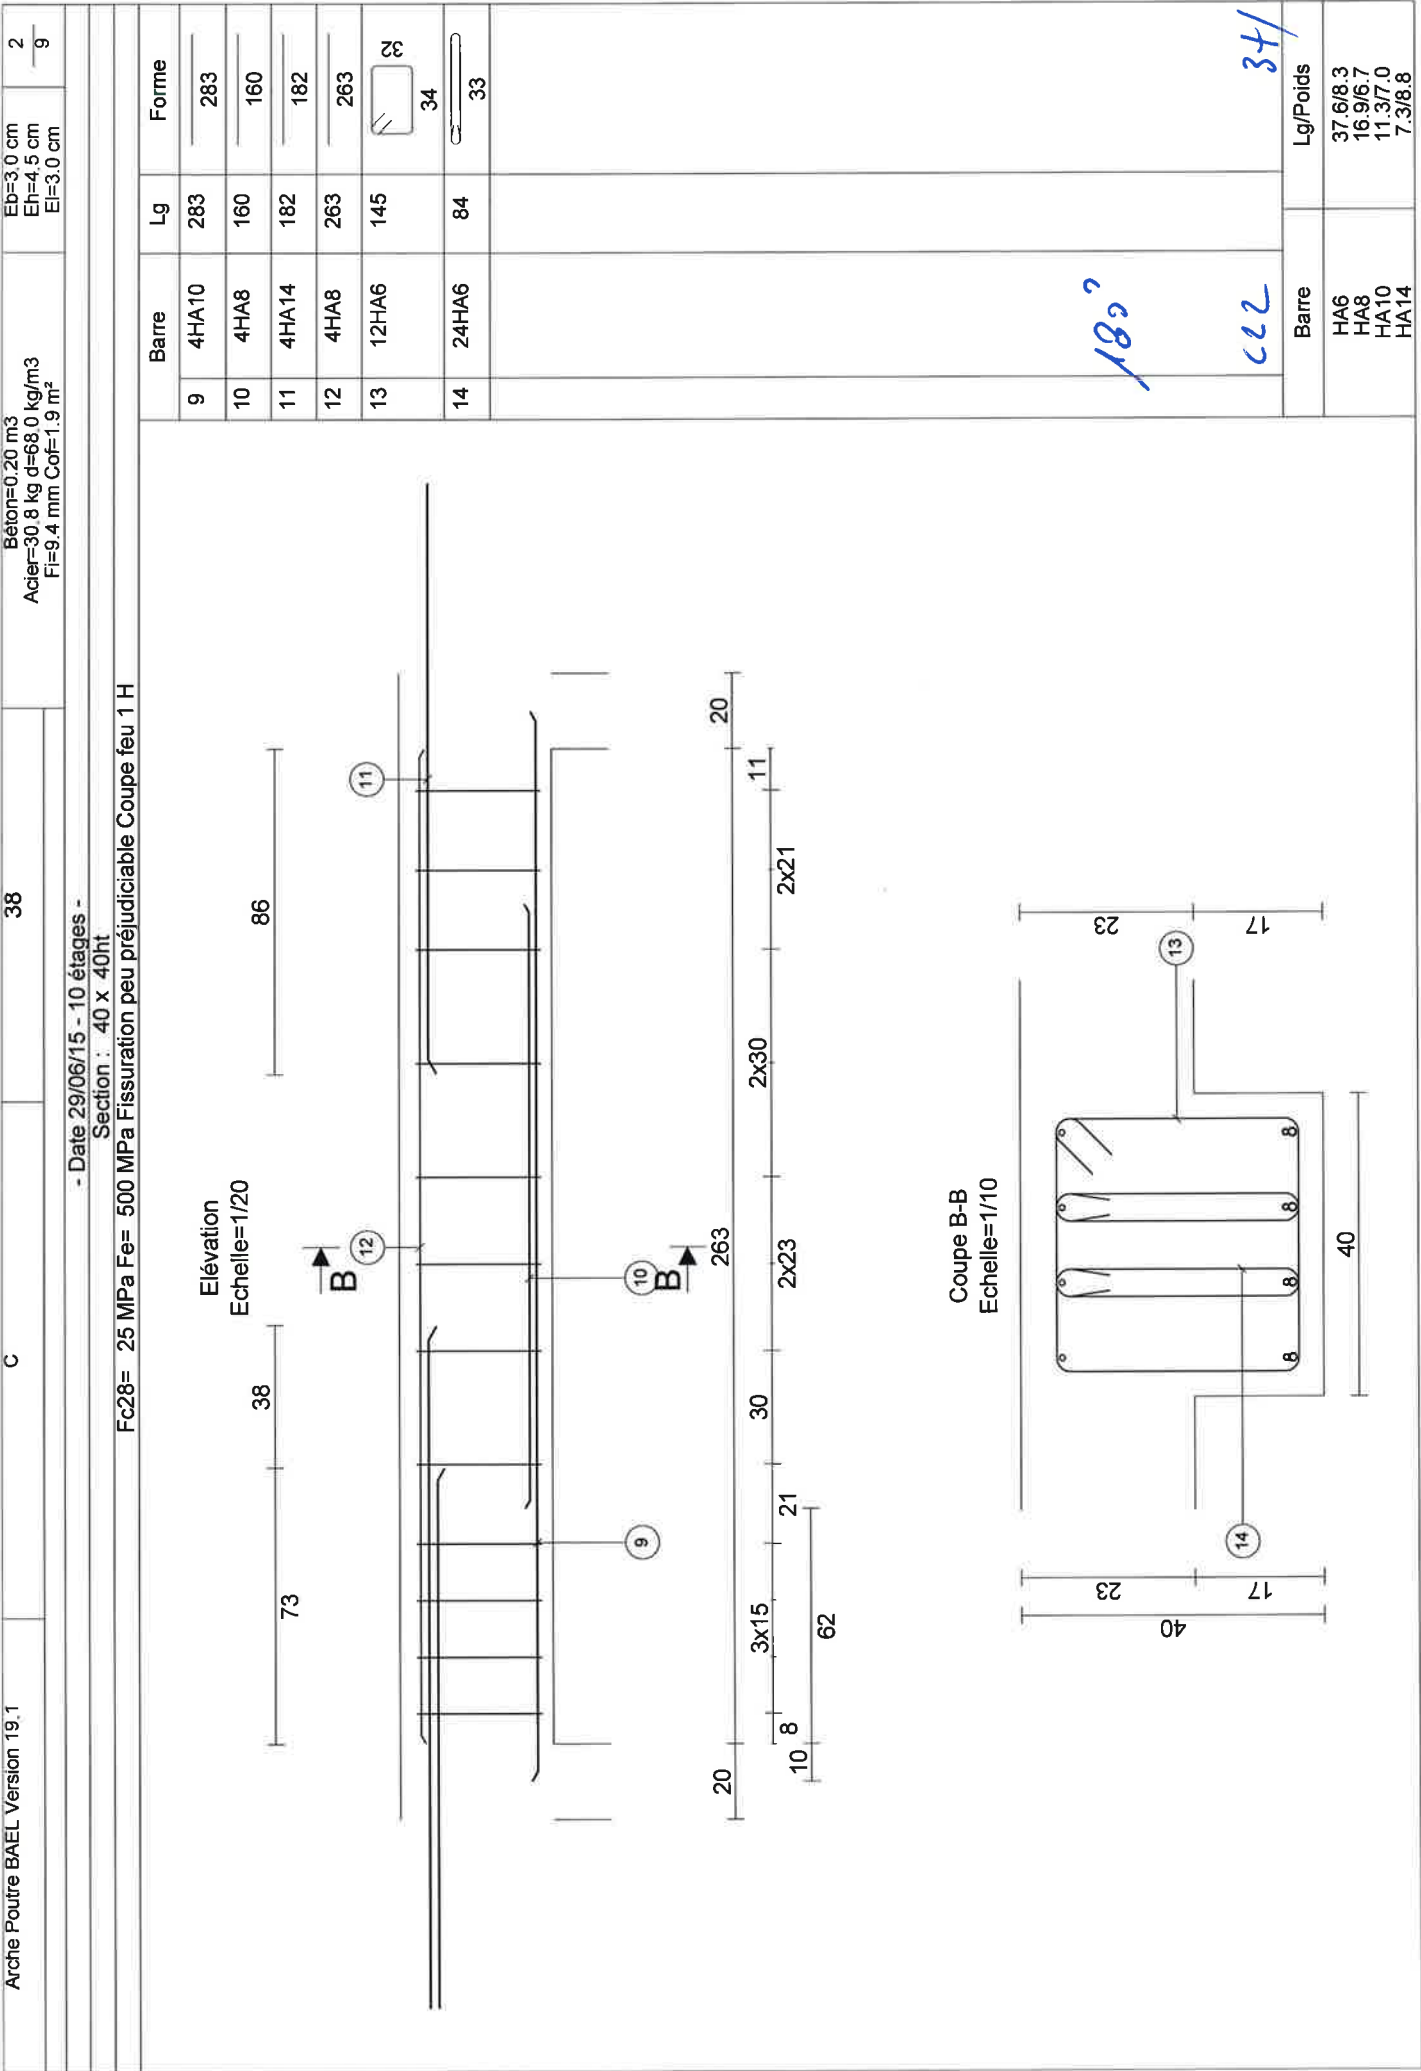


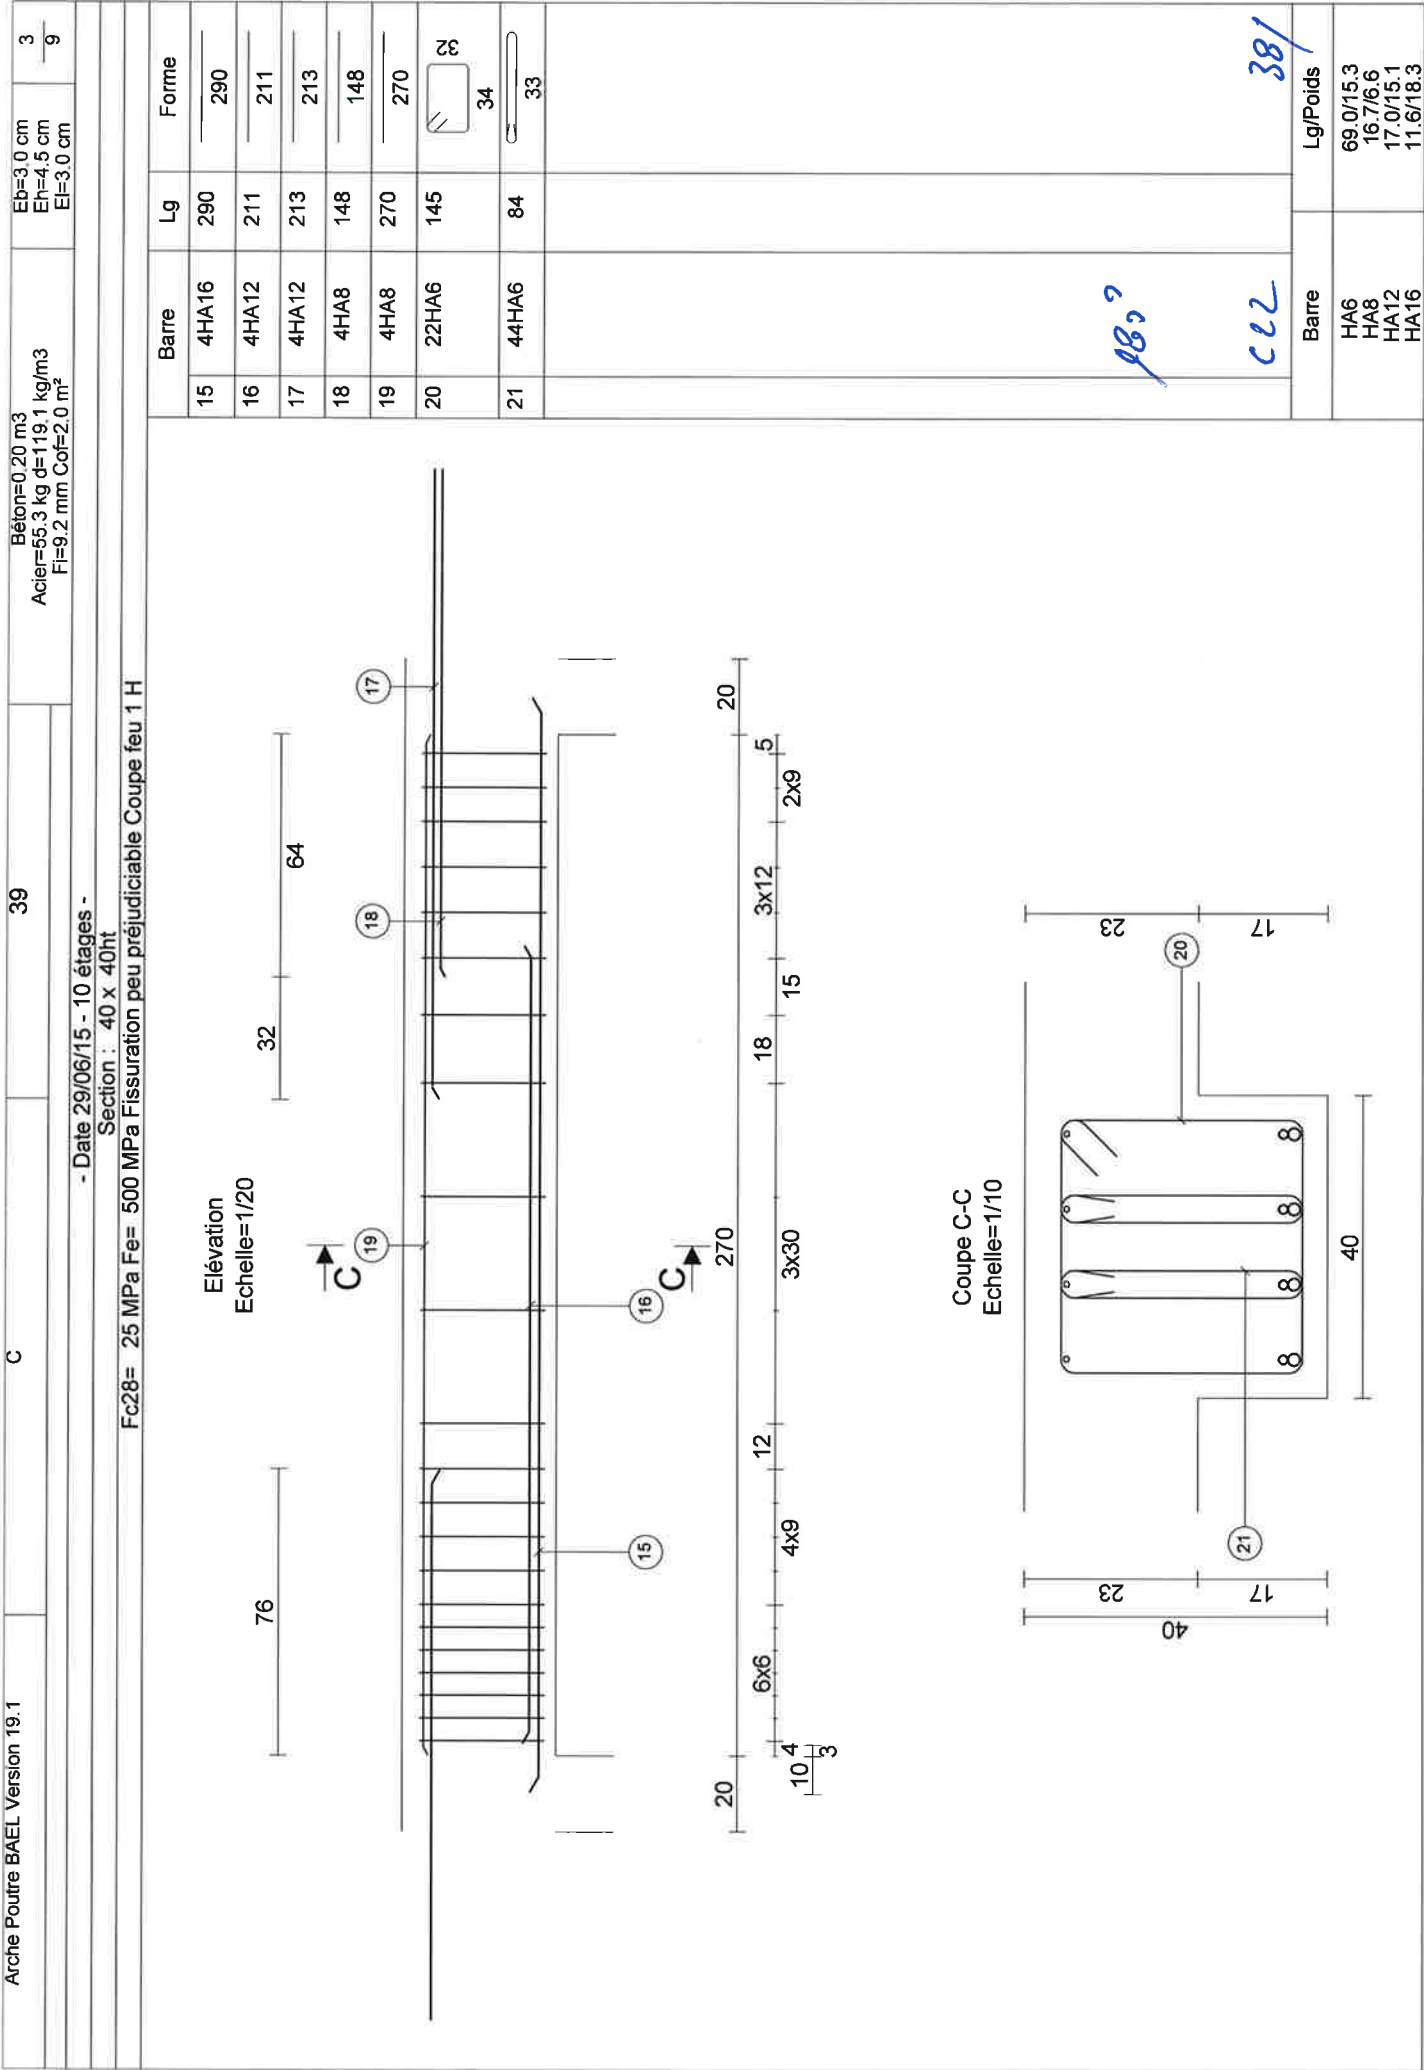


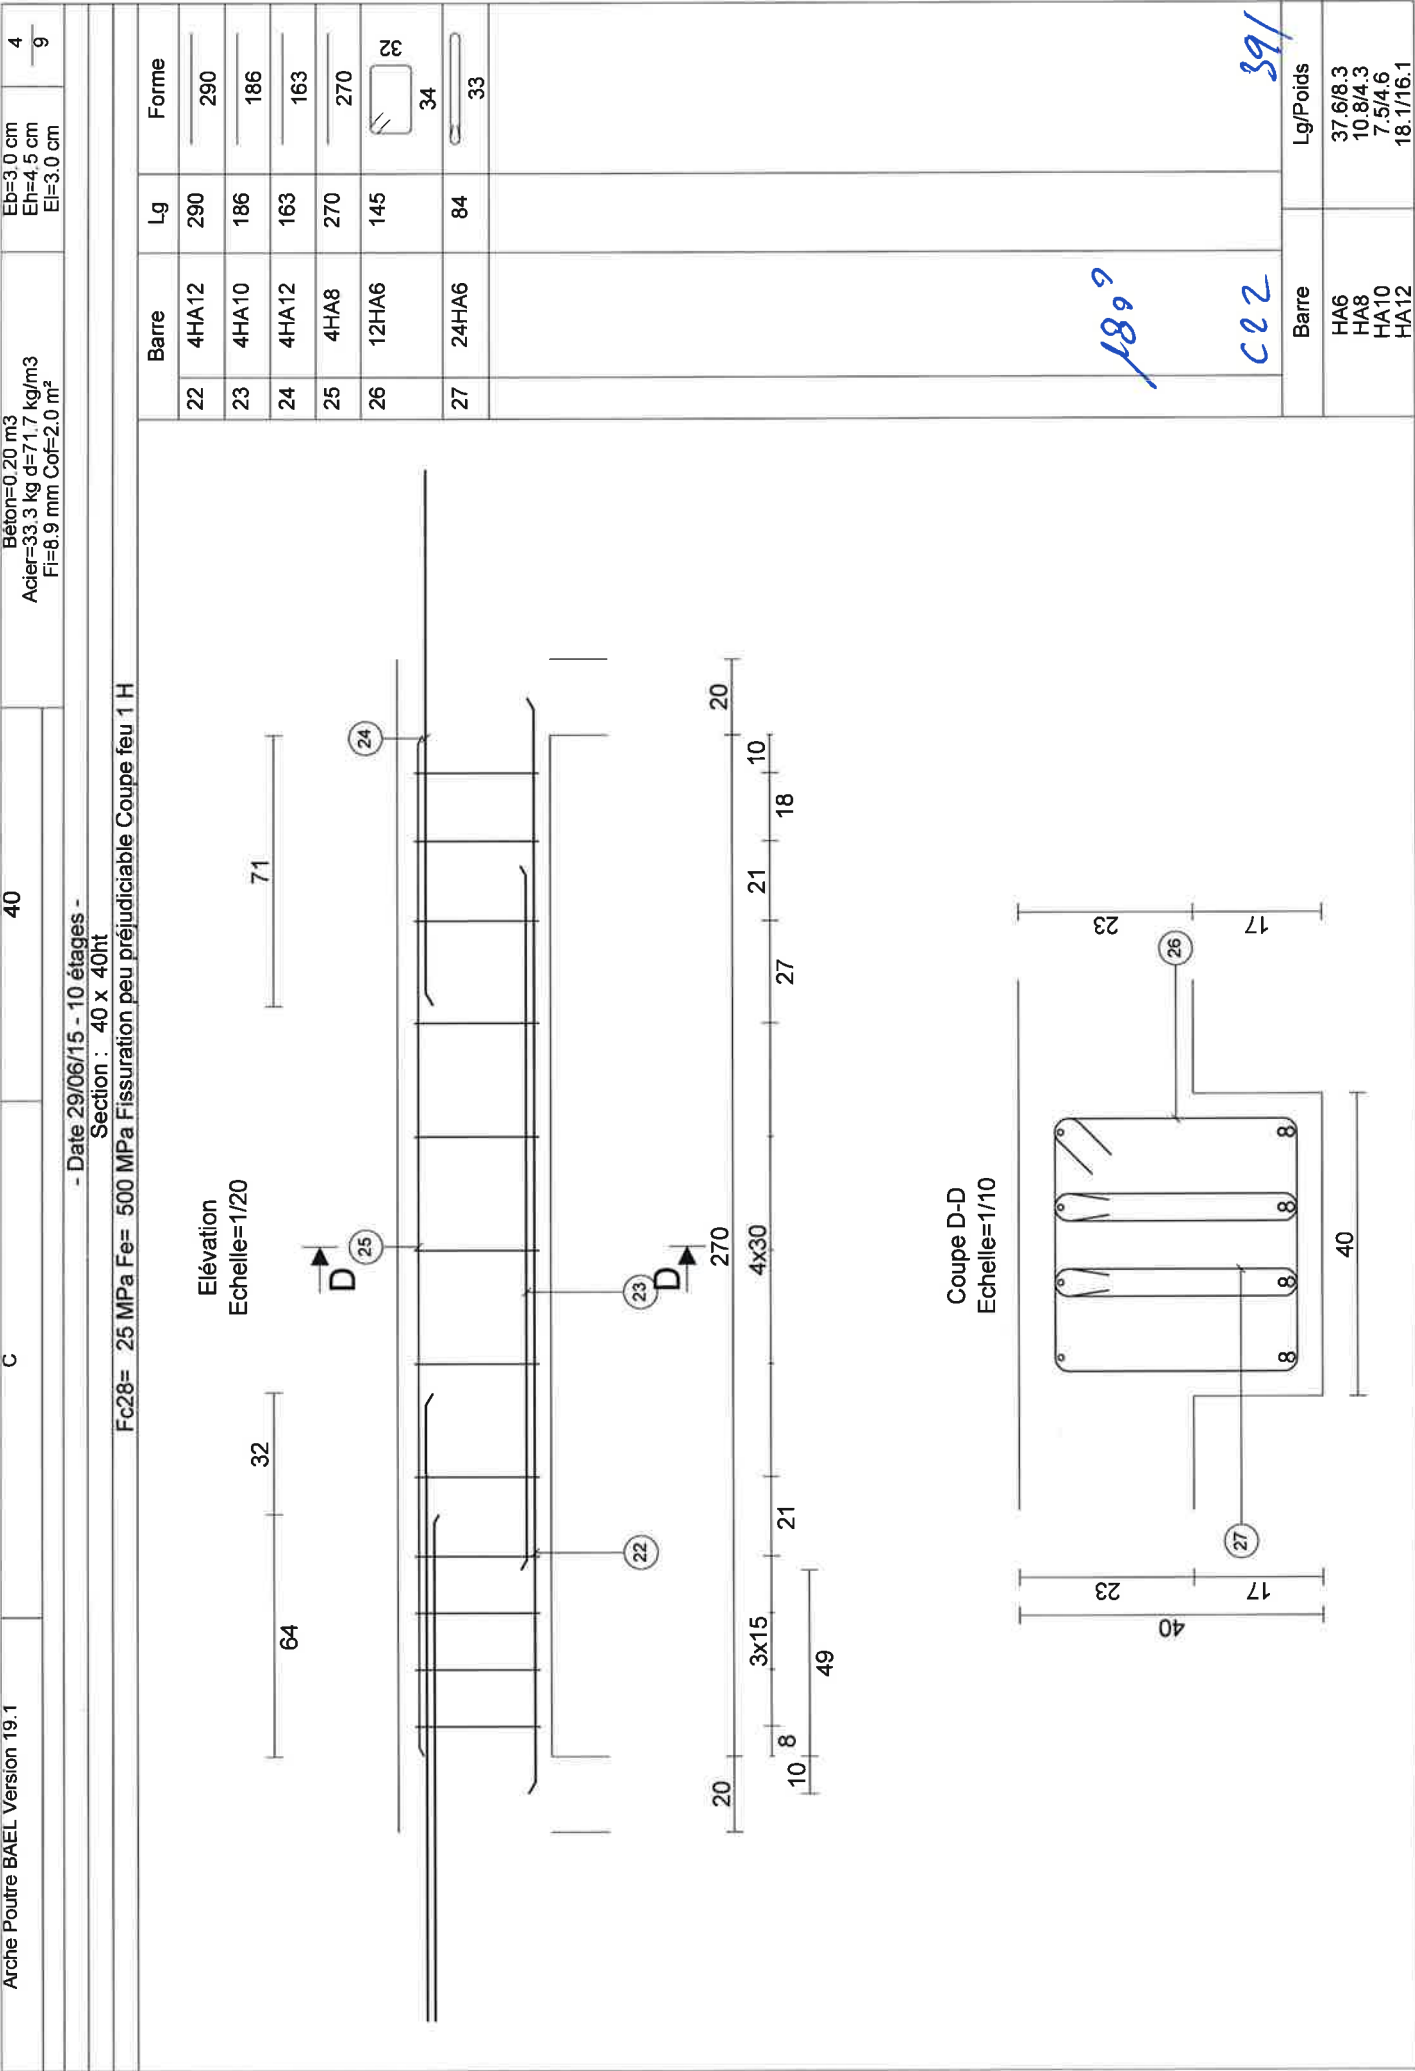

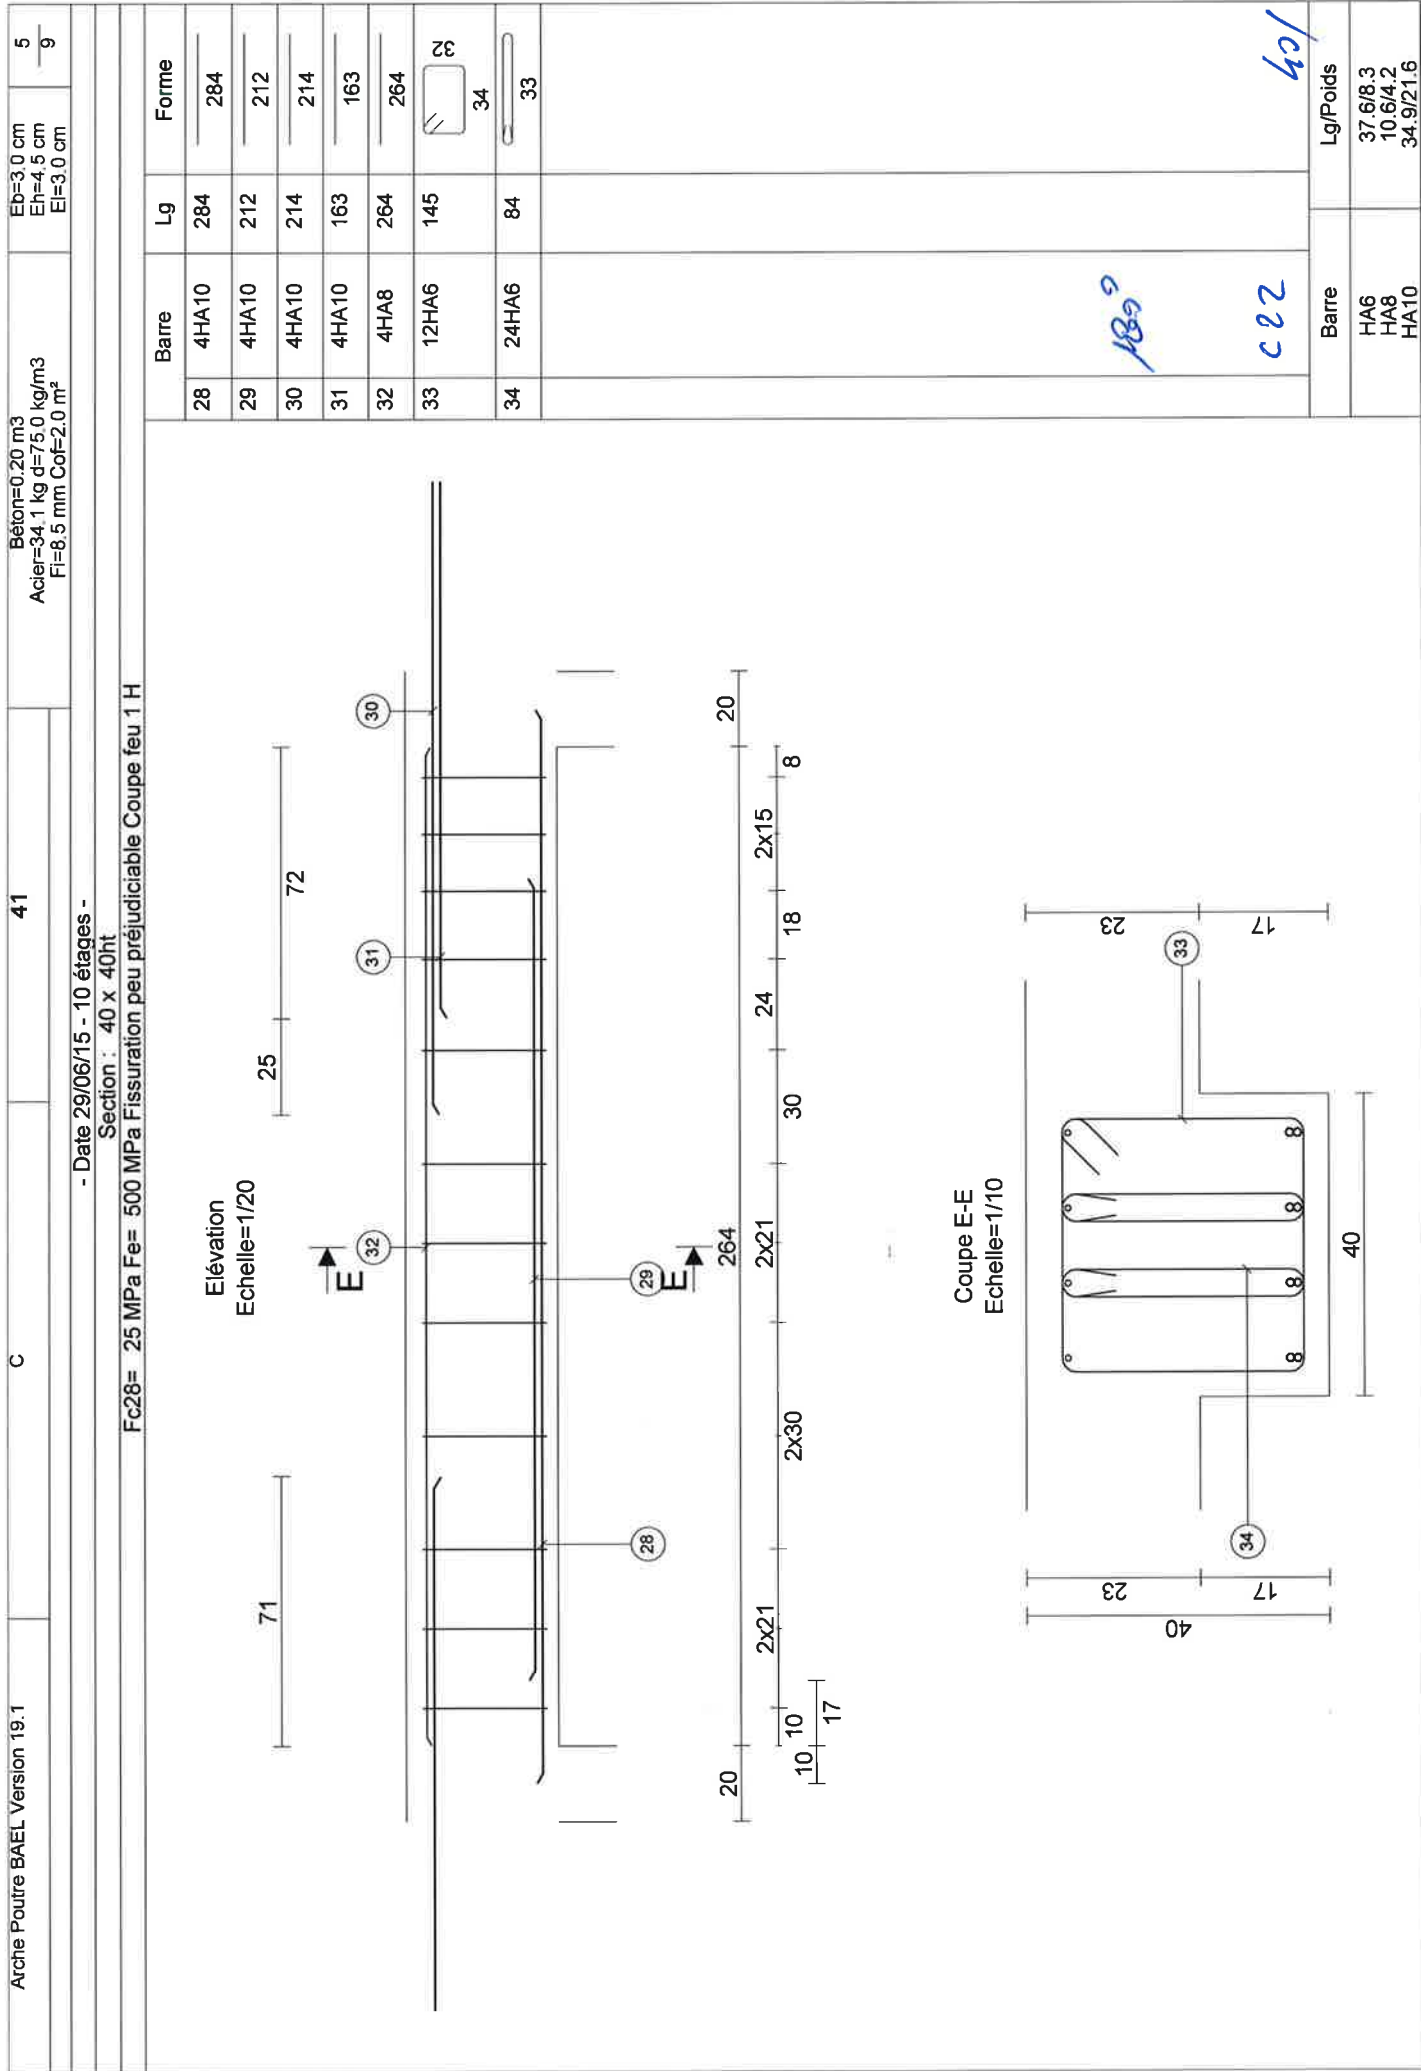

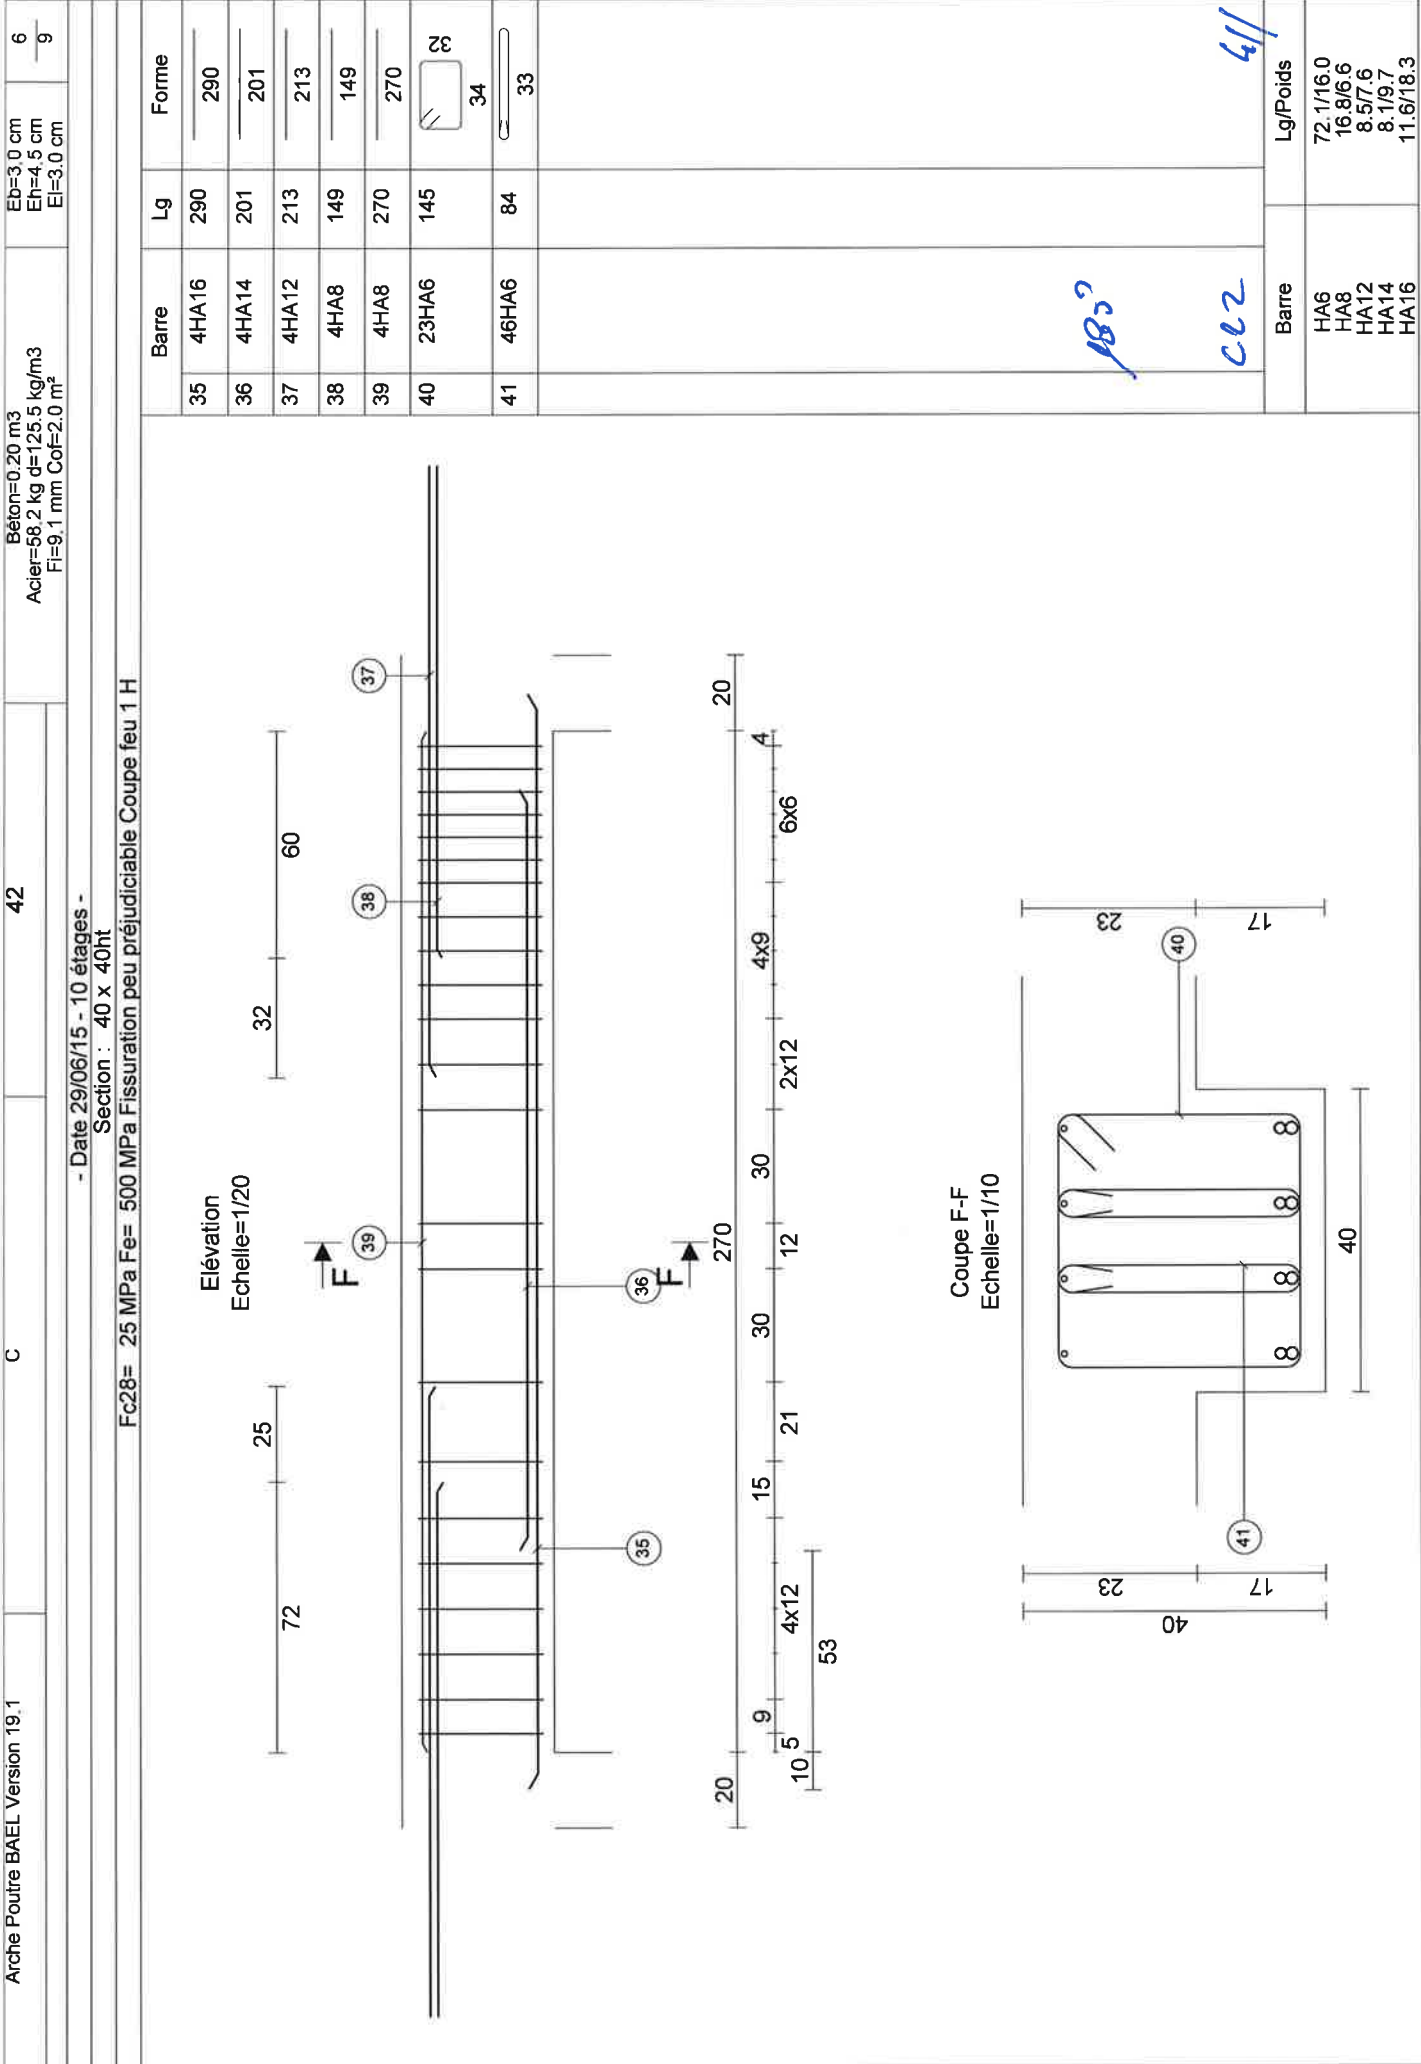

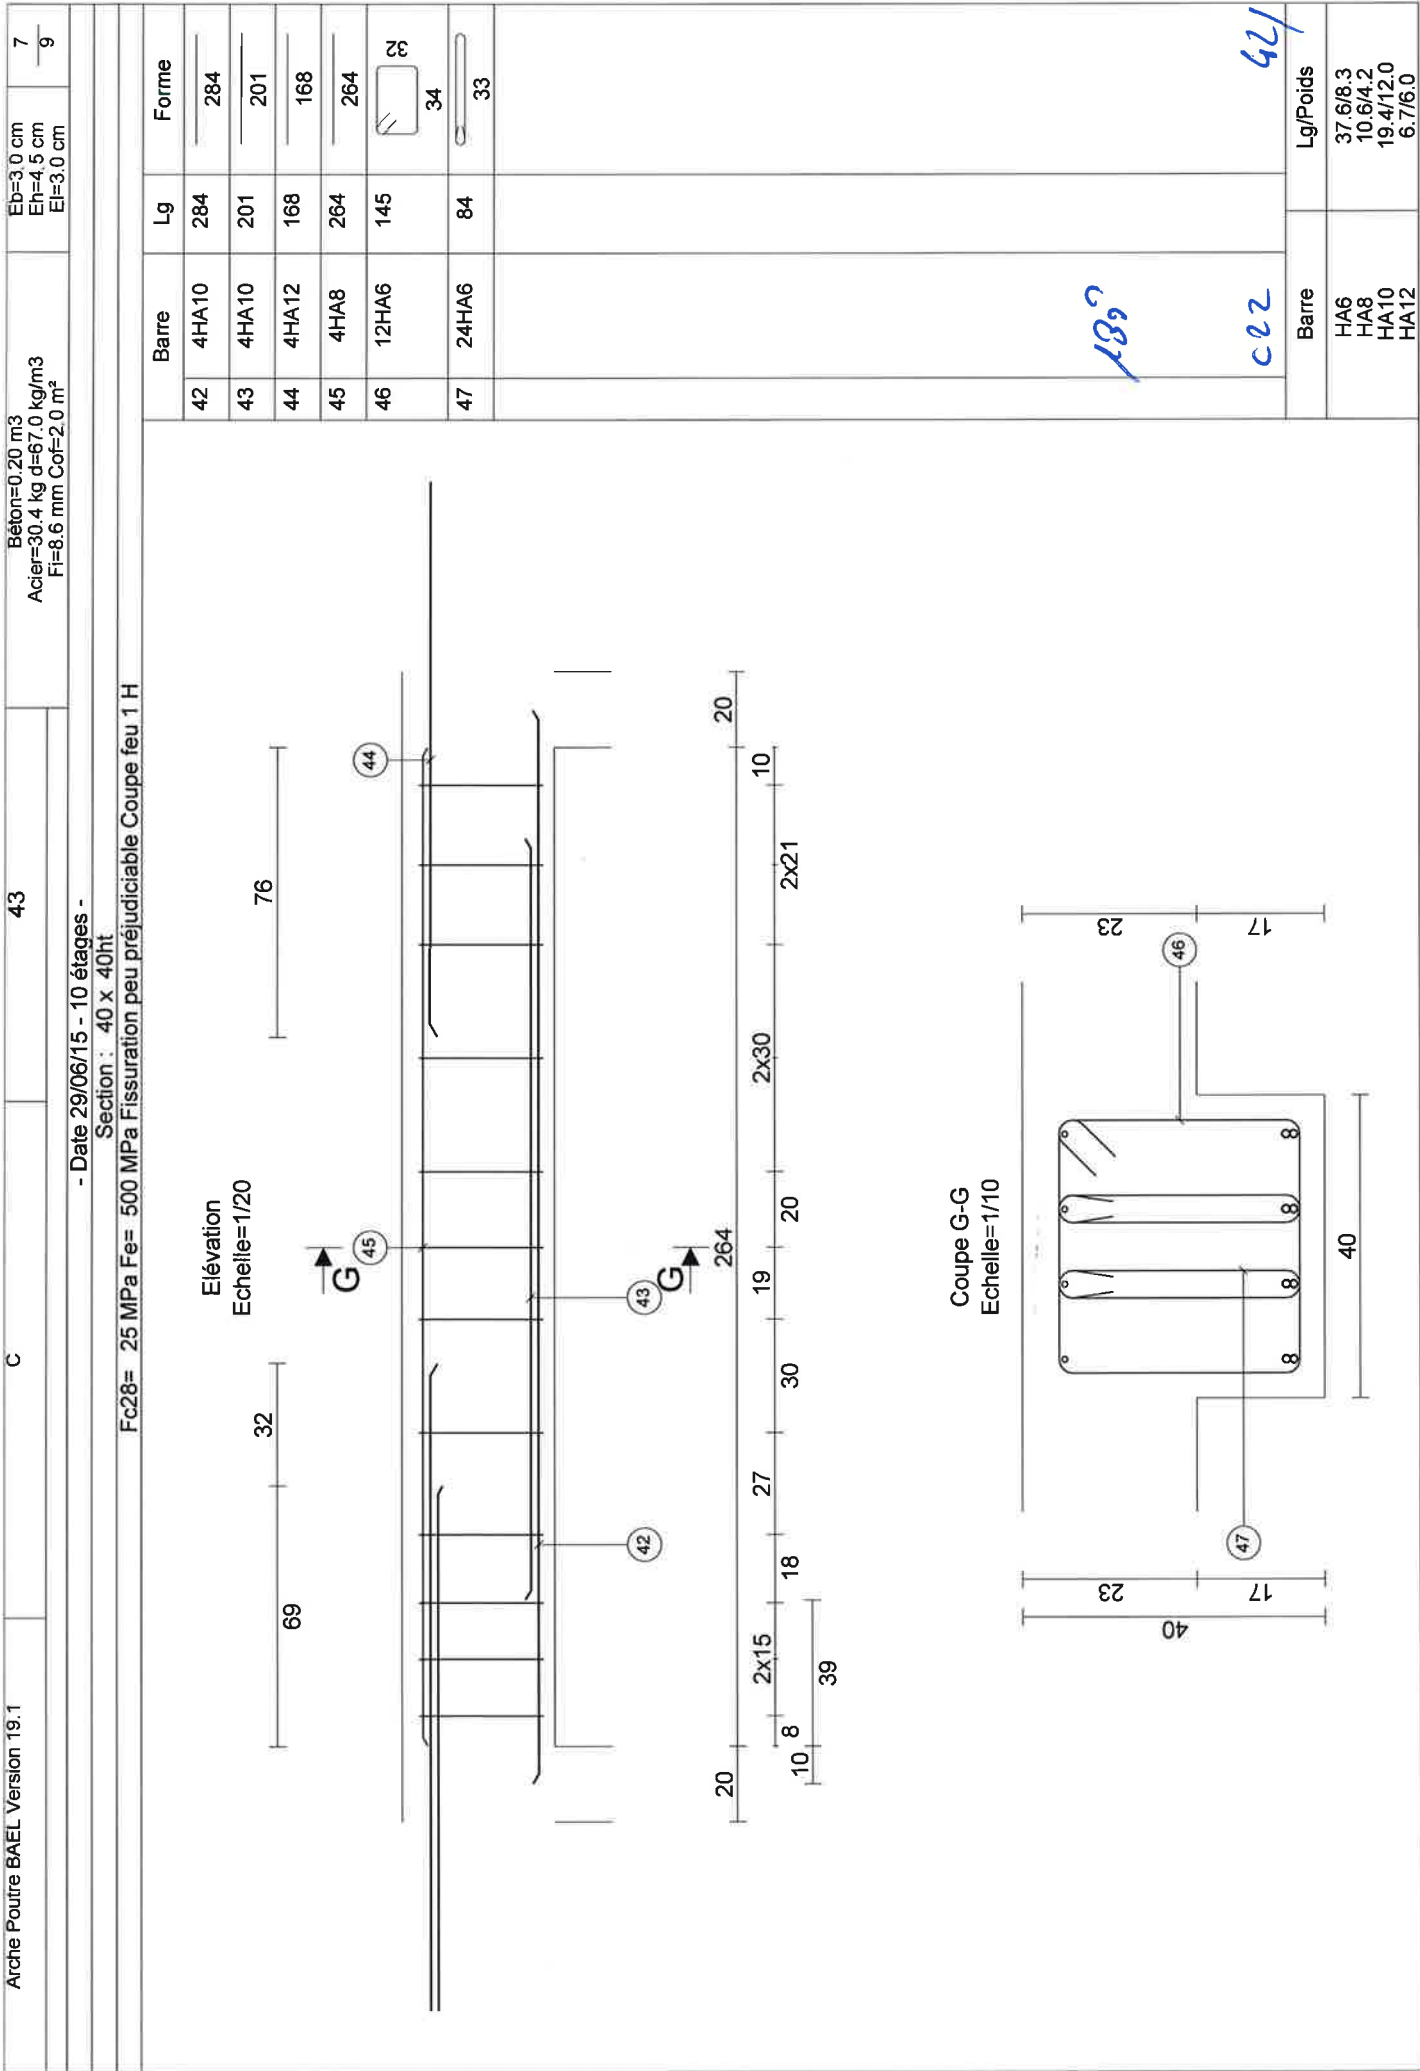

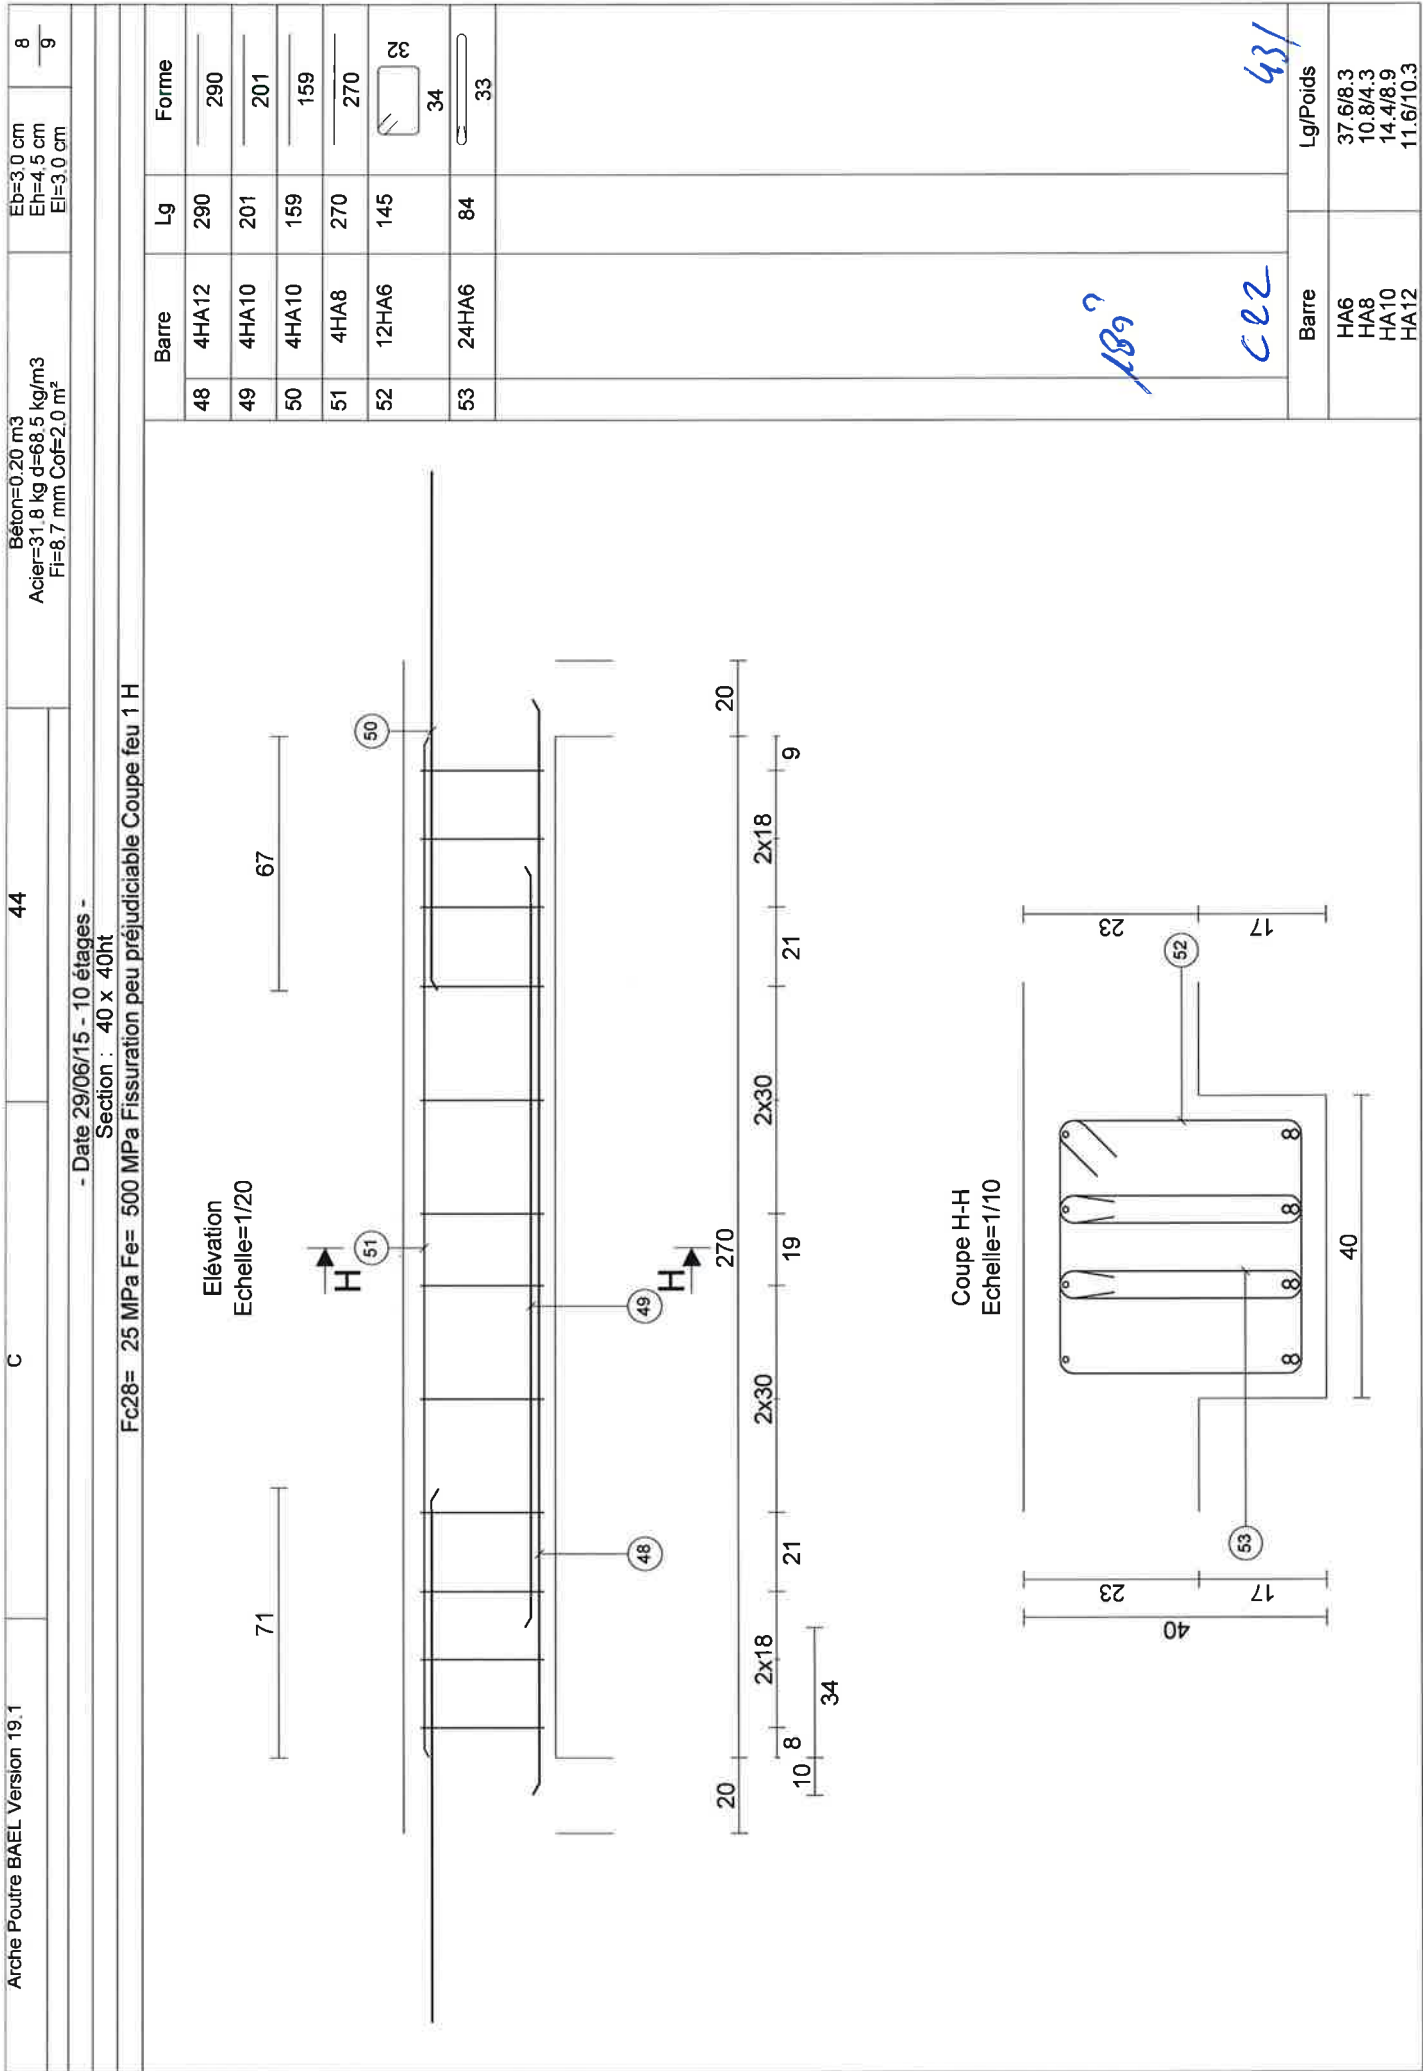

Arche Poutre BAEI Version 19.1	C	45	Béton=0.13 m3 Acier=13.4 kg d=49.1 kg/m3 Fi=8.3 mm Cof=1.1 m²	Eb=3.0 cm Eh=4.5 cm El=3.0 cm	9 9
- Date 29/06/15 - 10 étages - Section : 40 x 40ht					
Fc28= 25 MPa Fe= 500 MPa Fissuration peu préjudiciable Coupe feu 1 H					
Elévation Echelle=1/20 Coupe I-I Echelle=1/10					
54	4HA10	160	160	Forme	160
55	4HA10	96	96	135° 67	135° 67
56	4HA8	150	150	150	150
57	2HA10	96	96	67 135°	67 135°
58	5HA6	145	145	34	34
59	10HA6	84	84	33	33
18.7				441	
222				Lg/Poids	
Barre				15.7/3.5	
HA6				6.0/2.4	
HA8				12.2/7.5	
HA10					