


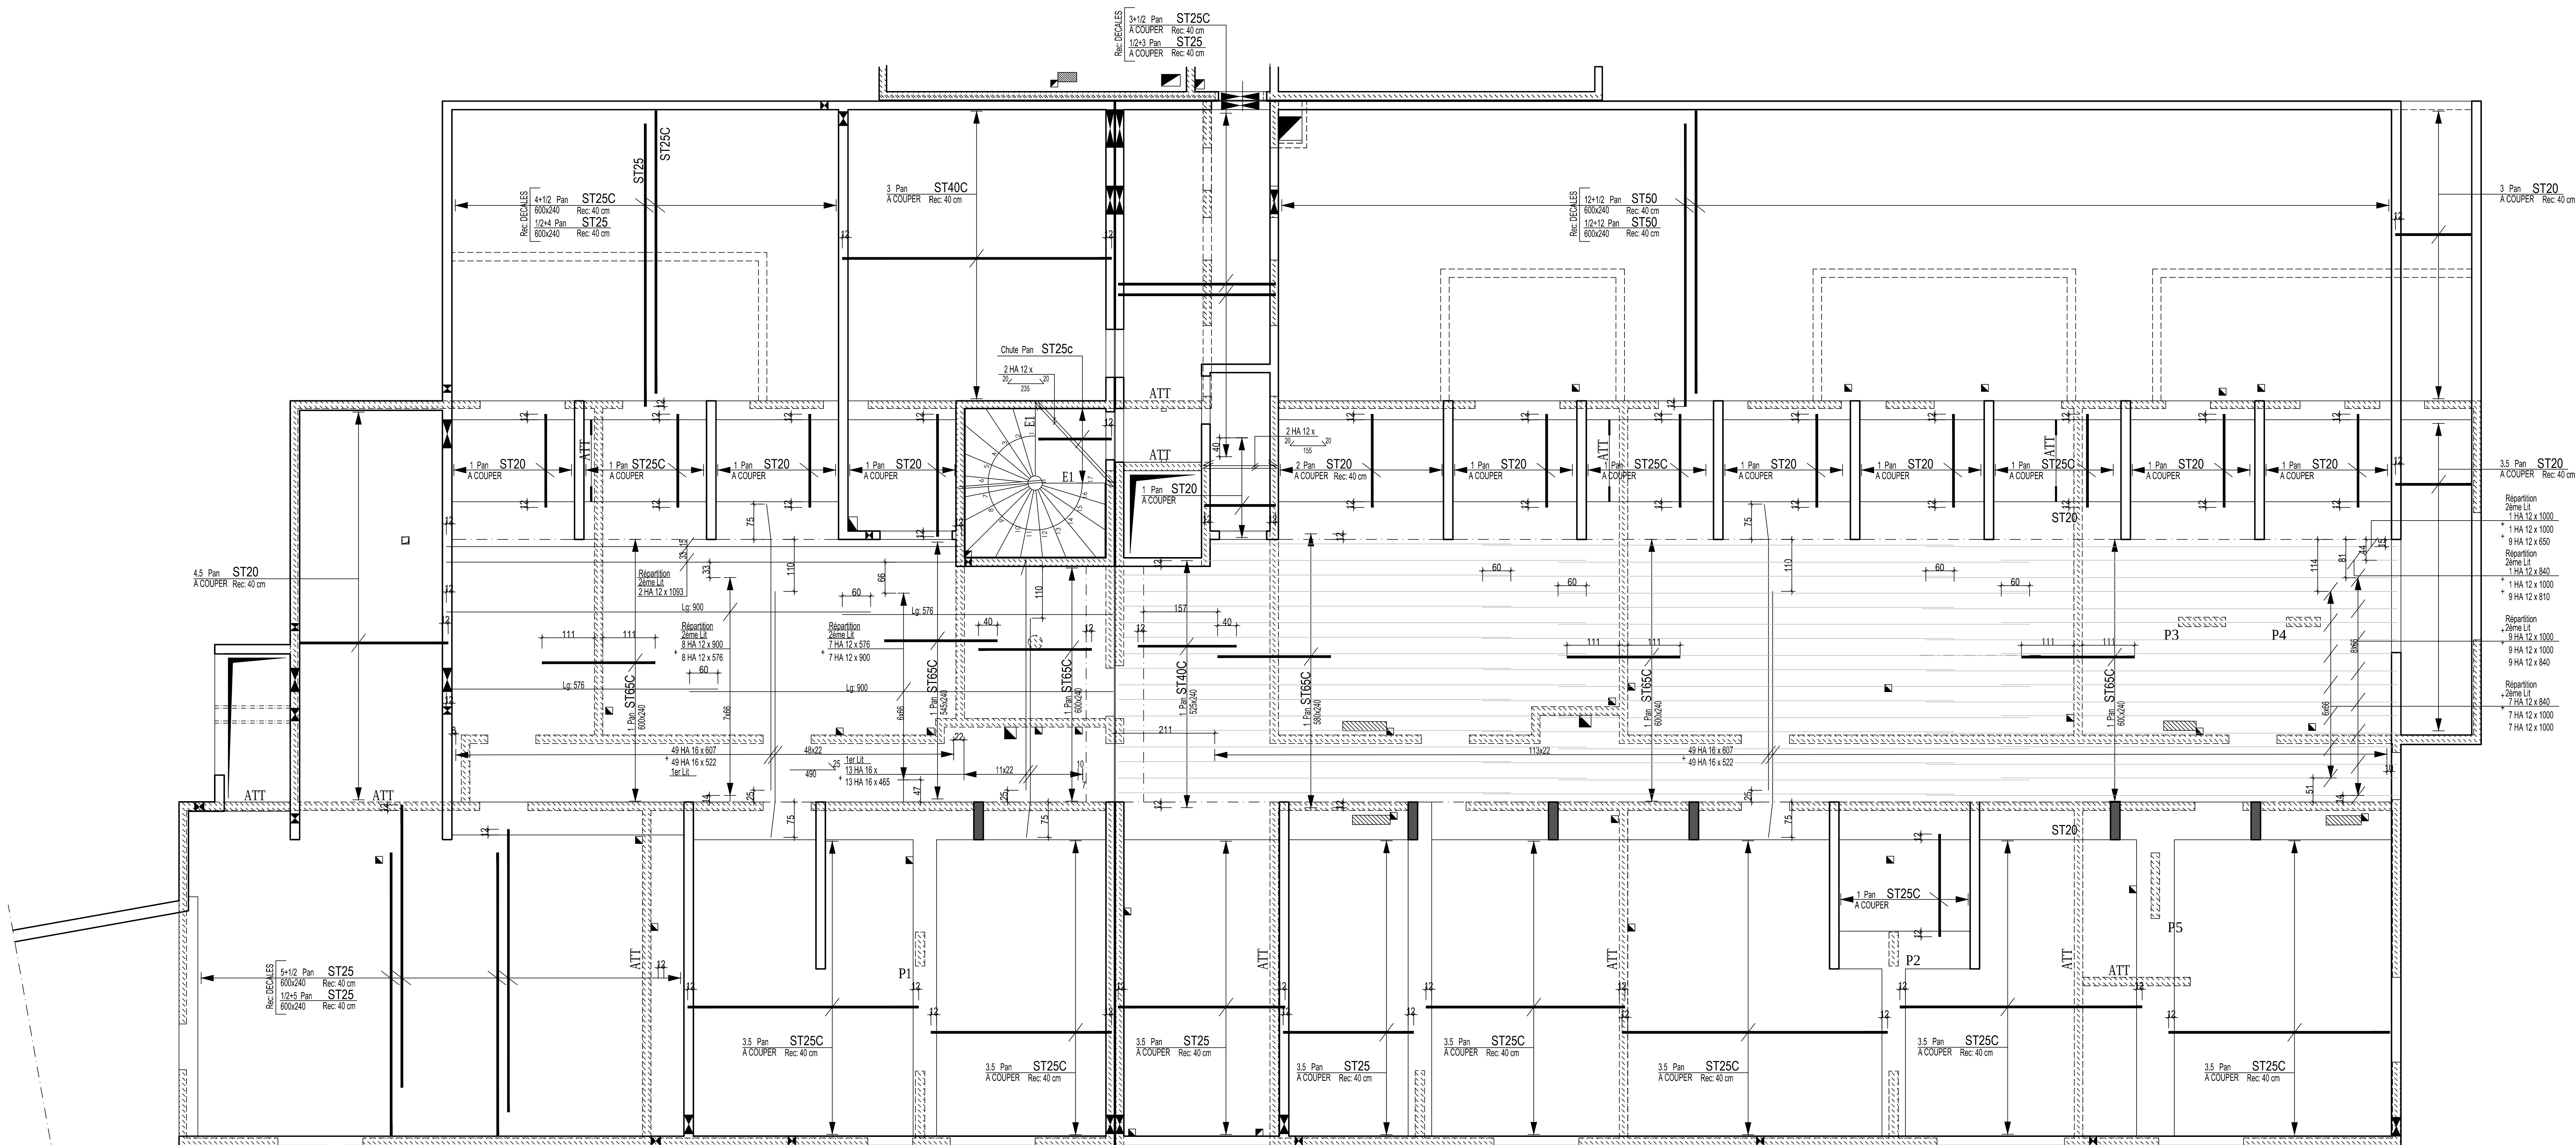


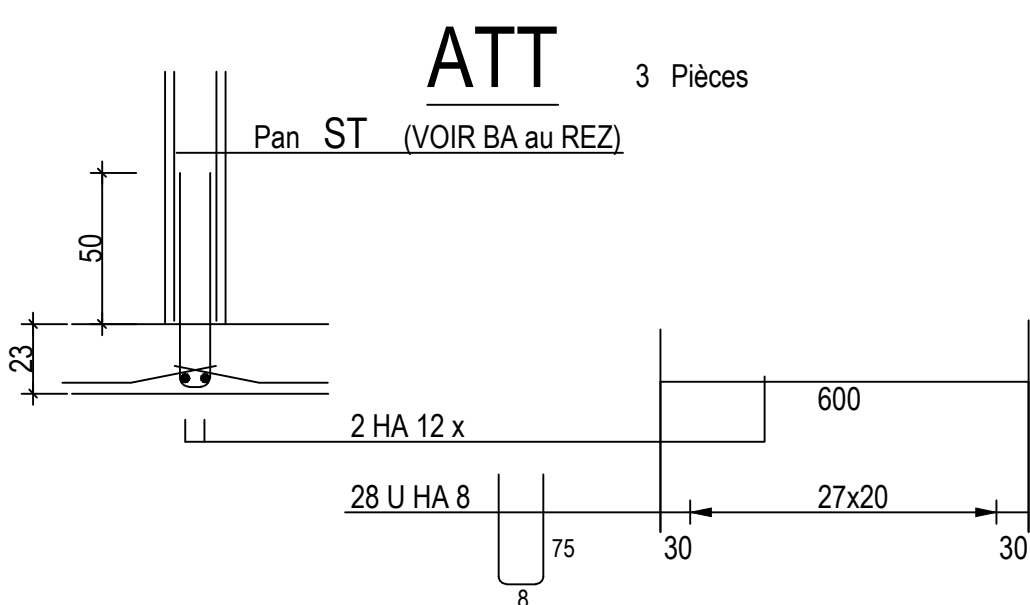


Attentes mur sur poutre, dalle épaisse
et muret des terrasses côté EST

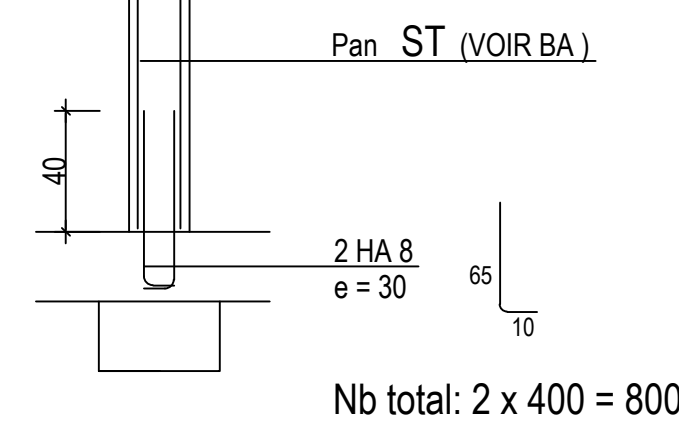



ATTENTES POTEAUX DANS SEMELLES

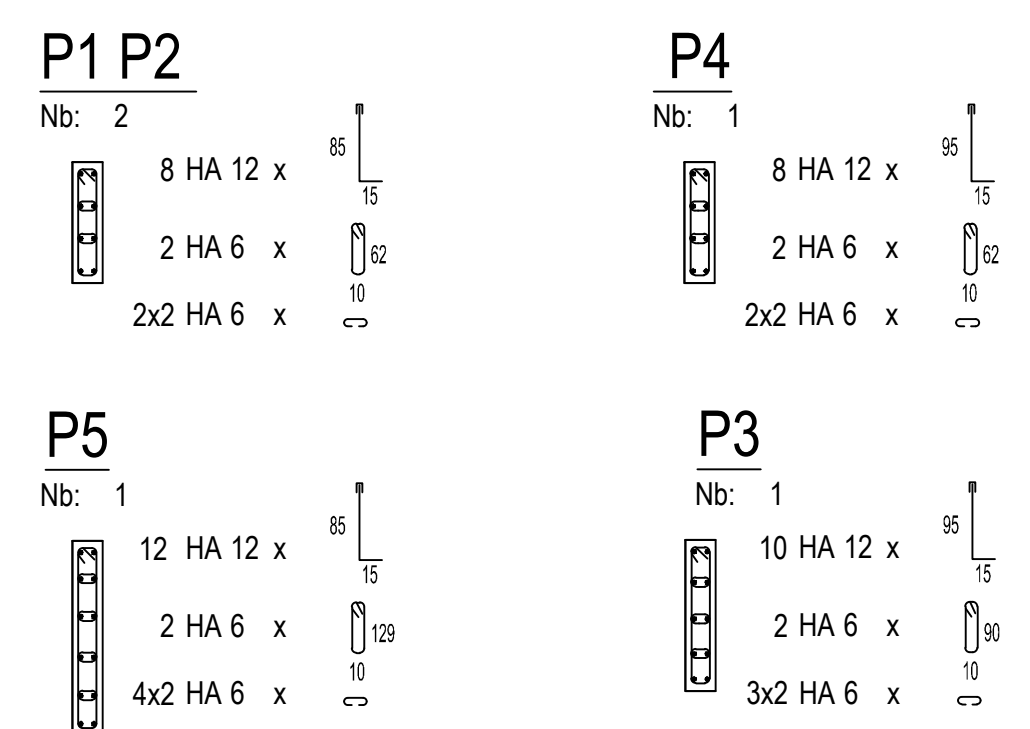

RENFORTS RESESERVATIONS
JUSQU'A Ø200 mm

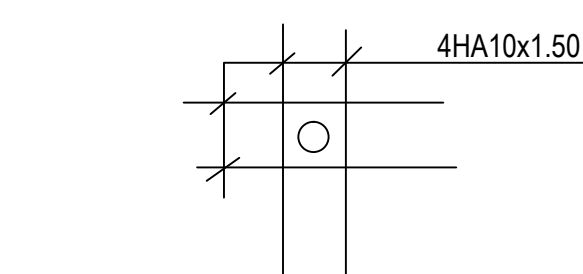


Principe de renfort aux droits des gaines:

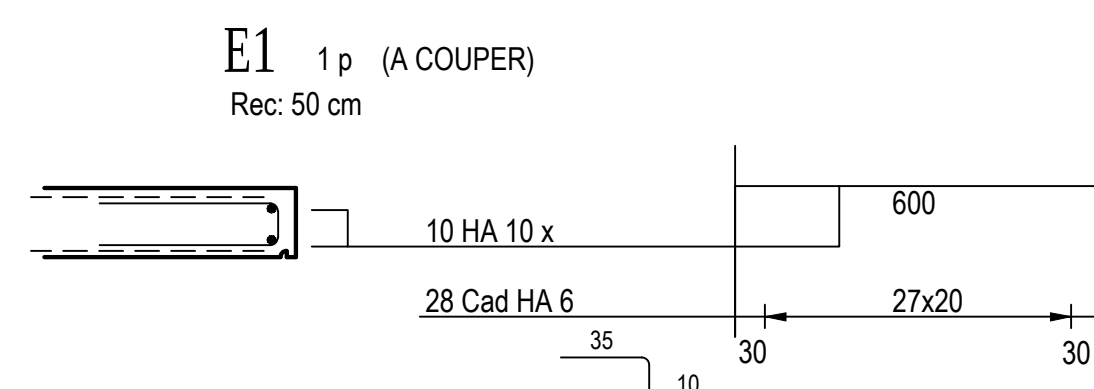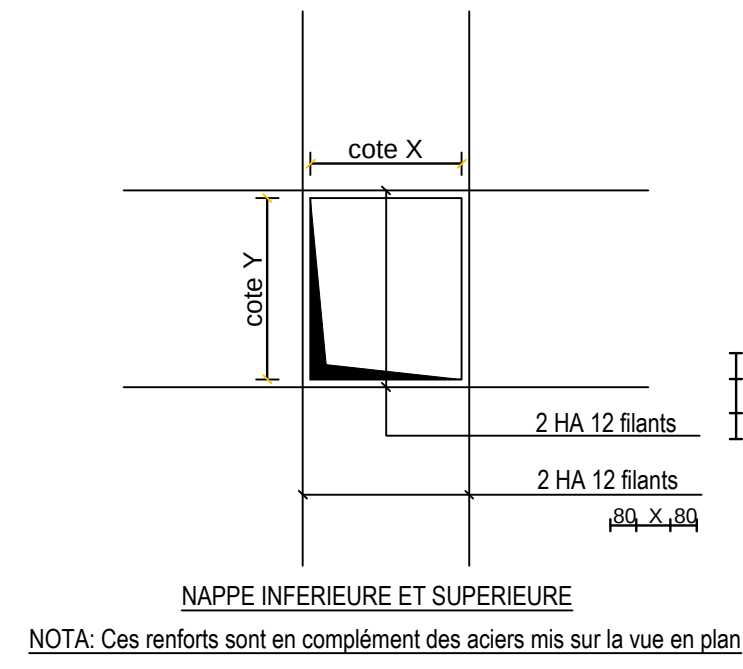

RECA. T.S.		
PAF 10	420x240	0
ST20	600x240	14
ST25	600x240	17
ST30	600x240	0
ST35	600x240	0
ST50	600x240	25
ST60	600x240	0
ST15C	400x240	0
ST25C	600x240	34
ST40C	600x240	4
ST50C	600x240	0
ST65C	600x240	5

ANGLE E1
Nombre: 1

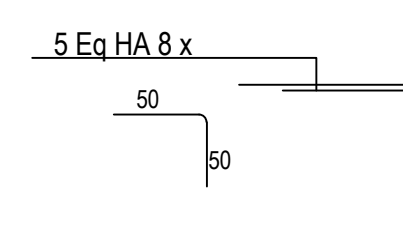

Les entreprises réalisant les travaux devront tenir compte des derniers plans architecturaux lors de la réalisation des travaux.
Les plans du MATTE doivent servir de référence pour la construction et doivent être sous peine d'annulation.

EX: 1er Lit. 2 panneaux
2ème Lit. 1/2-2+1/2 panneaux

EN TIRIOIR

NOAHO

Chemin de Fontanière - 69350 La Mulatière

Création de logements

Les entreprises réalisant les travaux devront tenir compte des derniers plans architecturaux lors de la réalisation des travaux.
Les plans du MATTE doivent servir de référence pour la construction et doivent être sous peine d'annulation.

ARCHITECTES: Atelier D1S
BET STRUCTURE: MATTE SAS
BET FLUIDES: PRELEM
ECONOMISTE: EXECO
BUREAU DE CONTROLE: Bureau VERITAS

MO DELEGUE: PSO Ingénierie
MOE: CSRS
CPC: ENTREPRISES: Fontanel-gbc

Bât: C Aile OUEST
PLANCHER SUR -1
ARMATURES DALLE INFERIEURE

DOE
Contrainte de sol: 8 bars ELS
Aciers HA (T) FyE500
Aciers Doux (D) FyE235
Aciers TS FyE500
Béton f28 >= 25MPa
Enrobage >= 3 cm

PLAN N° C23 0
DATE: 20/07/2015

MATTÉ
BUREAU D'ETUDES
STRUCTURES ET FLUIDES
119 BOULEVARD STALINGRAD 69100 VILLEURBANNE
Tél: 04 72 44 02 81 Fax: 04 72 44 25 59
E-mail: matt@matte.fr

Dessiné par: J.B.O.
Contrôlé par: P.LIN
Echelle: 1/150°

Affaire N° 13.12.119