


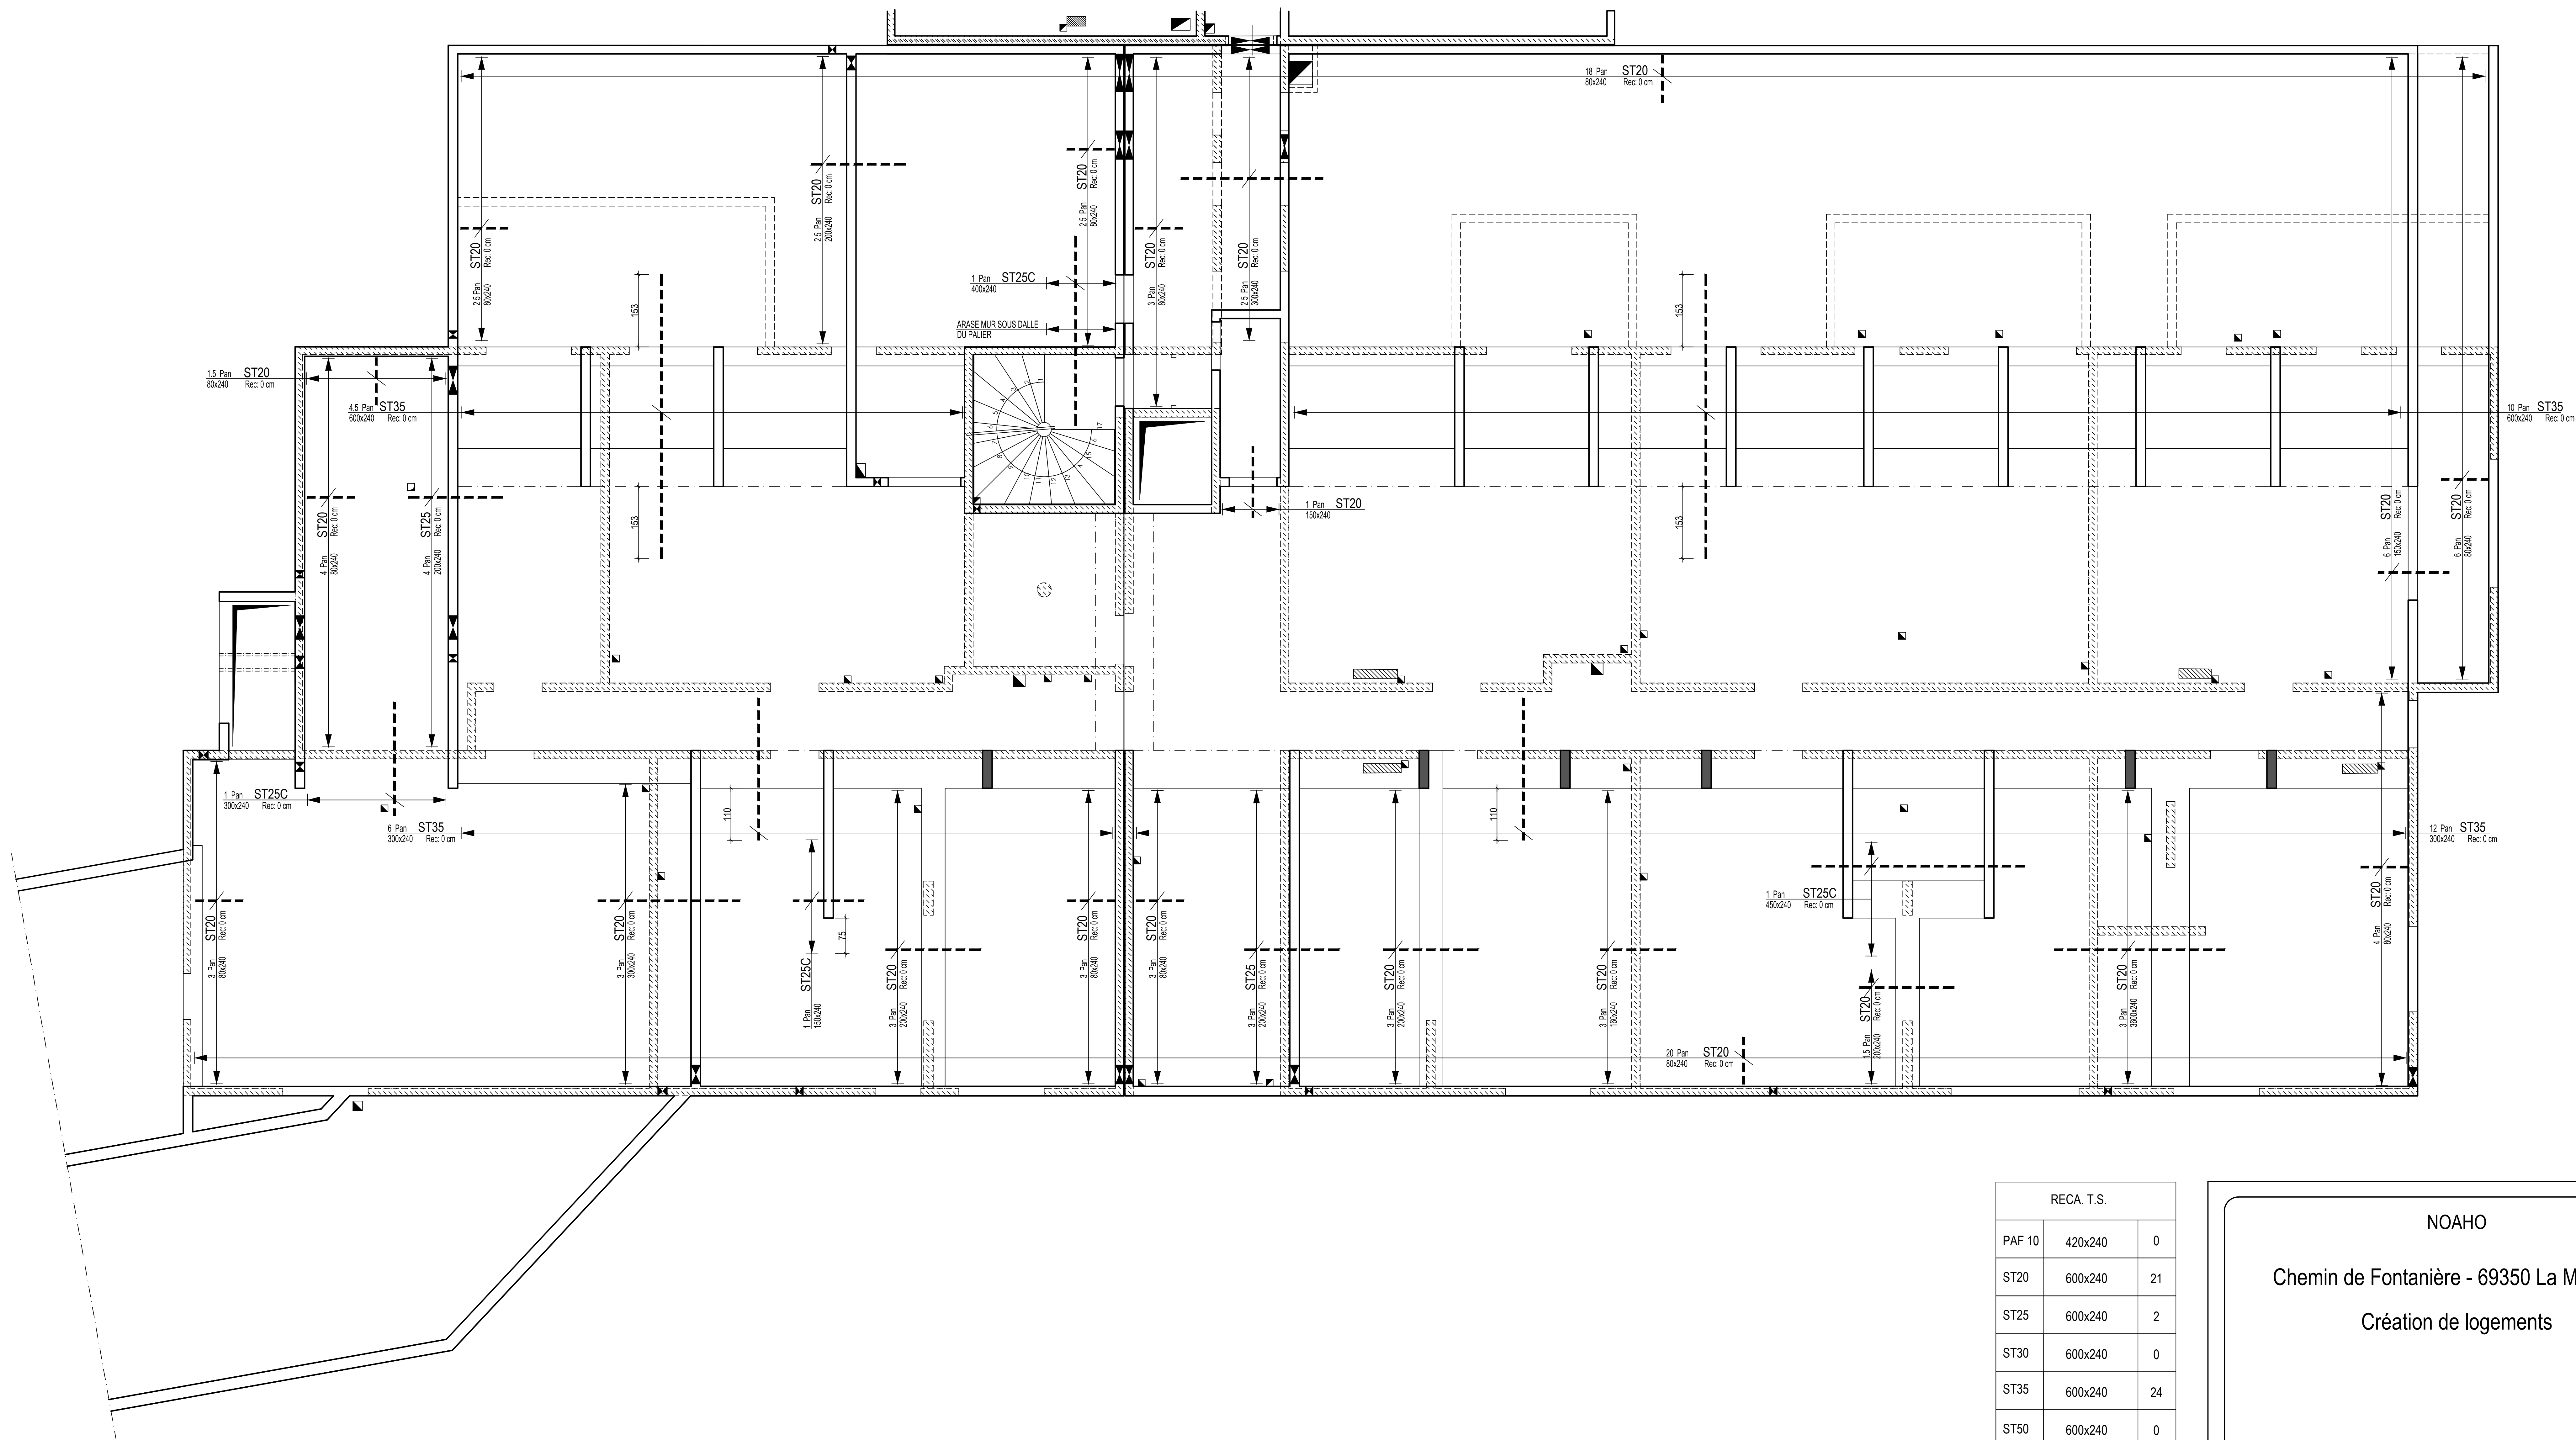

RECA. T.S.		
PAF 10	420x240	0
ST20	600x240	21
ST25	600x240	2
ST30	600x240	0
ST35	600x240	24
ST50	600x240	0
ST60	600x240	0
ST15C	400x240	0
ST25C	600x240	4
ST40C	600x240	0
ST50C	600x240	0
ST65C	600x240	0

NOAHO

Chemin de Fontanière - 69350 La Mulatière

Création de logements

Les entreprises réalisant les travaux devront tenir compte des derniers plans architectes lors de la réalisation des travaux.
Les plans du 30 MARS 2015 ne doivent servir qu'à titre consultatif et doivent être des plans d'exécution.

ARCHITECTES:Atelier D1S

BET STRUCTURE:MATTE SAS

BET FLUIDES:PRELEM

ECONOMISTE:EXECO

BUREAU DE CONTROLE:Bureau VERITAS

MO. DELEGUE:PSO Ingénierie

MOE:CSPS

ENTREPRISES:Fontanel-gbc

Bât: C Aile OUEST

PLANCHER SUR -1

ARMATURES DALE SUPERIEURE

DOE

Contrainte de sol: 8 bars ELS

Aciers HA (T) FdE500

Aciers Doux (O) FdE235

Aciers TS FdE500

Béton f28 >= 25MPa

Enrobage = 3 cm

PLAN N° C24_0

DATE: 20/07/2015

MATTÉ

BUREAU D'ETUDES

STRUCTURES ET FLUIDES

119 BOULEVARD STALINGRAD 69100 VILLEURBANNE

Tel: 04 72 44 12 81 Fax: 04 72 44 25 59

E-mail: s.legrenier@matte.fr

Dessiné par: J.BO

Contrôlé par: P.LIN

Echelle: 1/50'

Affaire N° 13.12.119