




COUPE A
Ech: 1/25

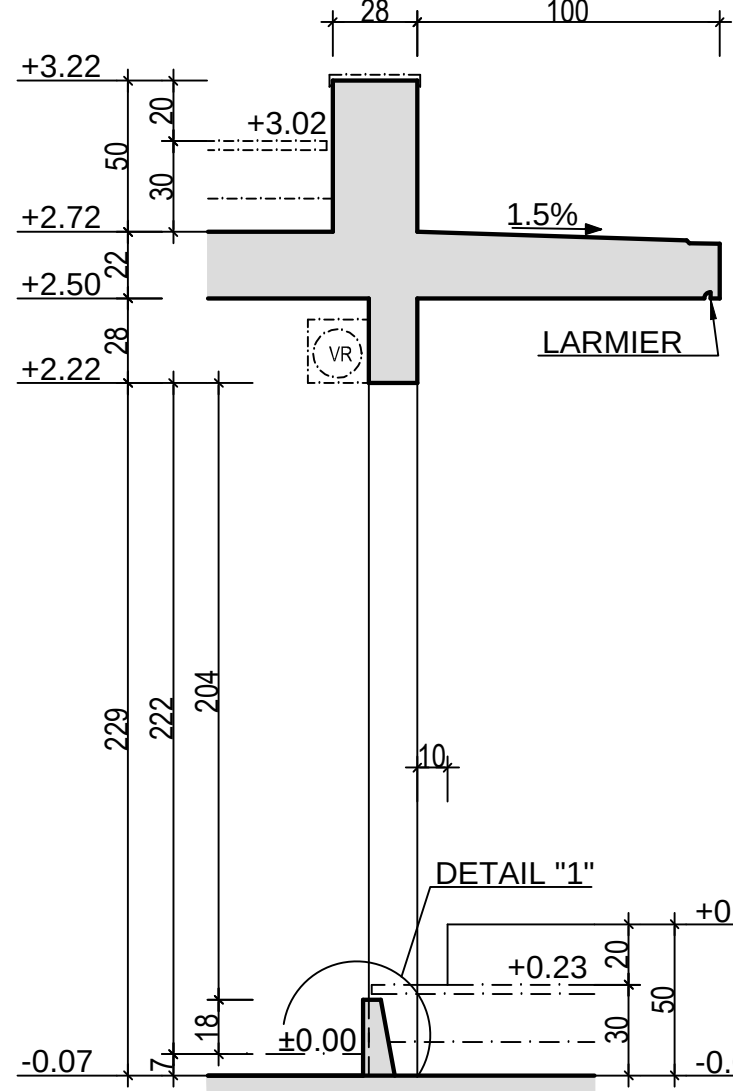


COUPE B
Ech: 1/25

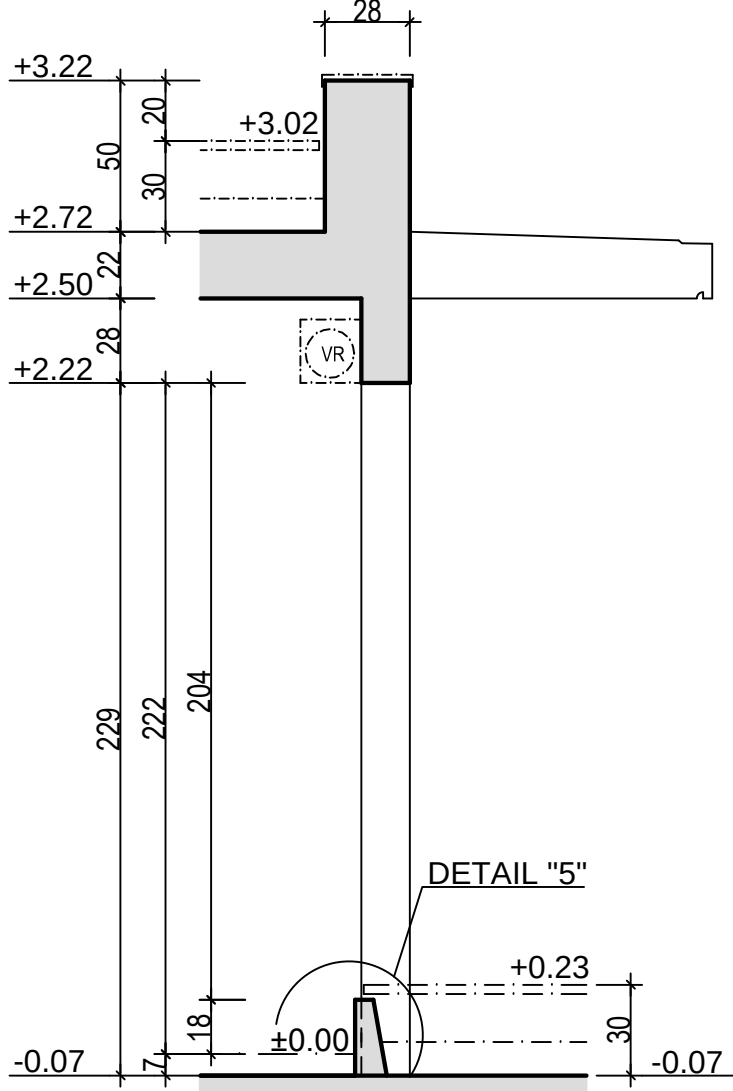


COUPE C
Ech: 1/25

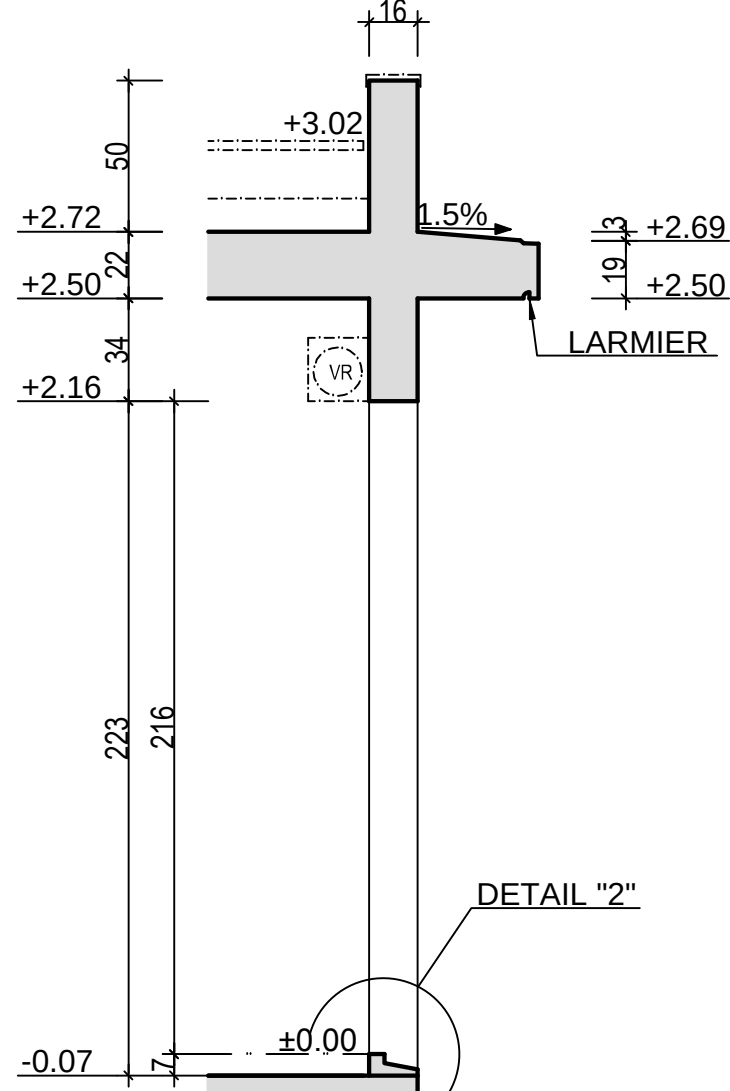


COUPE D
Ech: 1/25

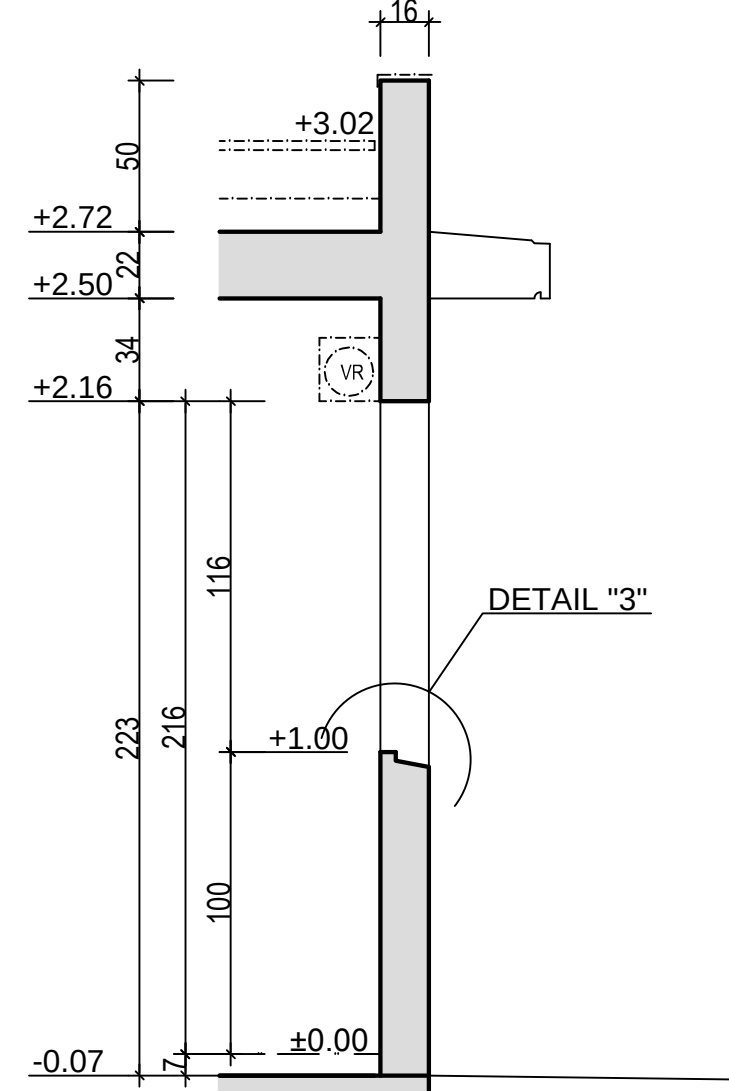


COUPE E
Ech: 1/25

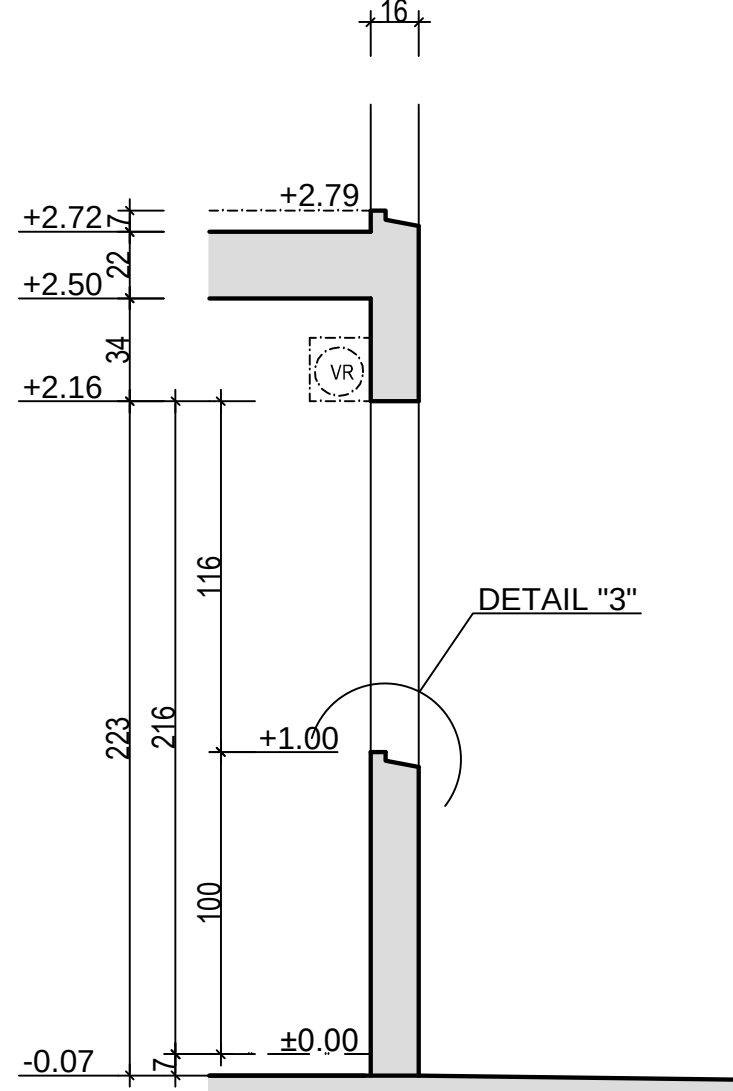


COUPE F
Ech: 1/25

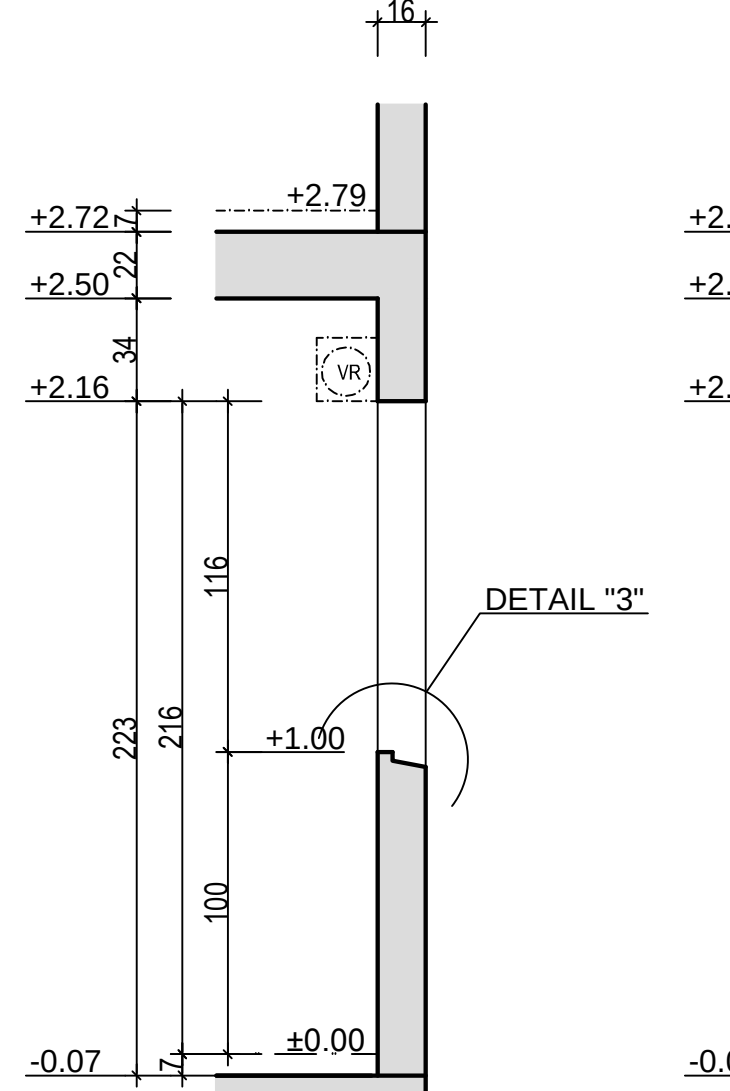


COUPE G
Ech: 1/25

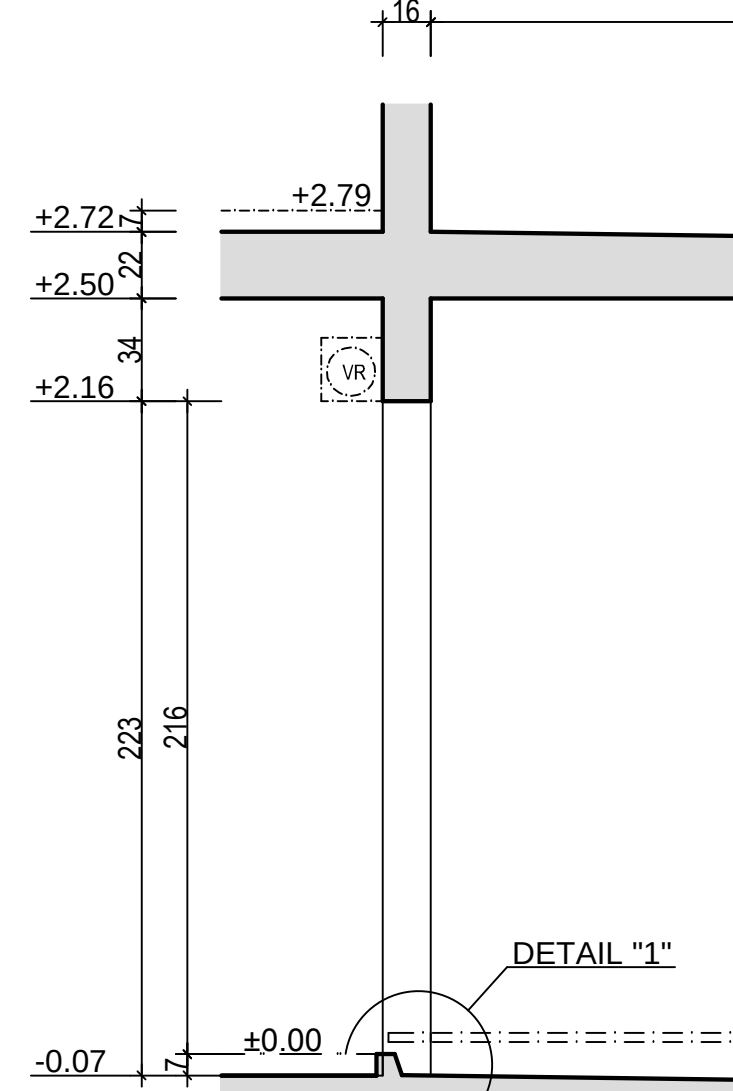


COUPE H
Ech: 1/25

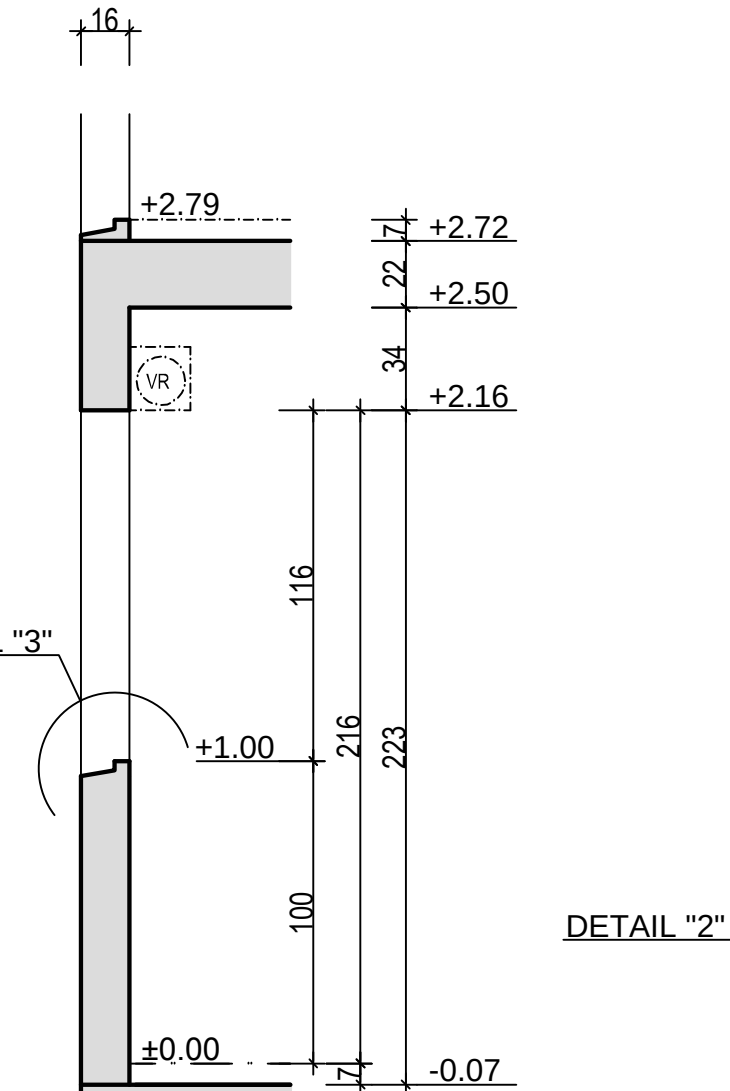


COUPE J
Ech: 1/25

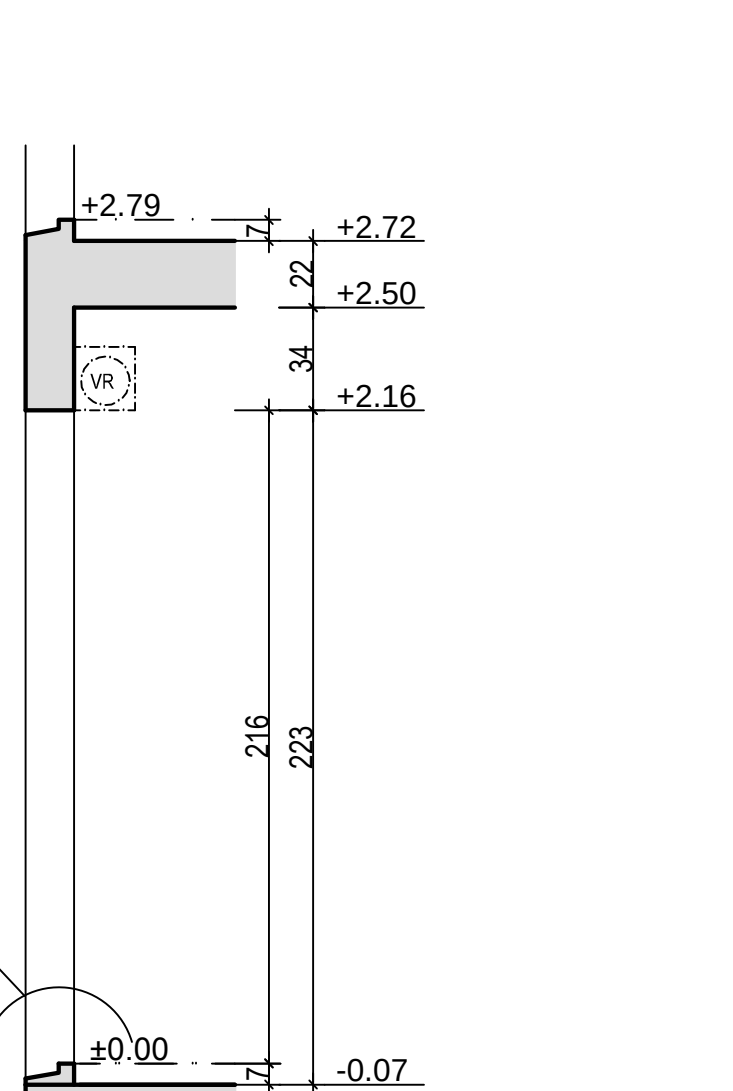


VUE EN PLAN
Ech: 1/50

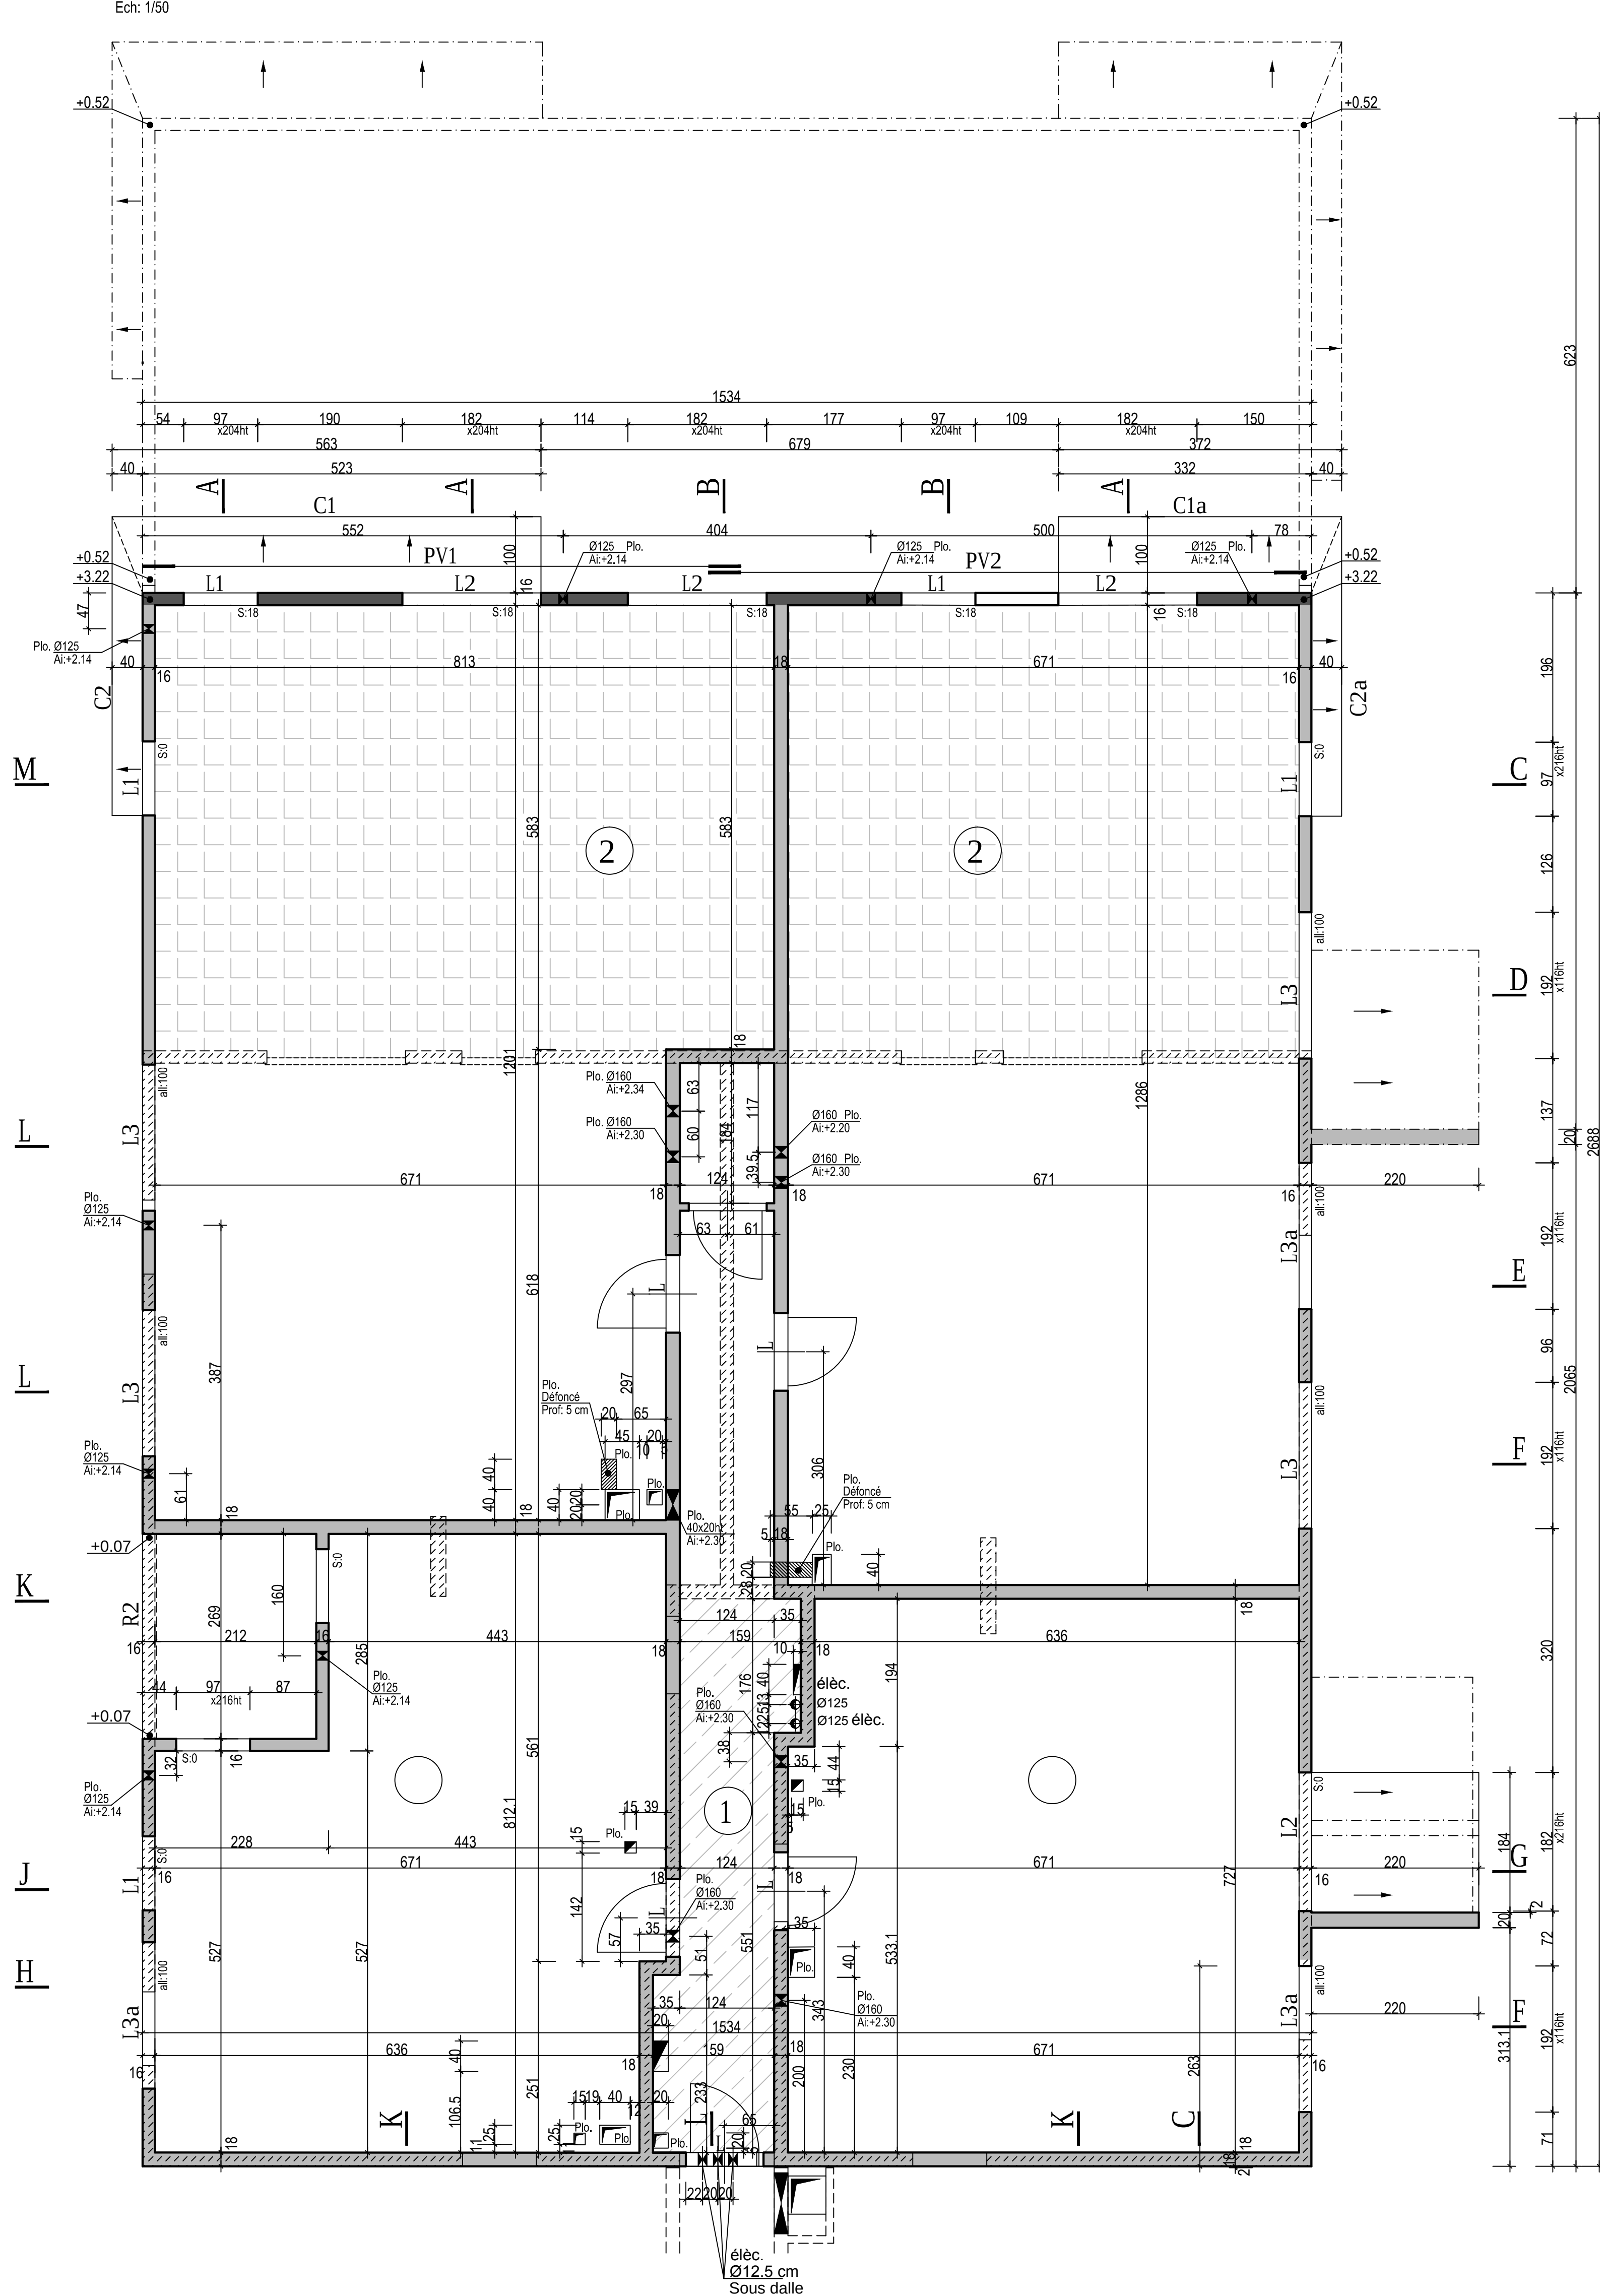


COUPE K
Ech: 1/25

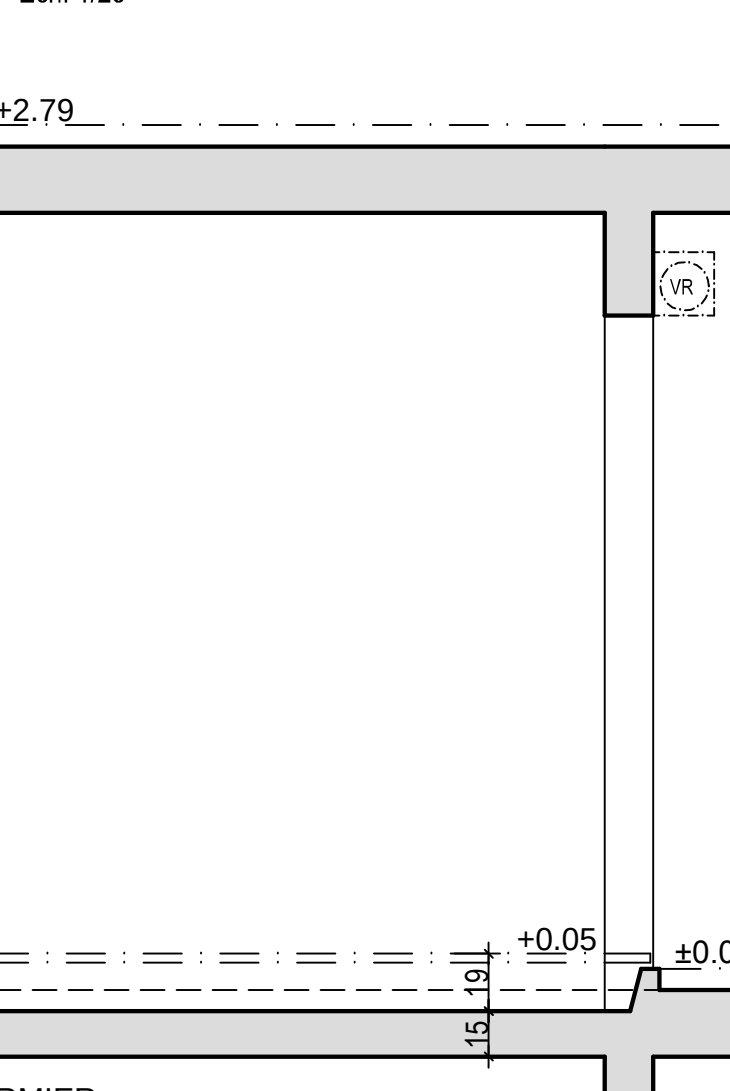


COUPE L
Ech: 1/25

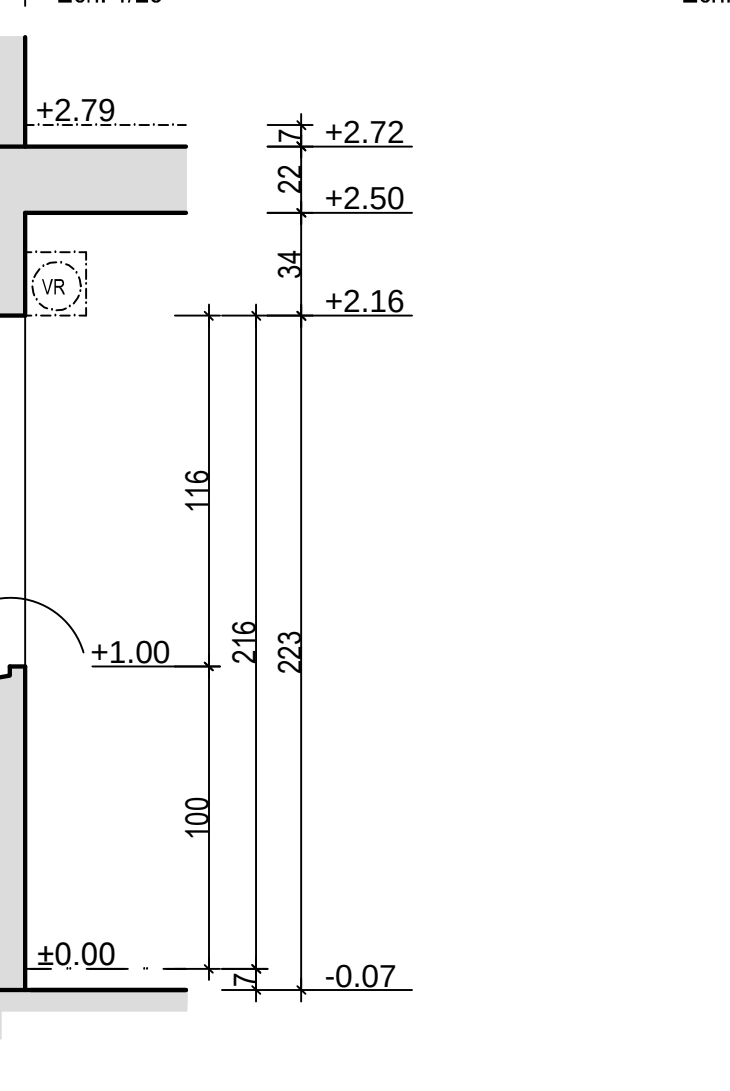


COUPE M
Ech: 1/25

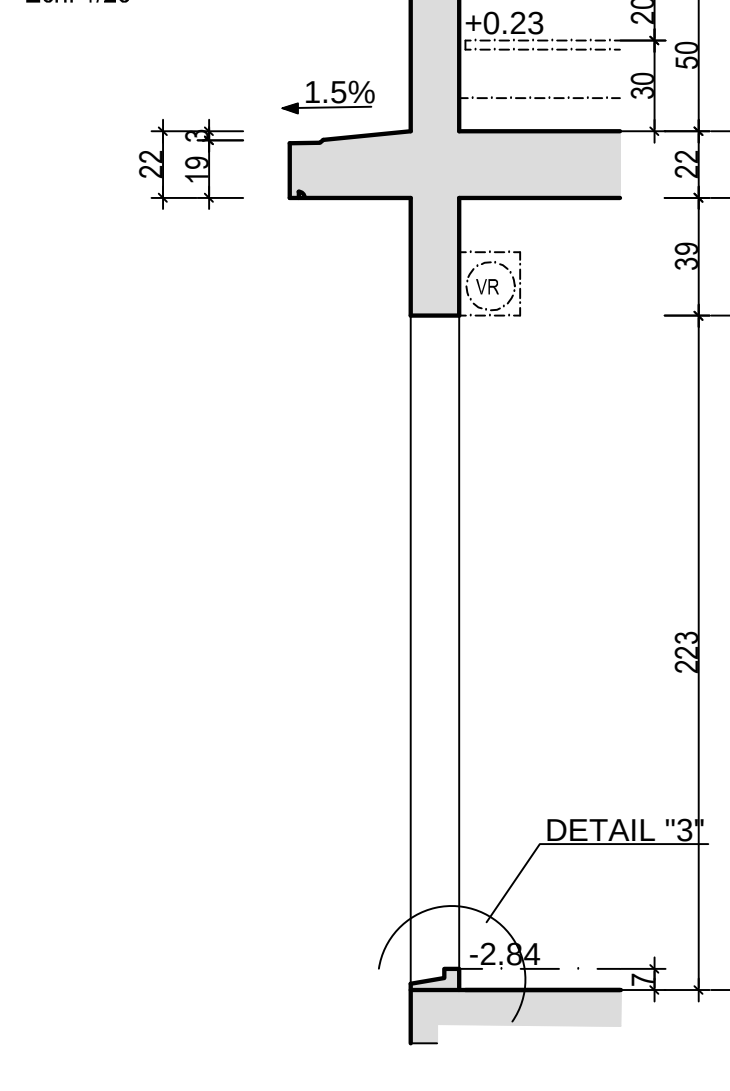


DETAIL "1"

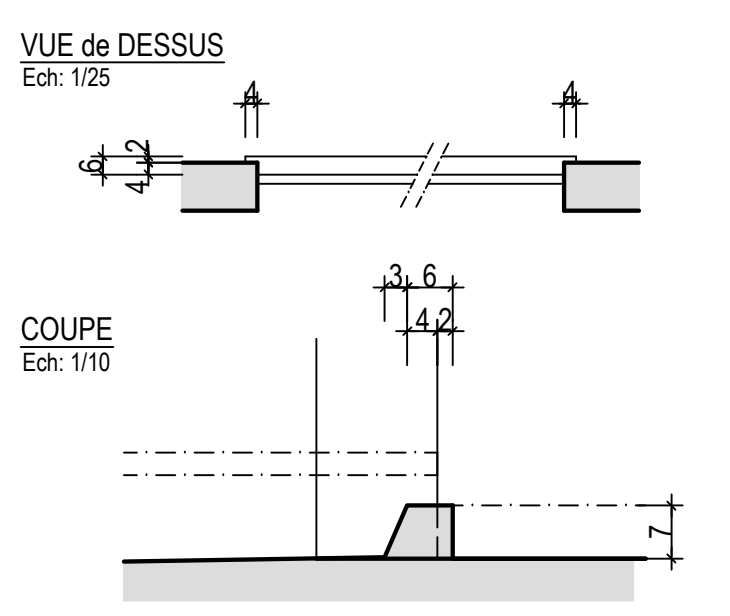


DETAIL "2"

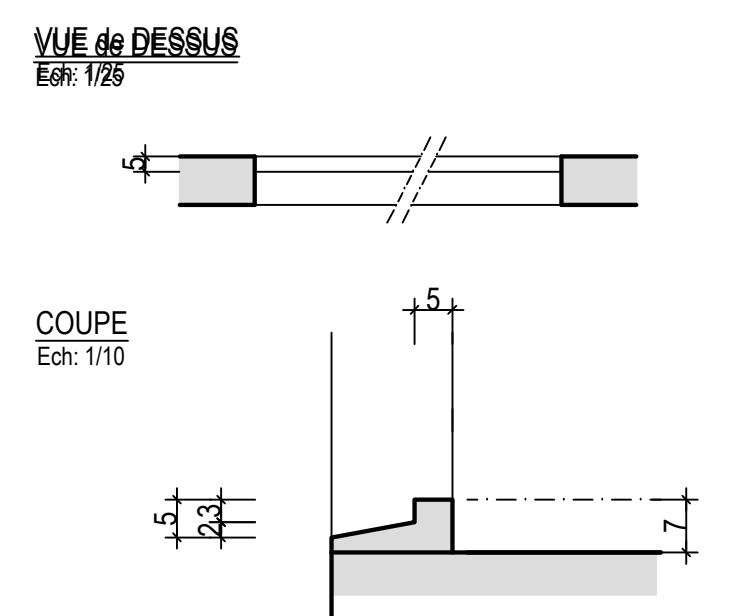

DETAIL "3"

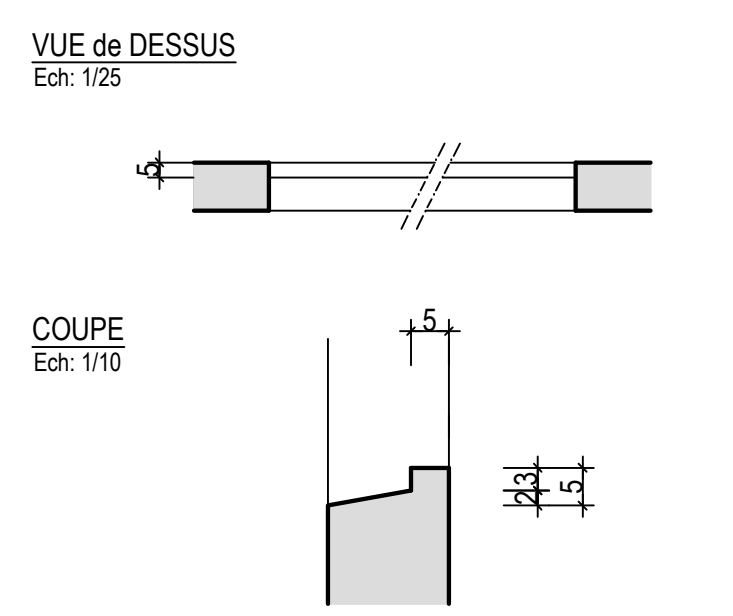

DETAIL "5"

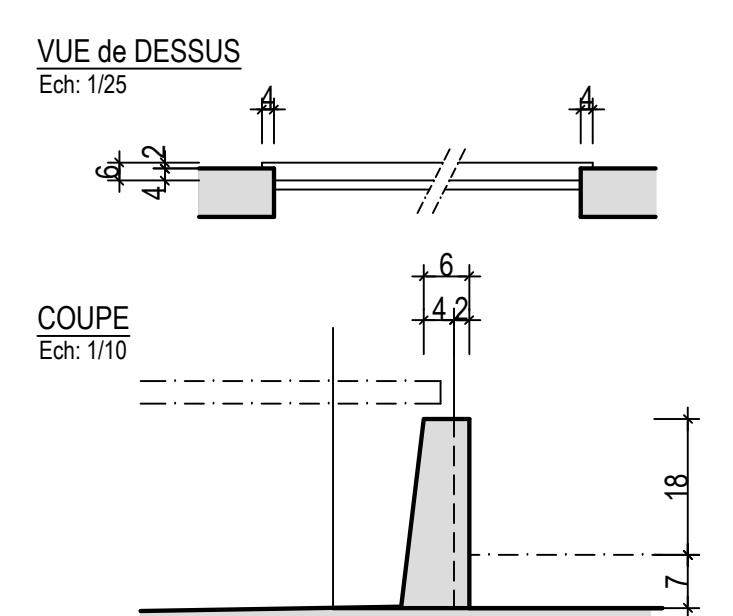

DALLES

FINI: +2.79=207.24
DALLE BA Epr: 22 cm
DESSUS BRUT: +2.72
RESERVE: 7 cm

1 FINI: +2.79=207.24
DALLE BA Epr: 25 cm
DESSUS BRUT: +2.72
RESERVE: 7 cm

2 FINI: +3.02=207.47
DALLE BA Epr: 22 cm
DESSUS BRUT: +2.72
RESERVE: 30 cm

±0.00 = 204.45 = NIVEAU FINI du REZ de CHAUSSEE Bât: C

NOAHO

Chemin de Fontanière - 69350 La Mulatière

Création de logements

Les entreprises réalisant les travaux devront tenir compte des derniers plans architecturaux lors de la réalisation des travaux.
Les plans du MATTE ne doivent pas être utilisés pour la construction et doivent être des plans d'exécution.

ARCHITECTES: Atelier D1S
BET STRUCTURE: MATTE SAS
BET FLUIDES: PRELEM
ECONOMISTE: EXECO
BUREAU DE CONTROLE: Bureau VERITAS

MO DELEGUE: PSO Ingénierie
SUD EST COORDINATION
ENTREPRISES: Fontanel-gbc

Bât: C Aile EST
PLANCHER SUR REZ
Coffrage

DOE

Contrainte de sol: 8 bars ELS
Aciers HA (T) FeE500
Aciers Dux (D) FeE235
Aciers TS FeE500
Béton f28 >= 25MPa
Enrobage: 3 cm

PLAN N° C25_0
DATE: 03-07-2015

MATTÉ
BUREAU D'ETUDES
STRUCTURES ET FLUIDES
119 BOULEVARD STALINGRAD 69100 VILLEURBANNE
Tel: 04 72 44 12 87 Fax: 04 72 44 25 59
Email: matt@matte.fr

Dessiné par: J.B.O.
Contrôle par: P.LIN
Echelle: 1/50

Affaire N° 13.12.119