

Chemin de Fontanière - 69350 La Mulatière

Création de logements

Les entreprises réalisant les travaux devront tenir compte des derniers plans architecte lors de la réalisation des travaux
Les plans du be MATTE ne doivent servir qu'au corps d'état concerné et doivent être des plans d'exécution.

ARCHITECTE(S): Atelier D'IS
BET STRUCTURE: MATTE SAS
BET FLUIDES: PRELEM
ECONOMISTE: EXECO
BUREAU DE CONTROLE: Bureau VERITAS

MO DELEGUE:
MOE: PSO Ingénierie
CSPS: SUD EST COORDINATION
OPC:
ENTREPRISE(S): Fontanel-pbc

Bât: C Aile EST
BA au REZ

DOE

Contrainte de sol: 8 bars ELS

Aciers HA (T) FeE500

Aciers Doux (Ø) FeE 235

Aciers TS FeE 500

Béton fc28 >= 25MPa

Enrobage = 3 cm

PLAN N°
C26 A

DATE : 02-10-2015

MATTÉ
BUREAU D'ÉTUDES
STRUCTURES ET FLUIDES

119 BOULEVARD STALINGRAD 69100 VILLEURBANNE

Tél. 04 72 44 02 87 Fax 04 72 44 26 59

E-mail : bet@matte.fr

Dessiné par : J.BO

Contrôlé par : P.LIN



Echelle : 1/50°

Affaire N°
13.12.119

MURS EXTERIEURS

ANGLES MURS

ARMATURES TETES DE MURS
et OUVERTURES

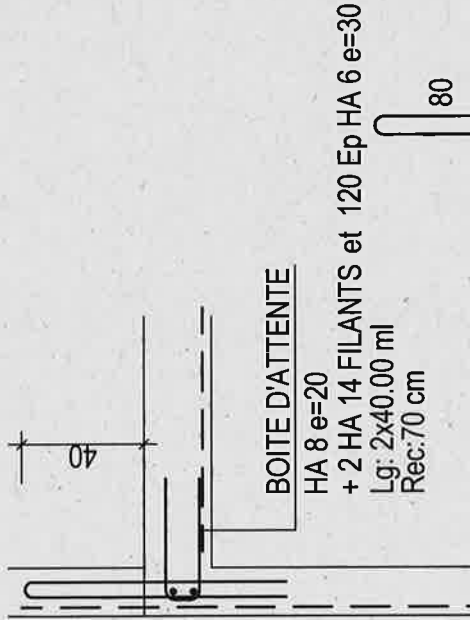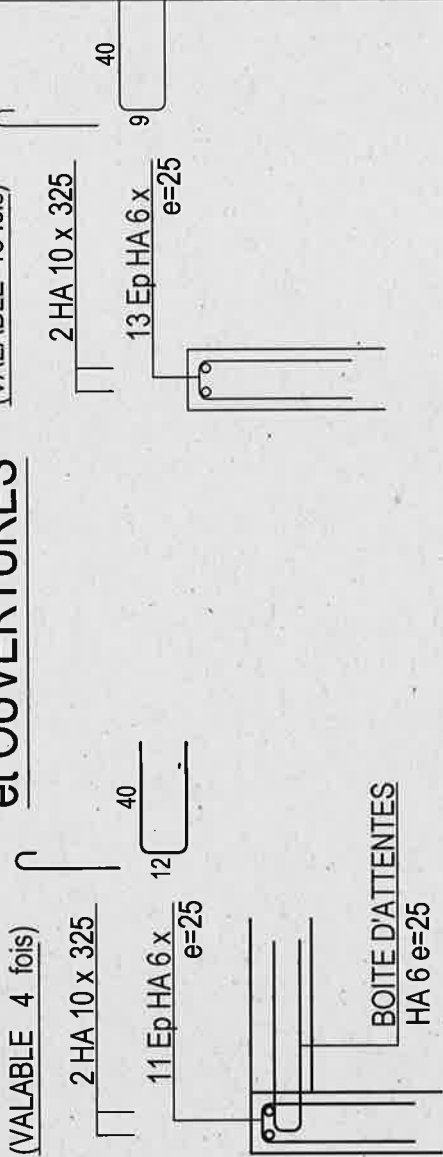

EXT.

Pan PAF V VERTICAUX


Rec: 40 cm

Nombre: 45

ARMATURES REJINGOT

(VALABLE 5 fois)

A COUPER SUIVANT OUVERTURES

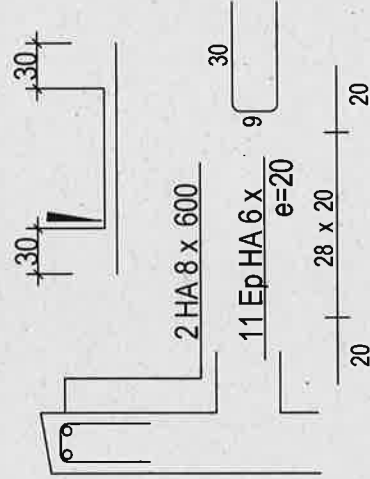

BOITE D'ATTENTES

HA 6 e=25
+ 2 HA 10 x 325


MURS M1

30.00 ml Env.

AVEC CASQUETTES R1

Nombre: 2

SANS CASQUETTES

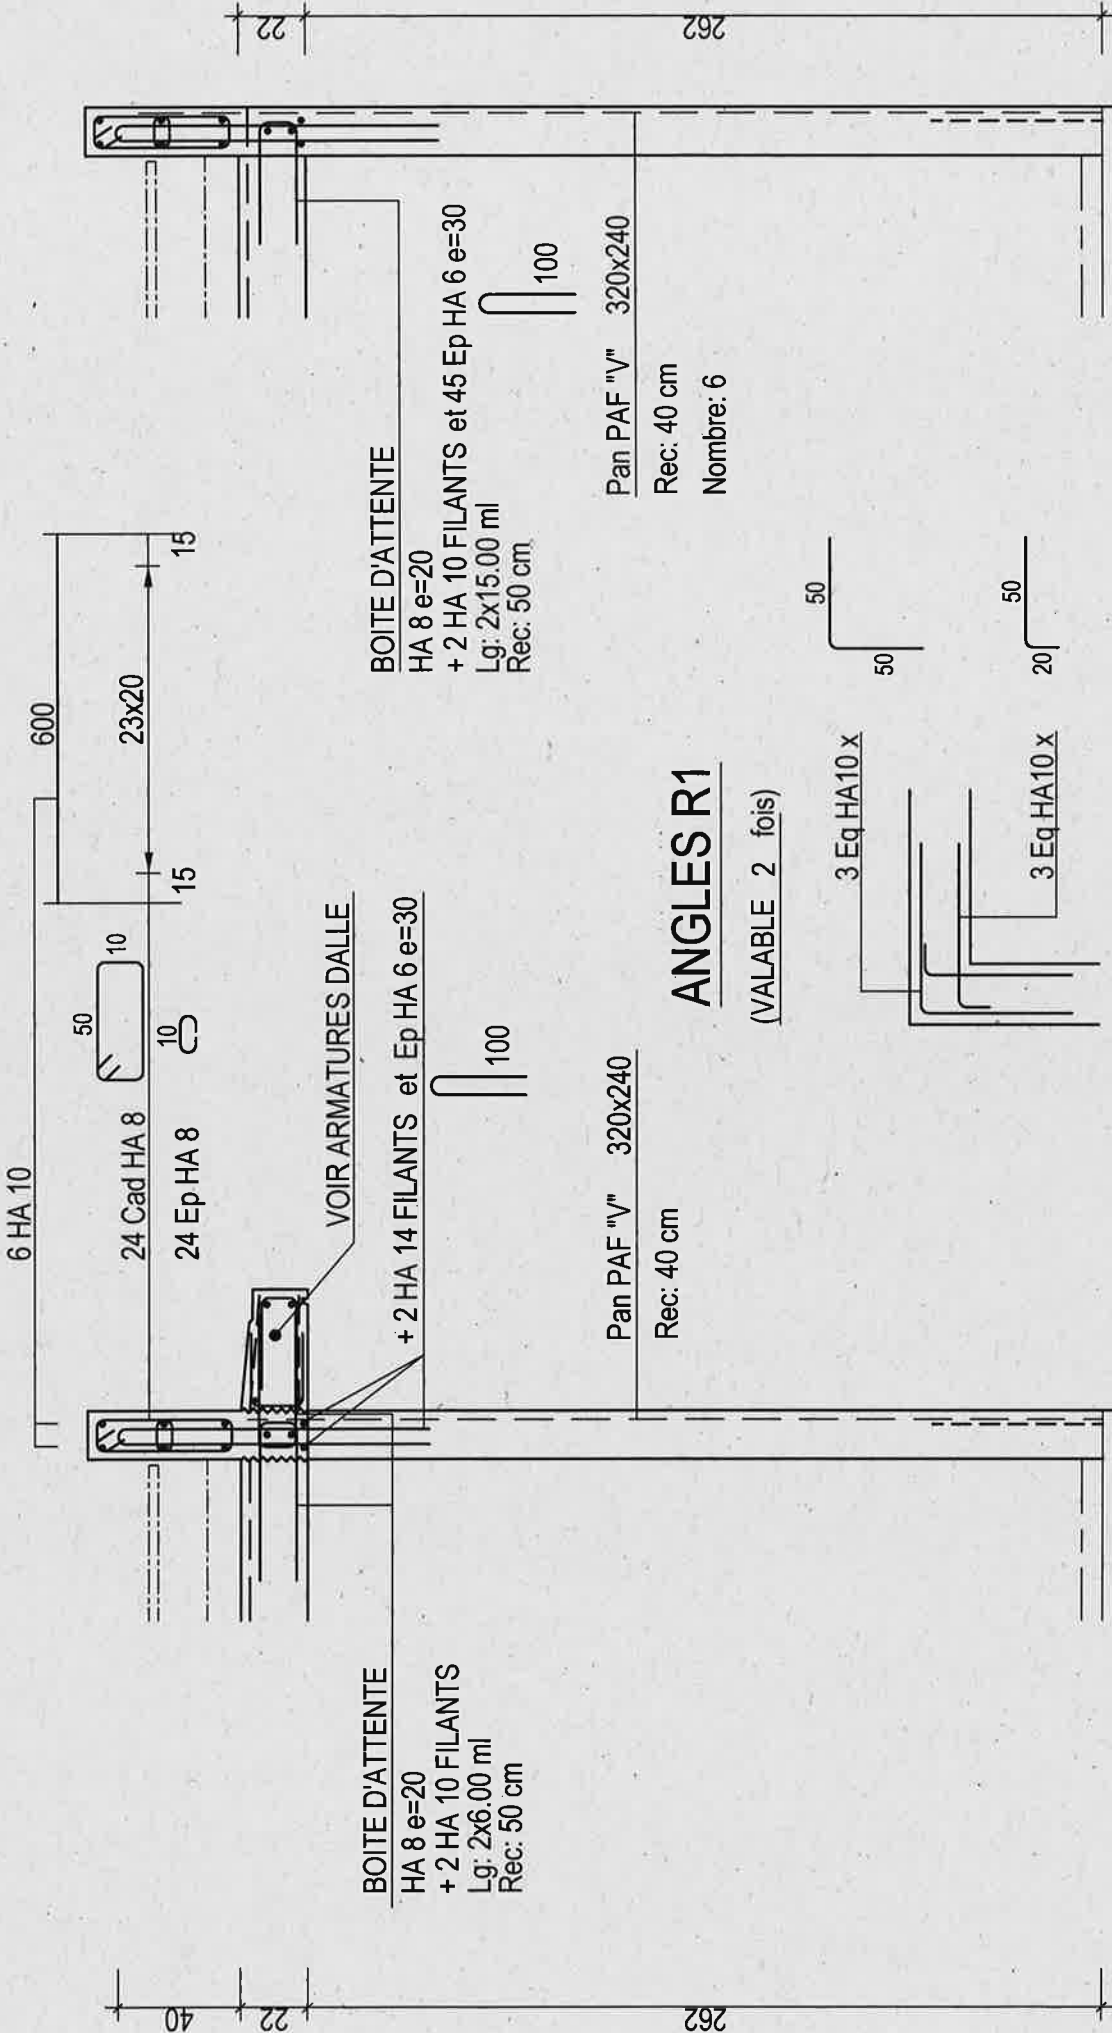

MURS PV1

AVEC CASQUETTES

SANS CASQUETTES

ELEMENT MONTE PV1
Voir page n° 4

ELEMENT MONTE PV1
Voir page n° 4

VOIR ARMATURES DALLE

BOITE D'ATTENTE
HA 8 e=20
+ 2 HA 10 FILANTS
Lg: 2x8.00 ml
Rec: 50 cm

ANGLES PV1
(VALABLE 1 fois)

BOITE D'ATTENTE
HA 8 e=20
+ 2 HA 10 FILANTS
Lg: 2x9.00 ml
Rec: 50 cm

CHAQUE FACE


Pan ST20 A COUPER
Rec: 40 cm

CHAQUE FACE

Pan ST20 A COUPER
Rec: 40 cm
Nombre: 2x4

(VALABLE 1 fois)


BOITE D'ATTENTES
HA 6 e=25
+ 2 HA 10 x 325

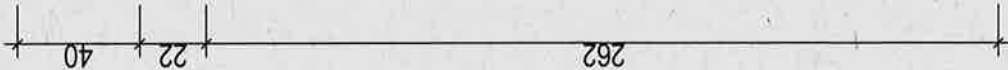



MURS PV2

AVEC CASQUETTES

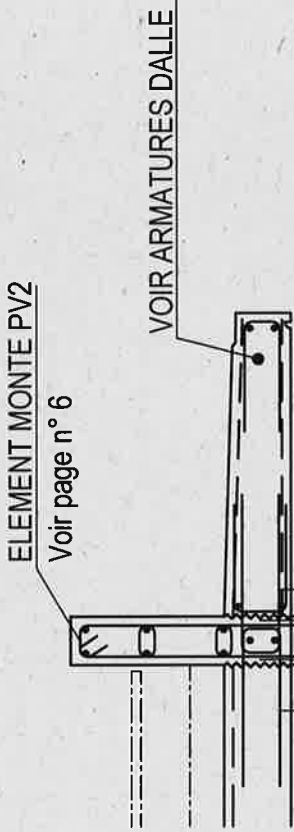

BOITE D'ATTENTE
HA 8 e=20
+ 2 HA 10 FILANTS
Lg: 2x8.00 ml
Rec: 50 cm

CHAQUE FACE

Pan ST20 A COUPER

Rec: 40 cm

ANGLES PV2

(VALABLE 1 fois)

5 Eq HA10 x


2X5 Eq HA10 x 20

50

50

50

SANS CASQUETTES

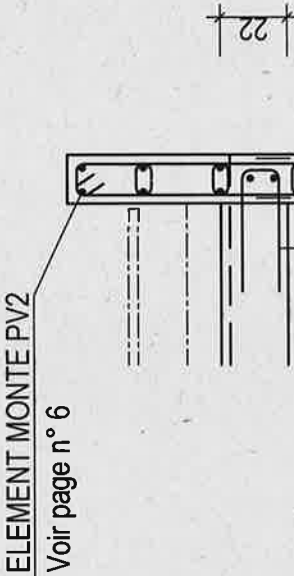

BOITE D'ATTENTE
HA 8 e=20
+ 2 HA 10 FILANTS
Lg: 2x9.00 ml
Rec: 50 cm

CHAQUE FACE

Pan ST20 A COUPER



Rec: 40 cm

Nombre: 2x4

- Date 06/07/15 - 10 étages -

Section : 16 x 100ht

f_{ck} = 25 MPa f_{yk} = 500 MPa Classe de ductilité B

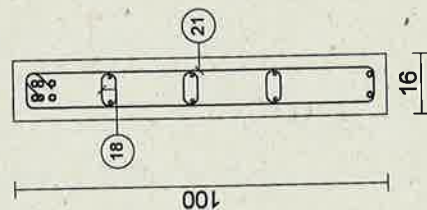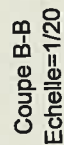[illegible]


180°
Back

920


9

MB1


1 Pièce

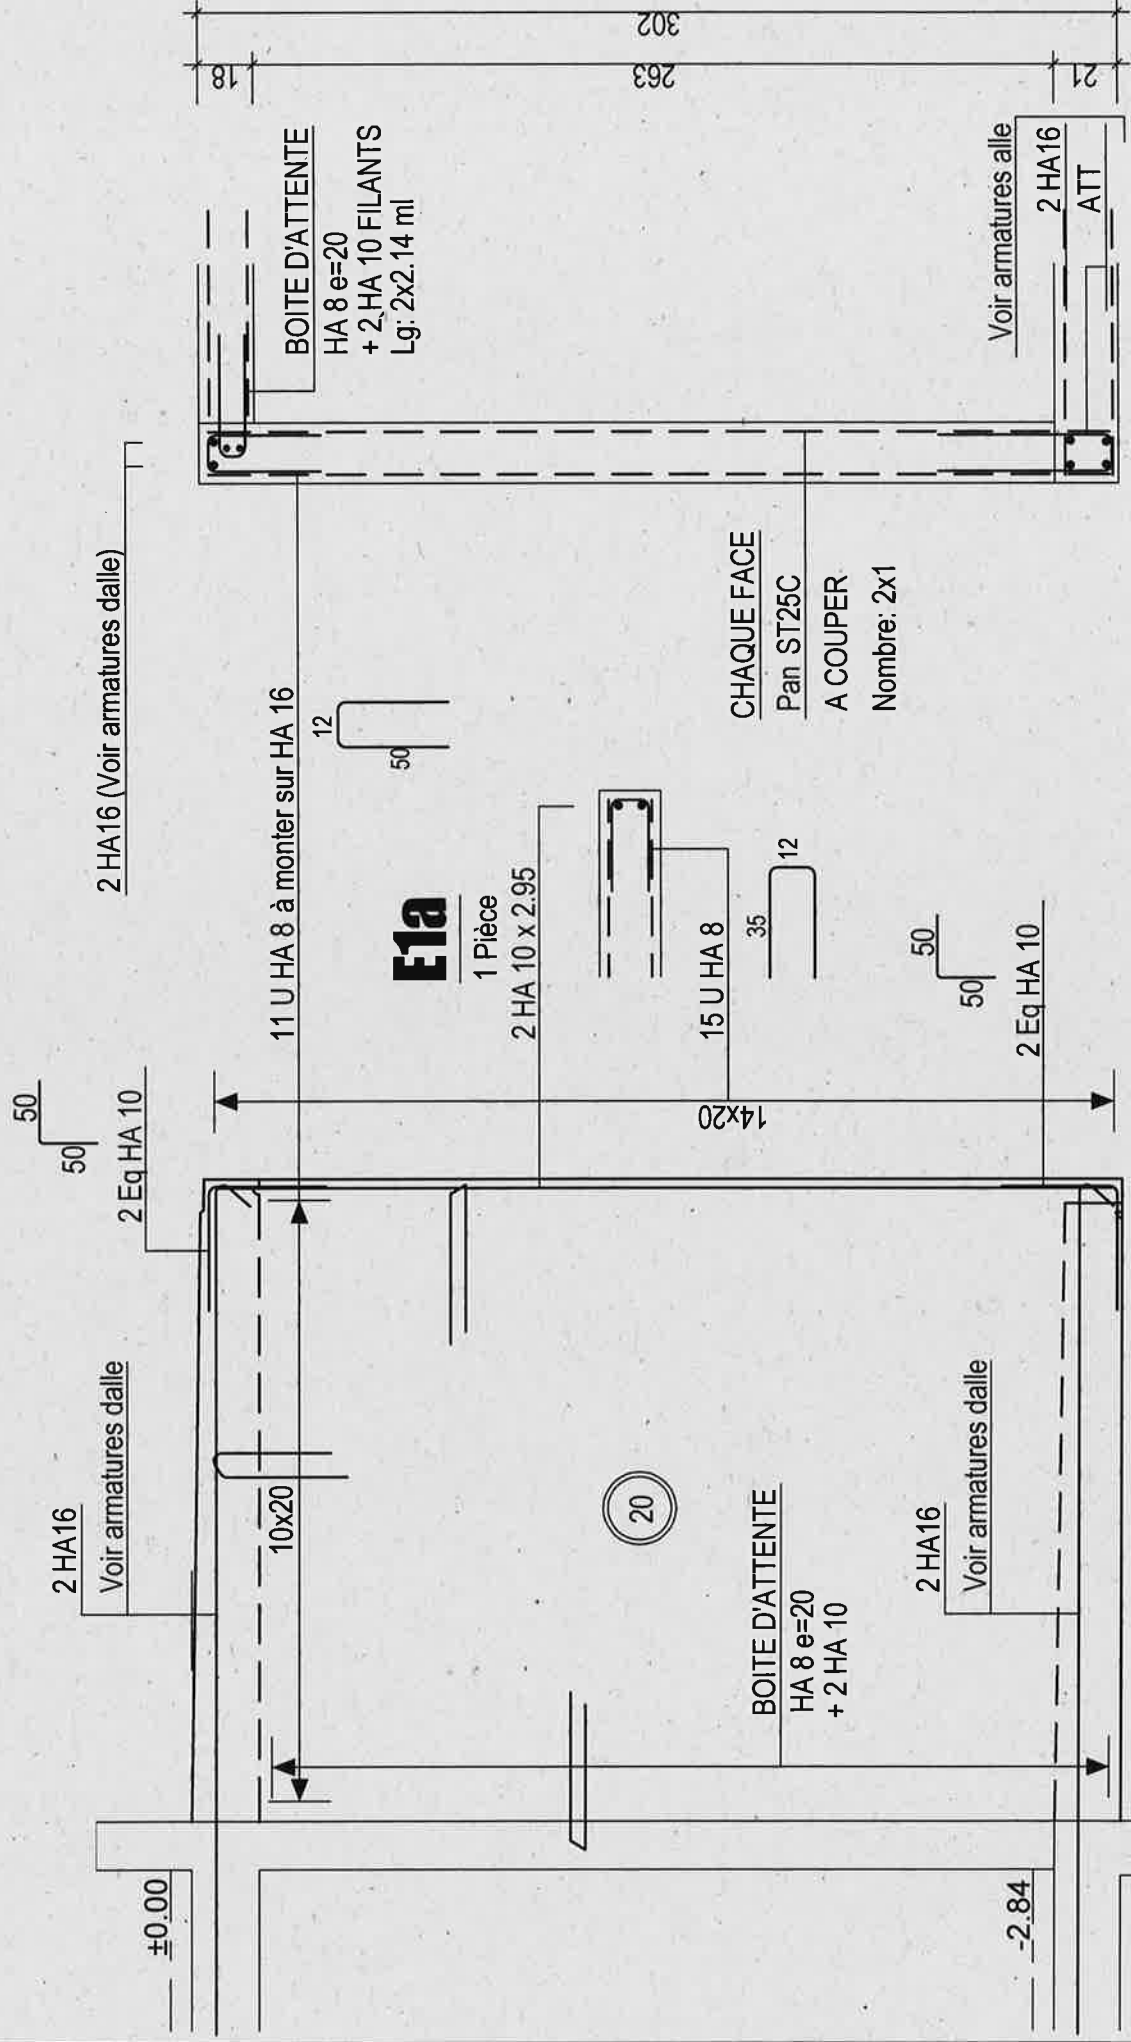


MURS INTERIEURS AVEC CONTINUITE

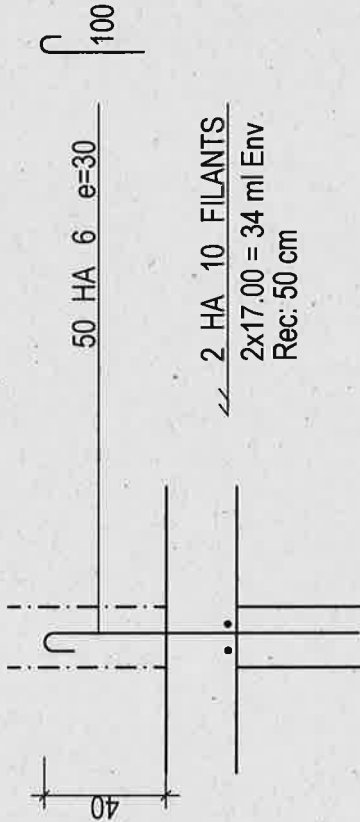

ANGLES MURS

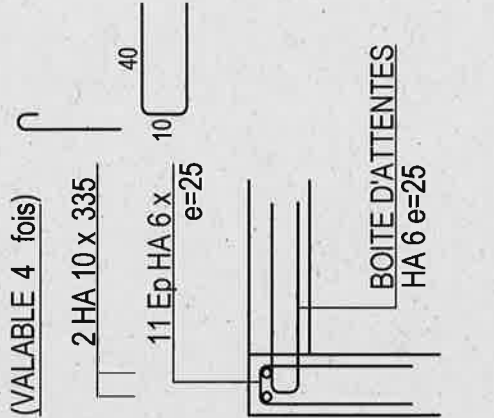



MURS INTERIEURS SANS CONTINUITE

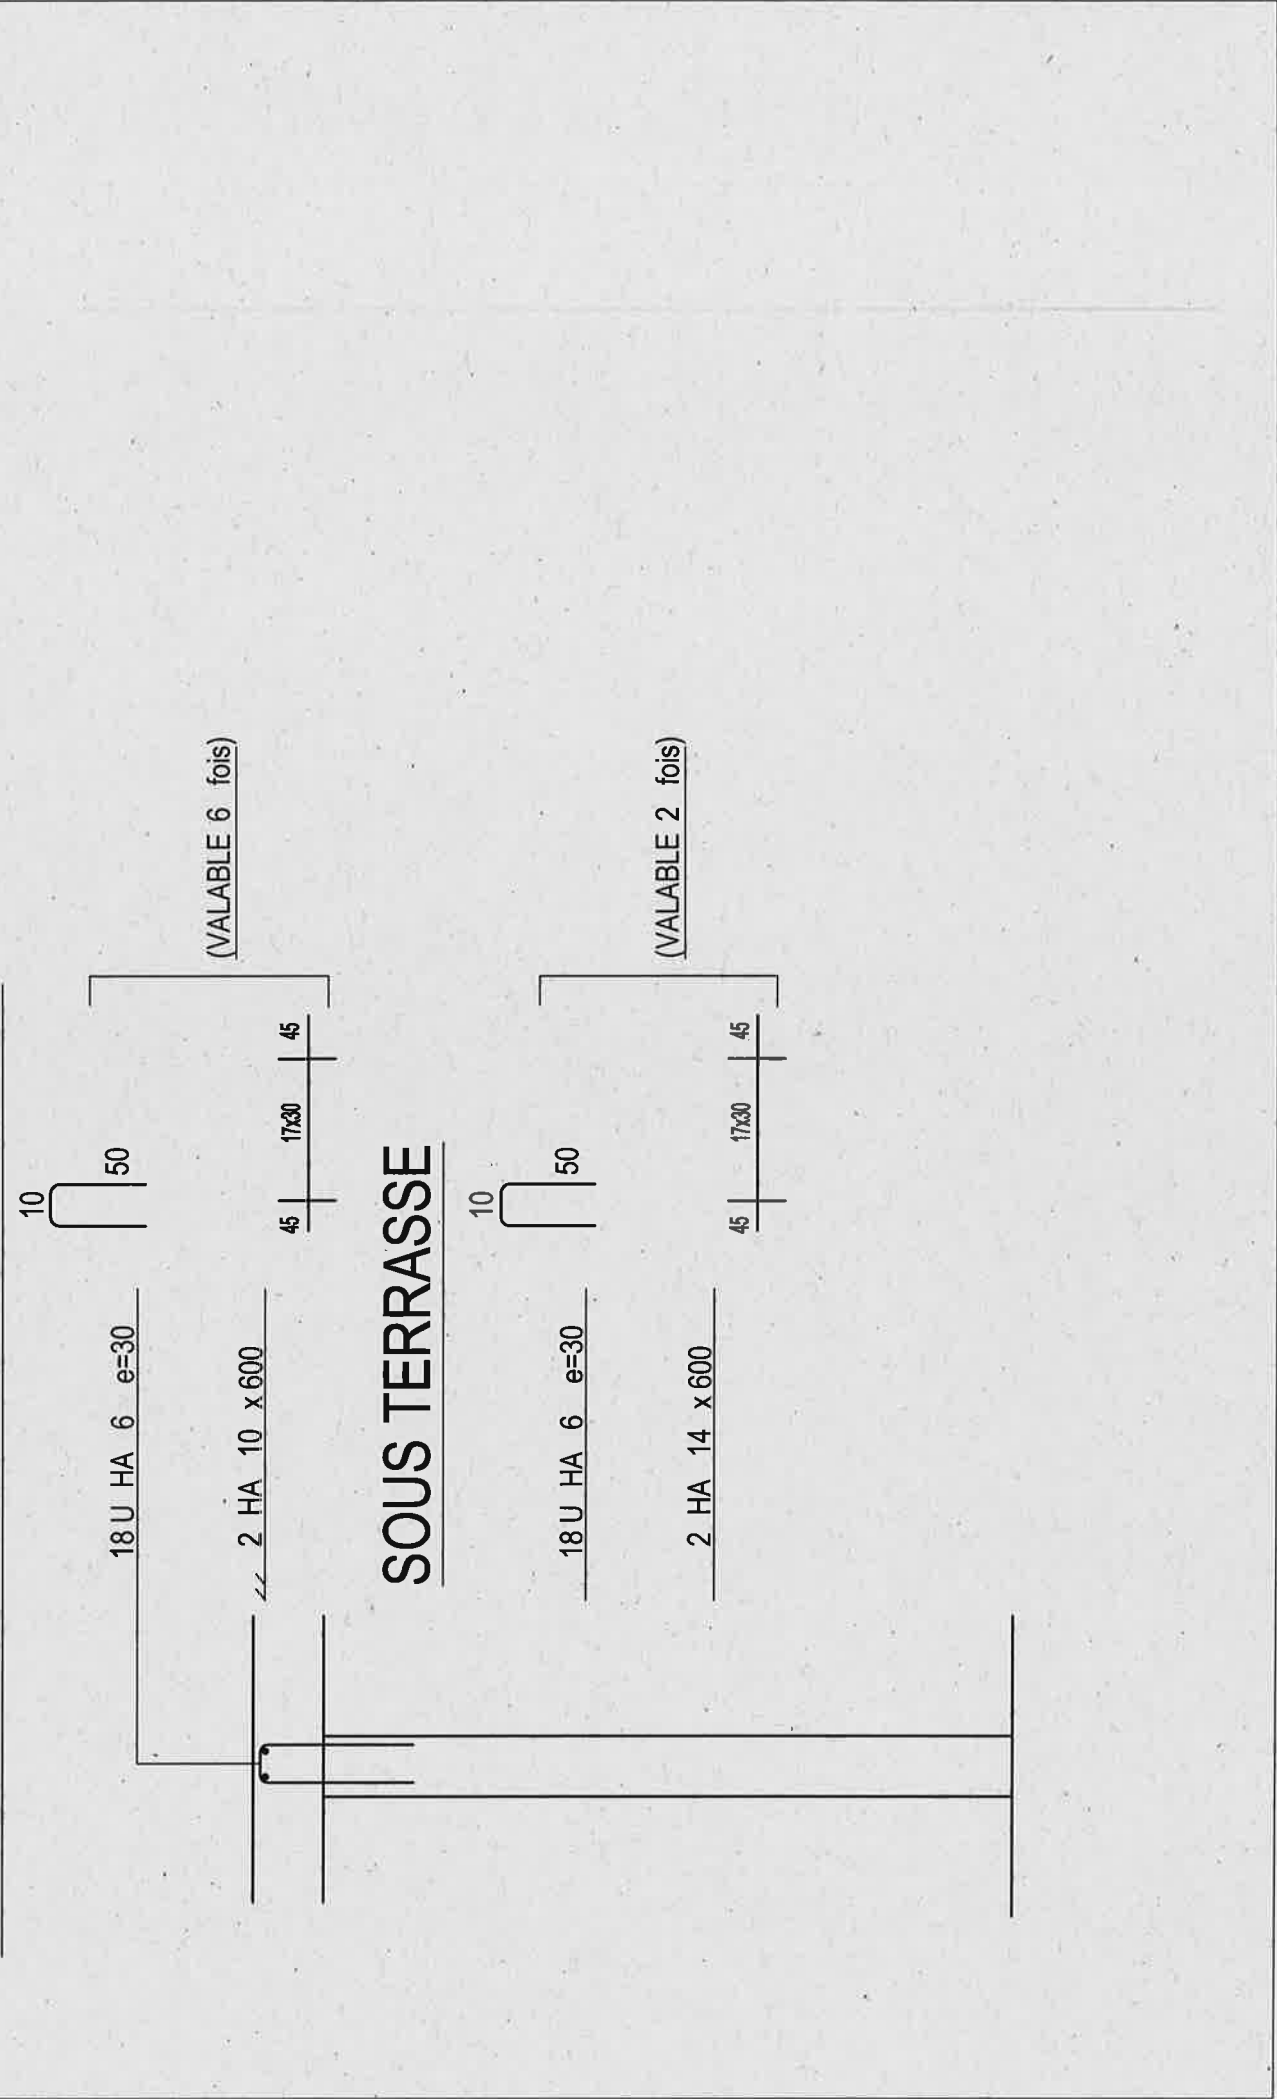

LINTEAUX EXT.

L
Nombre: 4

L3a
Nombre: 1
PORTEE: 192


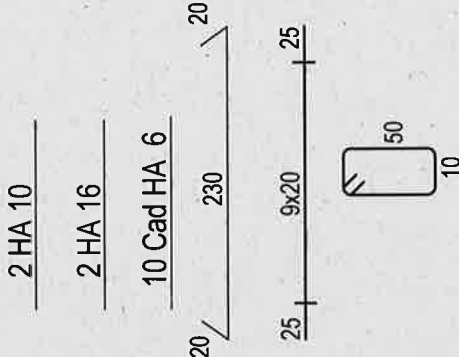
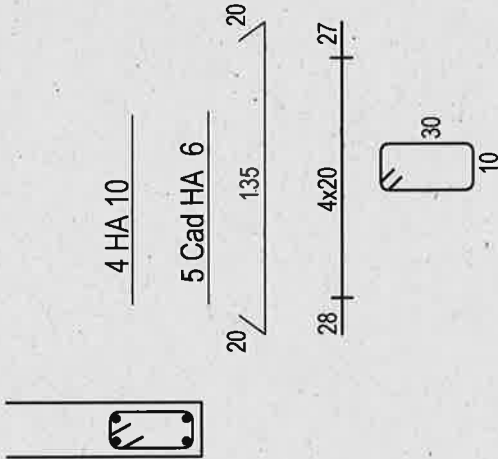


LINTEAUX EXT.

L1
Nombre: 5
PORTEE: 97

L2
Nombre: 1
PORTEE: 182


L3
Nombre: 4
PORTEE: 192

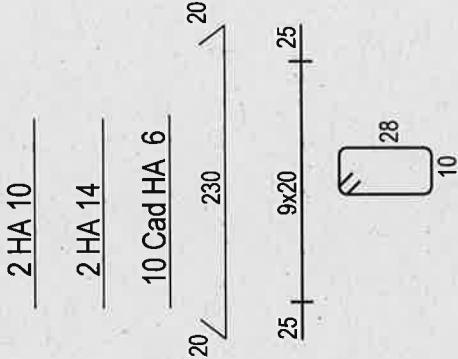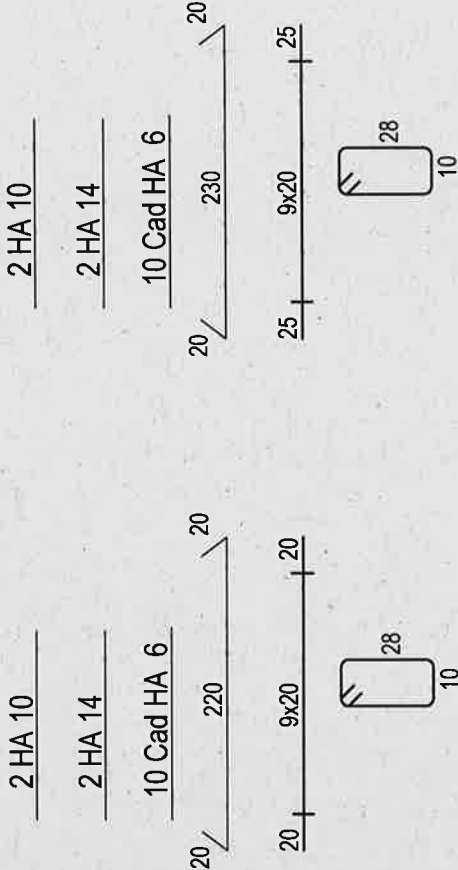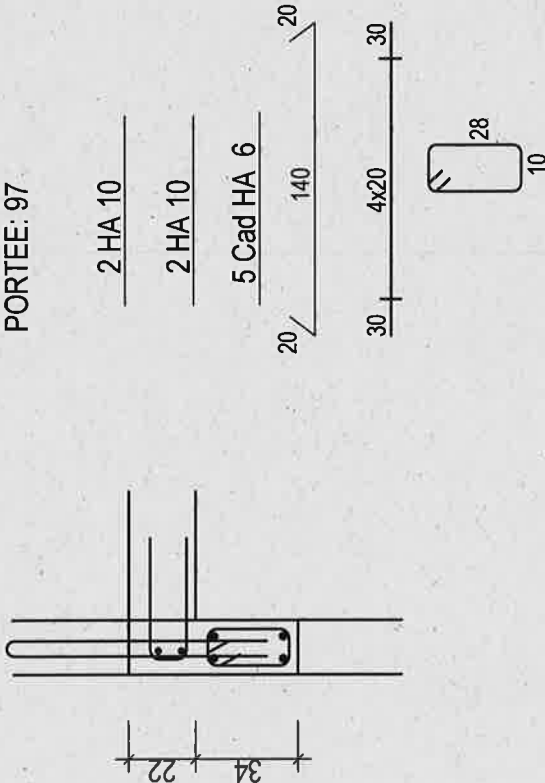

DETAIL DES PERFO A LA PLACE DES BOITE D'ATTENTES DES CASQUETTES

Coupe avec boîtes d'attentes

Coupe avec perfo

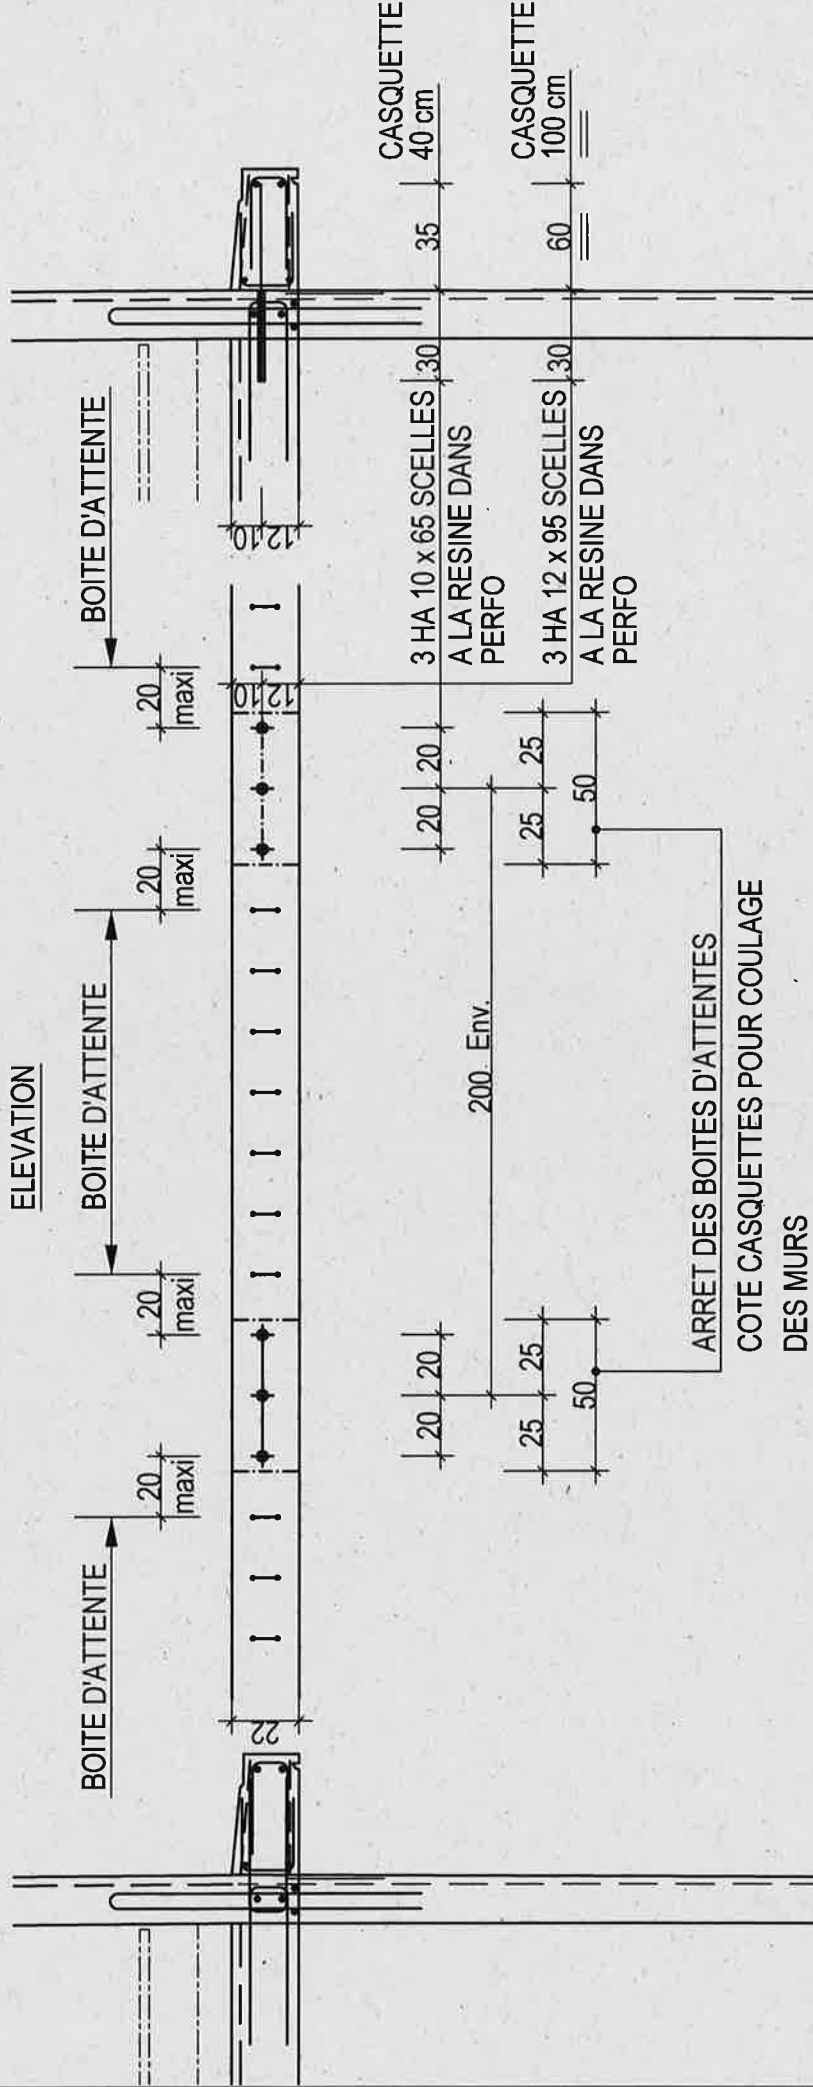

NOTA

_DETAIL VALABLE POUR LES CASQUETTES DE 40 cm et 100 cm