




ATTENTES POTEAUX DANS SEMELLES

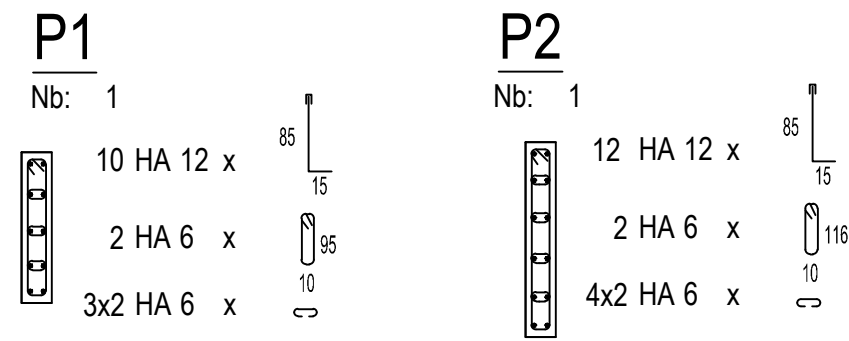


CASQUETTES 40 cm

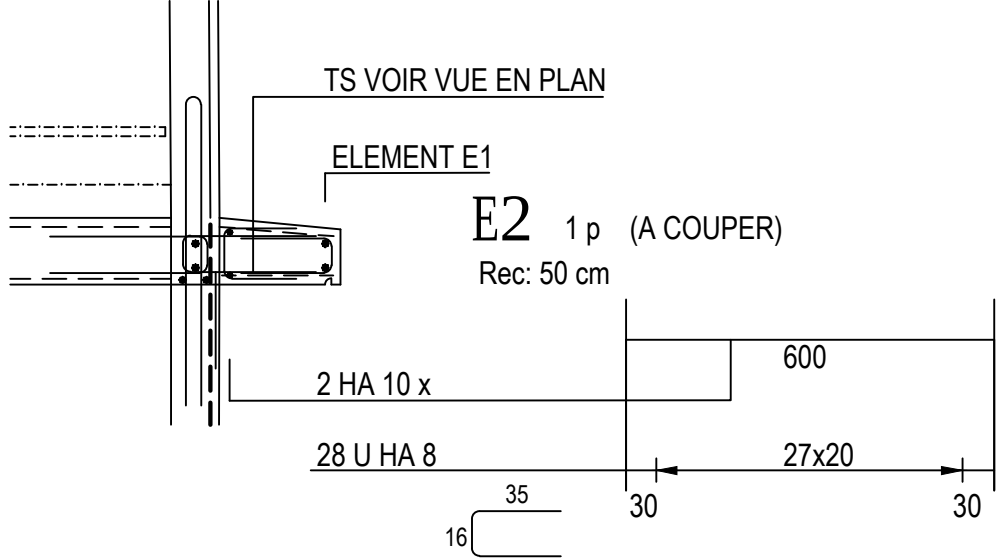


CASQUETTES 100 cm

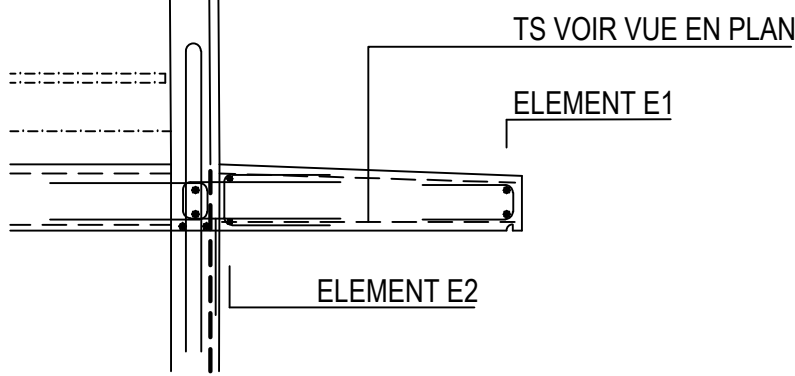


ATT1

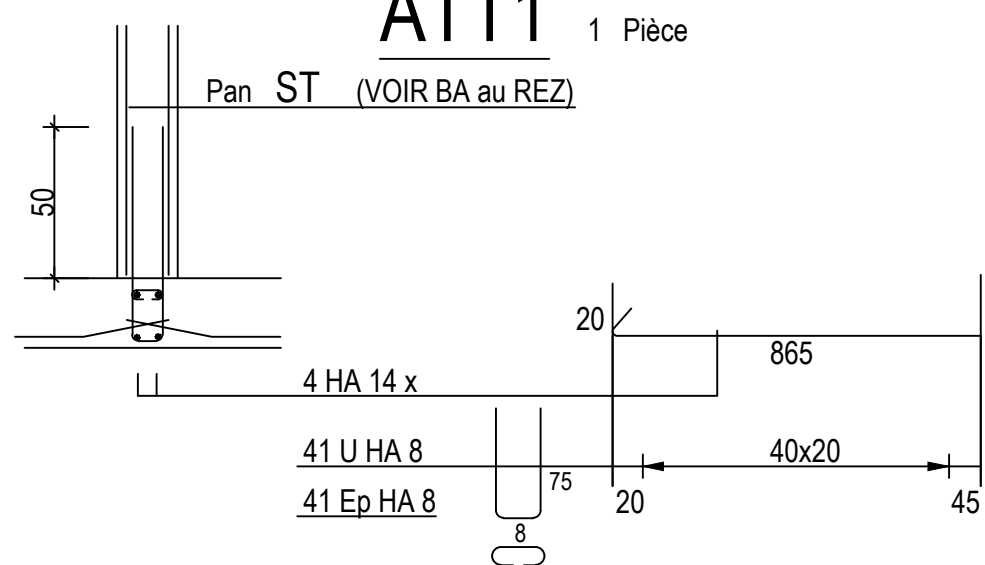


E1

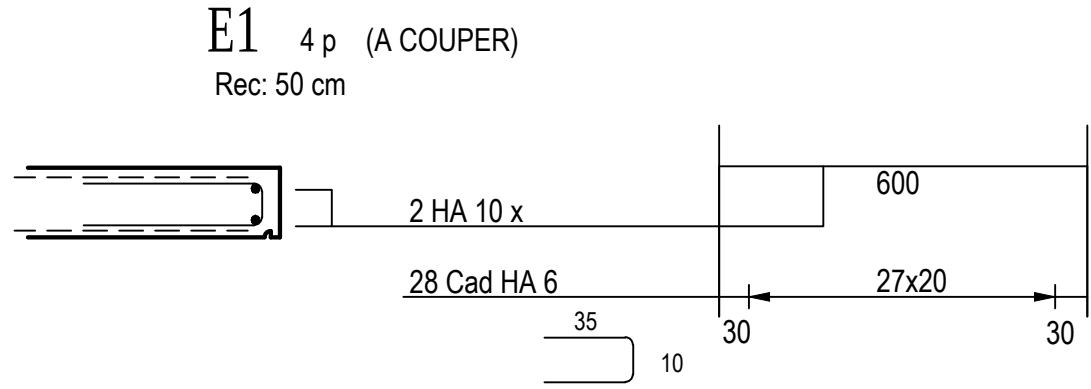


ATT2

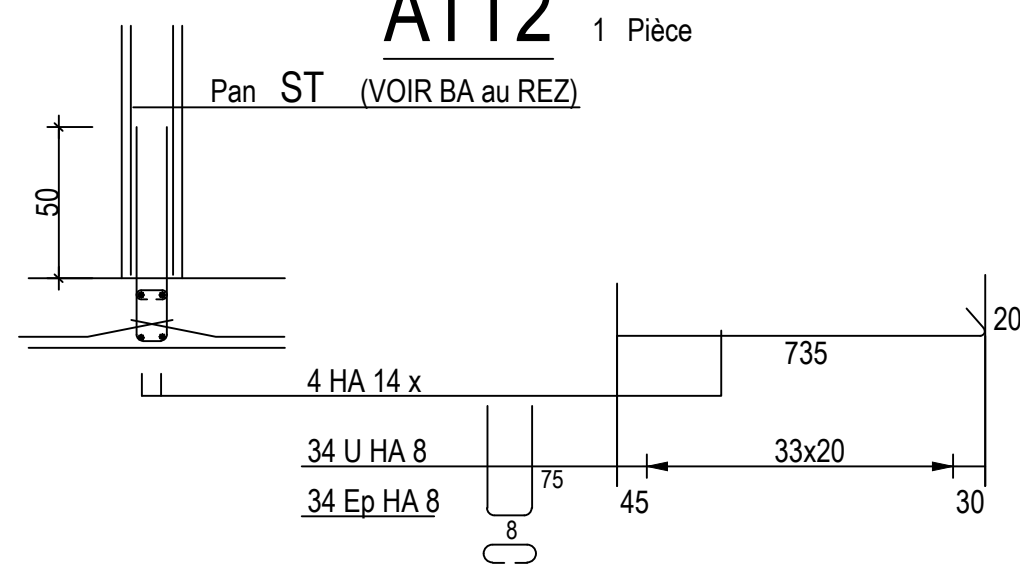

ANGLE E1

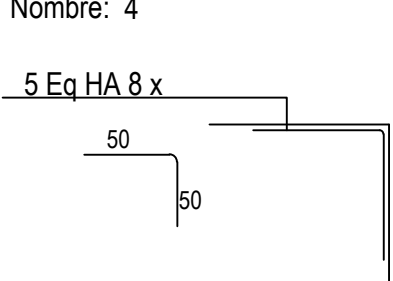

ATT

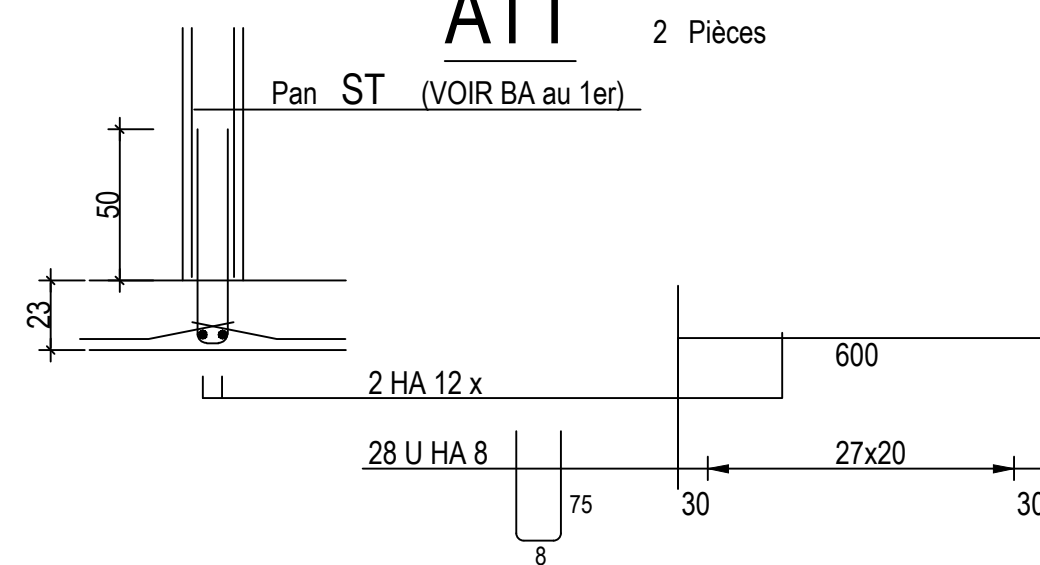


DETAIL D'ABOUTS DE CHAINAGES

INTERIEURS:

Position des étréques d'angles dans dalle 2 HA 14 x

à plat
vues en plan
chainage int. arrivant sur mur de façade
chainage int. arrivant sur mur int.

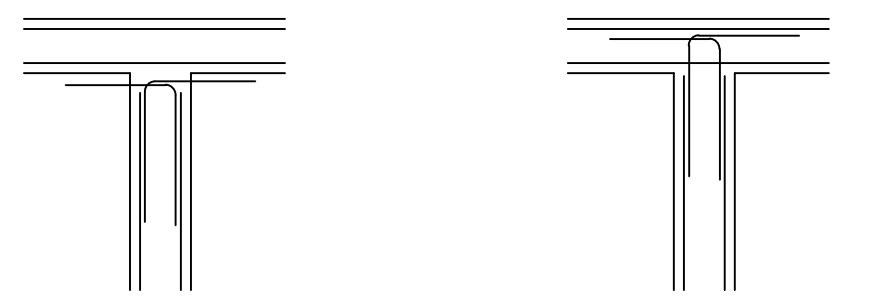


DETAIL D'ABOUTS DE CHAINAGES

EN ANGLE SUR FACADES:


Position des étréques d'angles dans dalle 2 HA 14

x
à plat
coupe
vue en plan

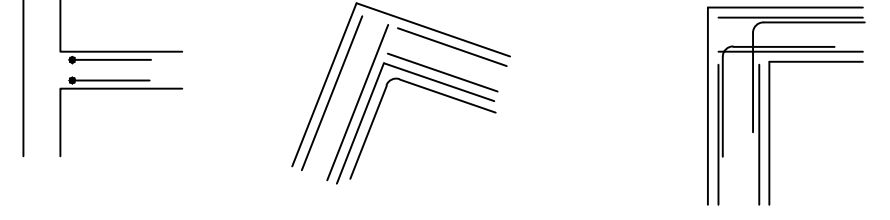


RECA. T.S.		
PAF 10	420x240	3
ST20	600x240	16
ST25	600x240	34
ST30	600x240	0
ST35	600x240	3
ST50	600x240	1
ST60	600x240	0
ST15C	400x240	1
ST25C	600x240	17
ST40C	600x240	4
ST50C	600x240	0
ST65C	600x240	0

ARMATURES SUPERIEURES

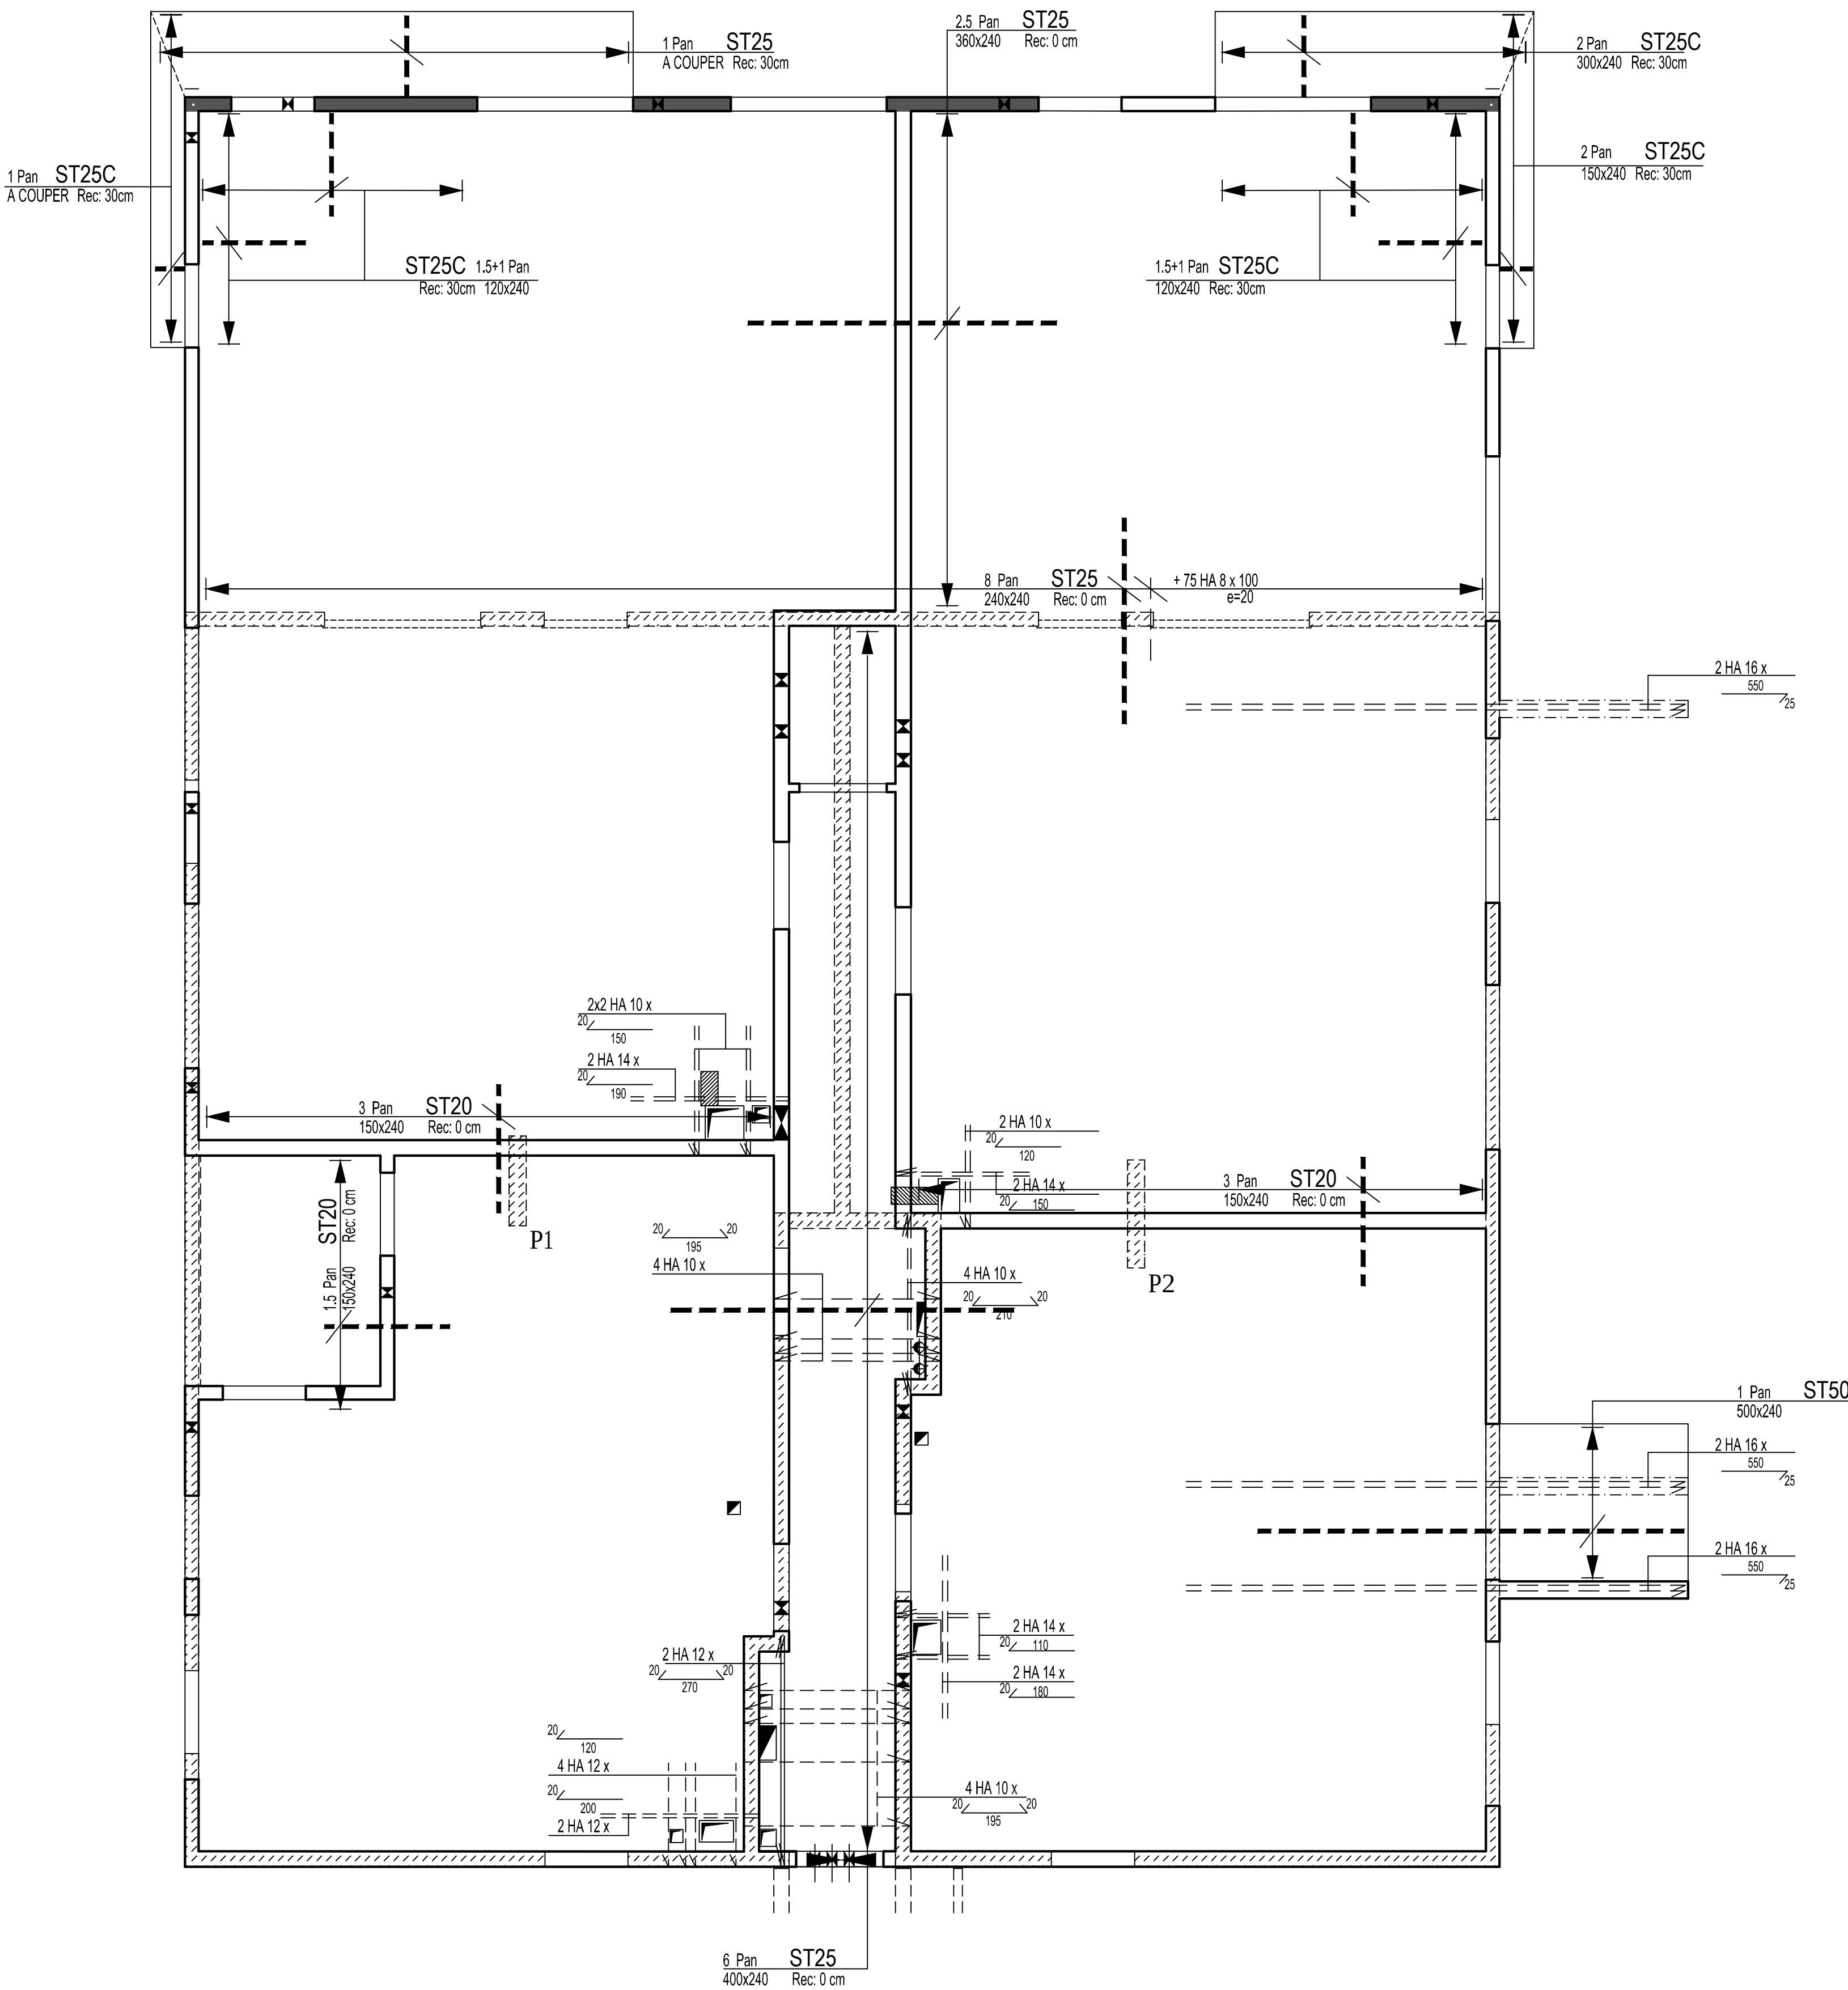


ARMATURES INFERIEURES

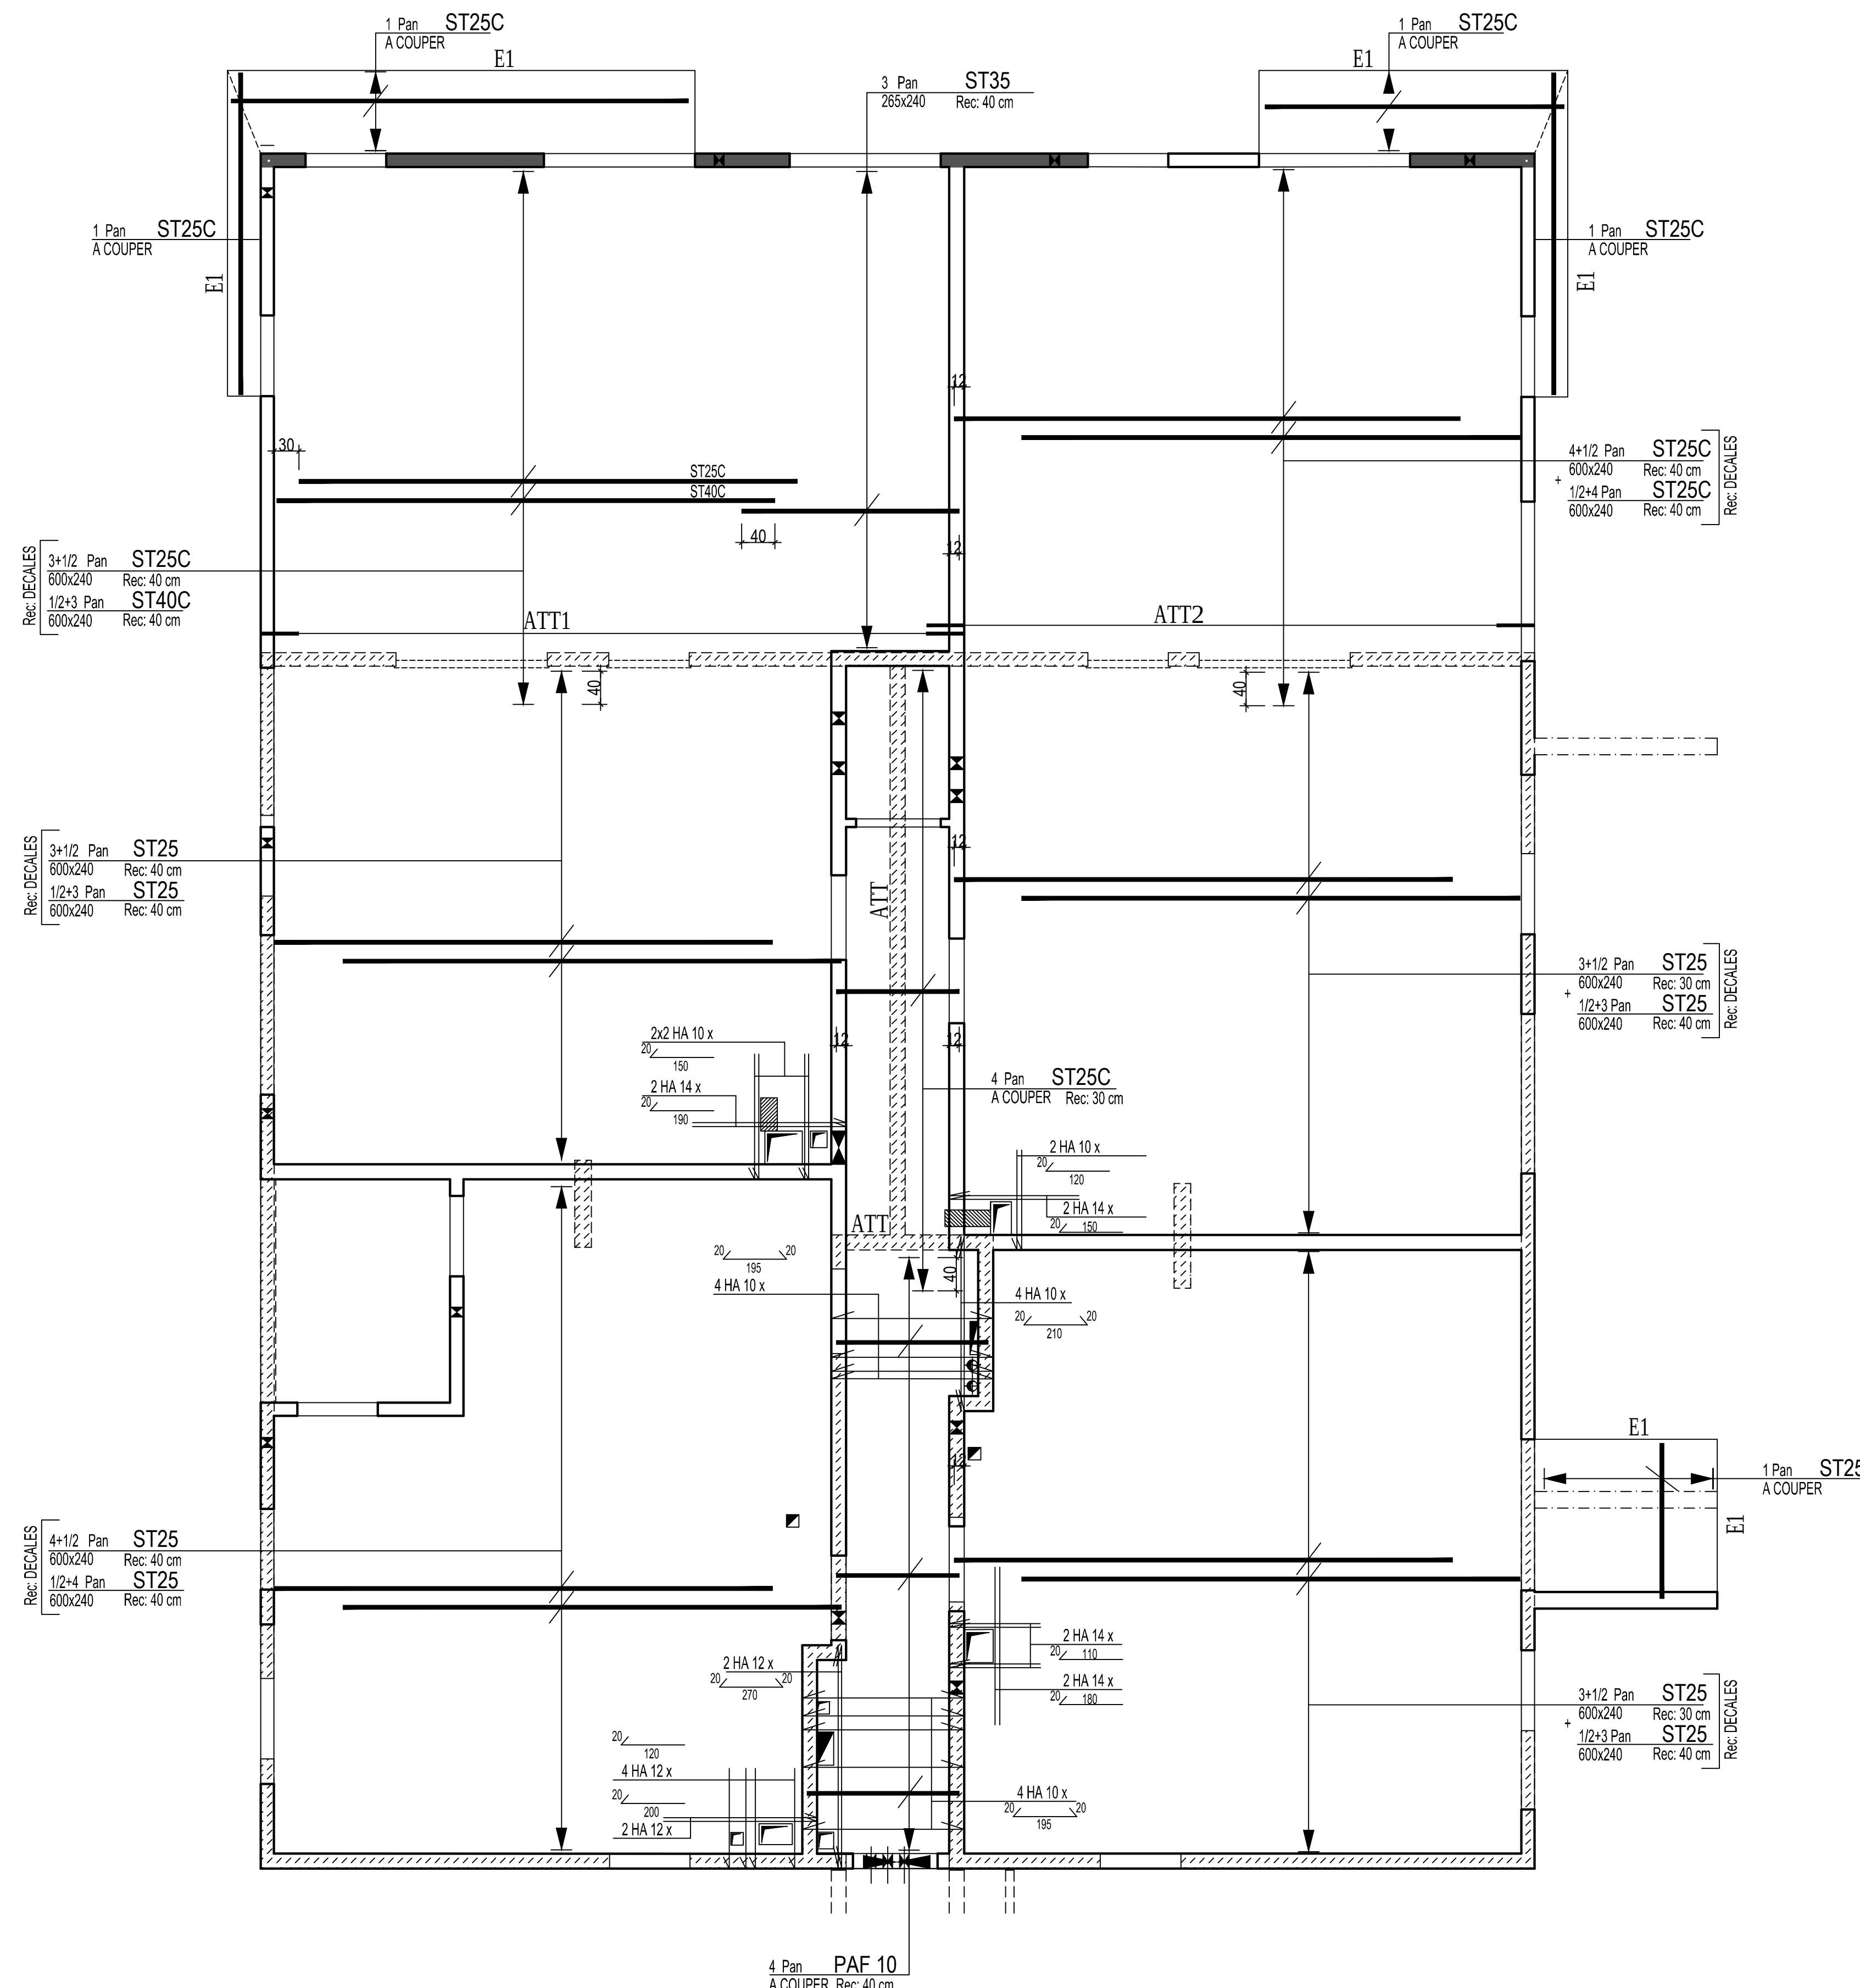


RENFORTS RESESERVATIONS

JUSQU'A Ø200 mm

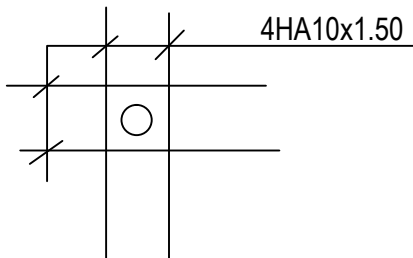

Principe de renfort aux droits des gaines:

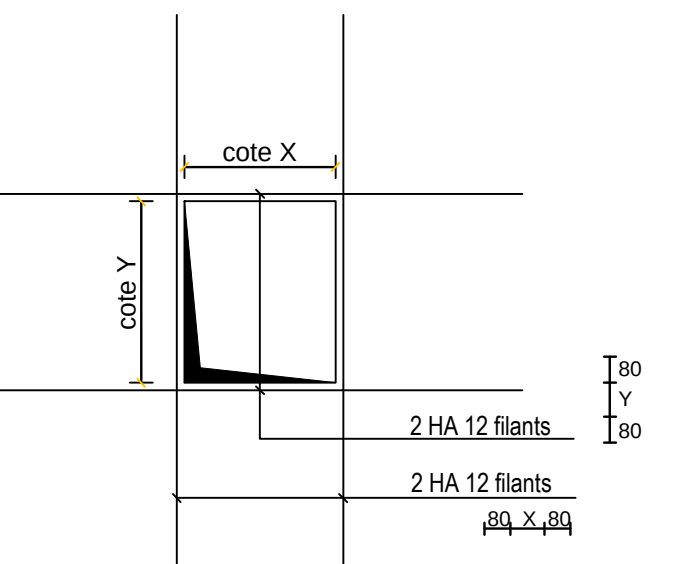

NOTA: Ces renforts sont en complément des aciers mis sur la vue en plan

..PANNEAUX EN TIROIRS PREVOIR RECouvreMENTS DECALES
EX: 1er Lit: 2 panneaux
2ème Lit: 1/2-2+1/2 panneaux

NOAHO

Chemin de Fontanière - 69350 La Mulatière

Création de logements

ARCHITECTES: Atelier D1S
BET STRUCTURE: MATTE SAS
BET FLUIDES: PRELEM
ECONOMISTE: EXECO
BUREAU DE CONTROLE: Bureau VERITAS

MO. DELEGUE: PSO Ingénierie
CSPS: SUD EST COORDINATION
CPC: ENTREPRISES: Fontanel-gbc

Bât: C Aile EST
PLANCHER SUR REZ
ARMATURES DALLE

DOE

INDICE

DATE

MODIFICATIONS

MATTÉ
BUREAU D'ETUDES
STRUCTURES ET FLUIDES
119 BOULEVARD STALINGRAD 69100 VILLEURBANNE
Tel: 04 72 44 12 81 Fax: 04 72 44 25 59
E-mail: s@matte.fr

Dessiné par: J.BO
Contrôlé par: P.LIN
Echelle: 1/50'

PLAN N°
C27 0
DATE: 05-10-2015

Affaire N°
13.12.119