



DETAILS DES SEUILS



DETAIL "1"

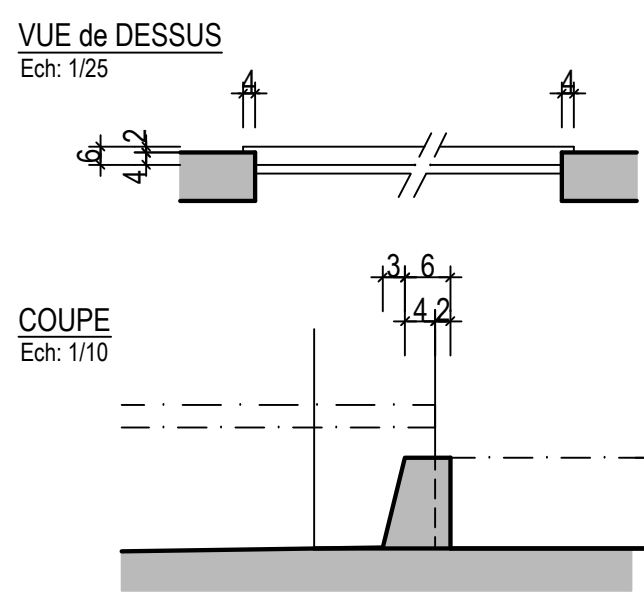


DETAIL "2"

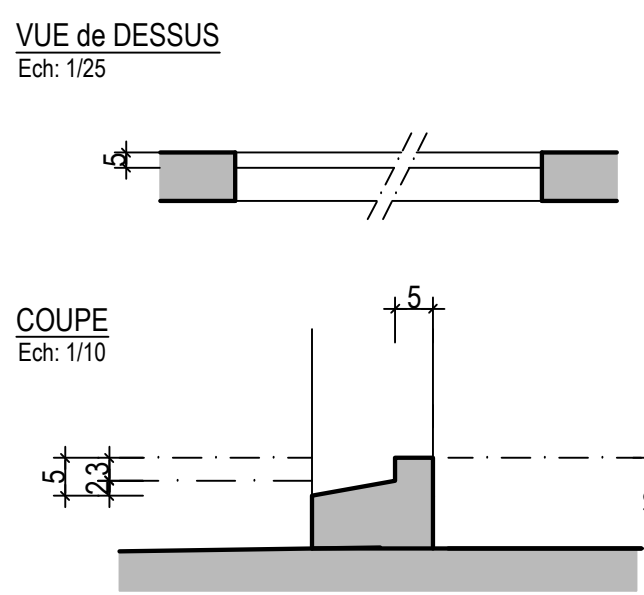


DETAIL "3"

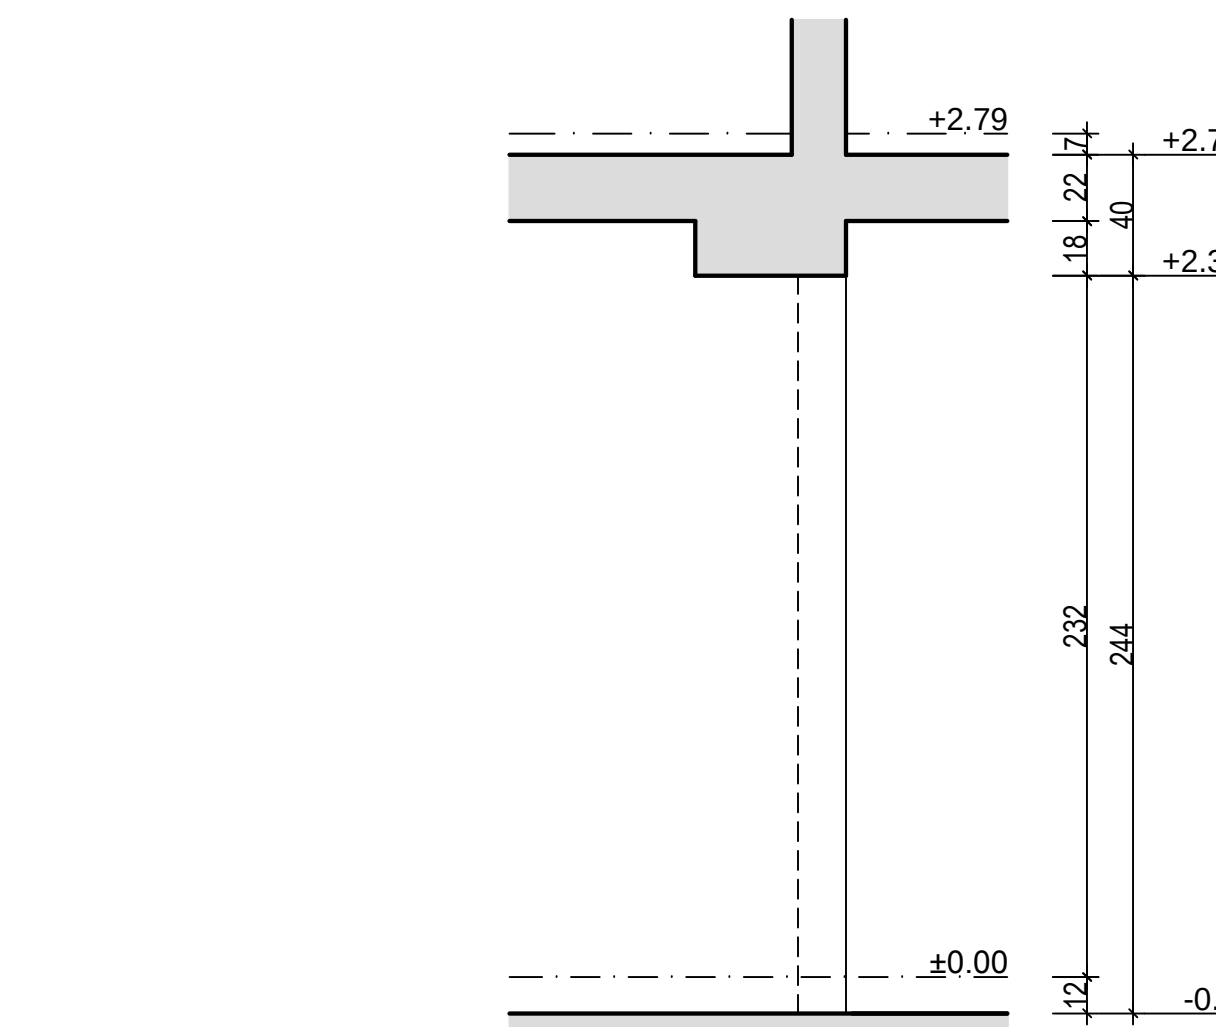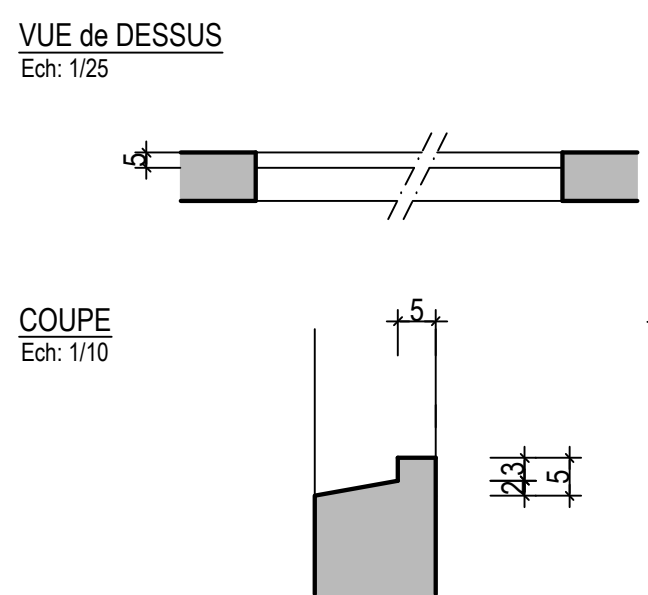


COUPE U

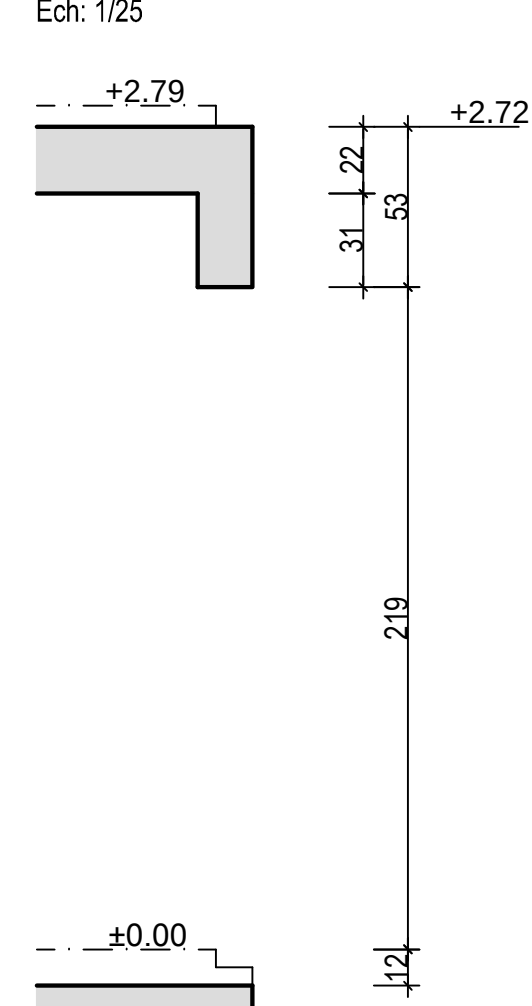


COUPE S

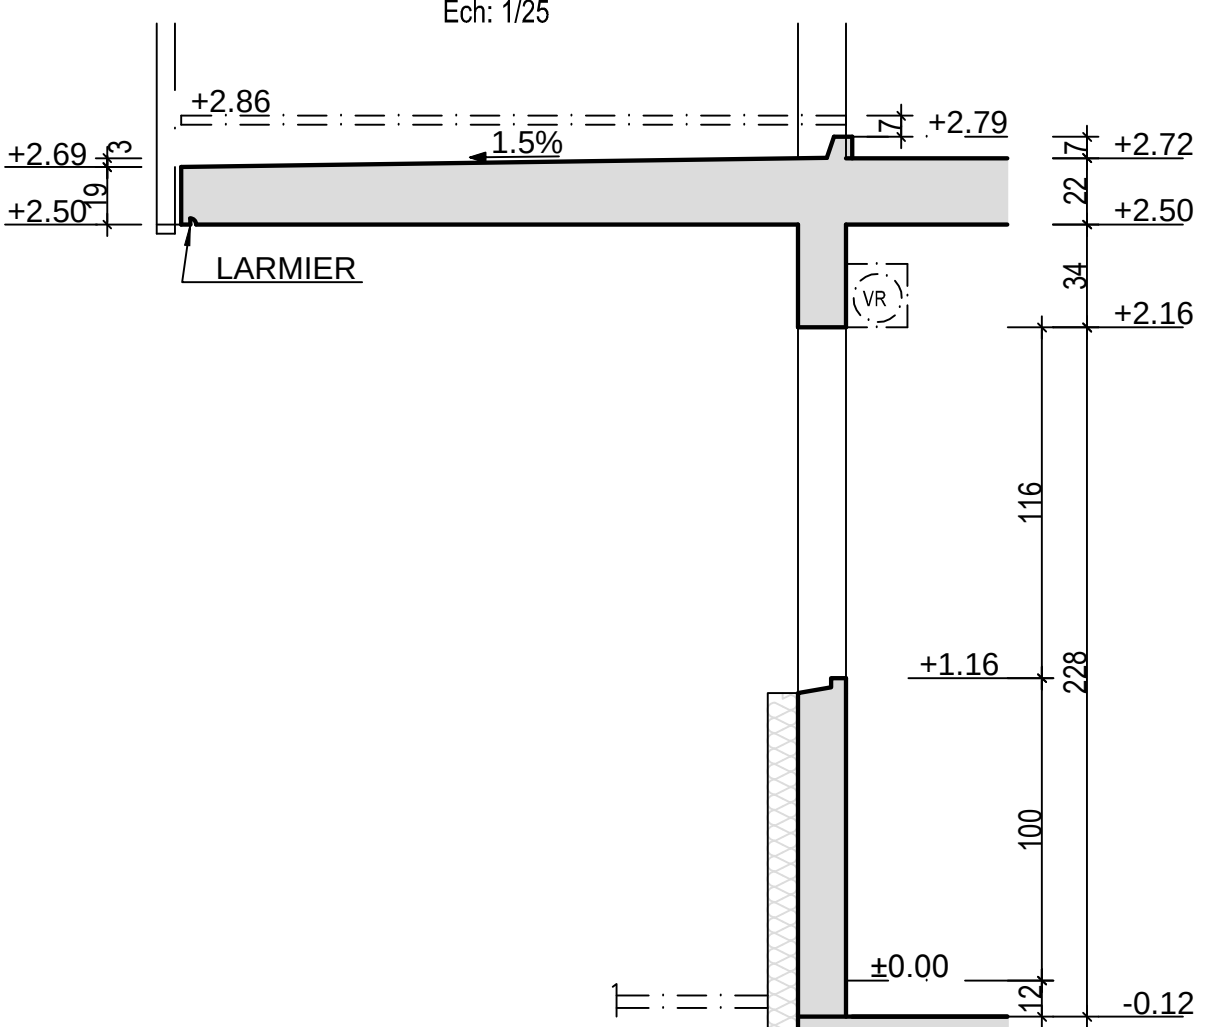


COUPE R

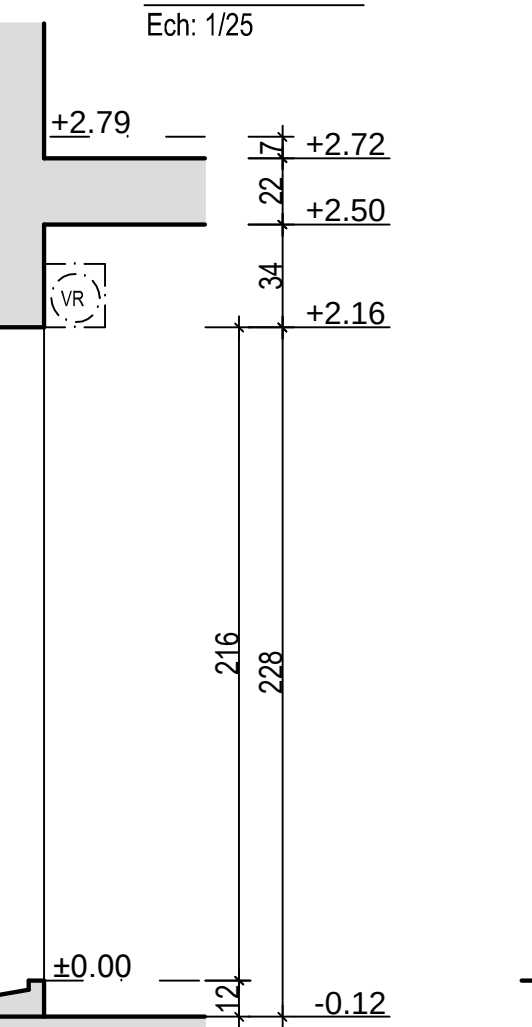


COUPE Q

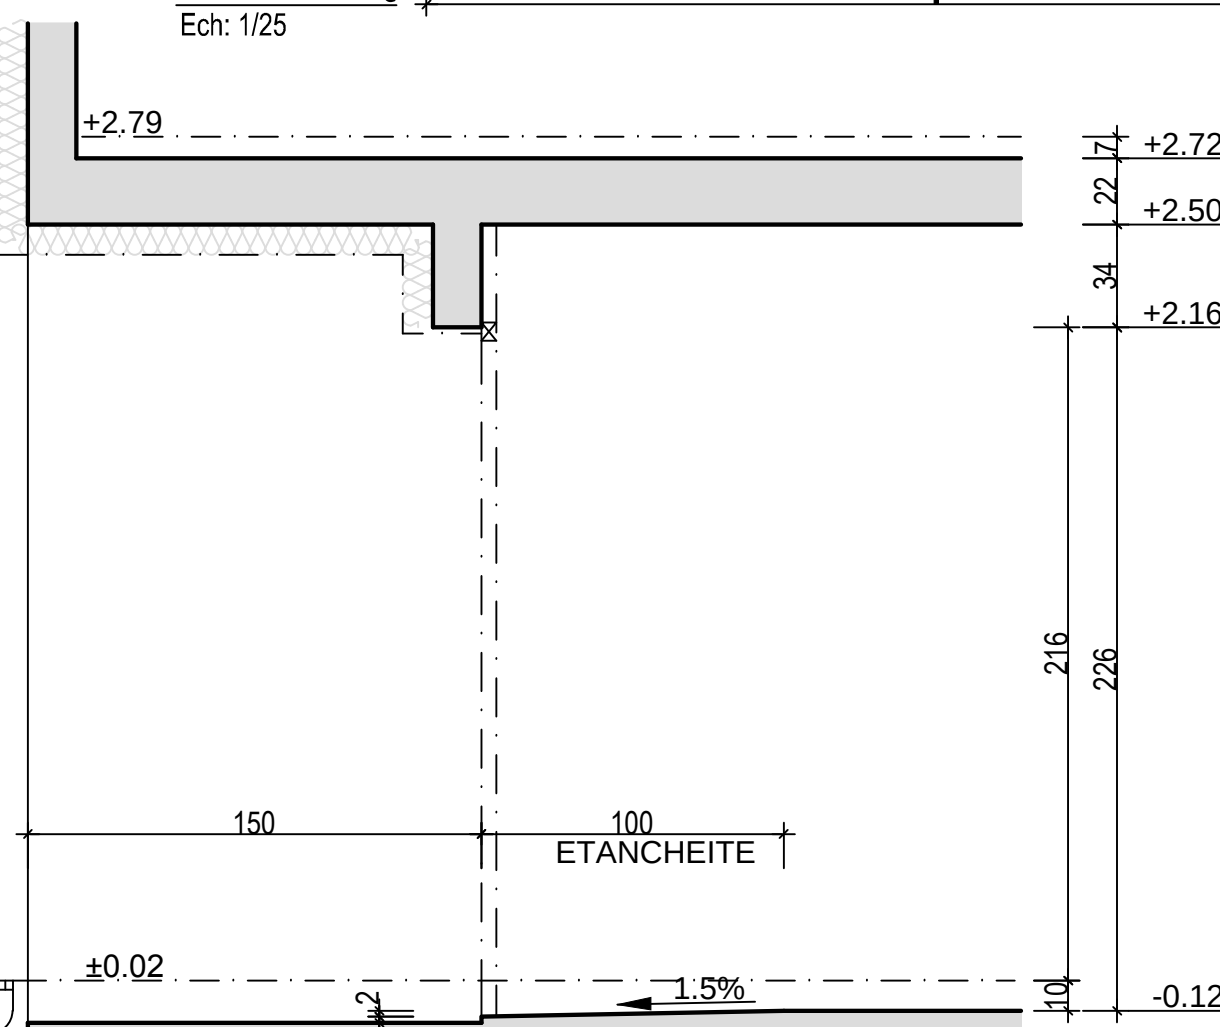


COUPE P

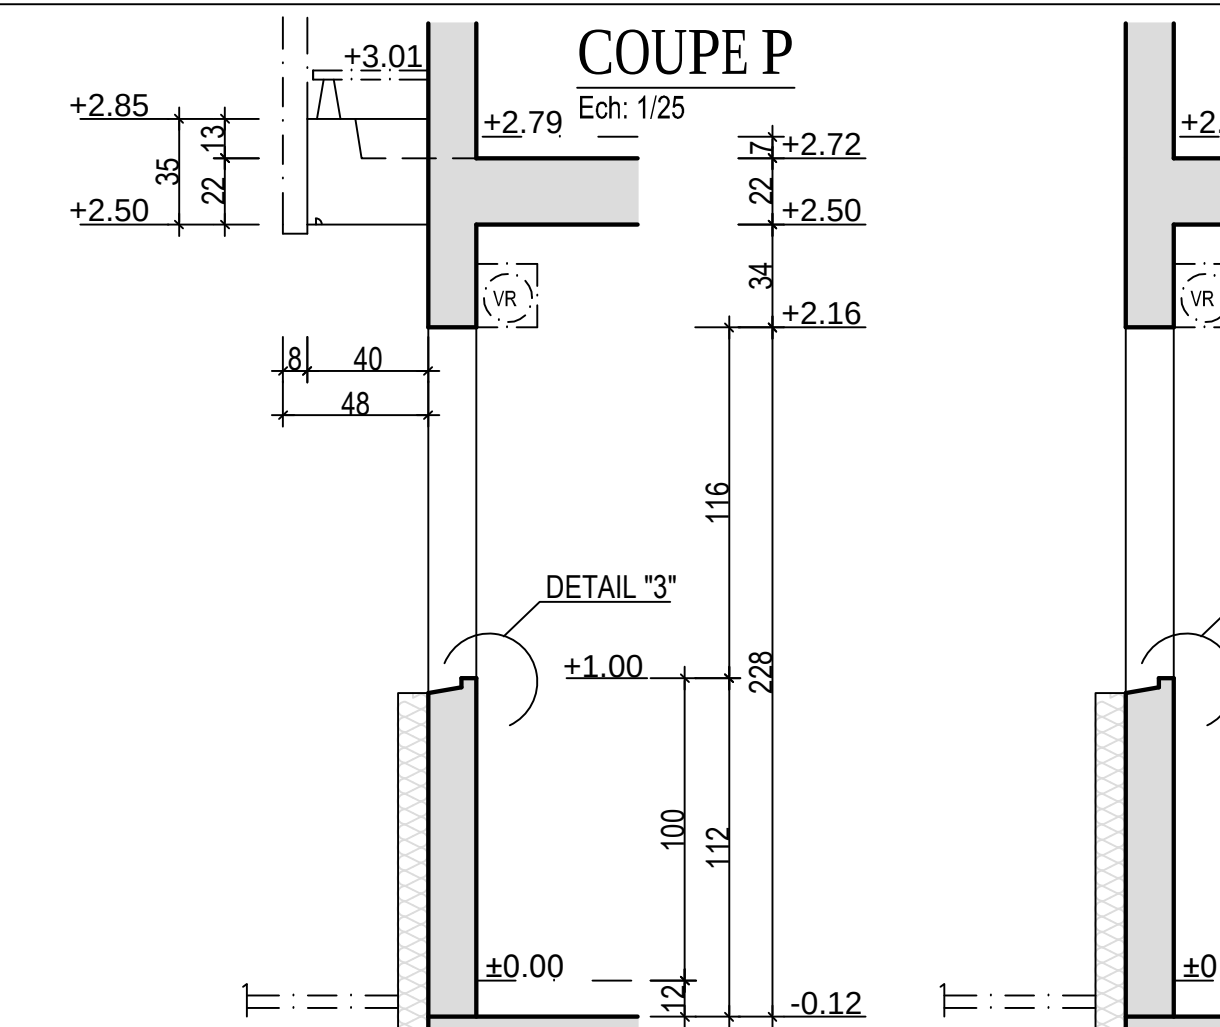


COUPE N

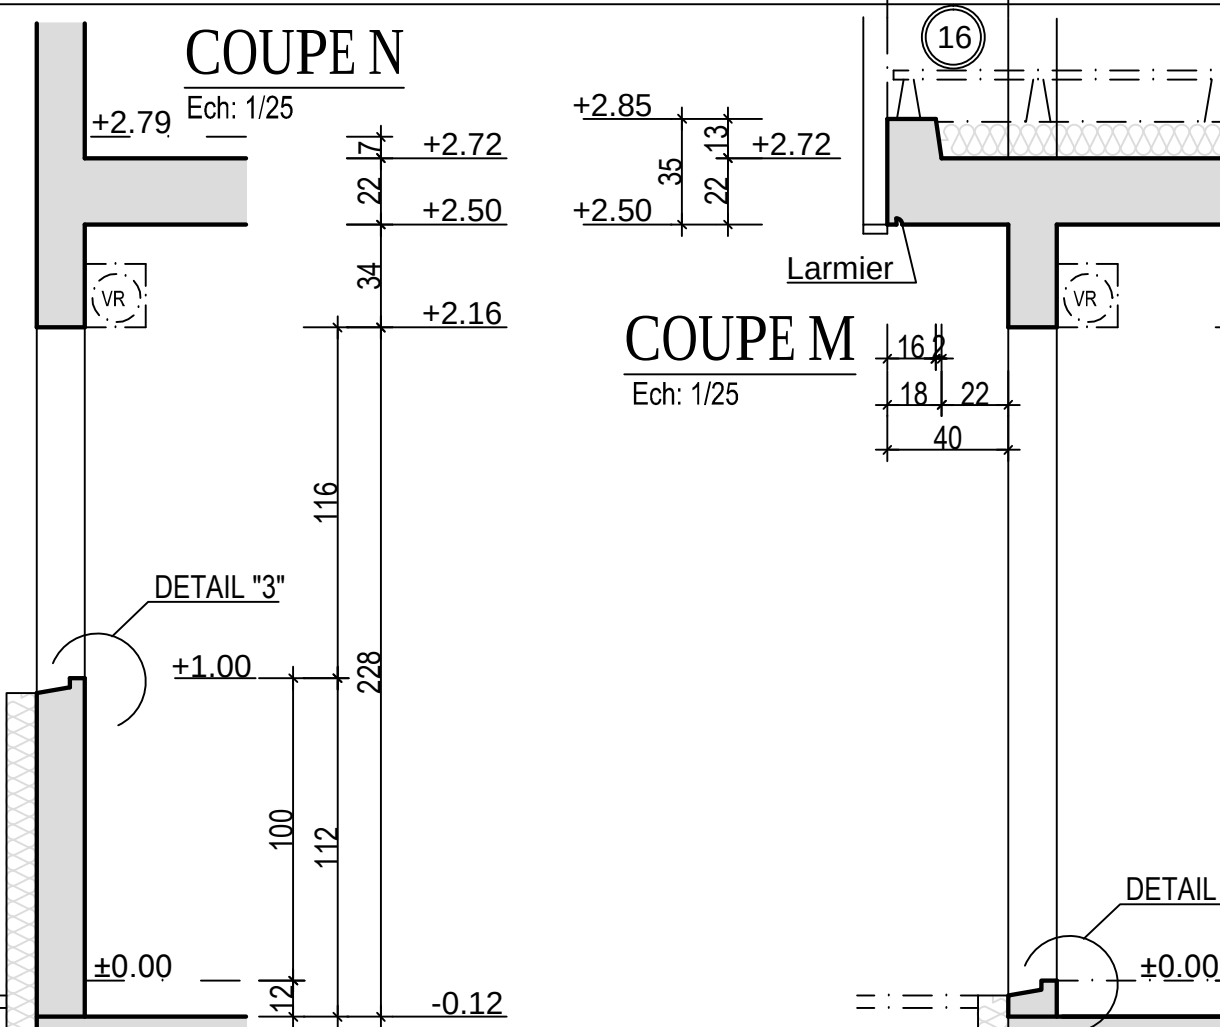


COUPE M

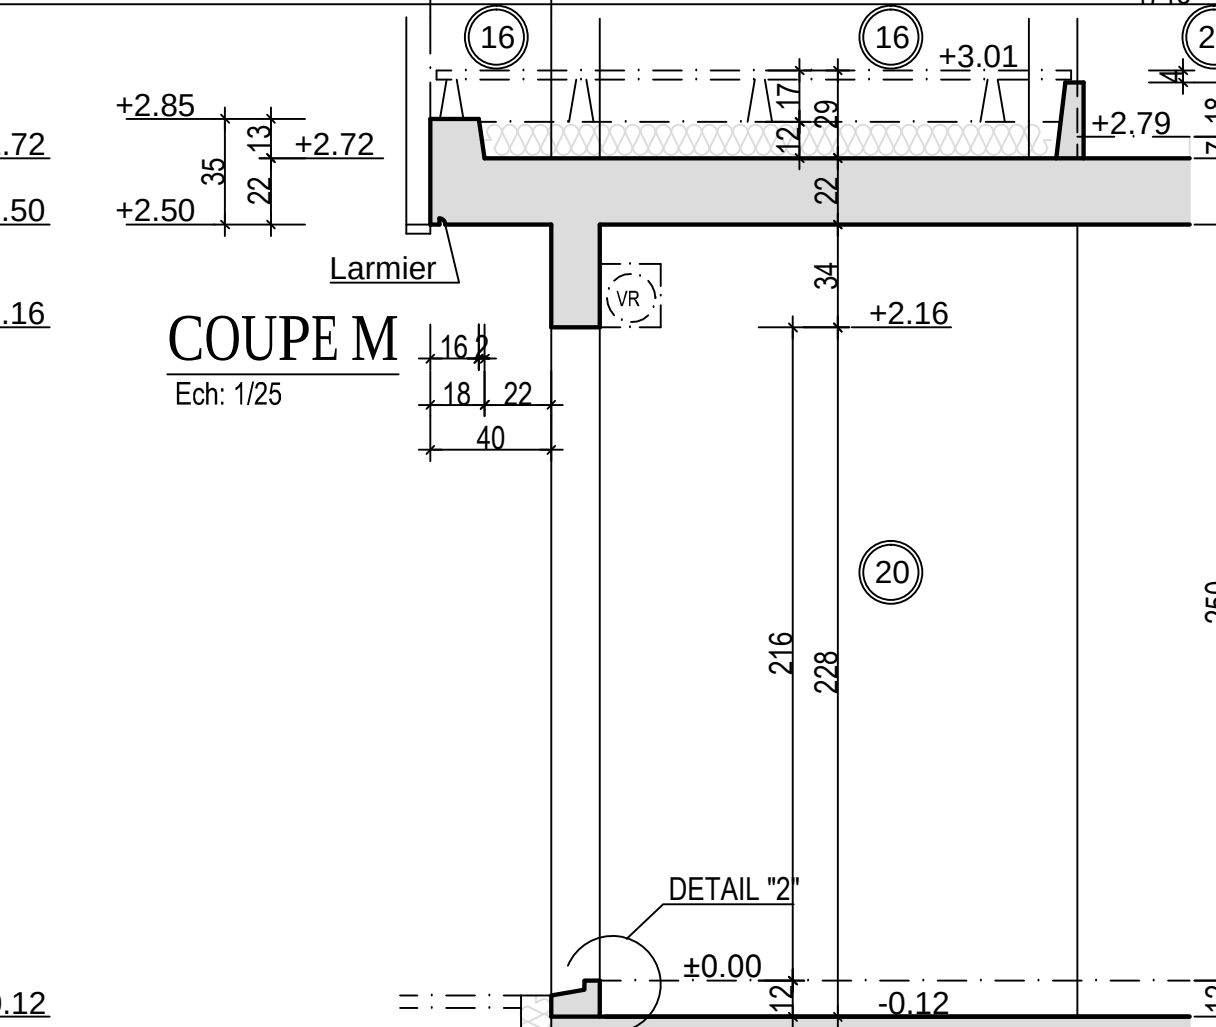


COUPE L

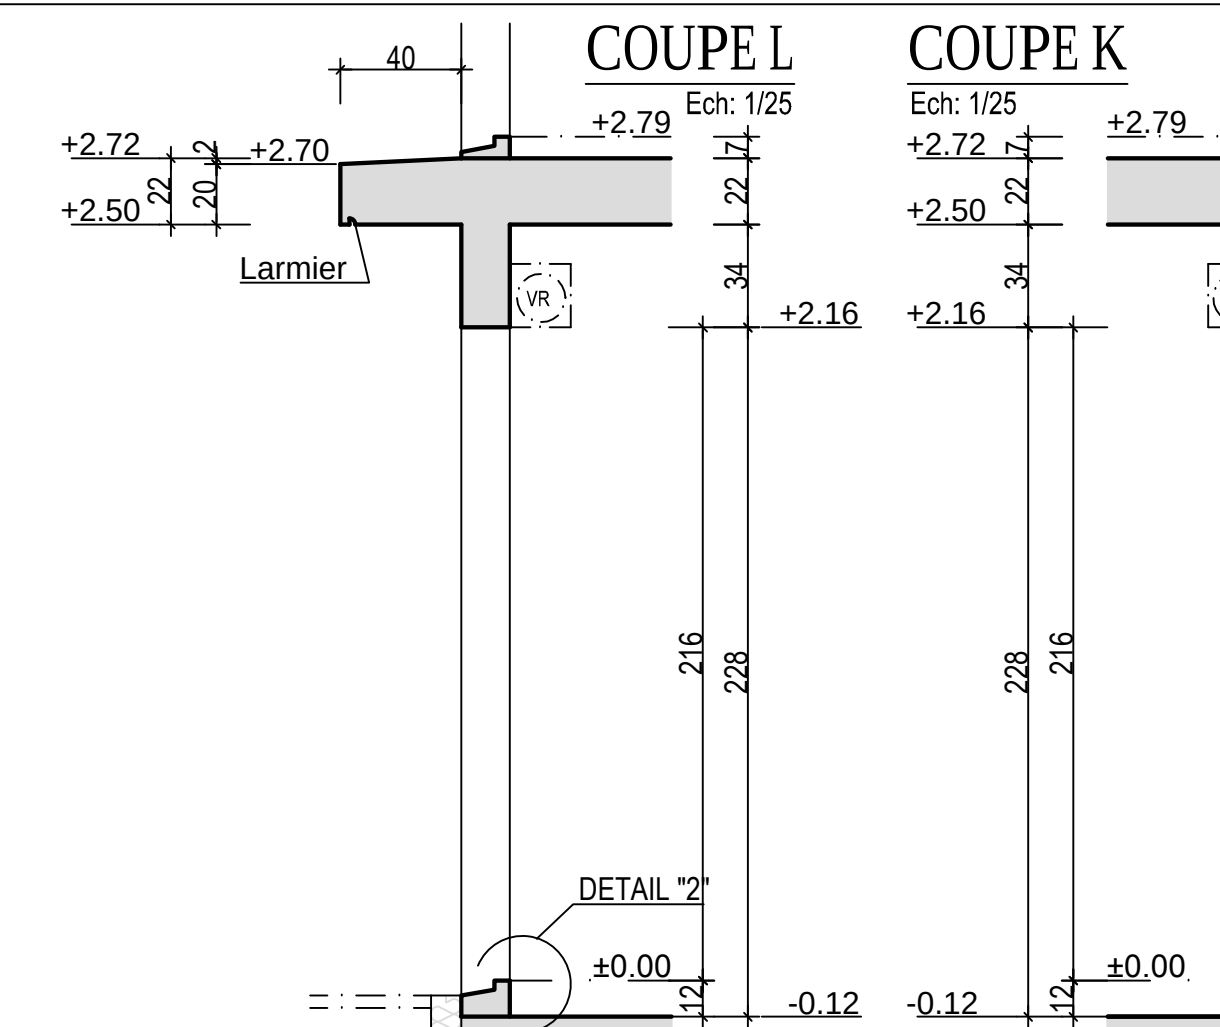


COUPE K

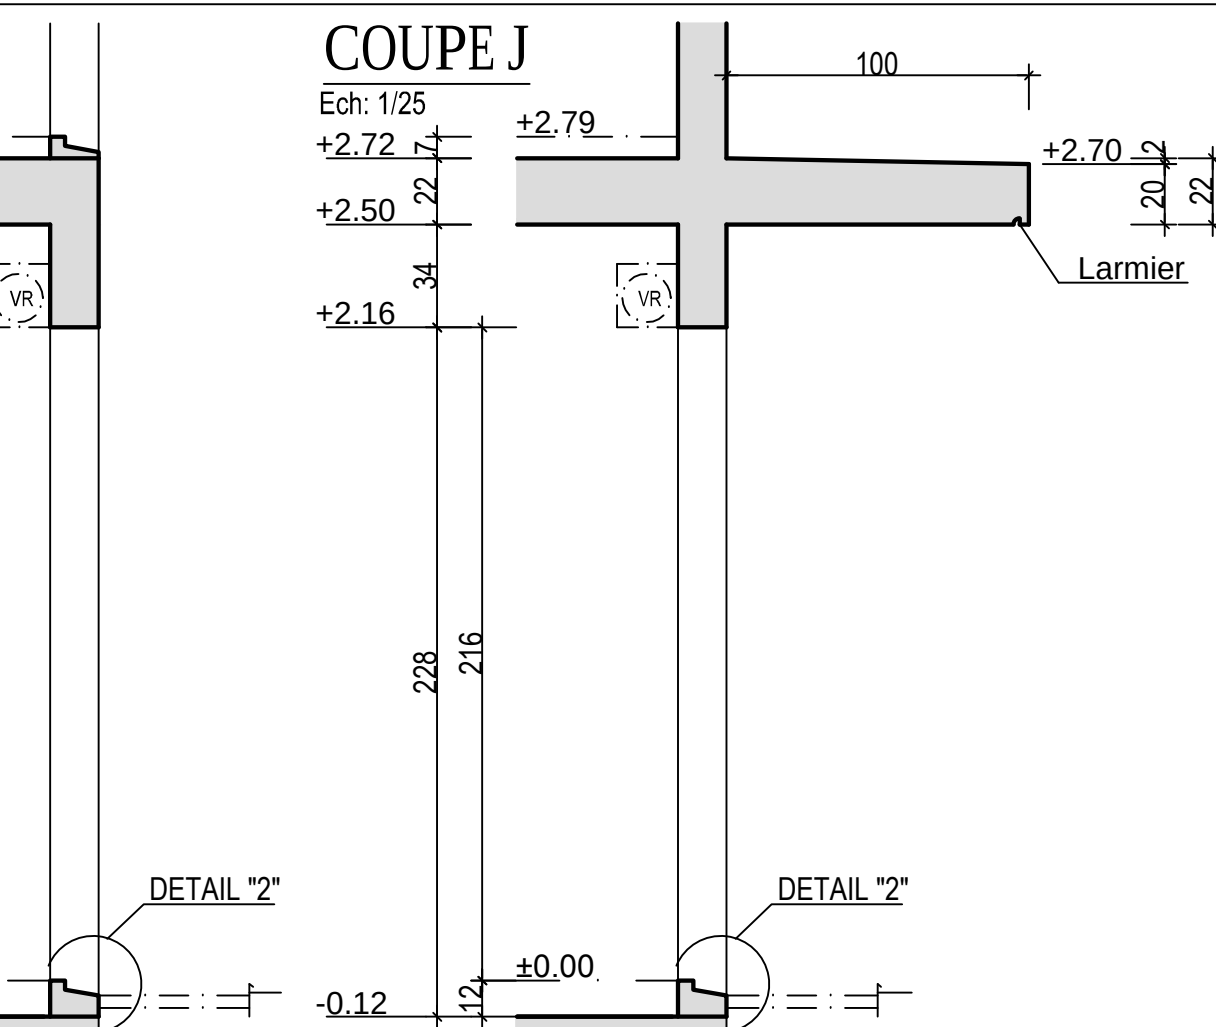


COUPE J

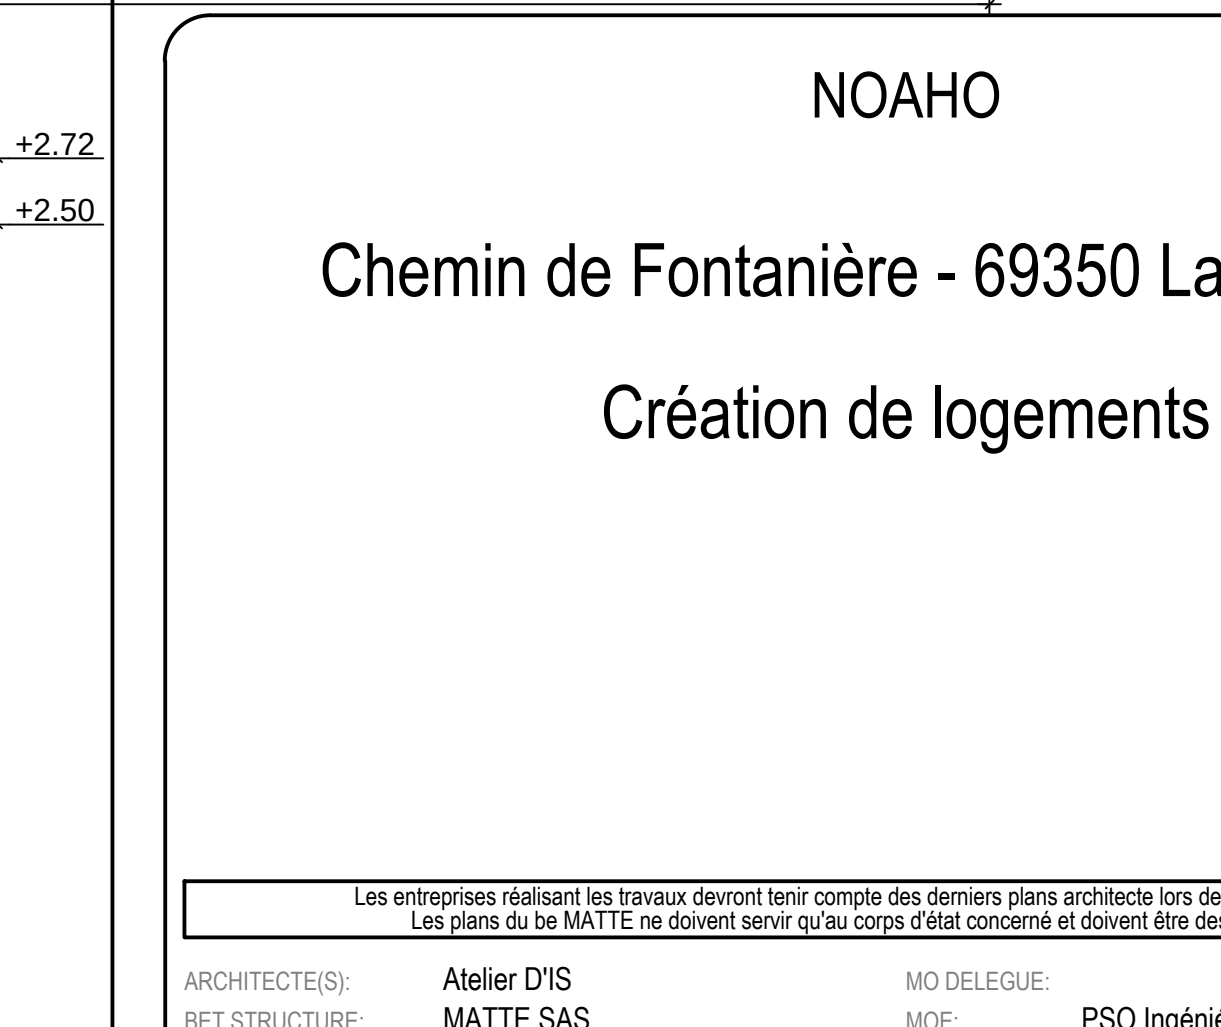


COUPE H

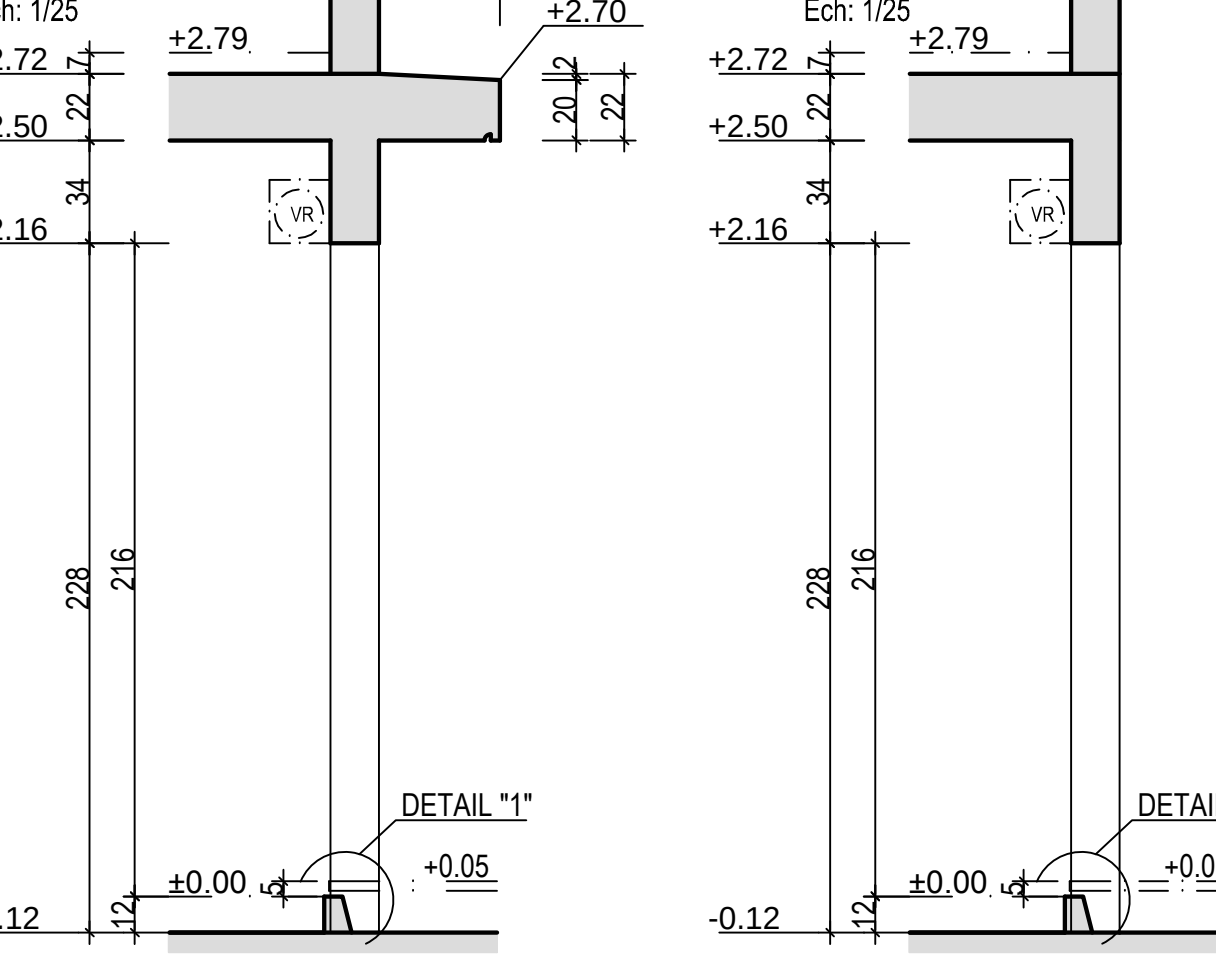


COUPE G

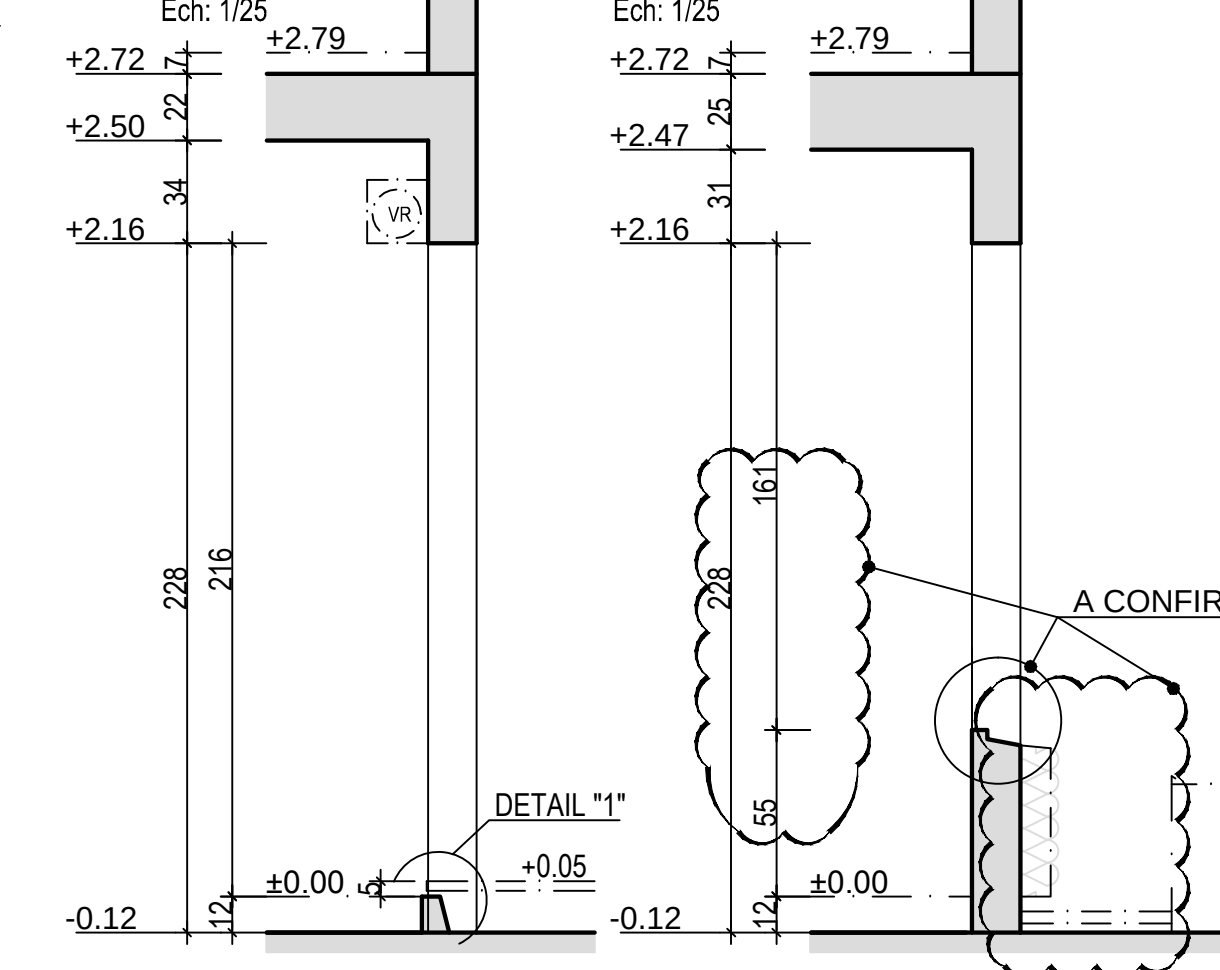


COUPE F

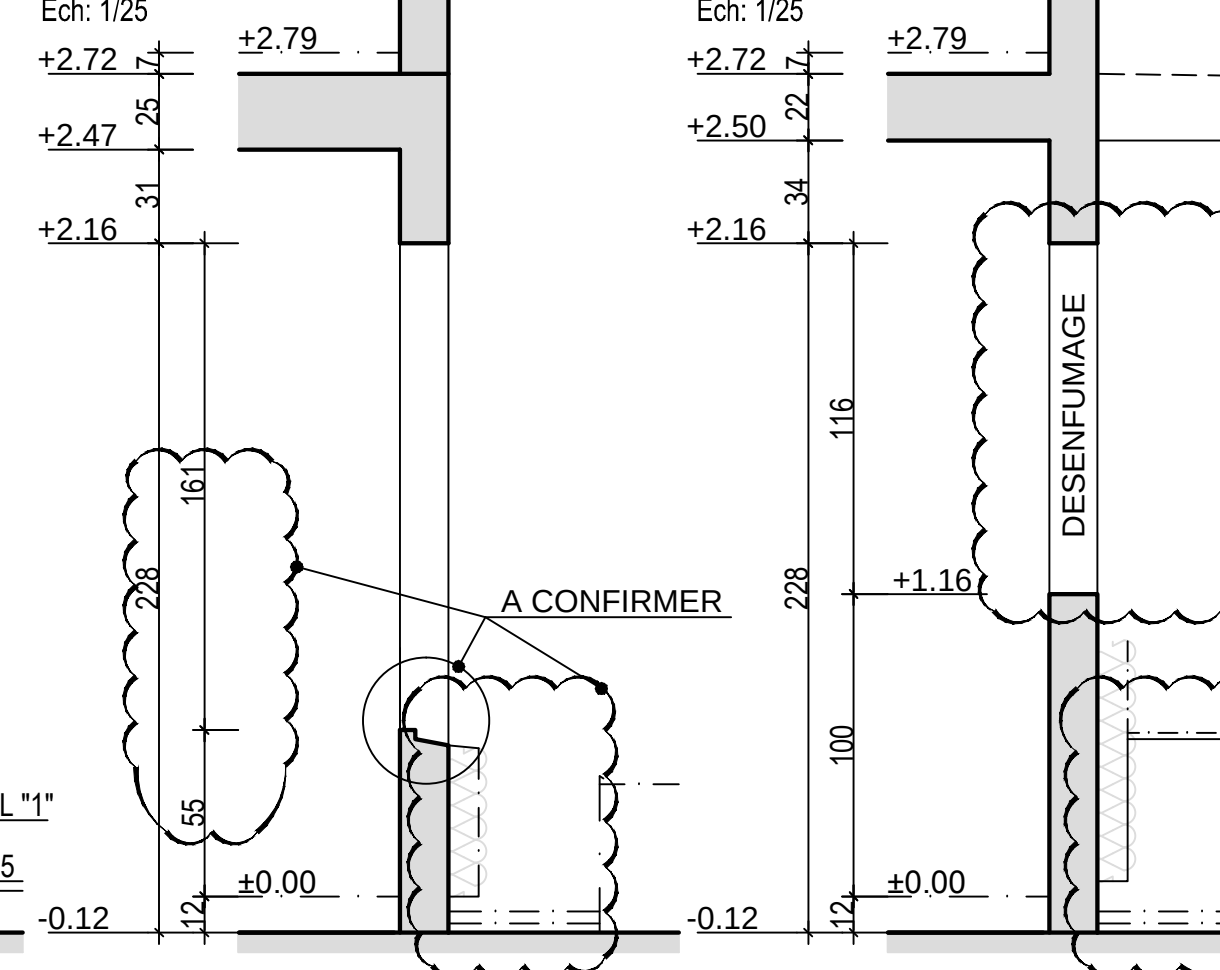


COUPE E

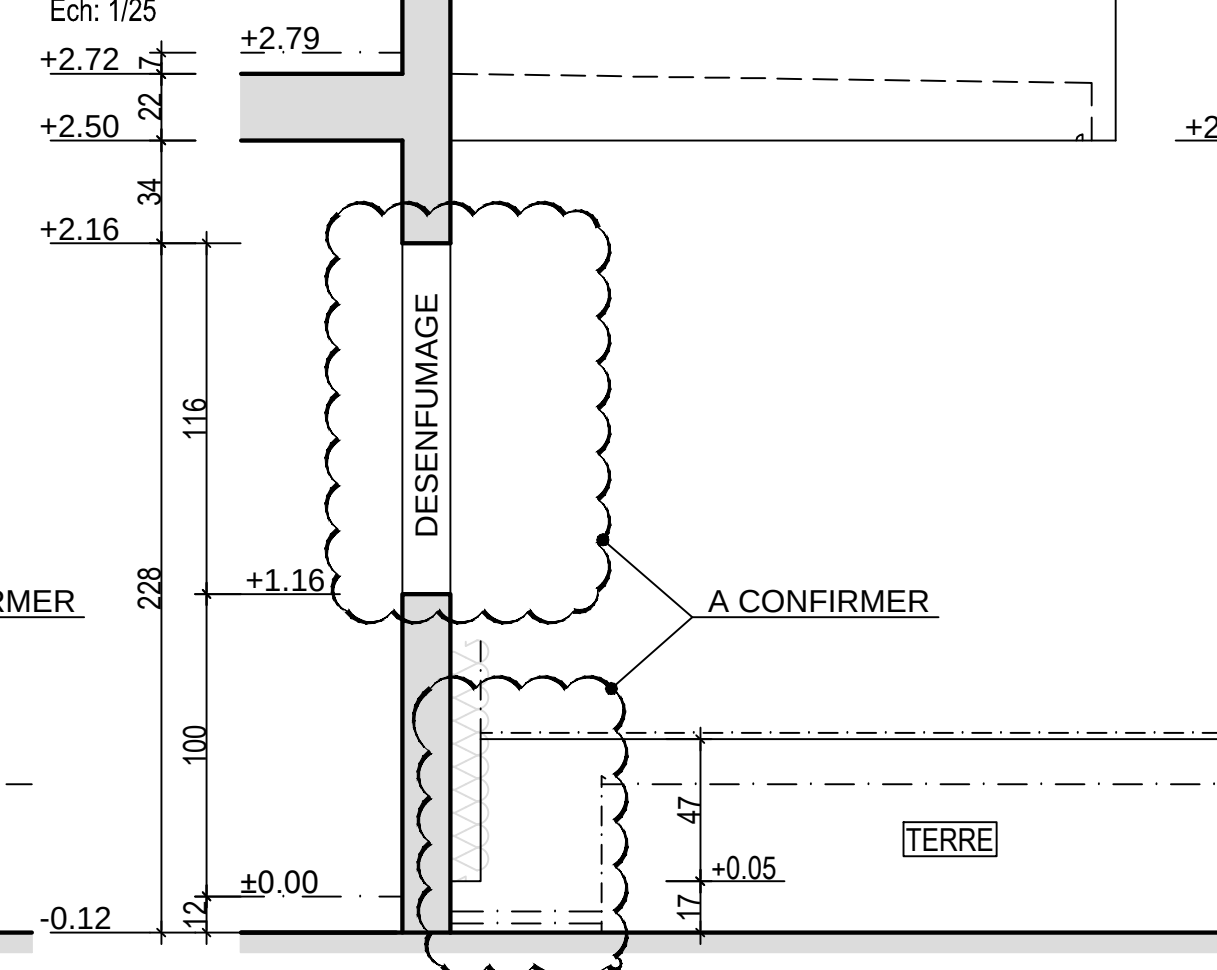


COUPE D

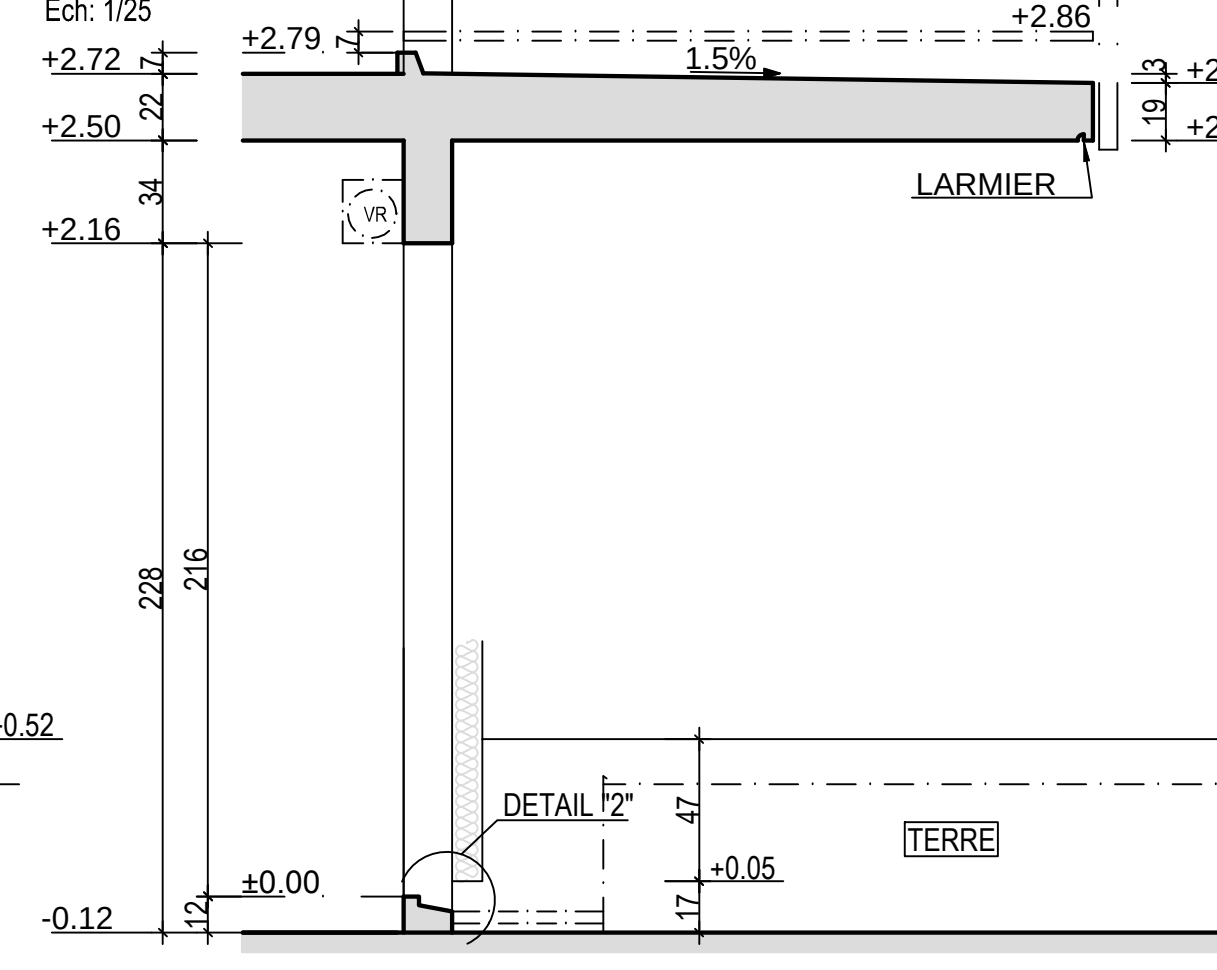


COUPE C

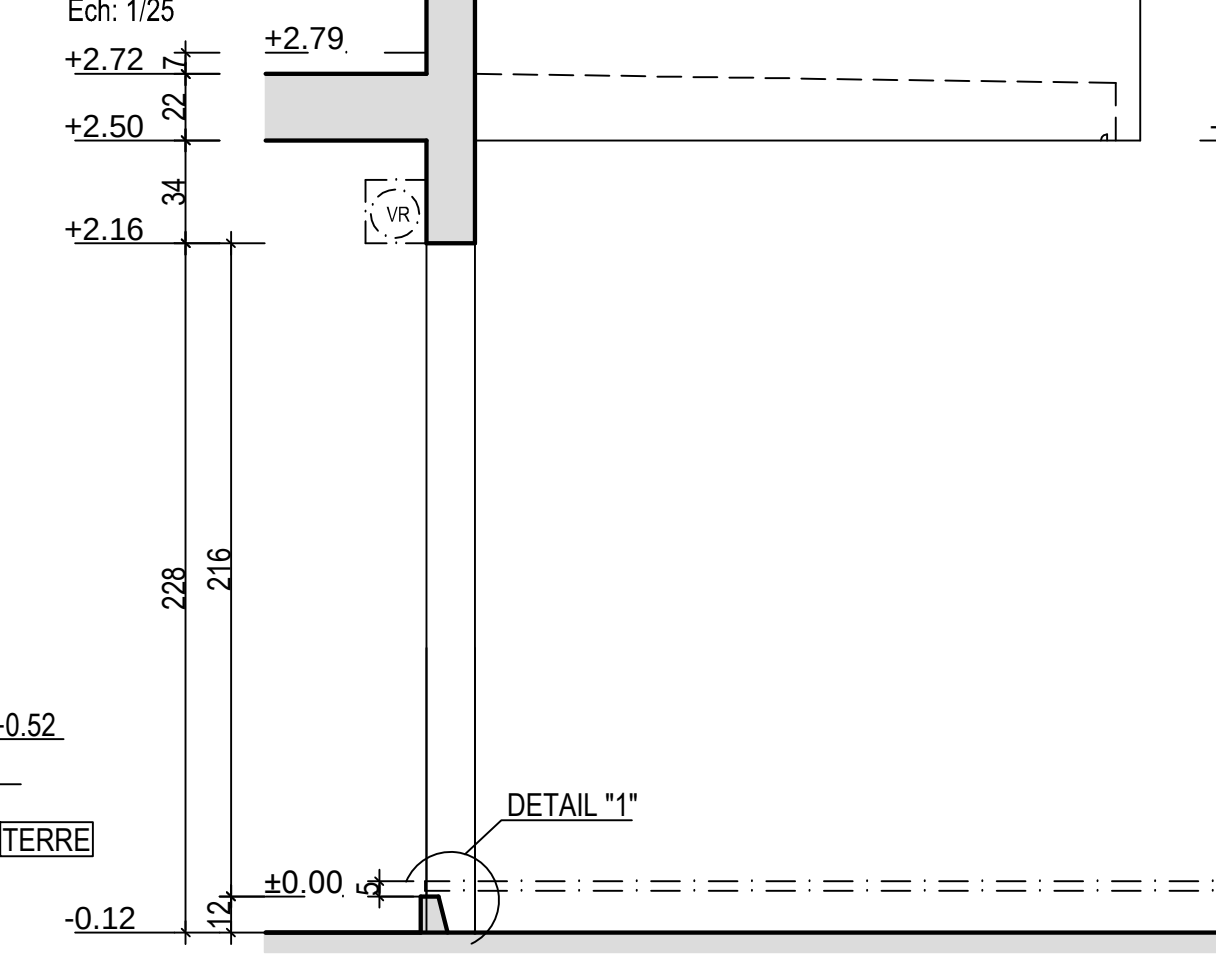

COUPE B

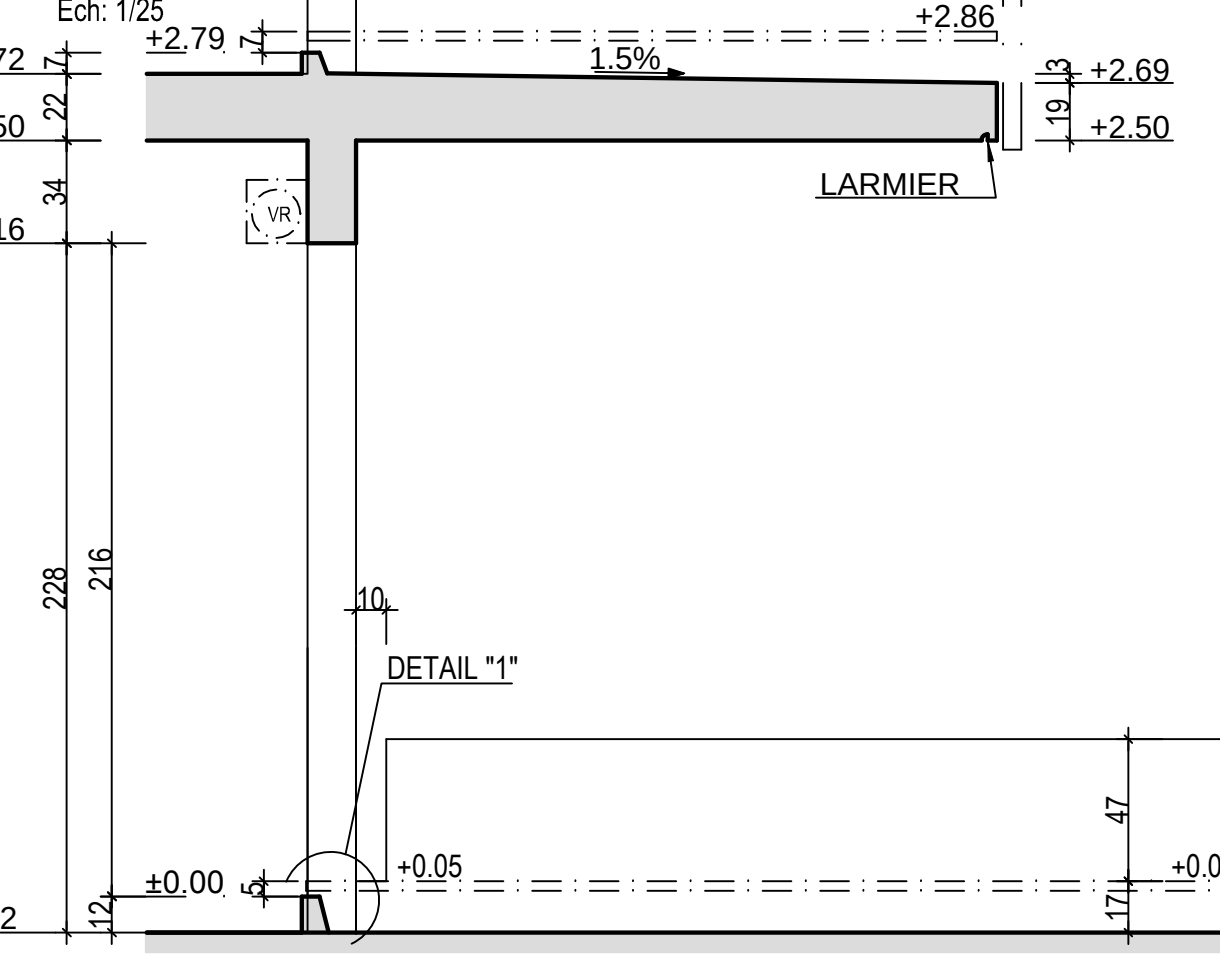

COUPE A

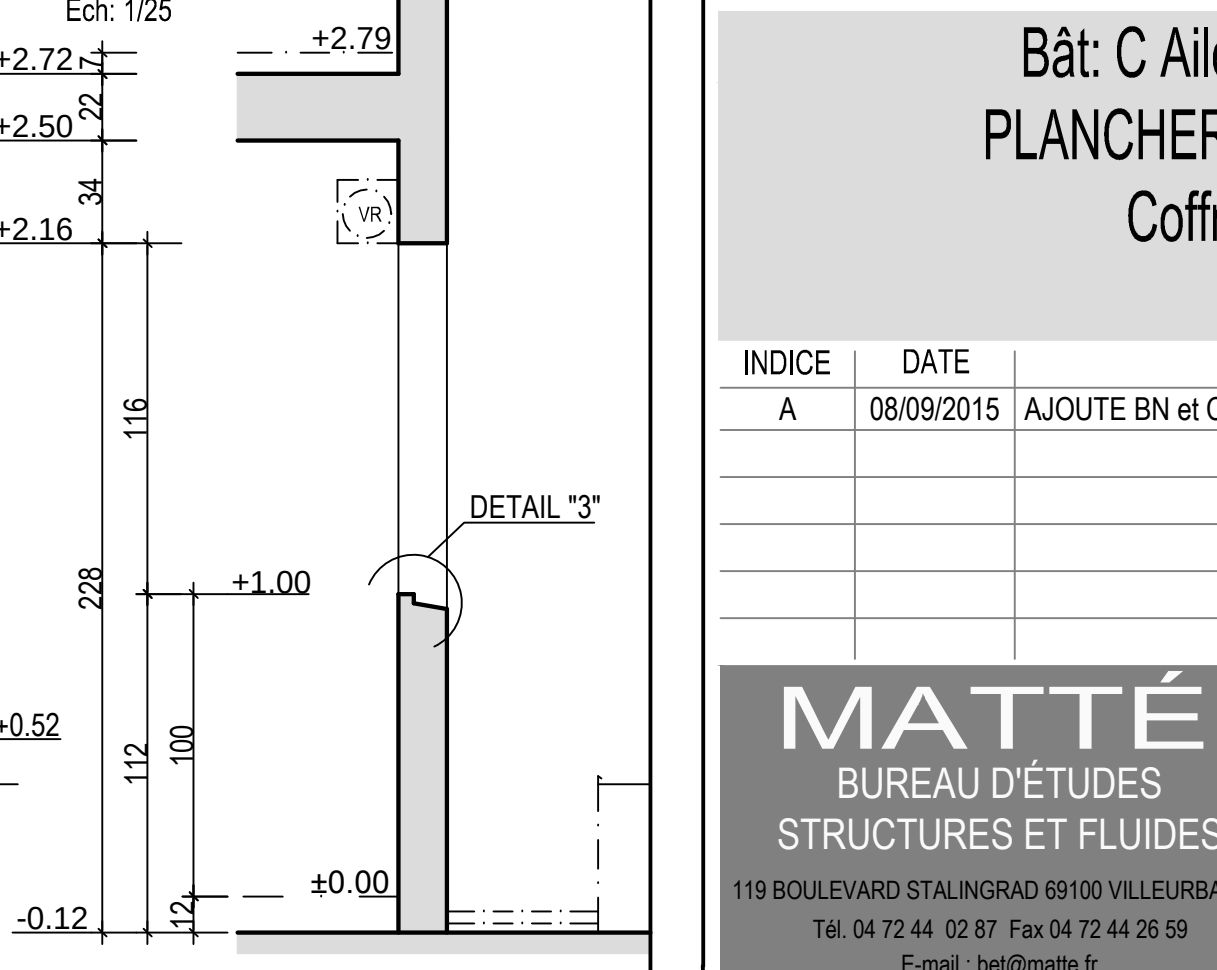


±0.00 = 204.45 = NIVEAU FINI du REZ de CHAUSSEE Bât: C

DALLES

1 FINI: +2.79=207.24
DALLE BA Epr: 22 cm
DESSUS BRUT: +2.72
RESERVE: 7 cm

2 FINI: +2.79=207.24
DALLE BA Epr: 22 cm
DESSUS BRUT: +2.72
RESERVE: 7 cm

3 FINI: +3.01=207.46
DALLE BA Epr: 22 cm
DESSUS BRUT: +2.72
RESERVE: 29 cm

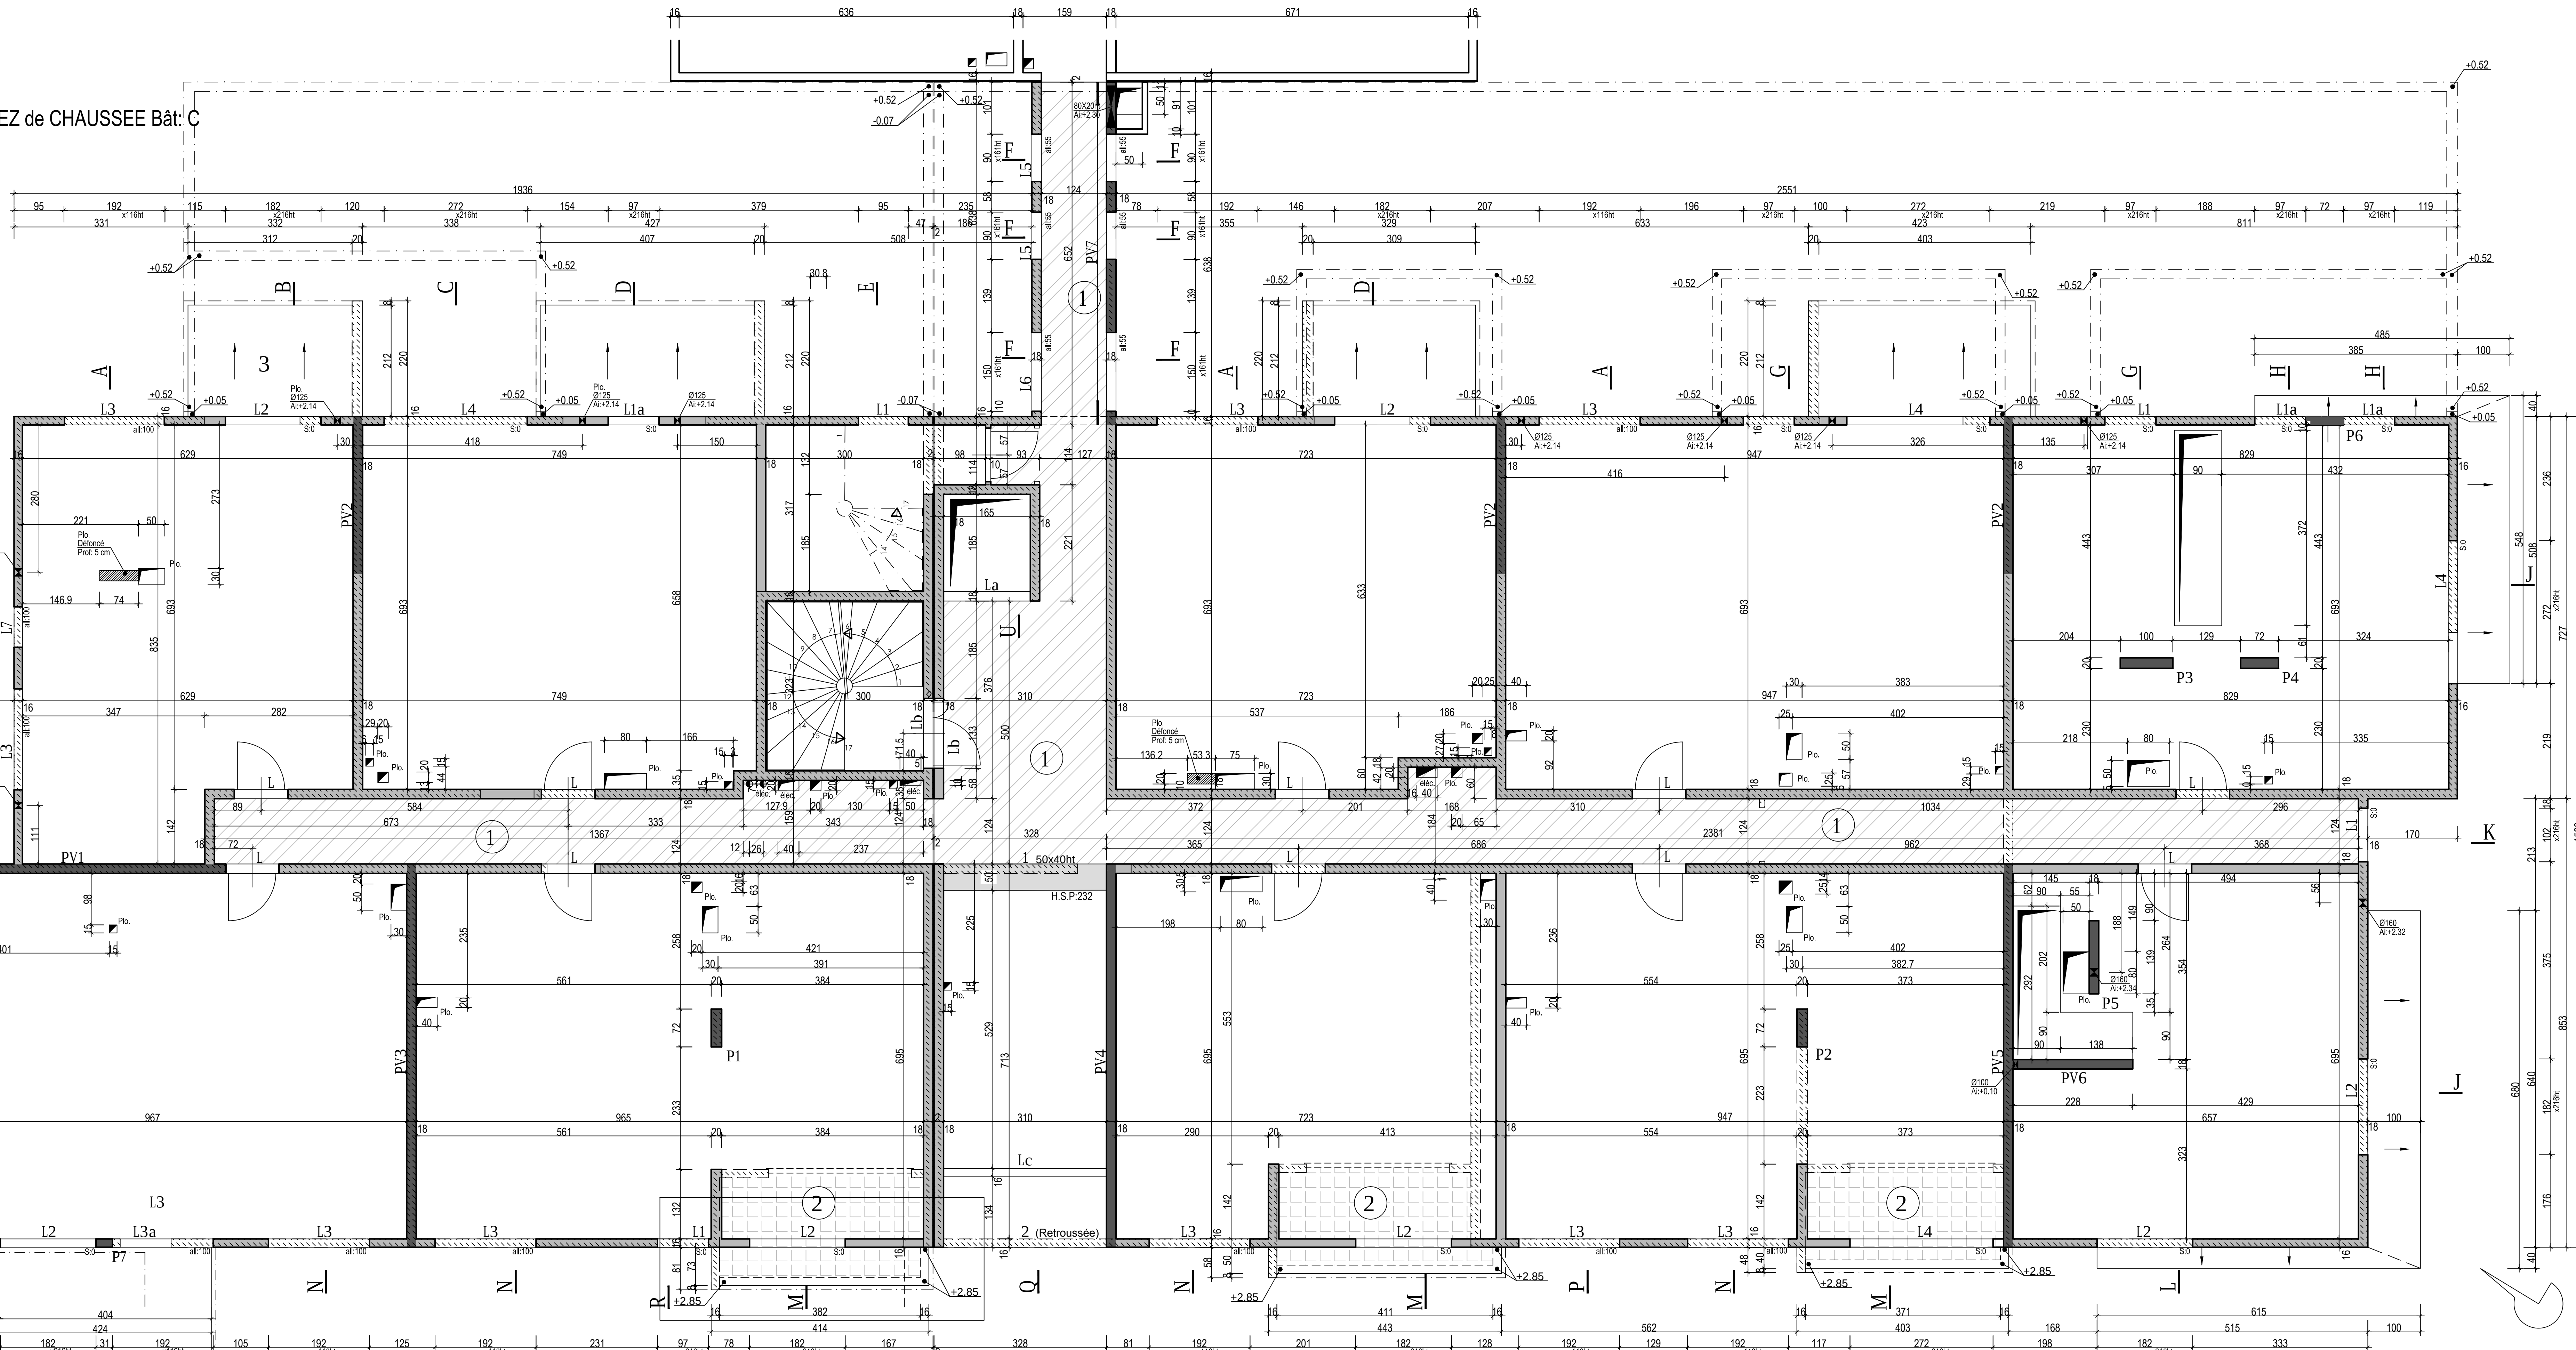

NOAHO

Chemin de Fontanière - 69350 La Mulatière

Création de logements

Les entreprises réalisant les travaux devront tenir compte des derniers plans architectes lors de la réalisation des travaux. Les plans de la MATTE ne doivent servir qu'à des coupes d'éléments constructifs et doivent être des plans d'exécution.

ARCHITECTES: Atelier DTS
SET STRUCTURE: MATTÉ SAS
RET FLUIDES: PRELEM
ECONOMISTE: EXECO
BUREAU DE CONTRÔLE: BUREAU VERITAS

MOULOURE: PSD Ingénierie
CSPS: SUD EST COORDINATION
OPC: ENTREPRISES: Fontanel-pbc

Bât: C Aile OUEST
PLANCHER SUR REZ
Coffrage

INDEX | DATE | MODIFICATIONS
A | 08/09/2015 | AJOUTE BN et COMPLETE REFERAGE

MATTÉ
BUREAU D'ETUDES
STRUCTURES ET FLUIDES
119 BOULEVARD STALINGRAD 69100 VILLEURBANNE
Tel: 04 72 44 12 87 Fax: 04 72 44 28 59
E-mail: matt@matte.fr

Dessiné par: JBO
Contrôlé par: S.BARRIERE
Echelle: 1/50'

DOE

Contraintes de sol 8 bars ELS

Aciers HA (T) FeE500

Aciers Dux (B) FeE 235

Aciers TS FeE 500

Barres t28 >= 239Pa

Enrobage: 3 cm

PLAN N°
C28 A
DATE: 31/08/2015

Affaire N°
13.12.119