

NOAHO

Chemin de Fontanière - 69350 La Mulatière

Création de logements

Les entreprises réalisant les travaux devront tenir compte des derniers plans architecte lors de la réalisation des travaux
Les plans du be MATTE ne doivent servir qu'au corps d'état concerné et doivent être des plans d'exécution.

ARCHITECTE(S): Atelier D'IS
BET STRUCTURE: MATTE SAS
BET FLUIDES: PRELEM
ECONOMISTE: EXECO
BUREAU DE CONTROLE: Bureau VERITAS

MO DELEGUE:
MOE: PSO Ingénierie
CSPS: SUD EST COORDINATION
OPC:
ENTREPRISE(S): Fontanel-pbc

Bât: C Aile OUEST
BA au REZ

DOE

Contrainte de sol: 8 bars ELS

Aciers HA (T) FeE500

Aciers Doux (Ø) FeE 235

Aciers TS FeE 500

Béton fc28 >= 25MPa

Enrobage = 3 cm

PLAN N°
C29 0

DATE : 07/09/2015

MATTÉ
BUREAU D'ÉTUDES
STRUCTURES ET FLUIDES

119 BOULEVARD STALINGRAD 69100 VILLEURBANNE

Tél. 04 72 44 02 87 Fax 04 72 44 26 59

E-mail : bet@matte.fr

Dessiné par : J.BO

Contrôlé par : P.LIN

Echelle : 1/50°

Affaire N°
13.12.119

MURS EXTERIEURS

ANGLES MURS


ARMATURES TETES DE MURS

et OUVERTURES

(VALABLE 68 fois)

(VALABLE 10 fois)

(VALABLE 68 fois)

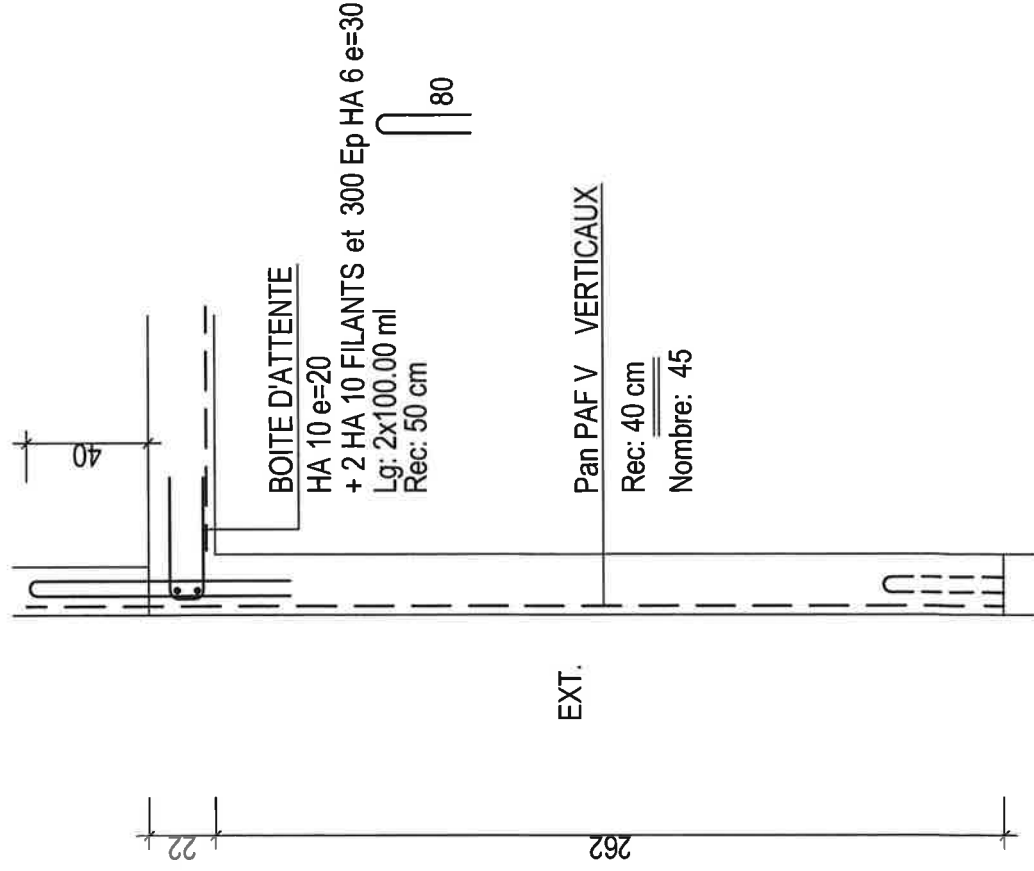

EXT.

Pan PAF V VERTICAUX

Rec: 40 cm

Nombre: 45

BOITE D'ATTENTE

HA 10 e=20

+ 2 HA 10 FILANTS et 300 Ep HA 6 e=30

Lg: 2x100.00 ml

Rec: 50 cm

BOITE D'ATTENTES

HA 6 e=25

2 HA 10 x 325

11 Ep HA 6 x

$$\frac{1}{e} = 25$$

40

12[

2 HA 10 x 325

13 Ep HA 6 x

$$e = 25$$


40

9

ARMATURES REJINGOT

(VALABLE 2 fois)

A COUPER SUIVANT OUVERTURES

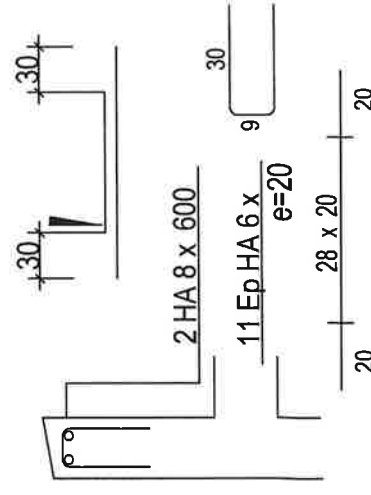

BOITE D'ATTENTES

HA 6 e=25

 $+ 2\text{HA} 10 \times 325$

2 HA 8 x 600

11 EpHA6x

$$\frac{e}{e} = 20$$

30

9

28 x 20



20

20


MURS INTERIEURS AVEC CONTINUITE

ARMATURES TETES DE MURS


30.00 ml Env:

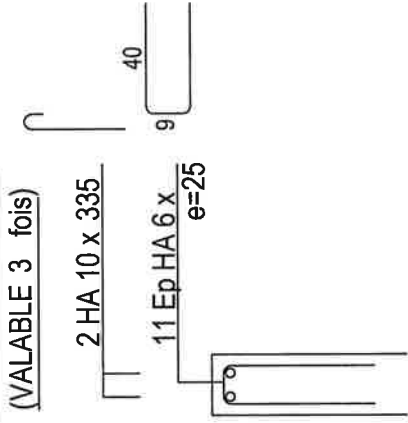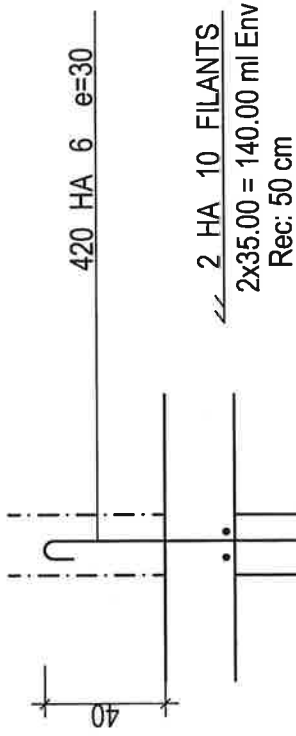

ANGLES MURS

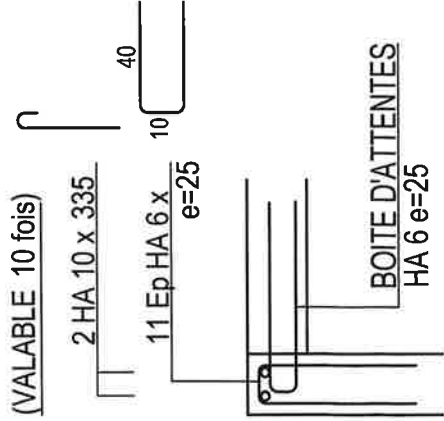


(VALABLE 8 fois)

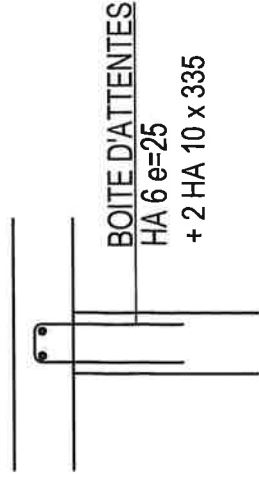

AFF: S.13.12.119	Bât: C	LA MULATIERE-69350 LaMulatiere CREATION de LOGEMENTS	BA au REZ Aile OUEST	Plan n° C 29	Page: 3
MURS INTERIEURS SANS CONTINUEITE 18 U HA 6 e=30 2 HA 10 x 600 10 50 45 17x30 45 (VALABLE 4 fois)					

AFF: S.13.12.119	Bât: C	LA MULATIERE-69350 La Mulatière CREATION de LOGEMENTS	BA au REZ Aile OUEST	Plan n° C 29	Page: 4
PV1 Nombre: 1	E1a		E1		

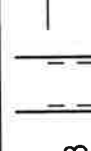
AFF: S.13.12.119	Bât: C	LA MULATIERE-69350 La Mulatière CREATION de LOGEMENTS	BA au REZ Aile OUEST	Plan n° C 29	Page: 5
PV2 Nombre: 3		E2a 2 HA 10 2 HA 8 15 U HA 8 Pan ST15C A COUPER Rec: 40 cm Nombre: 1.5		E2a	E2 BOITE D'ATTENTE HA 8 e=20 + 2 HA 10 x 325

AFF: S.13.12.119	Bât: C	LA MULATIERE-69350 La Mulatière CREATION de LOGEMENTS	BA au REZ Aile OUEST	Plan n° C 29	Page: 6
PV3 Nombre: 1		E3a		E3a	
E3		E3		E3	
E3		E3		E3	
E3		E3		E3	
E3		E3		E3	
E3		E3		E3	
E3		E3		E3	
E3		E3		E3	
E3		E3		E3	

PV4

Nombre: 1

E4a

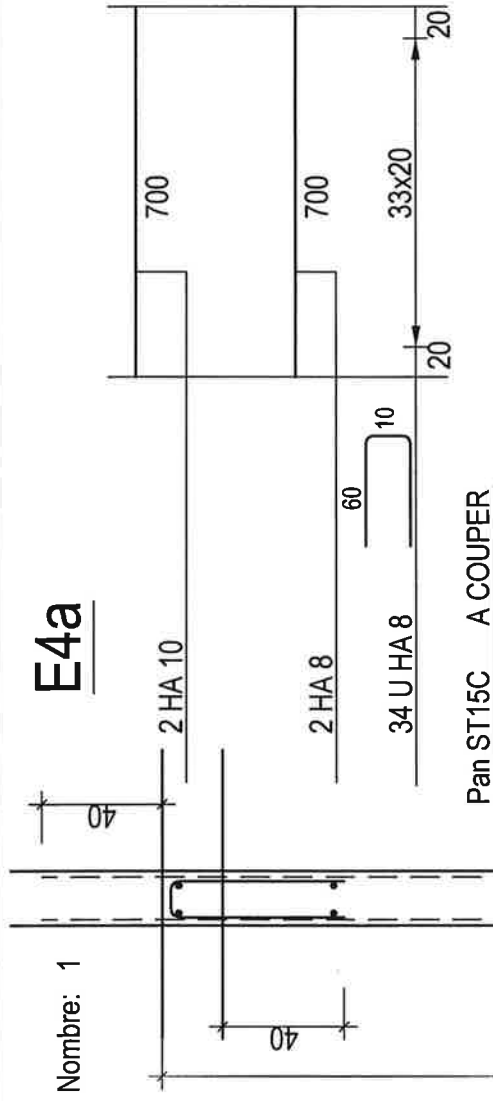

Pan ST15C A COUPER

Rec: 40 cm


Nombre: 2.5

Pan ST25C

Rec: 40 cm

Nombre: 2.5

4.

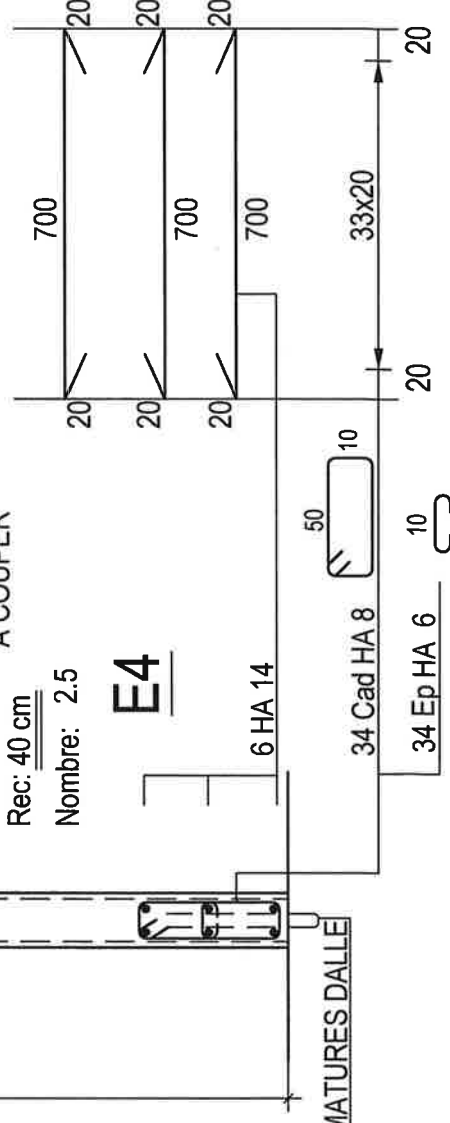

VOIR ARMATURES DALLE

6 HA 14

34 Cad HA 8


34 Ep HA 6 $\frac{10}{}$

BOITE D'ATTENTE

$$\text{HA } 8 \text{ e}=20$$

$$+ 2 \text{ HA } 10 \times 325$$

ELEVATION

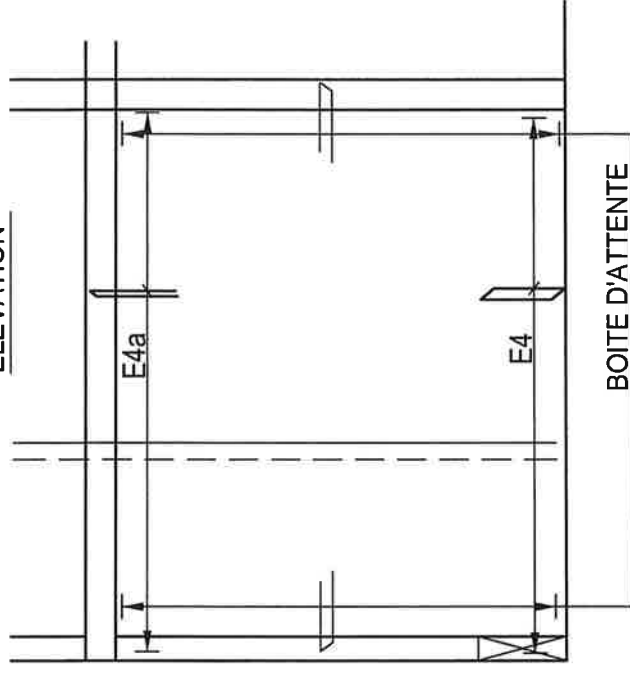


AFF: S.13.12.119	Bât: C	LA MULATIERE-69350 La Mulatiere CREATION de LOGEMENTS	BA au REZ Aile OUEST	Plan n° C 29	Page: 9
PV6 Nombre: 1		E6a			


AFF: S.13.12.119	Bât: C	LA MULATIERE-69350 La Mulatière CREATION de LOGEMENTS	BA au REZ Aile OUEST	Plan n° C 29	Page: 10
PV7 Nombre: 1 E7a E7 Pan ST15C A COUPER Rec: 40 cm Nombre: 1.5 Pan ST25C A COUPER Rec: 40 cm Nombre: 1.5 VOIR ARMATURES DALLE DANS MONOS entre OUVERTURES					

AFF: S.13.12.119	Bât: C	LA MULATIERE-69350 LaMulatiere CREATION de LOGEMENTS	BA au REZ Aile OUEST	Plan n° C 29	Page: 11
P1 Nombre: 1 20x72	P2 Nombre: 1 20x72				
①	②	③	④	⑤	⑥
8 HA 12 x		15 HA 6 x	2x15 HA 6 x		
⑦	⑧	⑨	⑩	⑪	⑫
⑬	⑭	⑮			

AFF: S.13.12.119	Bât: C	LA MULATIERE-69350 LaMulatiere CREATION de LOGEMENTS	BA au REZ Aile OUEST	Plan n° C 29	Page: 12
P3 Nombre: 1 20x100					
1				10 HA 12 x	C 330
2					
3				15 HA 6 x	94 12
4				3x15 HA 6 x	12
5					
6					
7					
8					
9					
10					
11					
12					
13					
14					
15					

AFF: S.13.12.119	Bât: C	LA MULATIERE-69350 LaMulatiere CREATION de LOGEMENTS	BA au REZ Aile OUEST	Plan n° C 29	Page: 13
P4 Nombre: 1 20x72					
				8 HA 12 x	C 270
				15 HA 6 x	66 12
				2x15 HA 6 x	12

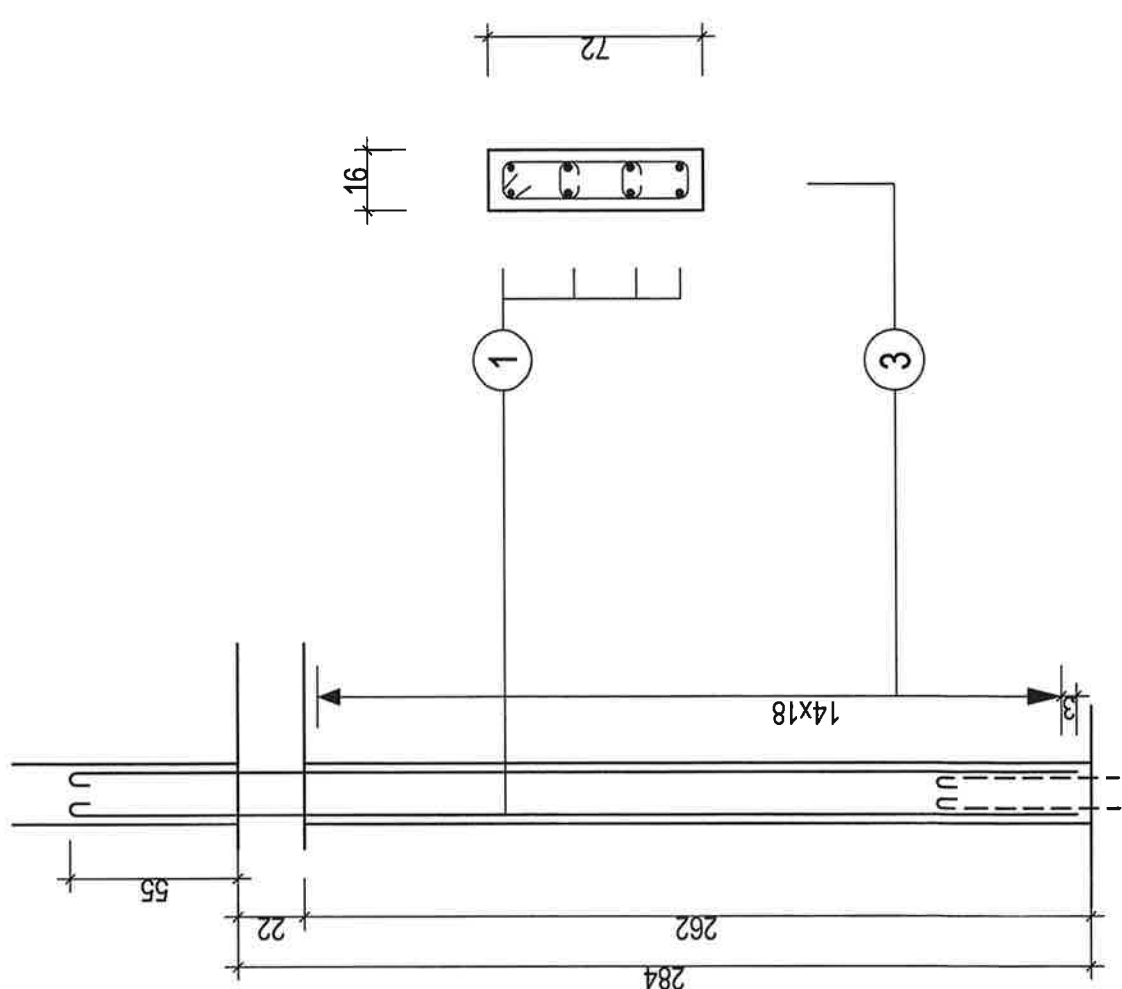AFF: S.13.12.119		Bât: C	LA MULATIERE-69350 LaMulatiere CREATION de LOGEMENTS		BA au REZ Aile OUEST	Plan n° C 29	Page: 15
P6 Nombre: 1 16x72 					①	8 HA 12 x	330
					②		
					③	15 HA 6 x	66 10
					④	2x15 HA 6 x	10
					⑤		
					⑥		
					⑦		
					⑧		
					⑨		
					⑩		
					⑪		
					⑫		
					⑬		
					⑭		
					⑮		

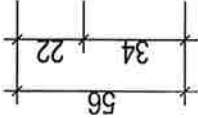
AFF: S.13.12.119	Bât: C	LA MULATIERE-69350 LaMulatiere CREATION de LOGEMENTS	BA au REZ Aile OUEST	Plan n° C 29	Page: 17
L Nombre: 10  4 HA 10 5 Cad HA 6 20 135 20 28 4x20 27 30 10  4 HA 12 9 Cad HA 6 20 194 20 17 8x20 17 30 12  4 HA 10 7 Cad HA 6 20 165 20 22 6x20 23 30 12					
LC Nombre: 1  2 HA 10 2 HA 16 16 Cad HA 8 56 22 34 20 340 20 20 15x20 20 50 10					
Lb Nombre: 1  4 HA 10 7 Cad HA 6 20 165 20 22 6x20 23 30 12					

AFF: S.13.12.119	Bât: C	LA MULATIERE-69350 LaMulatiere CREATION de LOGEMENTS	BA au REZ Aile OUEST	Plan n° C 29	Page: 18
LINTEAUX					
L1 Nombre: 6 PORTEE: 97	L3 Nombre: 9 PORTEE: 192	L7 Nombre: 2 PORTEE: 77			
2 HA 10	2 HA 10	2 HA 10	2 HA 10		
2 HA 10	2 HA 16	2 HA 10	2 HA 10		
5 Cad HA 6	10 Cad HA 6	4 Cad HA 6			
20 / 140 20 30 4x20 30	20 / 225 20 22 9x20 23	20 / 110 20 25 3x20 25	28 10	28 10	
34 22					
28 10	28 10	28 10			
L1a Nombre: 3 PORTEE: 97	L2 Nombre: 7 PORTEE: 182	L3a Nombre: 1 PORTEE: 182			
4 HA 10	2 HA 10	2 HA 10	2 HA 10		
2 HA 14	2 HA 16	2 HA 16	2 HA 16		
14 Cad HA 6 + 14 Ep HA 6	10 Cad HA 6 + 10 Ep HA 6	10 Cad HA 6 + 10 Ep HA 6	10 Cad HA 6 + 10 Ep HA 6		
20 / 140 20 30 4x20 30	20 / 215 20 17 9x20 18	20 / 225 20 22 9x20 23	28 10	28 10	
34 22					
28 10	28 10	28 10			
50 10	50 10	50 10			


AFF: S.13.12.119	Bât: C	LA MULATIERE-69350 LaMulatiere CREATION de LOGEMENTS	BA au REZ Aile OUEST	Plan n° C 29	Page: 19
LINTEAUX					
L5		Nombre: 2 PORTEE: 90	L6	Nombre: 1 PORTEE: 150	2 HA 10 2 HA 10 14 Cad HA 6 2 HA 10 2 HA 14 8 Cad HA 6 R1 Nombre: 3 Rec: 50 cm 28 Cad HA 8 28 U HA 8 60 15 BOITE D'ATTENTE HA 8 e=20

C	L4 (3 p)	Béton=0.22 m3 Adier=27.1 kg d=122.3 kg/m3 Fi=8.4 mm Cof=2.9 m²	Eb=3.0 cm Eh=6.0 cm El=4.0 cm	1 1
- Date 06/07/15 - 10 étages -				
Section : 16 x 56ht				
fck= 25 MPa fyk= 500 MPa				
Coupe feu R 120				

Elévation
Echelle=1/20

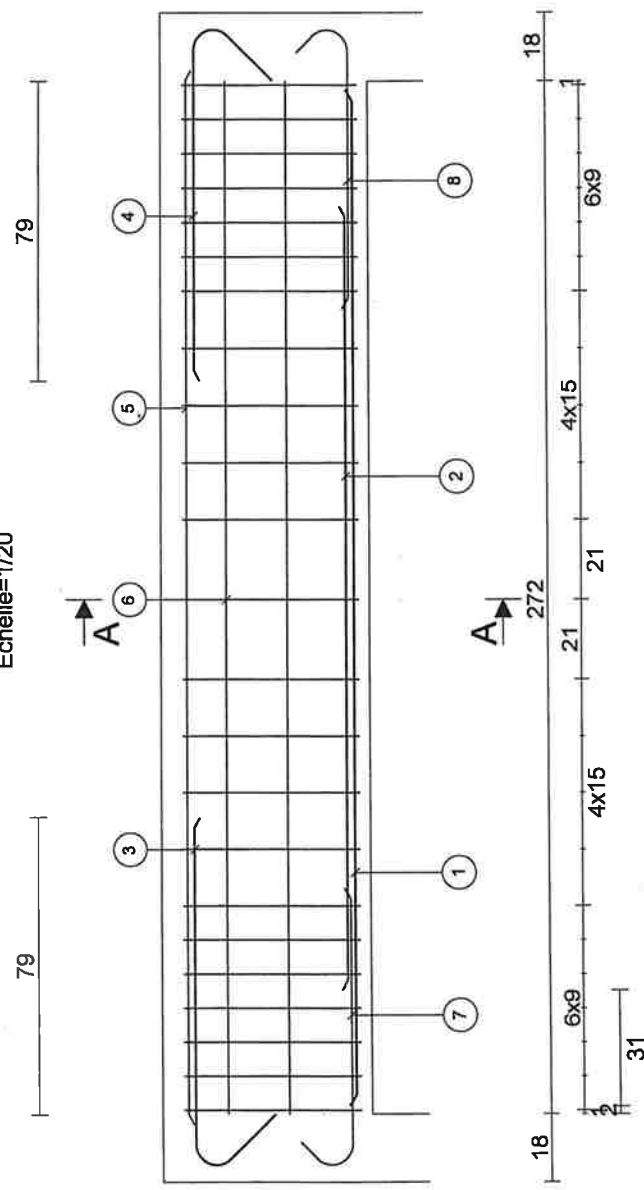


Coupe A-A
Echelle=1/20

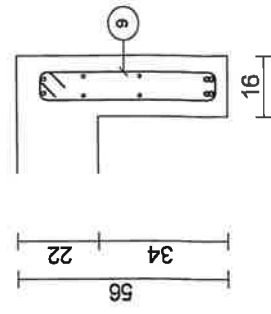


Barre	Lg	Forme
1 2HA12	268	268
2 2HA10	207	207
3 2HA10	116	93 135°
4 2HA10	116	93 135°
5 2HA10	278	278
6 4HA8	272	272
7 2HA12	87	87
8 2HA12	87	87
9 23HA6	120	120
180°		
c 29		
20/		
Barre	Lg/Poids	
HA6	27.6/6.1	
HA8	10.9/4.3	
HA10	14.3/6.8	
HA12	8.8/7.8	

Elévation
Echelle=1/25

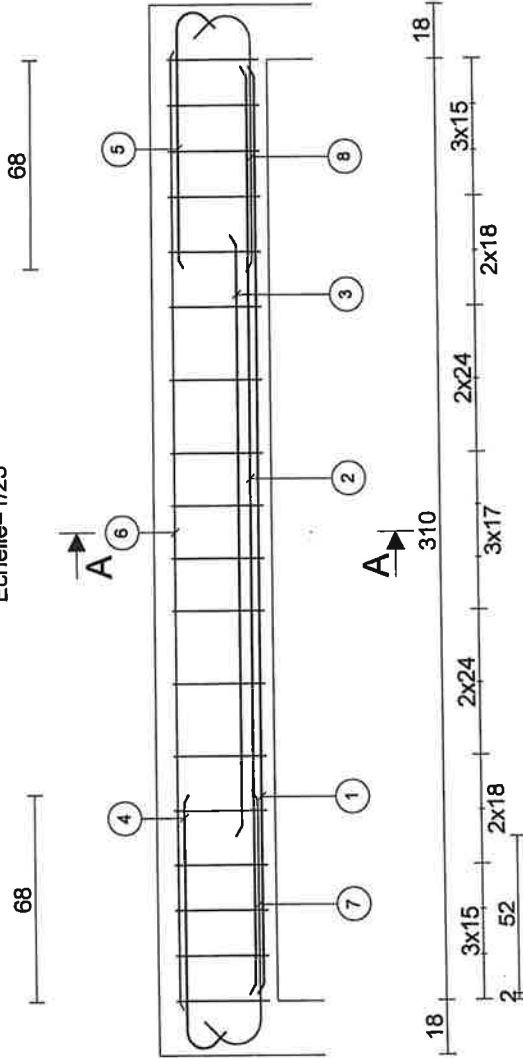


Coupe A-A
Echelle=1/10

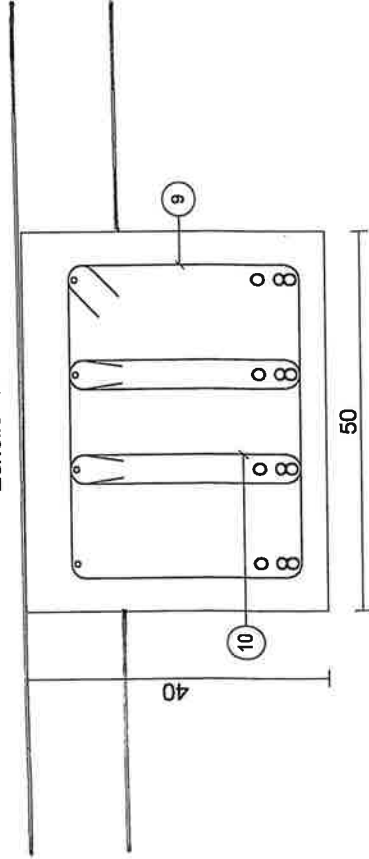


Barre		Lg	Forme
1	4HA14	306	 306
2	4HA14	306	 306
3	4HA14	199	 199
4	4HA10	96	 84 135°
5	4HA10	96	 135° 84
6	4HA8	316	 316
7	4HA14	102	 135° 85
8	4HA14	102	 85 135°
9	18HA8	156	 42
10	36HA8	81	 31
180°			
c29			
21/			
Barre		Lg/Poids	
HA8		69.9/27.6	
HA10		7.7/4.8	
HA14		40.6/49.1	

Elévation
Echelle=1/25

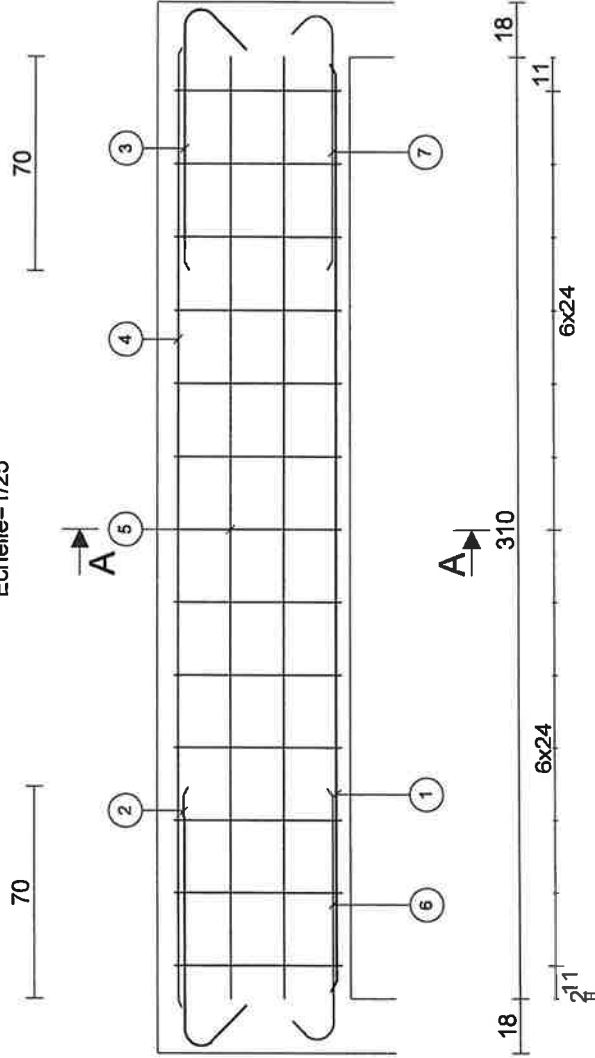


Coupe A-A
Echelle=1/20

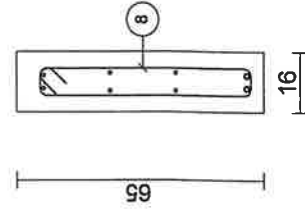

Barre	Lg	Forme
1 2HA14	306	306
2 2HA10	109	86 135°
3 2HA10	109	135° 86
4 2HA8	316	316
5 4HA8	310	310
6 2HA12	97	135° 84
7 2HA12	97	84 135°
8 13HA8	138	8
180° C29		
Barre		Lg/Poids
HA8		36.6/14.5
HA10		4.4/2.7
HA12		3.9/3.4
HA14		6.1/7.4

fck= 25 MPa f_{yk}= 500 MPa

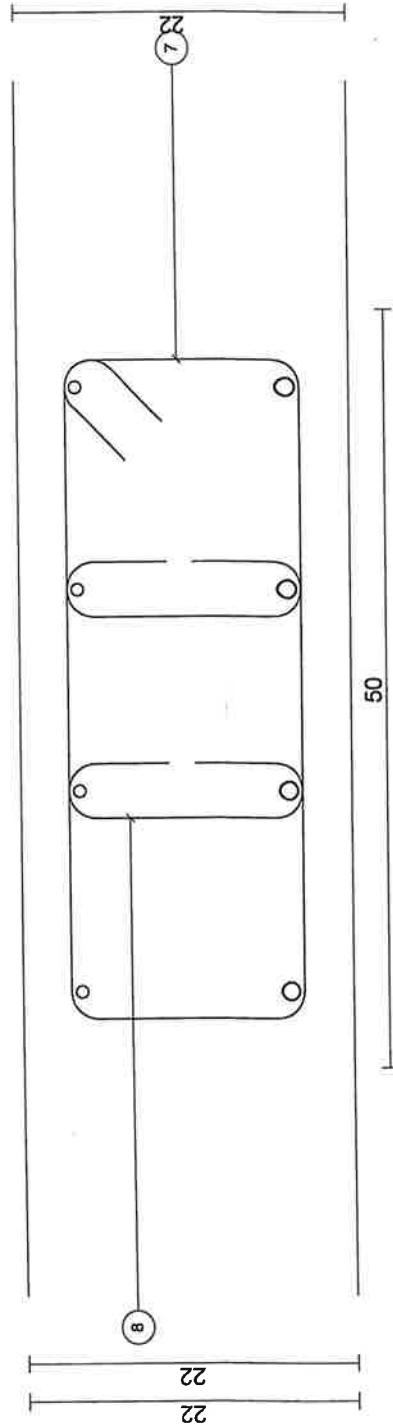
[illegible]

- Date 06/07/15 - 10 étages -


Section : 50 x 22ht

fck= 25 MPa fyk= 500 MPa

Elévation
Echelle=1/25

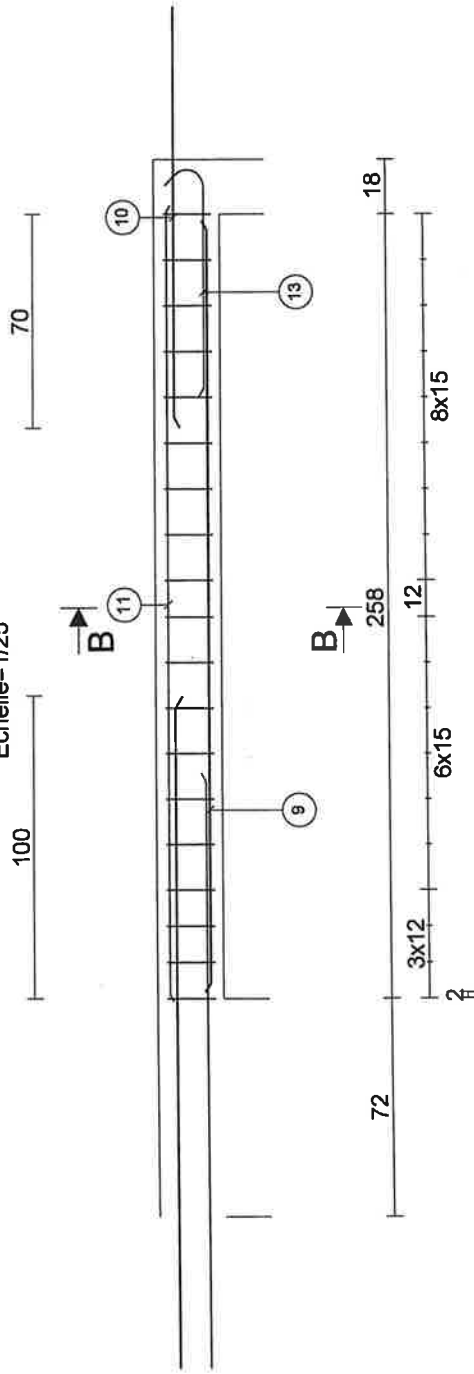

Coupe B-B
Echelle=1/5

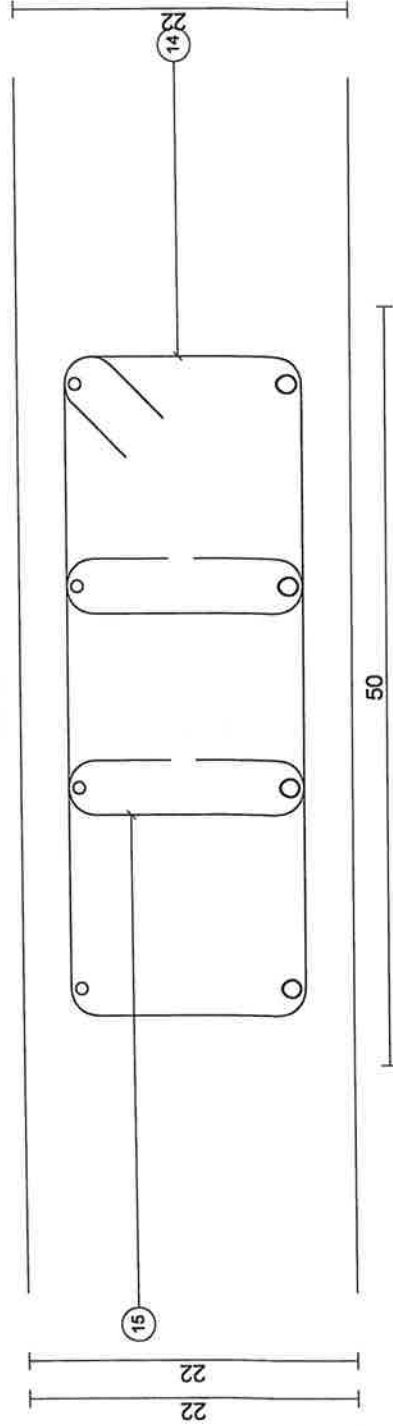


Barre	Lg	Forme
9	4HA12	254
10	4HA12	158
11	4HA8	262
13	4HA12	87
14	19HA6	130
15	38HA6	33
75 135° 44 16		
180° 229		
Barre	Lg/Poids	
HA6	37.3/8.3	
HA8	10.5/4.1	
HA12	20.0/17.7	

- Date 06/07/15 - 10 étages -
Section : 50 x 22ht


fck= 25 MPa fyk= 500 MPa

Barre	Lg	Forme
1	4HA14	254
2	4HA12	153
3	4HA12	158
4	4HA8	264
5	4HA12	142
6	4HA12	88
7	23HA6	130
8	46HA8	33
180 0229 25/		
Barre	Lg/Poids	
HA6	29.9/6.6	
HA8	25.9/10.2	
HA12	21.6/19.2	
HA14	10.2/12.3	


Elévation
Echelle=1/25

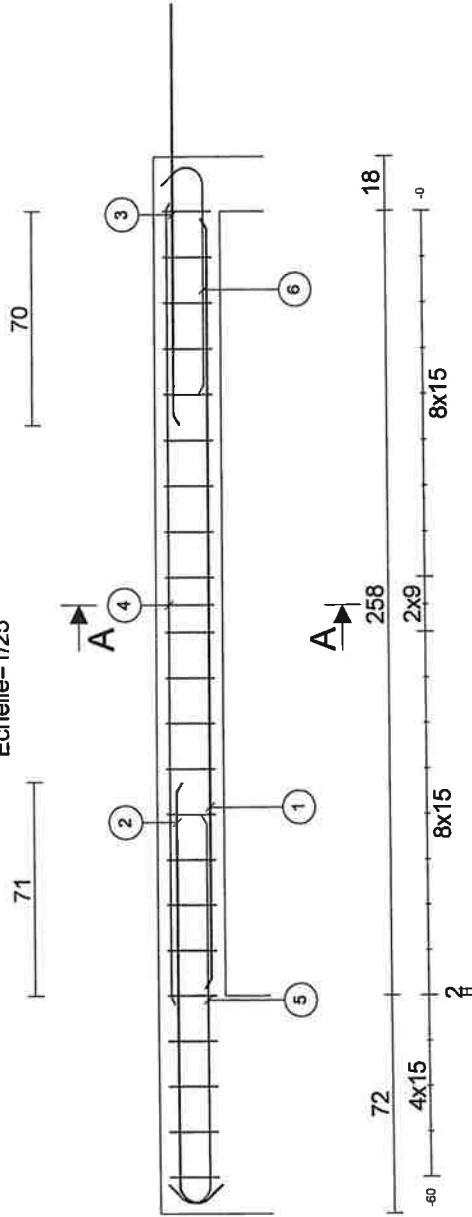


Coupe A-A
Echelle=1/5

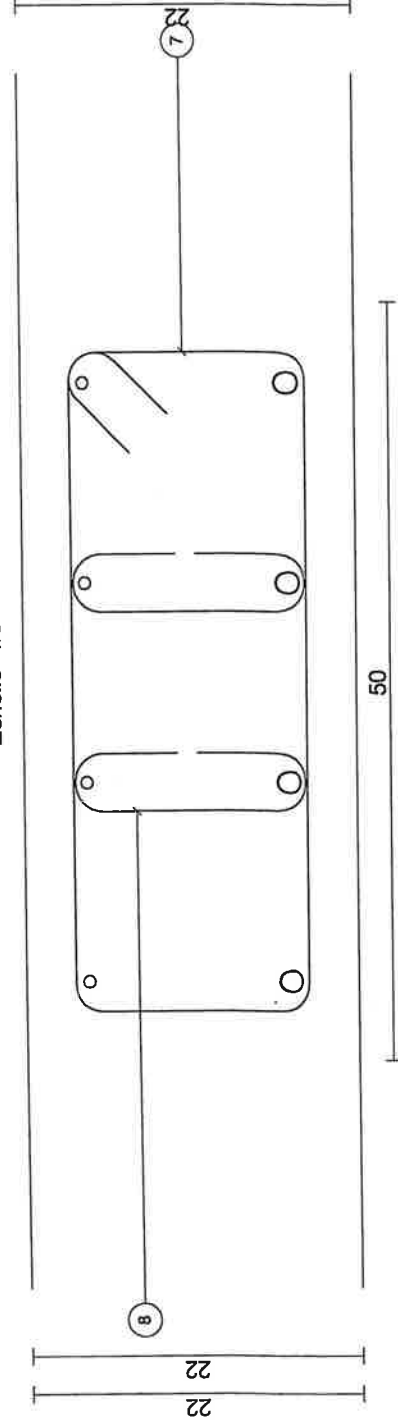

Bn4		Bn4	Béton=0.38 m ³ Acier=25.2 kg d=65.8 kg/m ³ Fi=10.9 mm Cof=0.4 m ²	Eb=3.0 cm Eh=3.0 cm El=3.0 cm	1 3
- Date 06/07/15 - 10 étages - Section : 20 x 22ht					
fck= 25 MPa fyk= 500 MPa					

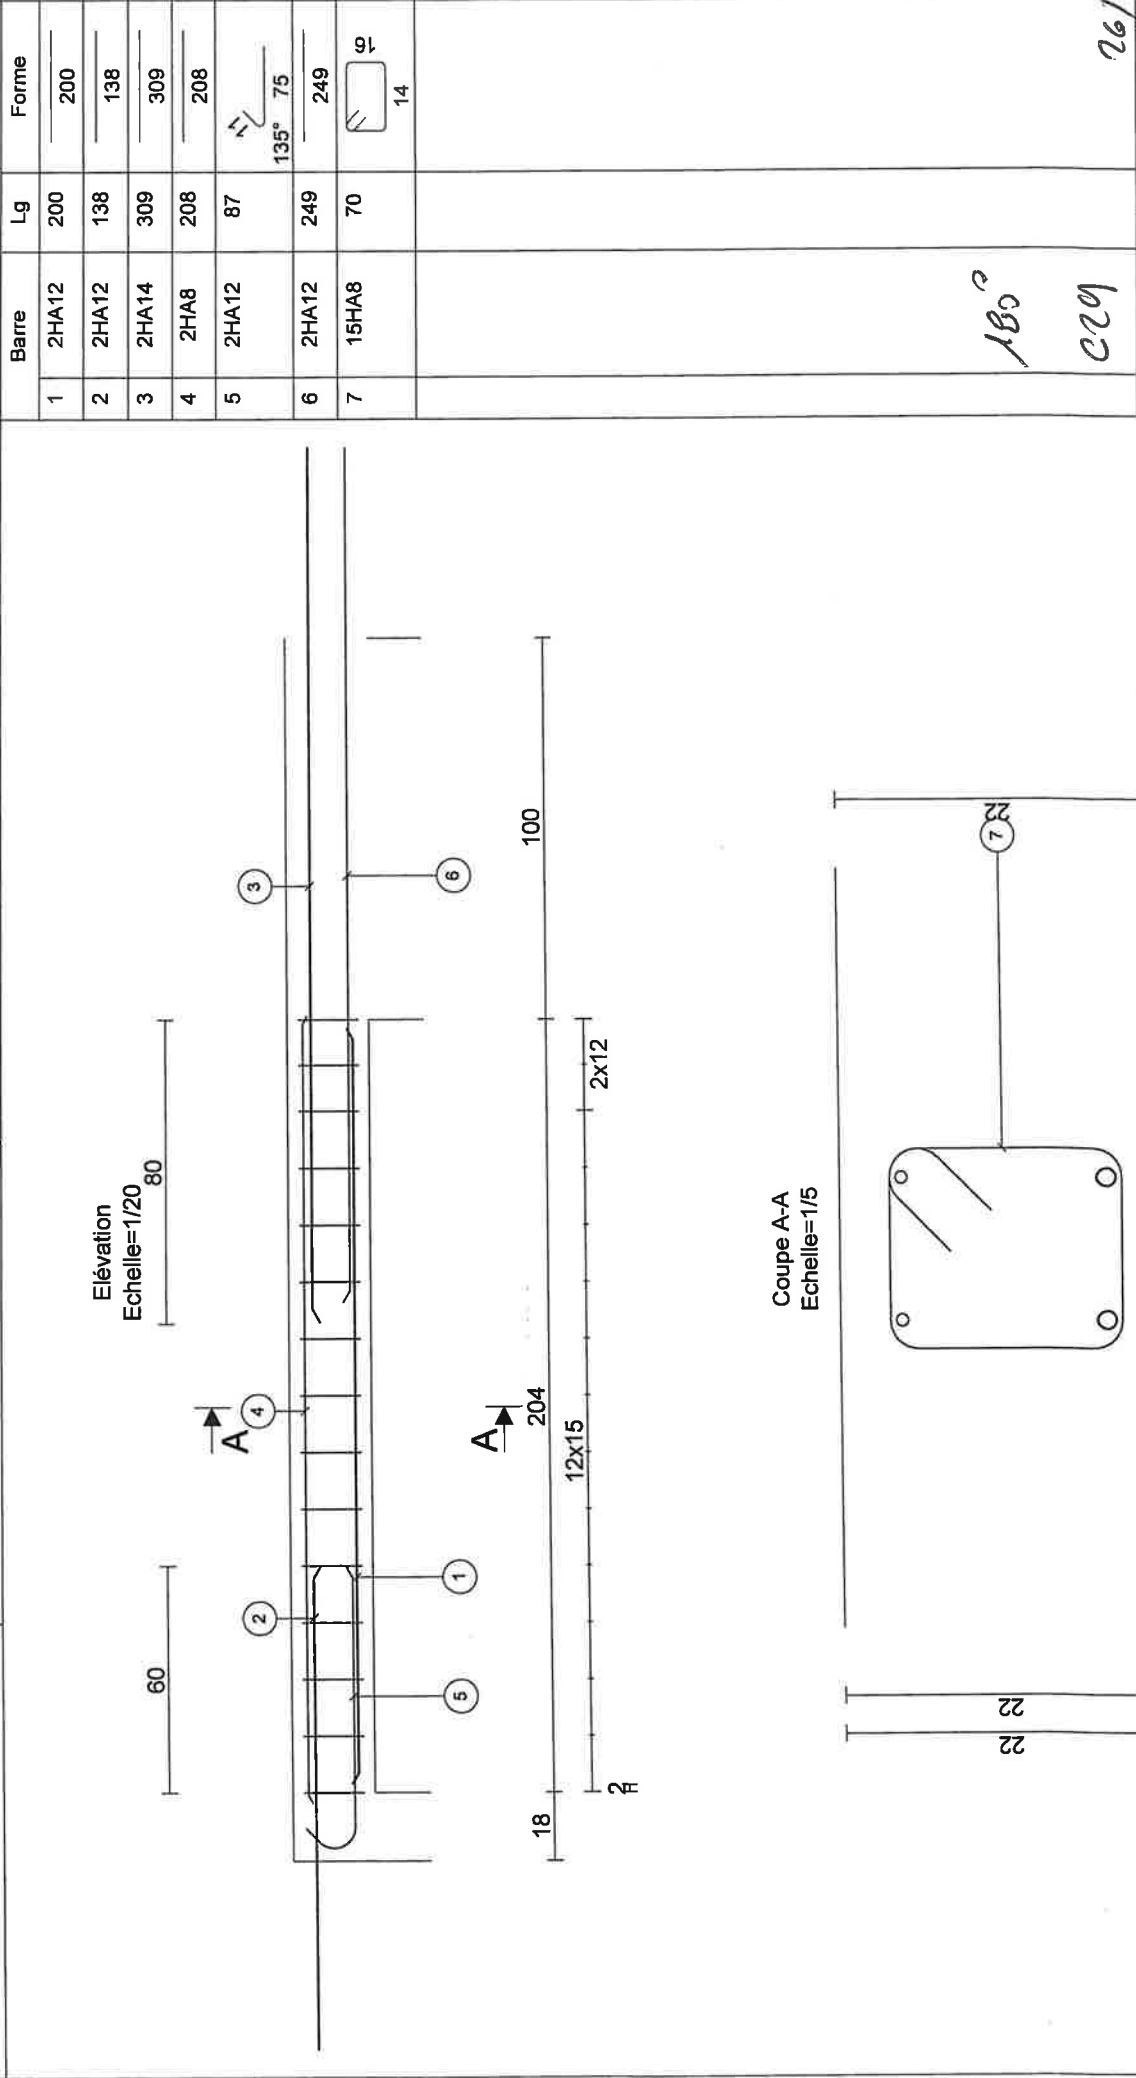

Bn4	Bn5	Béton=0.24 m ³ Acier=27.8 kg d=17.4 kg/m ³ Fi=13.5 mm Cof=0.3 m ²	Eb=3.0 cm Eh=3.0 cm El=3.0 cm	2 3
- Date 06/07/15 - 10 étages -				
Section : 20 x 22ht				
fck= 25 MPa fyk= 500 MPa				

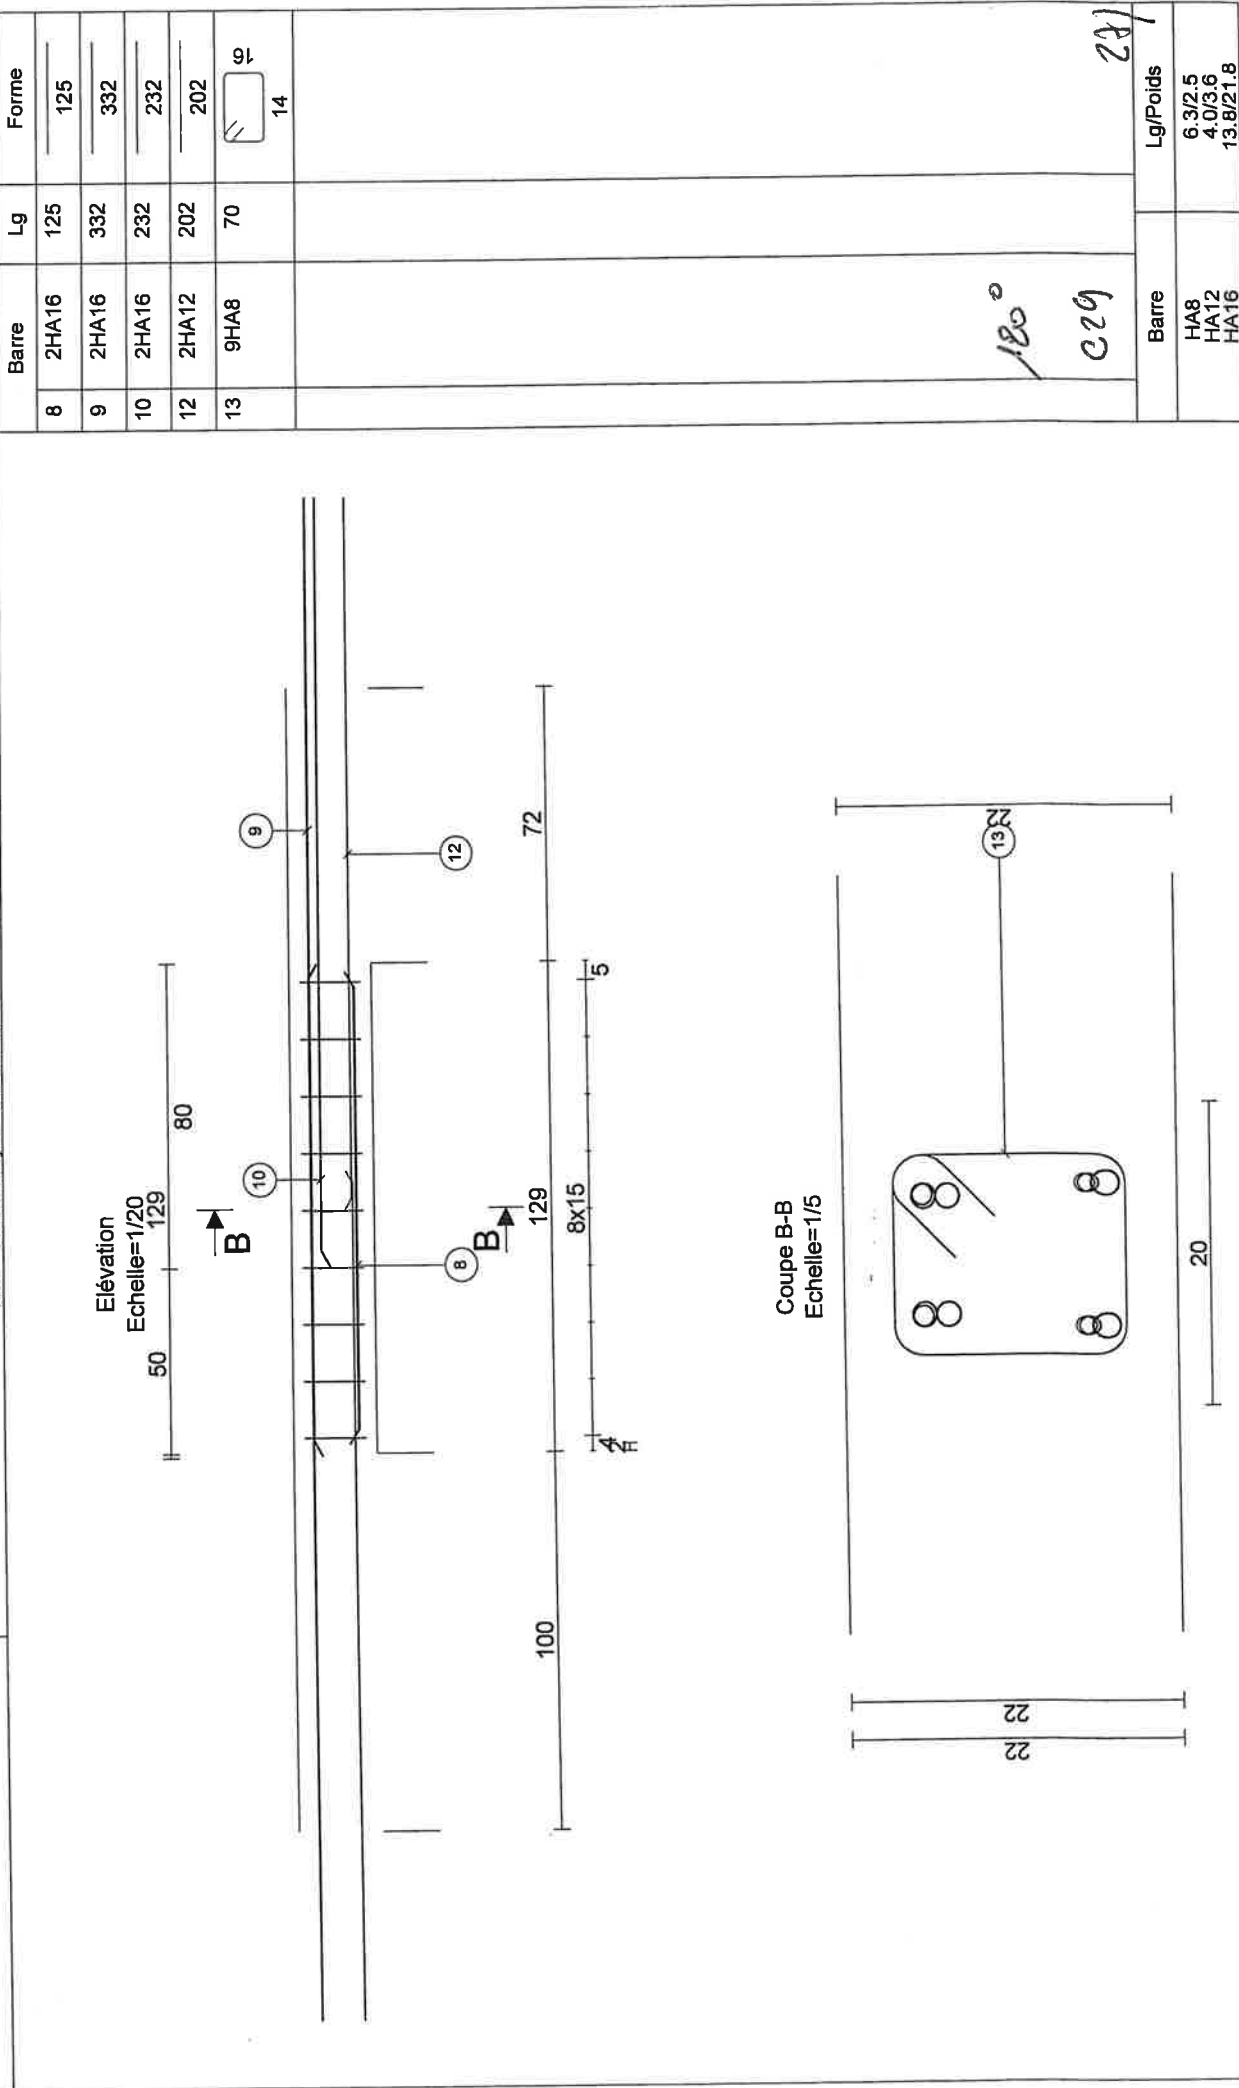

Bn4	Bn6	Béton=0.45 m ³ Acier=29.4 kg d=65.5 kg/m ³ F=12.0 mm Cof=0.6 m ²	Eb=3.0 cm Eh=3.0 cm El=3.0 cm	3 3
- Date 06/07/15 - 10 étages - Section : 20 x 22ht fck= 25 MPa fyk= 500 MPa				

