


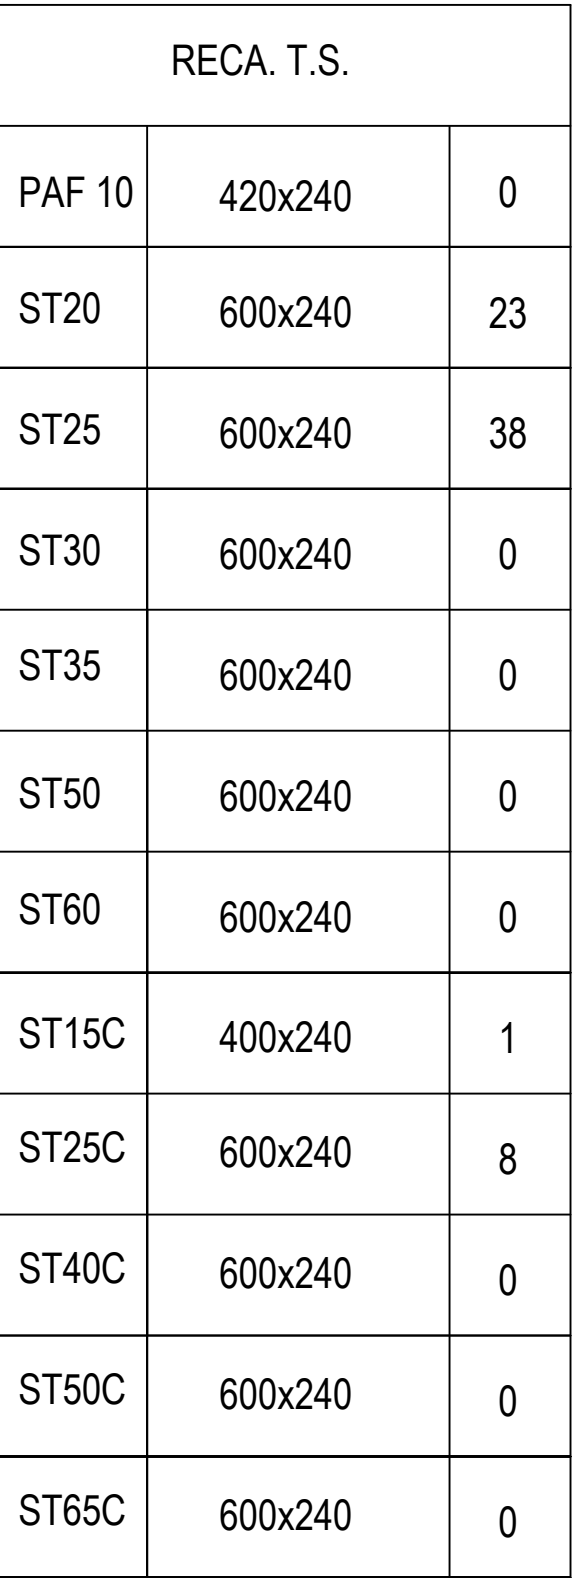

Chemin de Fontanière - 69350 La Mulatière

Création de logements

[illegible]

DOE
Contrainte de sol: 8 bars ELS
Aciers HA (T) FeE500
Aciers Doux (Ø) FeE 235
Aciers TS FeE 500
Béton f_{cd} ≥ 25MPa
Enrobage = 3 cm
N°
0
00/09/2015
Affaire N°
13.12.119