




DETAIL "1"

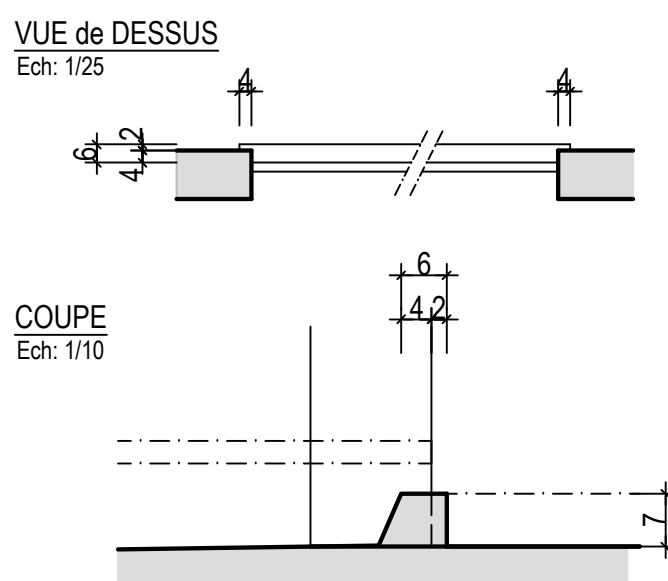

DETAIL "2"

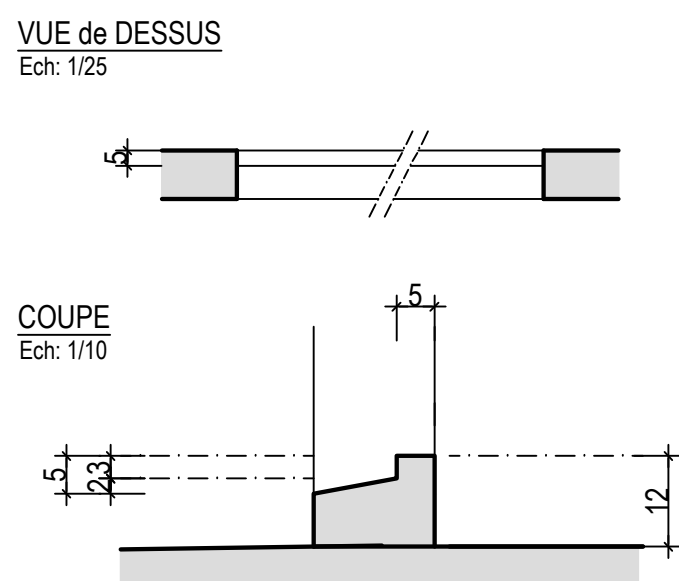

DETAIL "3"

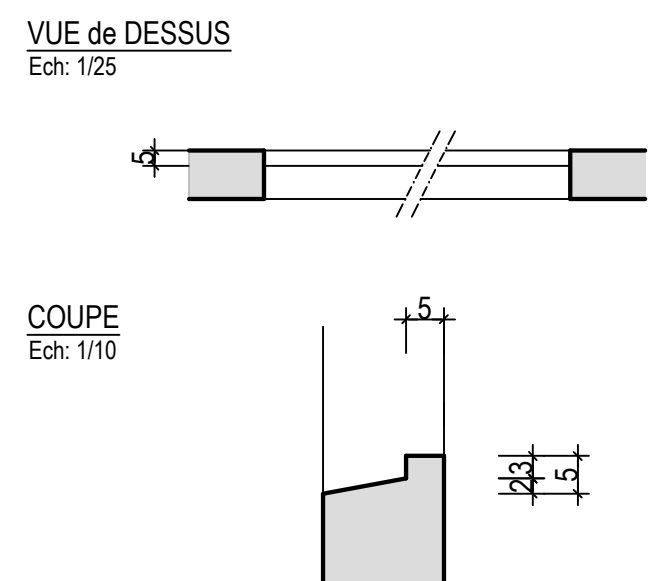


VUE EN PLAN

Ech: 1/50

DALLES

○	FINI: Voir plan TERRASSE DALLE BA Epr: 22 cm DESSUS BRUT: +5.51 RESERVE: 29 ou 49 cm
①	FINI: +6.00=210.45 DALLE BA Epr: 25 cm DESSUS BRUT: +5.51 RESERVE: 49 cm

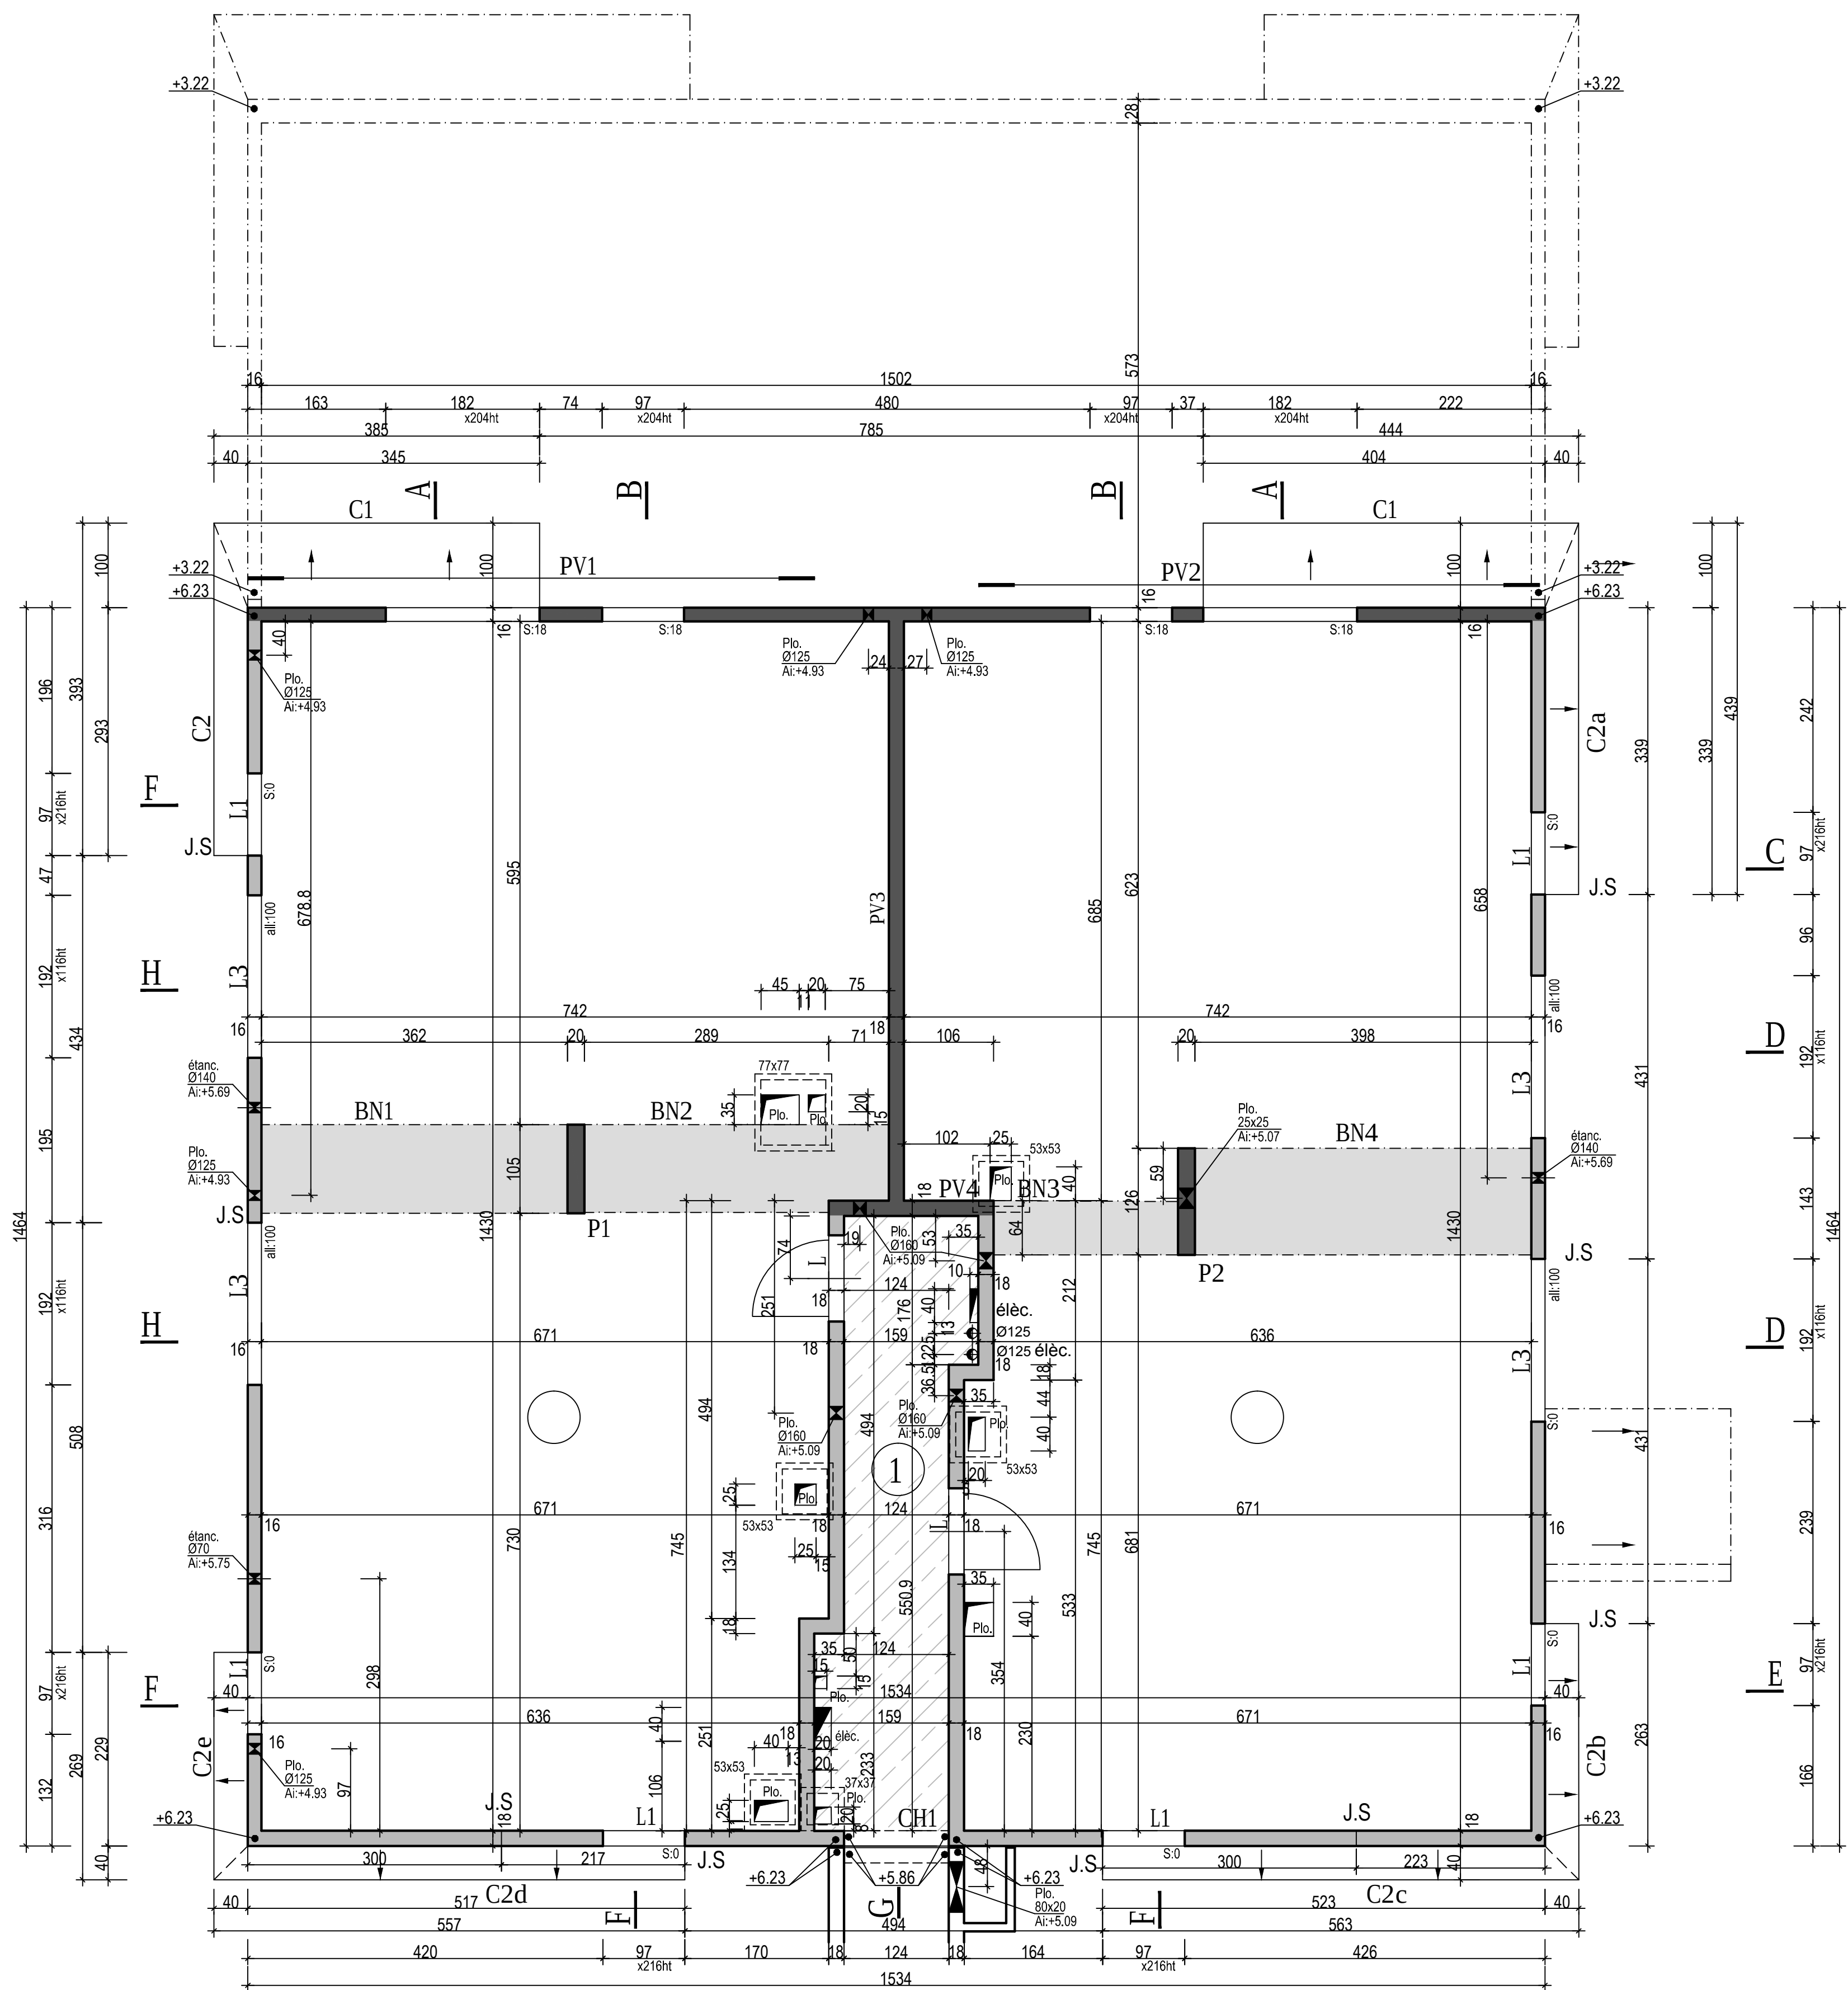

±0.00 = 204.45 = NIVEAU FINI du REZ de CHAUSSEE Bât: C

NOAHO

Chemin de Fontanière - 69350 La Mulatière

Création de logements

Les entreprises réalisant les travaux devront tenir compte des derniers plans architecturaux lors de la réalisation des travaux.
Les plans du SO MATTE ne doivent servir qu'à titre consultatif et doivent être des plans d'exécution.

ARCHITECTES:	Atelier D1S	MO. DELEGUE:	
BET STRUCTURE:	MATTE SAS	MOE:	PSO Ingénierie
BET FLUIDES:	PRELEM	CSPS:	SUD EST COORDINATION
ECONOMISTE:	EXECO	OPC:	
BUREAU DE CONTROLE:	Bureau VERITAS	ENTREPRISES:	Fontanel-gbc

Bât: C Aile EST
PLANCHER SUR +1
Coffrage

DOE

Contrainte de sol: 8 bars ELS

Aciers HA (T) FyE500
Aciers Dux (D) FyE235
Aciers TS FyE500
Béton f28 >= 25MPa
Enrobage = 3 cm

PLAN N°
C32 A
DATE: 31/08/2015

MATTÉ
BUREAU D'ETUDES
STRUCTURES ET FLUIDES
119 BOULEVARD STALINGRAD 69100 VILLEURBANNE
Tel: 04 72 44 02 81 Fax: 04 72 44 26 59
Email: s@matte.fr

Dessiné par: J.B.O.
Contrôlé par: P.LIN
Echelle: 1/150°

Affaire N°
13.12.119