




±0.00 = 204.45 = NIVEAU FINI DU REZ de CHAUSSEE Bât: C

NOAHO

Chemin de Fontanière - 69350 La Mulatière

Création de logements

Les informations relatives aux travaux doivent être conformes aux données plans architecturaux et doivent être les plans d'exécution.

ARCHITECTE: **Alain D'RS**
BETRIER: **MATTE SAS**
BETRIER: **PRELEM**
BETRIER: **ESCECO**
BUREAU DE CONTRÔLE: **Bureau VERITAS**

MOULÉ: **PSO Ingénierie**
CPS: **SUD EST COORDINATION**
ENTREPRENEUR: **Fontanière**

Bât: C Aile OUEST
PLANCHER SUR +1
Coffrage

DOE
Contraintes de sol 8 Bars ELS
Aciers HA (T) FeE500
Aciers Dca Ø1 FeE235
Aciers TS FeE 500
Béton C35/45 = 20MPa
Enrobage = 3 cm

MATTE
BUREAU D'ÉTUDES
STRUCTURES ET FLUIDES
110 Boulevard Stalingrad 69100 VILLEURBANNE
Tél. 04 72 44 12 17 Fax 04 72 44 12 18
E-mail: info@matte.fr

Dessiné par: J.B.O.
Contrôlé par: J.P.N.
Echelle: 1/50'

PLAN N°
C35 A
DATE: 31/08/2015

Affaire N°
13.12.119