

NOAHO

Chemin de Fontanière - 69350 La Mulatière

Création de logements

Les entreprises réalisant les travaux devront tenir compte des derniers plans architecte lors de la réalisation des travaux
Les plans du be MATTE ne doivent servir qu'au corps d'état concerné et doivent être des plans d'exécution.

ARCHITECTE(S):	Atelier D'IS	MO DELEGUE:	
BET STRUCTURE:	MATTE SAS	MOE:	PSO Ingénierie
BET FLUIDES:	PRELEM	CSPS:	SUD EST COORDINATION
ECONOMISTE:	EXECO	OPC:	
BUREAU DE CONTROLE:	Bureau VERITAS	ENTREPRISE(S):	Fontanel-pbc

Bât: C Aile OUEST
BA au +1

DOE

Contrainte de sol: 8 bars ELS

Aciers HA (T) FeE500

Aciers Doux (Ø) FeE 235

Aciers TS FeE 500

Béton fc28 >= 25MPa

Enrobage = 3 cm

PLAN N°
C36 0

DATE : 08/10/2015

MATTÉ
BUREAU D'ÉTUDES
STRUCTURES ET FLUIDES

119 BOULEVARD STALINGRAD 69100 VILLEURBANNE

Tél. 04 72 44 02 87 Fax 04 72 44 26 59

E-mail : bet@matte.fr

Dessiné par : J.BO


Contrôlé par : P.LIN

Echelle : 1/50°

Affaire N°
13.12.119

MURS EXTERIEURS

30.00 ml Env.

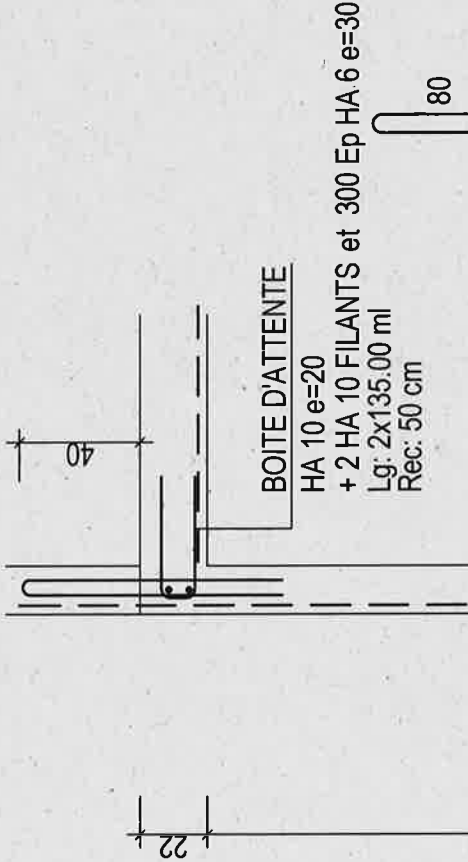

EXT.


Pan PAF V VERTICAUX

Rec: 40 cm

Nombre: 20

ANGLES MURS


(VALABLE 8 fois)

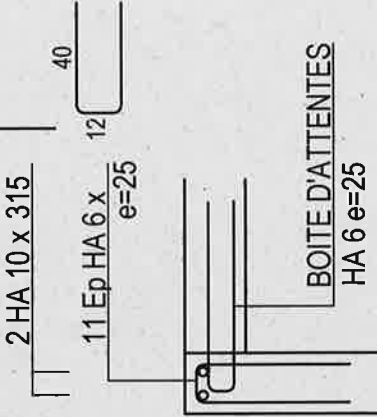

ARMATURES TETES DE MURS

et OUVERTURES


(VALABLE 68 fois)

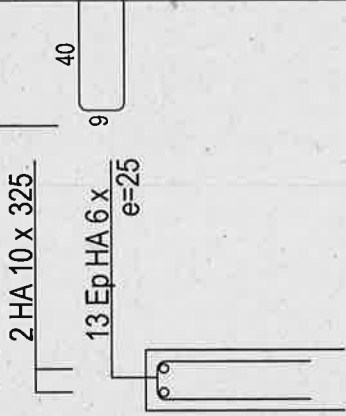

ARMATURES REJINGOT

(VALABLE 4 fois)

A COUPER SUIVANT OUVERTURES

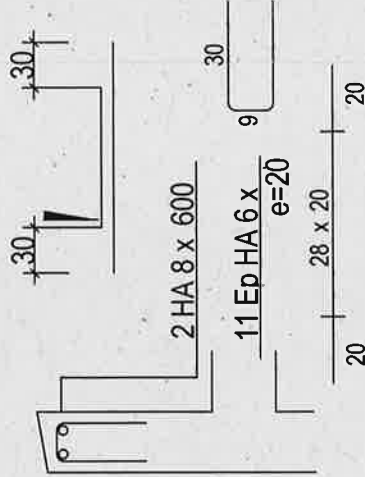


M1

23.00 ml Env.

E1

Nombre: 5


ANGLES MURS
VOIR MURS EXTERIEURS

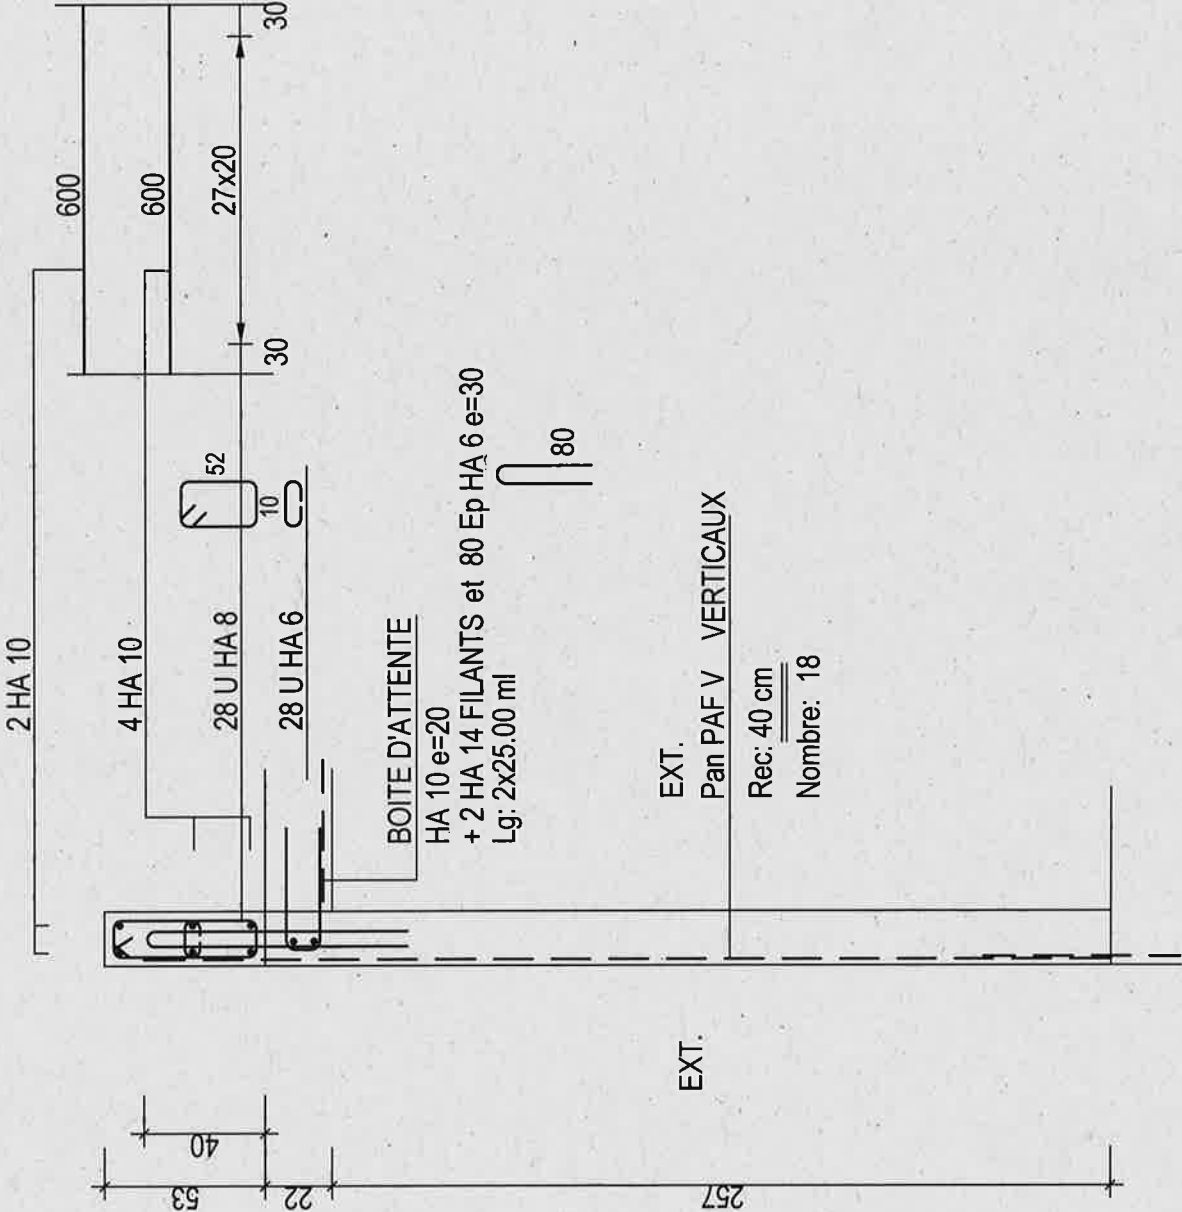


MURS INTERIEURS AVEC CONTINUITE

ARMATURES TETES DE MURS

50.00 ml Env:

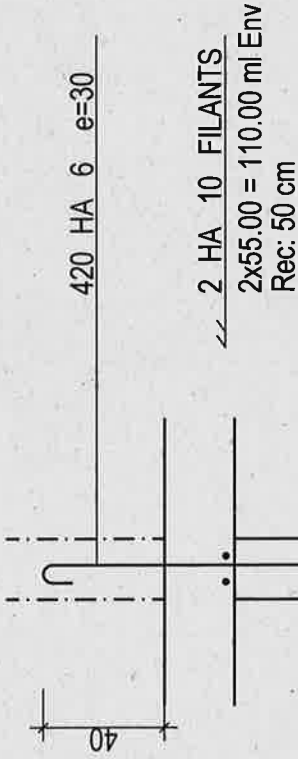


(VALABLE 4 fois)

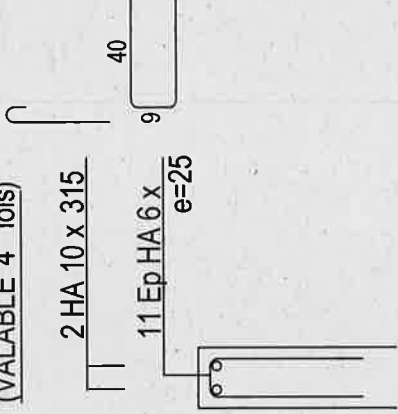


ANGLES MURS

(VALABLE 10 fois)

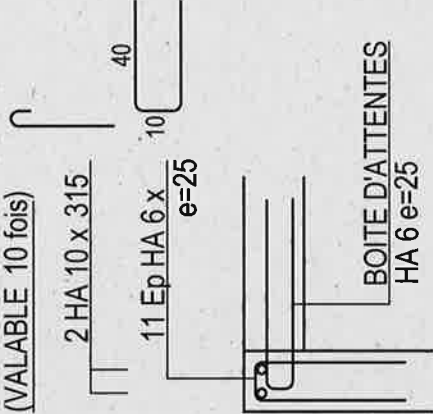


(VALABLE 8 fois)

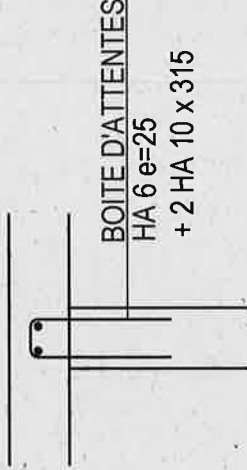


MURS INTERIEURS SANS CONTINUITE

35.00 ml.Env:

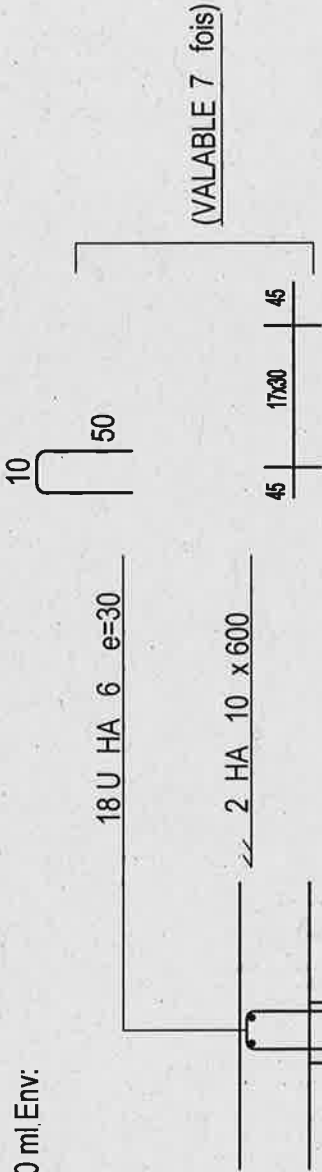

ML1

1 Pièce

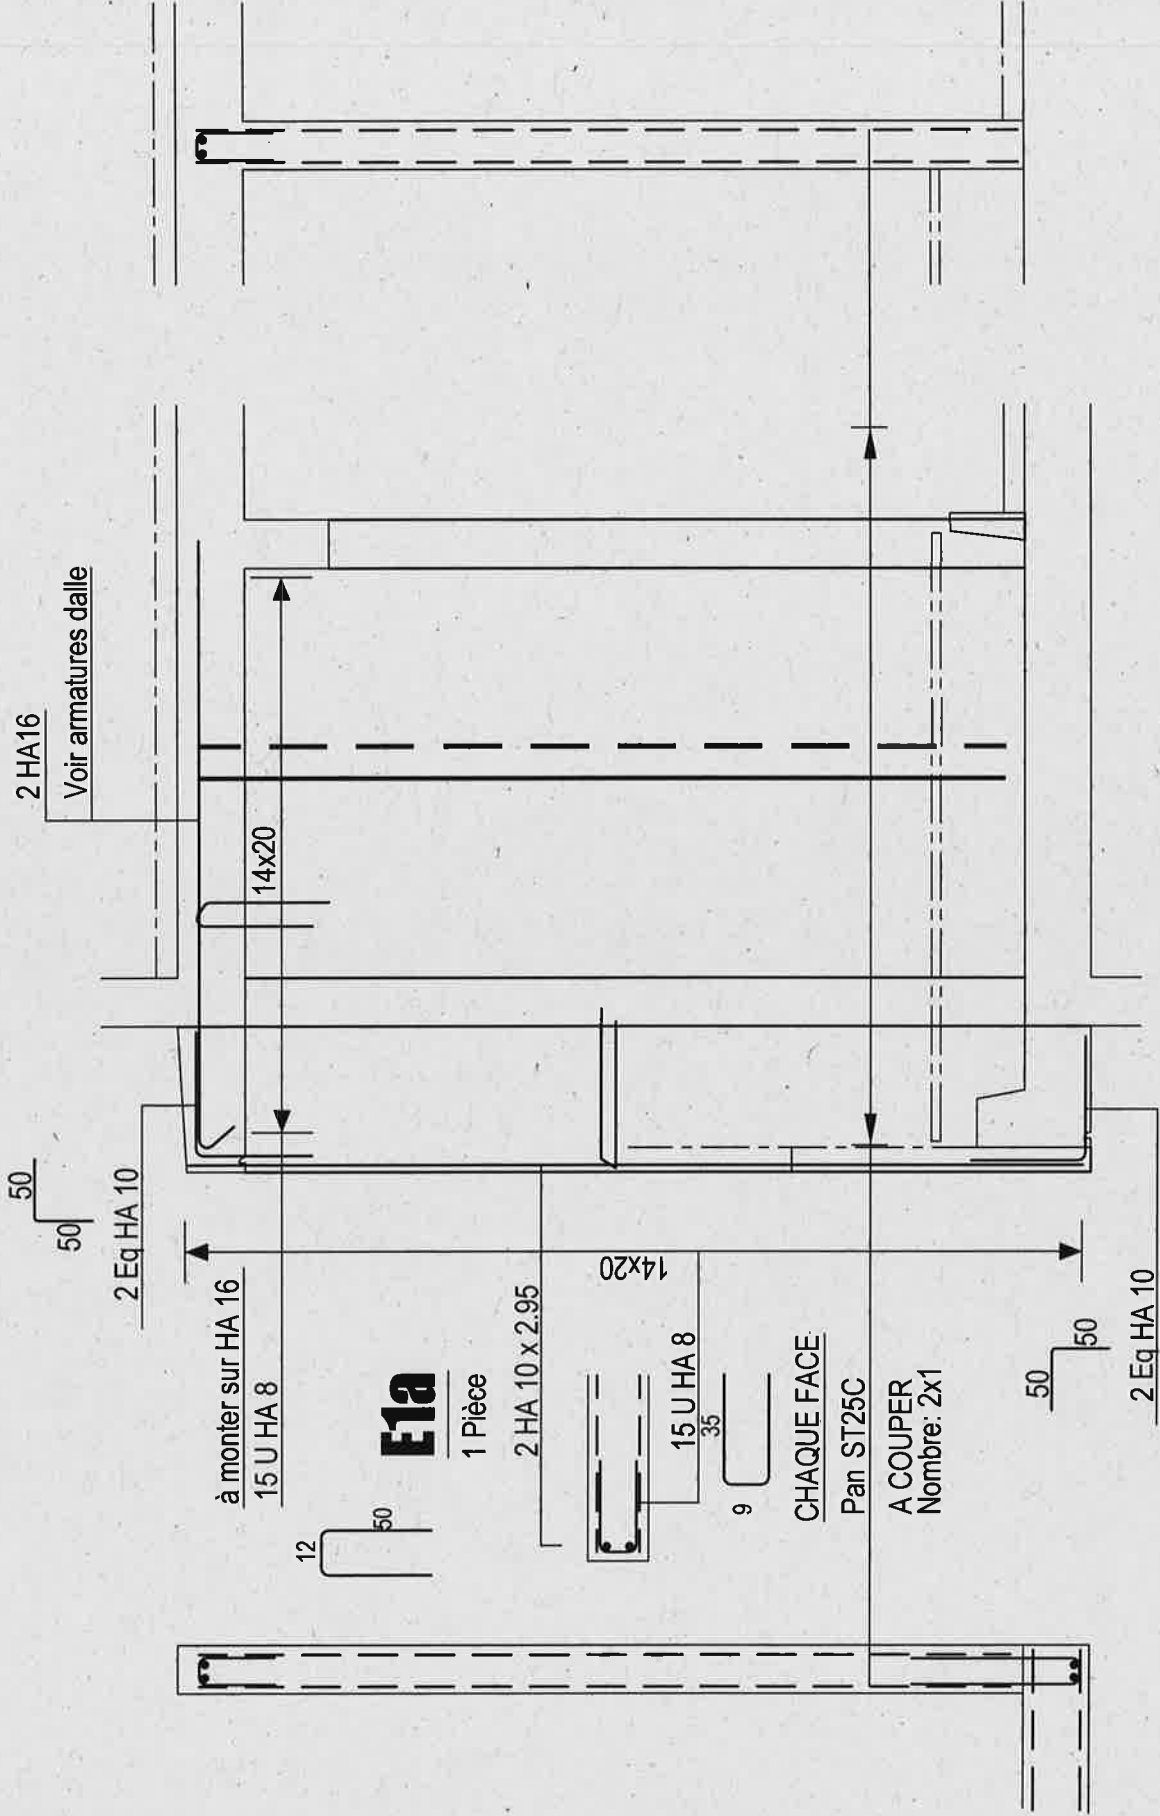


ML2

1 Pièce

ML3


1 Pièce

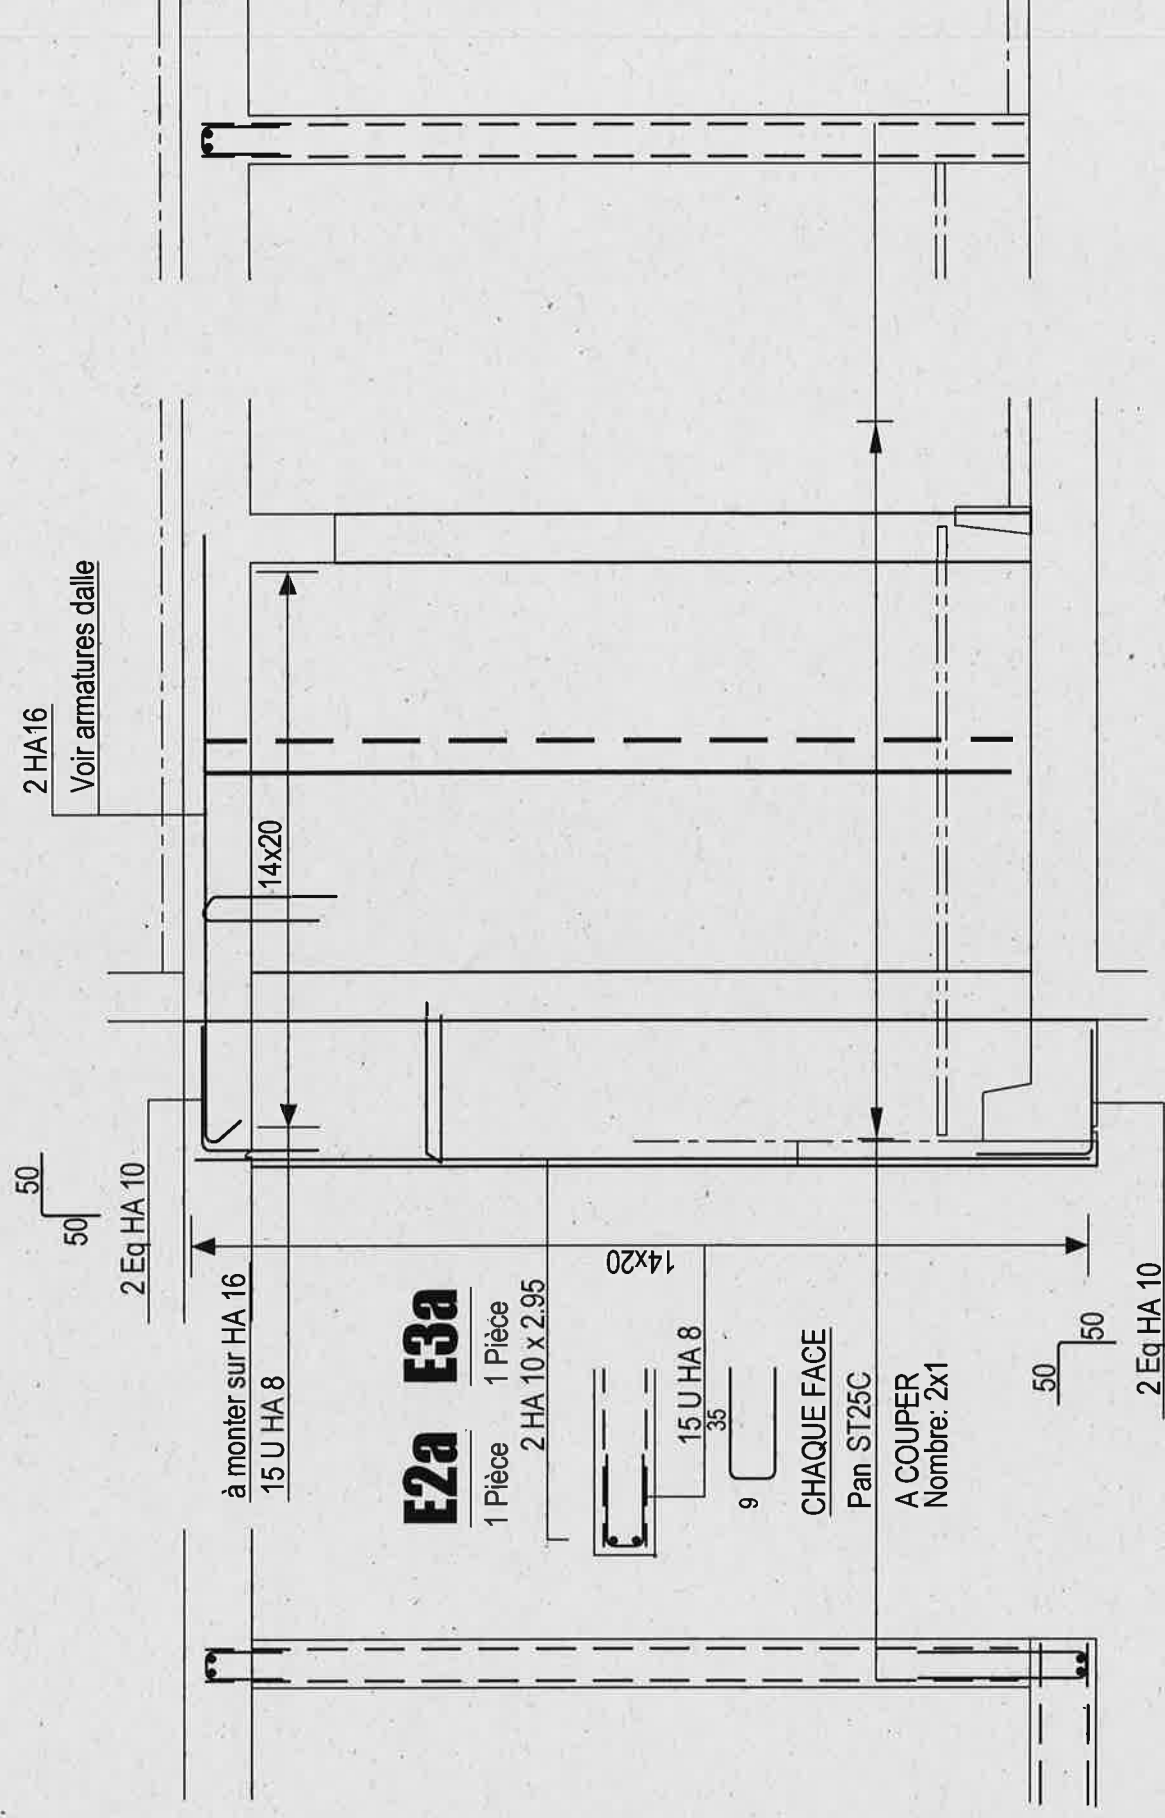

PV1

Nombre: 1

E1a

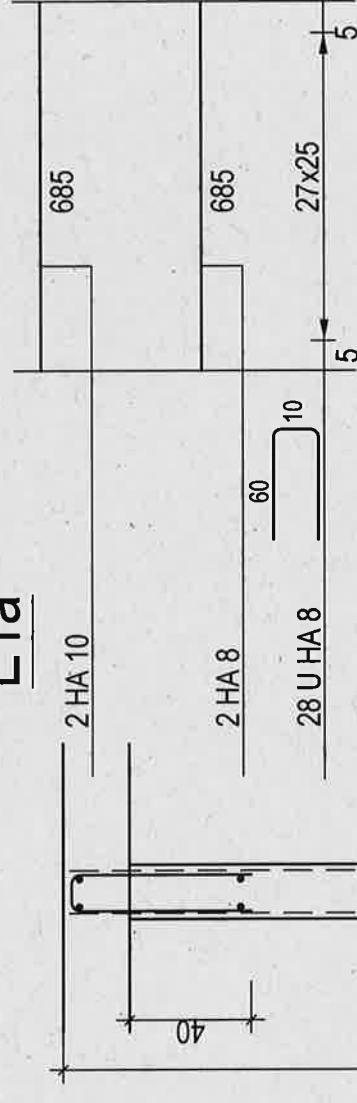


Pan ST15C A COUPER


Rec: 40 cm

Nombre: 3.5

三

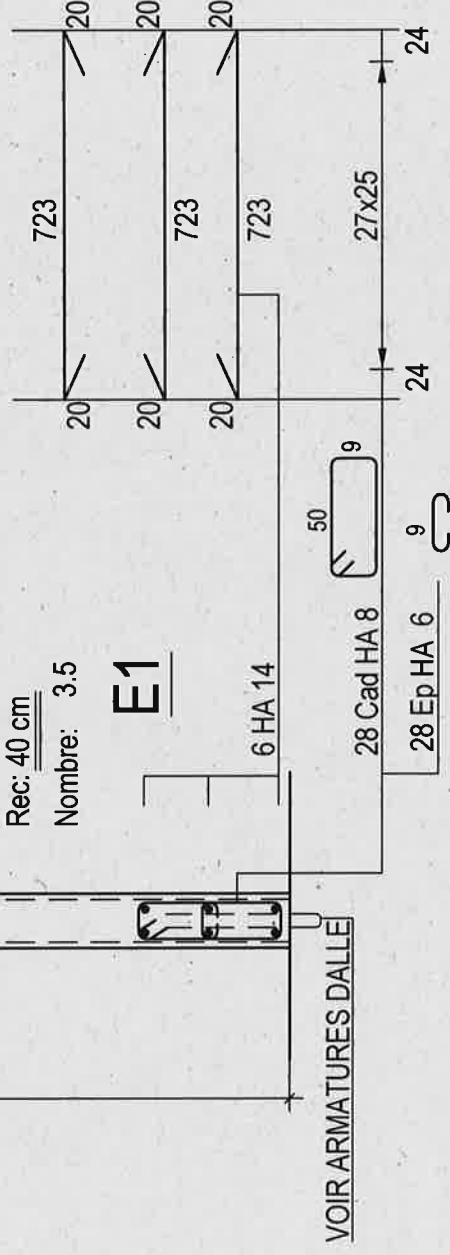

ELEVATION

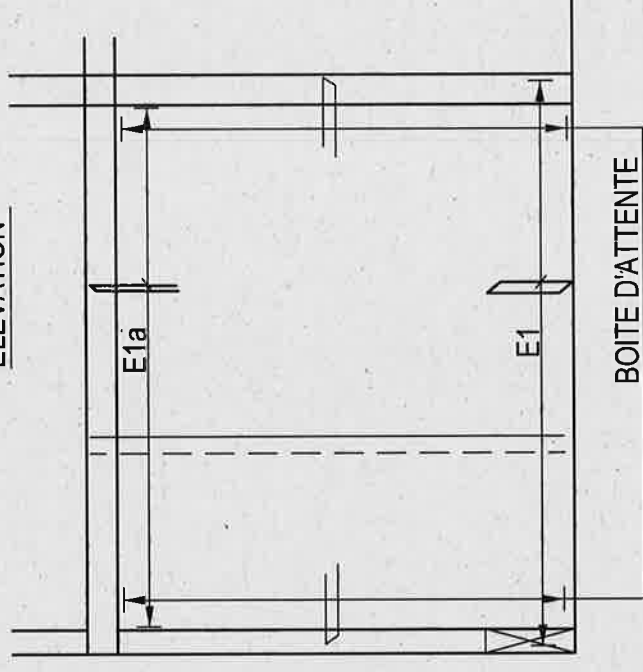

$$\text{HA } 8 \text{ e}=20$$

$$+ 2 \text{ HA } 10 \times 325$$

PV2

Nombre: 1

E2a

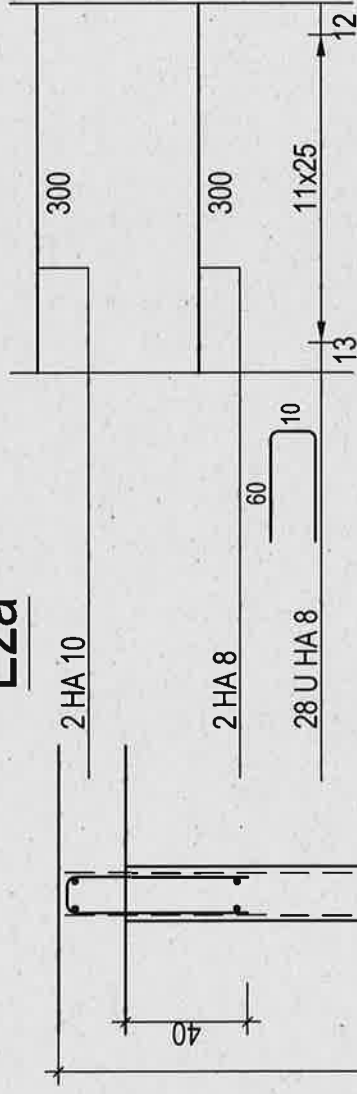

Pan ST15C A COUPER

Rec: 40 cm


Nombre: 1

Pan ST25C A COUPER


Rec: 40 cm

Nombre: 1

E2

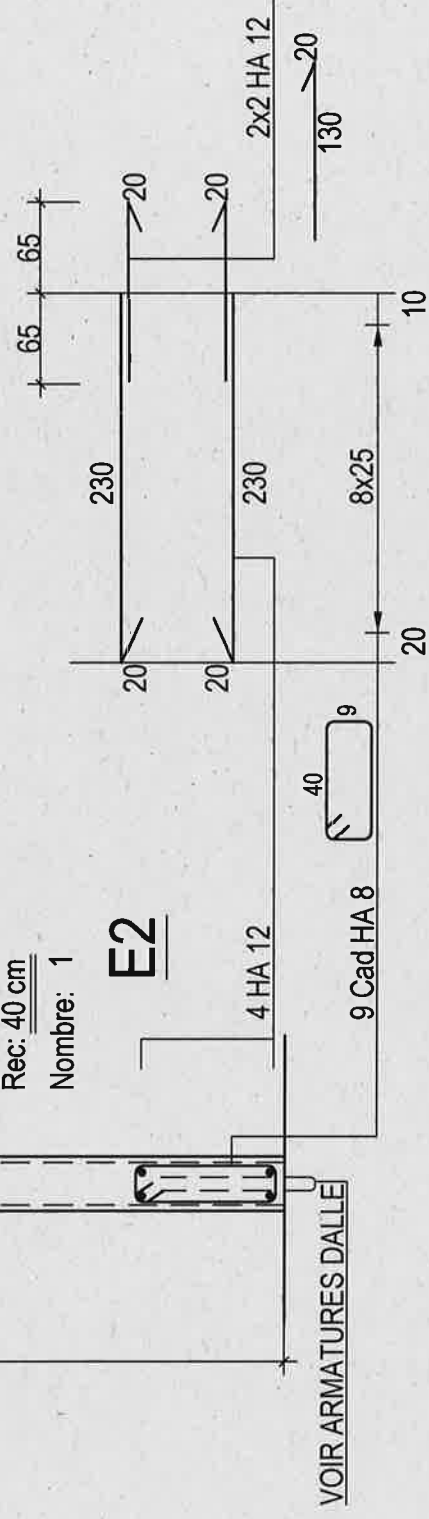


ELEVATION

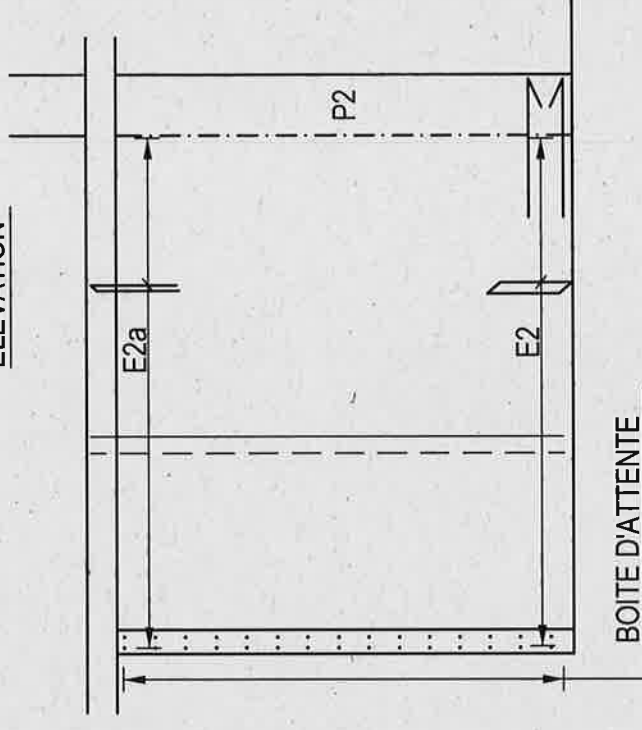

PV3
Nombre: 1

E3a

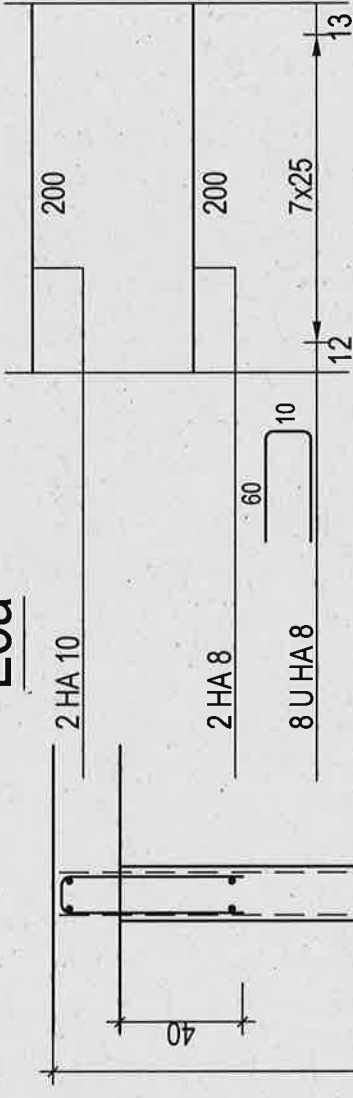

Pan ST15C A COUPER

Rec: 40 cm


Nombre: 1

Pan ST15C A COUPER

Rec: 40 cm


Nombre: 1

E3

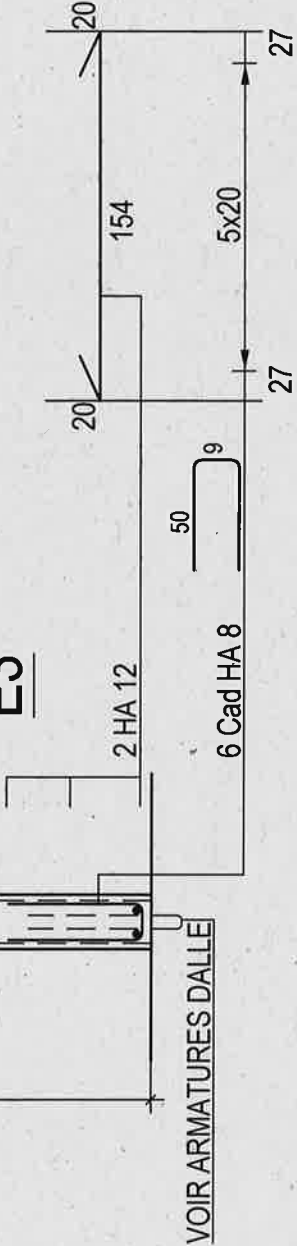

VOIR ARMATURES DALLE

ELEVATION

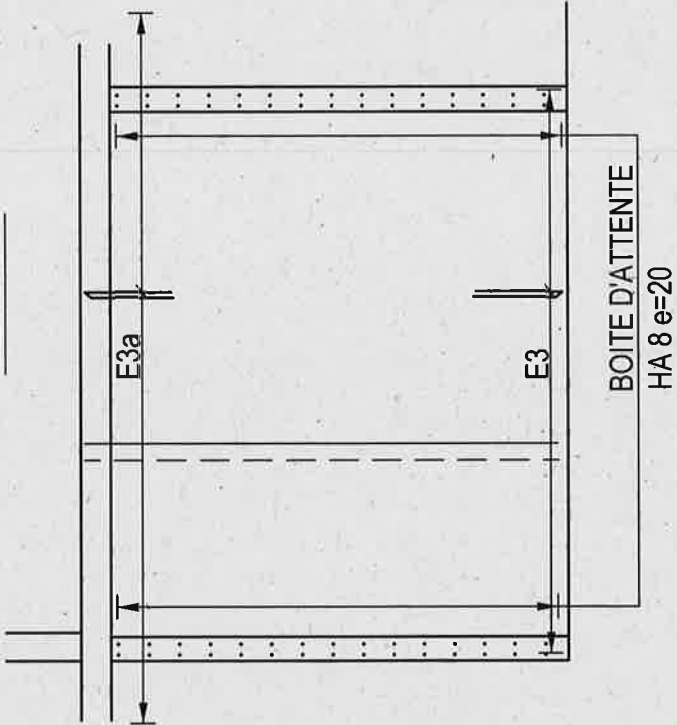

BOITE D'ATTENTE

HA 8 e=20

AFF: S.13.12.119	Bât: C	LA MULATIERE-69350 LaMulatiere CREATION de LOGEMENTS	BA au +1	Aile OUEST	Plan n° C 36	Page: 12
P1 Nombre: 1 20x72						
①	8 HA 12 x	C 265				
②						
③	15 HA 6 x	66 12				
④	2x15 HA 6 x	12				
⑤						
⑥						
⑦						
⑧						
⑨						
⑩						
⑪						
⑫						
⑬						
⑭						
⑮						

AFF: S.13.12.119	Bât: C	LA MULATIERE-69350 LaMulatiere CREATION de LOGEMENTS	BA au +1	Aile OUEST	Plan n° C 36	Page: 13
P2 Nombre: 1 20x72						
①	8 HA 12 x					
②						
③	15 HA 6 x					
④	2x15 HA 6 x					
⑤						
⑥						
⑦						
⑧						
⑨						
⑩						
⑪						
⑫						
⑬						
⑭						
⑮						


AFF: S.13.12.119	Bât: C	LA MULATIERE-69350 La Mulatiere CREATION de LOGEMENTS	BA au +1	Aile OUEST	Plan n° C 36	Page: 14
P3 Nombre: 1 16x75						
			①	6 HA 12 x	C 265	
			②			
			③	13 HA 6 x	69 10	
			④	2x13 HA 6 x	10	
			⑤			
			⑥			
			⑦			
			⑧			
			⑨			
			⑩			
			⑪			
			⑫			
			⑬			
			⑭			
			⑮			

AFF: S.13.12.119	Bât: C	LA MULATIERE-69350 LaMulatiere CREATION de LOGEMENTS	BA au +1	Aile OUEST	Plan n° C 36	Page: 15
P4 Nombre: 1 16x49						
①	6 HA 12 x					
②						
③	13 HA 6 x					
④	13 HA 6 x					
⑤						
⑥						
⑦						
⑧						
⑨						
⑩						
⑪						
⑫						
⑬						
⑭						
⑮						

59

Nombre: 1

16x35

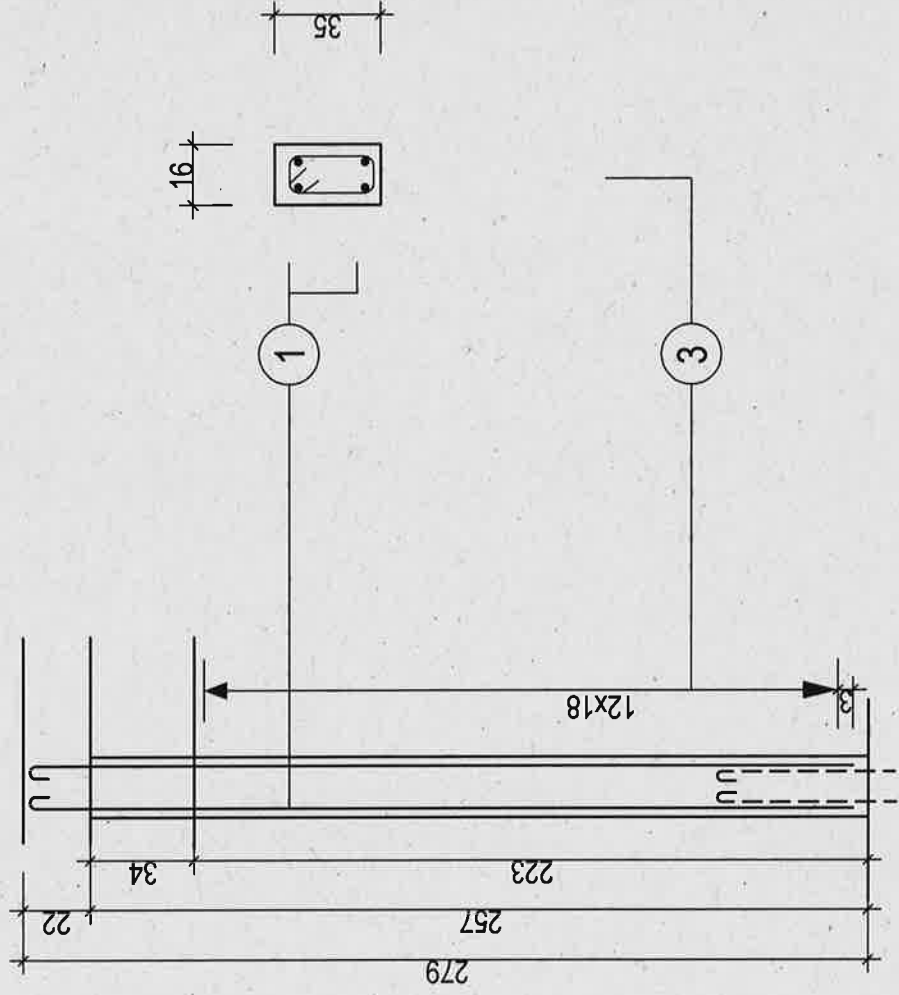

1

2

3

4

5



⑦



©



11

--	--

○

2)

⑤

 $4 \text{ HA} + 12 \text{ H}^+ + 12 \text{ e}^-$


13 HA 6 x

265

99

Nombre: 1

16x22

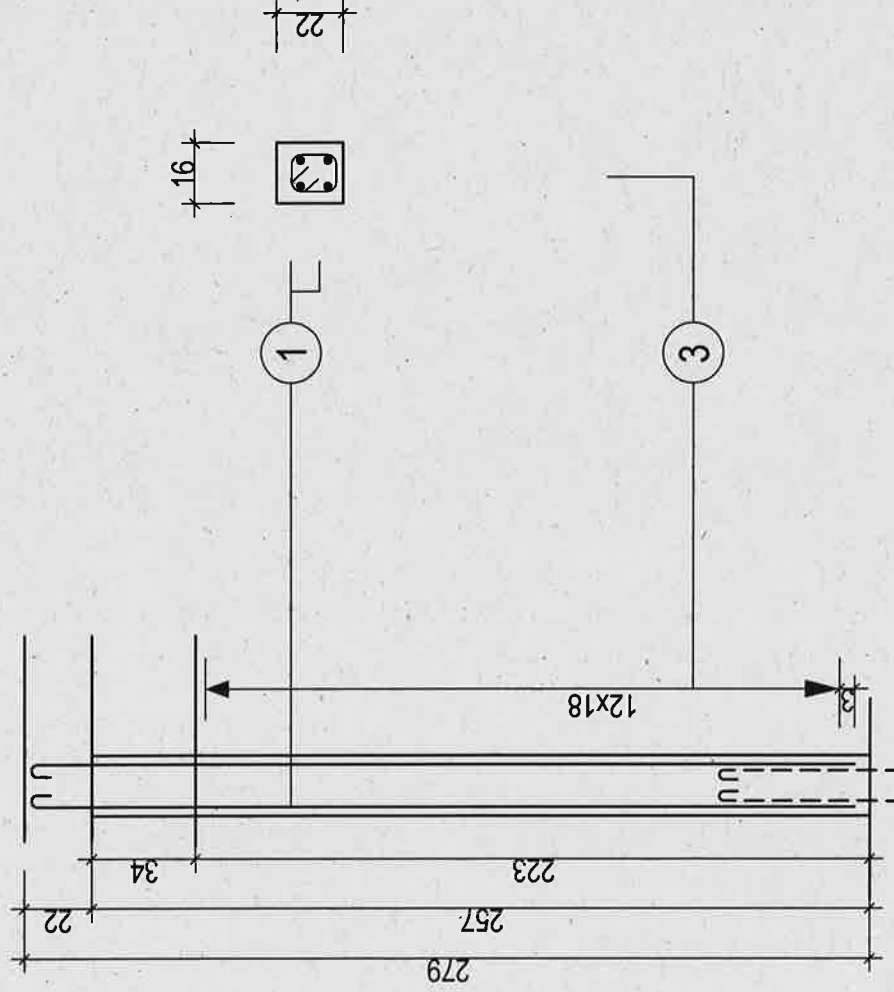

①

2

3

4

5

6

7

⑧

9

10

 $\oplus$

71

②

5

②




 $4 \text{ HA} + 12 \text{ H}^+$

13 HA 6 x


265

A rectangle with a width of 10 and a height of 16. The bottom-left corner is shaded with diagonal lines.


AFF: S.13.12.119		Bât: C	LA MULATIERE-69350 LaMulatiere CREATION de LOGEMENTS		BA au +1		Aile OUEST		Plan		n° C 36		Page: 18	
P7 Nombre: 1 16x46														Architectural drawing of a staircase. It shows a side view with dimensions: 279 (total width), 257 (platform width), 223 (flight width), 34 (nose overhang), and 16 (riser height). Numbered points 1, 3, and 4 are marked on the drawing. Point 1 is at the top of the flight, point 3 is at the bottom of the flight, and point 4 is on the platform. A section line 'F' is indicated.														1 2 3 4 5 6 7 8 9 10 11 12 13 14 15														6 HA 12 x 13 HA 6 x 13 HA 6 x														C 265 38 10 10													

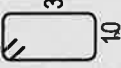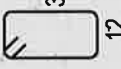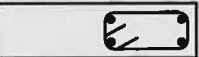AFF: S.13.12.119	Bât: C	LA MULATIERE-69350 LaMulatiere CREATION de LOGEMENTS	BA au +1	Aile OUEST	Plan n° C 36	Page: 19
L  4 HA 10 5 Cad HA 6 20 135 20 28 4x20 27  30 10	 4 HA 12 9 Cad HA 6 20 194 20 17 8x20 17  30 12	 4 HA 10 7 Cad HA 6 20 165 20 22 6x20 23  30 12	Lb Nombre: 1 La Nombre: 1			

Elévation
Echelle=1/25

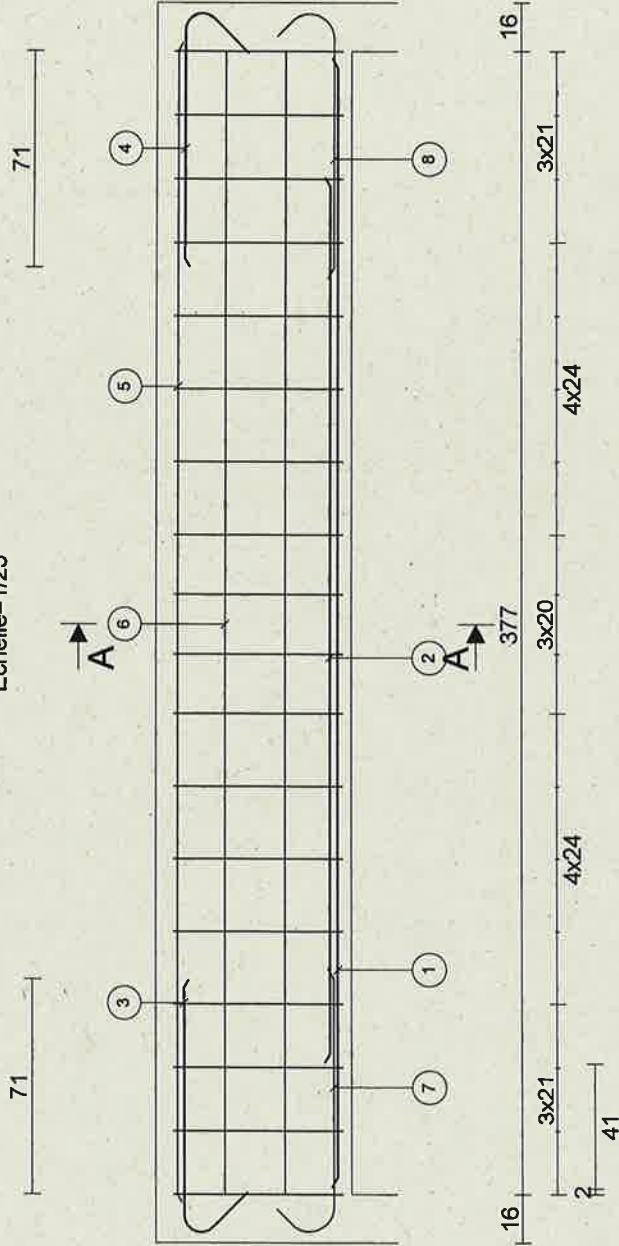

Coupe A-A
Echelle=1/20

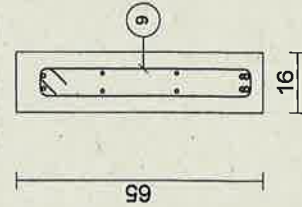


Barre		Lg	Forme
1	2HA14	373	 373
2	2HA12	292	 292
3	2HA10	107	 84 135°
4	2HA10	107	 135° 84
5	2HA10	383	 383
6	4HA8	377	 377
7	2HA14	105	 135° 88
8	2HA14	105	 88 135°
9	18HA8	138	 8
18° 256 241			
Barre		Lg/Poids	
HA8		39.8/15.7	
HA10		12.0/7.4	
HA12		5.8/5.2	
HA14		11.7/14.1	

- Date 06/07/15 - 10 étages -
Section : 16 x 56ht


Coupe feu R 120

fck= 25 MPa fyk= 500 MPa

Elévation
Echelle=1/20

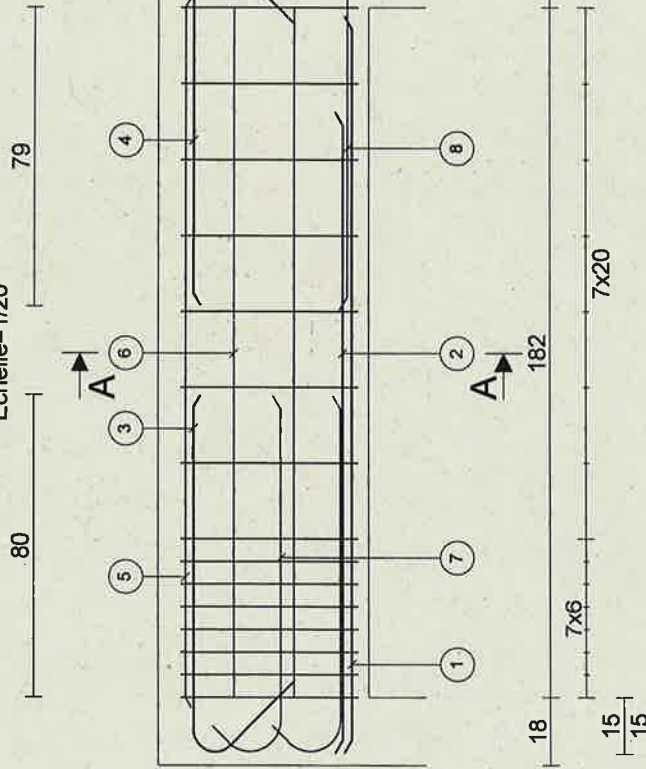

Coupe A-A
Echelle=1/20

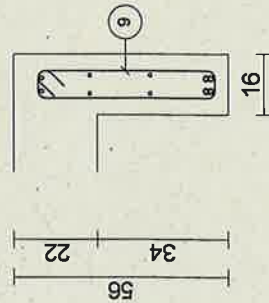

Barre	Lg	Forme
1 2HA14	195	195
2 2HA14	170	170
3 2HA12	126	95 135°
4 2HA12	125	95 135°
5 2HA10	188	188
6 4HA8	182	182
7 4HA14	111	135° 95
8 2HA14	111	95 135°
9 15HA8	120	8

Lg/Poids


25.2/10.0
3.8/2.3
5.0/4.5
14.0/16.9

- Date 06/07/15 - 10 étages -
Section : 16 x 56ht


Coupe feu R 120

fck= 25 MPa fyk= 500 MPa

Elévation
Echelle=1/20

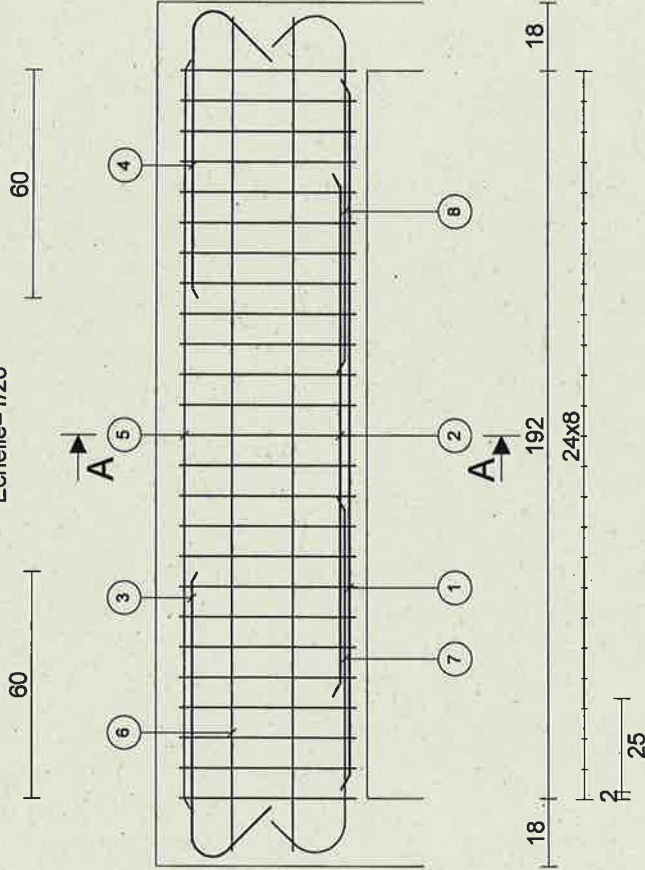

Coupe A-A
Echelle=1/20

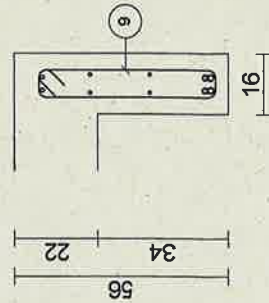

Barre		Lg	Forme
1	2HA16	188	
2	2HA14	138	
3	2HA10	99	
4	2HA10	99	
5	2HA10	198	
6	4HA8	220	
7	2HA14	113	
8	2HA14	113	
9	25HA8	120	


- Date 06/07/15 - 10 étages -

Section : 16 x 56ht


Coupe feu R 120

fck= 25 MPa fyk= 500 MPa

Elévation
Echelle=1/20

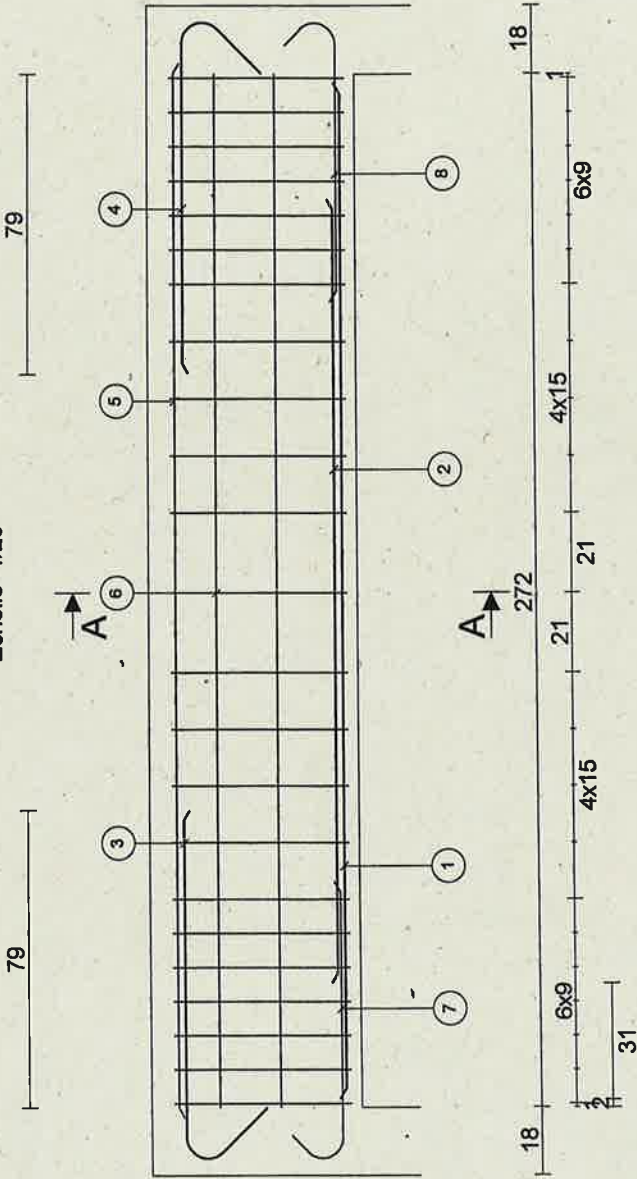


Coupe A-A
Echelle=1/20

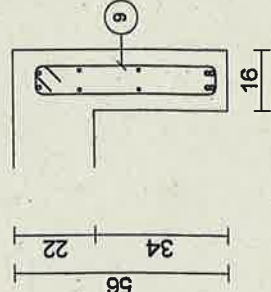

Barre	Lg	Forme
1 2HA12	268	268
2 2HA10	207	207
3 2HA10	116	93 135°
4 2HA10	116	135° 93
5 2HA10	278	278
6 4HA8	272	272
7 2HA12	87	135° 74
8 2HA12	87	74 135°
9 23HA6	120	8


Barre	Lg/Poids
HA6	27.8/6.1
HA8	10.9/4.3
HA10	14.3/8.8
HA12	8.8/7.8

$f_{ck} = 25 \text{ MPa}$ $f_{yk} = 500 \text{ MPa}$

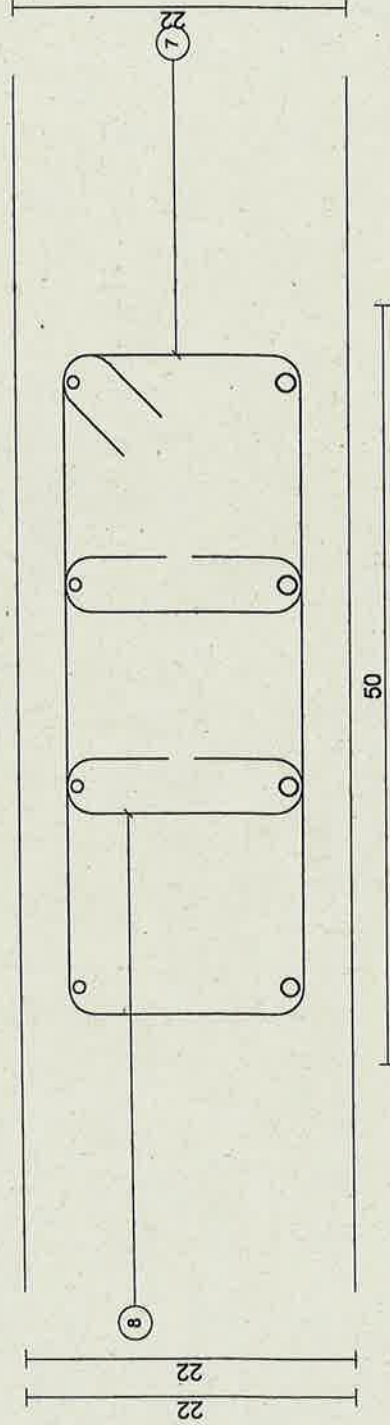
[illegible]

- Date 06/07/15 - 10 étages -
Section : 50 x 22ht
fck= 25 MPa fyk= 500 MPa

Elévation
Echelle=1/25

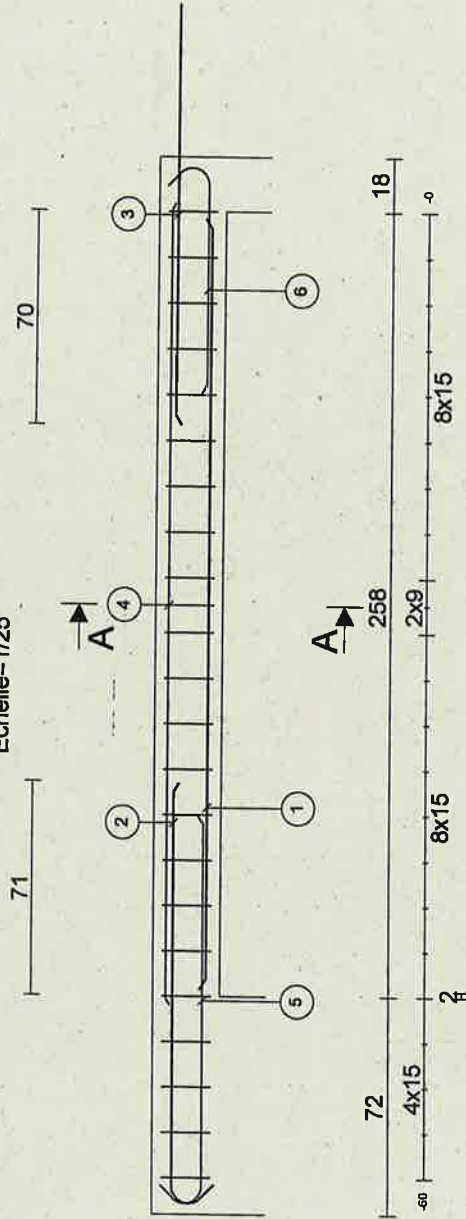


Coupe A-A
Echelle=1/5

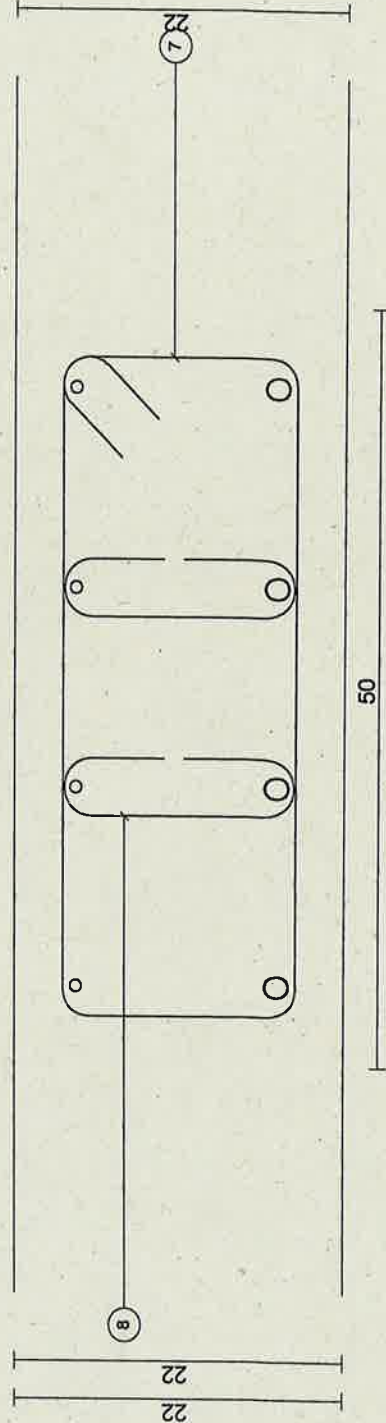


Barre	Lg	Forme
1 4HA14	254	254
2 4HA12	153	140 135°
3 4HA12	158	158
4 4HA8	264	264
5 4HA12	142	135° 129
6 4HA12	88	75 135°
7 23HA6	130	44
8 46HA8	33	16
Barre	Lg/Poids	
HA6	29.9/6.6	
HA8	25.9/10.2	
HA12	21.6/19.2	
HA14	10.2/12.3	


Barre	Lg	Forme
1 4HA12	313	313
2 4HA12	230	230
3 4HA10	90	70 135°
4 4HA10	95	135° 75
5 4HA8	323	323
6 4HA12	90	135° 77
7 4HA12	90	77 135°
8 25HA6	110	34
9 50HA6	33	16

Elévation
Echelle=1/25

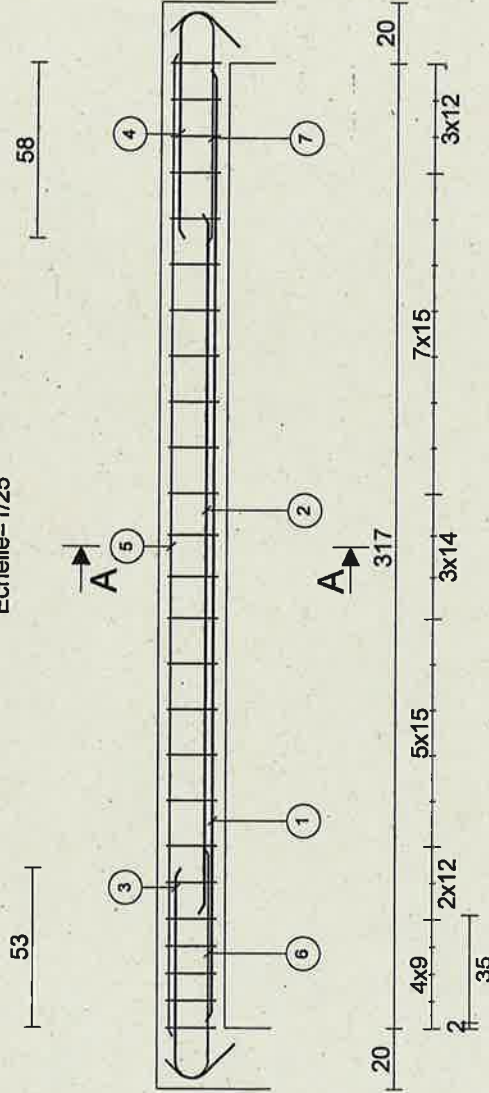

Coupe A-A
Echelle=1/5

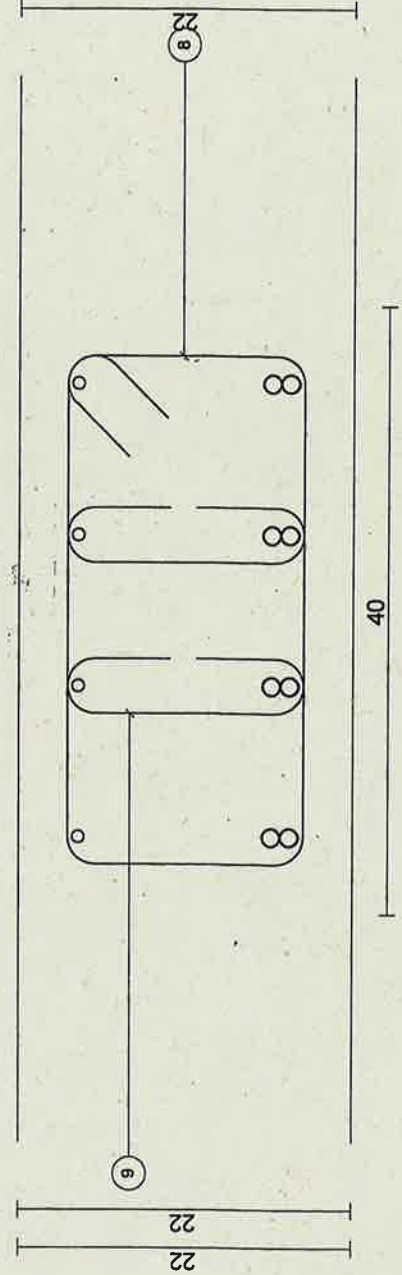


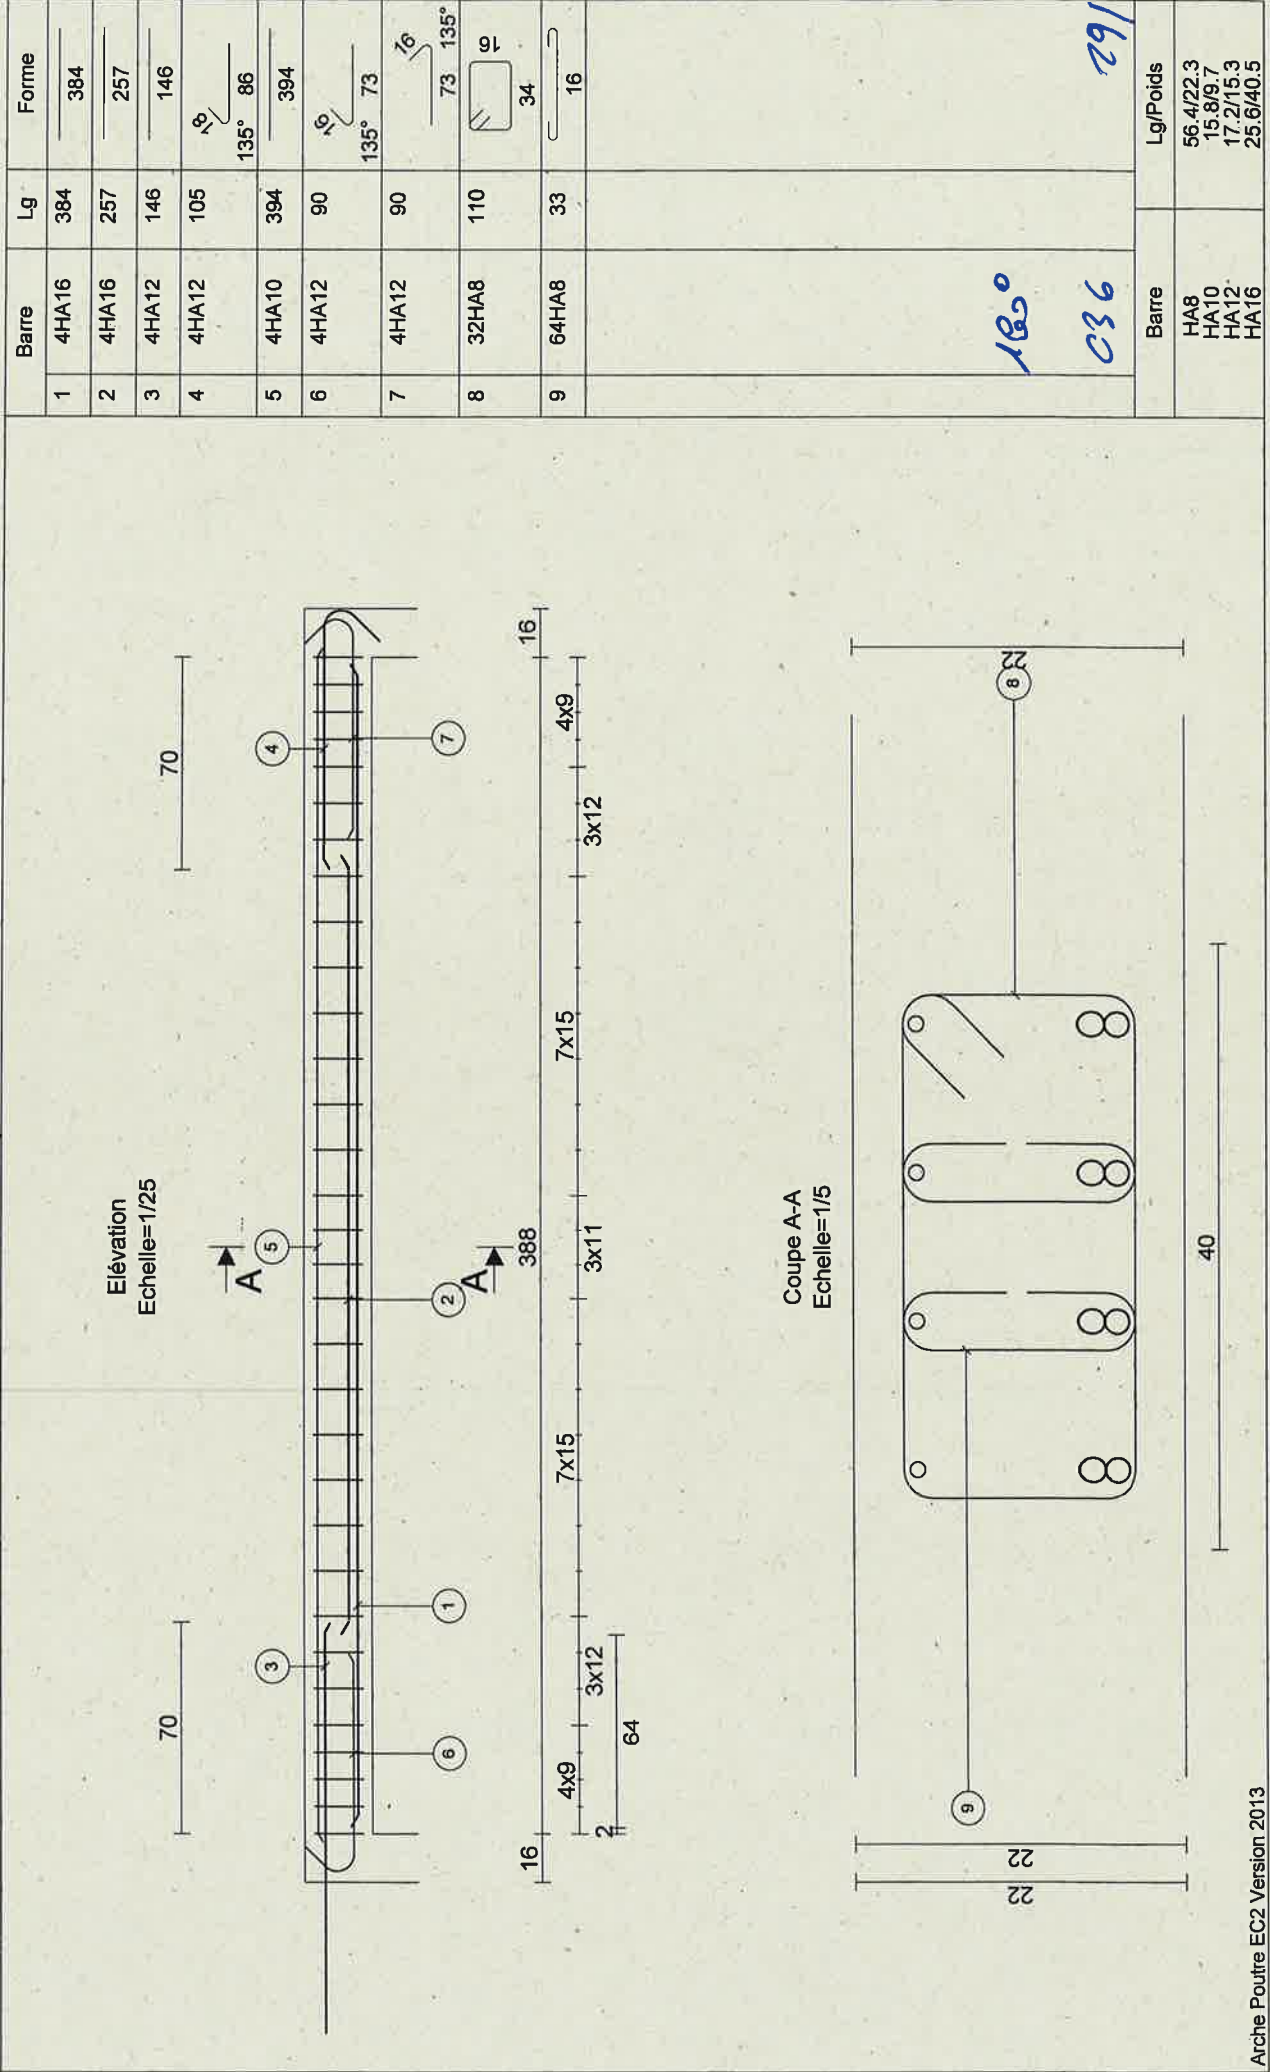


- Date 06/07/15 - 10 étages -
Section : 40 x 22ht

fck= 25 MPa fyk= 500 MPa

Elévation
Echelle=1/25

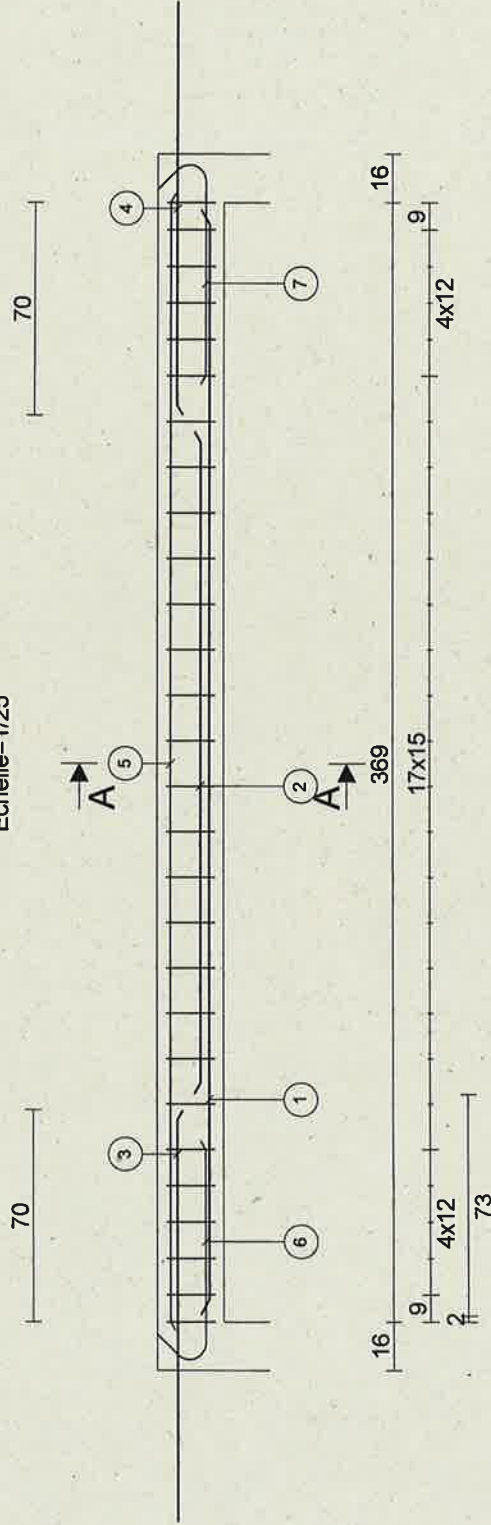

Coupe A-A
Echelle=1/5

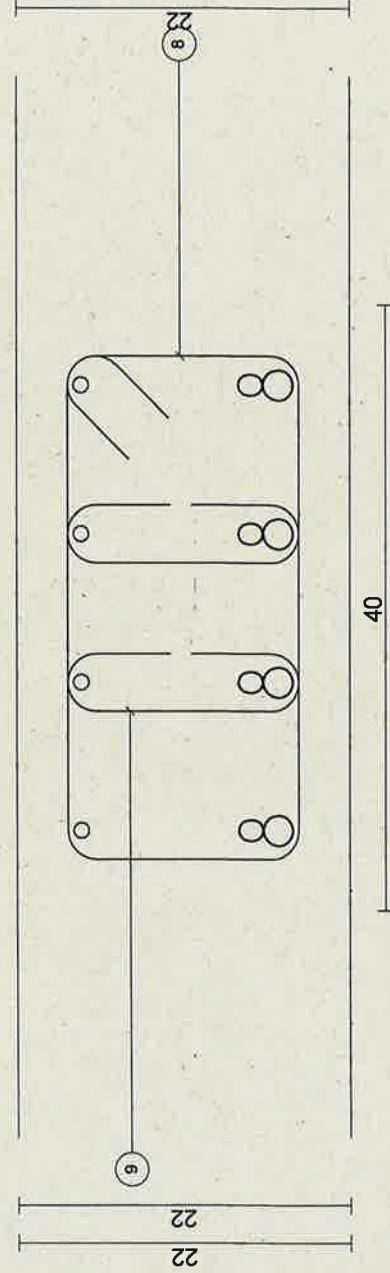

Barre	Lg	Forme
1 4HA20	365	365
2 4HA14	219	219
3 4HA12	146	146
4 4HA12	146	146
5 4HA10	375	375
6 4HA12	90	90
7 4HA12	90	90
8 28HA8	110	110
9 56HA8	33	33

18.5°

C36

30/

Barre	Lg/Poids
HA8	49.3/19.5
HA10	15.0/9.3
HA12	18.9/16.8
HA14	8.7/10.6
HA20	14.6/36.0