


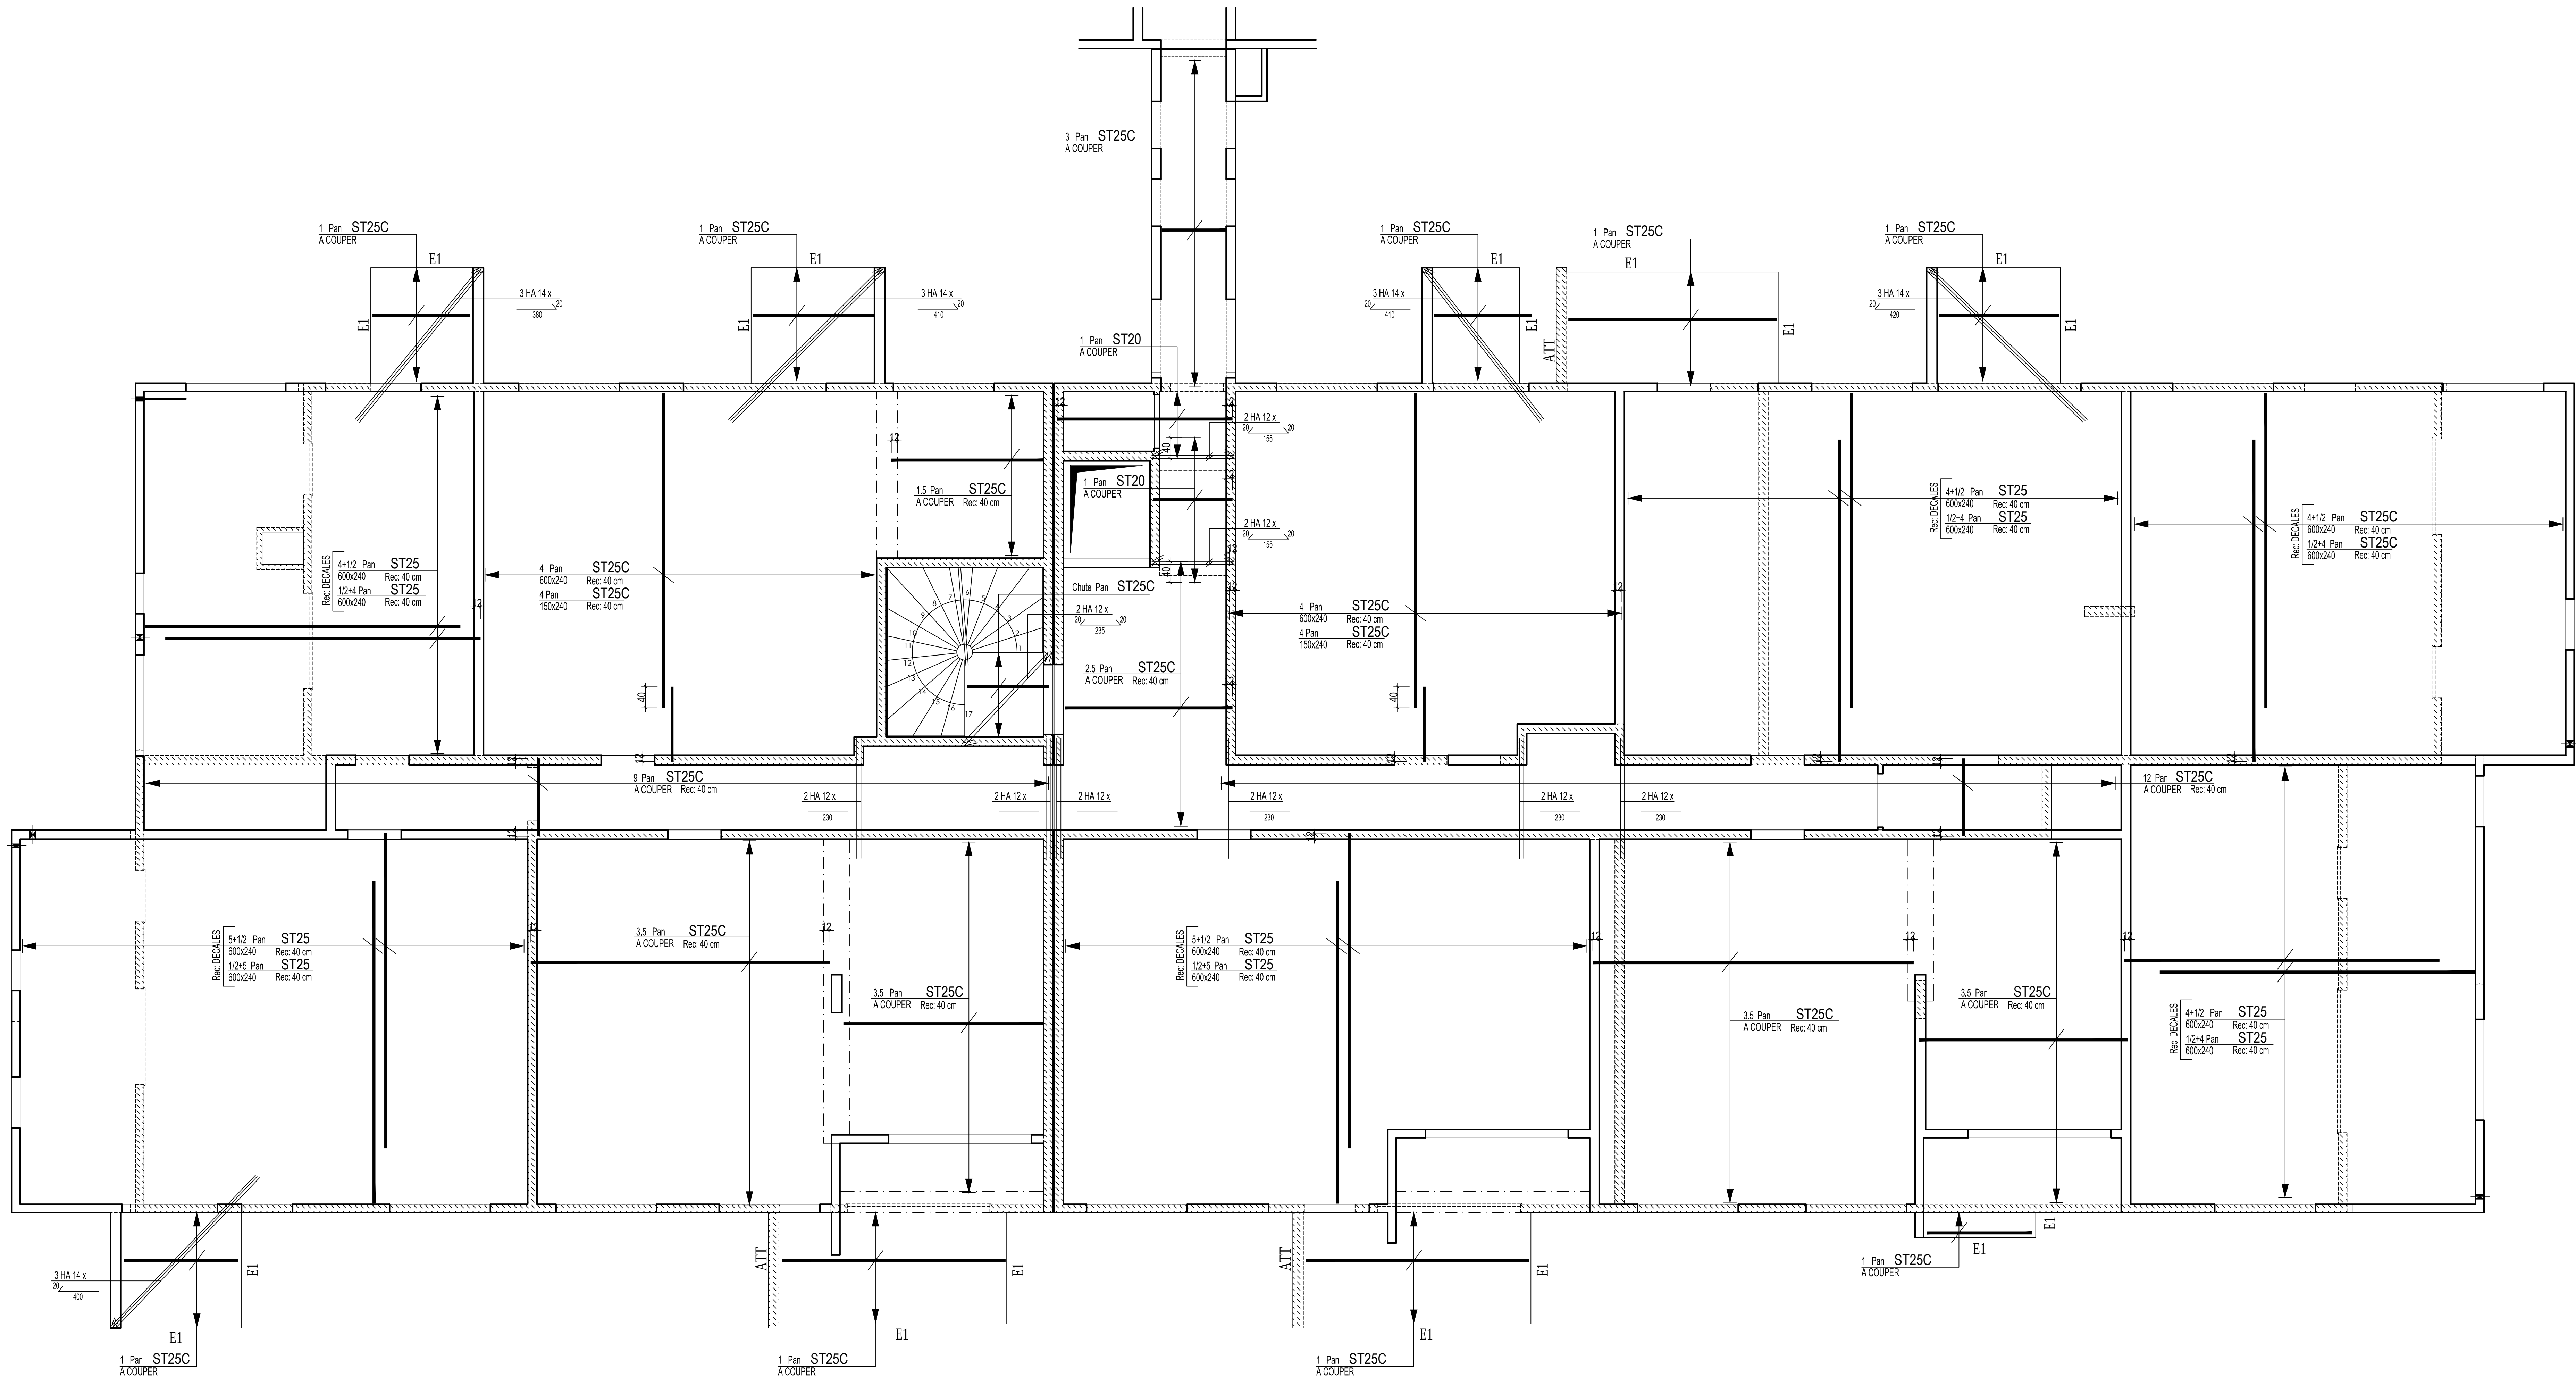

RECA. T.S.		
PAF 10	420x240	0
ST20	600x240	0
ST25	600x240	63
ST30	600x240	0
ST35	600x240	0
ST50	600x240	0
ST60	600x240	0
ST15C	400x240	0
ST25C	600x240	44
ST40C	600x240	0
ST50C	600x240	0
ST65C	600x240	0

NOAHO

Chemin de Fontanière - 69350 La Mulatière

Création de logements

Les entreprises réalisant les travaux devront tenir compte des derniers plans architectes lors de la réalisation des travaux.
Les plans du B.T. MATTE ne doivent servir qu'à titre d'élément de référence et doivent être complétés par les plans d'exécution.

ARCHITECTES: Atelier D'IS

BET STRUCTURE: MATTE SAS

BET FLUIDES: PRELEM

ECONOMISTE: EXECO

BUREAU DE CONTRÔLE: Bureau VERITAS

MO DELEGUE: PSO Ingénierie

CSPS: SUD EST COORDINATION

OPC: ENTREPRISES: Fontanel-jbc

Bât: C Aile OUEST

PLANCHER SUR +1

ARMATURES DALLE INFÉRIEURE

DOE

Contrainte de sol: 8 bars EL5

Aciers HA (T) F4E500

Aciers DDA (D) F4E235

Aciers TS F4E 500

Sécher fct33 > 20MPa

Enrobage = 3 cm

INDICE

DATE

MODIFICATIONS

MATTÉ

BUREAU D'ÉTUDES

STRUCTURES ET FLUIDES

119 BOULEVARD STALINGRAD 69100 VILLEURBANNE

Tél. 04 72 44 02 87 Fax 04 72 44 28 58

E-mail: matt@matte.fr

Dessiné par: J.BO

Contrôlé par: P.LIN

Echelle: 1/150"

PLAN N°

C37 0

DATE: 20/07/2015

Affaire N°

13.12.119