


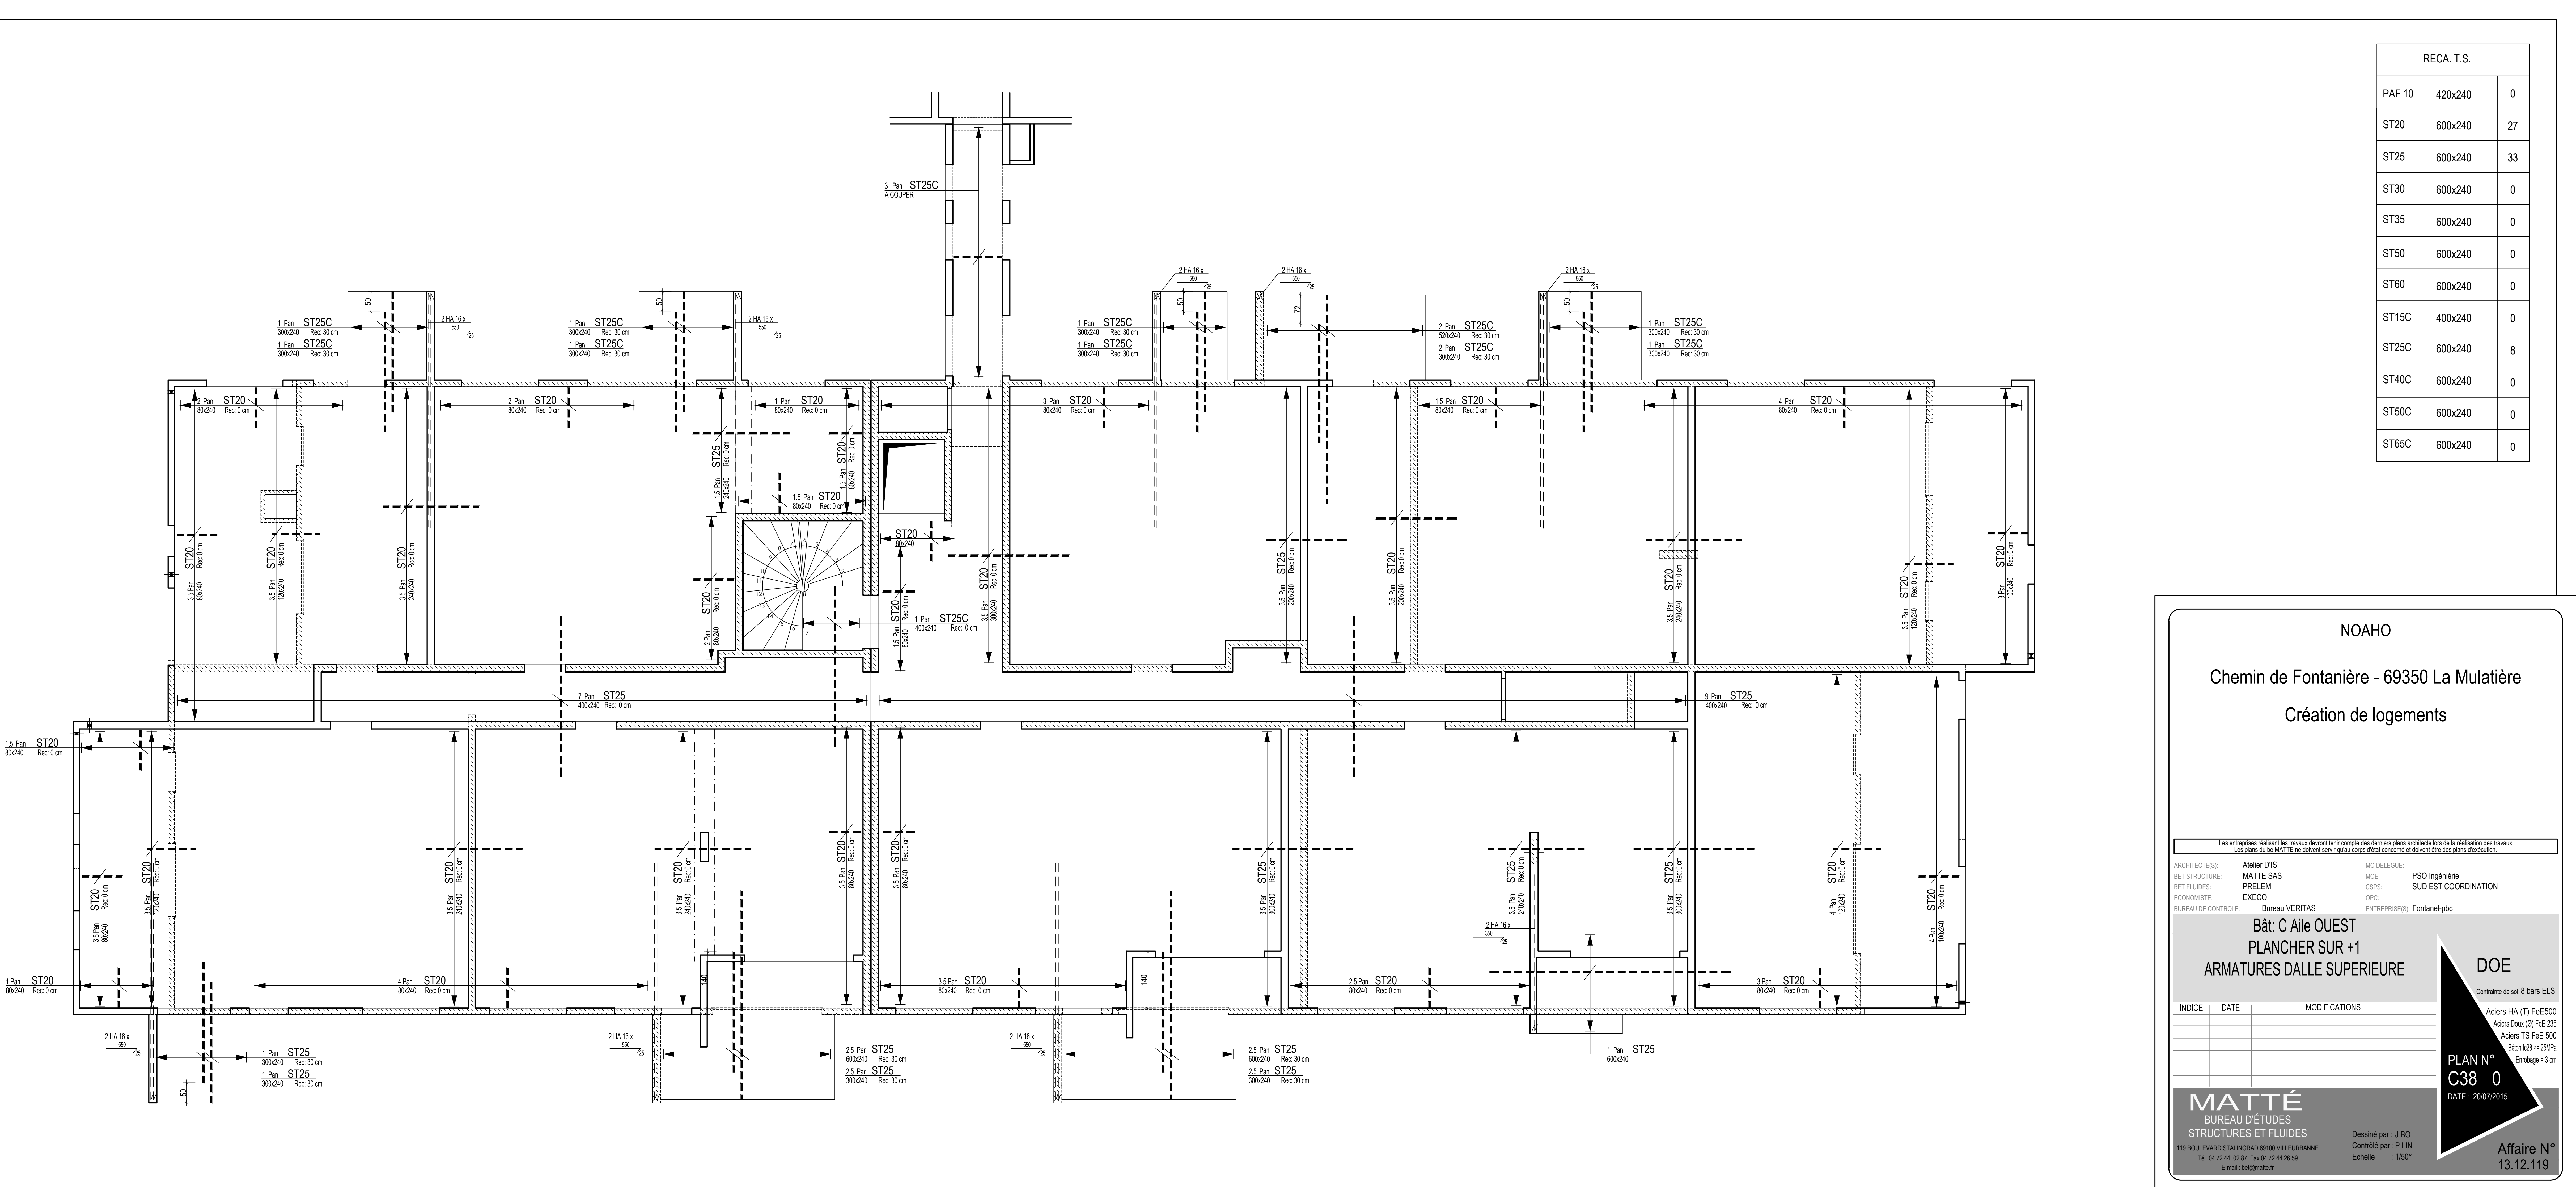

| RECA. T.S. |         |    |
|------------|---------|----|
| PAF 10     | 420x240 | 0  |
| ST20       | 600x240 | 27 |
| ST25       | 600x240 | 33 |
| ST30       | 600x240 | 0  |
| ST35       | 600x240 | 0  |
| ST50       | 600x240 | 0  |
| ST60       | 600x240 | 0  |
| ST15C      | 400x240 | 0  |
| ST25C      | 600x240 | 8  |
| ST40C      | 600x240 | 0  |
| ST50C      | 600x240 | 0  |
| ST65C      | 600x240 | 0  |

NOAHO

Chemin de Fontanière - 69350 La Mulatière

Création de logements

Les entreprises réalisant les travaux devront tenir compte des derniers plans architectes lors de la réalisation des travaux  
Les plans du Bât MATTÉ ne doivent servir qu'à titre d'élément de référence et ne doivent pas être utilisés pour la construction

ARCHITECTES: Atelier D'S  
BET STRUCTURE: MATTE SAS  
BET FLUIDES: PRELEM  
ECONOMISTE: EXECO  
BUREAU DE CONTROLE: Bureau VERITAS

MO DELEGUE: PSO Ingénierie  
CSPS: SUD EST COORDINATION  
CPC:   
ENTREPRISES: Fontanel-jbc

Bât: C Aile OUEST  
PLANCHER SUR +1  
ARMATURES DALLE SUPERIEURE

DOE  
Contrainte de sol: 8 bars EL5  
Aciers HA (T) FeE500  
Aciers Doux (D) FeE235  
Aciers TS FeE 500  
Béton C28-30 MPa  
Enrobage + 3 cm

| INDICE | DATE | MODIFICATIONS |
|--------|------|---------------|
|        |      |               |
|        |      |               |
|        |      |               |
|        |      |               |

MATTÉ  
BUREAU D'ETUDES  
STRUCTURES ET FLUIDES  
119 BOULEVARD STALINGRAD 69100 VILLEURBANNE  
Tél. 04 72 44 02 87 Fax 04 72 44 28 58  
E-mail: matt@matte.fr

Dessiné par : J.BO  
Contrôlé par : P.LIN  
Echelle : 1/150

PLAN N°  
C38 0  
DATE : 20/07/2015

Affaire N°  
13.12.119