

NOAHO

Chemin de Fontanière - 69350 La Mulatière

Création de logements

Les entreprises réalisant les travaux devront tenir compte des derniers plans architecte lors de la réalisation des travaux
Les plans du be MATTE ne doivent servir qu'au corps d'état concerné et doivent être des plans d'exécution.

ARCHITECTE(S): Atelier D'IS
BET STRUCTURE: MATTE SAS
BET FLUIDES: PRELEM
ECONOMISTE: EXECO
BUREAU DE CONTROLE: Bureau VERITAS

MO DELEGUE:
MOE: PSO Ingénierie
CSPS: SUD EST COORDINATION
OPC:
ENTREPRISE(S): Fontanel-pbc

Bât: C Aile OUEST
BA au +2

DOE

Contrainte de sol: 8 bars ELS

Aciers HA (T) FeE500

Aciers Doux (Ø) FeE 235

Aciers TS FeE 500

Béton fc28 >= 25MPa

Enrobage = 3 cm

PLAN N°
C40 0

DATE : 09/10/2015

MATTÉ
BUREAU D'ÉTUDES
STRUCTURES ET FLUIDES

119 BOULEVARD STALINGRAD 69100 VILLEURBANNE

Tél. 04 72 44 02 87 Fax 04 72 44 26 59

E-mail : bet@matte.fr

Dessiné par : J.BO

Contrôlé par : P.LIN

Echelle : 1/50°


Affaire N°
13.12.119

MURS EXTERIEURS


ARMATURES TETES DE MURS
et OUVERTURES

E1

Nombre: 18

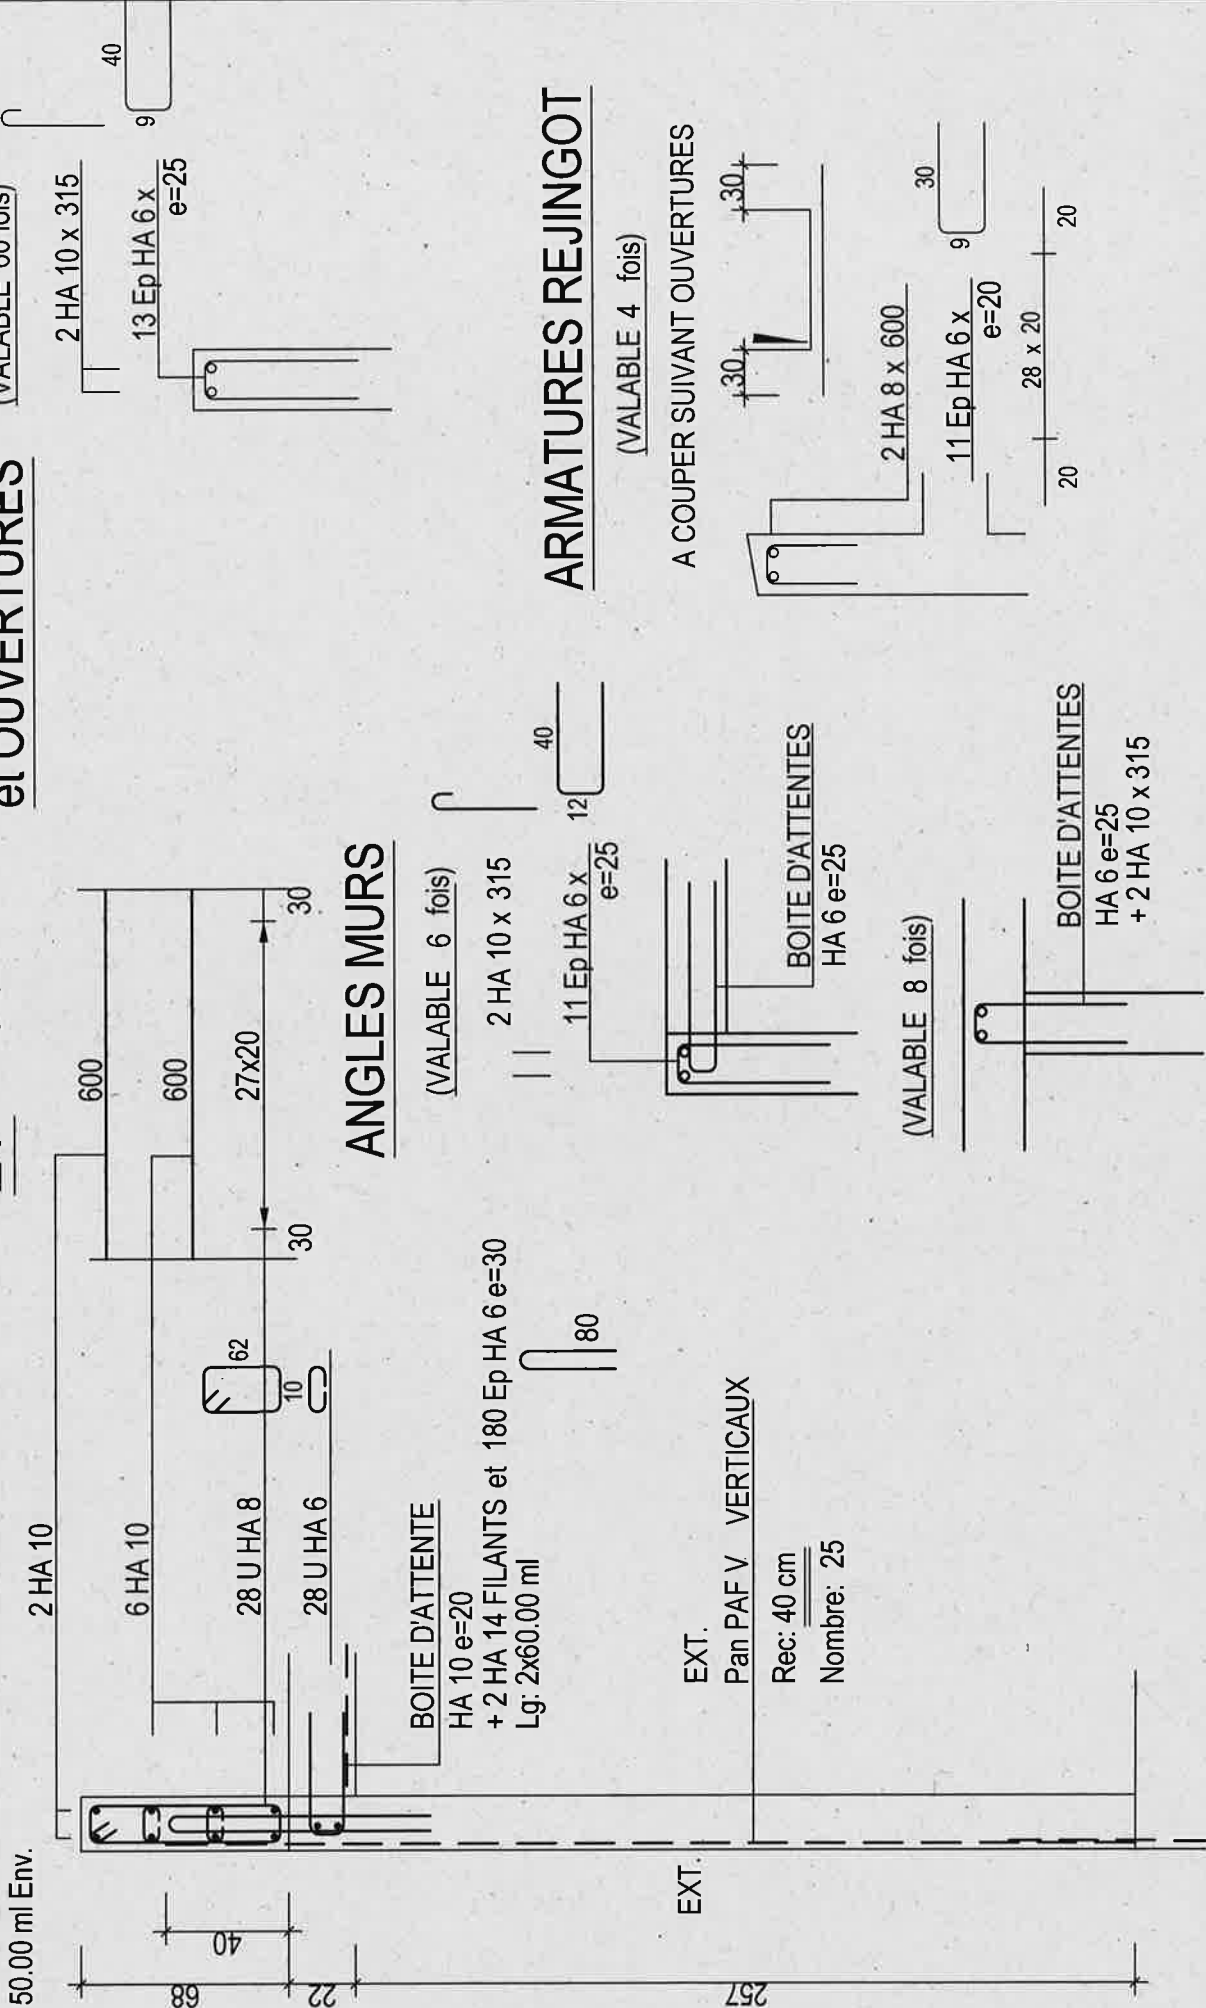



MURS EXTERIEURS AVEC CASQUETTES

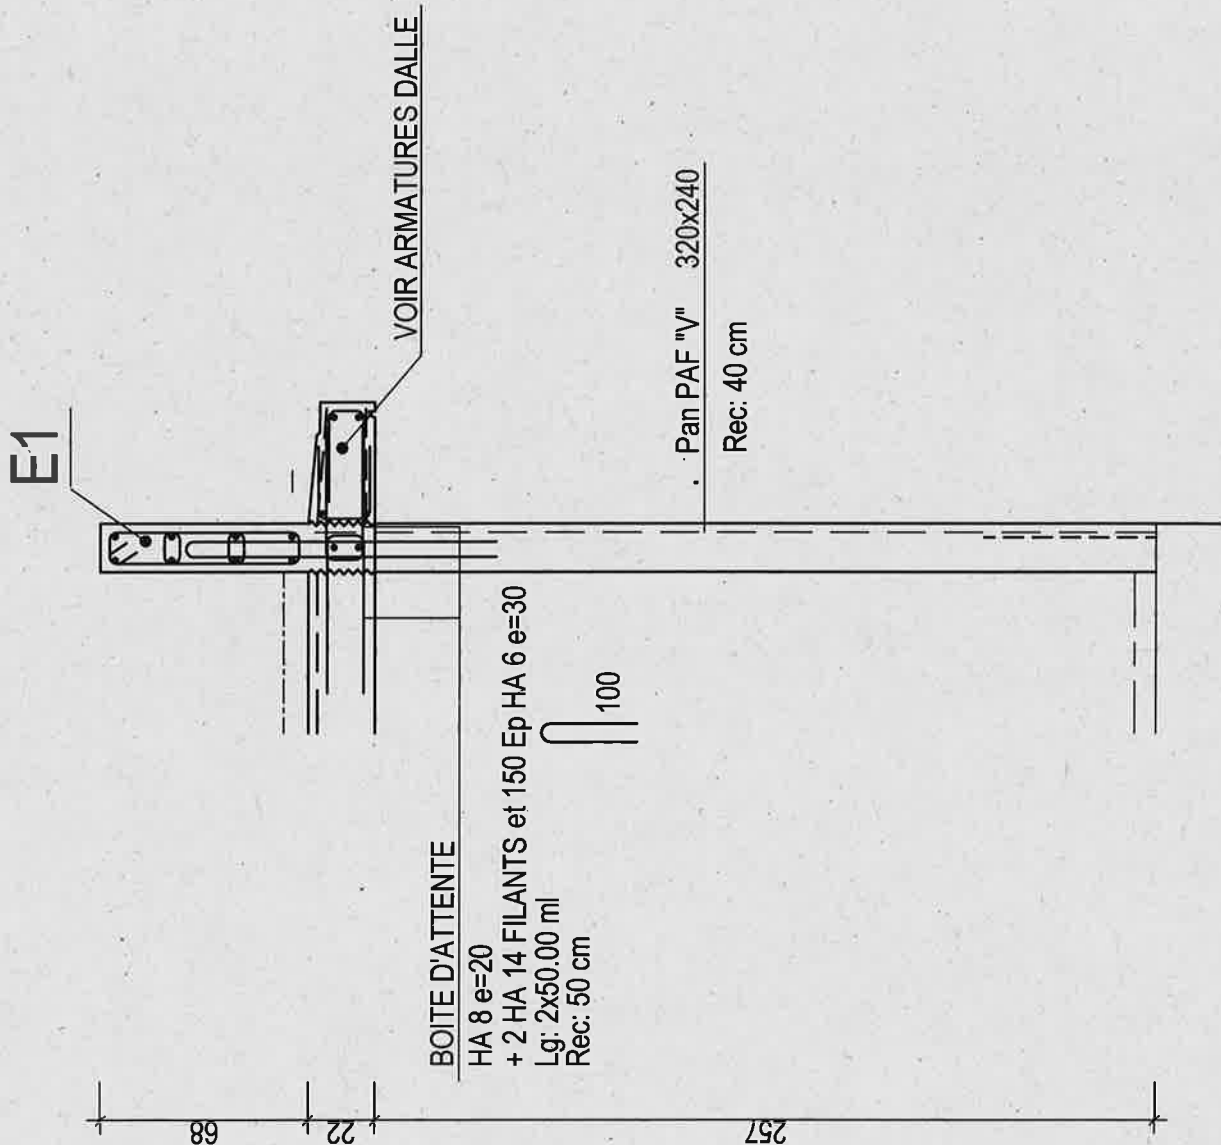

MURS INTERIEURS SANS CONTINUITE

ARMATURES TETES DE MURS

125.00 ml Env:

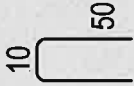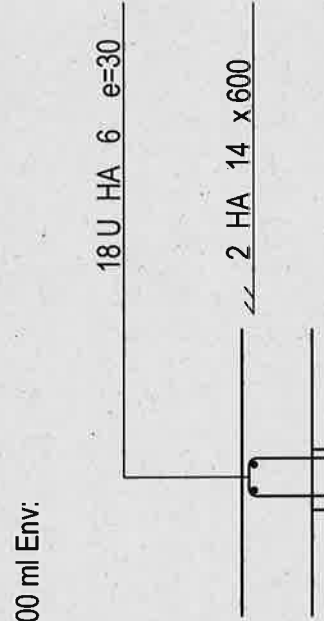


(VALABLE 24 fois)


(VALABLE 4 fois)

2 HA 10 x 270

11 Ep HA 6 x e=25

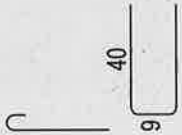


ANGLES MURS

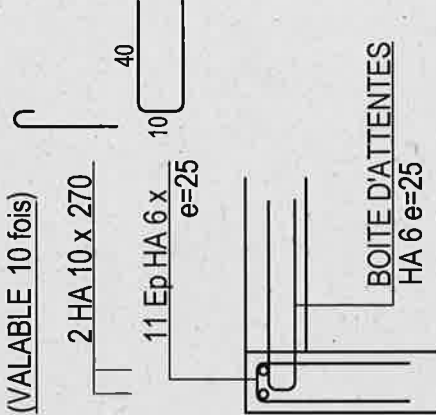

(VALABLE 10 fois)

2 HA 10 x 270

11 Ep HA 6 x e=25

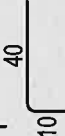

BOITE D'ATTENTES
HA 6 e=25

BOITE D'ATTENTES
HA 6 e=25
+ 2 HA 10 x 270


(VALABLE 8 fois)


PV6

Nombre: 1

E6a


ELEVATION

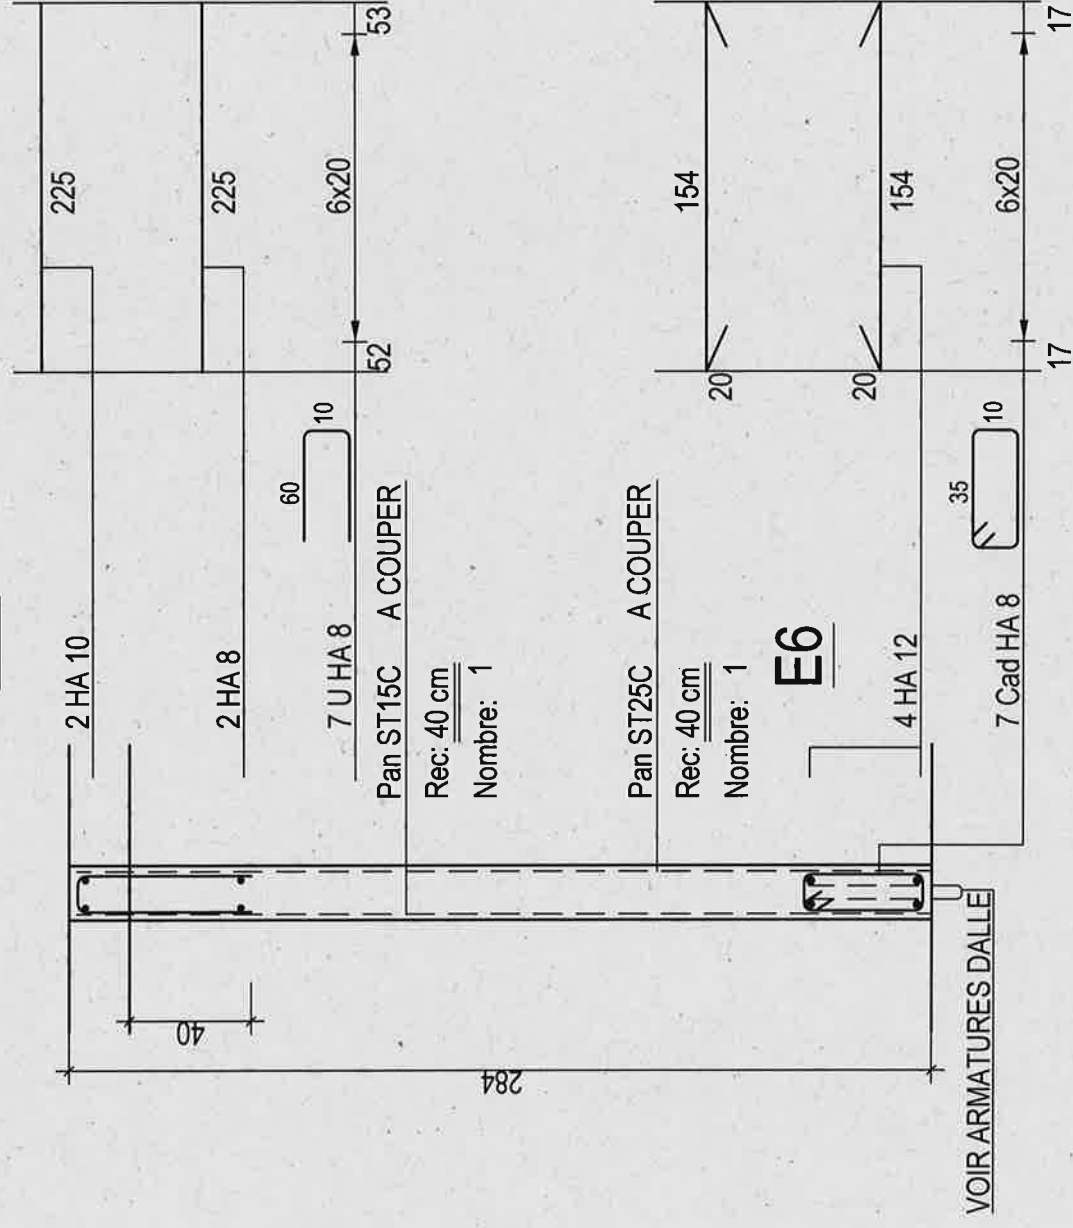

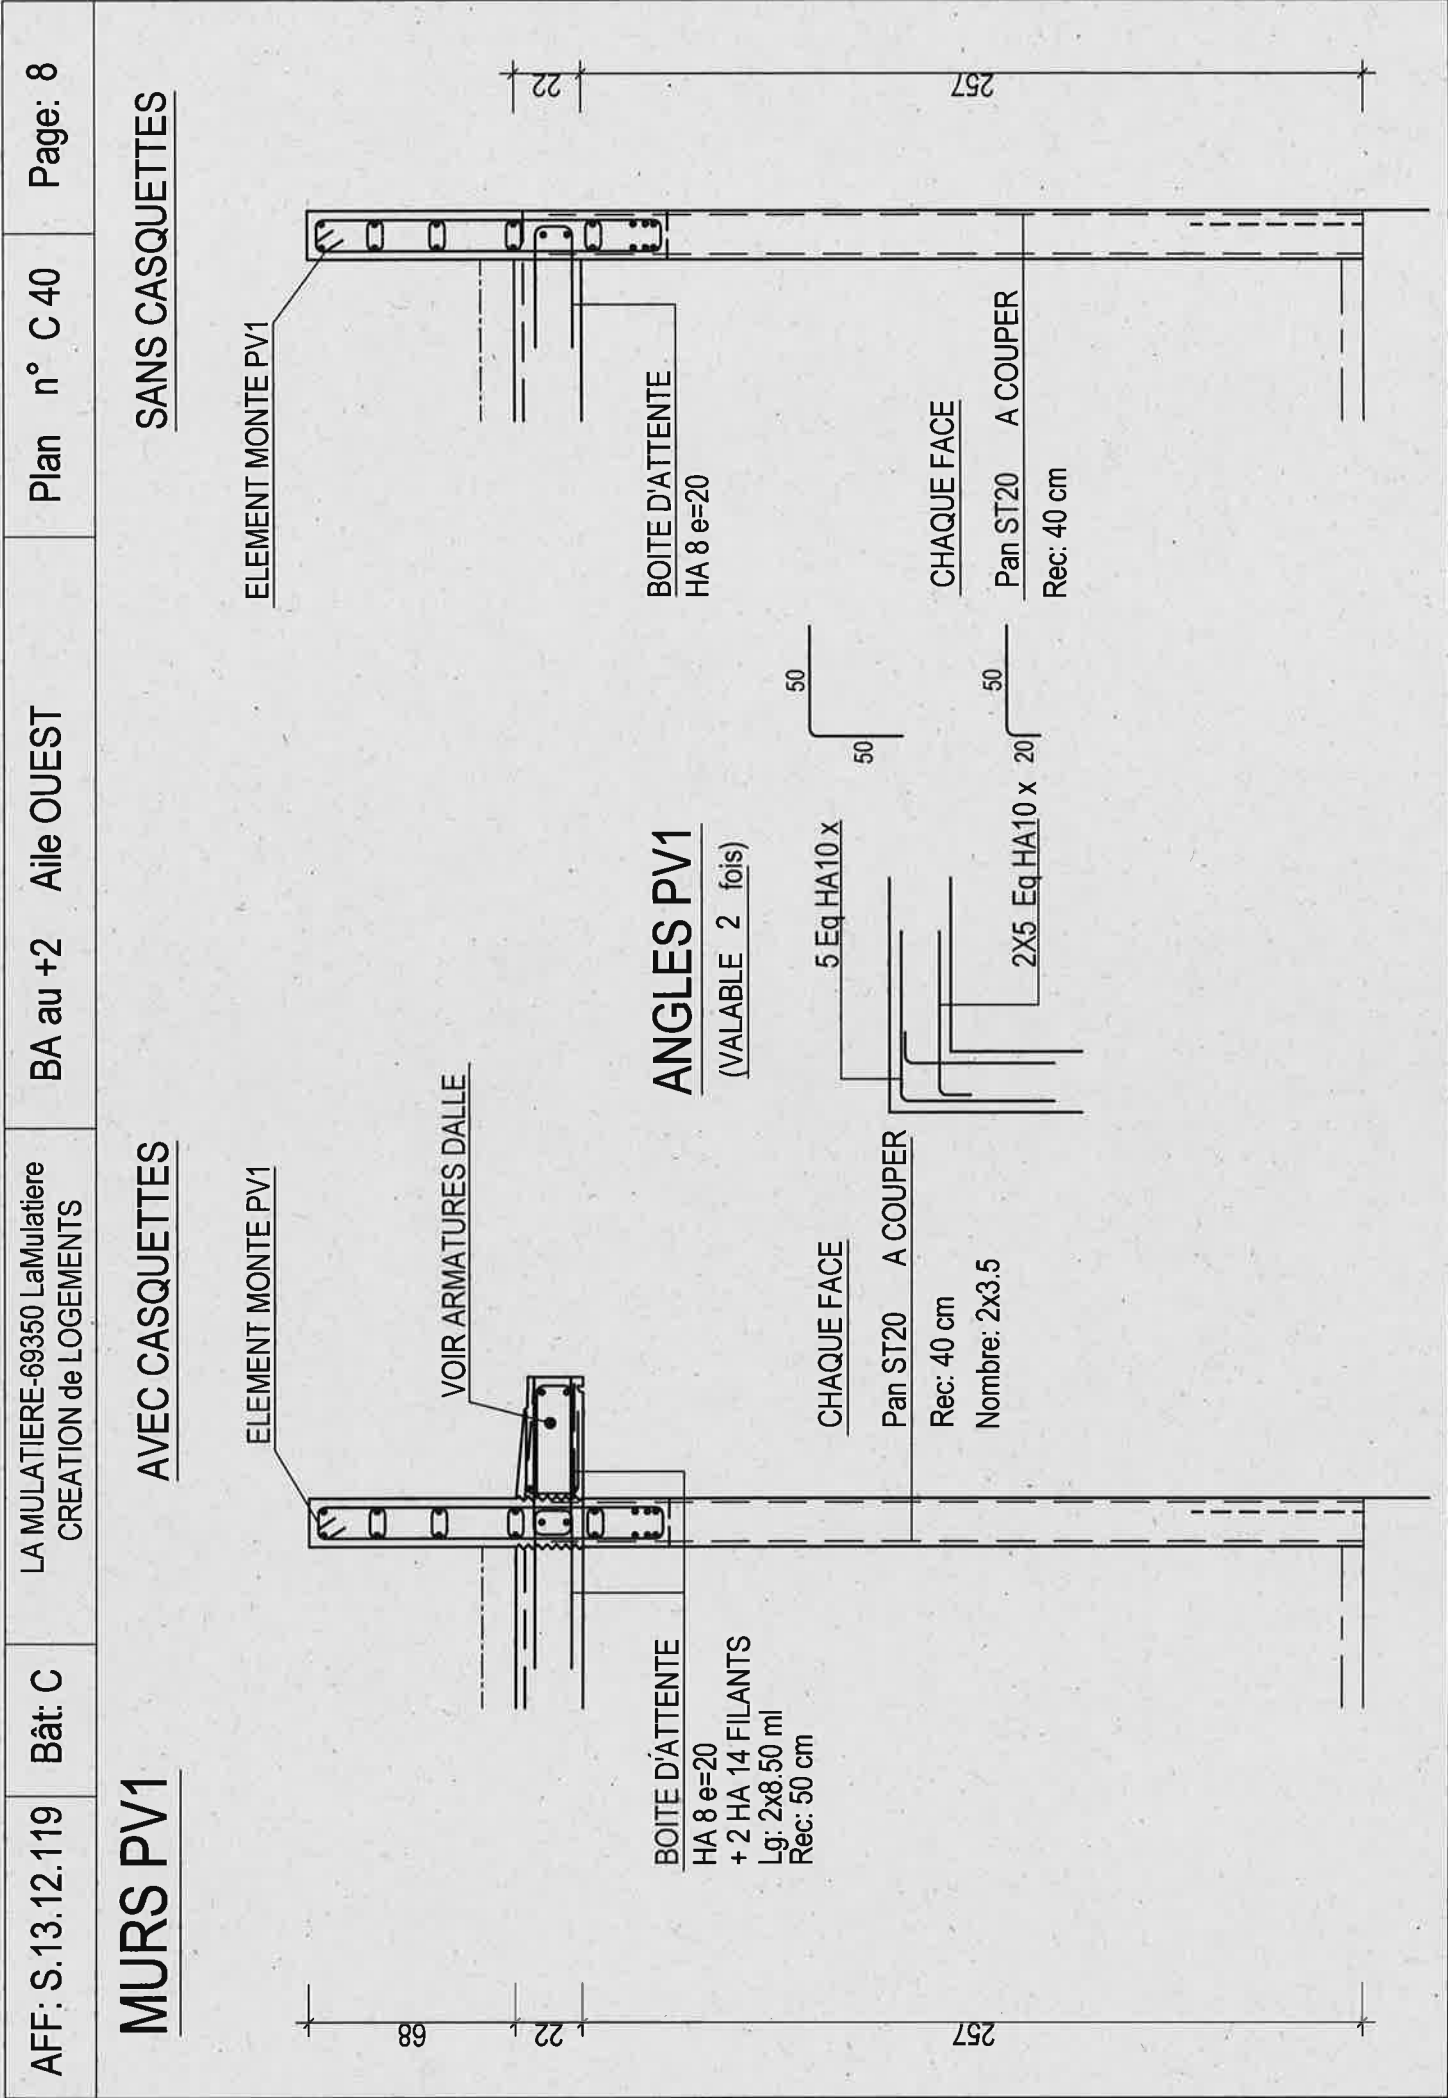


- Date 06/07/15 - 10 étages -
Section : 16 x 118ht
fck= 25 MPa fyk= 500 MPa

Elévation
Echelle=1/50

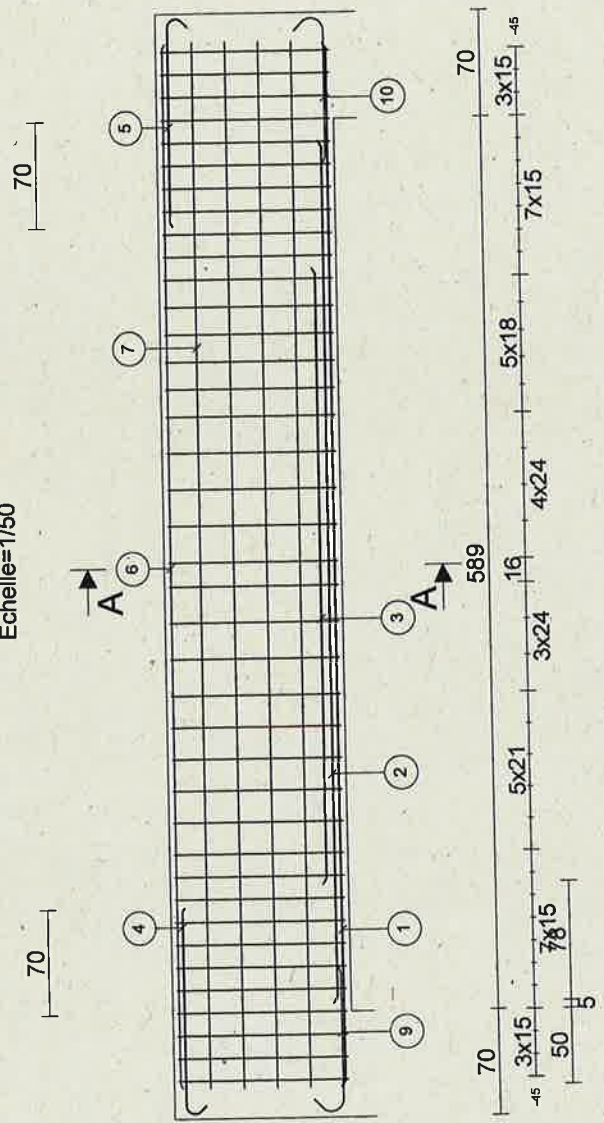


Coupe A-A
Echelle=1/25

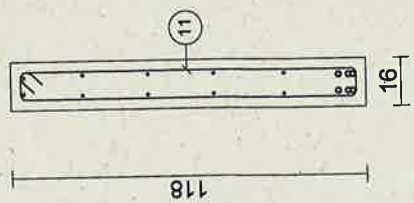

Barre	Lg	Forme
1 2HA16	689	689
2 2HA16	569	569
3 2HA16	407	407
4 2HA10	149	137 135°
5 2HA10	149	135° 137
6 2HA10	689	689
7 8HA8	690	690
8 48HA8	27	9
9 2HA16	115	135° 97
10 2HA16	115	97 135°
11 39HA8	254	10
182°		
C40		
Barre	Lg/Poids	
HA8	166.8/65.9	
HA10	19.7/12.2	
HA16	37.9/59.8	

MURS PV2

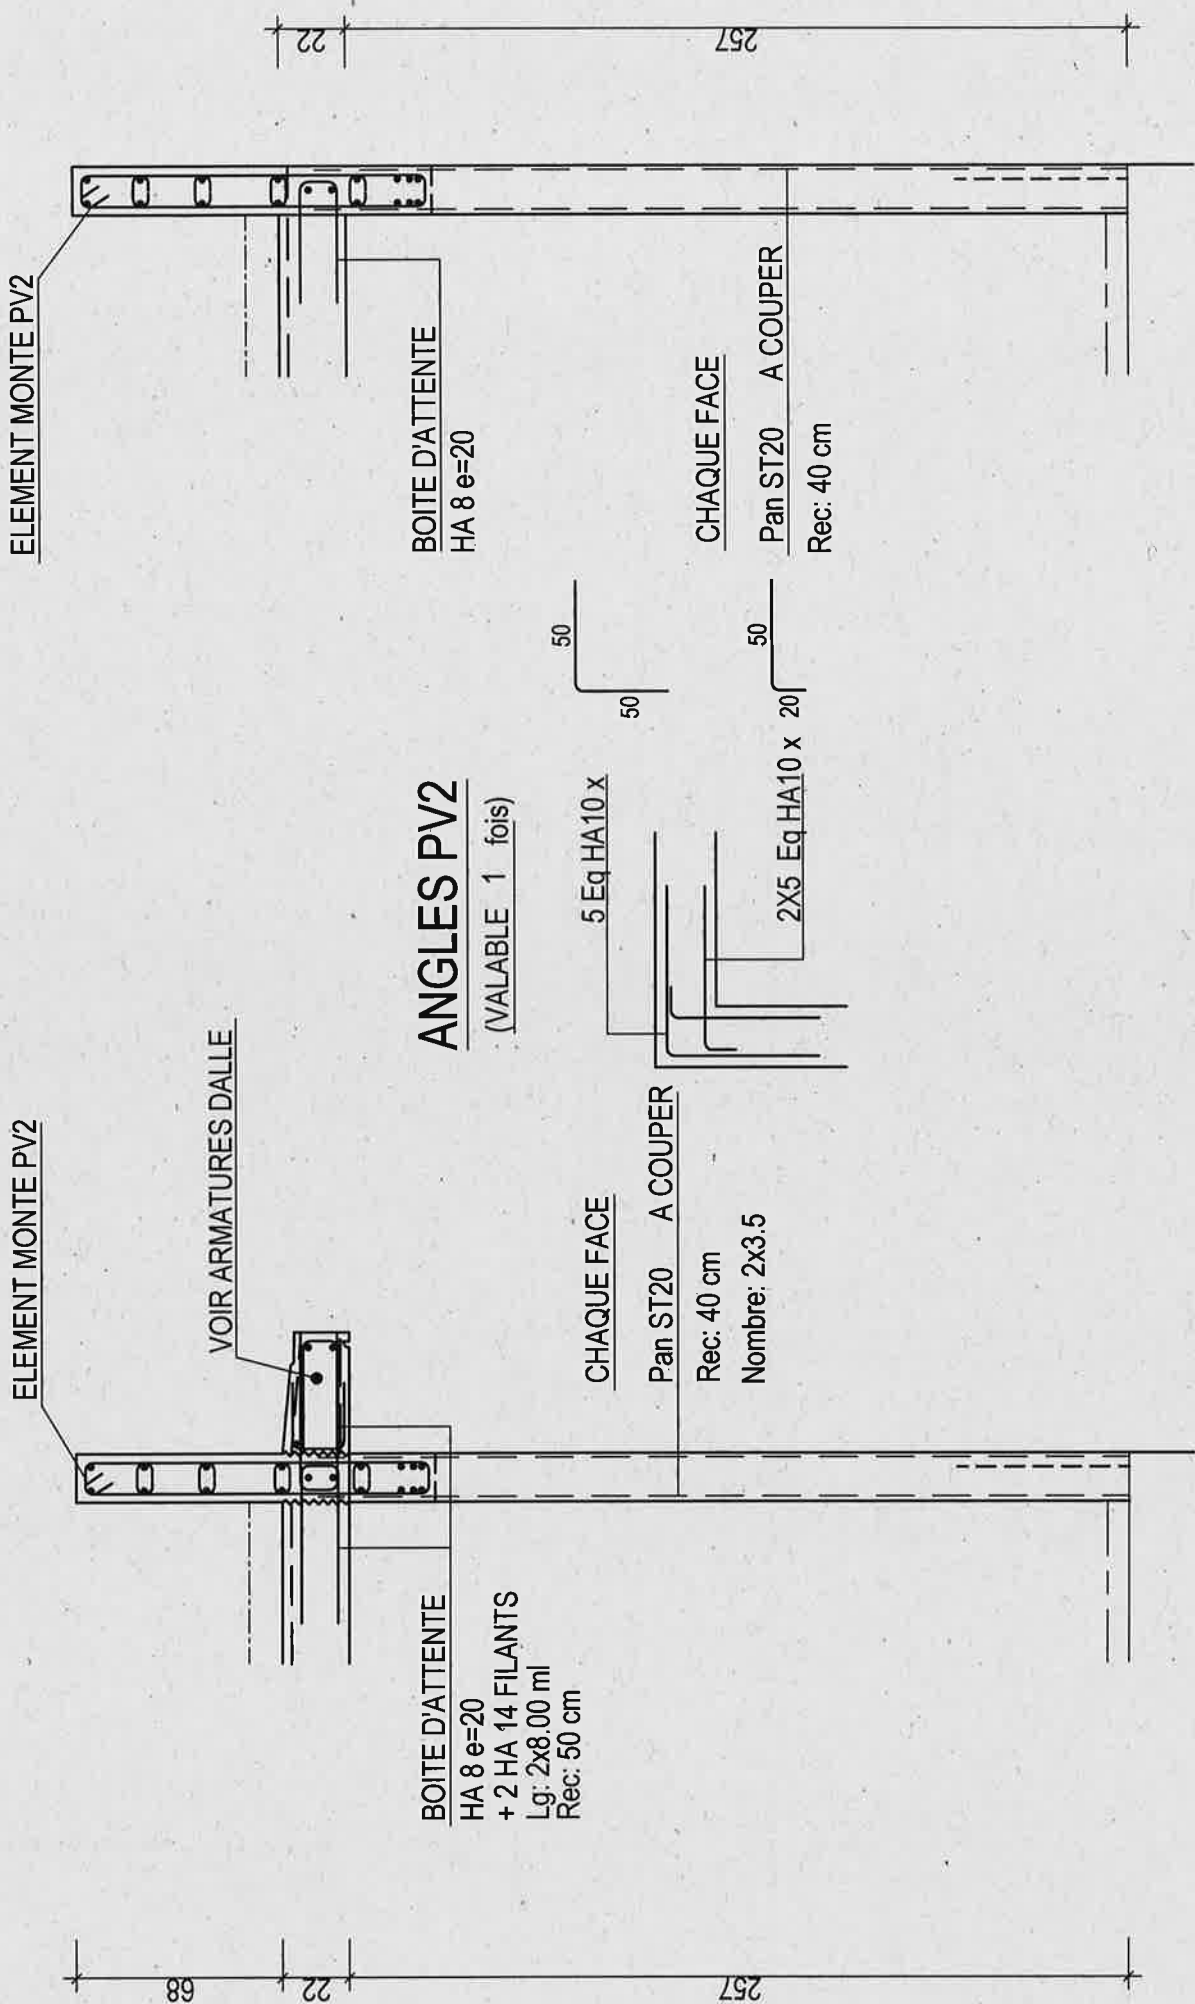


- Date 06/07/15 - 10 étages -


Section : 16 x 118ht

fck= 25 MPa fyk= 500 MPa

Elévation
Echelle=1/50

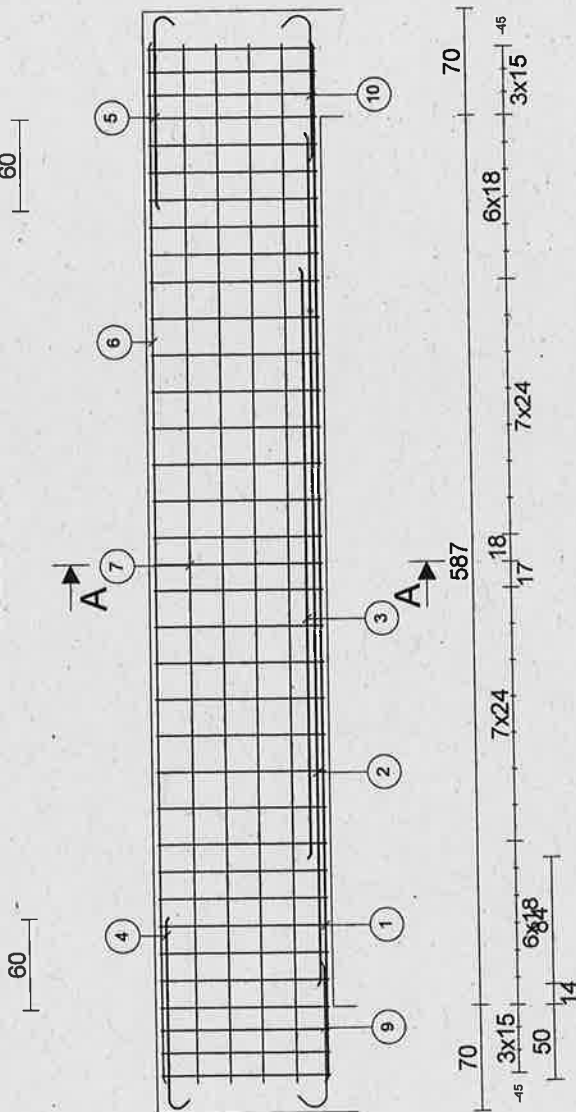


Coupe A-A
Echelle=1/25

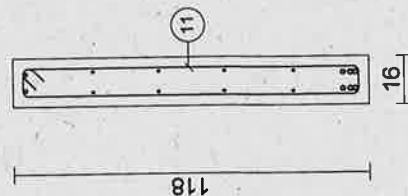

Barre	Lg	Forme
1 2HA14	687	687
2 2HA14	563	563
3 2HA12	390	390
4 2HA10	139	127 135°
5 2HA10	139	135° 127
6 2HA10	687	687
7 8HA8	685	685
8 48HA8	27	9
9 2HA14	114	135° 97
10 2HA14	114	97 135°
11 35HA8	254	10
160		
C40		
Barre	Lg/Poids	
HA8	156.3/61.7	
HA10	19.3/11.9	
HA12	7.8/6.9	
HA14	29.6/35.7	

MURS PV7

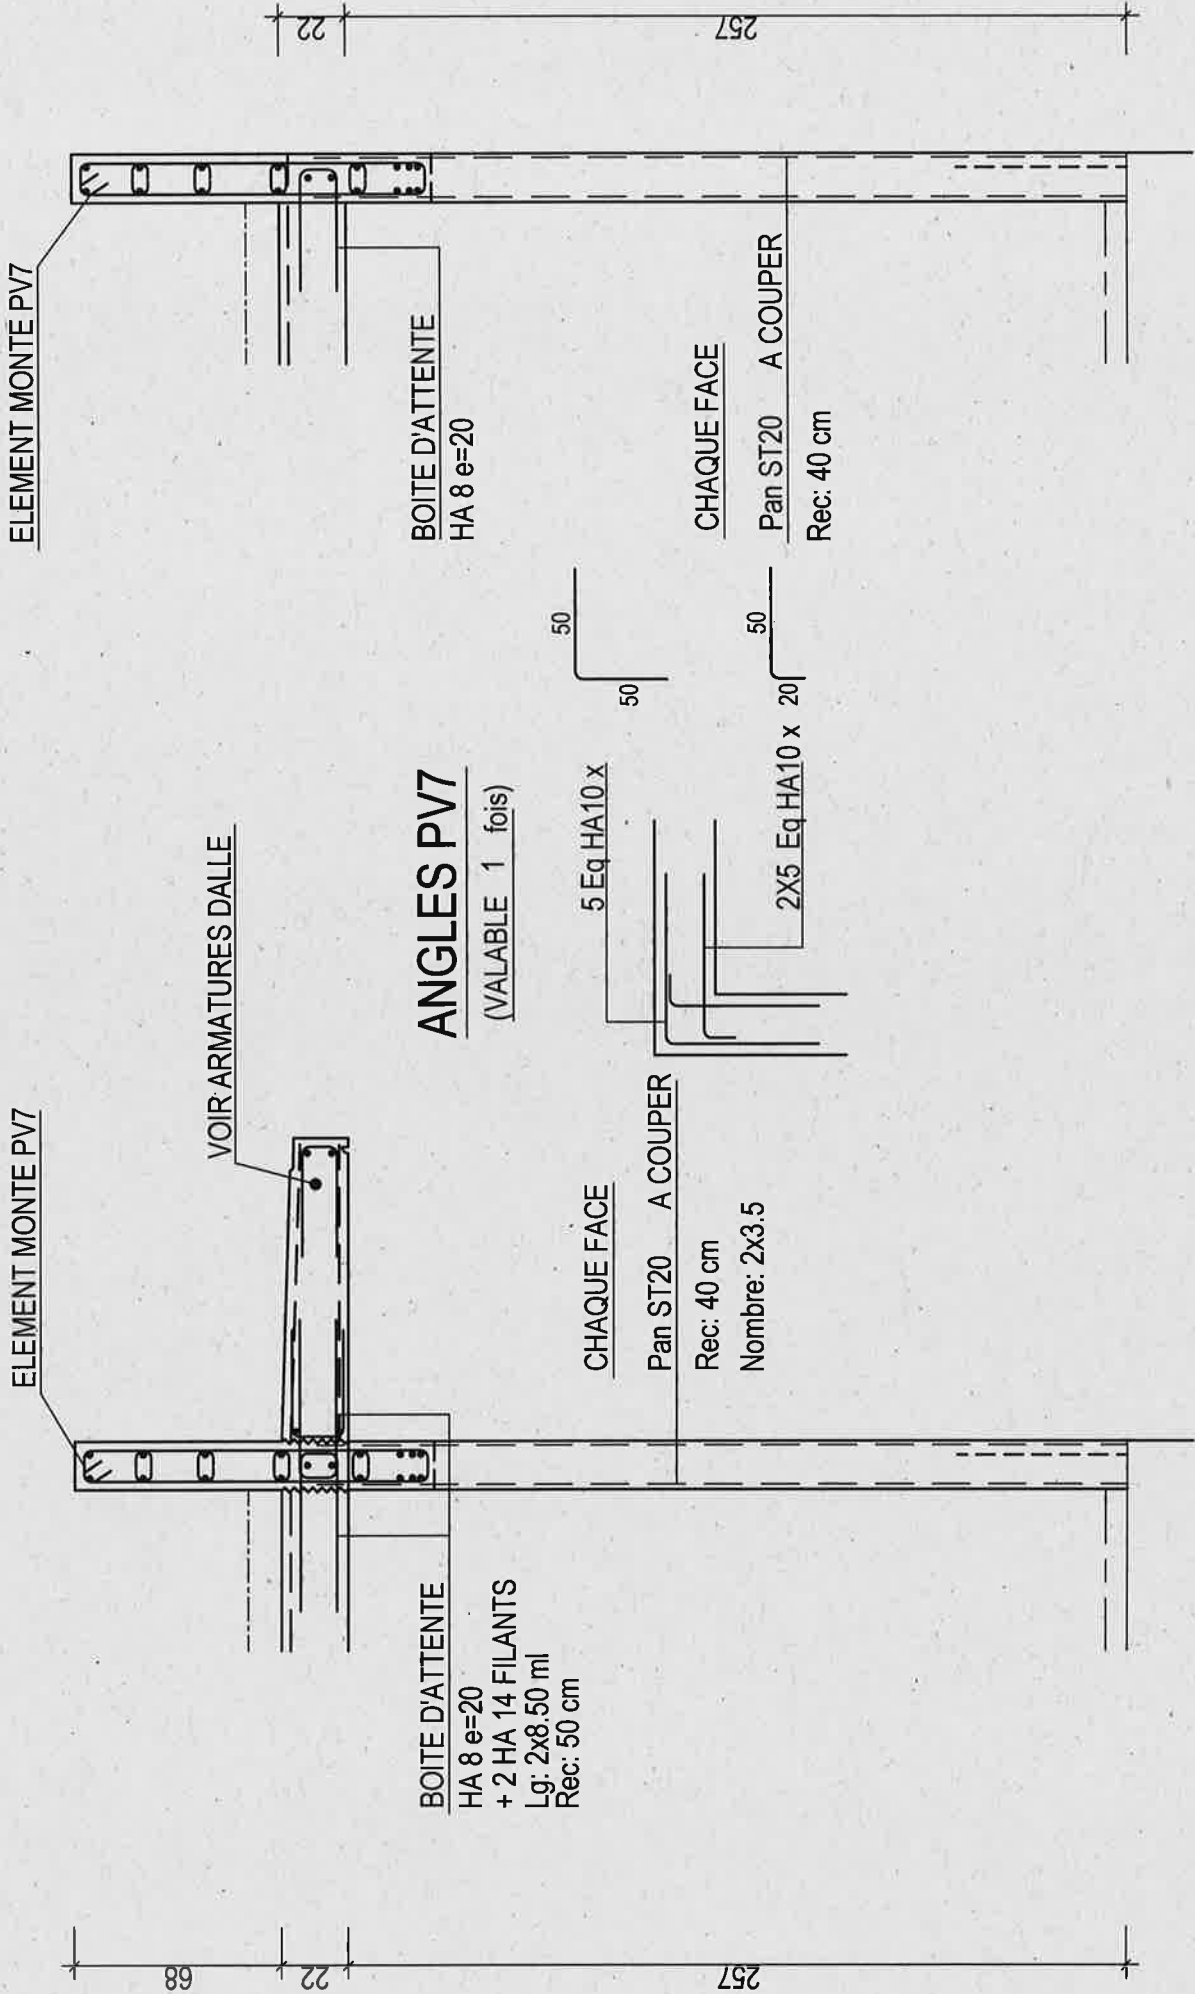


- Date 06/07/15 - 10 étages -


Section : 16 x 118ht

fck= 25 MPa fyk= 500 MPa

Elévation
Echelle=1/50

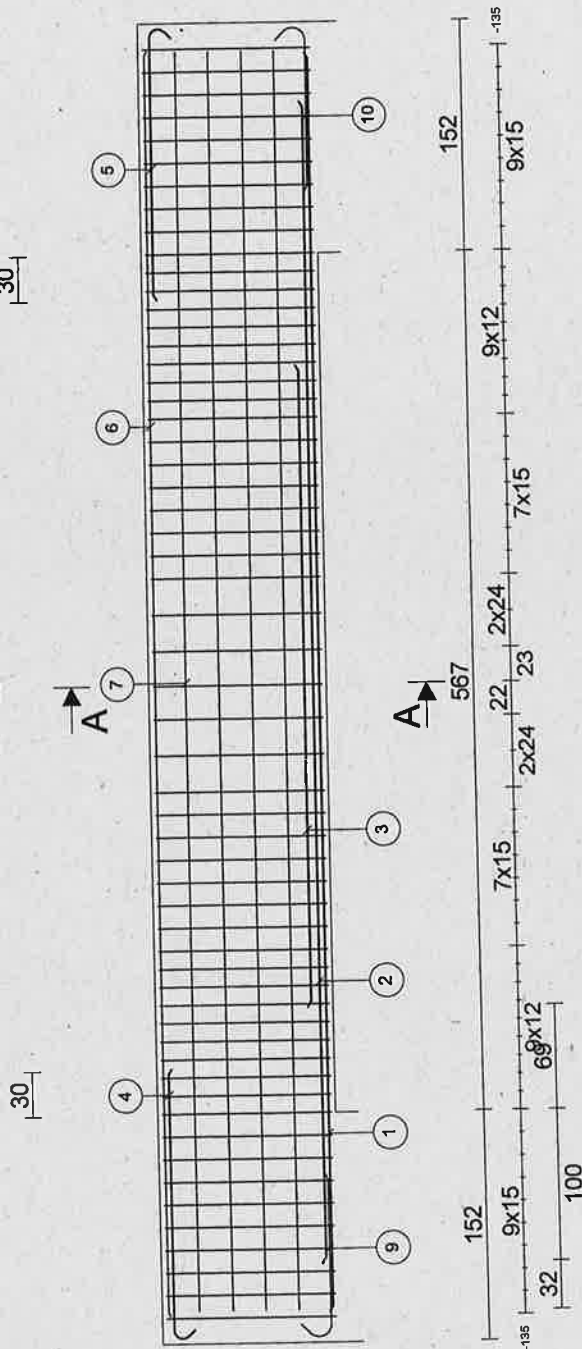


Coupe A-A
Echelle=1/25

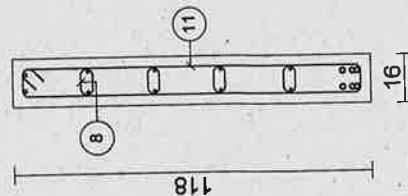

Barre	Lg	Forme
1 2HA16	831	831
2 2HA16	767	767
3 2HA16	424	424
4 2HA12	192	179 135°
5 2HA12	192	135° 179
6 2HA10	835	835
7 8HA8	830	830
8 48HA8	27	9
9 2HA16	127	135° 109
10 2HA16	127	109 135°
11 57HA8	254	10
180° C40		
Barre		Lg/Poids
HA8		223.6/88.3
HA10		16.7/10.3
HA12		7.7/6.8
HA16		45.5/71.9

MURS PV8

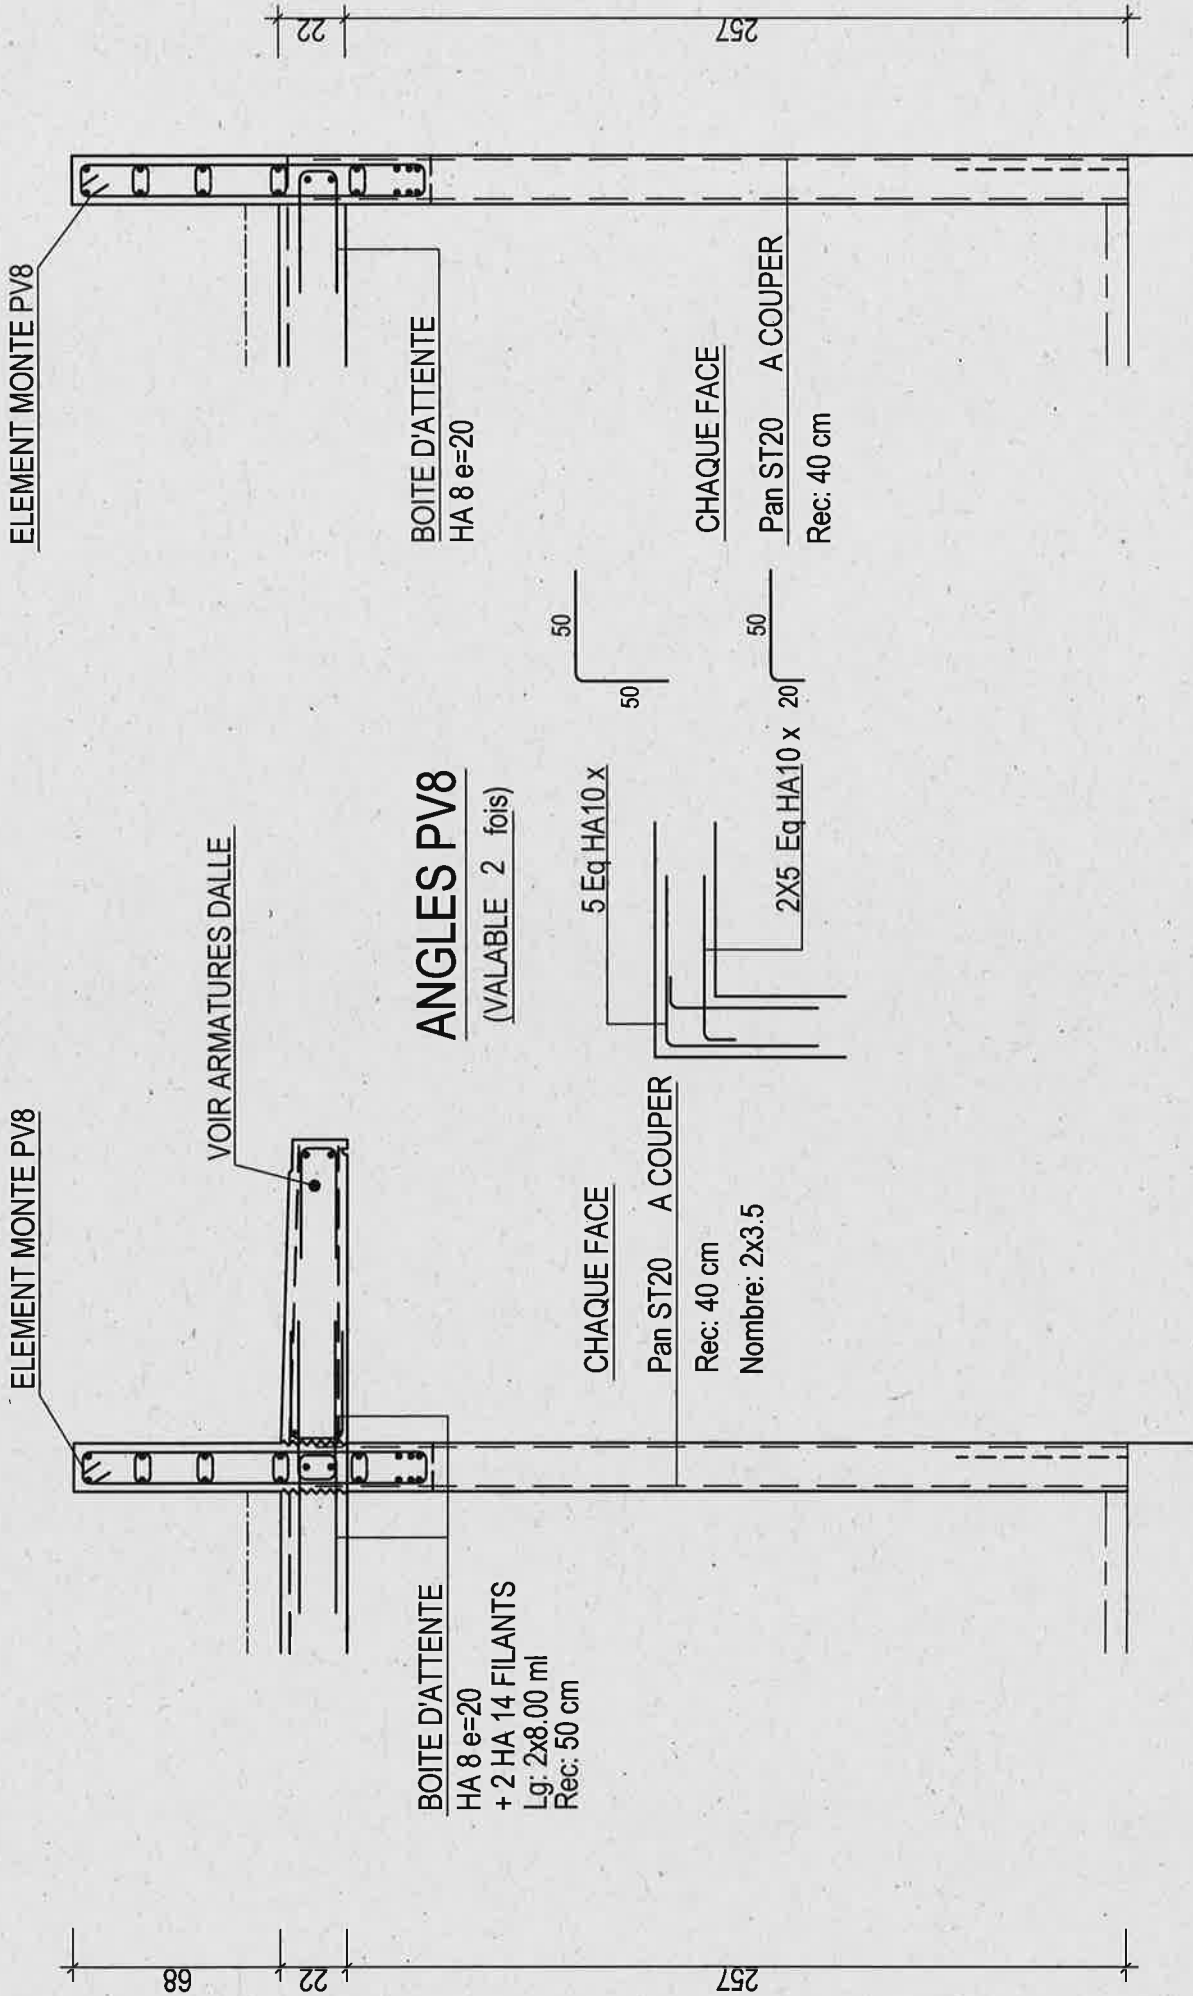


- Date 06/07/15 - 10 étages -


Section : 16 x 118ht



fck= 25 MPa fyk= 500 MPa

Elévation
 Echelle=1/50

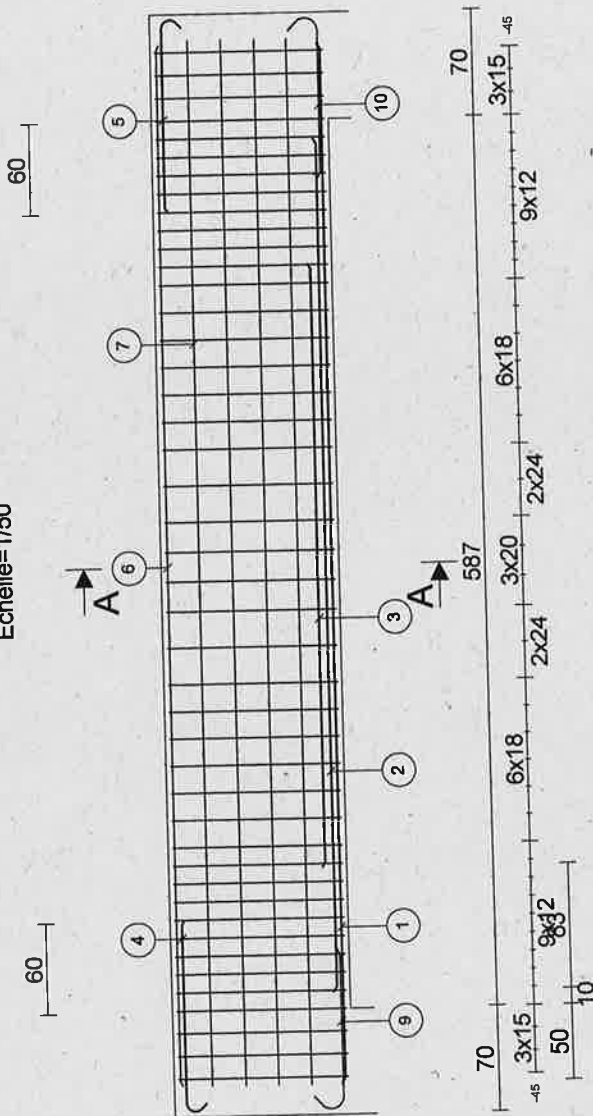


Coupe A-A
 Echelle=1/25

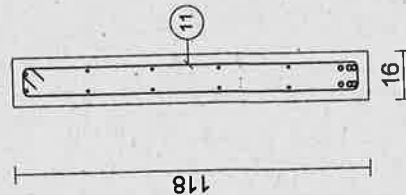

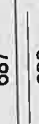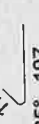
Barre		Lg	Forme
1	2HA16	687	
2	2HA16	564	
3	2HA14	399	
4	2HA10	139	
5	2HA10	139	
6	2HA10	687	
7	8HA8	690	
8	48HA8	27	
9	2HA16	125	
10	2HA16	125	
11	44HA8	254	


AFF: S.13.12.119	Bât: C	LA MULATIERE-69350 LaMulatiere CREATION de LOGEMENTS	BA au +2	Aile OUEST	Plan n° C 40	Page: 18
<						

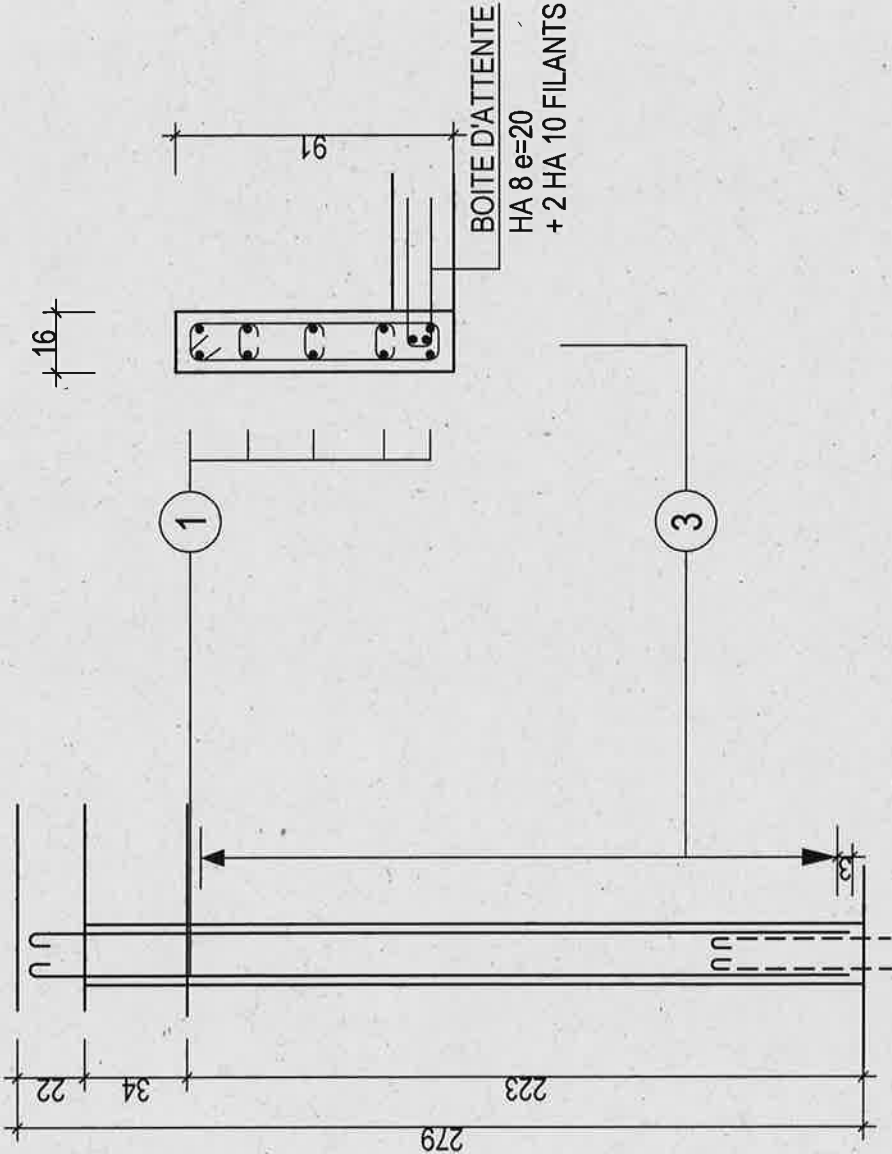


AFF: S.13.12.119	Bât: C	LA MULATIERE-69350 LaMulatiere CREATION de LOGEMENTS	BA au +2	Aile OUEST	Plan	n° C 40	Page: 19
P4 Nombre: 1 16x43					1 4 HA 12 x		
2							
3	13 HA 6 x				37 10		
4							
5							
6							
7							
8							
9							
10							
11							
12							
13							
14							
15							

AFF: S.13.12.119	Bât: C	LA MULATIERE-69350 LaMulatiere CREATION de LOGEMENTS	BA au +2	Aile OUEST	Plan n° C 40	Page: 20
P5			Nombre: 1			16x87
1	10 HA 12 x					
2						
3	13 HA 6 x					
4	3x13 HA 6 x					
5						
6						
7						
8						
9						
10						
11						
12						
13						
14						
15						

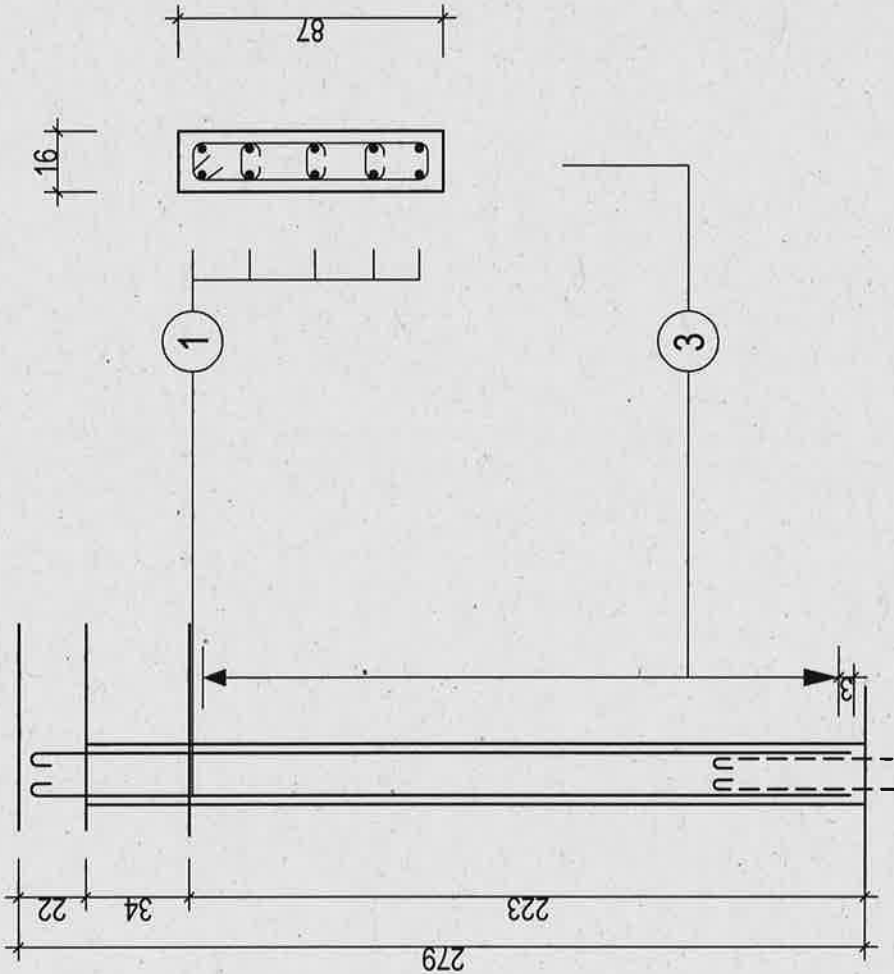

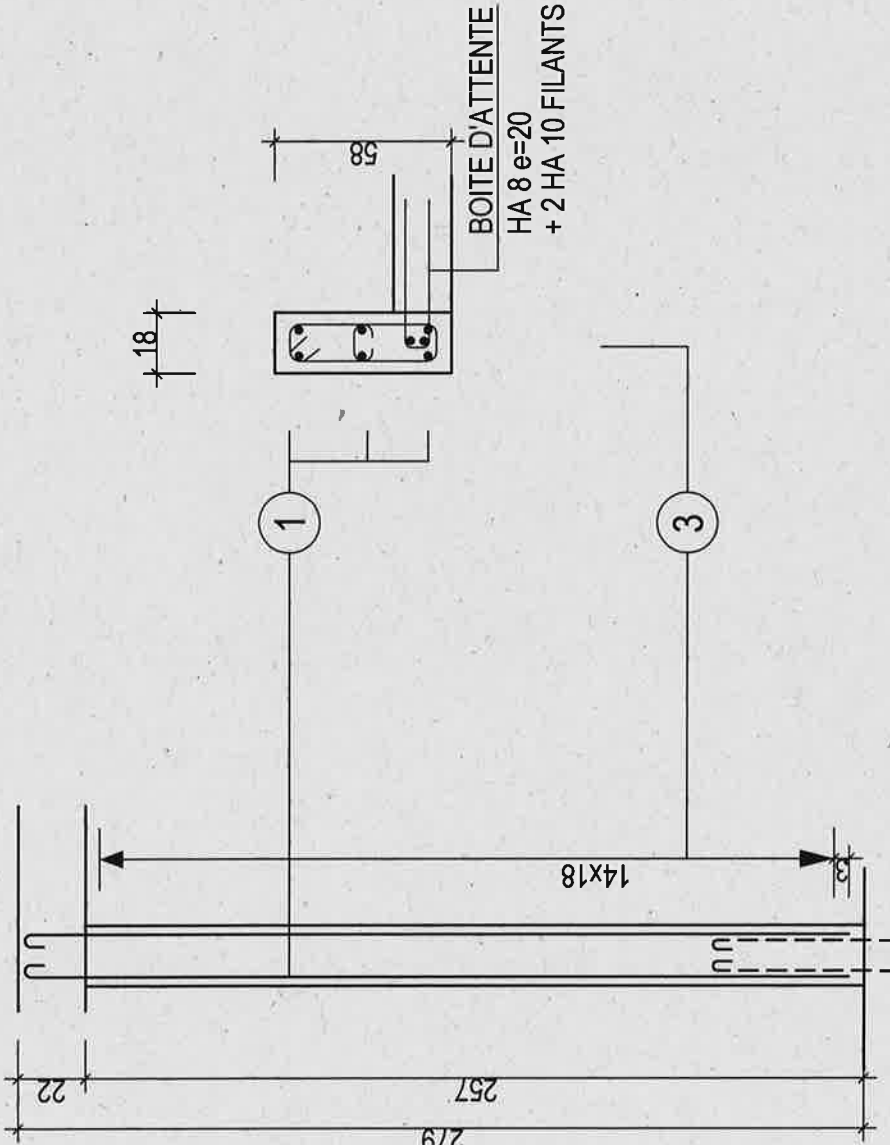AFF: S.13.12.119	Bât: C	LA MULATIERE-69350 LaMulatiere CREATION de LOGEMENTS	BA au +2	Aile OUEST	Plan n° C 40	Page: 21
P6 Nombre: 1 18x58						
						
①	8 HA 12 x					
②						
③	15 HA 6 x					
④	2x15 HA 6 x					
⑤						
⑥						
⑦						
⑧						
⑨						
⑩						
⑪						
⑫						
⑬						
⑭						
⑮						

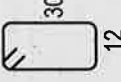AFF: S.13.12.119	Bât: C	LA MULATIERE-69350 LaMulatiere CREATION de LOGEMENTS	BA au +2	Aile OUEST	Plan n° C 40	Page: 23
L Nombre: 8		La Nombre: 1		Lb Nombre: 2		
 4 HA 10 5 Cad HA 6 20 135 20 28 4x20 27 		 4 HA 12 9 Cad HA 6 20 194 20 17 8x20 17 		 4 HA 10 7 Cad HA 6 20 165 20 22 6x20 23 		

LINTEAUX

L1


Nombre: 2
PORTEE: 97

L3

Nombre: 16
PORTEE: 192

L5


Nombre: 1
PORTEE: 102

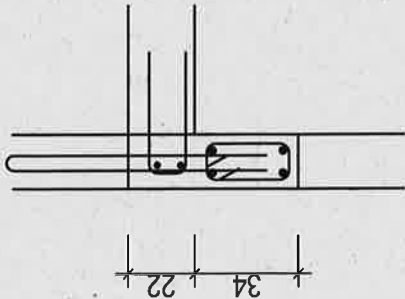

2 HA 10


2 HA 10

5 Cad HA 6

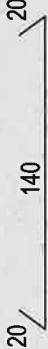

L1





Nombre: 2
PORTEE: 97

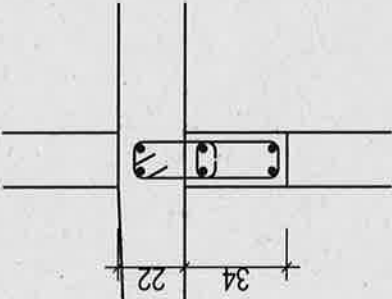

4 HA 10

2 HA 10

5 Cad HA 6 + 5 Ep HA 6

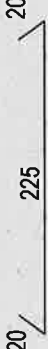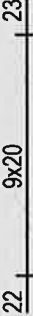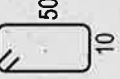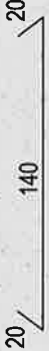

2 HA 10

2 HA 16

10 Cad HA 6



2 HA 10

2 HA 10

5 Cad HA 6




Date 06/07/15 - 10 étages -
Section : 16 x 56ht


Coupe feu R 120

fck= 25 MPa fyk= 500 MPa

Elévation
Echelle=1/20

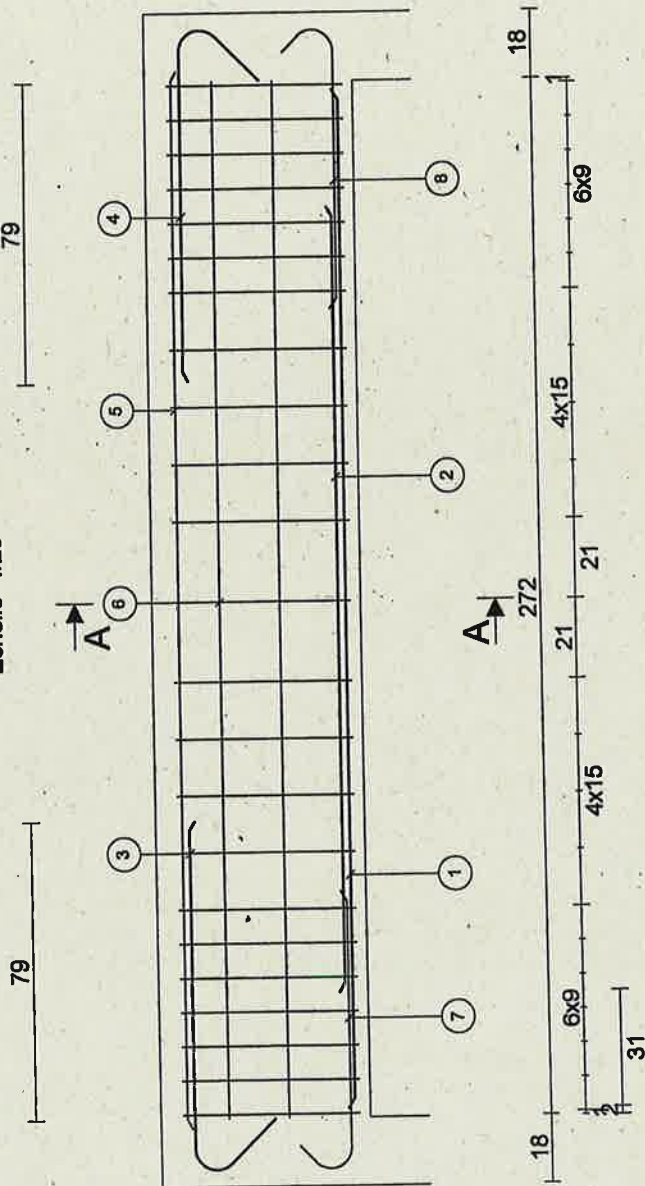

Coupe A-A
Echelle=1/20

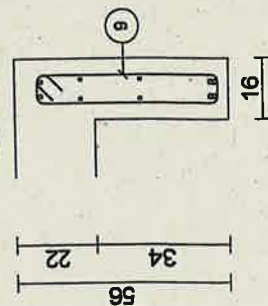

Barre		Lg	Forme
1	2HA12	268	<u>268</u>
2	2HA10	207	<u>207</u>
3	2HA10	116	<u>93 135°</u>
4	2HA10	116	<u>135° 93</u>
5	2HA10	278	<u>278</u>
6	4HA8	272	<u>272</u>
7	2HA12	87	<u>135° 74</u>
8	2HA12	87	<u>74 135°</u>
9	23HA6	120	47  8
185			
240			


- Date 06/07/15 - 10 étages -

Section : 50 x 22ht

fck= 25 MPa fyk= 500 MPa


Elévation

Echelle=1/33

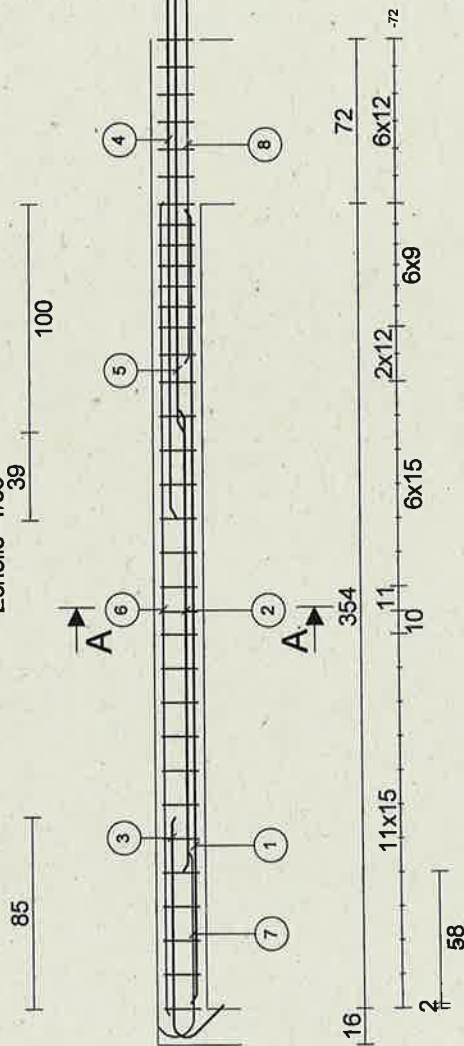

Coupe A-A

Echelle=1/5

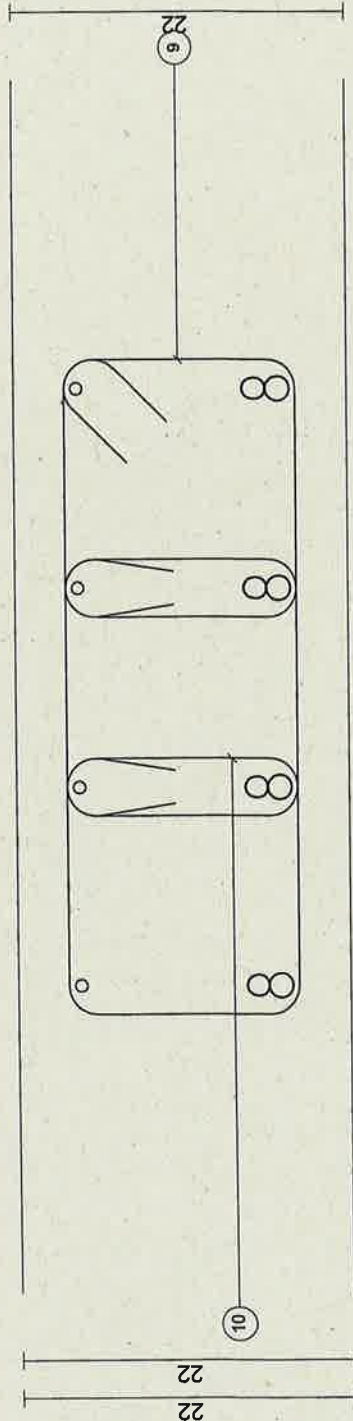

Barre	Lg	Forme
1 4HA16	350	350
2 4HA14	204	204
3 4HA10	122	98 135°
4 4HA20	354	354
5 4HA16	272	272
6 4HA8	358	358
7 4HA14	101	135° 83
8 4HA12	212	212
9 34HA8	130	44
10 68HA8	51	16
Barre	Lg/Poids	
HA8	93.2/36.8	
HA10	4.9/3.0	
HA12	8.5/7.5	
HA14	12.2/14.7	
HA16	24.9/39.3	
HA20	14.2/35.0	


- Date 06/07/15 - 10 étages -

Section: 50 x 22ht

fck= 25 MPa fyk= 500 MPa


Elévation

Echelle=1/25

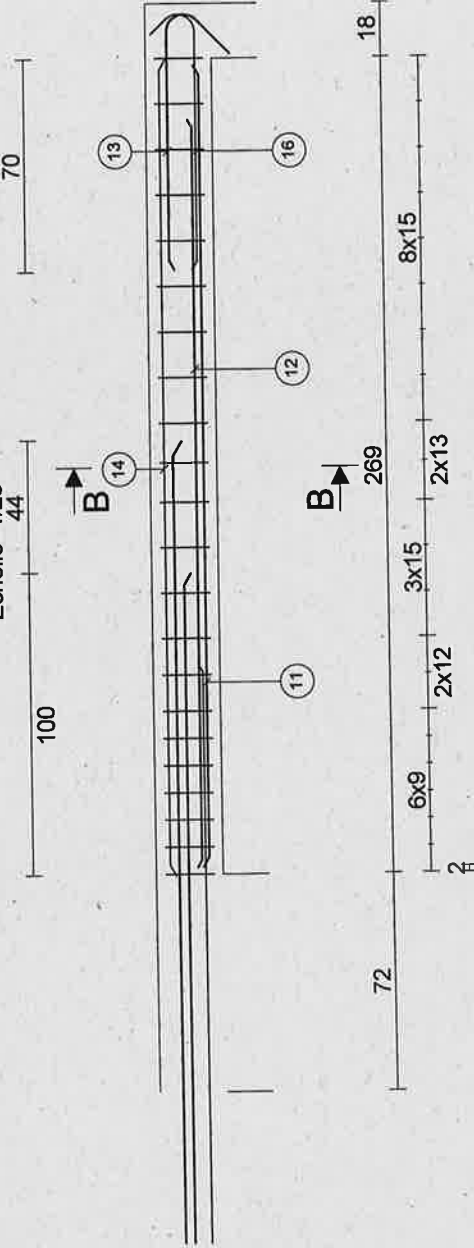

Coupe B-B

Echelle=1/5

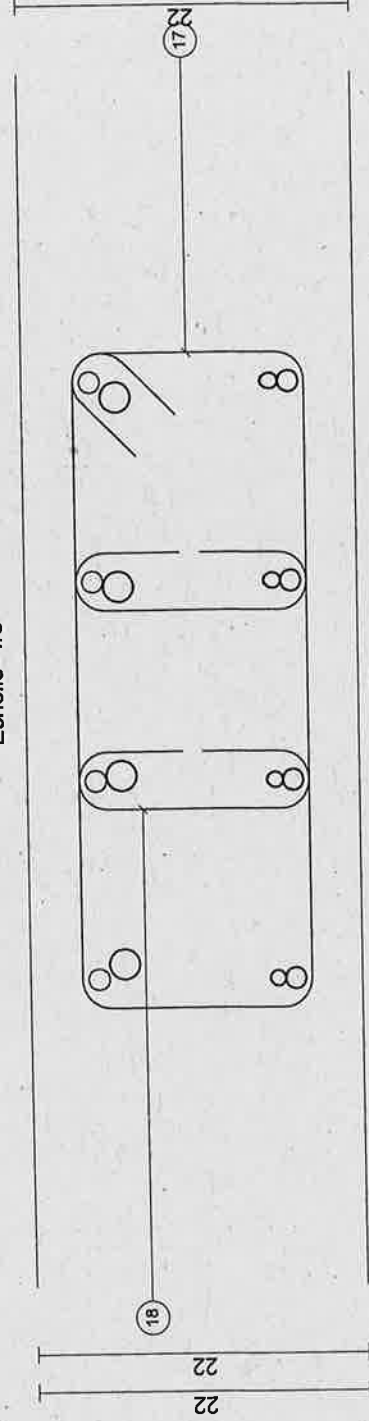


Barre	Lg	Forme
11	4HA14	265
12	4HA10	247
13	4HA12	108
14	4HA14	270
16	4HA12	99
17	22HA8	130
18	44HA8	33
180° 271		
Barre		Lg/Poids
HA8		43.2/17.0
HA10		9.9/6.1
HA12		8.3/7.4
HA14		21.4/25.9

- Date 06/07/15 - 10 étages -


Section : 40 x 22ht

fck= 25 MPa fyk= 500 MPa

Elévation
Echelle=1/25

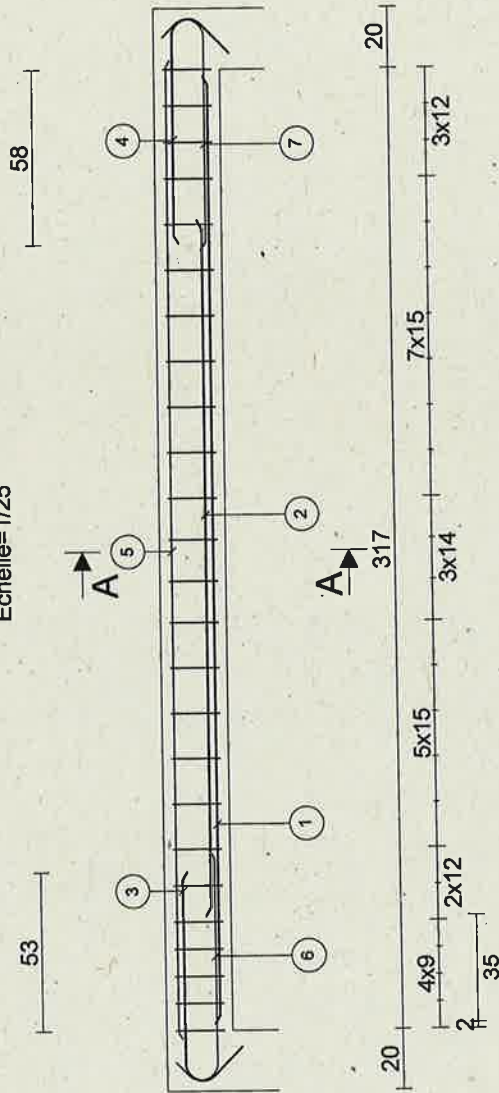

Coupe A-A
Echelle=1/5

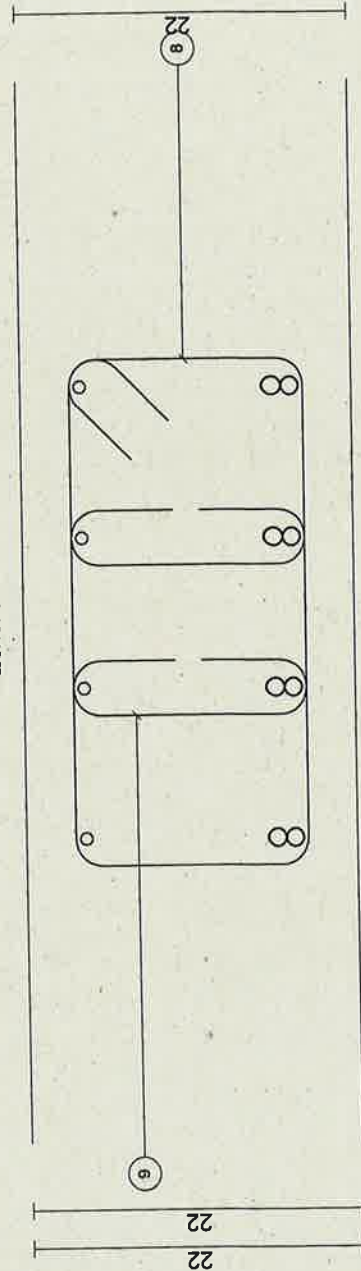


Barre		Lg	Forme
1	4HA12	313	 313
2	4HA12	230	 230
3	4HA10	90	 70 135°
4	4HA10	95	 135° 75
5	4HA8	323	 323
6	4HA12	90	 135° 77
7	4HA12	90	 77 135°
8	25HA6	110	 34
9	50HA6	33	 16

- Date 06/07/15 - 10 étages -


Section : 50 x 22ht


fck= 25 MPa fyk= 500 MPa

Elévation
Echelle=1/20

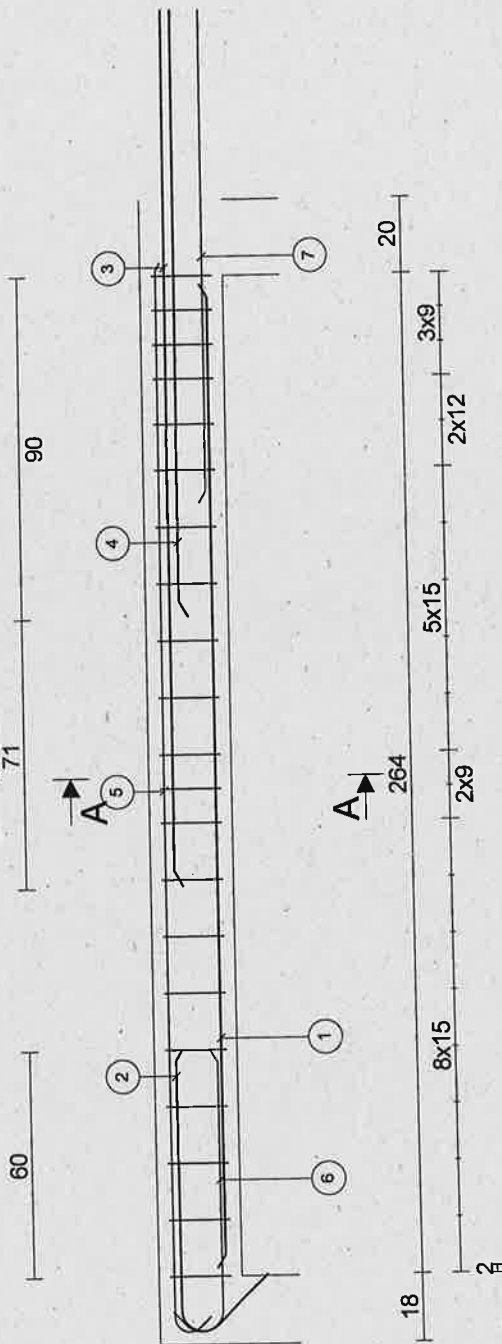


Coupe A-A
Echelle=1/5

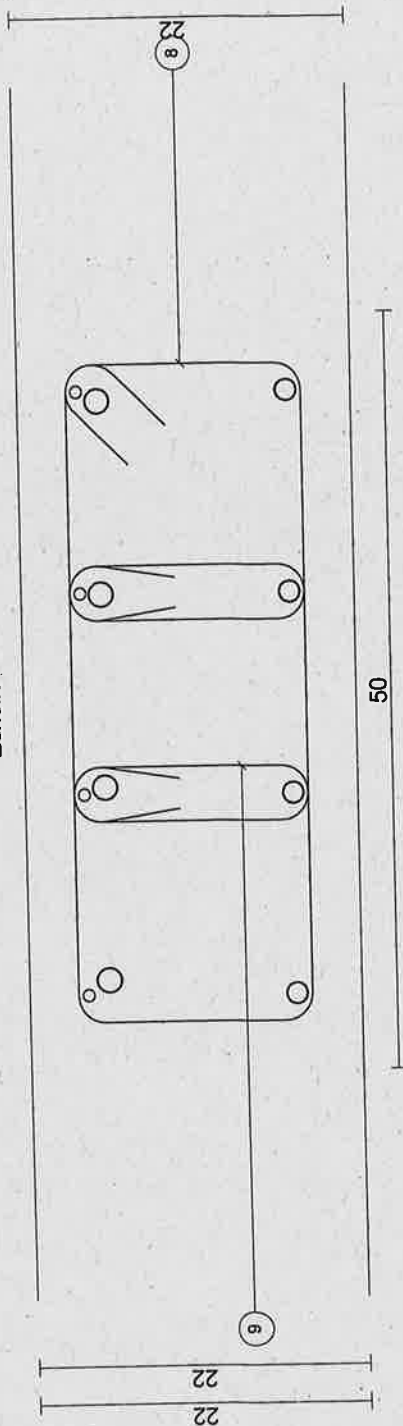

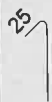Barre		Lg	Forme
1	4HA14	260	260
2	4HA10	101	 75 135°
3	4HA16	307	307
4	4HA16	200	200
5	4HA8	291	 283 135°
6	4HA12	87	 135° 75
7	4HA12	140	140
8	21HA6	130	 90° 44
9	42HA6	51	 16

kg/m3 m²		Eb=3.0 cm Eh=3.0 cm El=3.0 cm		2 -2	
Barre		Lg	Forme		
10	4HA14	405	405		
11	4HA14	249	249		
12	4HA10	122	135° 98		
13	4HA8	413	413		
15	4HA12	97	83 135°		
16	30HA8	130	44		
17	60HA8	51	16		

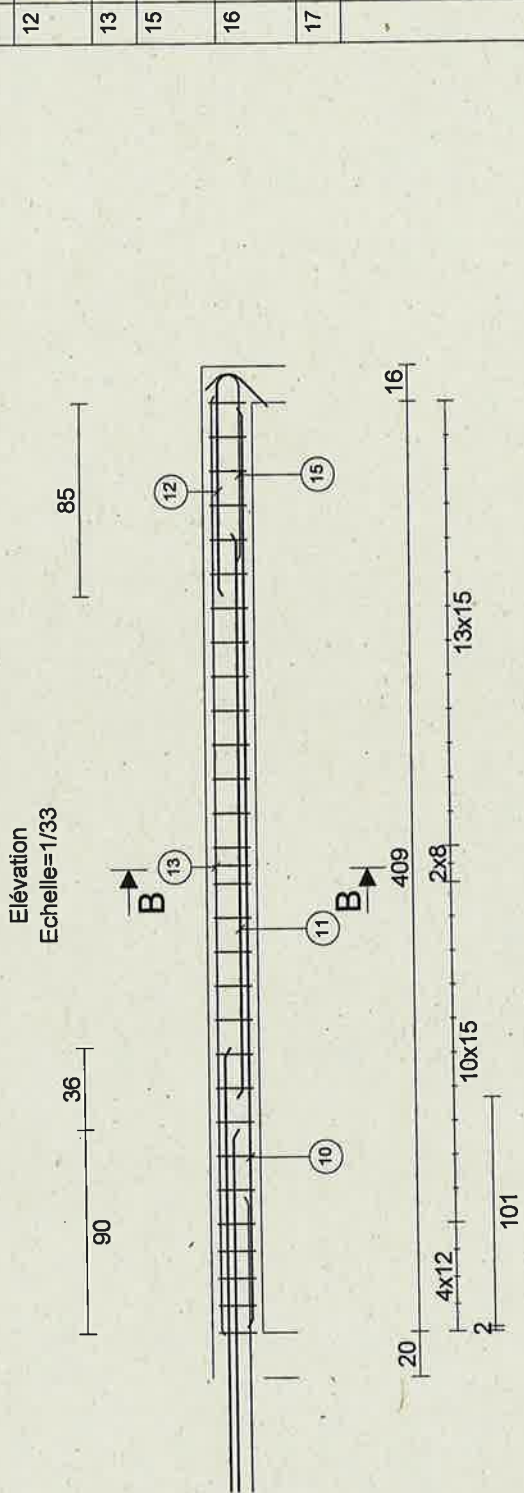

Coupe B-B
Echelle=1/5

