


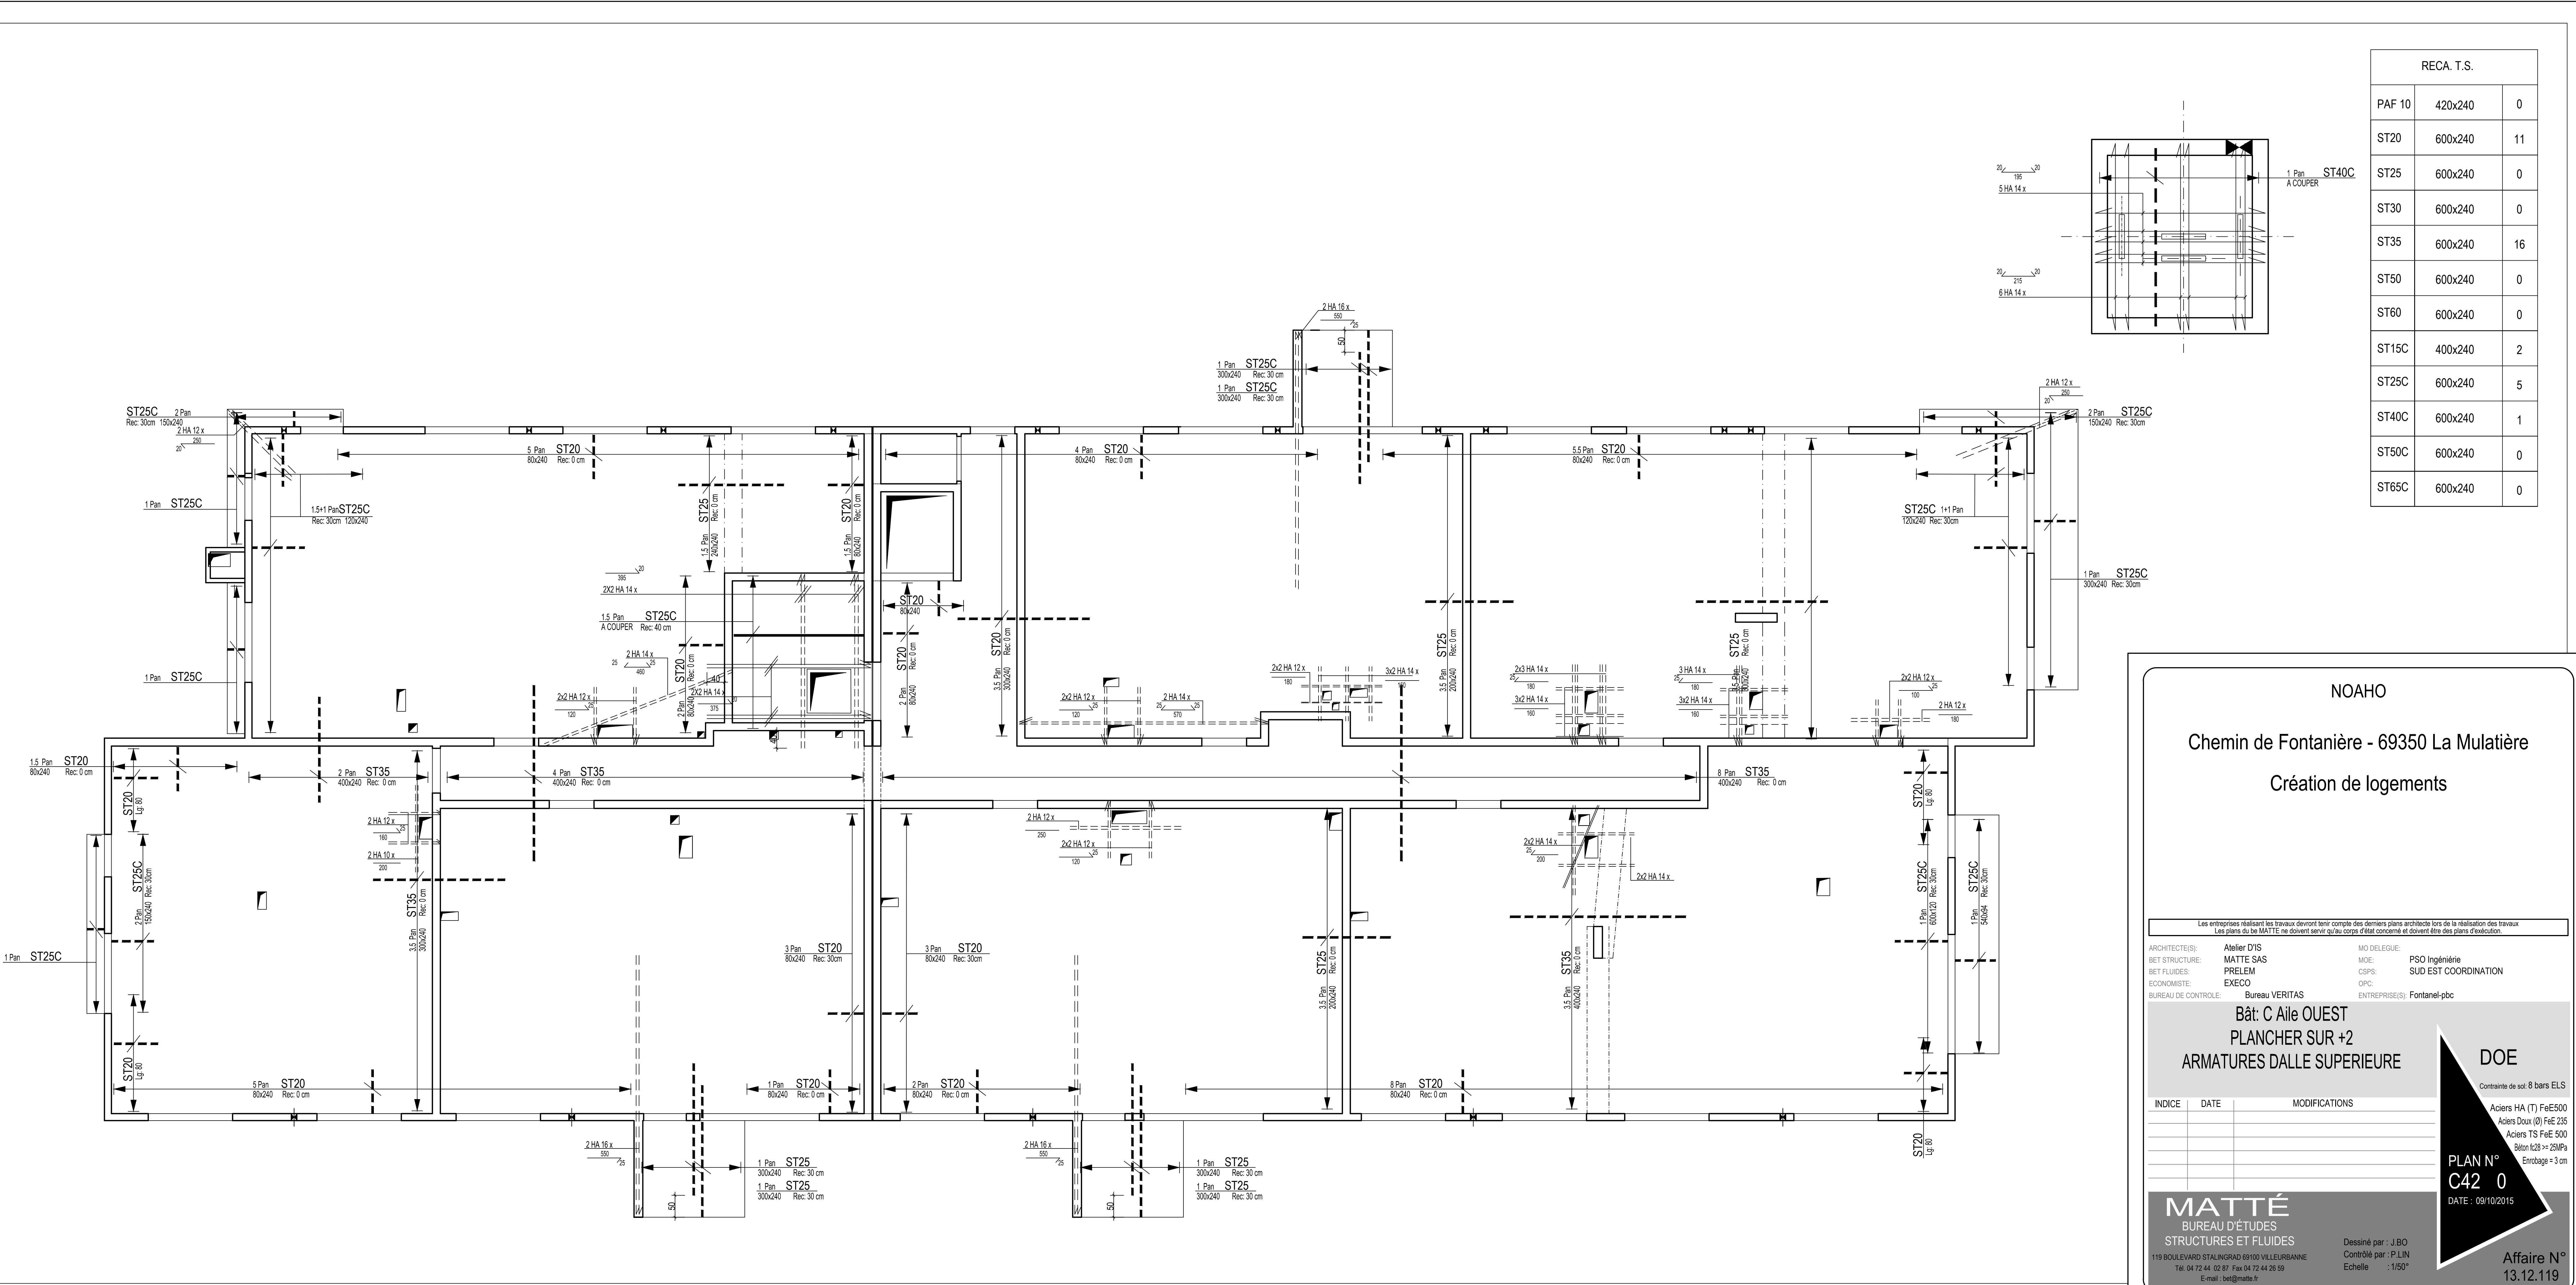

NOAHO

Chemin de Fontanière - 69350 La Mulatière

Création de logements

Les entreprises réalisant les travaux devront tenir compte des derniers plans architecturaux lors de la réalisation des travaux.
Les plans du de MATTÉ ne doivent servir qu'au corps d'état concerné et doivent être des plans d'exécution.

ARCHITECTES: Atelier D'S

BET STRUCTURE: MATTÉ SAS

BET FLUIDES: PRELEM

ECONOMISTE: EXECO

BUREAU DE CONTRÔLE: Bureau VERITAS

MO DELEGUE: PSO Ingénierie

CSPS: SUD EST COORDINATION

OPC: ENTREPRISES: Fontanel-pbc

Bât: C Aile OUEST

PLANCHER SUR +2

ARMATURES DALLE SUPERIEURE

DOE

Contraintes de sol: 8 bars EL5

Aciers HA (T) FeE500

Aciers Doux (D) FeE235

Aciers TS FeE500

Béton f28 >= 20MPa

Enrobage >= 3 cm

INDEXE

DATE

MODIFICATIONS

MATTÉ

BUREAU D'ÉTUDES

STRUCTURES ET FLUIDES

119 BOULEVARD STALINGRAD 69100 VILLEURBANNE

Tel: 04 72 44 12 87 Fax: 04 72 44 26 59

E-mail: bde@matté.fr

Dessiné par: J.B.O.

Contrôle par: P.LIN

Echelle: 1/50'

PLAN N° C42_0

DATE: 09/10/2015

Affaire N° 13.12.119