


|                     |  |   |    |              |                       |  |   |    |              |                   |             |    |              |                     |        |  |
|---------------------|--|---|----|--------------|-----------------------|--|---|----|--------------|-------------------|-------------|----|--------------|---------------------|--------|--|
| MOULE               |  | N | NC | observations | CONTROLE              |  | N | NG | observations | BETON             | N           | NC | observations | FICHE AUTO-CONTROLE |        |  |
| Conformité moule    |  |   |    |              | Dimensions            |  |   |    |              | Conformité béton  |             |    |              | Opérateur :         |        |  |
| Etat du moule       |  |   |    |              | Armature              |  |   |    |              | Mise en place     |             |    |              | Responsable prod :  |        |  |
| Propreté et hullage |  |   |    |              | Inserts               |  |   |    |              | Aspect de surface |             |    |              | Date :              |        |  |
| FONTANEL            |  |   |    |              | Elément: BALCONS      |  |   |    | COUPE TYPE   |                   | Surface: m² |    | POIDS        |                     | REPERE |  |
| LA MULATIERE        |  |   |    |              | coffrage / ferrillage |  |   |    |              |                   | Volume: m3  |    | T            |                     | Nbr    |  |

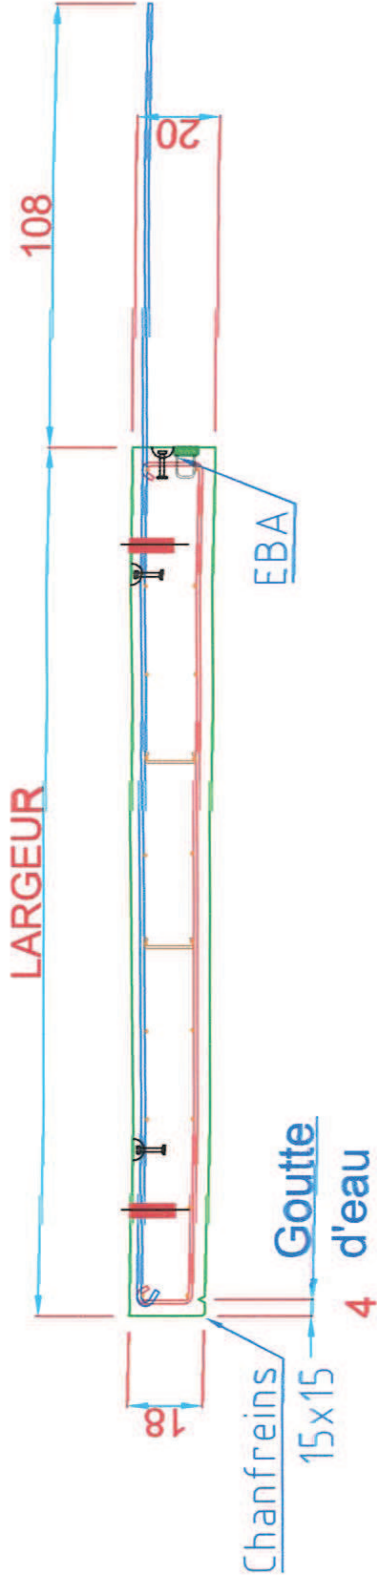

HA12 e = 20

HA8 e = 20

FILANT HA8

| LEVAGE    |    | INSERTS   |    | Ancre Frimeda T |  | INSERTS   |  | EBA               |  | INSERTS           |  | TP - JV          |  | DATE: 05/11/2015 |         |
|-----------|----|-----------|----|-----------------|--|-----------|--|-------------------|--|-------------------|--|------------------|--|------------------|---------|
| Douille Ø |    | Douille Ø |    | Renfort Ø       |  | Renfort Ø |  | Douille étalement |  | Douille étalement |  | PVC Ø80          |  | Plan N°          | Page N° |
| Renfort Ø | dx | Renfort Ø | dx | Trifer          |  | Trifer    |  | Ankrobox Ø50      |  | Ankrobox Ø50      |  | Tube garde-corps |  | Indice           |         |