



GROUPE PLATTARD

CHANTIER

LA MULATIERE LE 180°



ENTREPRISE



BALCONS PRINCIPE ARMATURE

INDICE

A

mis à jour Plan B.E BN

CARNET DE DETAIL PREFA

18

B.N

$\phi 8^r$

3

Enrobage

2

Enrobage

$\phi 14^r$

cadre $\phi 8^r$

le 2 dec ②

4

1

10⁵


2⁵

2


20

Armature entre BN

6 Paine de Roche


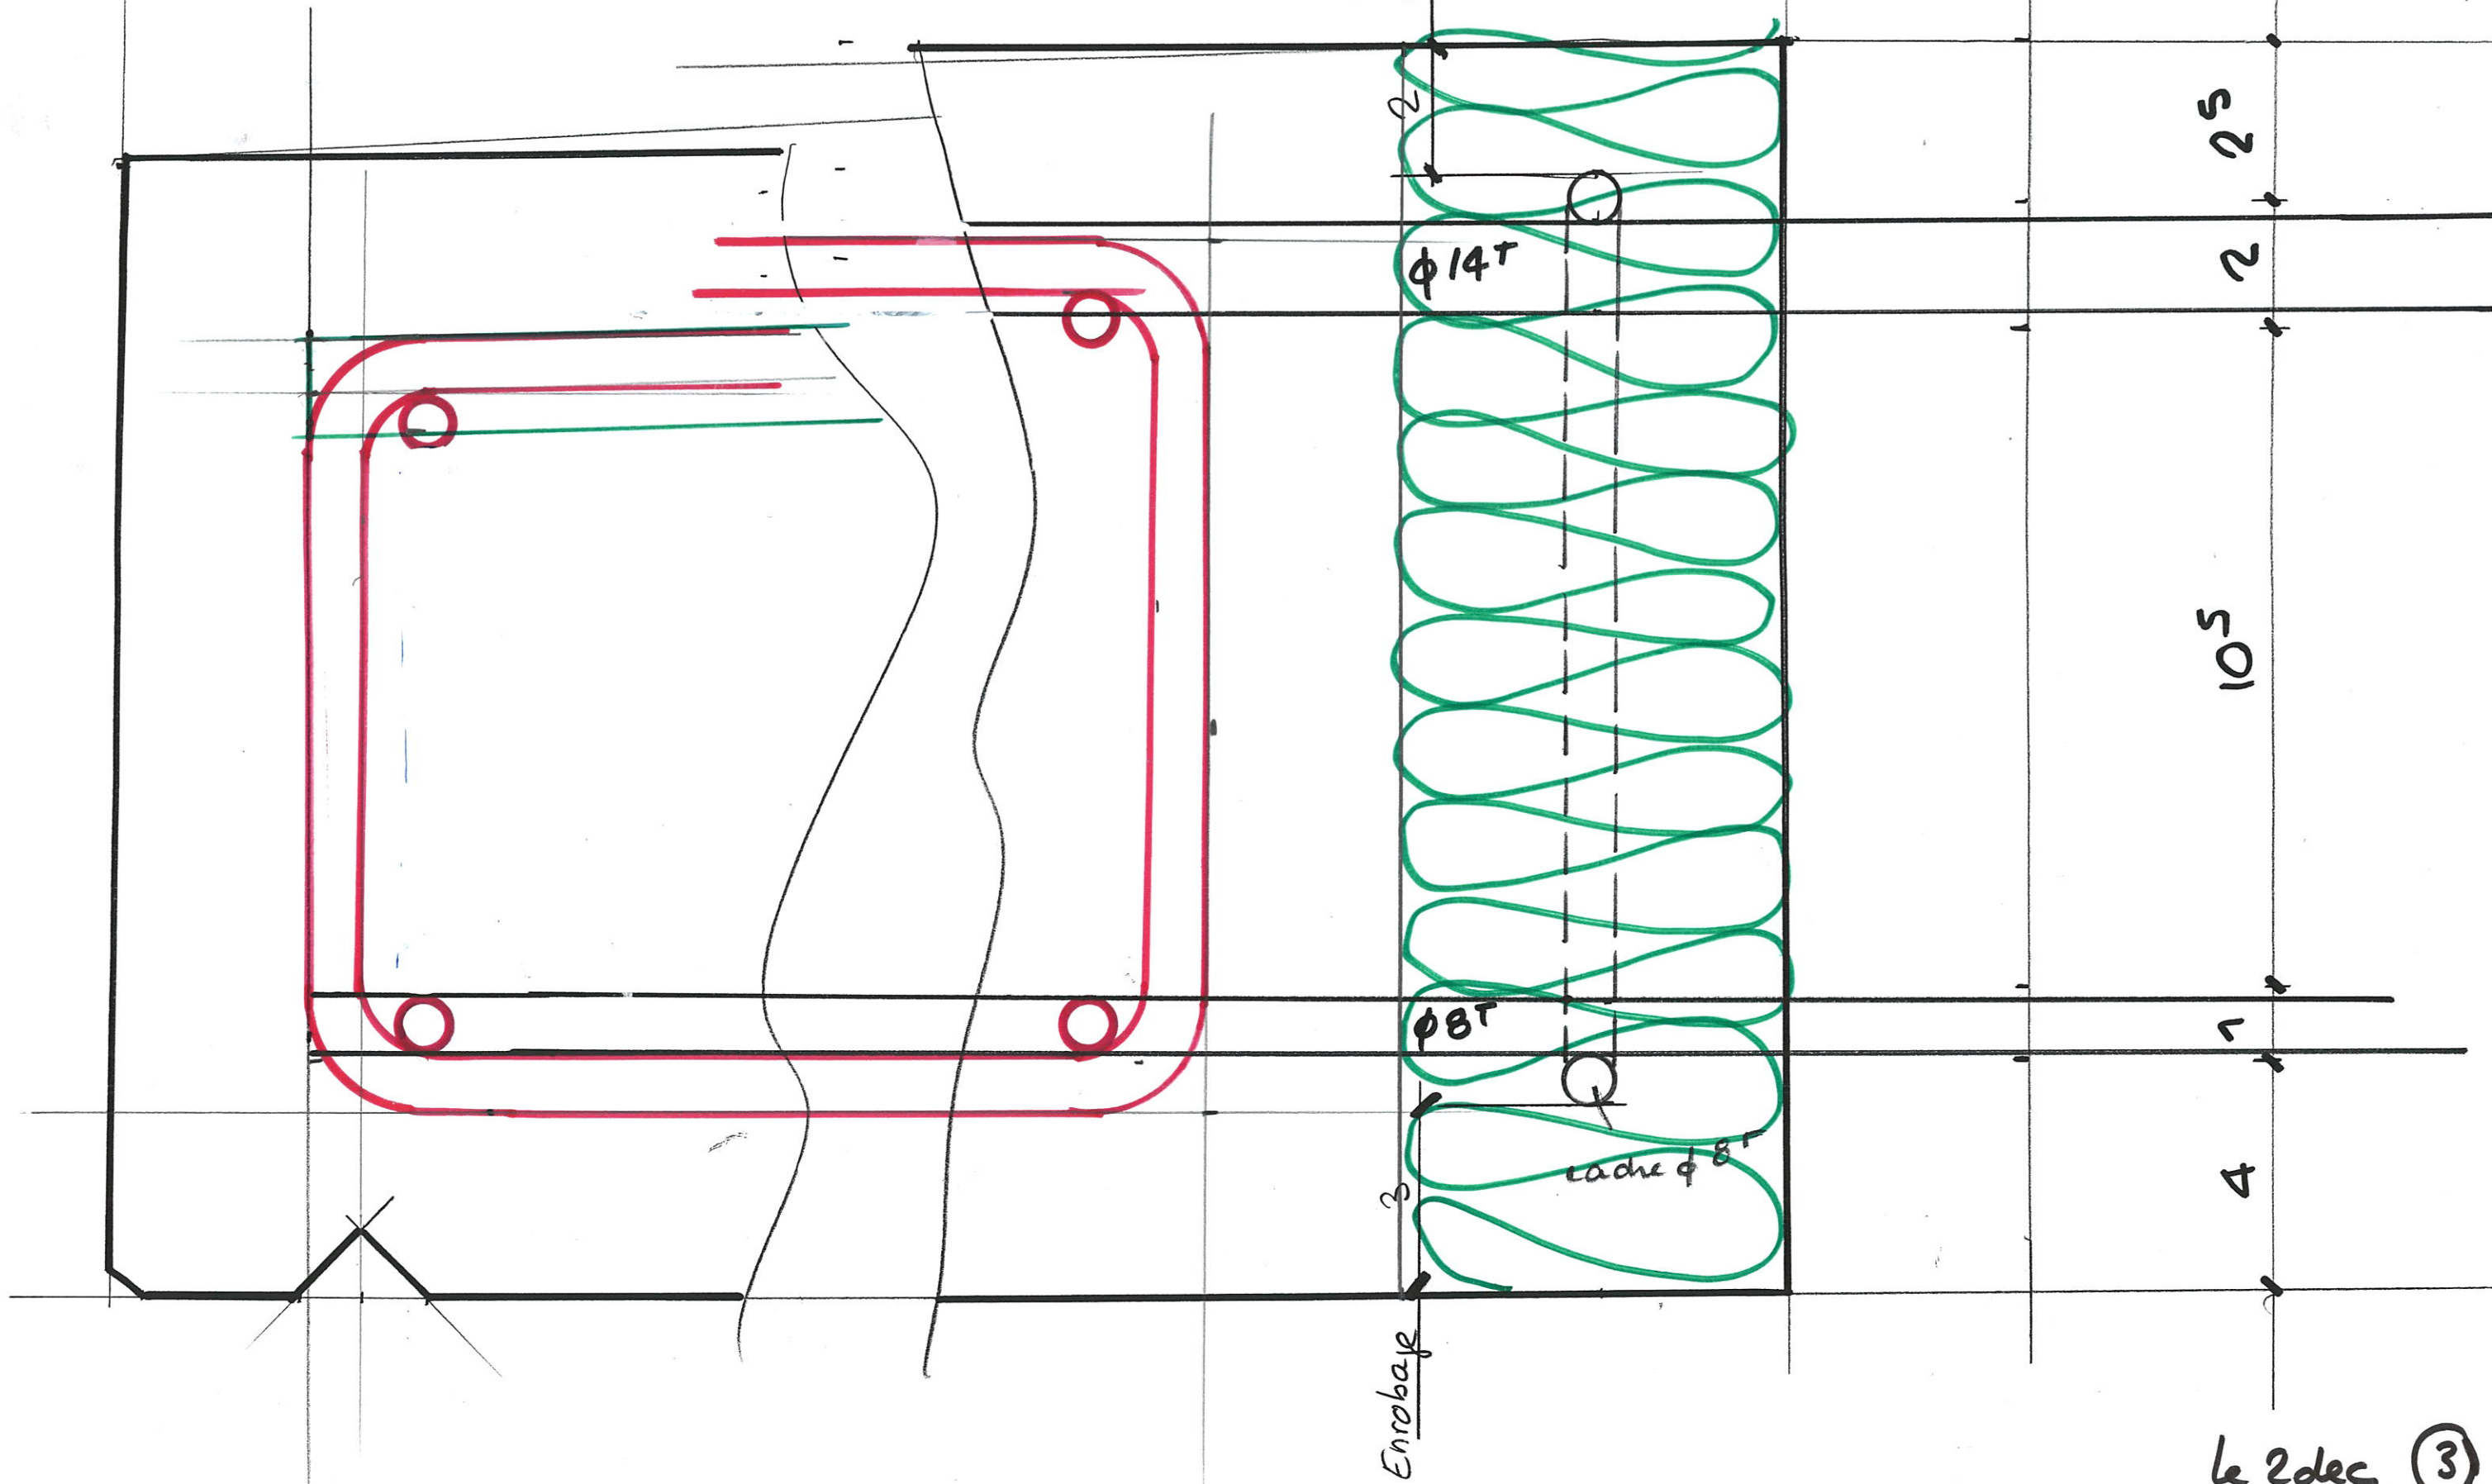


le 2 dec (3)

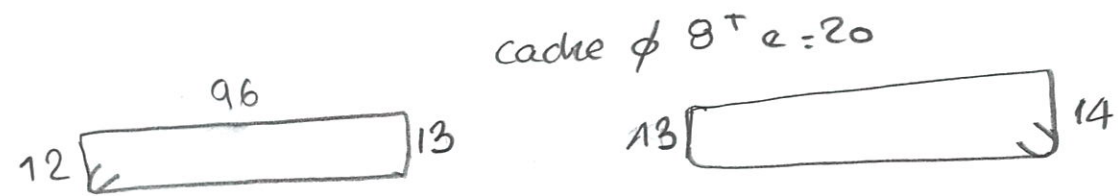

22 fils $\phi 8^T e=20$

Armature entre B.N

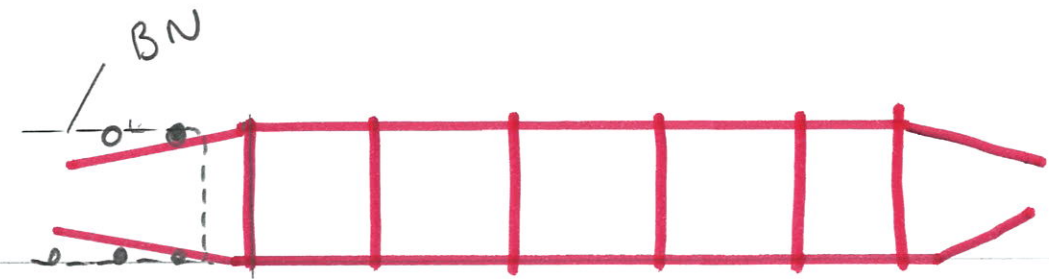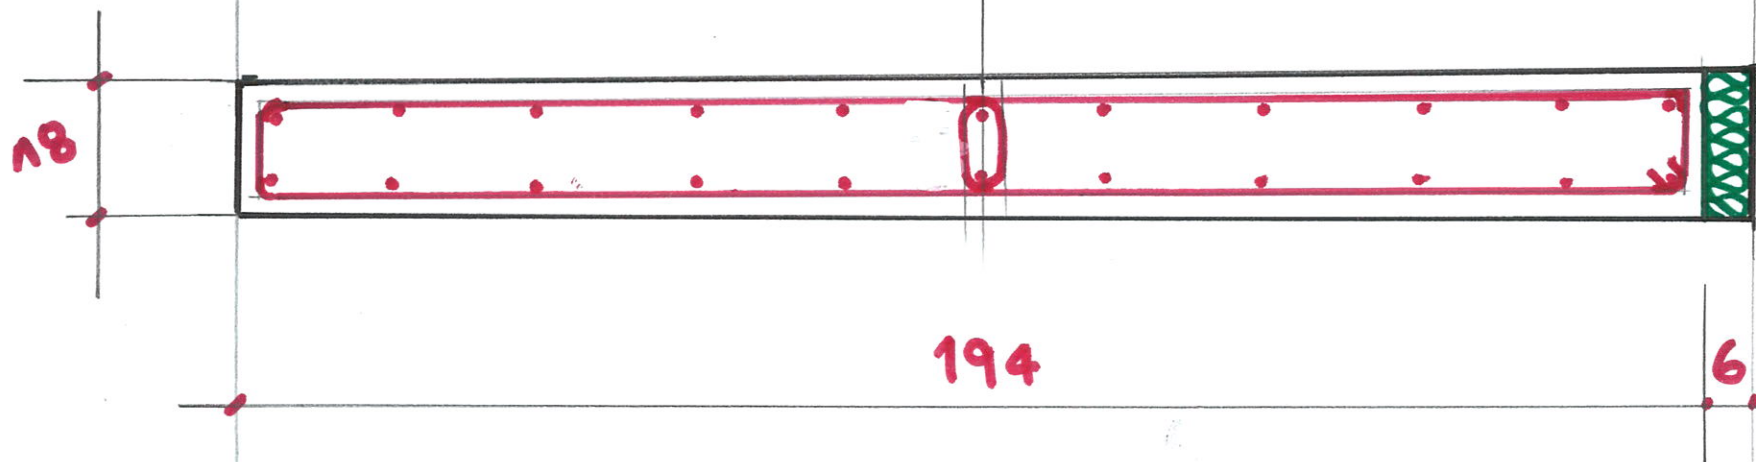

200

BN

Enrobage 2 cm

$\phi 14 \times 3,40$

1.40

Enrobage 3 cm


$\phi 8 \times 2,30$

PLAN BE le 2. dec



FERRAILLAGE BN POUR BALCONS ISOLES

Armature à poser
dans le m^e plan

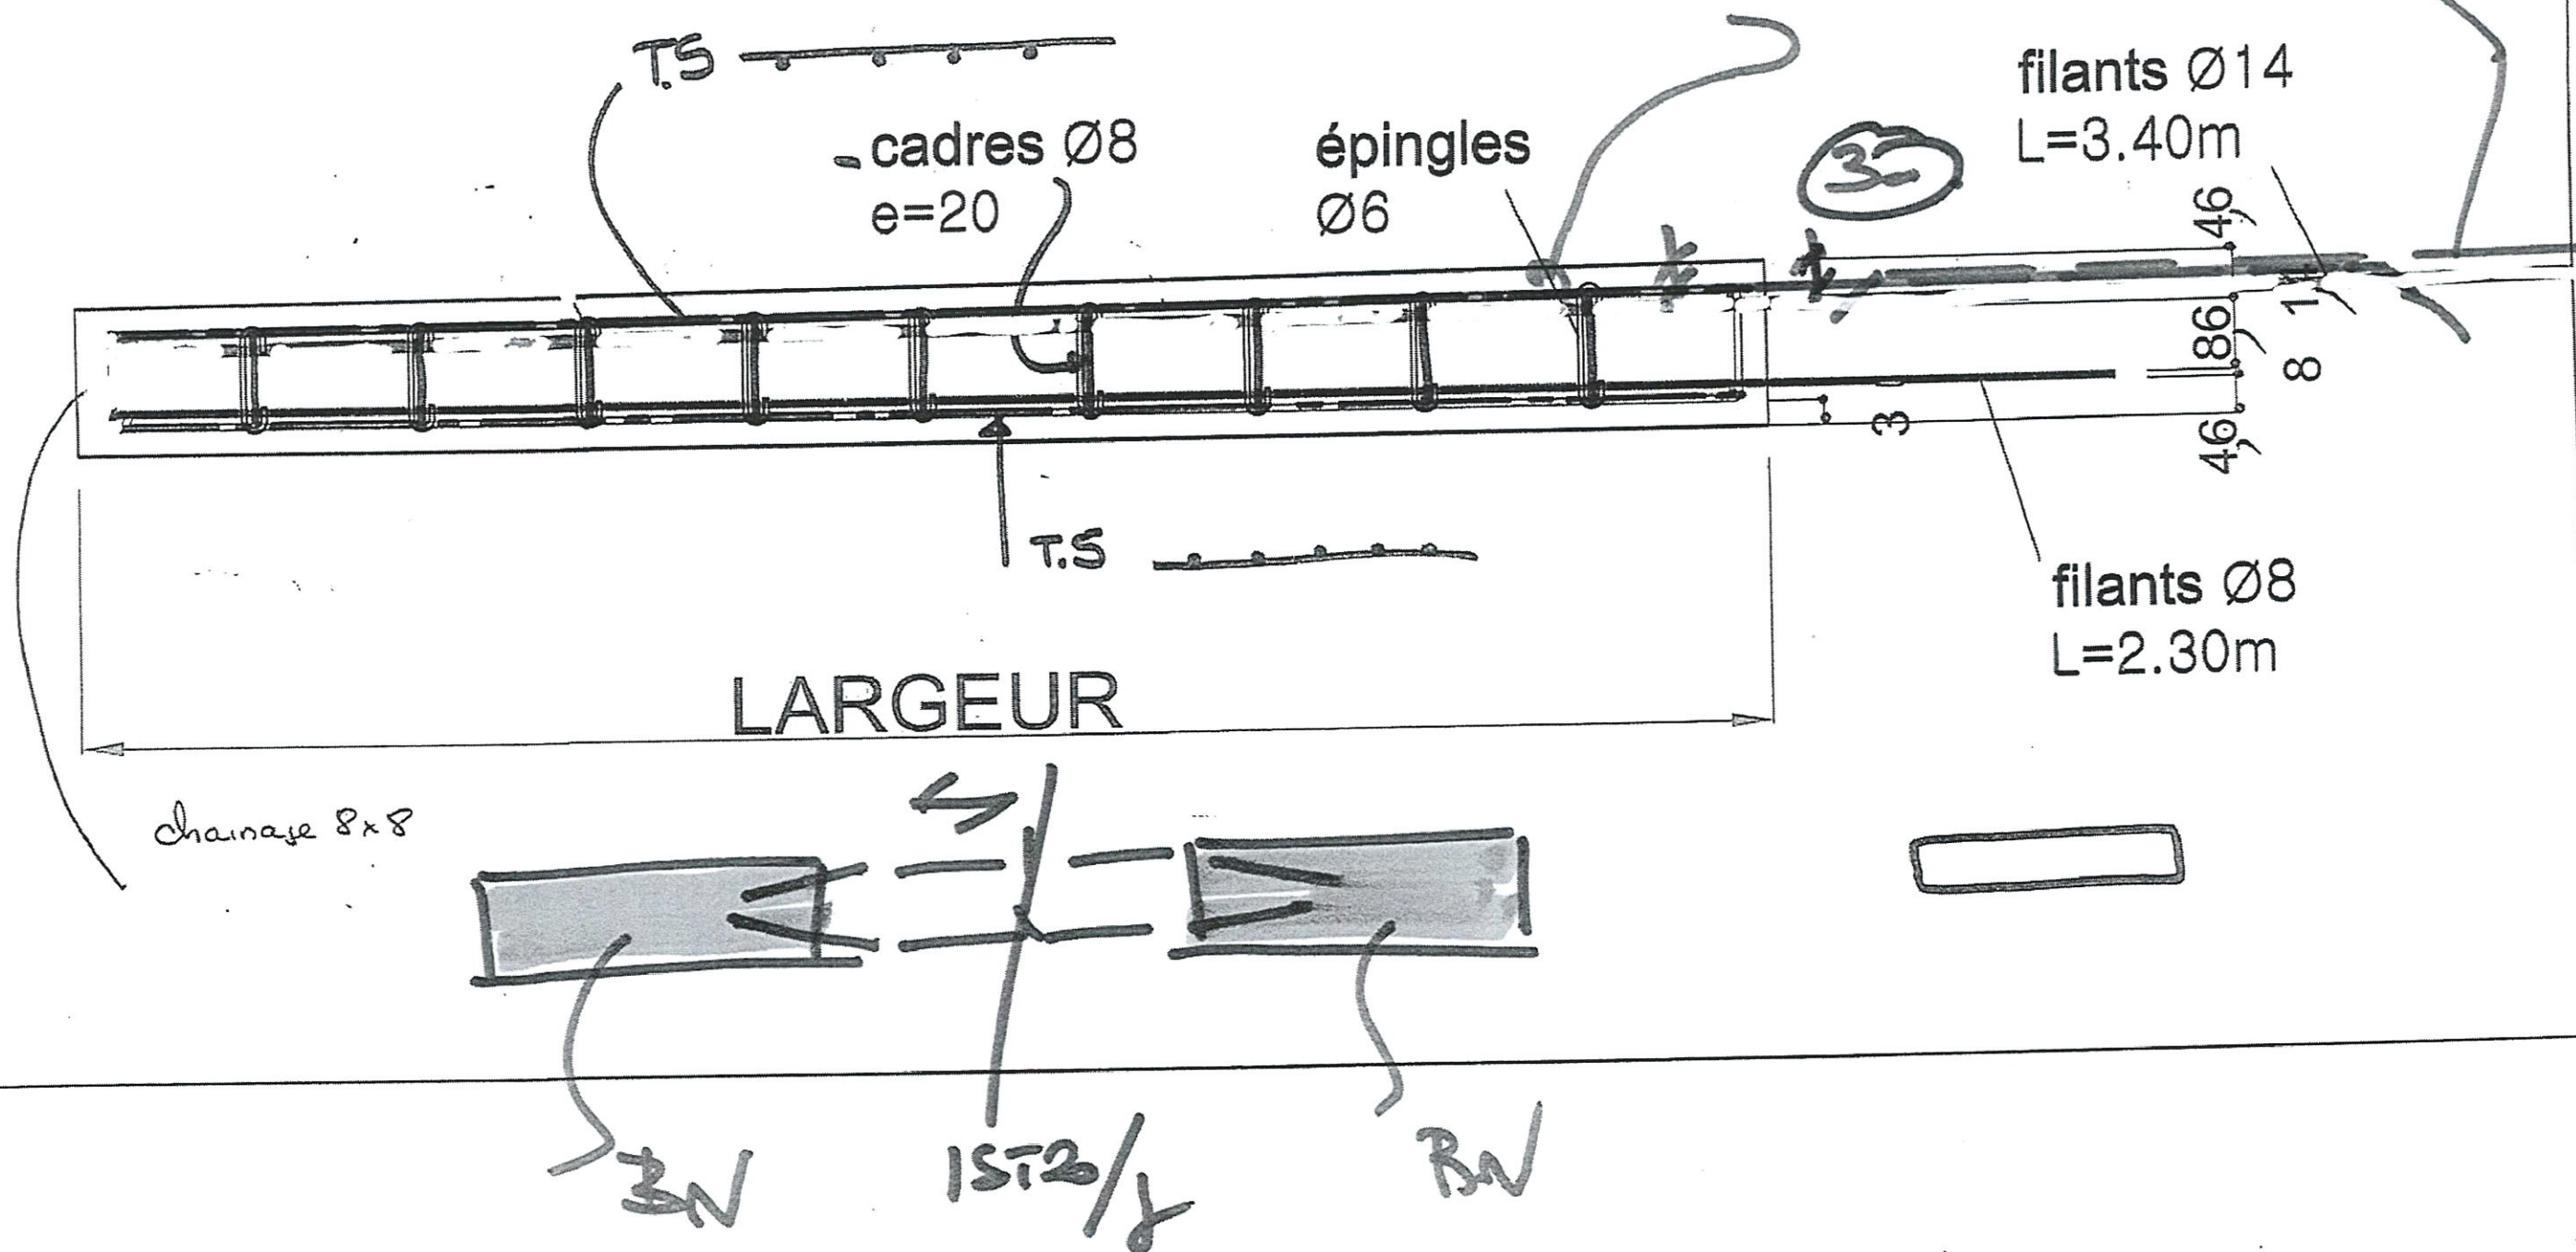

Technical drawing of a lifting beam (Bn 130) showing dimensions and components. The drawing includes a side view on the left and a top view on the right.

Side View Dimensions:

- Overall height: 200
- Top section height: 140
- Top section width: 20
- Bottom section height: 18
- Bottom section width: 4

Top View Dimensions:

- Overall width: 460.5
- Overall height: 200
- Section width: 130
- Section width: 200.5
- Section width: 130
- Section height: 50
- Section height: 100
- Section height: 50
- Section height: 10
- Section width: 10
- Section width: 220
- Section width: 10

Components and Labels:


- ISOLANT A INTEGRER AU COULAGE**: Insulation to be integrated into the casting.
- PVC Ø120**: PVC pipe with diameter 120.
- GOUJON ANTI-PIANOTEMENT**: Anti-rattle pin.
- TUBES DE SECURITE Ø42**: Safety tubes with diameter 42.
- 6 ANCRÉS DE LEVAGE 5T**: 6 lifting anchors with 5T capacity.
- Bn 130**: Lifting beam model.

Handwritten Notes:

- Ecarter les Ø120*: Move the Ø120 pipes.
- 30*: Handwritten dimension.
- 16*: Handwritten dimension.
- 32*: Handwritten dimension.

LEVAGE		Douille Ø	INSERTS		Ancre Frimeda T	INSERTS		EBA	INSERTS		TP - JV	DATE: 16/11/2015									
		Douille Ø			Renfort Ø		 	Douille étalement			PVC Ø80	Plan N°					Page N°				
		Renfort Ø dx			Trifer			Ankrobox Ø50			Tube garde-corps	Indice									



MOULE	N	NC	observations	CONTROLE	N	NC	observations	BETON	N	NC	observations	FICHE AUTO-CONTROLE	
Conformité moule				Dimensions				Conformité béton				Opérateur :	
Etat du moule				Armature				Mise en place				Responsable prod :	
Propreté et huilage				Inserts				Aspect de surface				Date :	
Ent. FONTANEL								Surface: 9.21 m²	POIDS		REPERE		Nbr
		Elément: BALCONS							4.10 T		B5a		1
LA MULATIERE		coffrage / ferrailage						Volume: 1.70 m3					

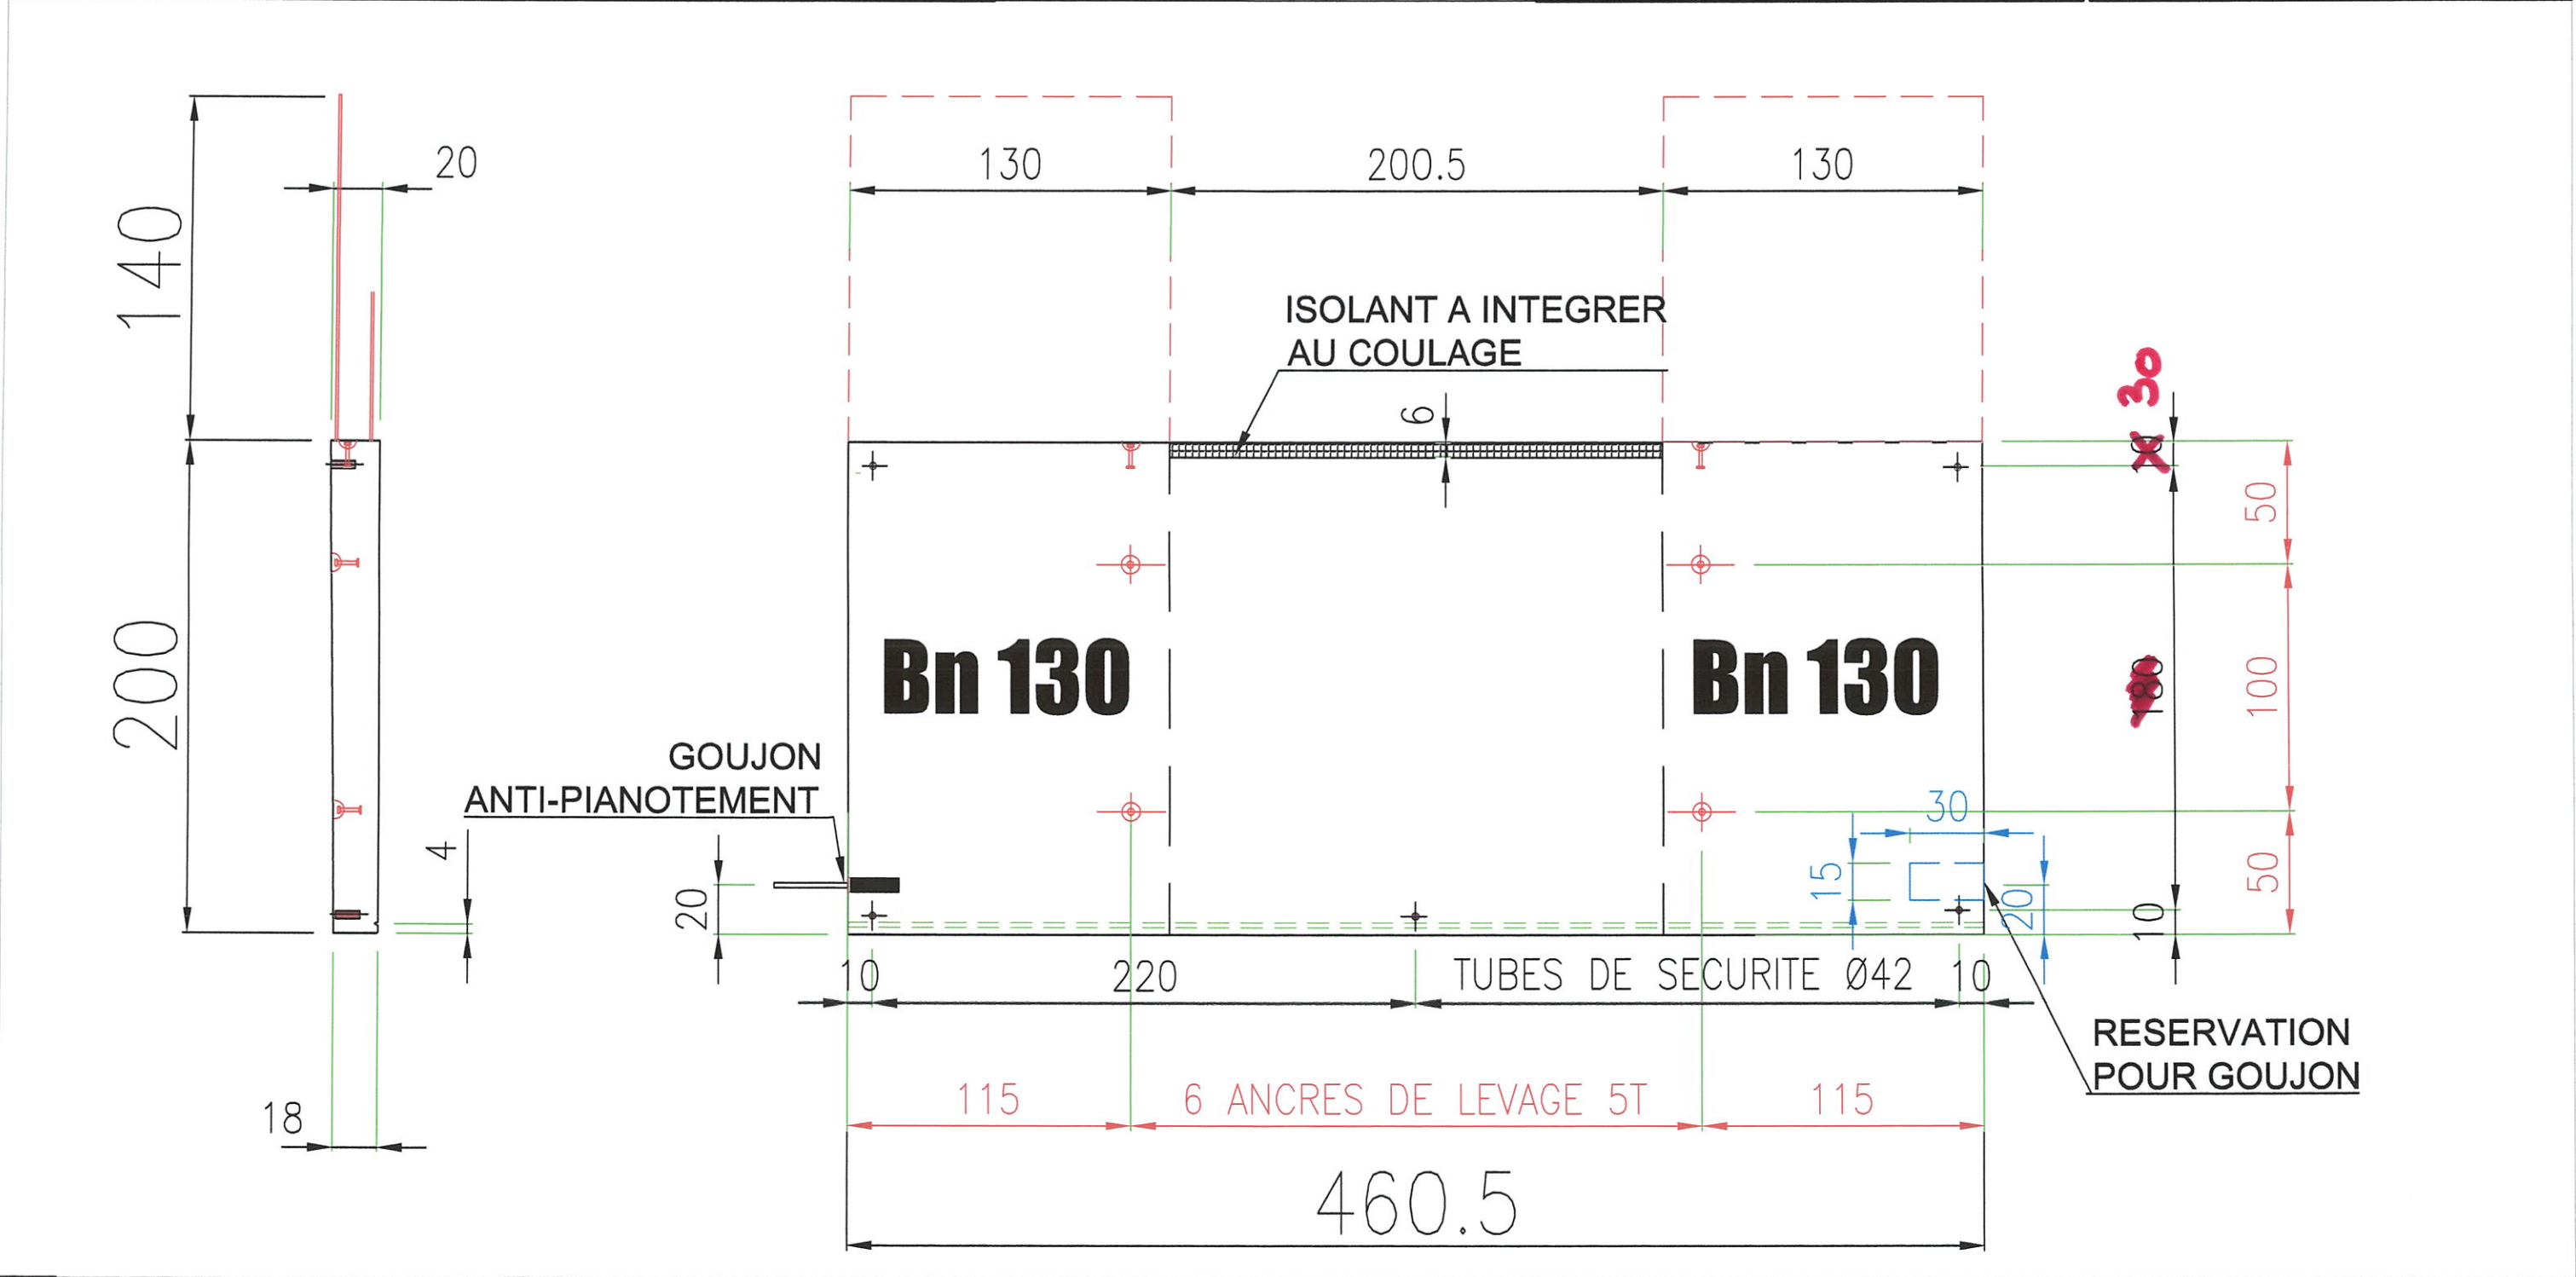

LEVAGE		Douille Ø	INSERTS		Ancre Frimeda T	INSERTS		EBA	INSERTS		TP - JV	DATE: 16/11/2015			
		Douille Ø			Renfort Ø			Douille étaie			PVC Ø80	Plan N°		Page N°	
		Renfort Ø dx			Trifer			Ankrobox Ø50			Tube garde-corps	Indice			


MOULE	N	NC	observations	CONTROLE	N	NC	observations	BETON	N	NC	observations	FICHE AUTO-CONTROLE	
Conformité moule				Dimensions				Conformité béton				Opérateur :	
Etat du moule				Armature				Mise en place				Responsable prod :	
Propreté et huilage				Inserts				Aspect de surface				Date :	

Ent. FONTANEL	Elément: BALCONS	PLATTARD S.A.S.	PLAN DE FABRICATION	Surface: 9.21 m²	POIDS 4.10 T	REPERE B5b	Nbr 1
				Volume: 1.70 m3			

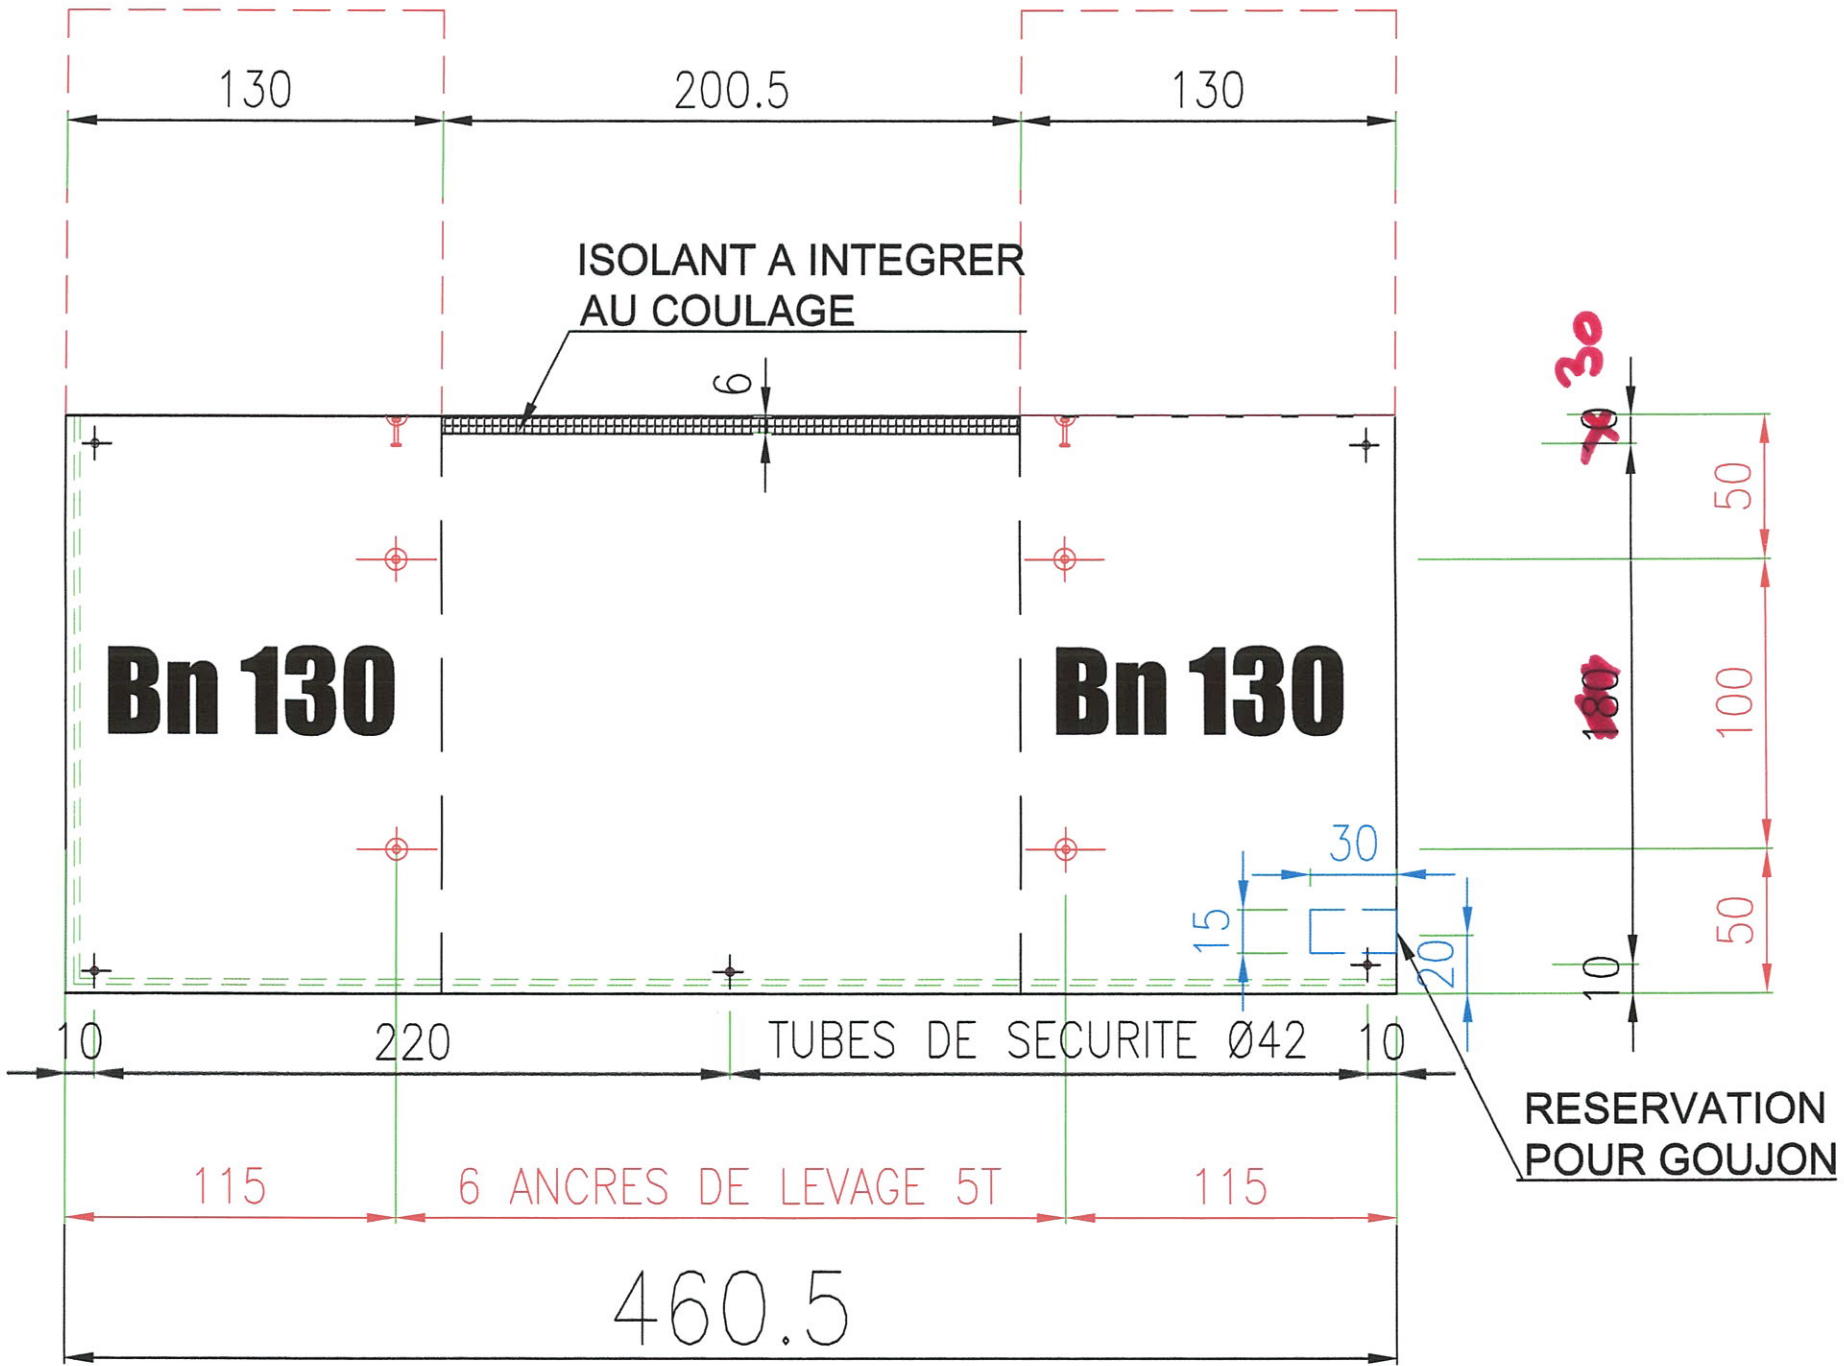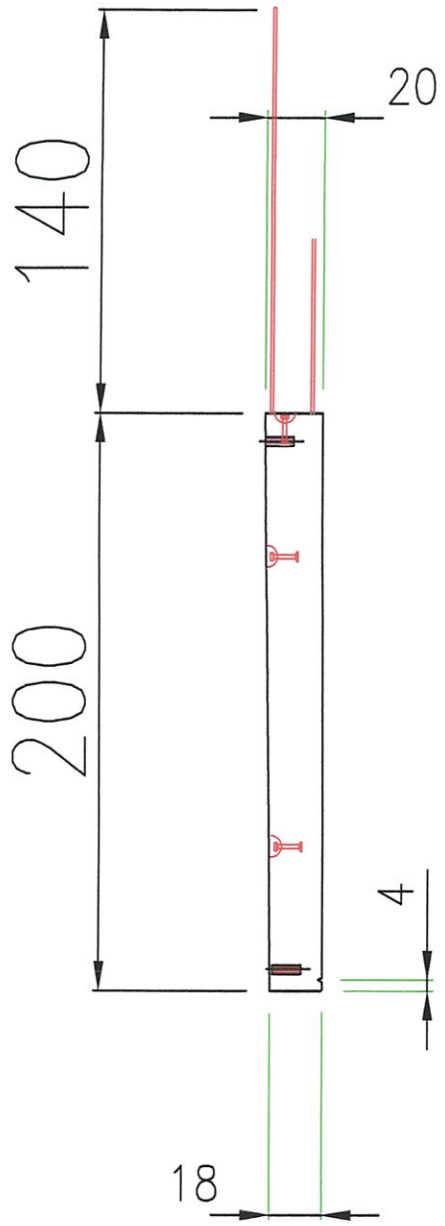


LEVAGE		Douille Ø	INSERTS		Ancre Frimeda T	INSERTS		EBA	INSERTS		TP - JV	DATE: 16/11/2015				
		Douille Ø			Renfort Ø			Douille étaieement			PVC Ø80	Plan N°	Page N°			
		Renfort Ø dx			Trifer			Ankrobox Ø50			Tube garde-corps	Indice				


FERRAILLAGE BN POUR BALCONS ISOLES

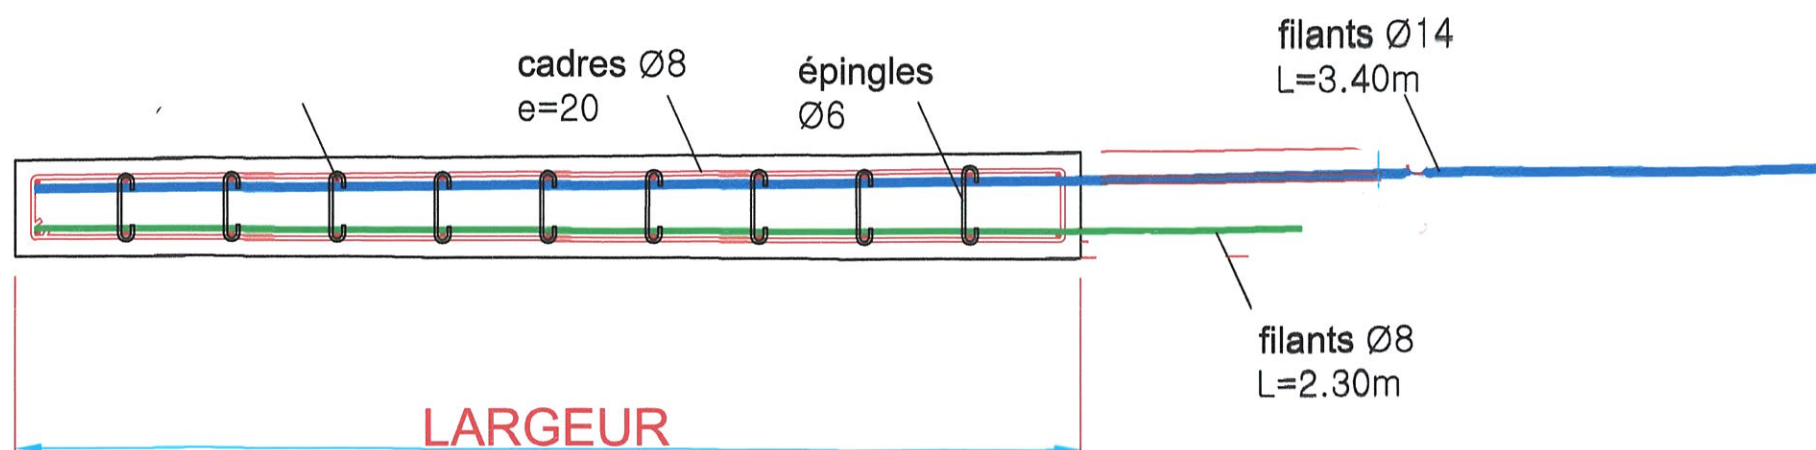



BALCON PORTEUR AVEC BN Larg.1.00 m

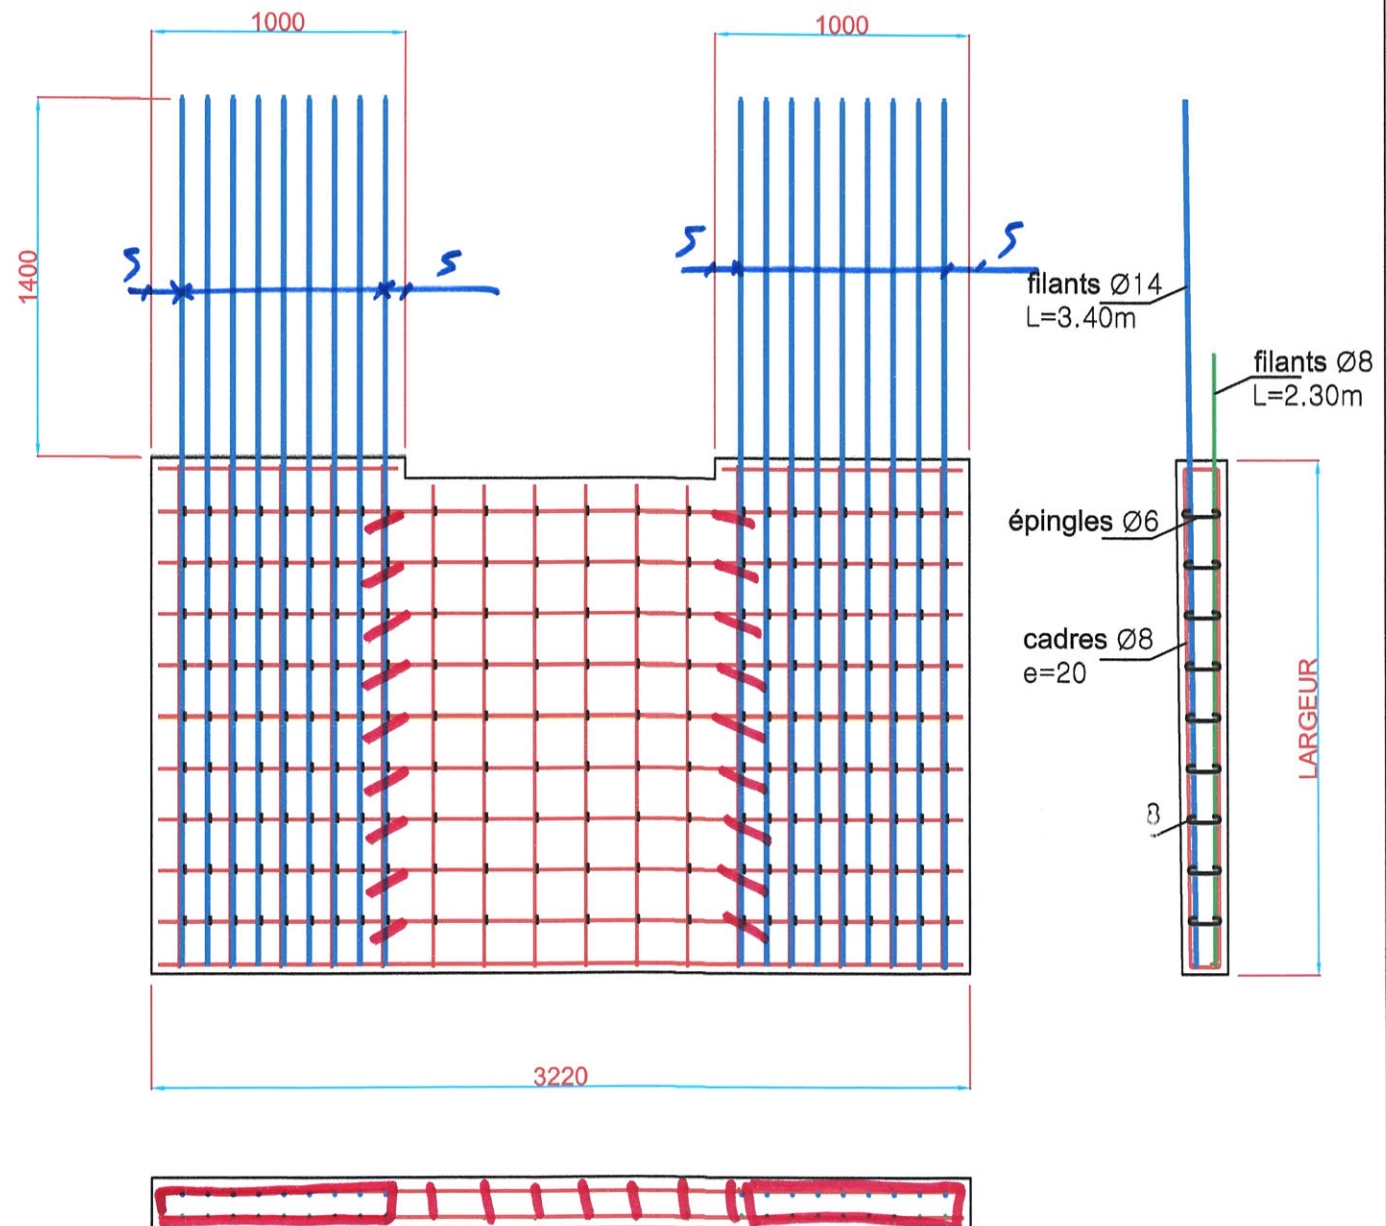



BALCON PORTEUR AVEC BN Larg.1.30 m

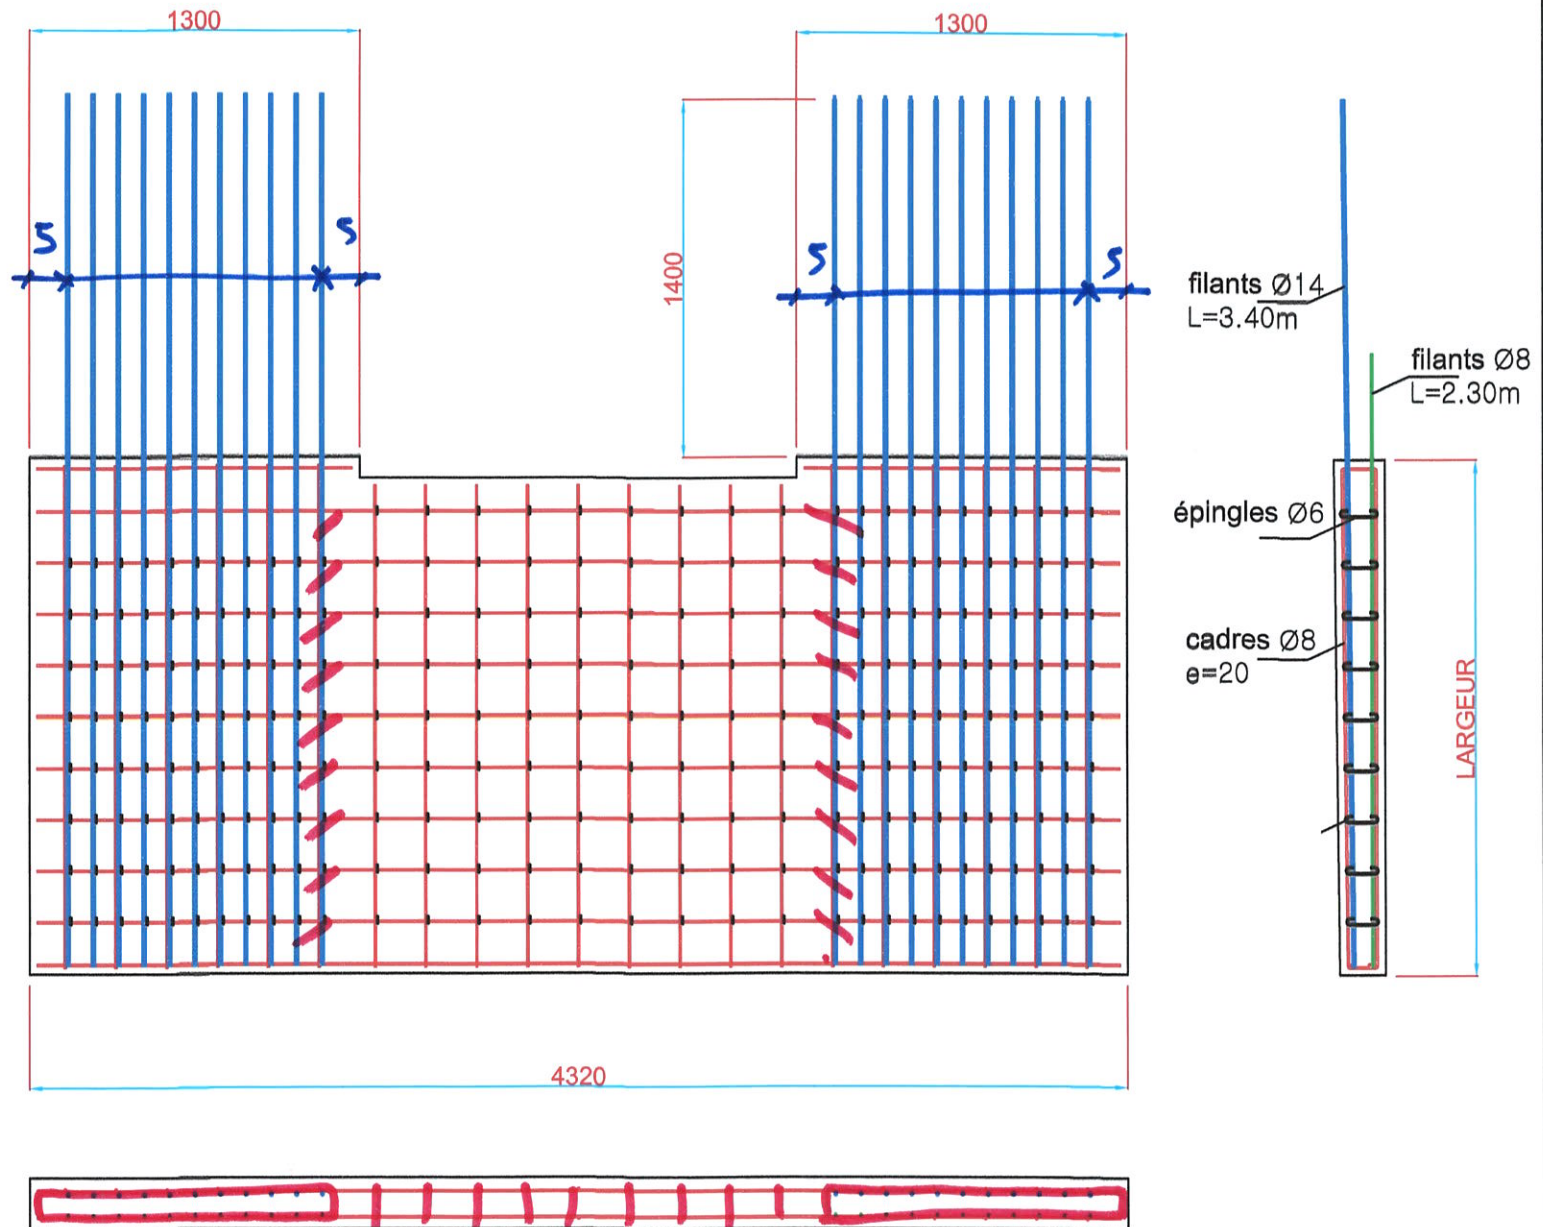

BALCON PORTEUR AVEC BN Larg.1.50 m

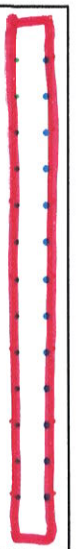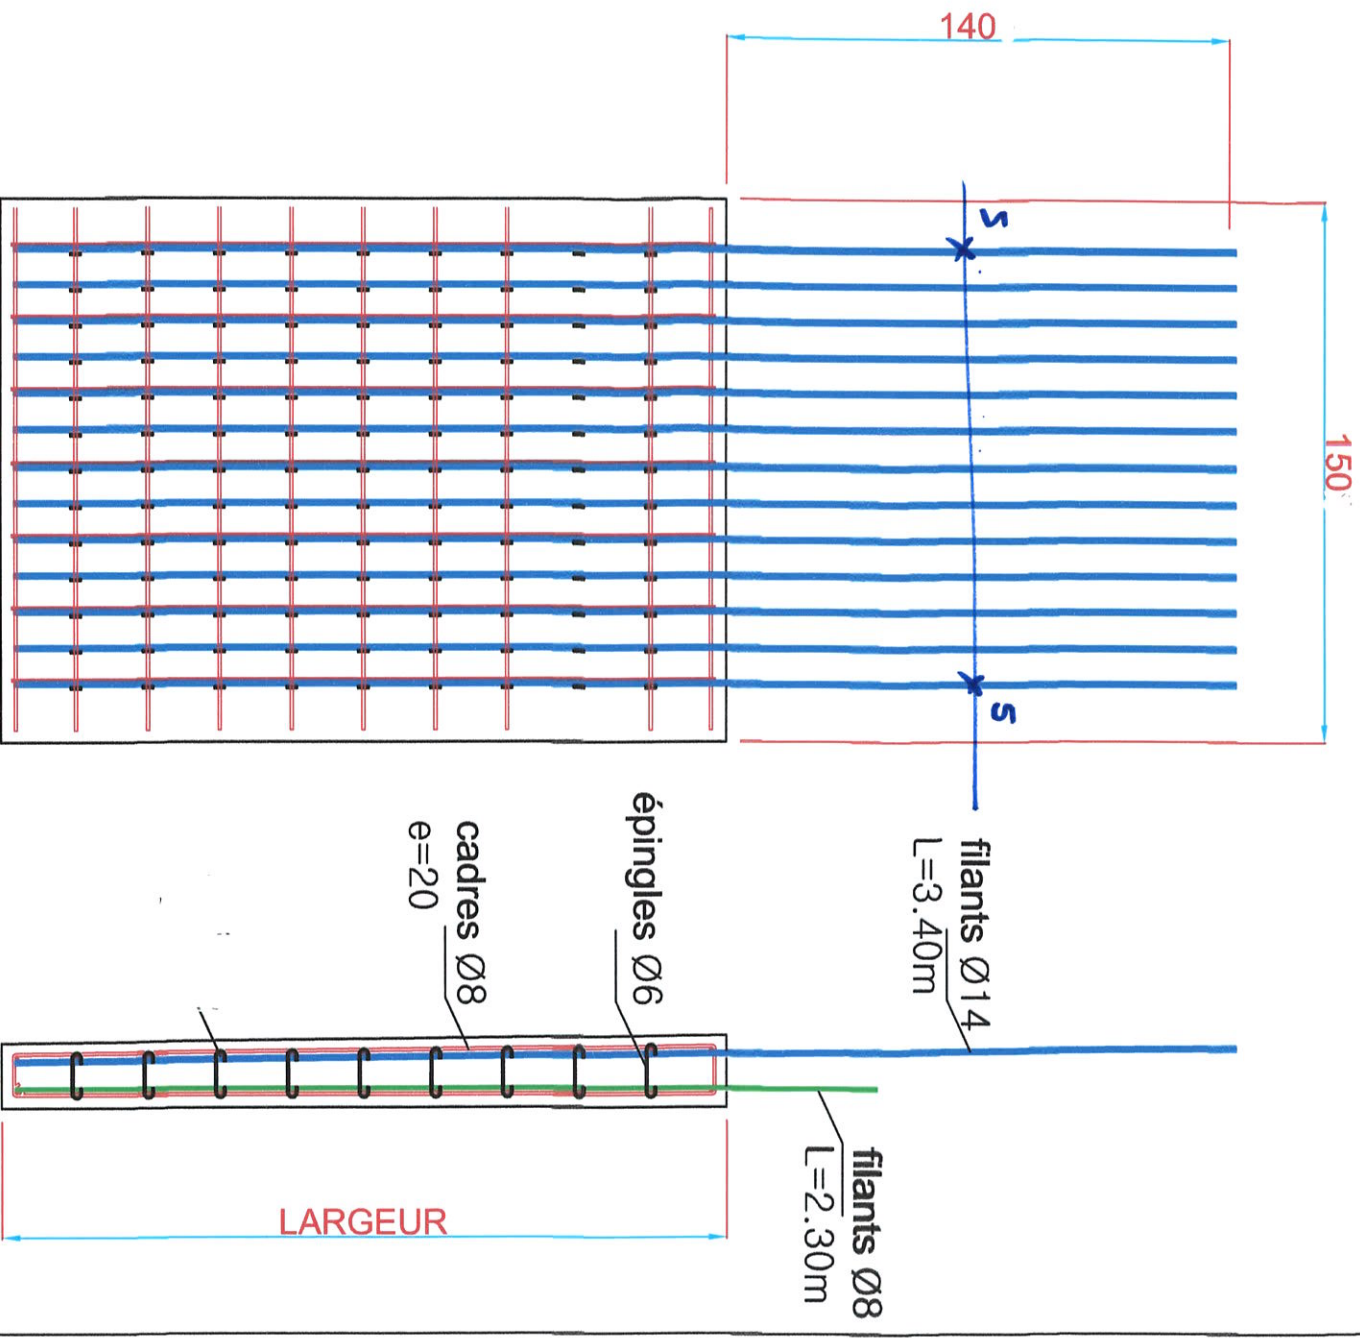

BALCON PORTEUR AVEC BN Larg. 2.00 m

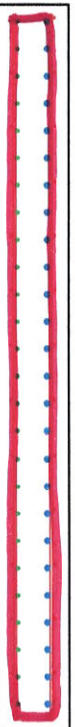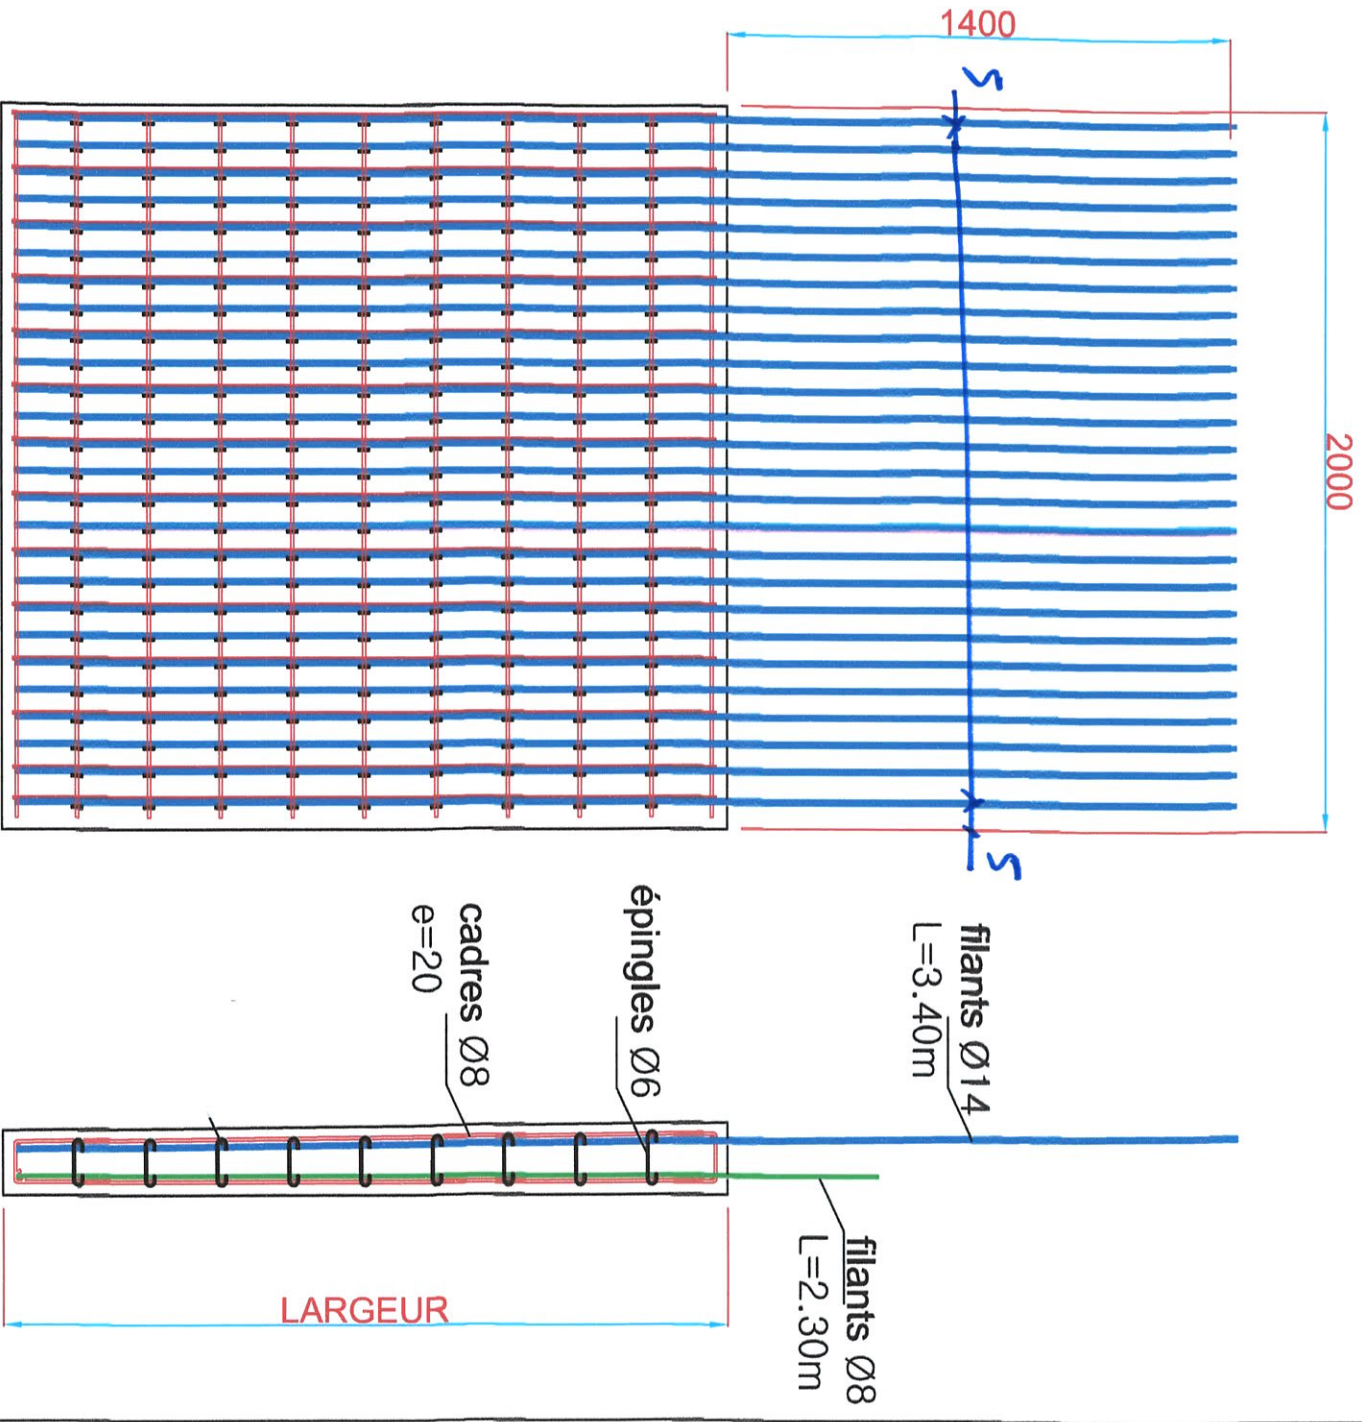

LEVAGE		Douille Ø	INSERTS		Ancre Frimeda T	INSERTS		EBA	INSERTS		TP - JV	DATE: 05/11/2015									
		Douille Ø			Renfort Ø			Douille étaie			PVC Ø80	Plan N°					Page N°				
		Renfort Ø dx			Trifer			Ankrobox Ø50			Tube garde-corps	Indice									