



GROUPE PLATTARD

CHANTIER

LA MULATIERE LE 180°



ENTREPRISE




**BALCONS_NIV -5_BAT A
ETUDE REPERAGE**

INDICE

CARNET DE DETAIL PREFA

MOULE	N	NC	observations	CONTROLE	N	NC	observations	BETON	N	NC	observations	FICHE AUTO-CONTROLE			
Conformité moule				Dimensions				Conformité béton				Opérateur :			
Etat du moule				Armature				Mise en place				Responsable prod :			
Propreté et huilage				Inserts				Aspect de surface				Date :			
FONTANEL				Elément: BALCONS		COUPE TYPE		Surface: m²		POIDS		REPERE		Nbr	
LA MULATIERE				coffrage / ferrillage				Volume: m3		T					
						PLATINAD S.A.S.									

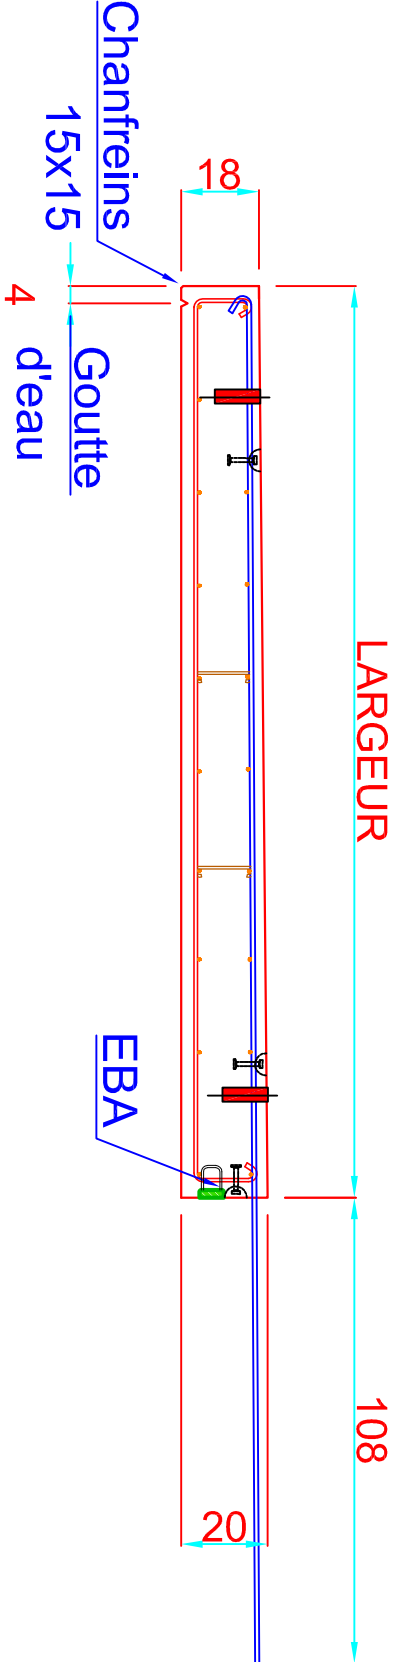


HA12 e = 20

HA8 e = 20


FILANT HA8

LEVAGE		INSERTS		INSERTS		INSERTS	
	Douille Ø		Ancre Frimeda T		EBA		TP - JV
	Douille Ø		Renfort Ø		Douille étaiement		PVC Ø80
	Renfort Ø dx		Trifer		Ankrobox Ø50		Tube garde-corps
DATE: 05/11/2015				Page N°			

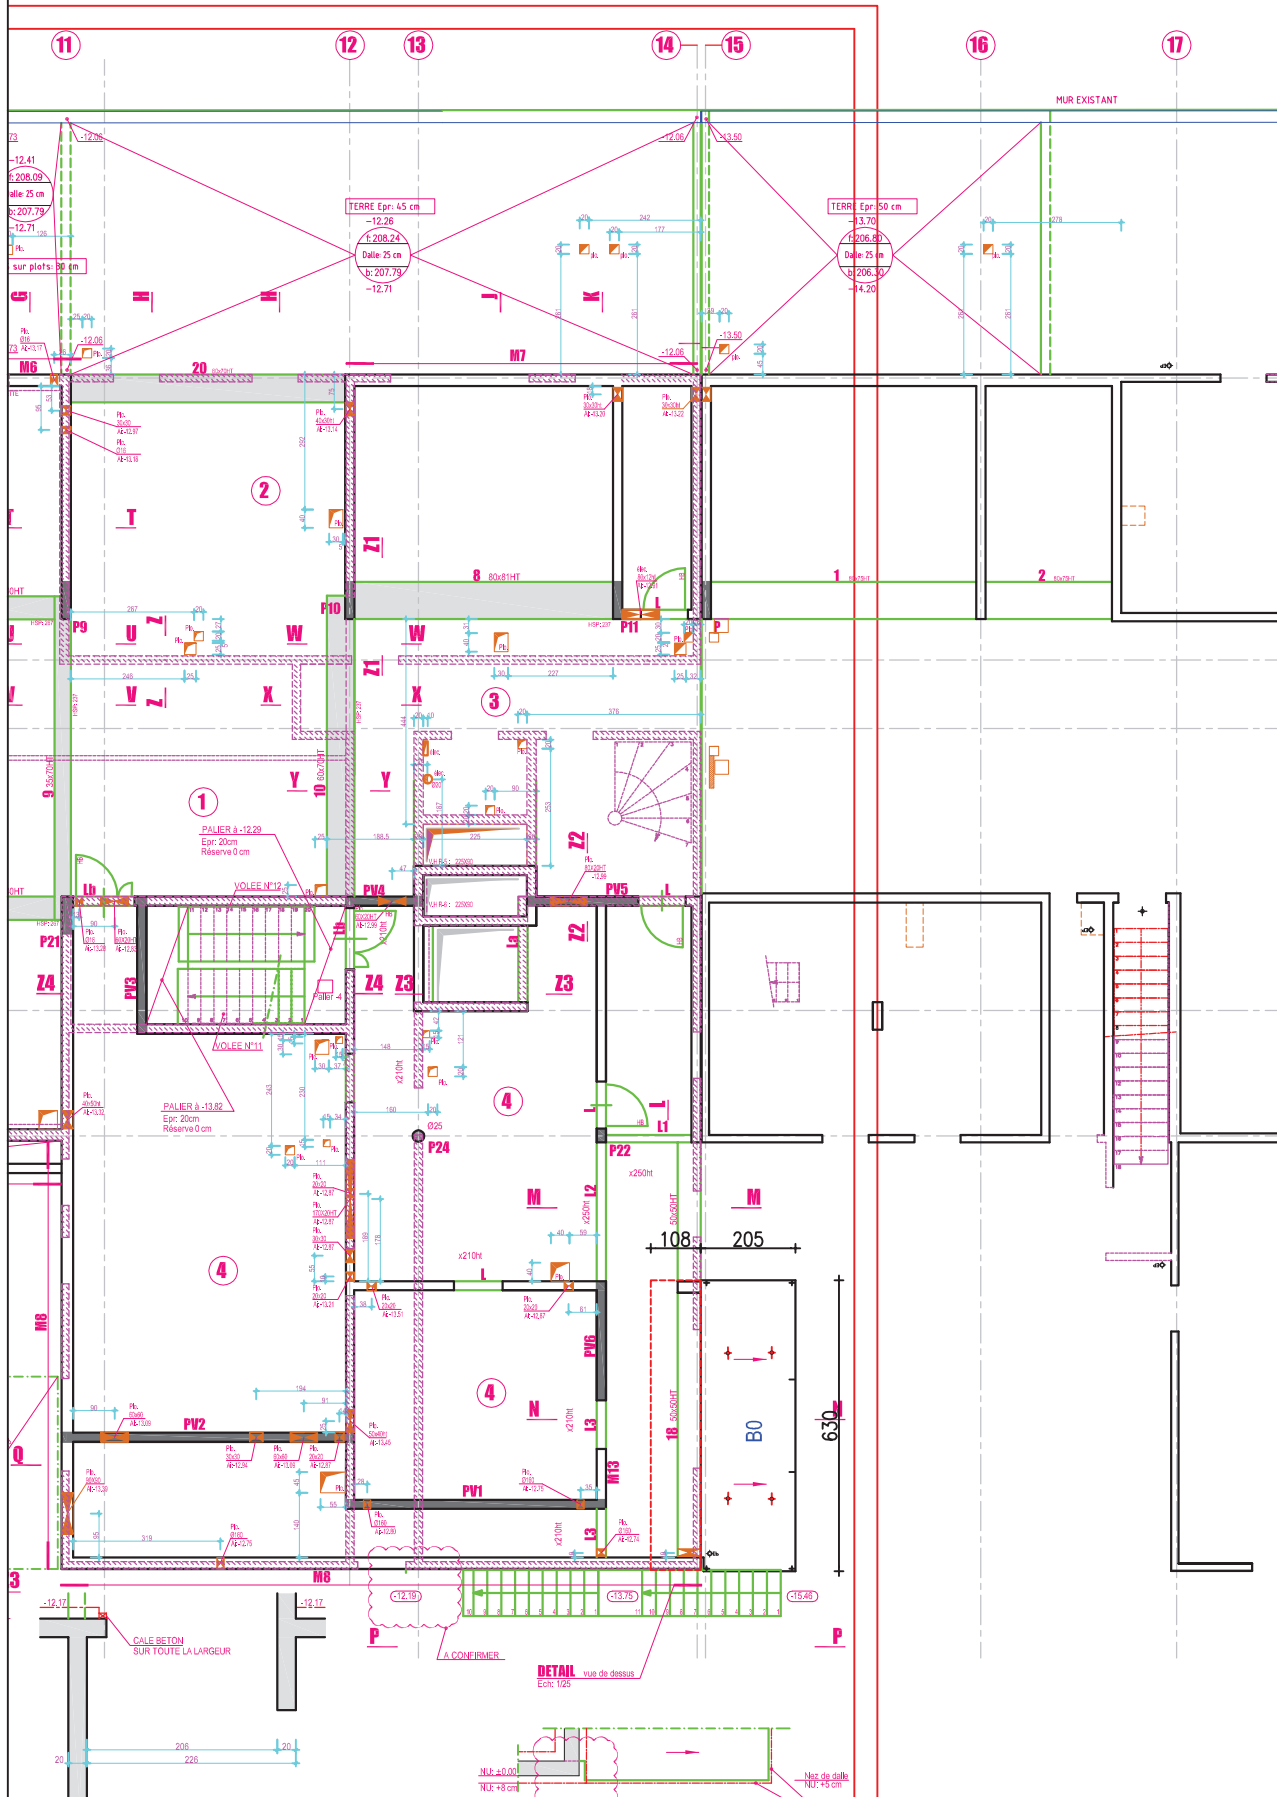

MOULE	N	NC	observations	CONTRÔLE	N	NC	observations	BETON	N	NC	observations	FICHE AUTO-CONTROLE
Conformité moule				Dimensions				Conformité béton				Opérateur :
Etat du moule				Armature				Mise en place				Responsable prod :
Propreté et huilage				Inserts				Aspect de surface				Date :

Ent. FONTANEL		Elément: BALCONS				PLAN DE FABRCATION		Surface: 12.92 m²		POIDS		REPERE		Nbr	
LA MULATIERE		coffrage / ferrillage				Volume: 2.45 m3		5.89 T		B0		1			

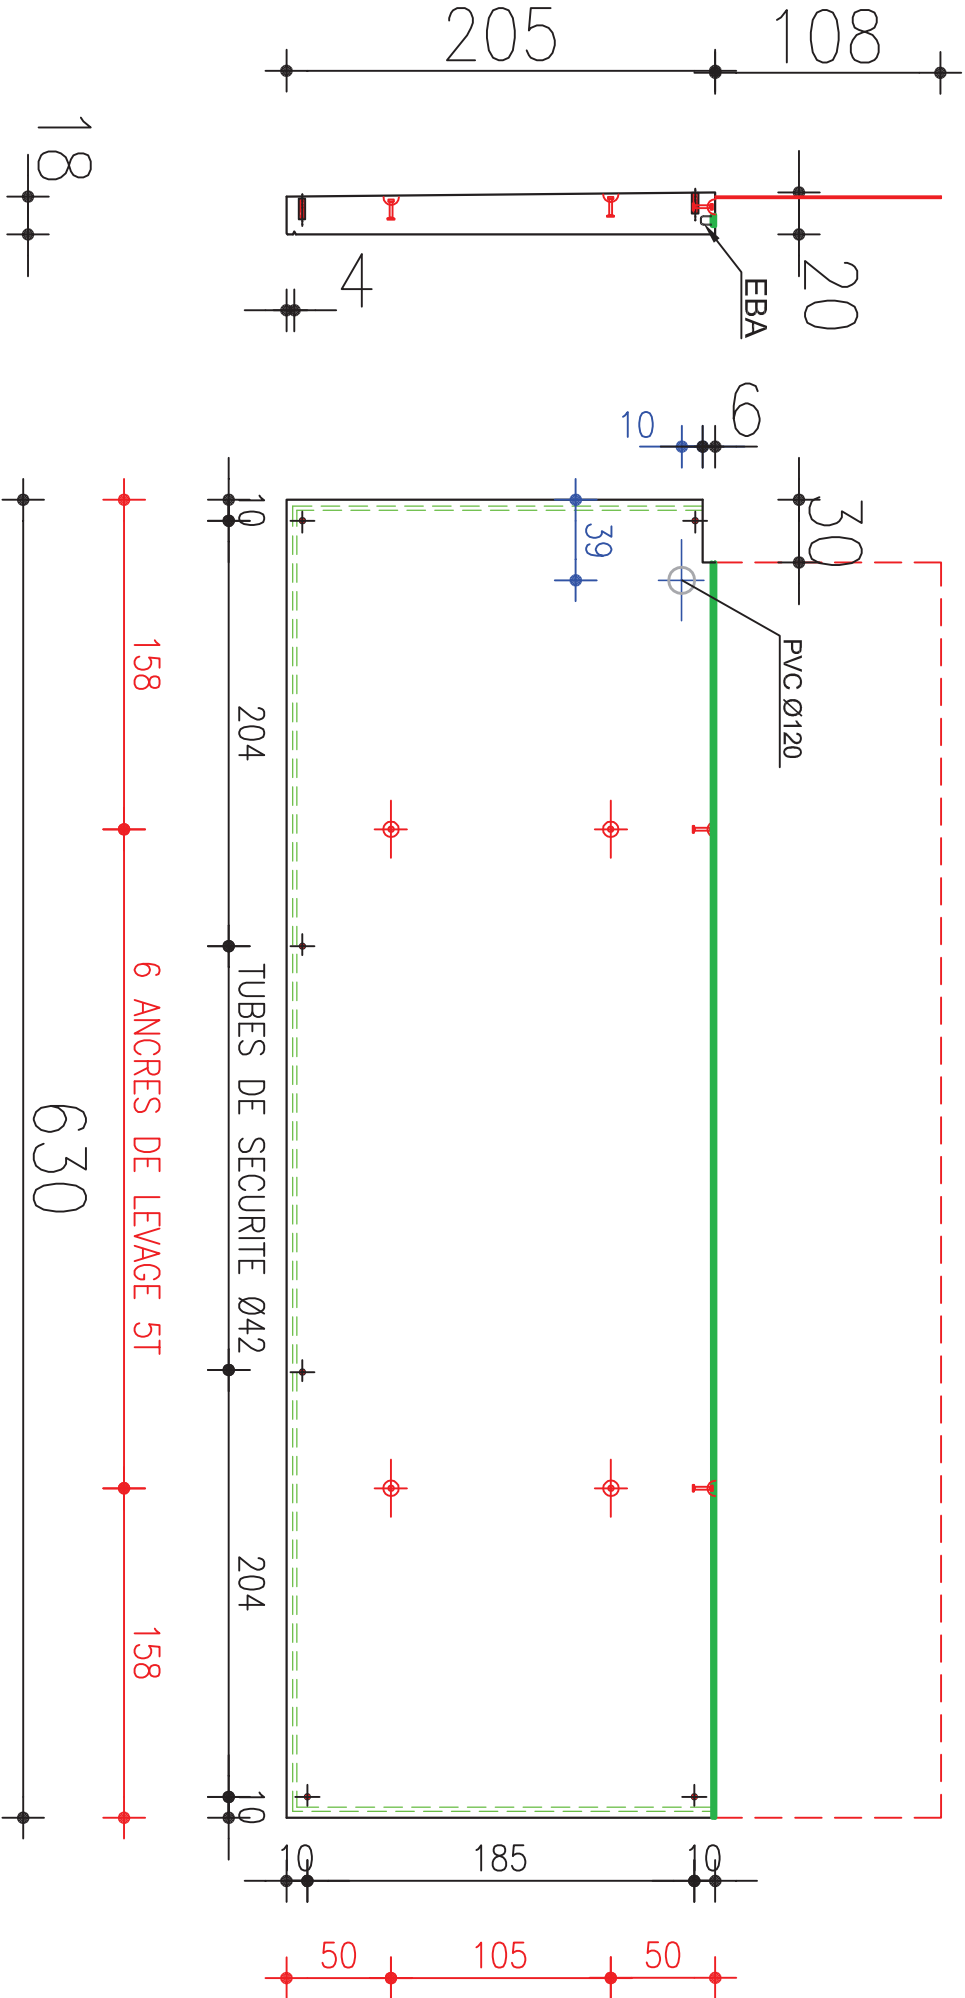

LEVAGE			INSERTS			INSERTS			INSERTS			DATE: 18/11/2015		
	Douille Ø	Renfort Ø dx		Ancre Frimeda T	Renfort Ø		EBA	Douille étalement	Ankrobox Ø50		TP - JV	Plan N°		
												Page N°		