

FONTANEL- LE 180°

69 LA MULATIERE


BALCONS DU NIVEAU N-1
BAT A

N°

EXE

Indice	Date	Designation des Modifications	Date :
A			22/05/15
B			Affaire :
C			
D			Echelle :
E			
F			
G			
H			
I			

Type béton = B35 XF1
Aciers H.A et T.S = Fe E 500
Enrobage des armatures = ENR_{CA}ARMAT
Manutention = Tonnes

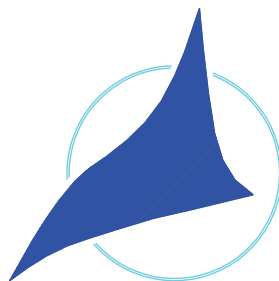

P L A T T A R D



BUREAU D'ETUDE
PLATTARD SAS
414 Avenue de la
plage
BP 119
69540
Villefrance-sur-Saône
Tél: 04 74 02 20 20
Fax: 04 74 62 26 62

Ce plan est la propriété intellectuelle de la PLATTARD SAS, il ne peut être reproduit sans son autorisation.

NOAHO

LE 180°

Chemin de Fontanière - 69350 La Mulatière

Création de logements

Les entreprises réalisant les travaux devront tenir compte des derniers plans architecte lors de la réalisation des travaux
Les plans du be MATTE ne doivent servir qu'au corps d'état concerné et doivent être des plans d'exécution.

ARCHITECTE(S): ATELIER DE LA PASSERELLE MO DELEGUE:
BET STRUCTURE: MATTE SAS MOE: PSO Ingénierie
BET FLUIDES: PRELEM CSPS: SUD EST COORDINATION
ECONOMISTE: EXECO OPC:
BUREAU DE CONTROLE: Bureau VERITAS ENTREPRISE(S): Fontanel

Bât:A
PLANCHER SUR -1
Coffrage

EXE

Contrainte de sol: 8 bars ELS

Aciers HA (T) FeE500
Aciers Doux (Ø) FeE 235
Aciers TS FeE 500
Béton fc28 >= 25MPa
Enrobage = 3 cm

PLAN N°
A35 0

DATE : 26/01/2016

MATTÉ
BUREAU D'ÉTUDES
STRUCTURES ET FLUIDES


119 BOULEVARD STALINGRAD 69100 VILLEURBANNE
Tél. 04 72 44 02 87 Fax 04 72 44 26 59
E-mail : bet@matte.fr


Dessiné par : J.BO
Contrôlé par : P.LIN
Echelle : 1/50°

Affaire N°
13.12.118

Ent. FONTANEL LA MULATIERE


FERRAILLAGE B10

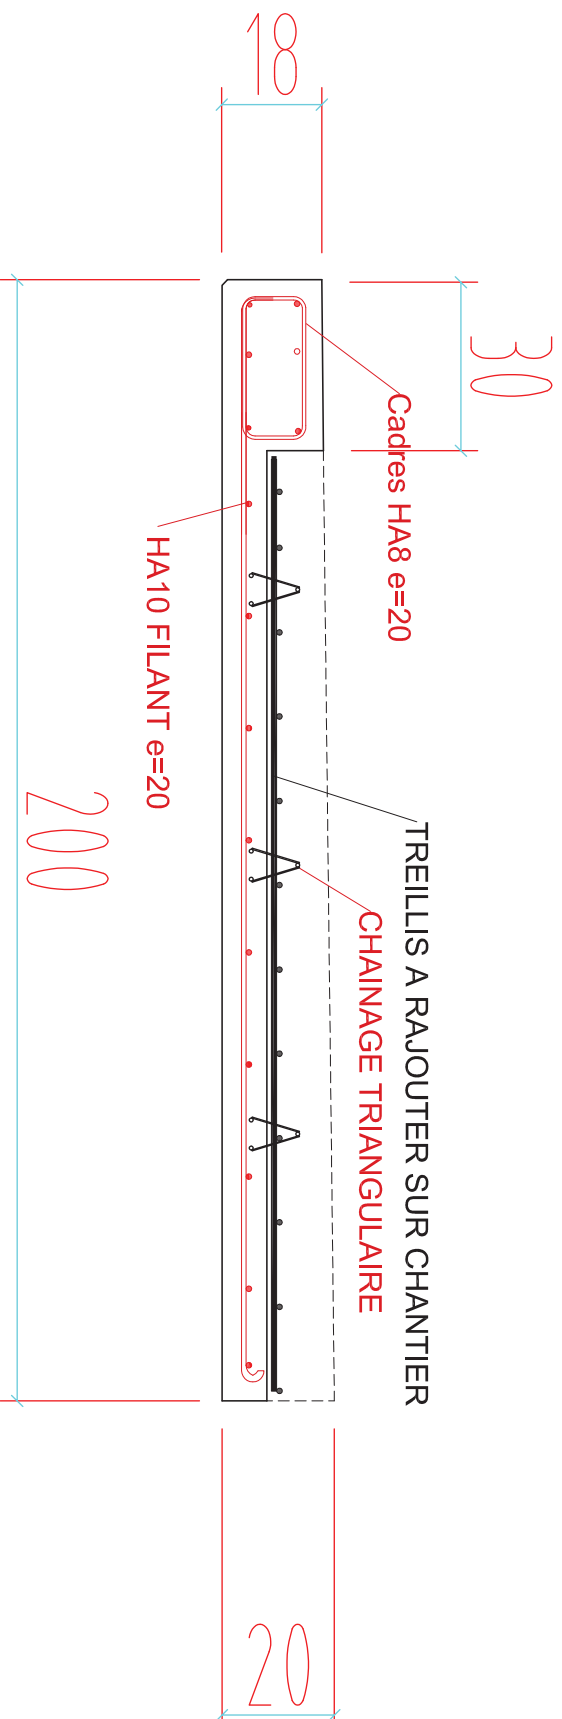

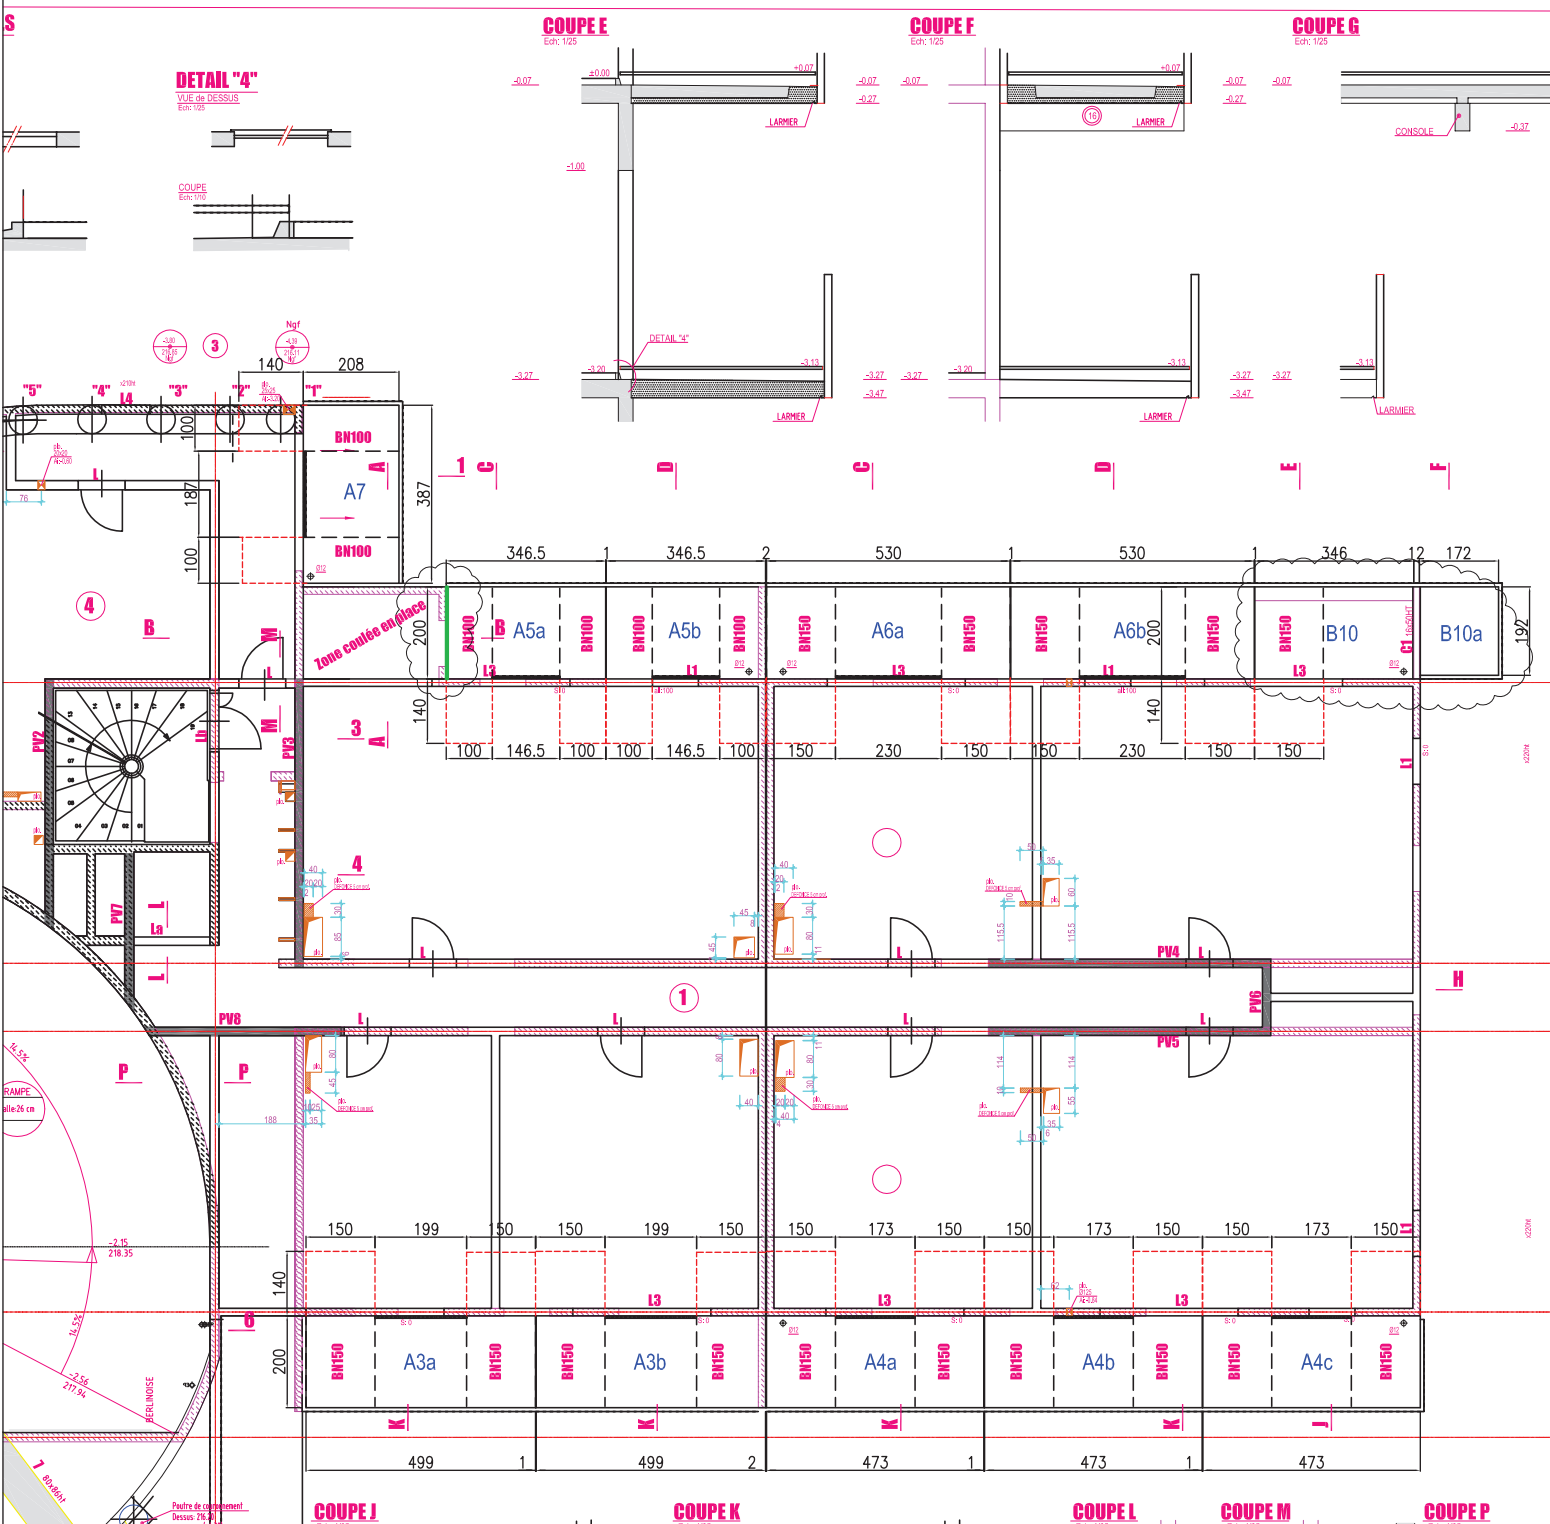

MOULE	N	NC	observations	CONTROLE	N	NC	observations	BETON	N	NC	observations	FICHE AUTO-CONTROLE
Conformité moule				Dimensions				Conformité béton				Opérateur :
Etat du moule				Armature				Mise en place				Responsable prod :
Propreté et huilage				Inserts				Aspect de surface				Date :


Ent. FONTANEL			Elément: BALCONS			PLAN DE FABRCATION			Surface: 9.98 m²		POIDS		REPERE		Nbr	
LA MULATIERE			coffrage / ferrailage			PLATTARD S.A.S.			Volume: 1.89 m3		4.55 T		A3a		1	

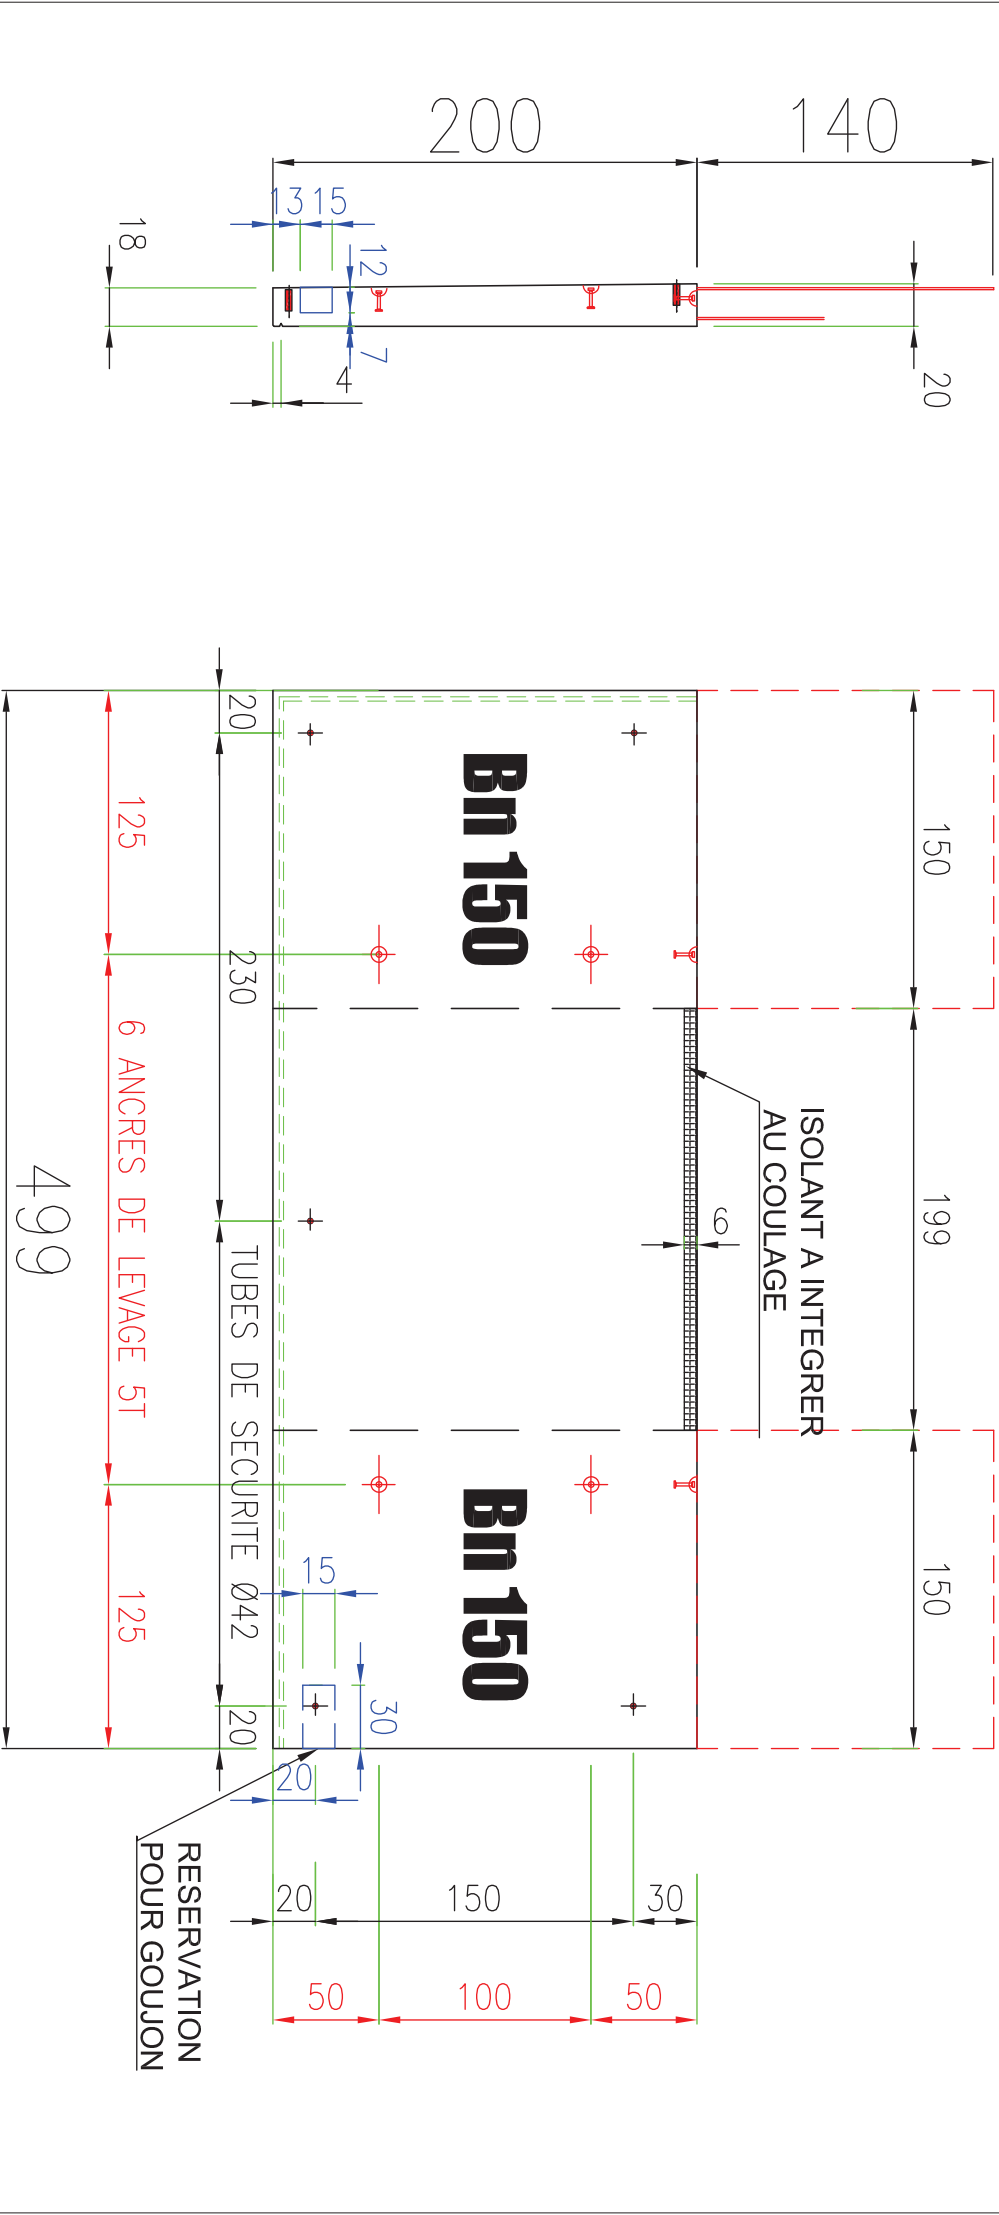

LEVAGE											
	Douille Ø		INSERTS								
	Douille Ø										
	Reinfort Ø dx										
			INSERTS								
	Ancre Frimeda T		INSERTS								
	Reinfort Ø										
	Trifer										
	EBA		INSERTS								
	Douille étalement										
	Ankrobox Ø50										
			INSERTS								
	TP - JV		INSERTS								
	PVC Ø80										
	Tube garde-corps										
Indice											
DATE:		16/11/2015									
Plan N°		Page N°									

MOULE	N	NC	observations	CONTROLE	N	NC	observations	BETON	N	NC	observations	FICHE AUTO-CONTROLE
Conformité moule				Dimensions				Conformité béton				Opérateur :
Etat du moule				Armature				Mise en place				Responsable prod :
Propreté et huilage				Inserts				Aspect de surface				Date :


Ent. FONTANEL				 PLATTARD S.A.S.		PLAN DE FABRCATION		Surface: 9.46 m²		POIDS		REPERE		Nbr	
LA MULATIERE		Elément: BALCONS				coffrage / ferrailage				Volume: 1.80 m3		4.31 T		A4b	

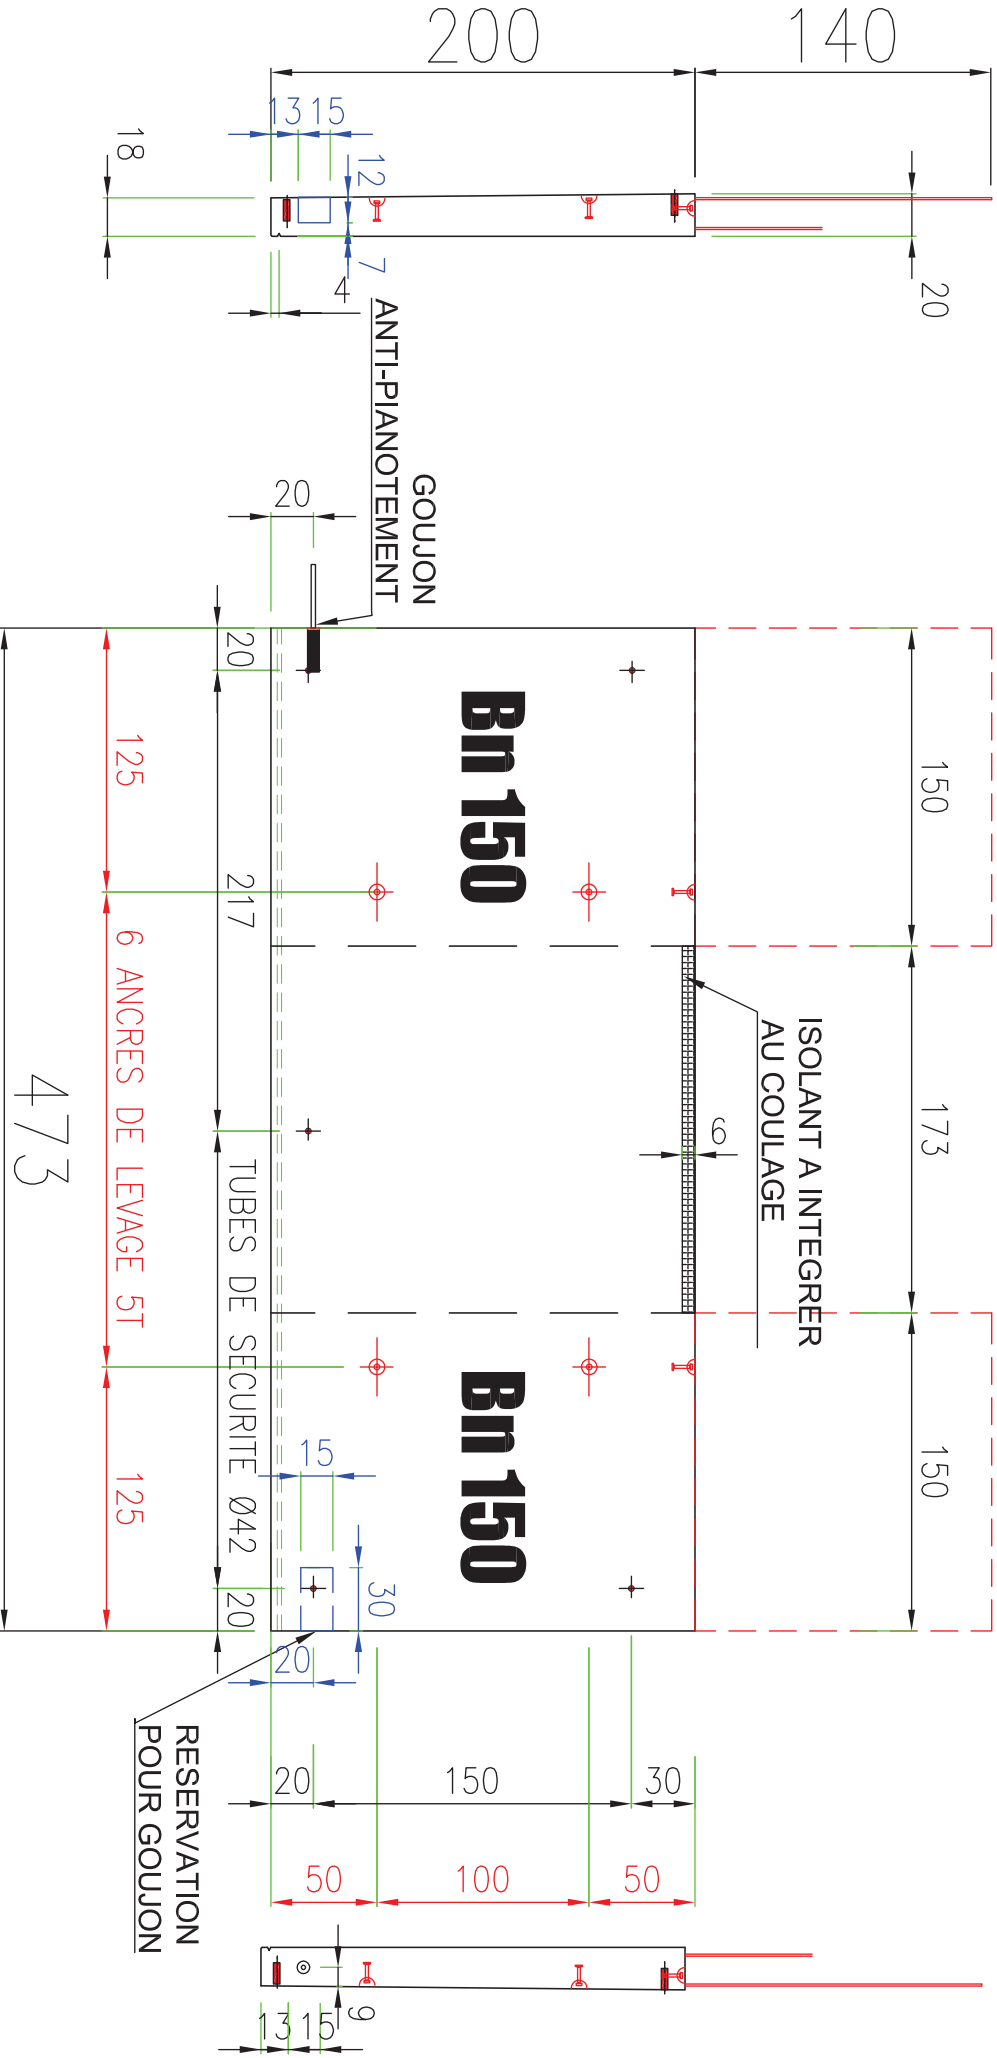

LEVAGE		INSERTS		INSERTS		INSERTS		INSERTS	
	Douille Ø		Ancre Frimeda T		EBA		TP - JV		DATE: 16/11/2015
	Douille Ø		Renfort Ø		Douille étalement		PVC Ø80		Plan N°
	Renfort Ø dx		Trifer		Ankrobox Ø50		Tube garde-corps		Indice
								Page N°	

MOULE	N	NC	observations	CONTROLE	N	NC	observations	BETON	N	NC	observations	FICHE AUTO-CONTROLE
Conformité moule				Dimensions				Conformité béton				Opérateur :
Etat du moule				Armature				Mise en place				Responsable prod :
Propreté et huilage				Inserts				Aspect de surface				Date :


Ent. FONTANEL			PLAN DE FABRCATION				REPERE	
LA MULATIERE			Elément: BALCONS		Surface:	POIDS	Nbr	
			coffrage / ferrailage		Volume:		1	
			PLATTARD S.A.S.		6.93 m²	3.16 T	A5b	

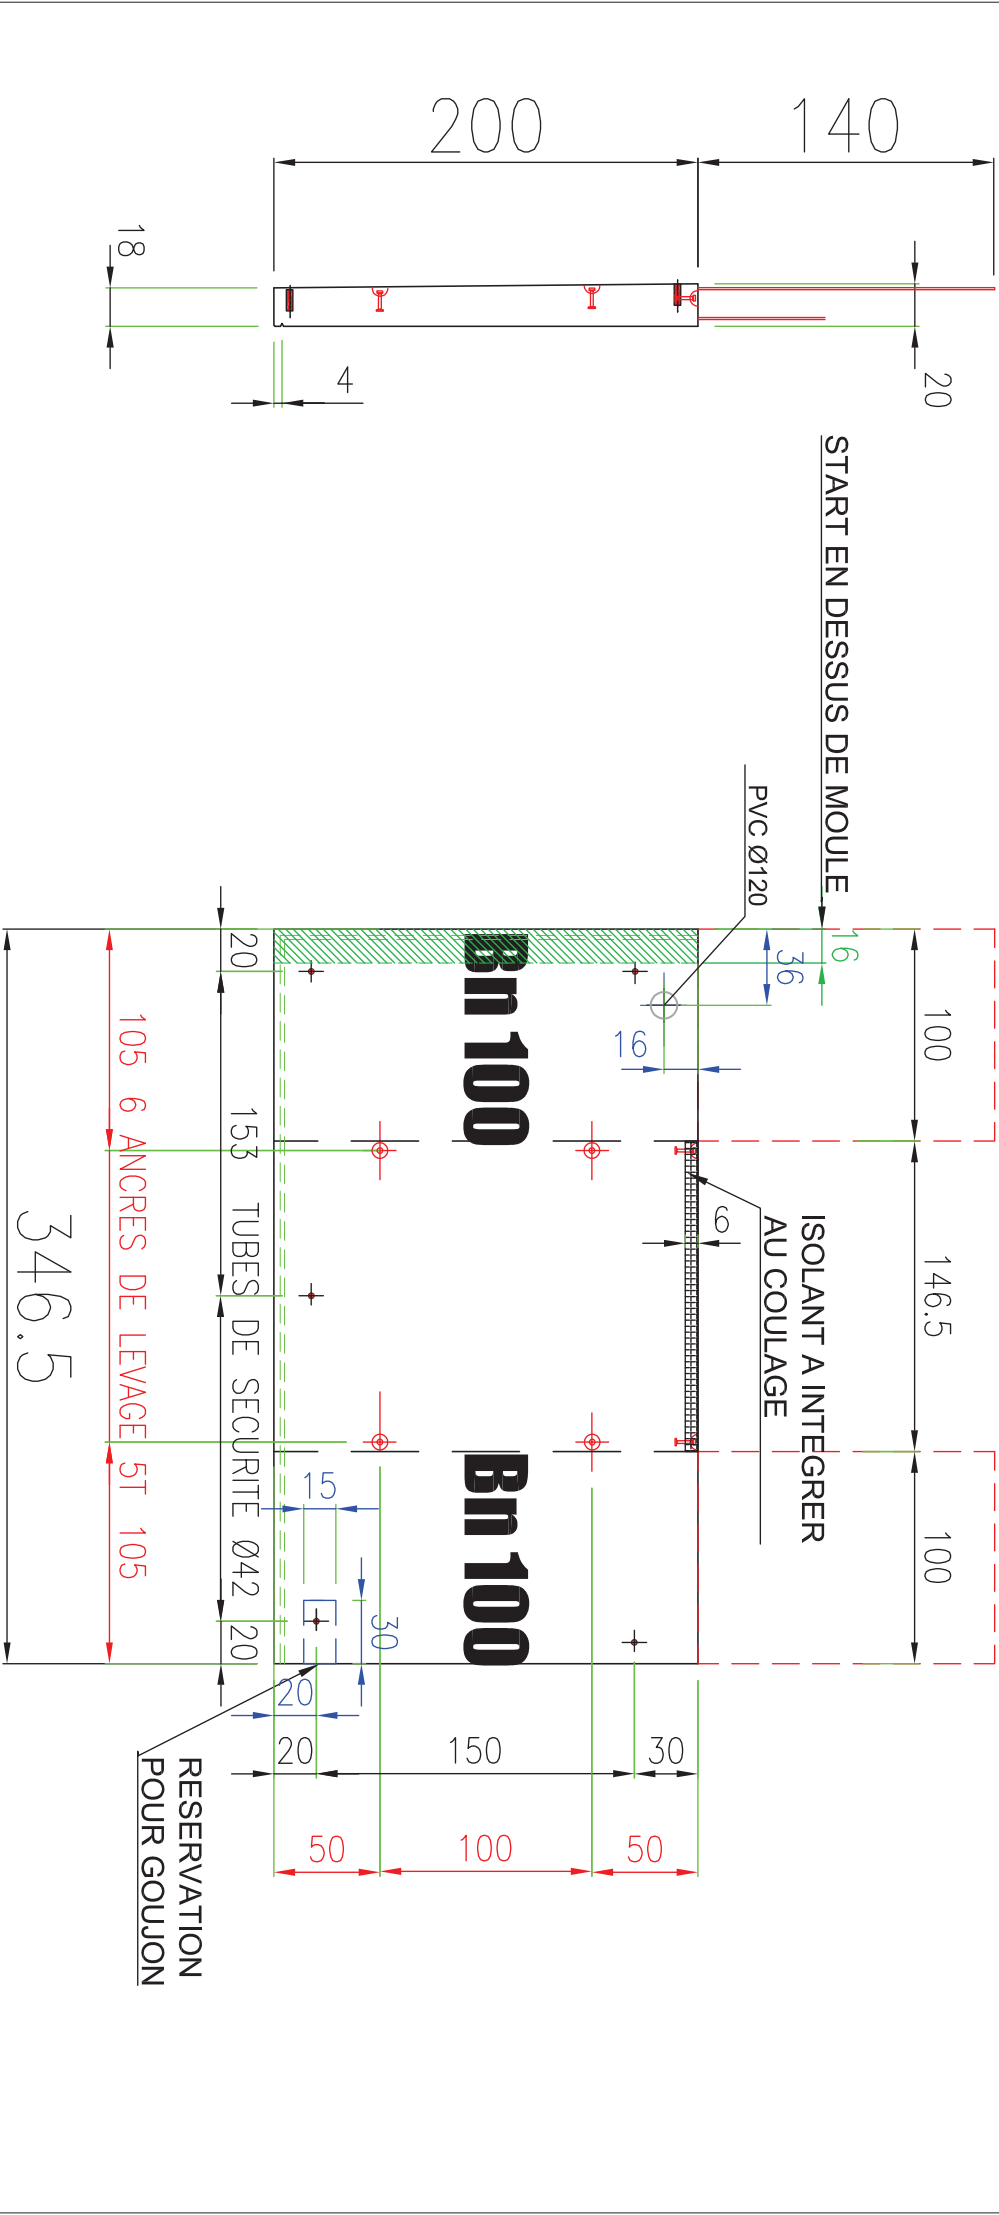

LEVAGE									
	Douille Ø	INSERTS							
	Douille Ø								
	Renfort Ø dx								
	Douille Ø	INSERTS							
	Ancre Frimeda T								
	Renfort Ø								
	Trifer	INSERTS							
	Renfort Ø								
	Trifer								
	Douille Ø	INSERTS							
	Douille étalement								
	Ankrobox Ø50								
	Ankrobox Ø50	INSERTS							
	Ankrobox Ø50								
	Ankrobox Ø50								
	Ankrobox Ø50	INSERTS							
	Ankrobox Ø50								
MOULE	N	NC	observations	CONTROLE	N	NC	observations	BETON	N	NC	observations	FICHE AUTO-CONTROLE
Conformité moule				Dimensions				Conformité béton				Opérateur :
Etat du moule				Armature				Mise en place				Responsable prod :
Propreté et huilage				Inserts				Aspect de surface				Date :

Ent. FONTANEL			Elément: BALCONS			PLAN DE FABRCATION			Surface: 10.60 m²		POIDS		REPERE	Nbr
LA MULATIERE			coffrage / ferrailage			PLATTARD S.A.S.			Volume: 2.01 m3		4.84 T		A6a	1

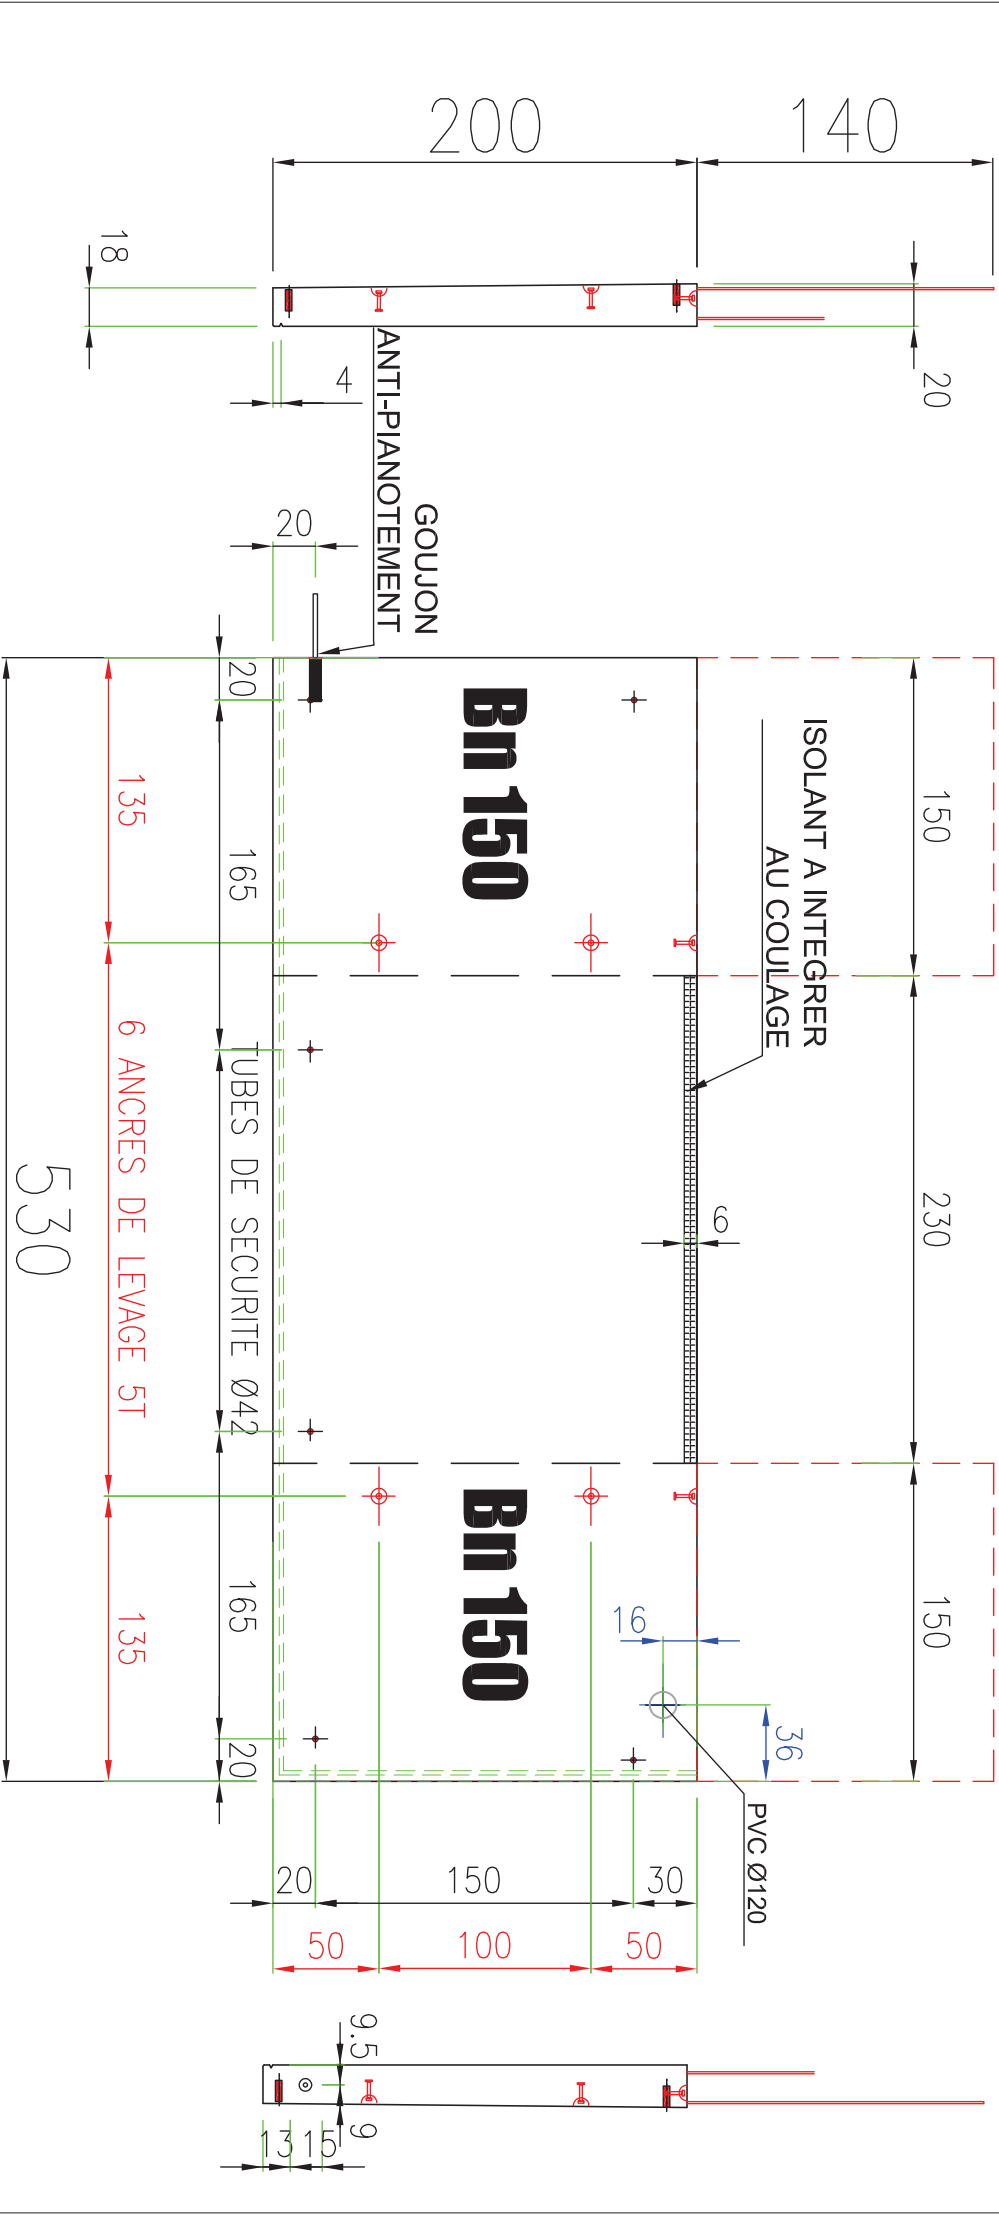


LEVAGE				INSERTS				INSERTS				INSERTS			
	Douille Ø				Ancre Frimeda T				EBA				TP - JV		DATE: 16/11/2015
	Douille Ø				Renfort Ø				Douille étalement				PVC Ø80		Plan N°
	Renfort Ø dx				Trifer				Ankrobox Ø50				Tube garde-corps		Indice

MOULE	N	NC	observations	CONTROLE	N	NC	observations	BETON	N	NC	observations	FICHE AUTO-CONTROLE
Conformité moule				Dimensions				Conformité béton				Opérateur :
Etat du moule				Armature				Mise en place				Responsable prod :
Propreté et huilage				Inserts				Aspect de surface				Date :

Ent. FONTANEL			Elément: BALCONS			PLAN DE FABRCATION			Surface:	10.60 m²	POIDS	REPERE	Nbr
LA MULATIERE			coffrage / ferrailage			PLATTARD S.A.S.			Volume:	2.01 m3	4.84 T	A6b	1

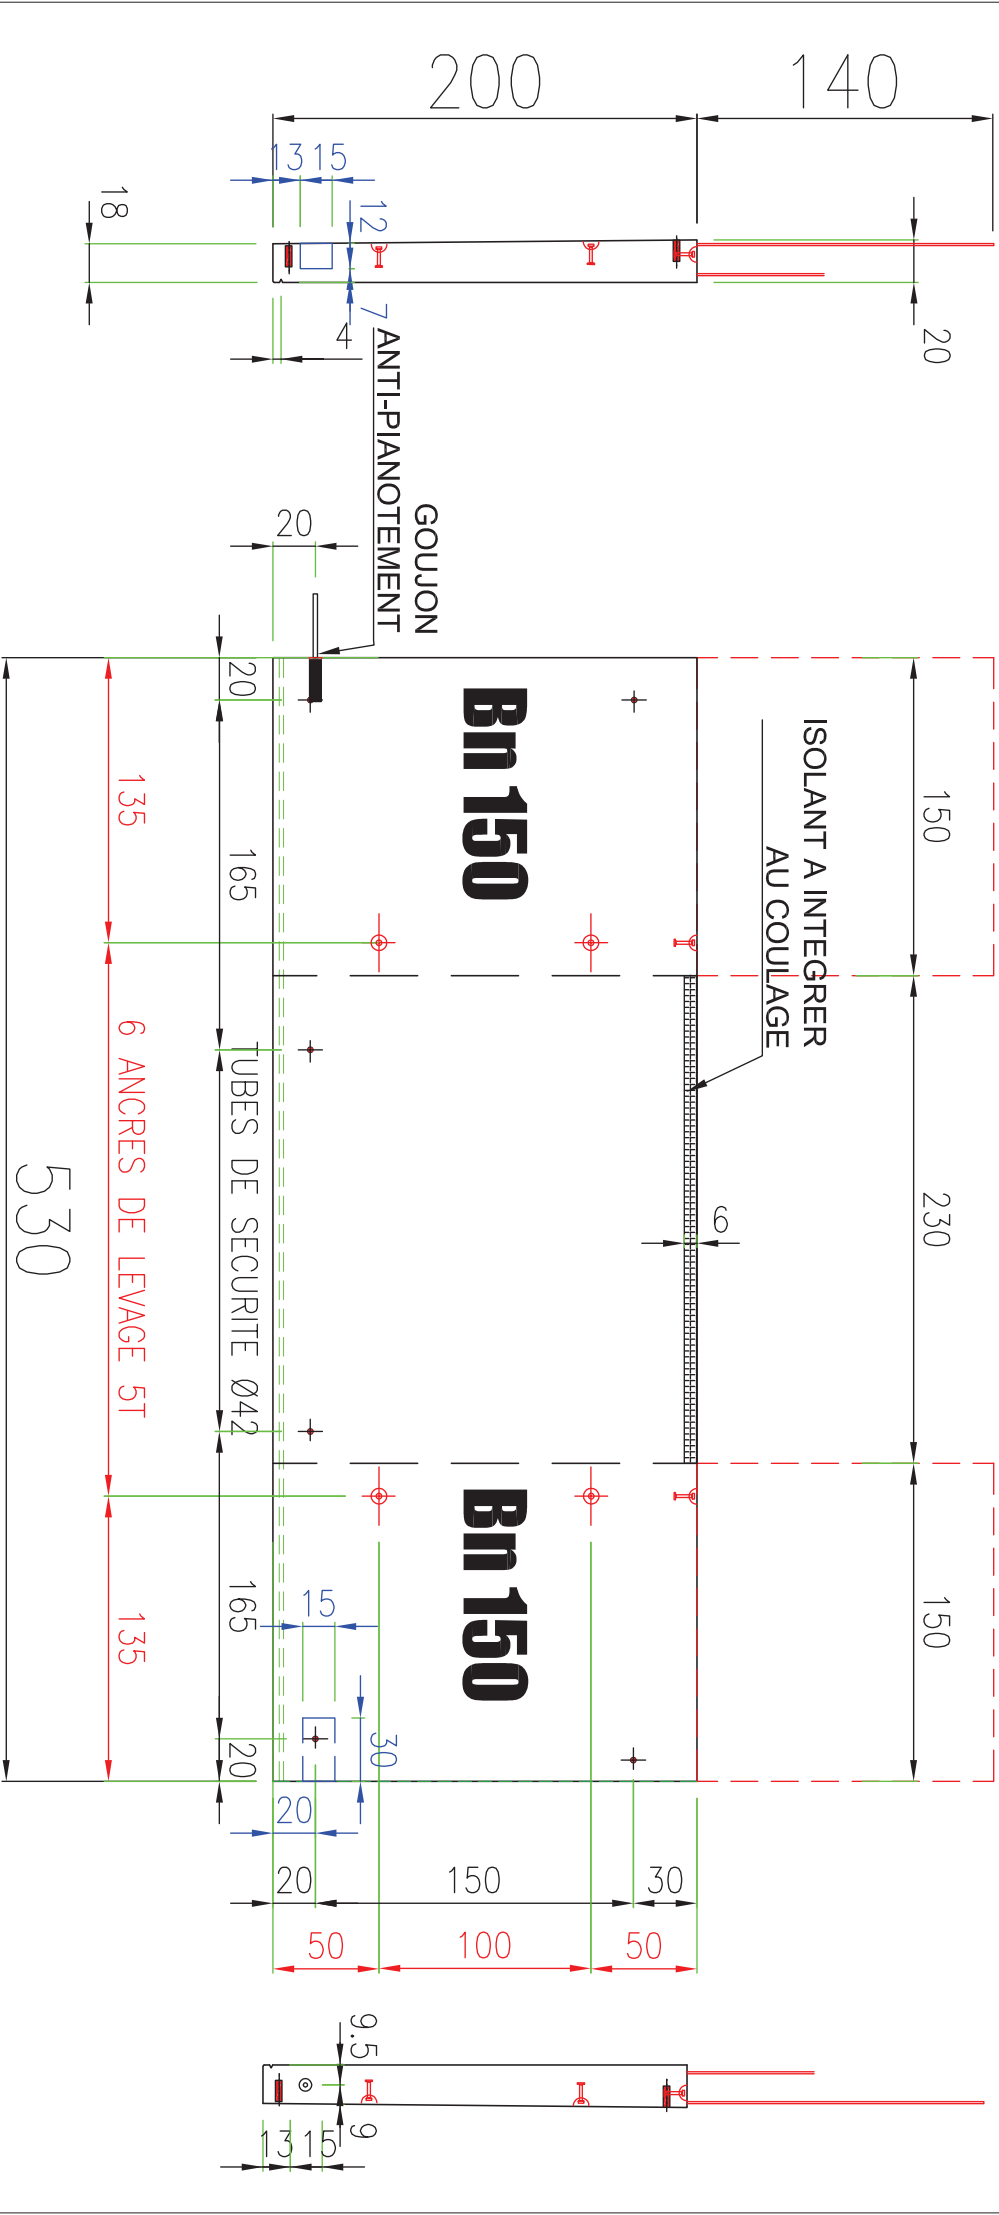

LEVAGE			INSERTS			INSERTS			INSERTS		
	Douille Ø			Ancre Frimeda T			EBA			TP - JV	DATE: 16/11/2015
	Douille Ø			Renfort Ø			Douille étalement			PVC Ø80	Plan N°
	Renfort Ø dx			Trifer			Ankrobox Ø50			Tube garde-corps	Indice
									Page N°		

	N	NC	observations		N	NC	observations		N	NC	observations	FICHE AUTO-CONTROLE
MOULE				CONTROLE				BETON				Opérateur :
Conformité moule				Dimensions				Conformité béton				Responsable prod :
Etat du moule				Armature				Mise en place				Date :
Propreté et huilage				Inserts				Aspect de surface				

Ent. FONTANEL		Elément: BALCONS		 PLATTARD S.A.S.	PLAN DE FABRICATION		Surface: 3.30 m²		POIDS		REPERE		Nbr	
LA MULATIERE		coffrage / ferrailage					Volume: 0.62 m3		1.50 T		B10A		1	

