

NOAHO

Chemin de Fontanière - 69350 La Mulatière

Création de logements

Les entreprises réalisant les travaux devront tenir compte des derniers plans architecte lors de la réalisation des travaux
Les plans du be MATTE ne doivent servir qu'au corps d'état concerné et doivent être des plans d'exécution.

ARCHITECTE(S): ATELIER DE LA PASSERELLE
BET STRUCTURE: MATTE SAS
BET FLUIDES: PRELEM
ECONOMISTE: EXECO
BUREAU DE CONTROLE: Bureau VERITAS

MO DELEGUE:
MOE: PSO Ingénierie
CSPS: SUD EST COORDINATION
OPC:
ENTREPRISE(S): Fontanel-pbc

Bât: A
PLANCHER sur -2 entre files 1 et 9
Coffrage

EXE

Contrainte de sol: 8 bars ELS

Aciers HA (T) FeE500
Aciers Doux (Ø) FeE 235
Aciers TS FeE 500
Béton fc28 >= 25MPa
Enrobage = 3 cm

PLAN N°
A32 0

DATE : 17/12/2015

MATTÉ
BUREAU D'ÉTUDES
STRUCTURES ET FLUIDES


119 BOULEVARD STALINGRAD 69100 VILLEURBANNE
Tél. 04 72 44 02 87 Fax 04 72 44 26 59
E-mail : bet@matte.fr

Dessiné par : J.BO
Contrôlé par : P.LIN
Echelle : 1/50°

Affaire N°
13.12.119


Plancher Niveau R-2

BAT. A

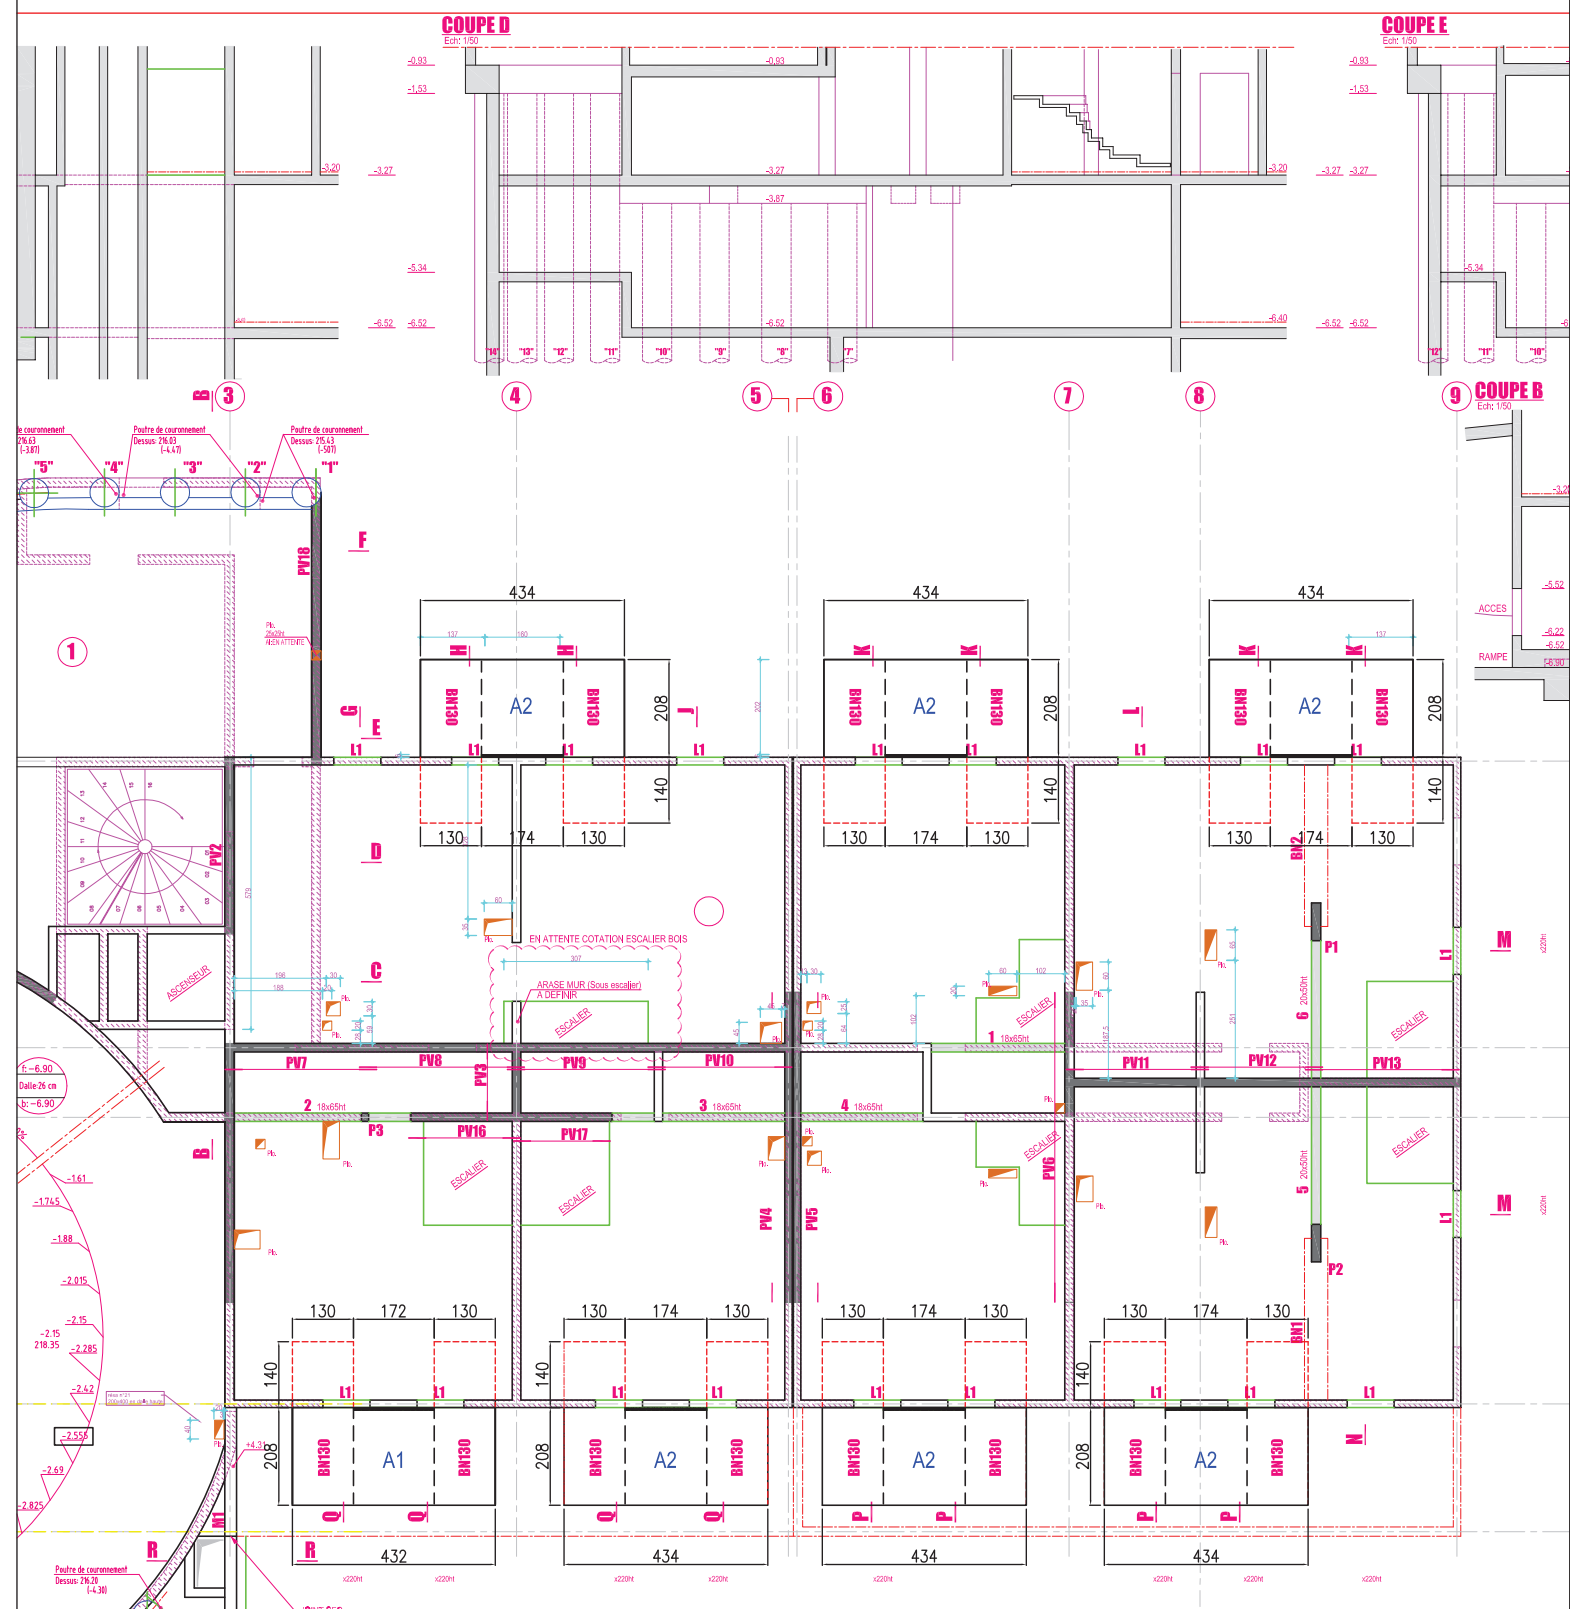

MOULE	N	NC	observations	CONTROLE	N	NC	observations	BETON	N	NC	observations	FICHE AUTO-CONTROLE
Conformité moule				Dimensions				Conformité béton				Opérateur :
Etat du moule				Armature				Mise en place				Responsable prod :
Propreté et huilage				Inserts				Aspect de surface				Date :


Ent. FONTANEL			PLAN DE FABRCATION			Surface: 8.99 m²		POIDS		REPERE	Nbr
LA MULATIERE			Elément: BALCONS			Volume: 1.70 m3		4.10 T		A1	
			coffrage / ferrailage								

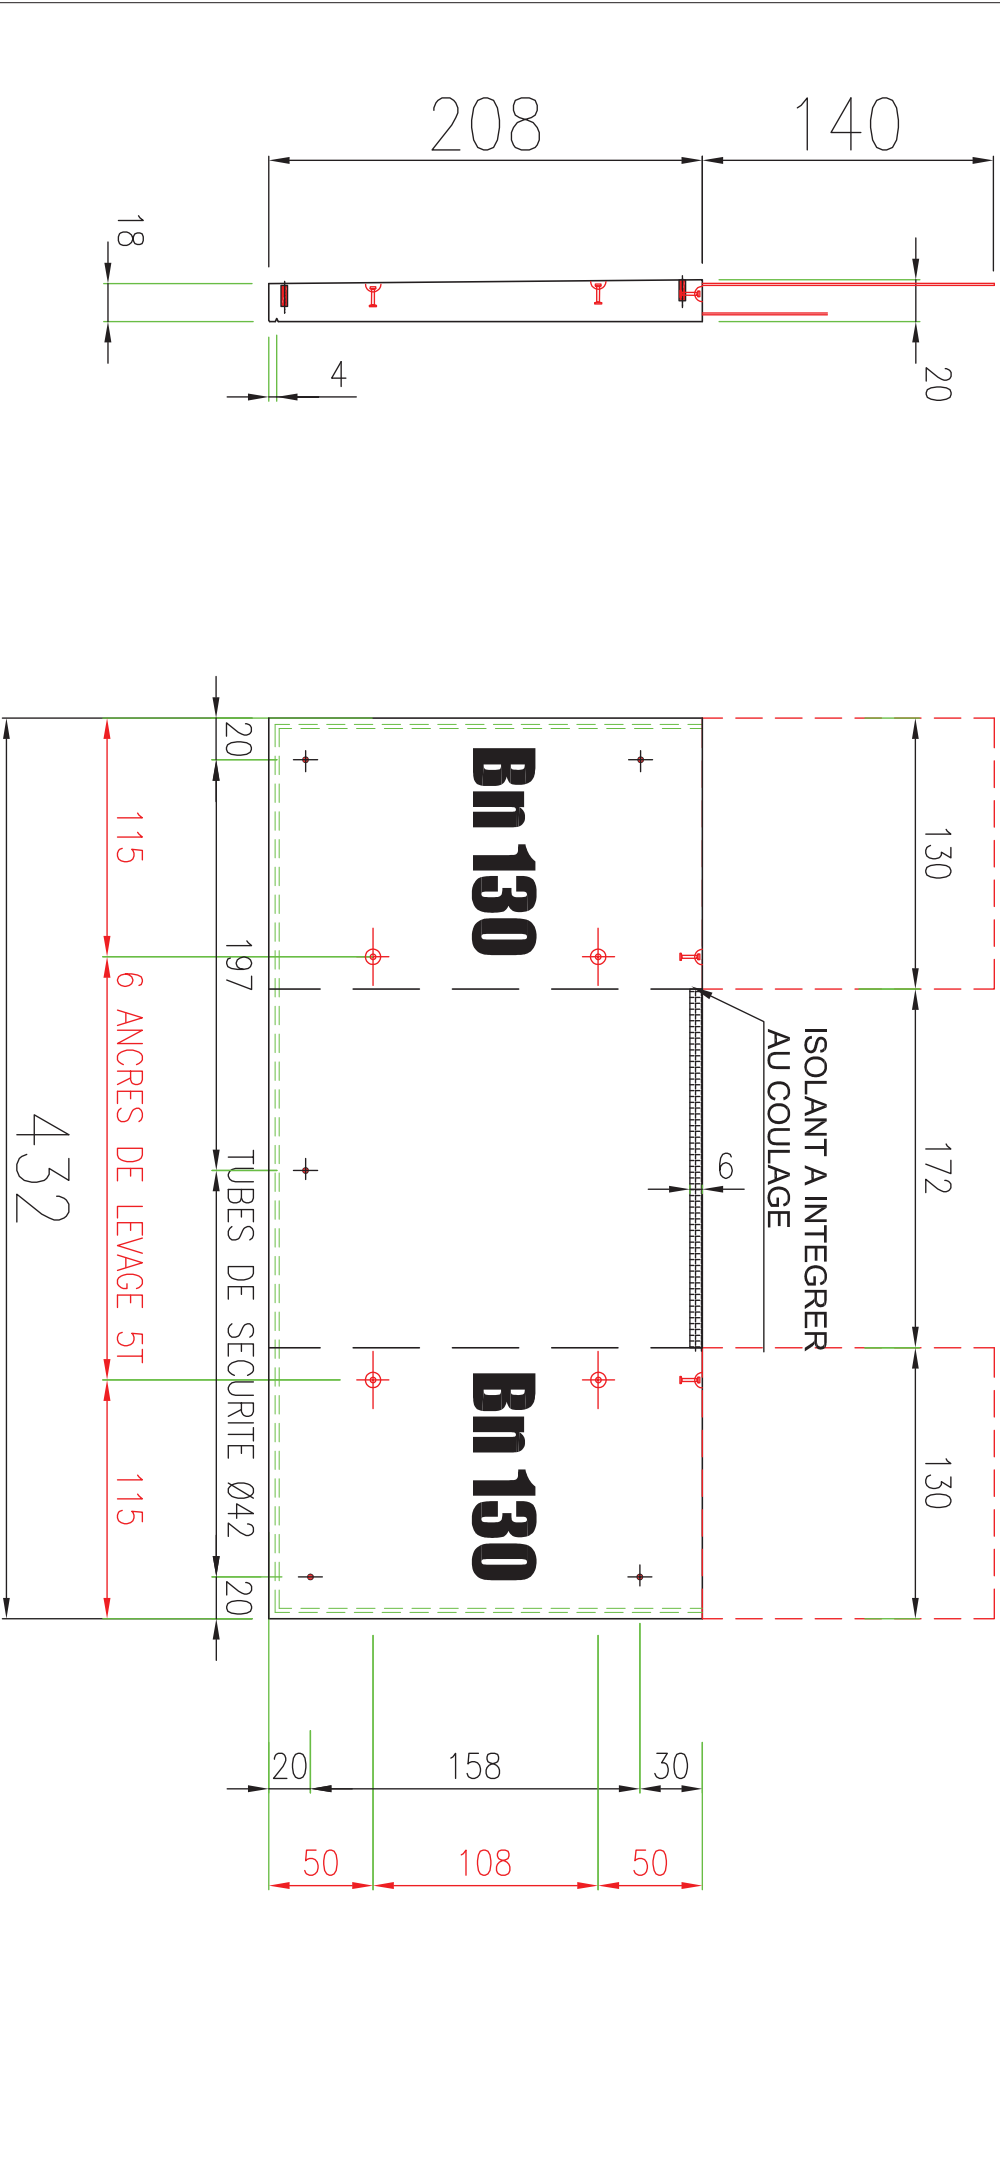

LEVAGE			INSERTS			INSERTS			INSERTS			INSERTS			INSERTS		
	Douille Ø	Renfort Ø dx		Ancre Frimeda T	Trifler		EBA	Ankrebox Ø50		TP - JV	DATE: 22/12/2015		PVC Ø80	Tube garde-corps	Indice	Plan N°	Page N°

MOULE	N	NC	observations	CONTROLE	N	NC	observations	BETON	N	NC	observations	FICHE AUTO-CONTROLE
Conformité moule				Dimensions				Conformité béton				Opérateur :
Etat du moule				Armature				Mise en place				Responsable prod :
Propreté et huilage				Inserts				Aspect de surface				Date :

Ent. FONTANEL											
LA MULATIERE		Elément: BALCONS				coffrage / ferrillage		PLAN DE FABRCATION			
		Surface:		9.03 m²		POIDS		REPERE		Nbr	
						4.11 T					
		Volume:		1.71 m3				A2		6	

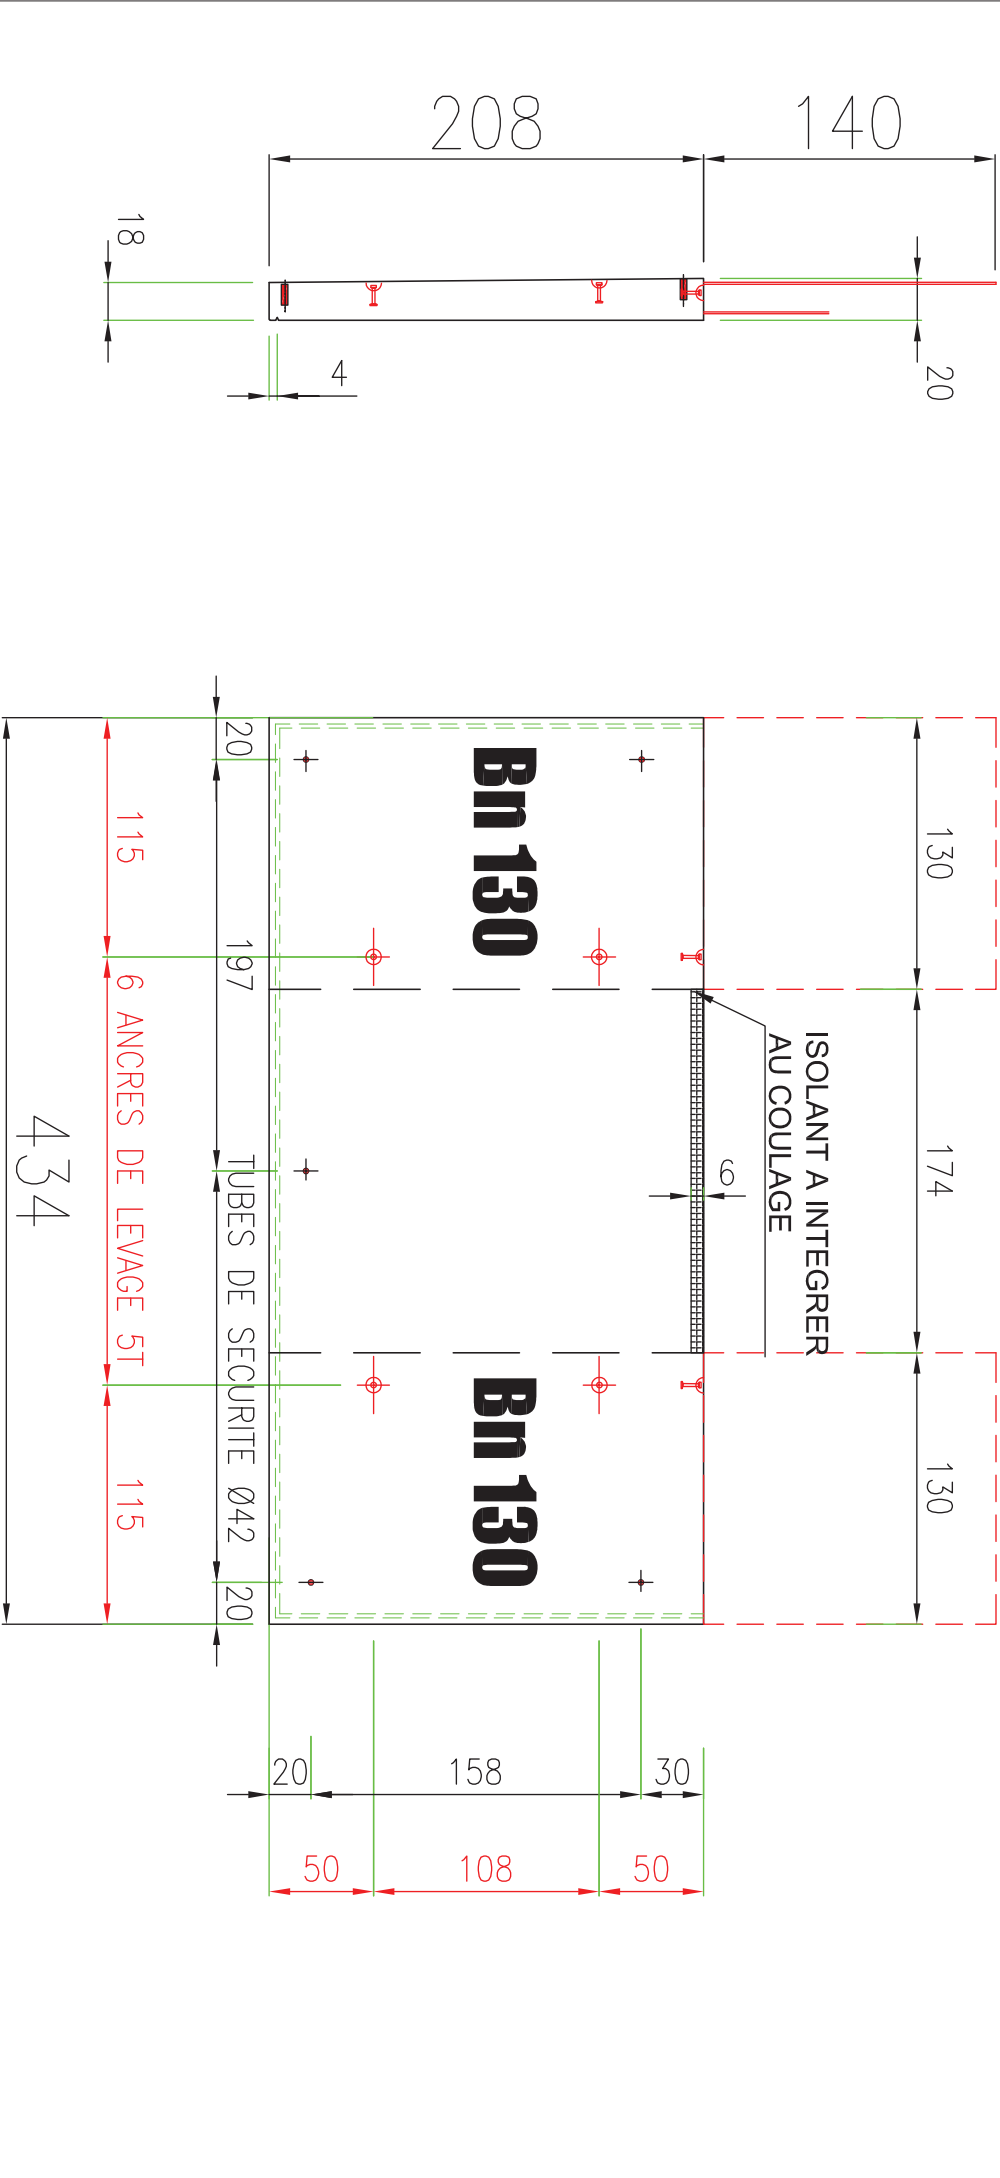

LEVAGE		INSERTS		INSERTS		INSERTS		DATE: 22/12/2015	
	Douille Ø		Ancre Frimeda T		EBA		TP - JV	Plan N° Page N°	
	Douille Ø		Renfort Ø		Douille étalement		PVC Ø80		
	Renfort Ø dx		Trifer		Ankrobox Ø50		Tube garde-corps	Indice	