

NOAHO

Chemin de Fontanière - 69350 La Mulatière

Création de logements

Les entreprises réalisant les travaux devront tenir compte des derniers plans architecte lors de la réalisation des travaux
Les plans du be MATTE ne doivent servir qu'au corps d'état concerné et doivent être des plans d'exécution.

ARCHITECTE(S): ATELIER DE LA PASSERELLE

MO DELEGUE:

BET STRUCTURE: MATTE SAS

MOE: PSO Ingénierie

BET FLUIDES: PRELEM

CSPS: SUD EST COORDINATION

ECONOMISTE: EXECO

OPC:

BUREAU DE CONTROLE: Bureau VERITAS

ENTREPRISE(S): Fontanel-pbc

Bât: A et B

ESCALIER SUR RAMPE NORD POSITION DES MASSIFS BA

EXE

Contrainte de sol: 8 bars ELS

INDICE	DATE	MODIFICATIONS
A	30/11/2015	AJOUTE ESCALIERS
B	4/12/2015	MISE A JOUR MASSIFS et AJOUTE COUPES F,G,H
C	08/12/2015	MISE A JOUR COUPES B et C
D	15/12/2015	MISE A JOUR ESCALIERS FILES 6 et 7
E	17/12/2015	MISE A JOUR ESCALIER FILE 16

Aciers HA (T) FeE500

Aciers Doux (Ø) FeE 235

Aciers TS FeE 500

Béton fc28 >= 25MPa

Enrobage = 3 cm

PLAN N°
B05 E

DATE : 25/09/2015

MATTÉ
BUREAU D'ÉTUDES
STRUCTURES ET FLUIDES

119 BOULEVARD STALINGRAD 69100 VILLEURBANNE

Tél. 04 72 44 02 87 Fax 04 72 44 26 59

E-mail : bet@matte.fr

Dessiné par : J.BO


Contrôlé par : P.LIN

Echelle : 1/50°

Affaire N°
13.12.119


BAT.A

PLANS REALISES A PARTIR DU PLAN BE B05_E

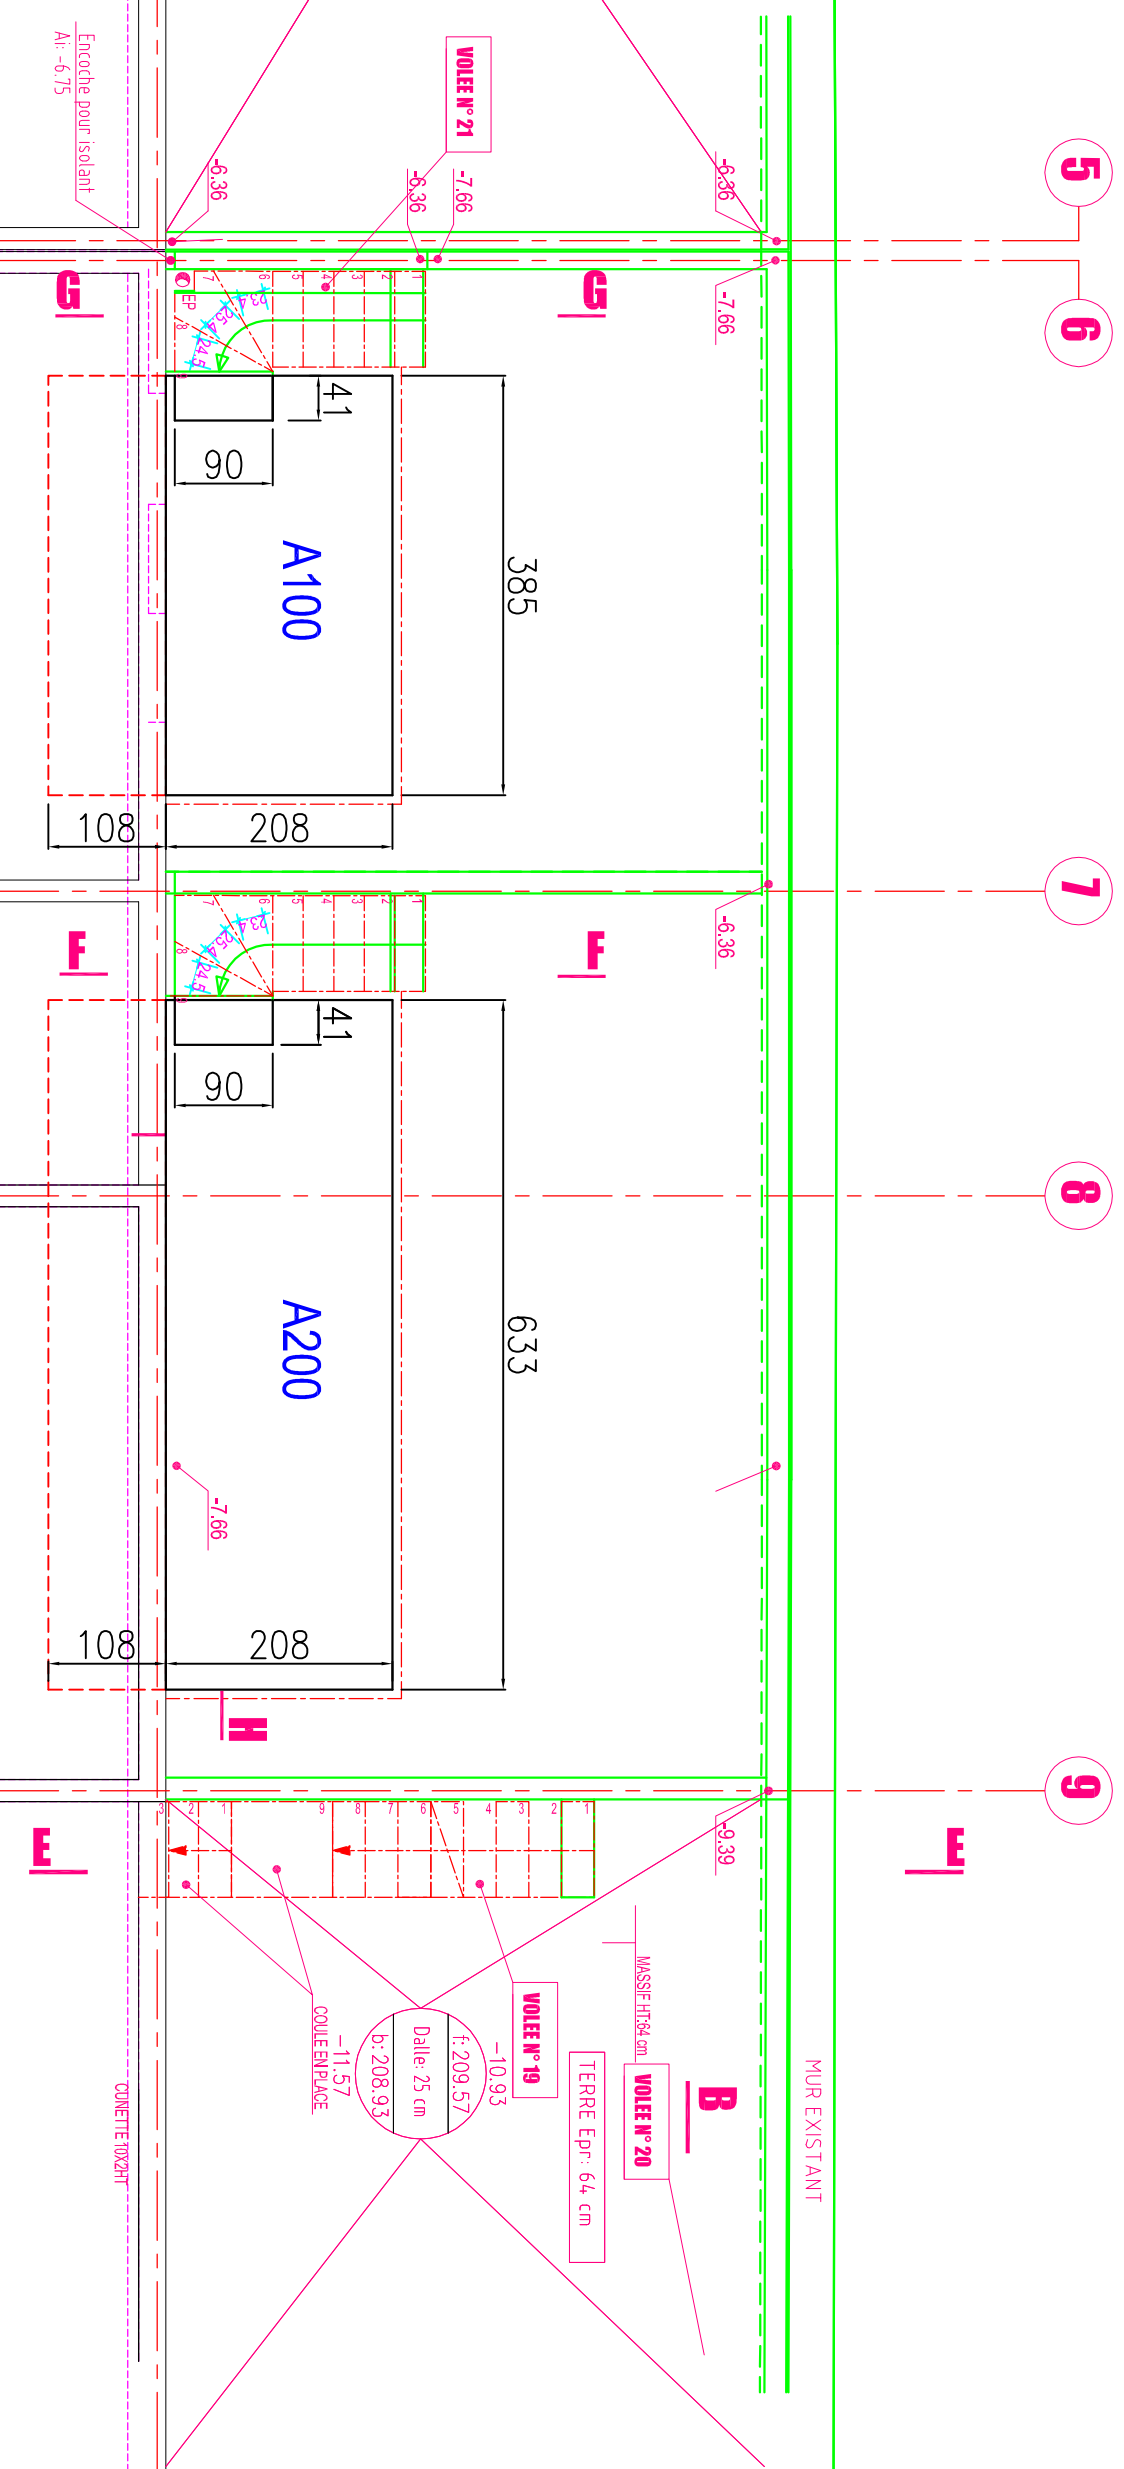

MOULE	N	NC	observations	CONTROLE	N	NC	observations	BETON	N	NC	observations	FICHE AUTO-CONTROLE
Conformité moule				Dimensions				Conformité béton				Opérateur :
Etat du moule				Armature				Mise en place				Responsable prod :
Propreté et huilage				Inserts				Aspect de surface				Date :

Ent. FONTANEL				 PLATTARD S.A.S.		PLAN DE FABRCATION		Surface: 13.17 m²		POIDS		REPERE		Nbr	
LA MULATIERE		Elément: BALCONS						Volume: 2.46 m3		5.90 T		A200		1	
		coffrage / ferrailage													

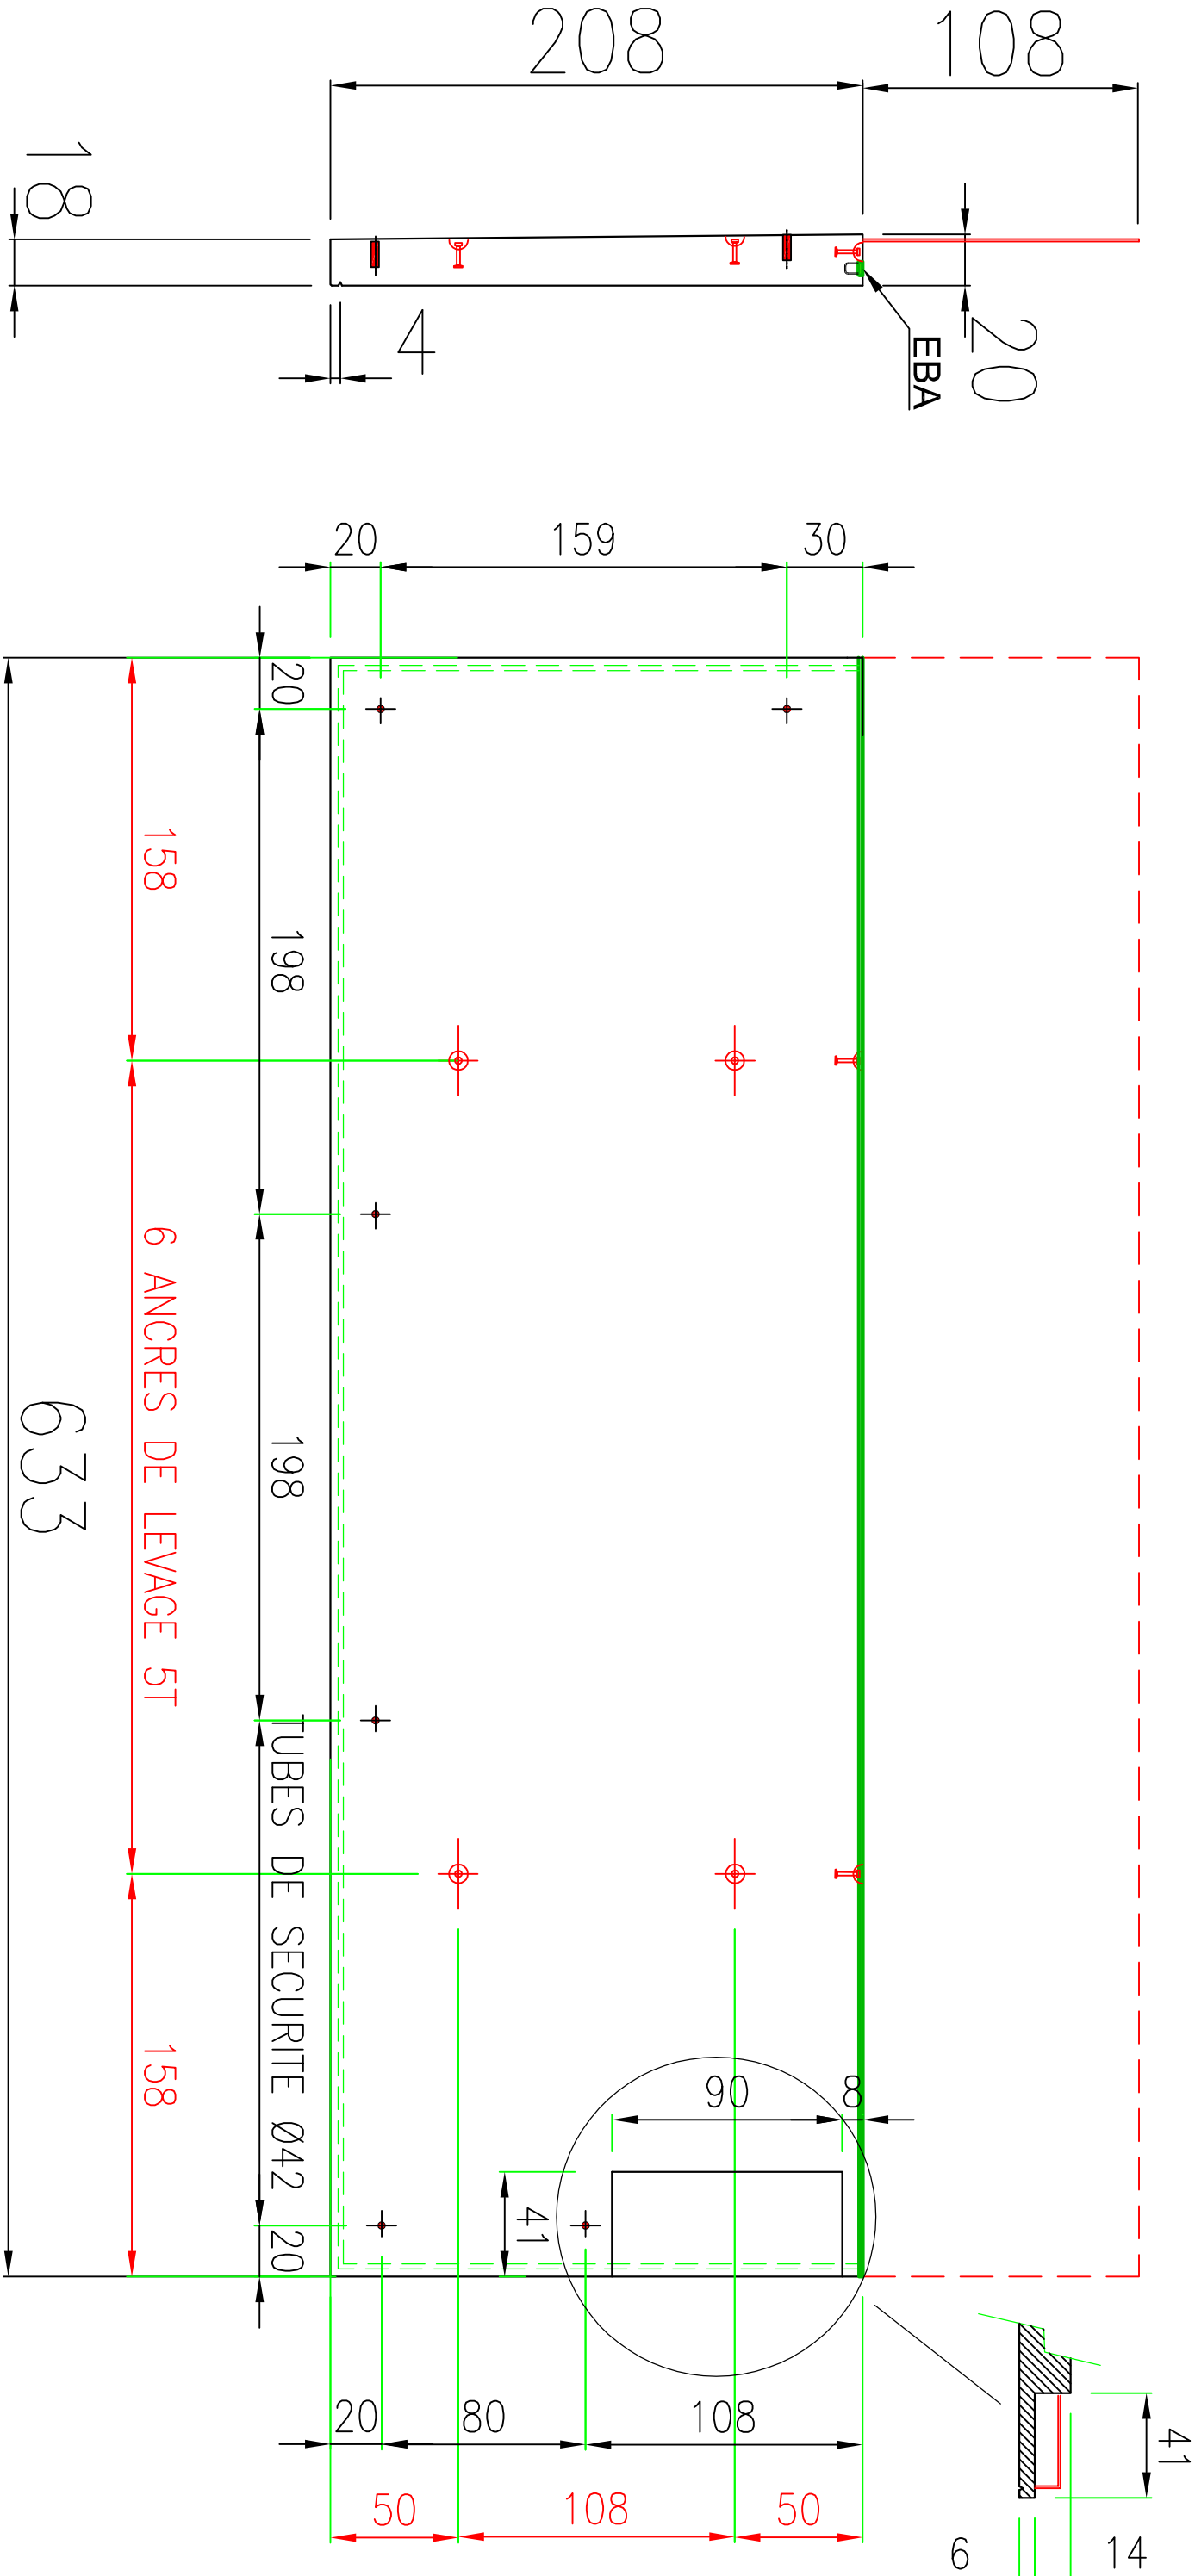

LEVAGE									
		Douille Ø		INSERTS					
		Douille Ø							
		Renfort Ø dx							
		Ancre Frimeda T		INSERTS					
		Renfort Ø							
		Trifer							
		EBA		INSERTS					
		Douille étalement							
		Ankrobox Ø50							
		TP - JV		INSERTS					
		PVC Ø80							
		Tube garde-corps							
DATE: 07/01/2016		Plan N°		Indice		Page N°			