


Plancher Niveau R0


BAT. A

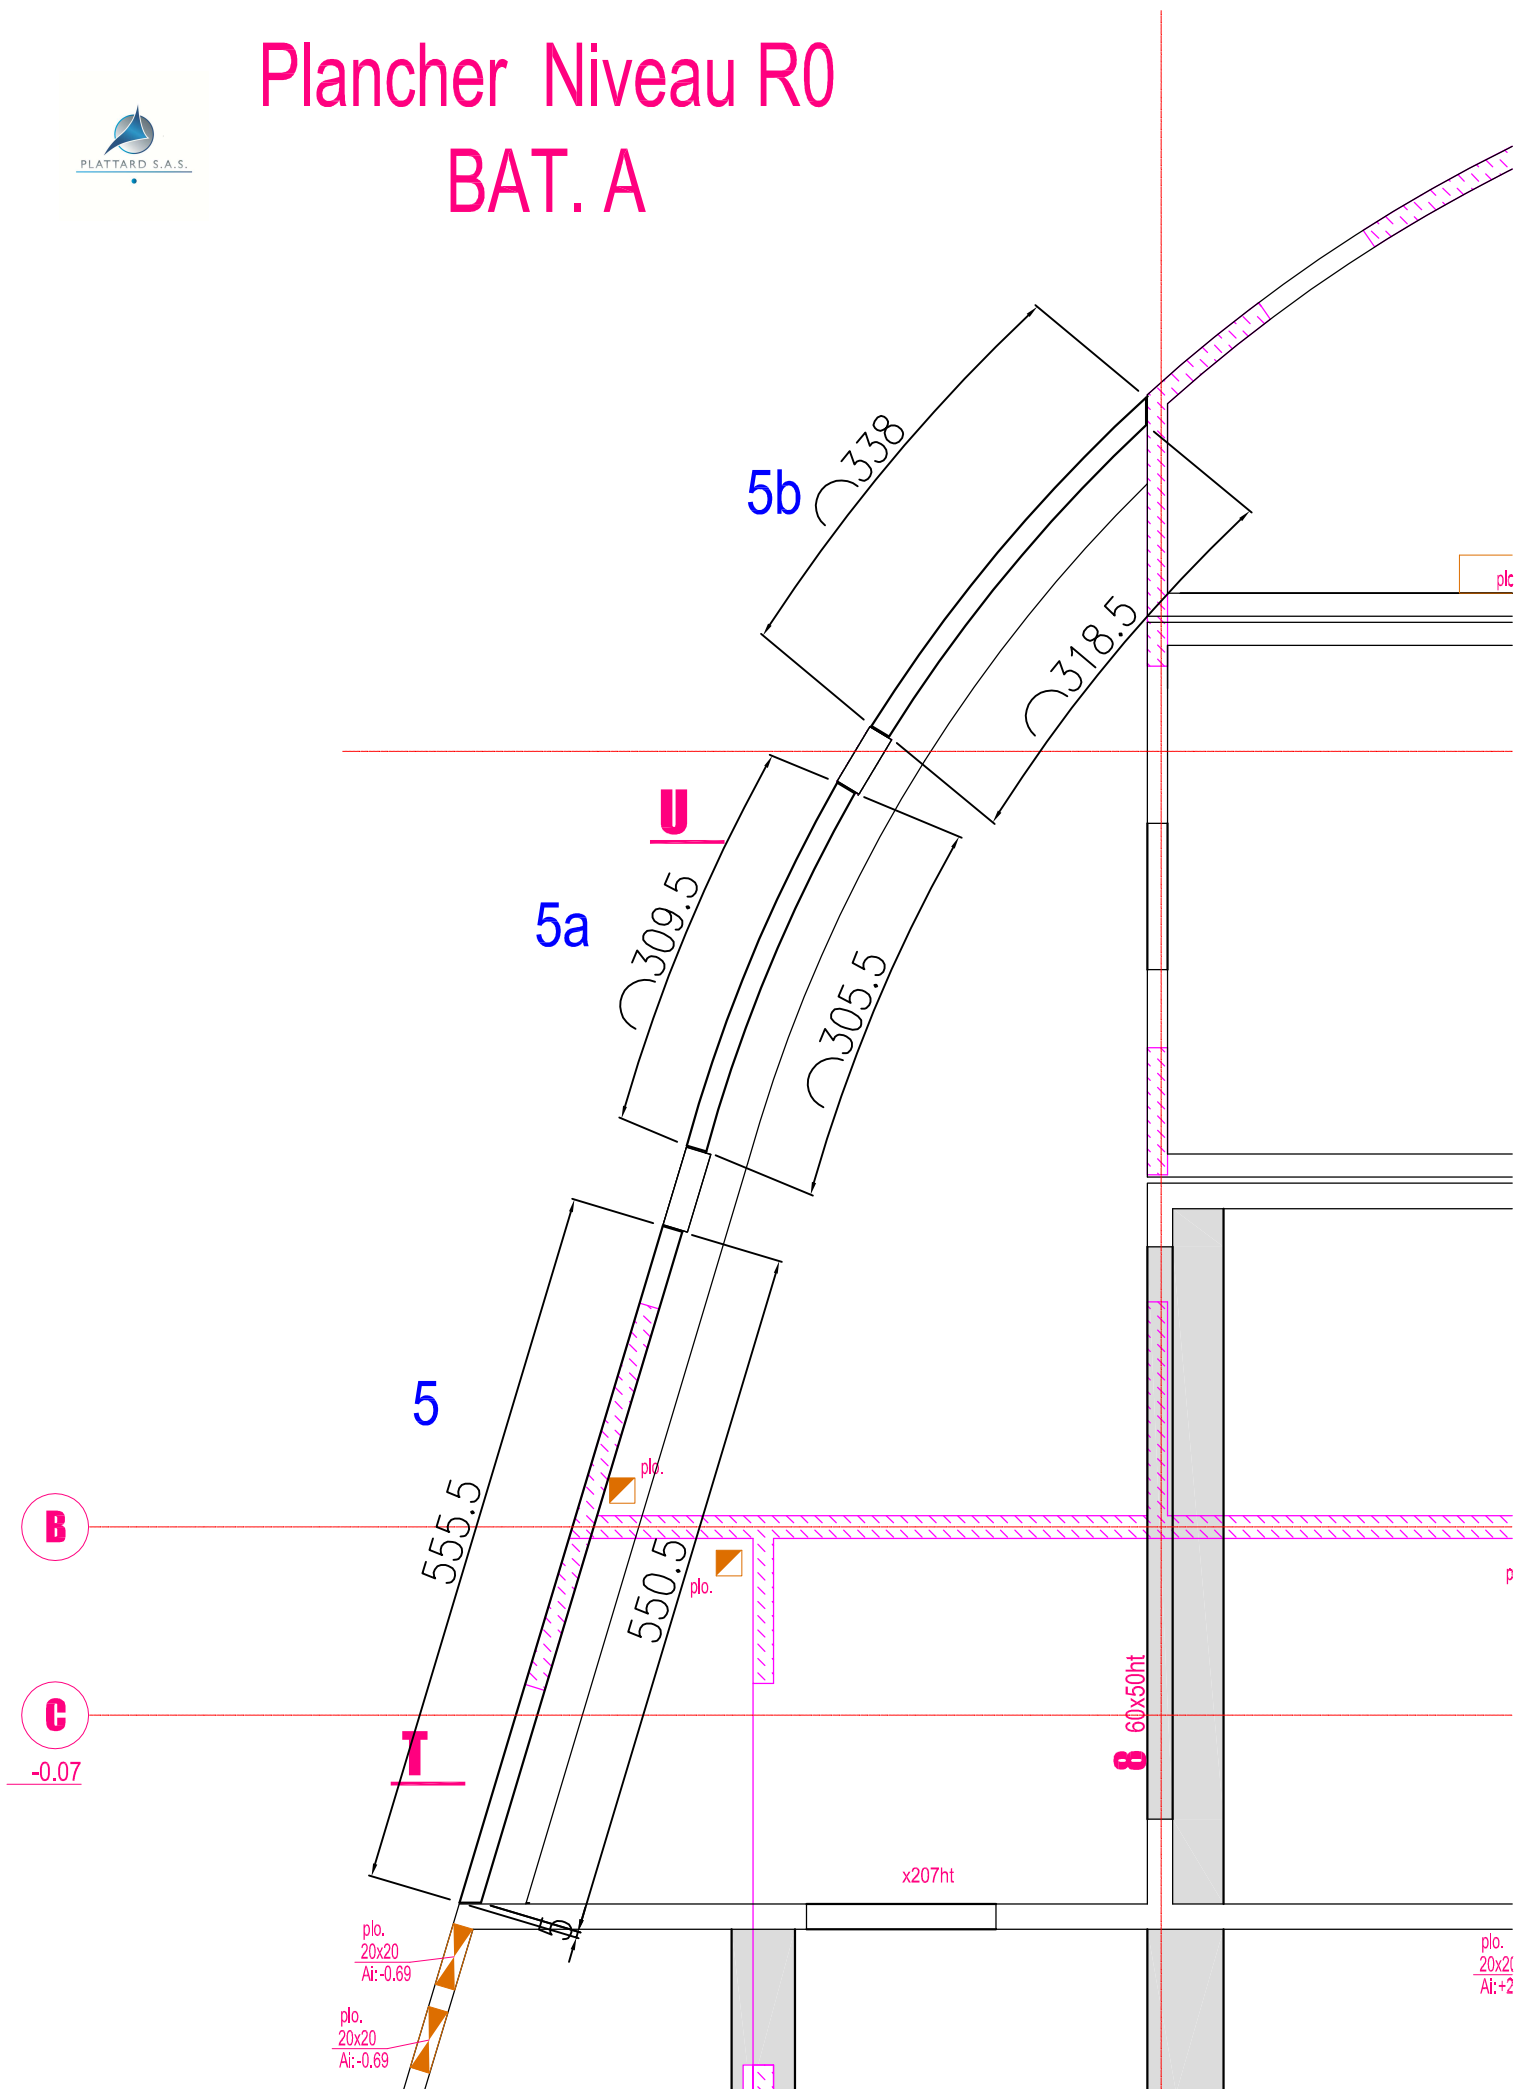

LE 180 - LA MULATIERE

BANDEAU TYPE 5


NIVEAU 0

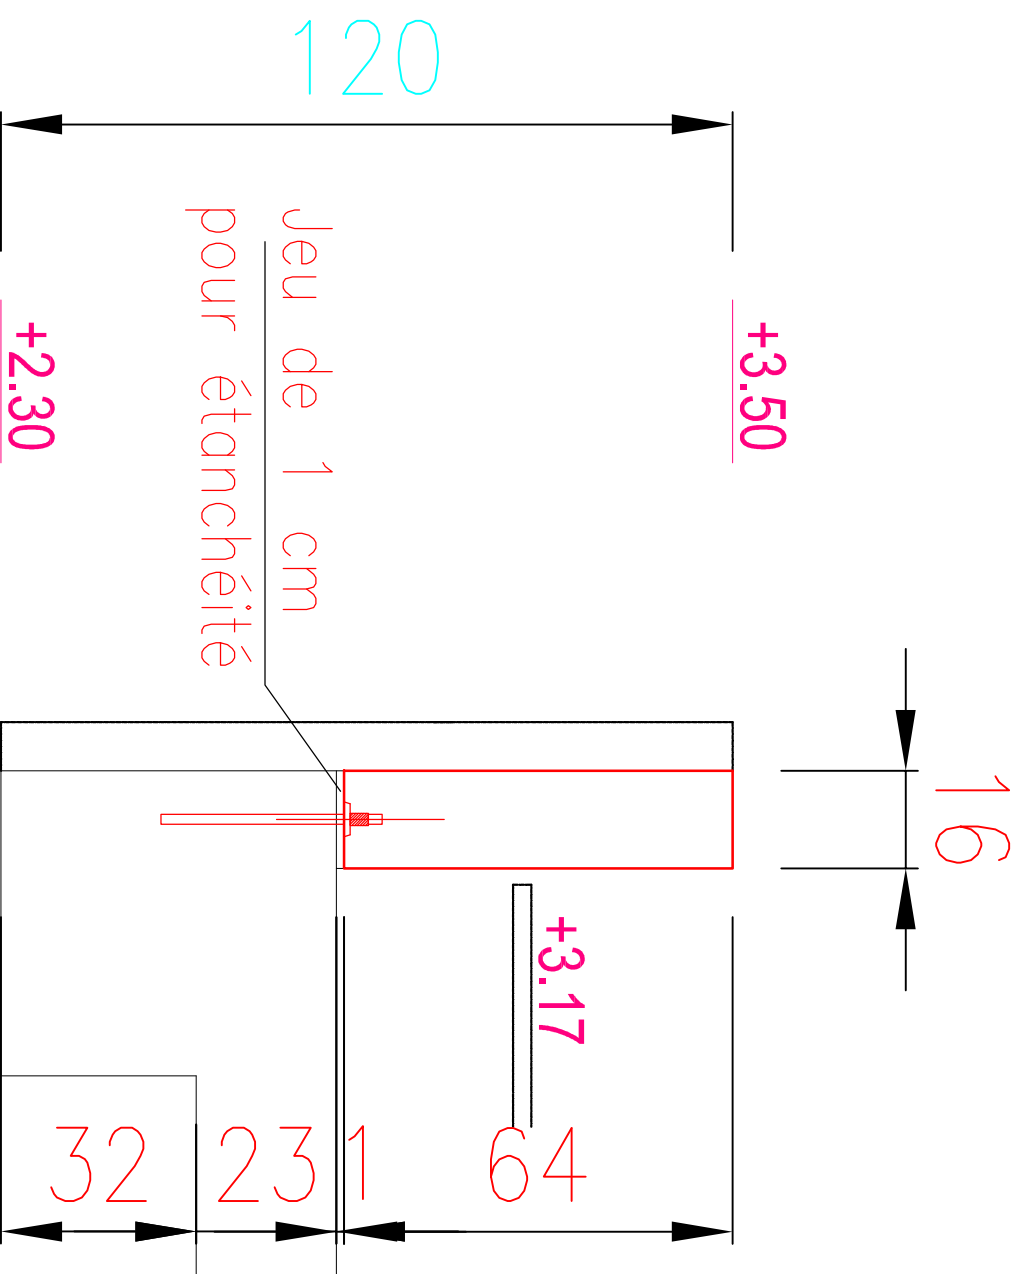

LE 180 - LA MULATIERE

BANDEAU TYPE 5

NIVEAU 0

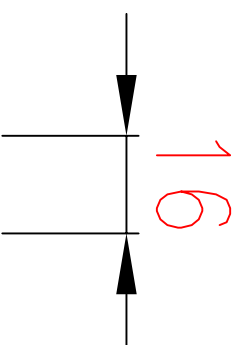

10


56



Cadres HA6 e=20




2 Filants HA10

6 Filants HA8

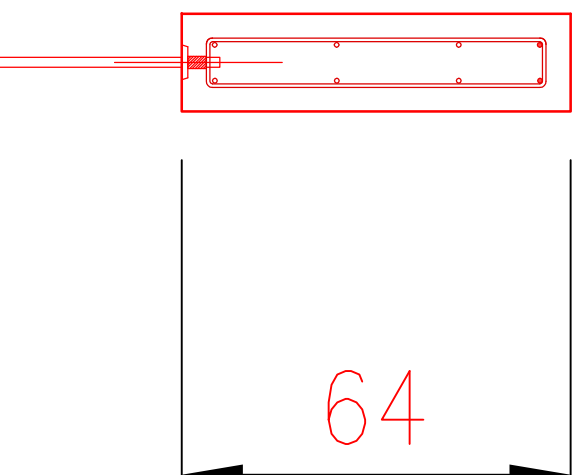

MOULE	N	NC	observations	CONTROLE	N	NC	observations	BETON	N	NC	observations	FICHE AUTO-CONTROLE
Conformité moule				Dimensions				Conformité béton				Opérateur :
Etat du moule				Armature				Mise en place				Responsable prod :
Propreté et huilage				Inserts				Aspect de surface				Date :



Ent. FONTANEL		Elément: BANDEAUX		 PLATTARD S.A.S. FICHE DE FABRICATION		Surface: m²		POIDS		REPERE		Nbr	
LE 180 - LA MULATIERE		ø coffrage				Volume: 0.57 m3		1.24 T		5		1	

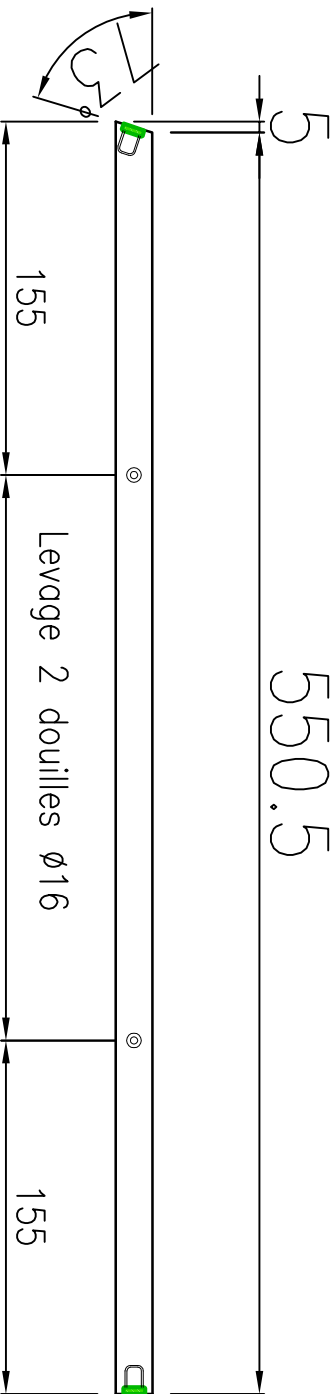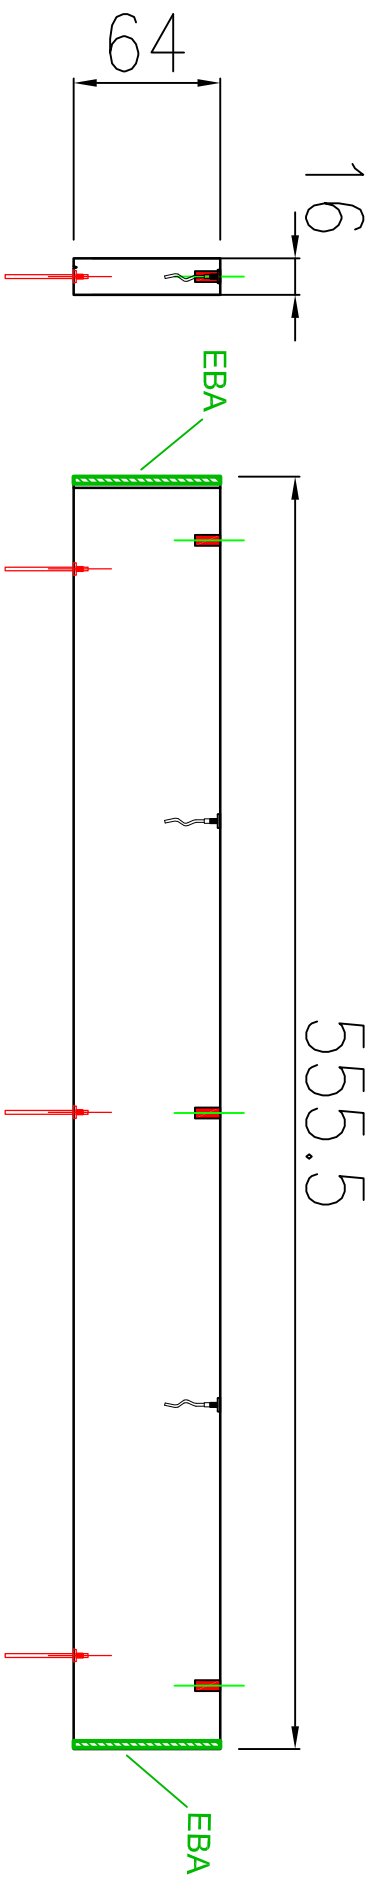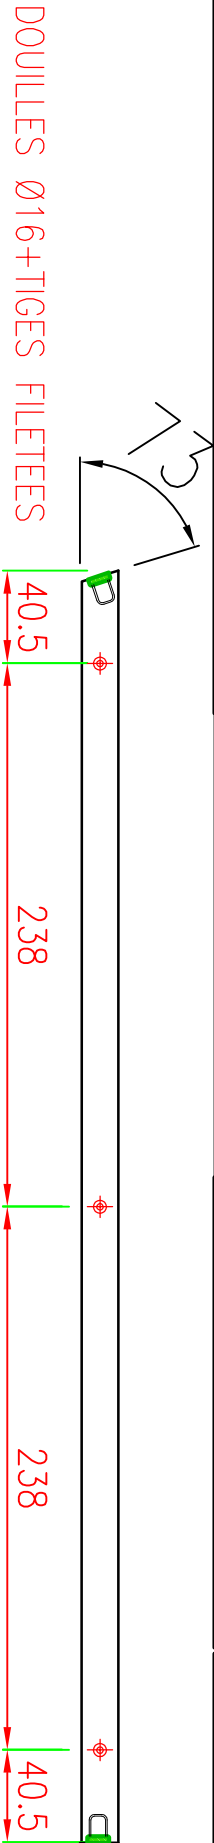

LEVAGE		INSERTS		INSERTS		INSERTS	
	Douille Ø		Ancre Frimeda T		EBA		TP - JV
	Douille Ø		Renfort Ø		Douille étalement		PVC Ø80
	Renfort Ø dx		Trifier		Ankrobox Ø50		Tube garde-corps
DATE: 16/11/2015		Plan N°		Indice		Page N°	

MOULE	N	NC	observations	CONTROLE	N	NC	observations	BETON	N	NC	observations	FICHE AUTO-CONTROLE
Conformité moule				Dimensions				Conformité béton				Opérateur :
Etat du moule				Armature				Mise en place				Responsable prod :
Propreté et huilage				Inserts				Aspect de surface				Date :

Ent. FONTANEL			Elément: BANDEAUX		FICHE DE FABRICATION			Surface: m²	POIDS	REPERE	Nbr
LE 180 - LA MULATIERE			coffrage		PLATTARD S.A.S.			Volume: 0.32 m3	0.76 T	5a	1

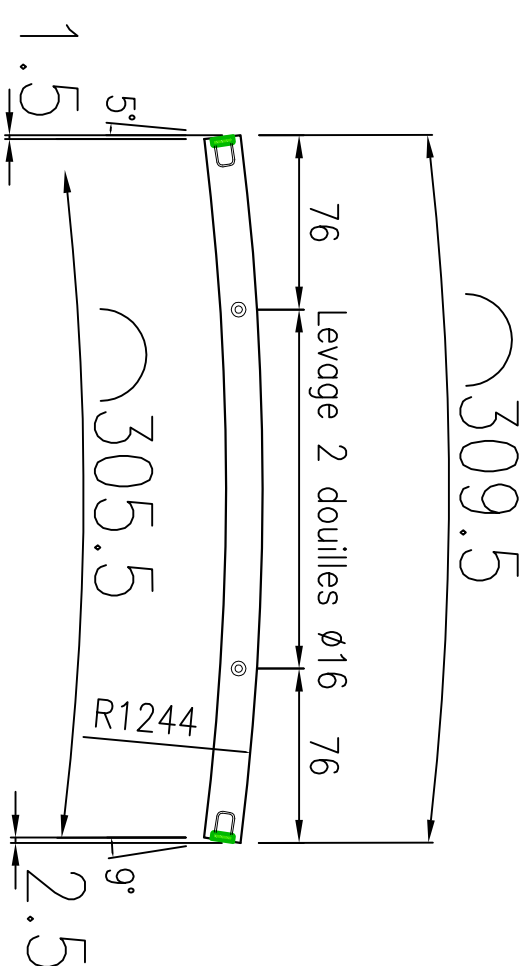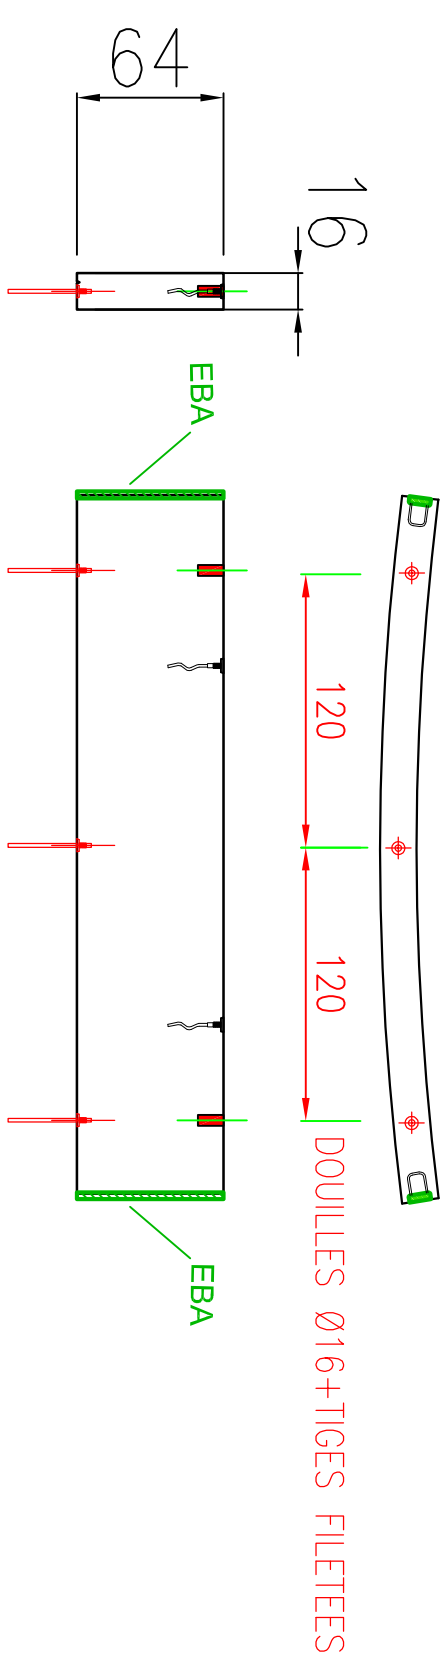

LEVAGE			INSERTS			INSERTS			INSERTS		
	Douille Ø			Ancre Frimeda T			EBA			TP - JV	DATE: 16/11/2015
	Douille Ø			Renfort Ø			Douille étalement			PVC Ø80	Plan N°
	Renfort Ø dx			Trifier			Ankrobox Ø50			Tube garde-corps	Indice

