

FONTANEL- LE 180°

69 LA MULATIERE

BALCONS DU NIVEAU N0
BAT A




EXE

Indice	Date	Designation des Modifications	Date :
A			01/02/2016
B			Affaire :
C			
D			Echelle :
E			
F			
G			
H			
I			

Type béton = B35 XF1
Aciers H.A et T.S = Fe E 500
Enrobage des armatures = ENR_CARMAT
Manutention = Tonnes

BUREAU D'ETUDE
PLATTARD SAS
414 Avenue de la
plage
BP 119
69540
Villefrance-sur-Saône
Tél: 04 74 02 20 20
Fax: 04 74 62 26 62

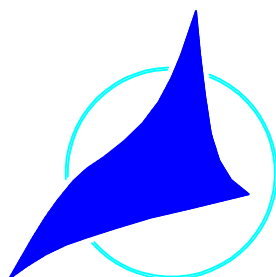

P L A T T A R D

Ce plan est la propriété intellectuelle de la PLATTARD SAS, il ne peut être reproduit sans son autorisation.

NOAHO
LE 180°
Chemin de Fontanière - 69350 La Mulatière
Création de logements

Les entreprises réalisant les travaux devront tenir compte des derniers plans architecte lors de la réalisation des travaux
Les plans du be MATTE ne doivent servir qu'au corps d'état concerné et doivent être des plans d'exécution.

ARCHITECTE(S): ATELIER DE LA PASSERELLE MO DELEGUE:
BET STRUCTURE: MATTE SAS MOE: PSO Ingénierie
BET FLUIDES: PRELEM CSPS: SUD EST COORDINATION
ECONOMISTE: EXECO OPC:
BUREAU DE CONTROLE: Bureau VERITAS ENTREPRISE(S): Fontanel

Bât:A
PLANCHER SUR REZ
Coffrage

EXE

Contrainte de sol: 8 bars ELS

INDICE	DATE	MODIFICATIONS

Aciers HA (T) FeE500
Aciers Doux (Ø) FeE 235
Aciers TS FeE 500
Béton fc28 >= 25MPa
Enrobage = 3 cm

PLAN N°
A40 0

DATE : 29/01/2016

MATTÉ
BUREAU D'ÉTUDES
STRUCTURES ET FLUIDES

119 BOULEVARD STALINGRAD 69100 VILLEURBANNE

Tél. 04 72 44 02 87 Fax 04 72 44 26 59

E-mail : bet@matte.fr


Dessiné par : J.BO

Contrôlé par : P.LIN

Echelle : 1/50°


Affaire N°
13.12.118

1

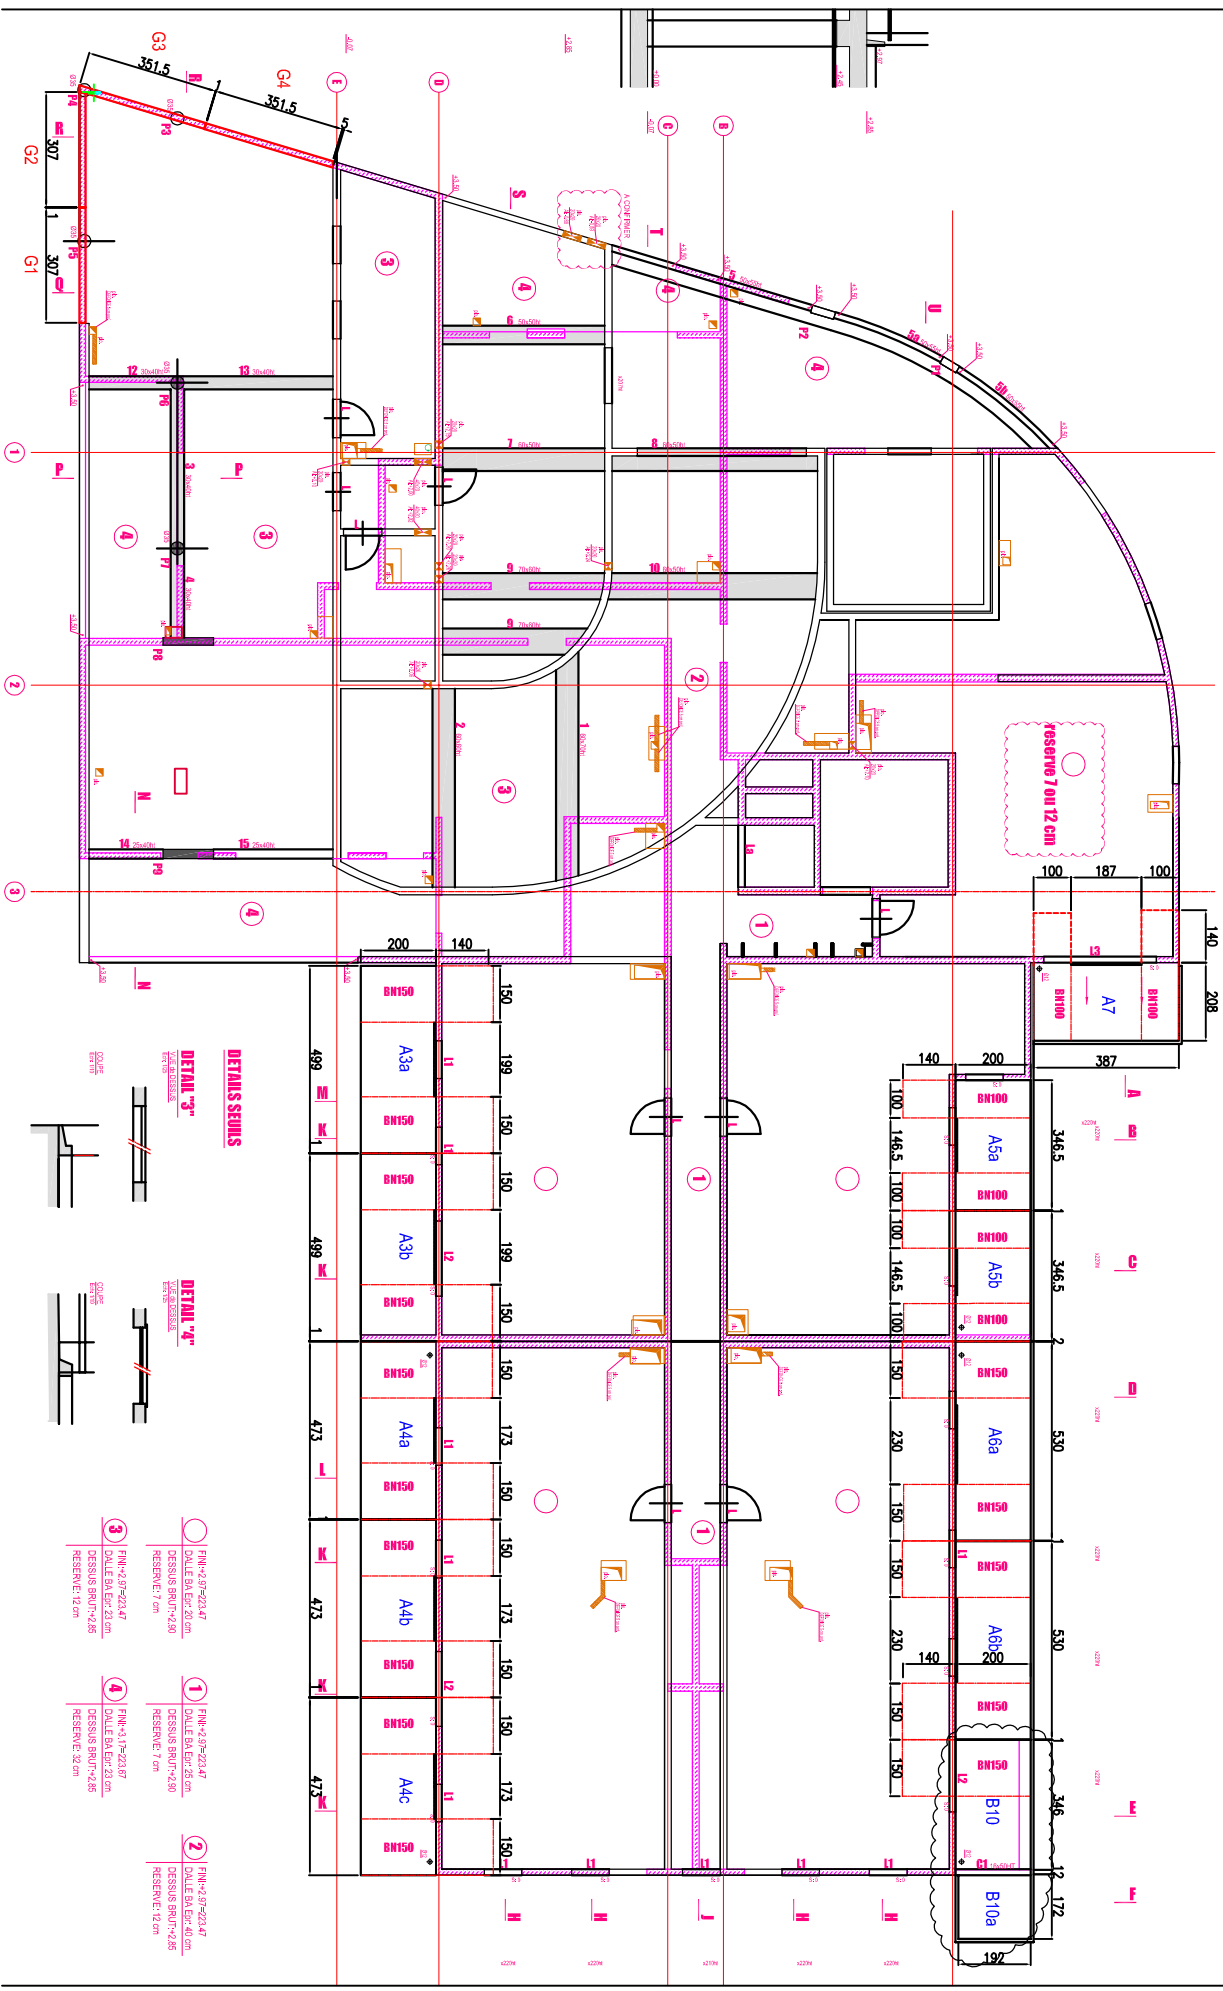

MOULE	N	NC	observations	CONTROLE	N	NC	observations	BETON	N	NC	observations	FICHE AUTO-CONTROLE
Conformité moule				Dimensions				Conformité béton				Opérateur :
Etat du moule				Armature				Mise en place				Responsable prod :
Propreté et huilage				Inserts				Aspect de surface				Date :


Ent. FONTANEL		Elément: BALCONS		 PLATTARD S.A.S. PLAN DE FABRCATION		Surface: 9.98 m²		POIDS		REPERE		Nbr	
LA MULATIERE		coffrage / ferrallage				Volume: 1.89 m3		4.55 T		A3a		1	

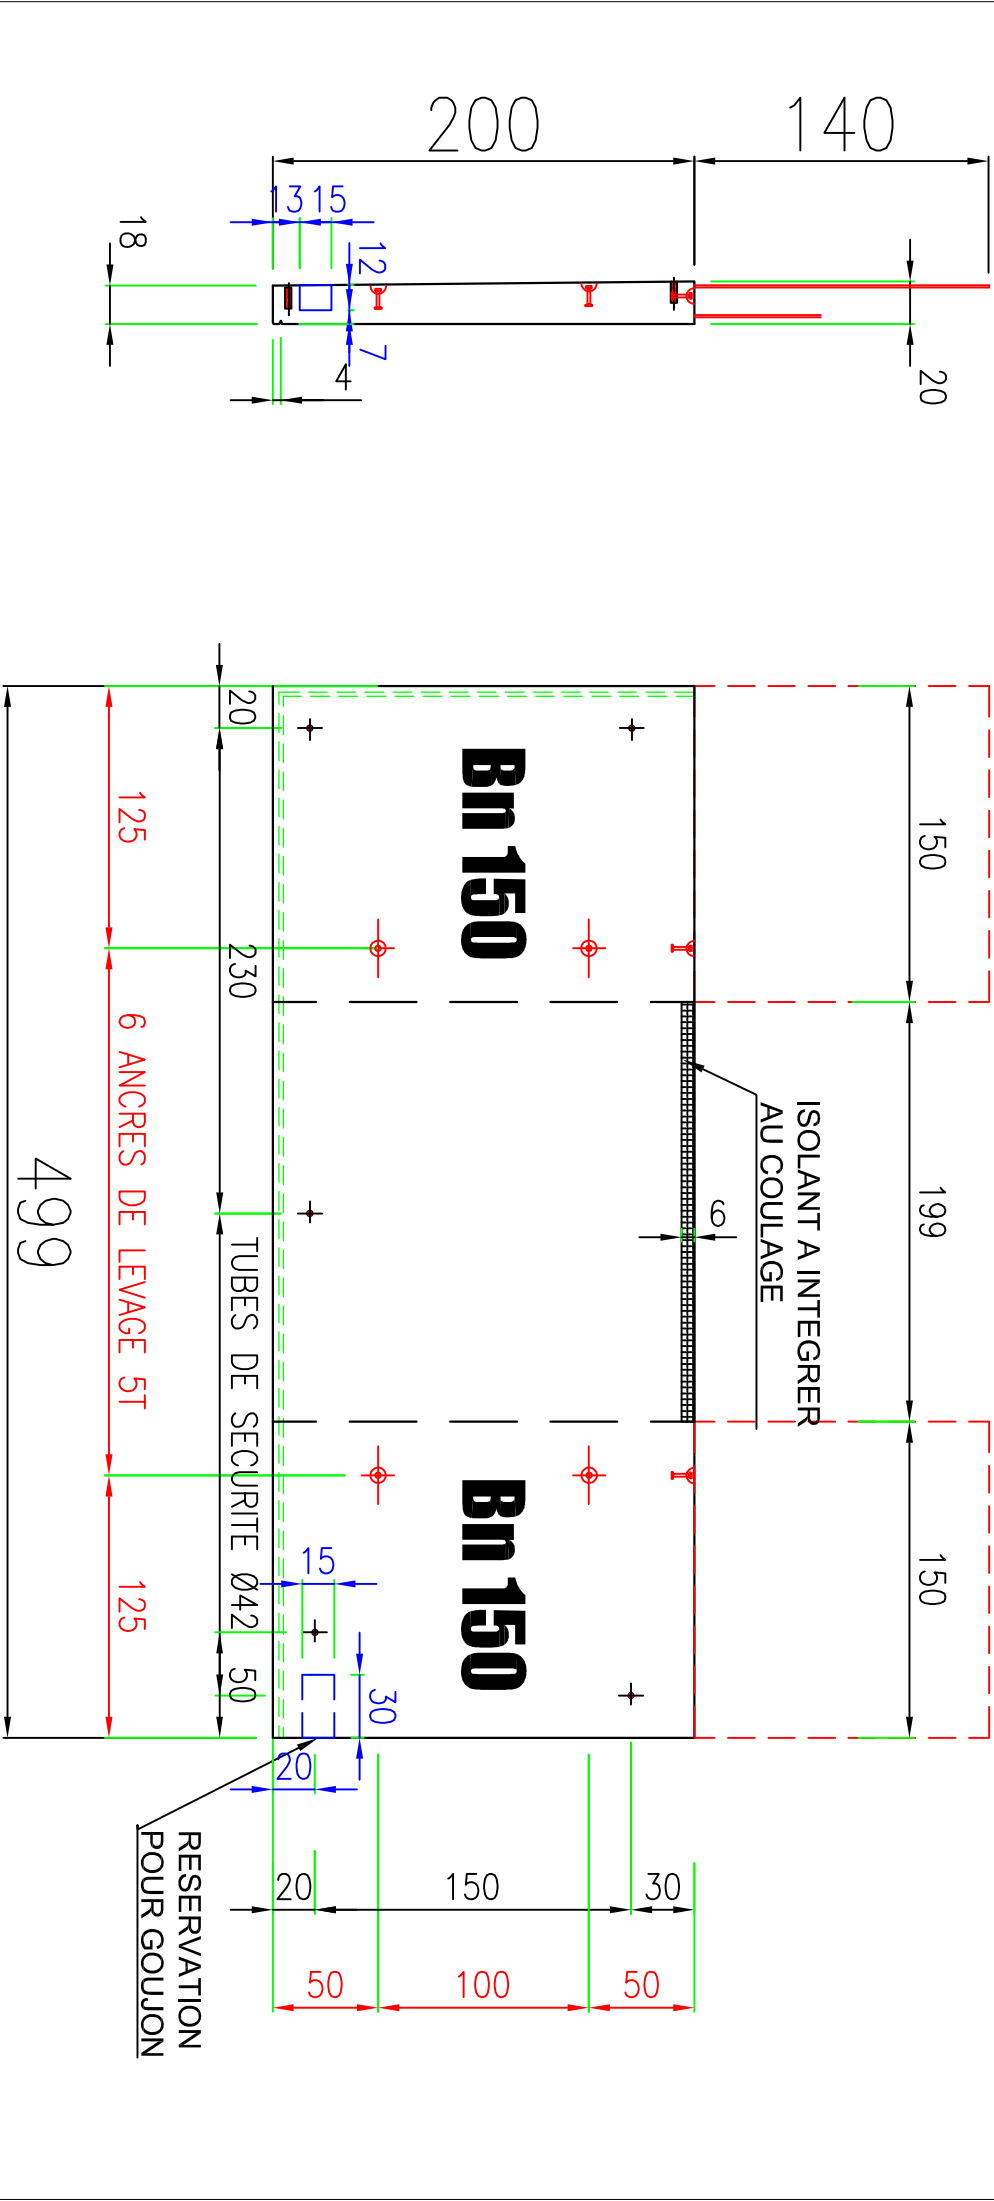

LEVAGE			INSERTS			INSERTS			INSERTS		
	Douille Ø			Ancre Frimeda T			EBA			TP - JV	DATE: 16/11/2015
	Douille Ø			Renfort Ø			Douille étalement			PVC Ø80	Plan N°
	Renfort Ø dx			Trifier			Ankrobox Ø50			Tube garde-corps	Indice

MOULE	N	NC	observations	CONTROLE	N	NC	observations	BETON	N	NC	observations	FICHE AUTO-CONTROLE
Conformité moule				Dimensions				Conformité béton				Opérateur :
Etat du moule				Armature				Mise en place				Responsable prod :
Propreté et huilage				Inserts				Aspect de surface				Date :


Ent. FONTANEL			Elément: BALCONS			PLAN DE FABRCATION			Surface:	9.98 m²	POIDS	REPERE	Nbr
LA MULATIERE			coffrage / ferrailage			PLATTARD S.A.S.			Volume:	1.89 m3	4.55 T	A3b 1	

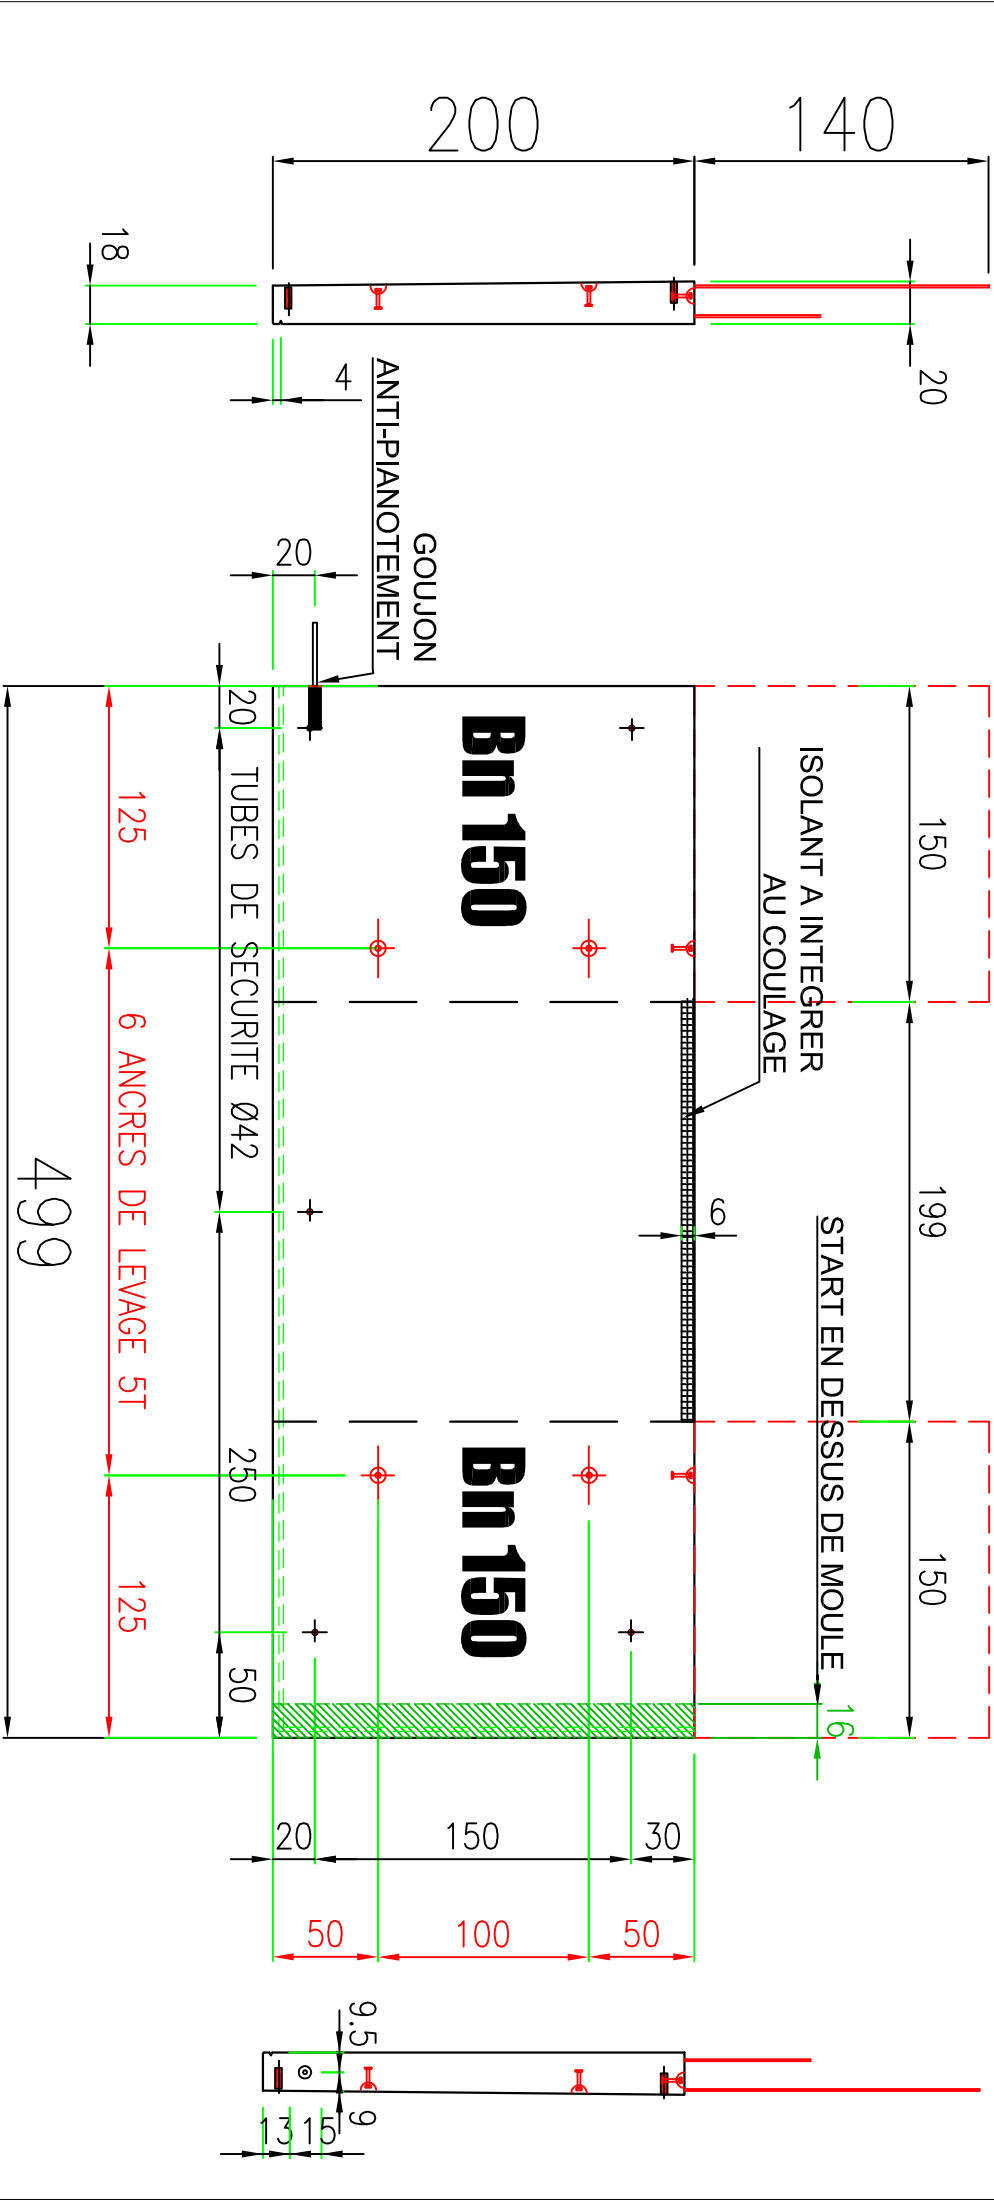

LEVAGE		INSERTS		INSERTS		INSERTS		DATE: 16/11/2015	
	Douille Ø		Ancre Frimeda T		EBA		TP - JV	Plan N°	
	Douille Ø		Renfort Ø		Douille étalement		PVC Ø80	Page N°	
	Renfort Ø dx		Trifier		Ankrobox Ø50		Tube garde-corps	Indice	

MOULE	N	NC	observations	CONTROLE	N	NC	observations	BETON	N	NC	observations	FICHE AUTO-CONTROLE
Conformité moule				Dimensions				Conformité béton				Opérateur :
Etat du moule				Armature				Mise en place				Responsable prod :
Propreté et huilage				Inserts				Aspect de surface				Date :



Ent. FONTANEL		Elément: BALCONS		 PLAN DE FABRCATION		Surface: 9.46 m²	POIDS	REPERE	Nbr
LA MULATIERE		coffrage / ferrailage				Volume: 1.80 m3	4.31 T	A4a	1

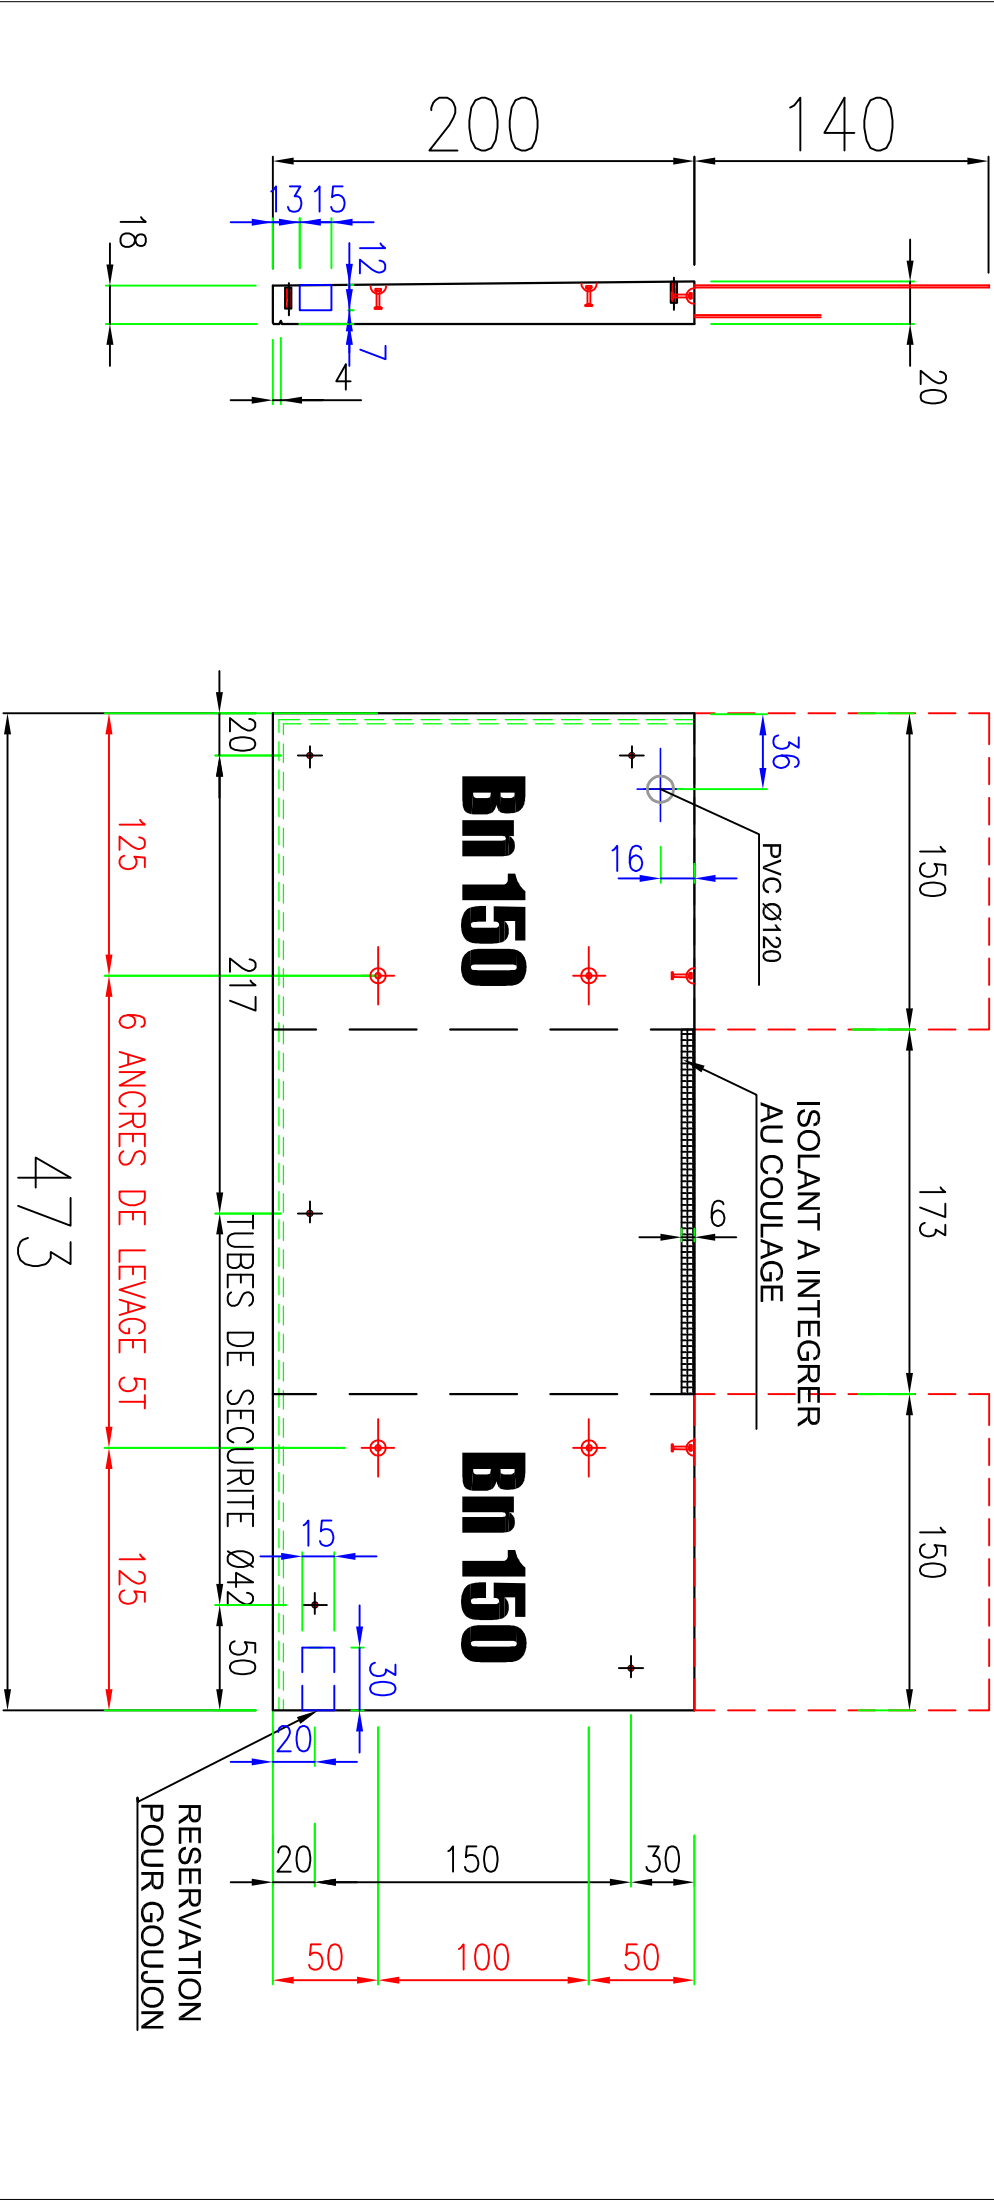

LEVAGE		INSERTS		INSERTS		INSERTS	
	Douille Ø		Ancre Frimeda T		EBA		TP - JV
	Douille Ø		Renfort Ø		Douille étalement		PVC Ø80
	Renfort Ø dx	Λ	Trifier		Ankrobox Ø50		Tube garde-corps
DATE: 16/11/2015		Plan N°		Indice		Page N°	

MOULE	N	NC	observations	CONTROLE	N	NC	observations	BETON	N	NC	observations	FICHE AUTO-CONTROLE
Conformité moule				Dimensions				Conformité béton				Opérateur :
Etat du moule				Armature				Mise en place				Responsable prod :
Propreté et huilage				Inserts				Aspect de surface				Date :


Ent. FONTANEL				 PLATTARD S.A.S.											
LA MULATIERE		Elément: BALCONS				coffrage / ferrillage		PLAN DE FABRCATION							
						Surface: 6.93 m²		POIDS		REPERE		Nbr			
								Volume: 1.32 m3		3.16 T		A5a		1	

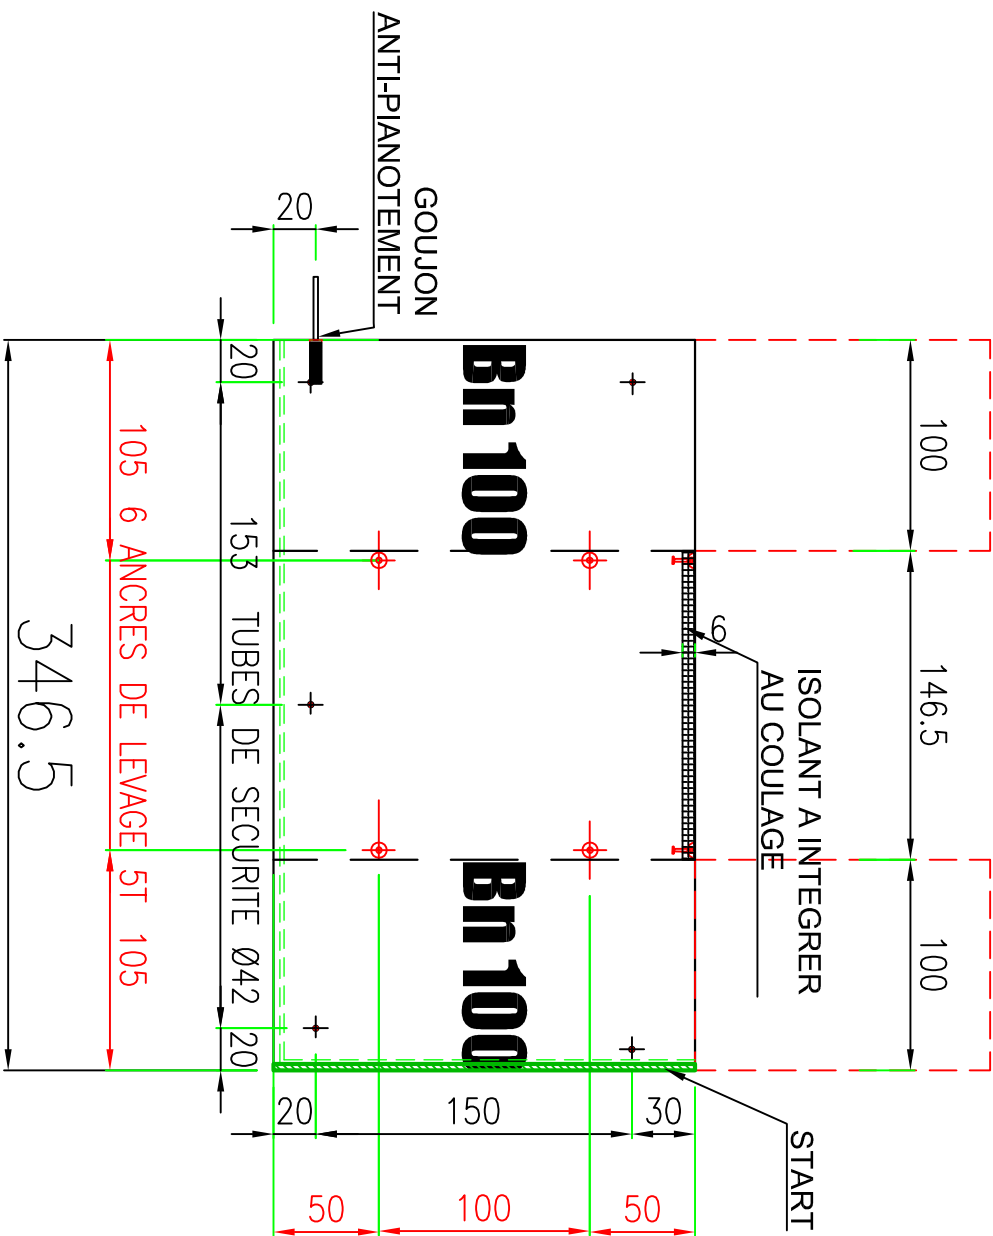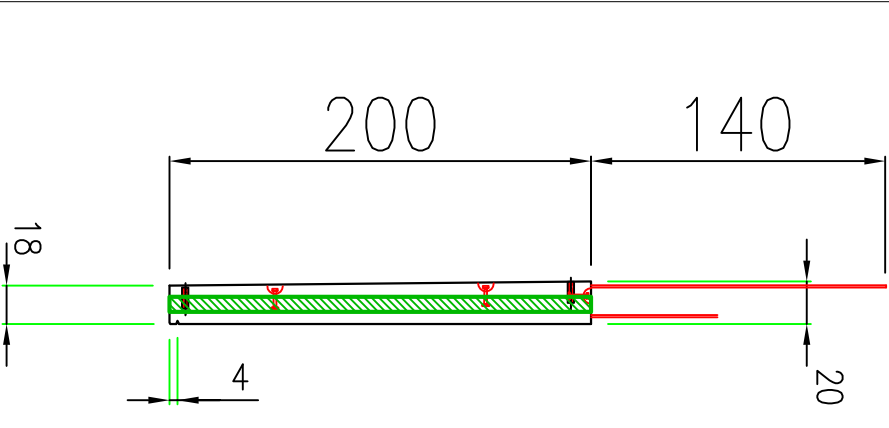

LEVAGE			INSERTS			INSERTS			INSERTS			INSERTS		
	Douille Ø			Ancre Frimeda T			EBA			TP - JV	DATE: 16/11/2015		Douille Ø	
	Douille Ø			Renfort Ø			Douille étalement			PVC Ø80	Plan N°		Renfort Ø	
	Renfort Ø dx			Trifier			Ankrobox Ø50			Tube garde-corps	Indice		Renfort Ø	

MOULE	N	NC	observations	CONTROLE	N	NC	observations	BETON	N	NC	observations	FICHE AUTO-CONTROLE
Conformité moule				Dimensions				Conformité béton				Opérateur :
Etat du moule				Armature				Mise en place				Responsable prod :
Propreté et huilage				Inserts				Aspect de surface				Date :


Ent. FONTANEL		Elément: BALCONS		 PLATTARD S.A.S. PLAN DE FABRCATION		Surface: 10.60 m²		POIDS		REPERE		Nbr	
LA MULATIERE		coffrage / ferrillage				Volume: 2.01 m3		4.84 T		A6a		1	

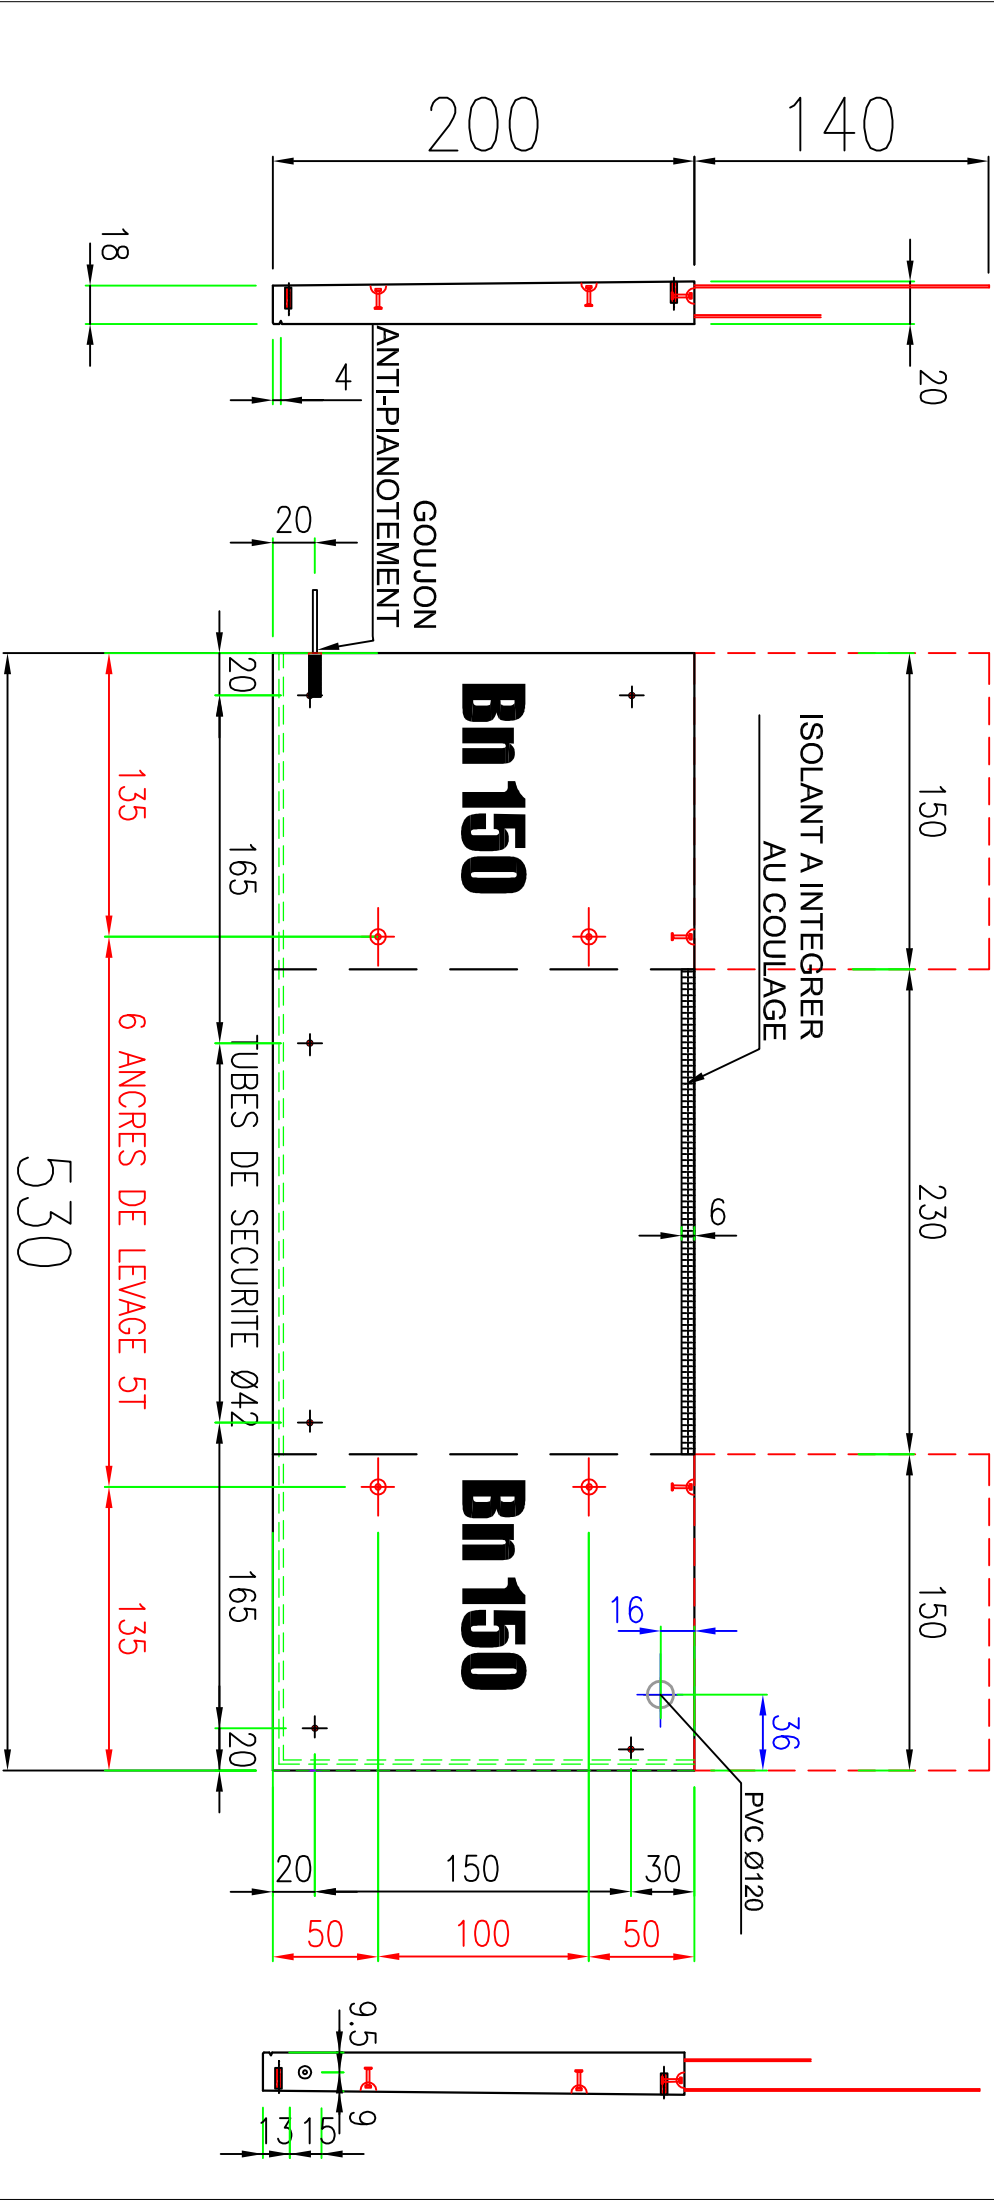

LEVAGE			INSERTS			INSERTS			INSERTS		
	Douille Ø			Ancre Frimeda T			EBA			TP - JV	DATE: 16/11/2015
	Douille Ø			Renfort Ø			Douille étalement			PVC Ø80	Plan N°
	Renfort Ø dx			Trifier			Ankrobox Ø50			Tube garde-corps	Indice

MOULE	N	NC	observations	CONTROLE	N	NC	observations	BETON	N	NC	observations	FICHE AUTO-CONTROLE
Conformité moule				Dimensions				Conformité béton				Opérateur :
Etat du moule				Armature				Mise en place				Responsable prod :
Propreté et huilage				Inserts				Aspect de surface				Date :

Ent. FONTANEL		Elément: BALCONS		 PLATTARD S.A.S. PLAN DE FABRCATION		Surface: 3.30 m²		POIDS		REPERE		Nbr	
LA MULATIERE		coffrage / ferrailage				Volume: 0.62 m3		1.50 T		B10A		1	

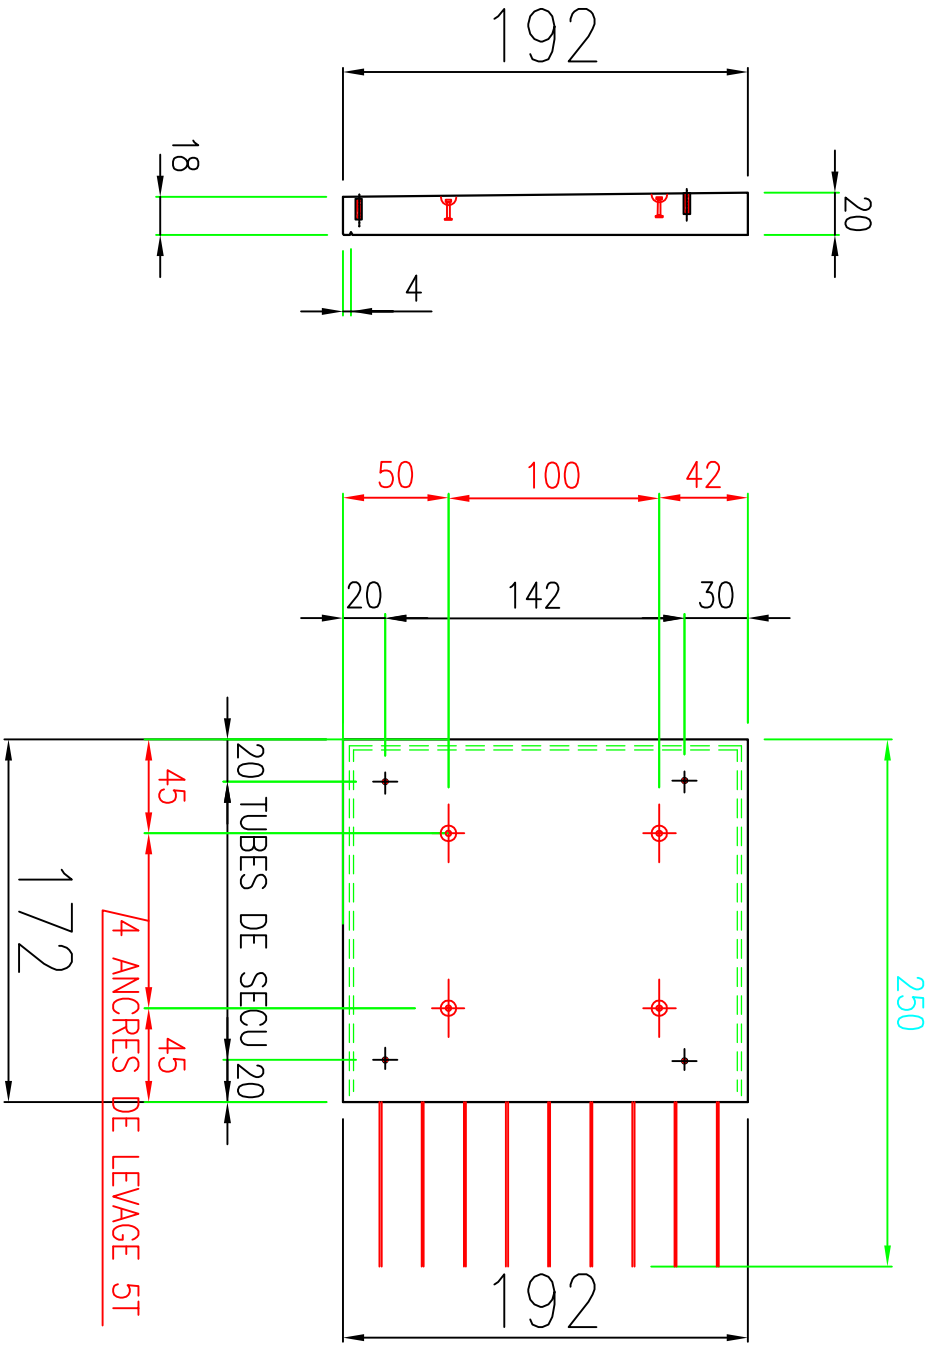

LEVAGE				INSERTS				INSERTS				INSERTS			
	Douille Ø				Ancre Frimeda T				EBA				TP - JV		DATE: 16/11/2015
	Douille Ø				Renfort Ø				Douille étalement				PVC Ø80		Plan N°
	Renfort Ø dx				Trifier				Ankrobox Ø50				Tube garde-corps		Indice


Page N°				Page N°			
---------	--	--	--	---------	--	--	--

FONTANEL

LE 180 - LA MULATIERE



10		86
	•	Cadres HA6 e=20
	•	2 Filants HA10
	◦	14 Filants HA8
60		11
		Attentes Ø8dx e=15

SECTION A CONFIRMER

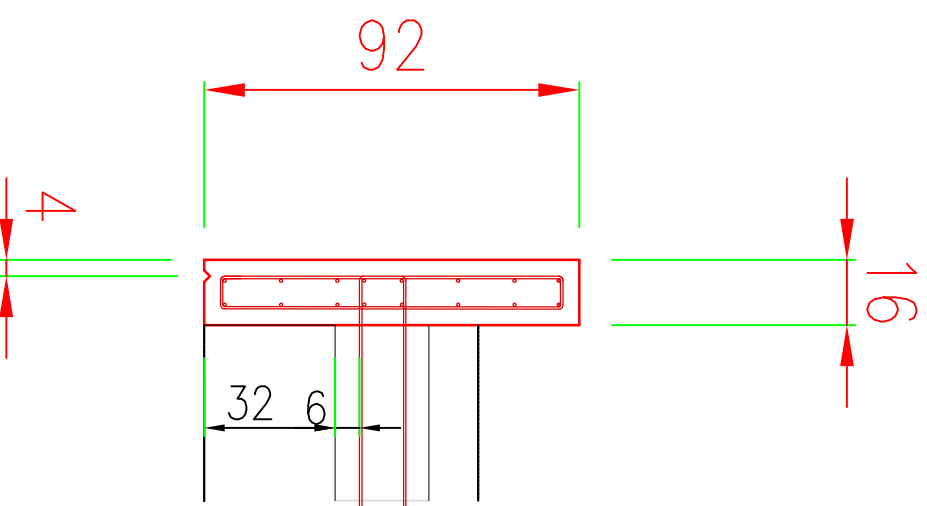

MOULE	N	NC	observations	CONTROLE	N	NC	observations	BETON	N	NC	observations	FICHE AUTO-CONTROLE
Conformité moule				Dimensions				Conformité béton				Opérateur :
Etat du moule				Armature				Mise en place				Responsable prod :
Propreté et huilage				Inserts				Aspect de surface				Date :




Ent. FONTANEL				 PLATTARD S.A.S.				REPERE		Nbr
Elément: BANDEAUX						FICHE DE FABRICATION		G1		1
LE 180 - LA MULATIERE		coffrage				Surface: 2.82 m²		POIDS		
						Volume: 0.45 m3		1.09 T		

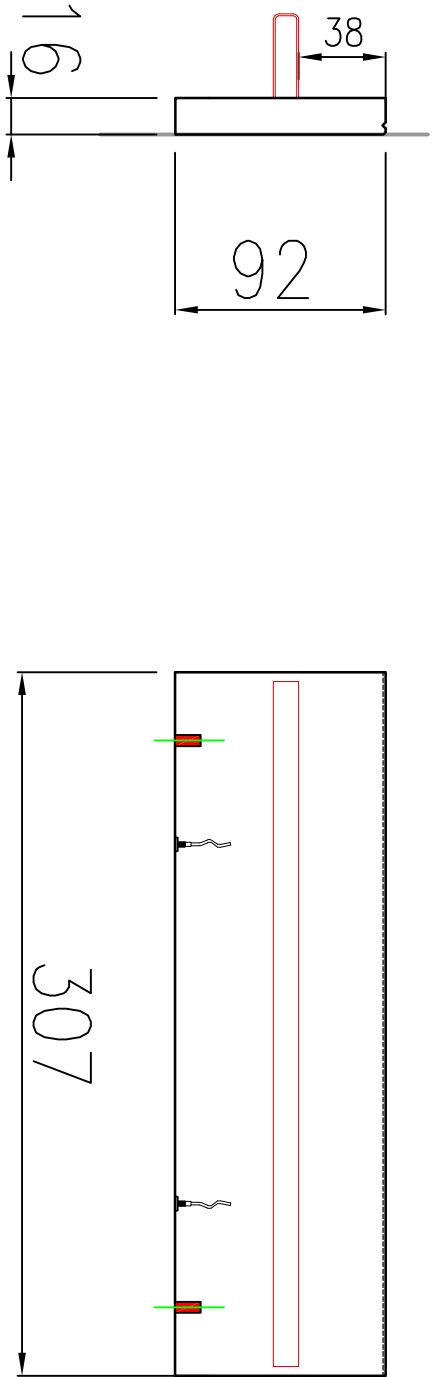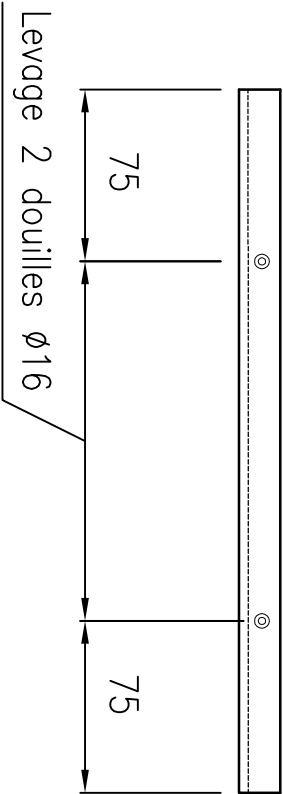

LEVAGE										INSERTS										INSERTS										INSERTS	
					Douille Ø										Ancre Frimeda T										EBA										TP - JV					DATE: 16/11/2015	
					Douille Ø										Renfort Ø										Douille étalement										PVC Ø80					Plan N°					Page N°	
					Renfort Ø dx										Trifler										Ankrobox Ø50										Tube garde-corps					Indice	

MOULE	N	NC	observations	CONTROLE	N	NC	observations	BETON	N	NC	observations	FICHE AUTO-CONTROLE
Conformité moule				Dimensions				Conformité béton				Opérateur :
Etat du moule				Armature				Mise en place				Responsable prod :
Propreté et huilage				Inserts				Aspect de surface				Date :




Ent. FONTANEL				 PLATTARD S.A.S.									
Elément: BANDEAUX						FICHE DE FABRICATION							
LE 180 - LA MULATIERE		coffrage		Surface: 2.82		m²		POIDS		REPERE		Nbr	
				Volume: 0.45		m3		1.09 T		G2		1	

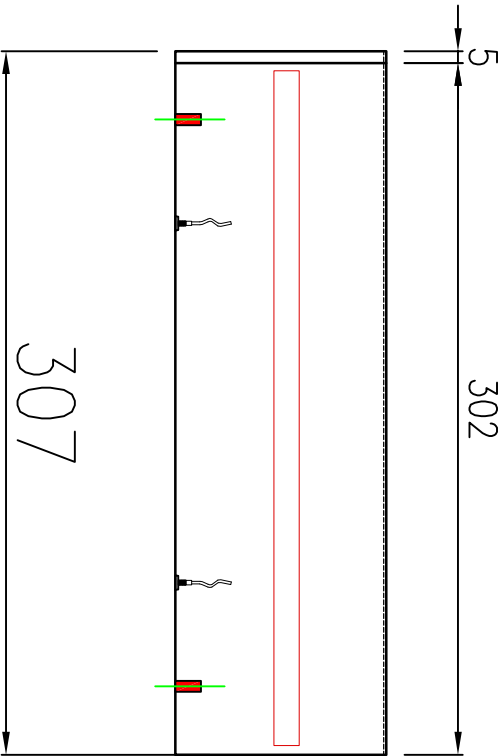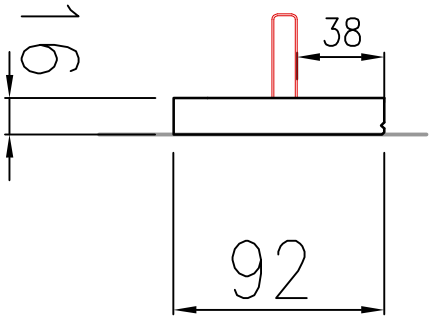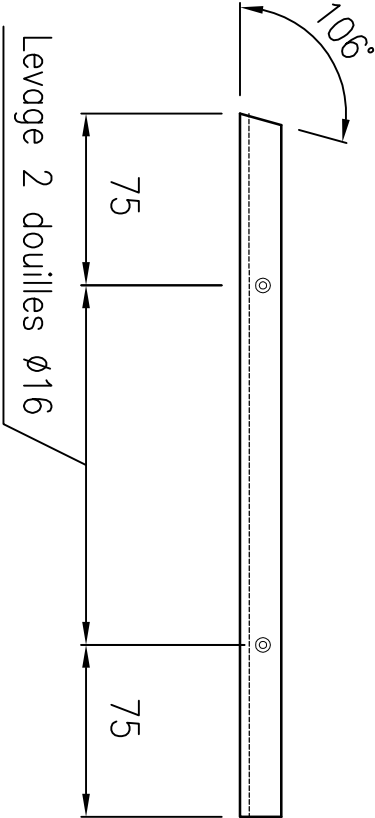

LEVAGE				INSERTS				INSERTS				INSERTS			
	Douille Ø				Ancre Frimeda T				EBA				TP - JV		DATE: 16/11/2015
	Douille Ø				Renfort Ø				Douille étalement				PVC Ø80		Plan N°
	Renfort Ø	dx			Trifier				Ankrobox Ø50				Tube garde-corps		Indice

MOULE	N	NC	observations	CONTROLE	N	NC	observations	BETON	N	NC	observations	FICHE AUTO-CONTROLE
Conformité moule				Dimensions				Conformité béton				Opérateur :
Etat du moule				Armature				Mise en place				Responsable prod :
Propreté et huilage				Inserts				Aspect de surface				Date :


Ent. FONTANEL			Elément: BANDEAUX		FICHE DE FABRICATION			Surface: 3.23	m²	POIDS	REPERE	Nbr
LE 180 - LA MULATIERE			coffrage		Plattard S.A.S.			Volume: 0.52	m3	1.24 T	G3	1

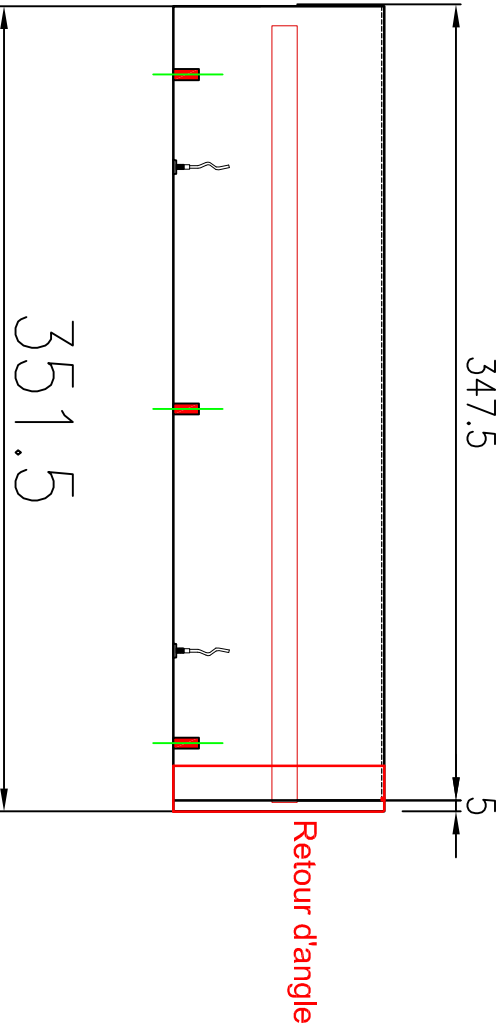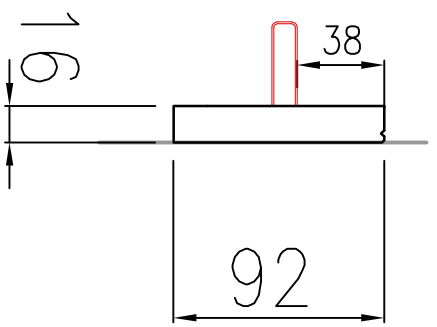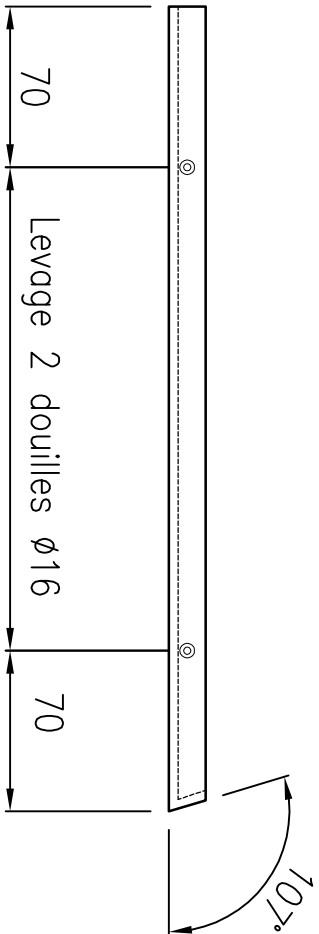

LEVAGE			INSERTS			INSERTS			INSERTS			DATE: 16/11/2015		
	Douille Ø			Ancre Frimeda T			EBA			TP - JV		Page N°		
	Douille Ø			Renfort Ø			Douille étalement			PVC Ø80		Page N°		
	Renfort Ø dx			Trifier			Ankrobox Ø50			Tube garde-corps		Indice		

MOULE	N	NC	observations	CONTROLE	N	NC	observations	BETON	N	NC	observations	FICHE AUTO-CONTROLE
Conformité moule				Dimensions				Conformité béton				Opérateur :
Etat du moule				Armature				Mise en place				Responsable prod :
Propreté et huilage				Inserts				Aspect de surface				Date :

Ent. FONTANEL				 PLATTARD S.A.S.		FICHE DE FABRICATION				REPERE		Nbr
Elément: BANDEAUX						Surface: 3.23 m²		POIDS				
LE 180 - LA MULATIERE		coffrage				Volume: 0.52 m3		1.24 T		G4		1

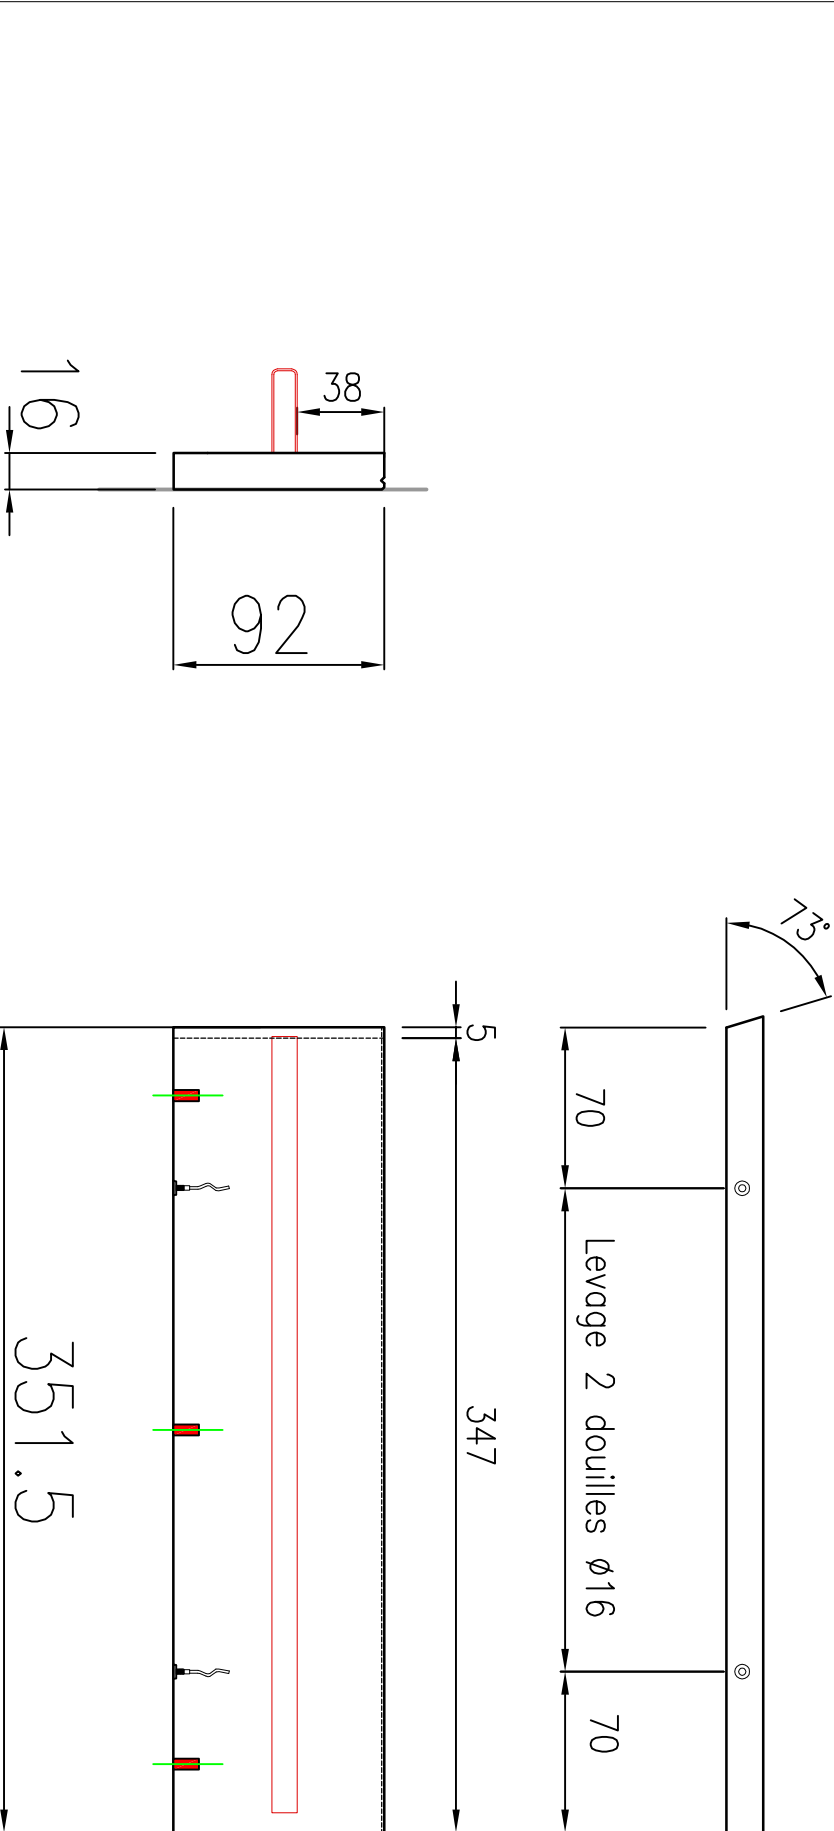

LEVAGE				INSERTS				INSERTS				INSERTS			
	Douille Ø				Ancre Frimeda T				EBA				TP - JV		DATE: 16/11/2015
	Douille Ø				Renfort Ø				Douille étalement				PVC Ø80		Plan N°
	Renfort Ø	dx			Trifier				Ankrobox Ø50				Tube garde-corps	Indice	Page N°