



MOULE	N	NC	observations	CONTROLE	N	NC	observations	BETON	N	NC	observations	FICHE AUTO-CONTROLE
Conformité moule				Dimensions				Conformité béton				Opérateur :
Etat du moule				Armature				Mise en place				Responsable prod :
Propreté et huilage				Inserts				Aspect de surface				Date :

Ent. FONTANEL			Elément: BANDEAUX		FICHE DE FABRICATION			Surface:	m²	POIDS	REPERE	Nbr
LE 180 - LA MULATIERE			coffrage		PLATTARD S.A.S.			Volume:	0.13 m3	0.310 T	S3	1

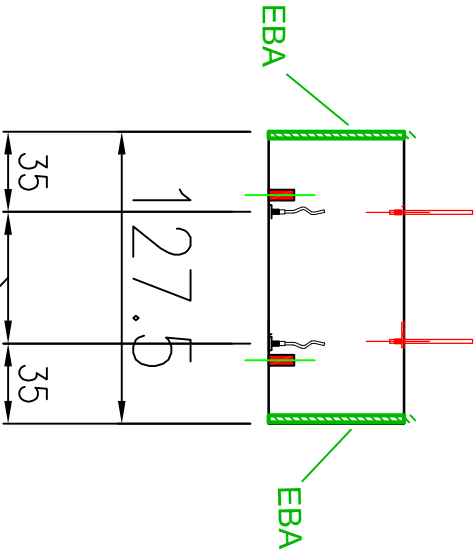

DOUILLES Ø16+TIGES FILETEES

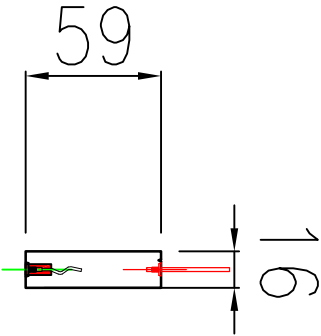

Levage 2 douilles Ø16

LEVAGE			INSERTS			INSERTS			INSERTS		
	Douille Ø			Ancre Frimeda T			EBA			TP - JV	DATE: 16/11/2015
	Douille Ø			Renfort Ø			Douille étalement			PVC Ø80	Plan N°
	Renfort Ø dx			Trifier			Ankrobox Ø50			Tube garde-corps	Indice



MOULE	N	NC	observations	CONTROLE	N	NC	observations	BETON	N	NC	observations	FICHE AUTO-CONTROLE
Conformité moule				Dimensions				Conformité béton				Opérateur :
Etat du moule				Armature				Mise en place				Responsable prod :
Propreté et huilage				Inserts				Aspect de surface				Date :

Ent. FONTANEL

LE 180 - LA MULATIERE

Elément: BANDEAUX	coffrage		FICHE DE FABRICATION	Surface:	m²	POIDS	REPÈRE	Nbr
				Volume:	0.310 m3	0.740 T	S5	1

DOUILLES Ø16+TIGES FILETEES

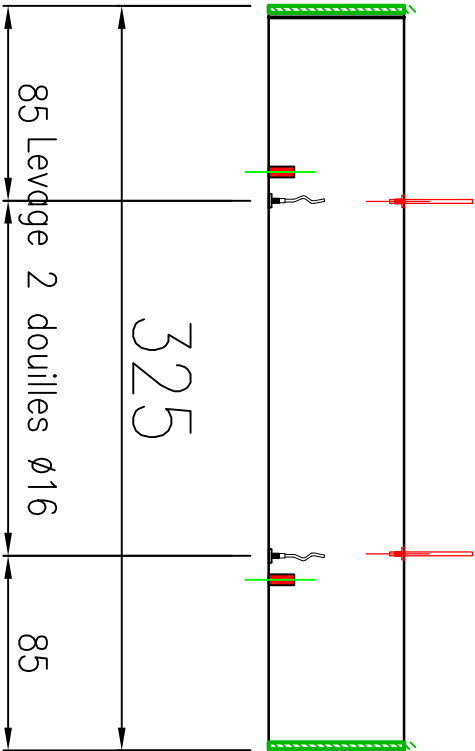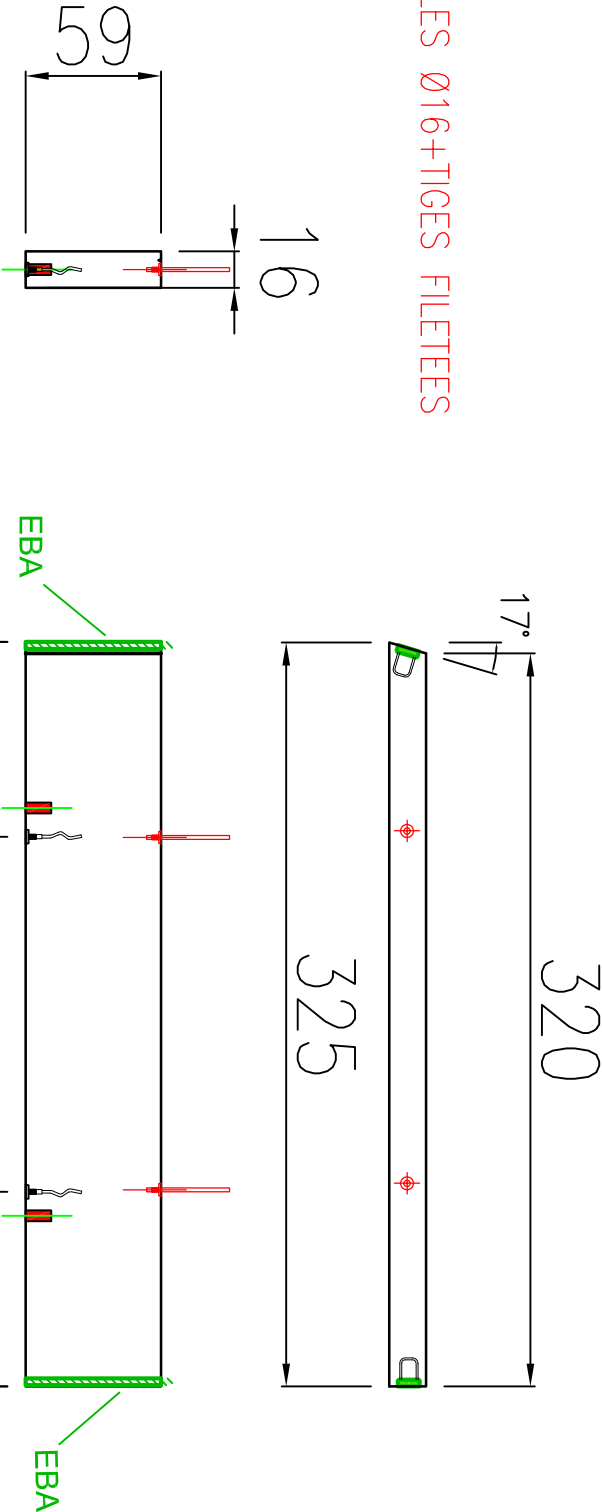

LEVAGE

	Douille Ø		Ancre Frimeda T		EBA		TP - JV	DATE: 16/11/2015
	Douille Ø		Renfort Ø		Douille étalement		PVC Ø80	Plan N°
	Renfort Ø dx		Trifier		Ankrobox Ø50		Tube garde-corps	Indice
INSERTS				INSERTS				Page N°
INSERTS				INSERTS				Page N°