

FONTANEL- LE 180°

69 LA MULATIERE


BALCONS DU NIVEAU N-2

N°

EXE

Indice	Date	Designation des Modifications	Date :
A			22/05/15
B			
C			
D			Affaire :
E			
F			Echelle :
G			
H			
I			

Type béton = B35 XF1
Aciers H.A et T.S = Fe E 500
Enrobage des armatures = ENR_{CA}ARMAT
Manutention = Tonnes

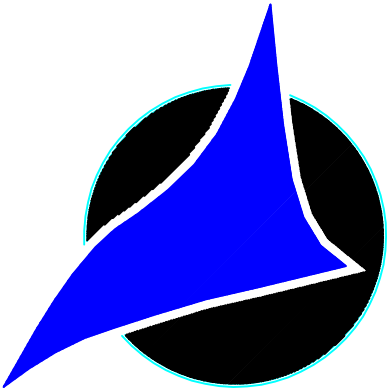

P L A T T A R D



BUREAU D'ETUDE
PLATTARD SAS
414 Avenue de la
plage
BP 119
69540
Villefrance-sur-Saône
Tél: 04 74 02 20 20
Fax: 04 74 62 26 62

Ce plan est la propriété intellectuelle de la PLATTARD SAS, il ne peut être reproduit sans son autorisation.

NOAHO

Chemin de Fontanière - 69350 La Mulatière

Création de logements

Les entreprises réalisant les travaux devront tenir compte des derniers plans architecte lors de la réalisation des travaux
Les plans du be MATTE ne doivent servir qu'au corps d'état concerné et doivent être des plans d'exécution.

ARCHITECTE(S): ATELIER DE LA PASSERELLE

MO DELEGUE:

BET STRUCTURE: MATTE SAS

MOE: PSO Ingénierie

BET FLUIDES: PRELEM

CSPS: SUD EST COORDINATION

ECONOMISTE: EXECO

OPC:

BUREAU DE CONTROLE: Bureau VERITAS

ENTREPRISE(S): Fontanel-pbc

Bât: A
PLANCHER sur -2 entre files 1 et 9
Coffrage

EXE

Contrainte de sol: 8 bars ELS

INDICE	DATE	MODIFICATIONS
A		
B		
C		

Aciers HA (T) FeE500

Aciers Doux (Ø) FeE 235

Aciers TS FeE 500

Béton fc28 >= 25MPa

Enrobage = 3 cm

PLAN N°
A32 0

DATE : 17/12/2015

MATTÉ
BUREAU D'ÉTUDES
STRUCTURES ET FLUIDES

119 BOULEVARD STALINGRAD 69100 VILLEURBANNE

Tél. 04 72 44 02 87 Fax 04 72 44 26 59

E-mail : bet@matte.fr

Dessiné par : J.BO

Contrôlé par : P.LIN



Echelle : 1/50°

Affaire N°
13.12.119



MOULE	N	NC	observations	BETON	N	NC	observations	FICHE AUTO-CONTROLE
Conformité moule			Dimensions	Conformité béton				Opérateur :
Etat du moule			Armature	Mise en place				Responsable prod :
Propreté et huilage			Inserts	Aspect de surface				Date :


Ent. FONTANEL		Elément: BALCONS		PLAN DE FABRCATION		Surface: 9.03 m²	POIDS	REPERE	Nbr
LA MULATIERE		coffrage / ferrailage		PLATTARD S.A.S.		Volume: 1.71 m3	4.11 T	A27	

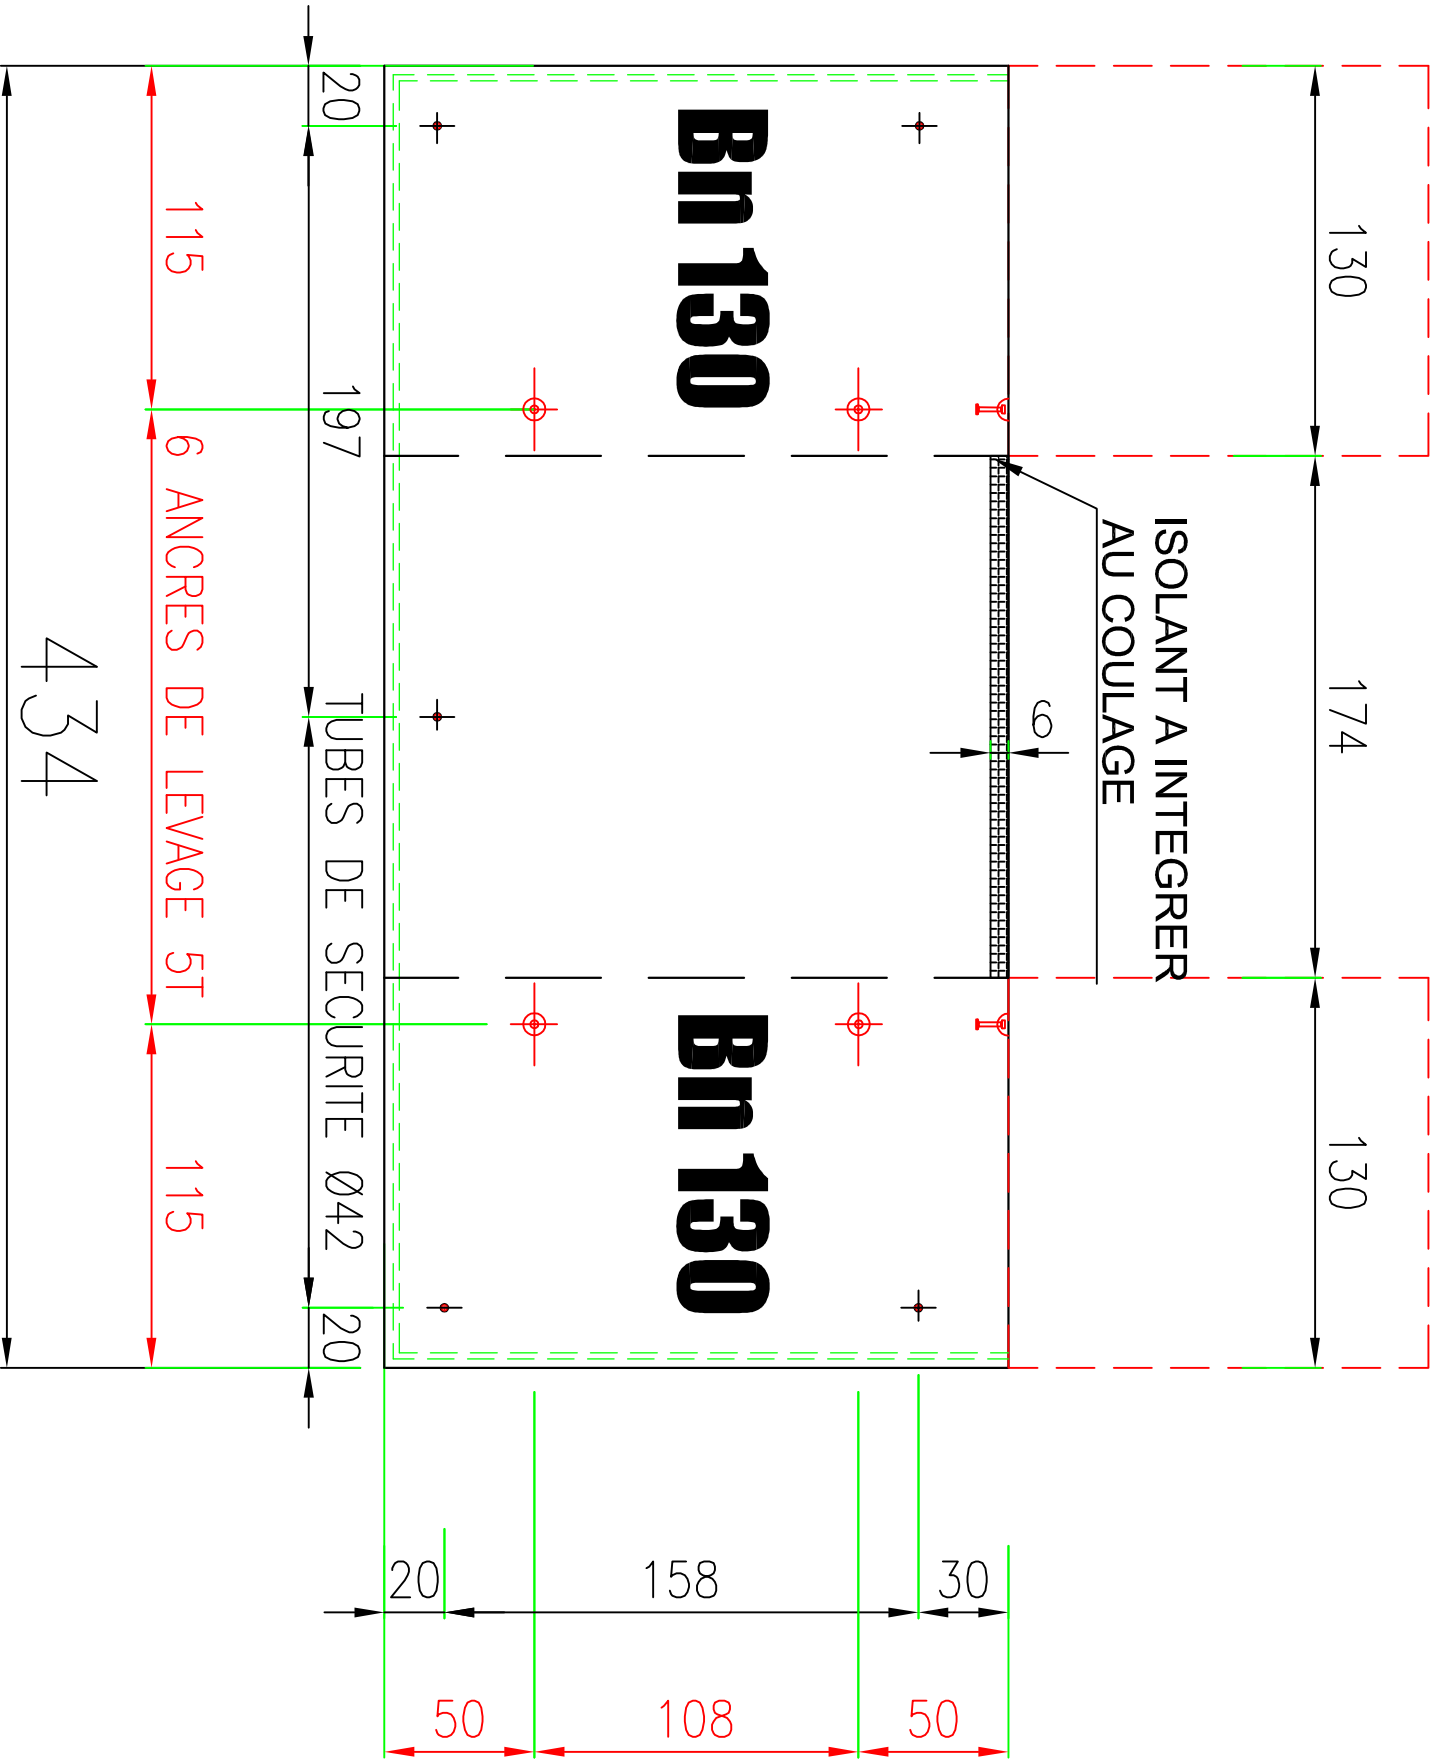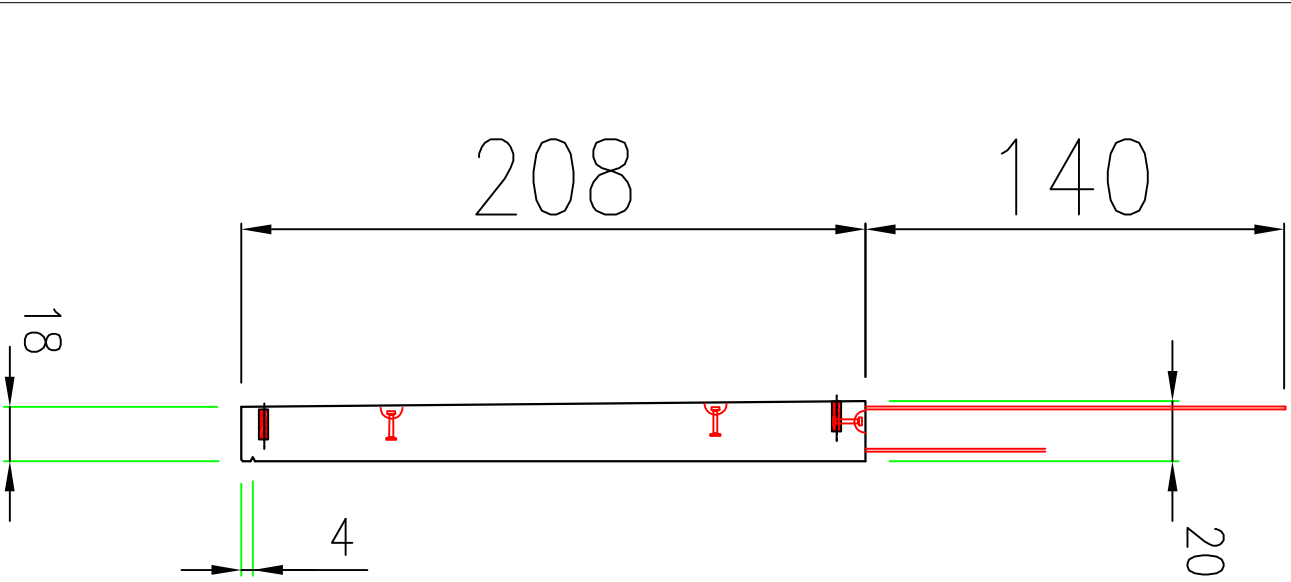

LEVAGE		INSERTS		INSERTS		INSERTS		INSERTS	
	Douille Ø		Ancre Frimeda T		EBA		TP - JV	DATE: 22/12/2015	
	Douille Ø		Renfort Ø		Douille étaieement		PVC Ø80	Plan N°	
	Renfort Ø dx		Trifer		Ankrobox Ø50		Tube garde-corps	Indice	
								Page N°	


Plancher Niveau R-2

BAT. B

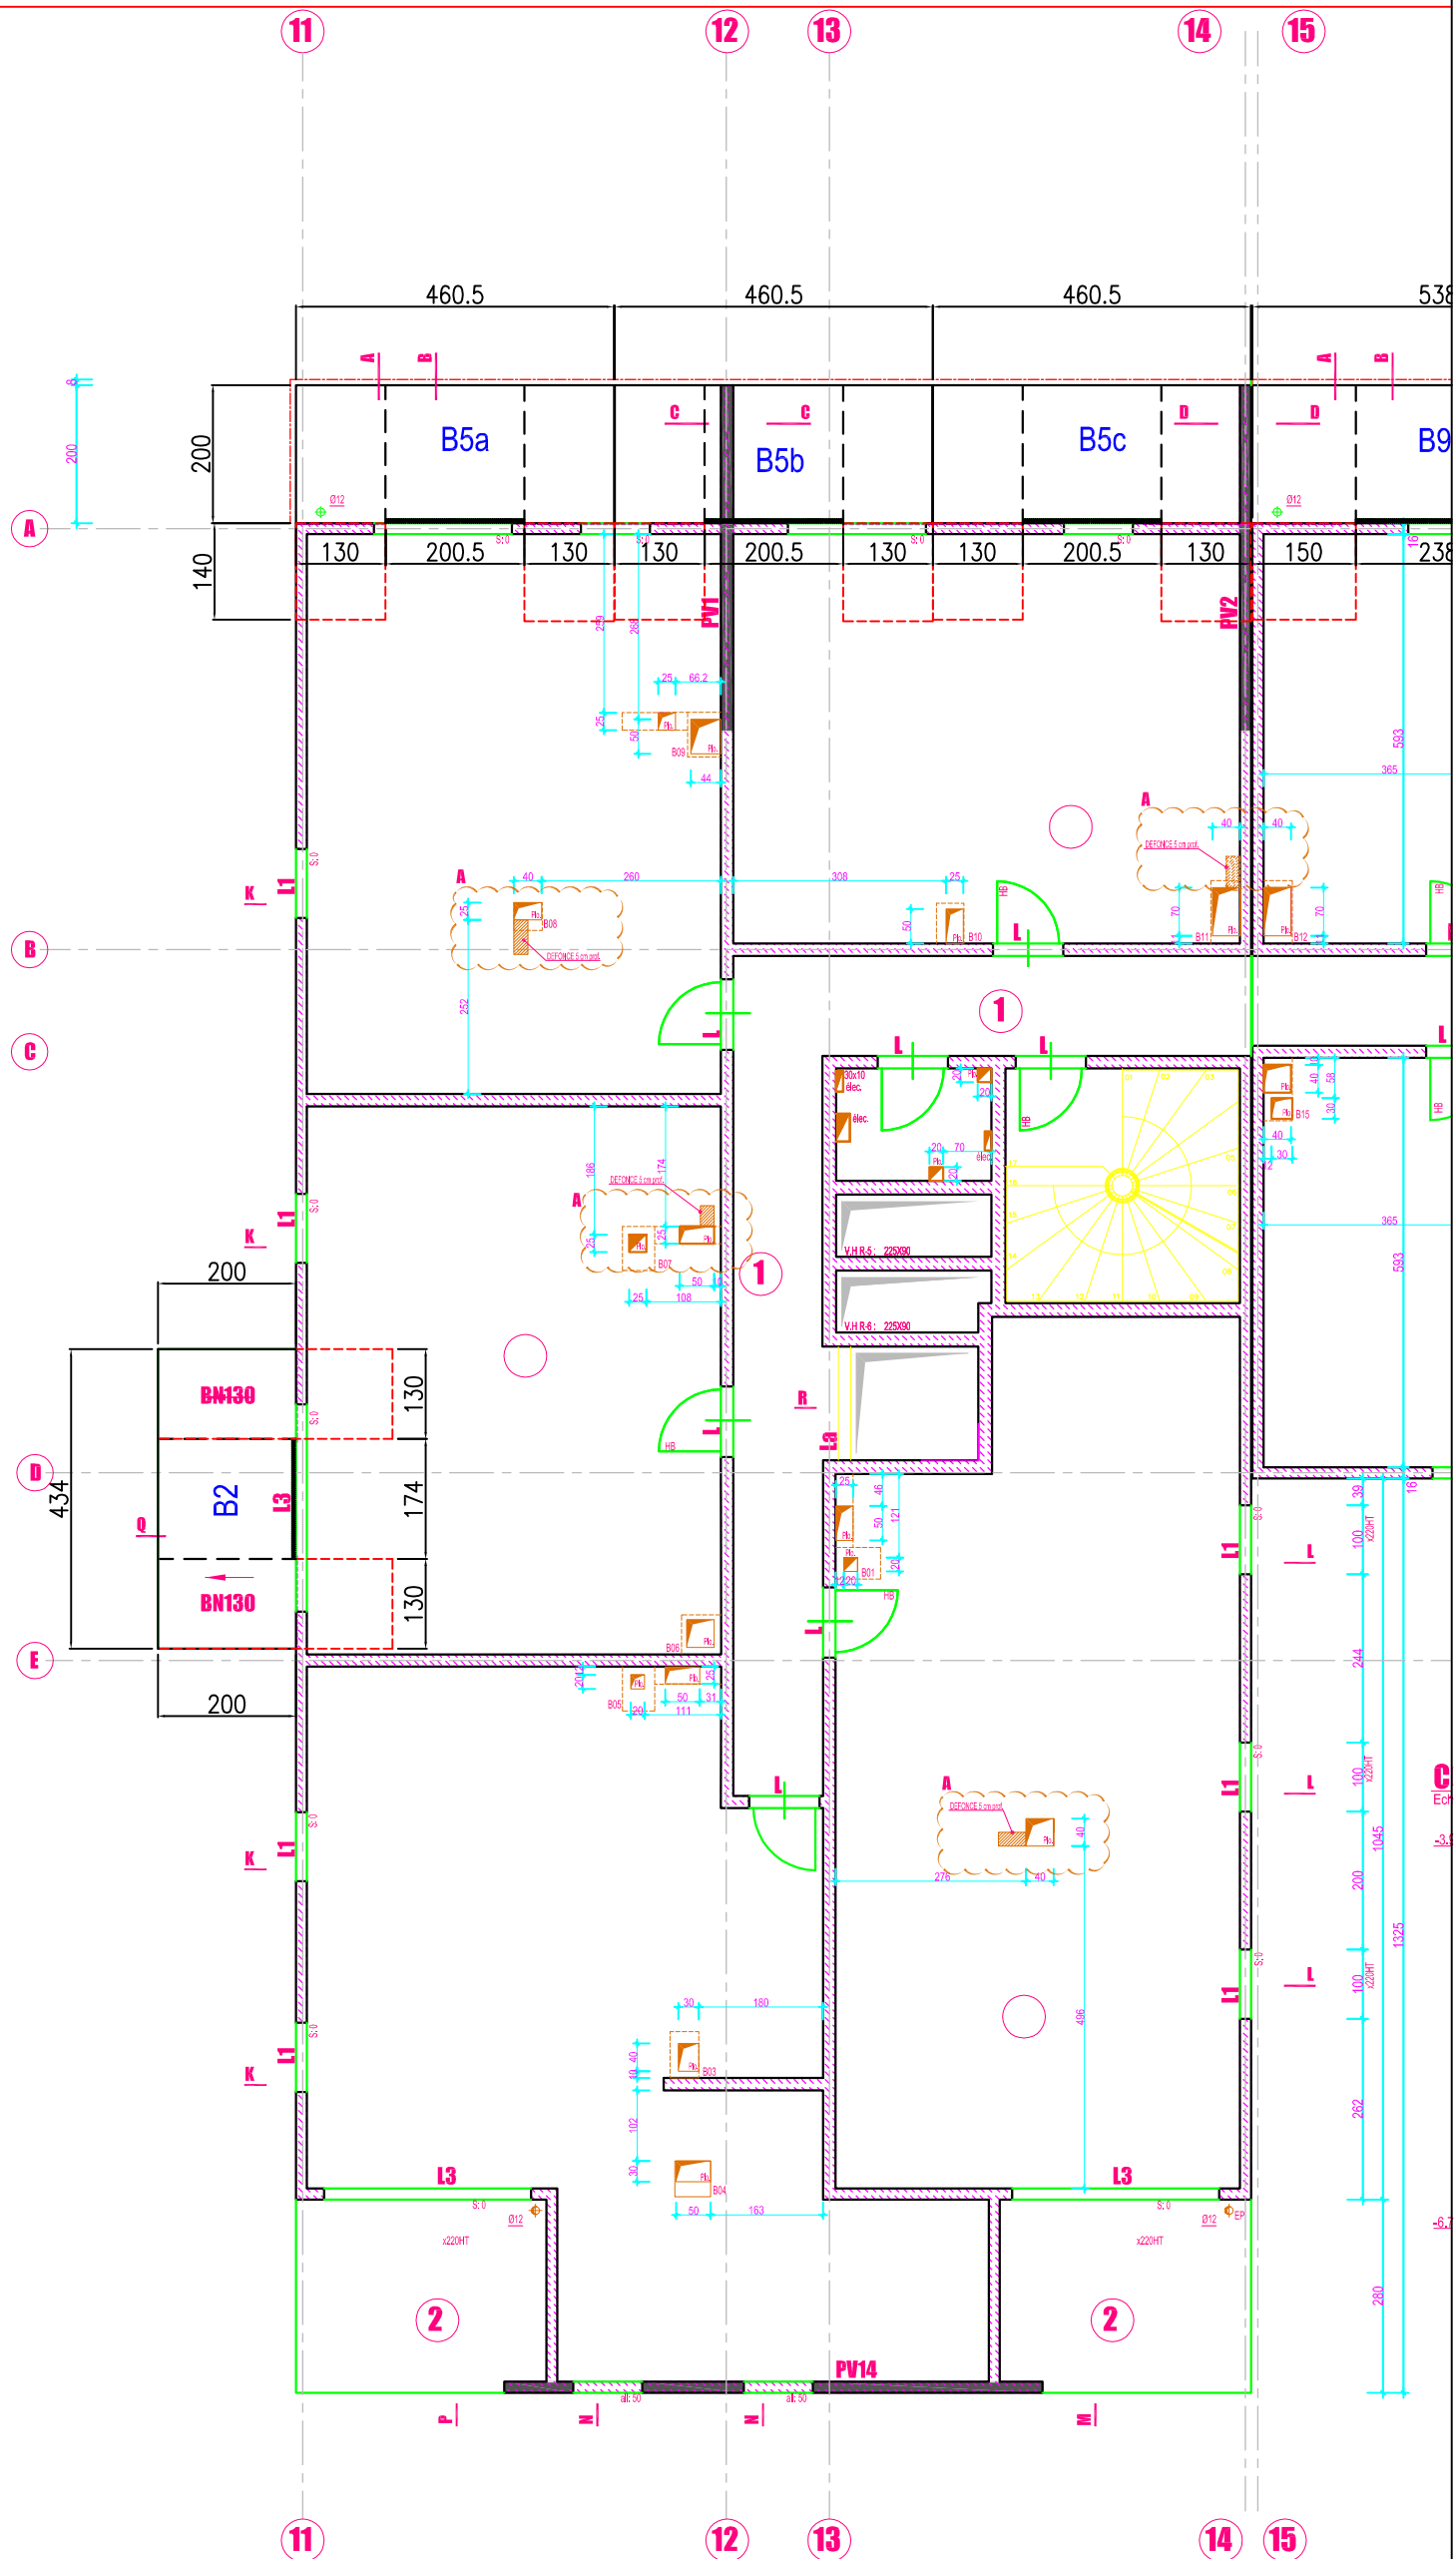

FICHE AUTO-CONTROLE												
MOULE	N	NC	observations	CONTROLE	N	NC	observations	BETON	N	NC	observations	Opérateur :
Conformité moule				Dimensions				Conformité béton				Responsable prod :
Etat du moule				Armature				Mise en place				Date :
Propreté et huilage				Inserts				Aspect de surface				


Ent. FONTANEL		Elément: BALCONS		 PLAN DE FABRICATION		Surface: 8.68 m²		POIDS		REPERE		Nbr	
LA MULATIERE		coffrage / ferrailage				Volume: 1.65 m3		3.95 T		B2		1	

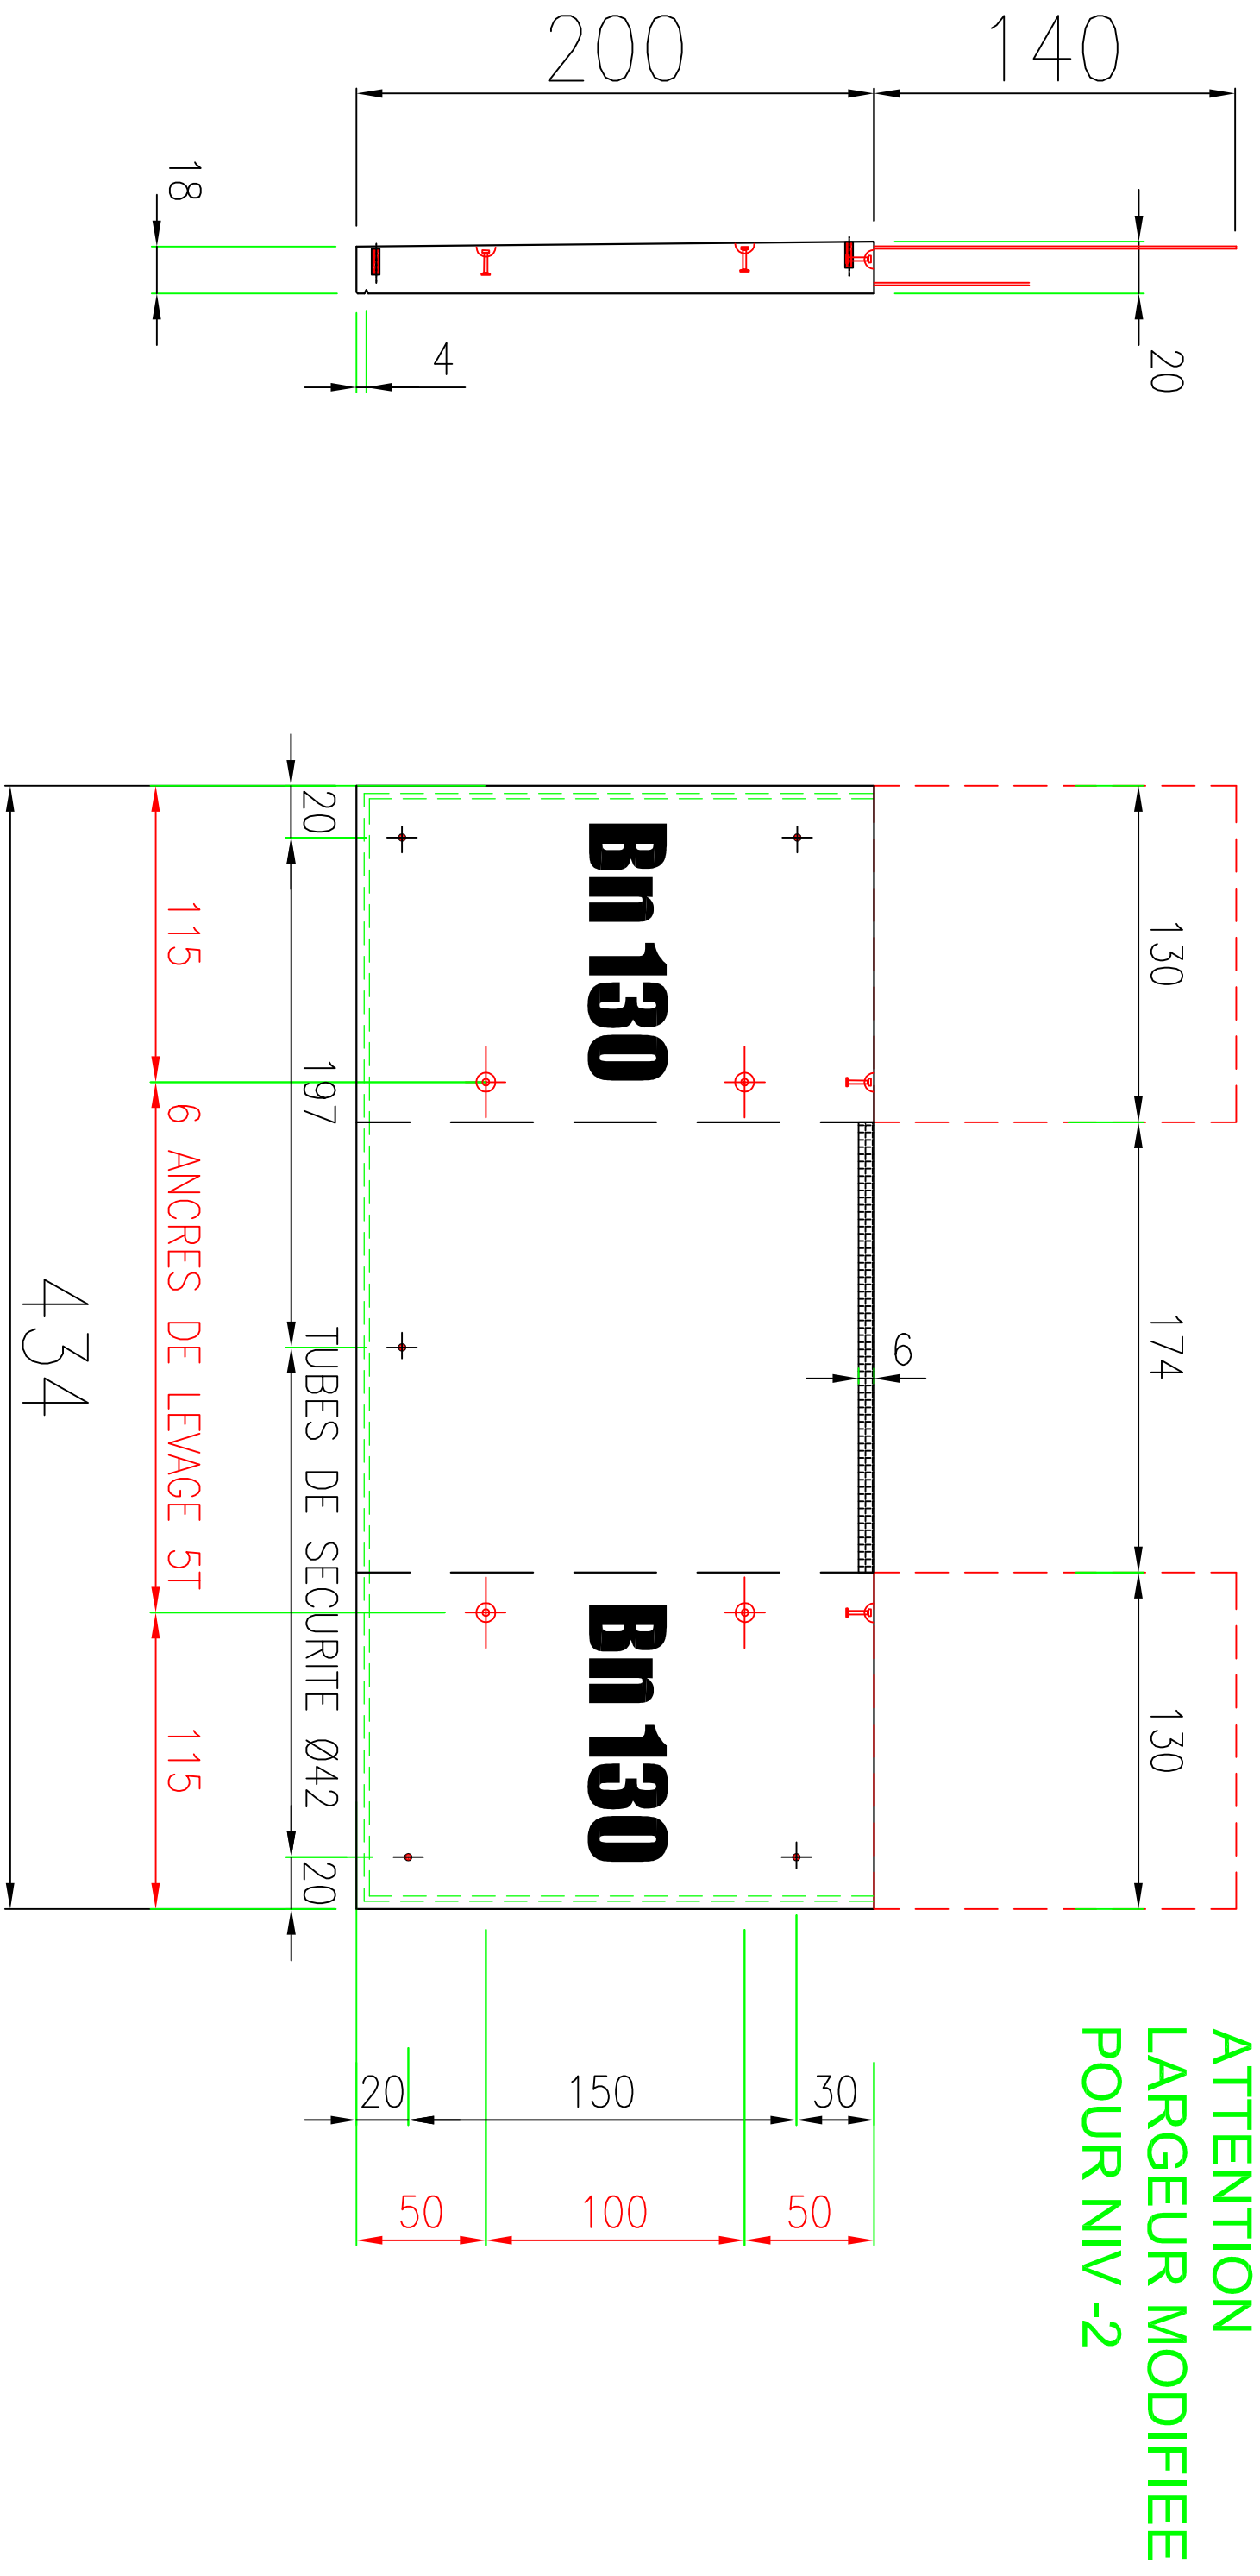

LEVAGE									
	Douille Ø								
	Douille Ø								
	Renfort Ø dx								
INSERTS									
	Ancre Frimeda T								
	Renfort Ø								
	Trifer								
INSERTS									
	EBA								
	Douille étalement								
	Ankrobox Ø50								
INSERTS									
	TP - JV								
	PVC Ø80								
	Tube garde-corps								
DATE: 22/12/2015									
Plan N°			Page N°						
Indice									

MOULE	N	NC	observations	CONTROLE	N	NC	observations	BETON	N	NC	observations	FICHE AUTO-CONTROLE
Conformité moule				Dimensions				Conformité béton				Opérateur :
Etat du moule				Armature				Mise en place				Responsable prod :
Propreté et huilage				Inserts				Aspect de surface				Date :


Ent. FONTANEL		Elément: BALCONS		PLAN DE FABRCATION		Surface: 9.21 m²	POIDS	REPERE	Nbr
LA MULATIERE		coffrage / ferrailage		PLATTARD S.A.S.		Volume: 1.70 m3	4.10 T	B5a	1

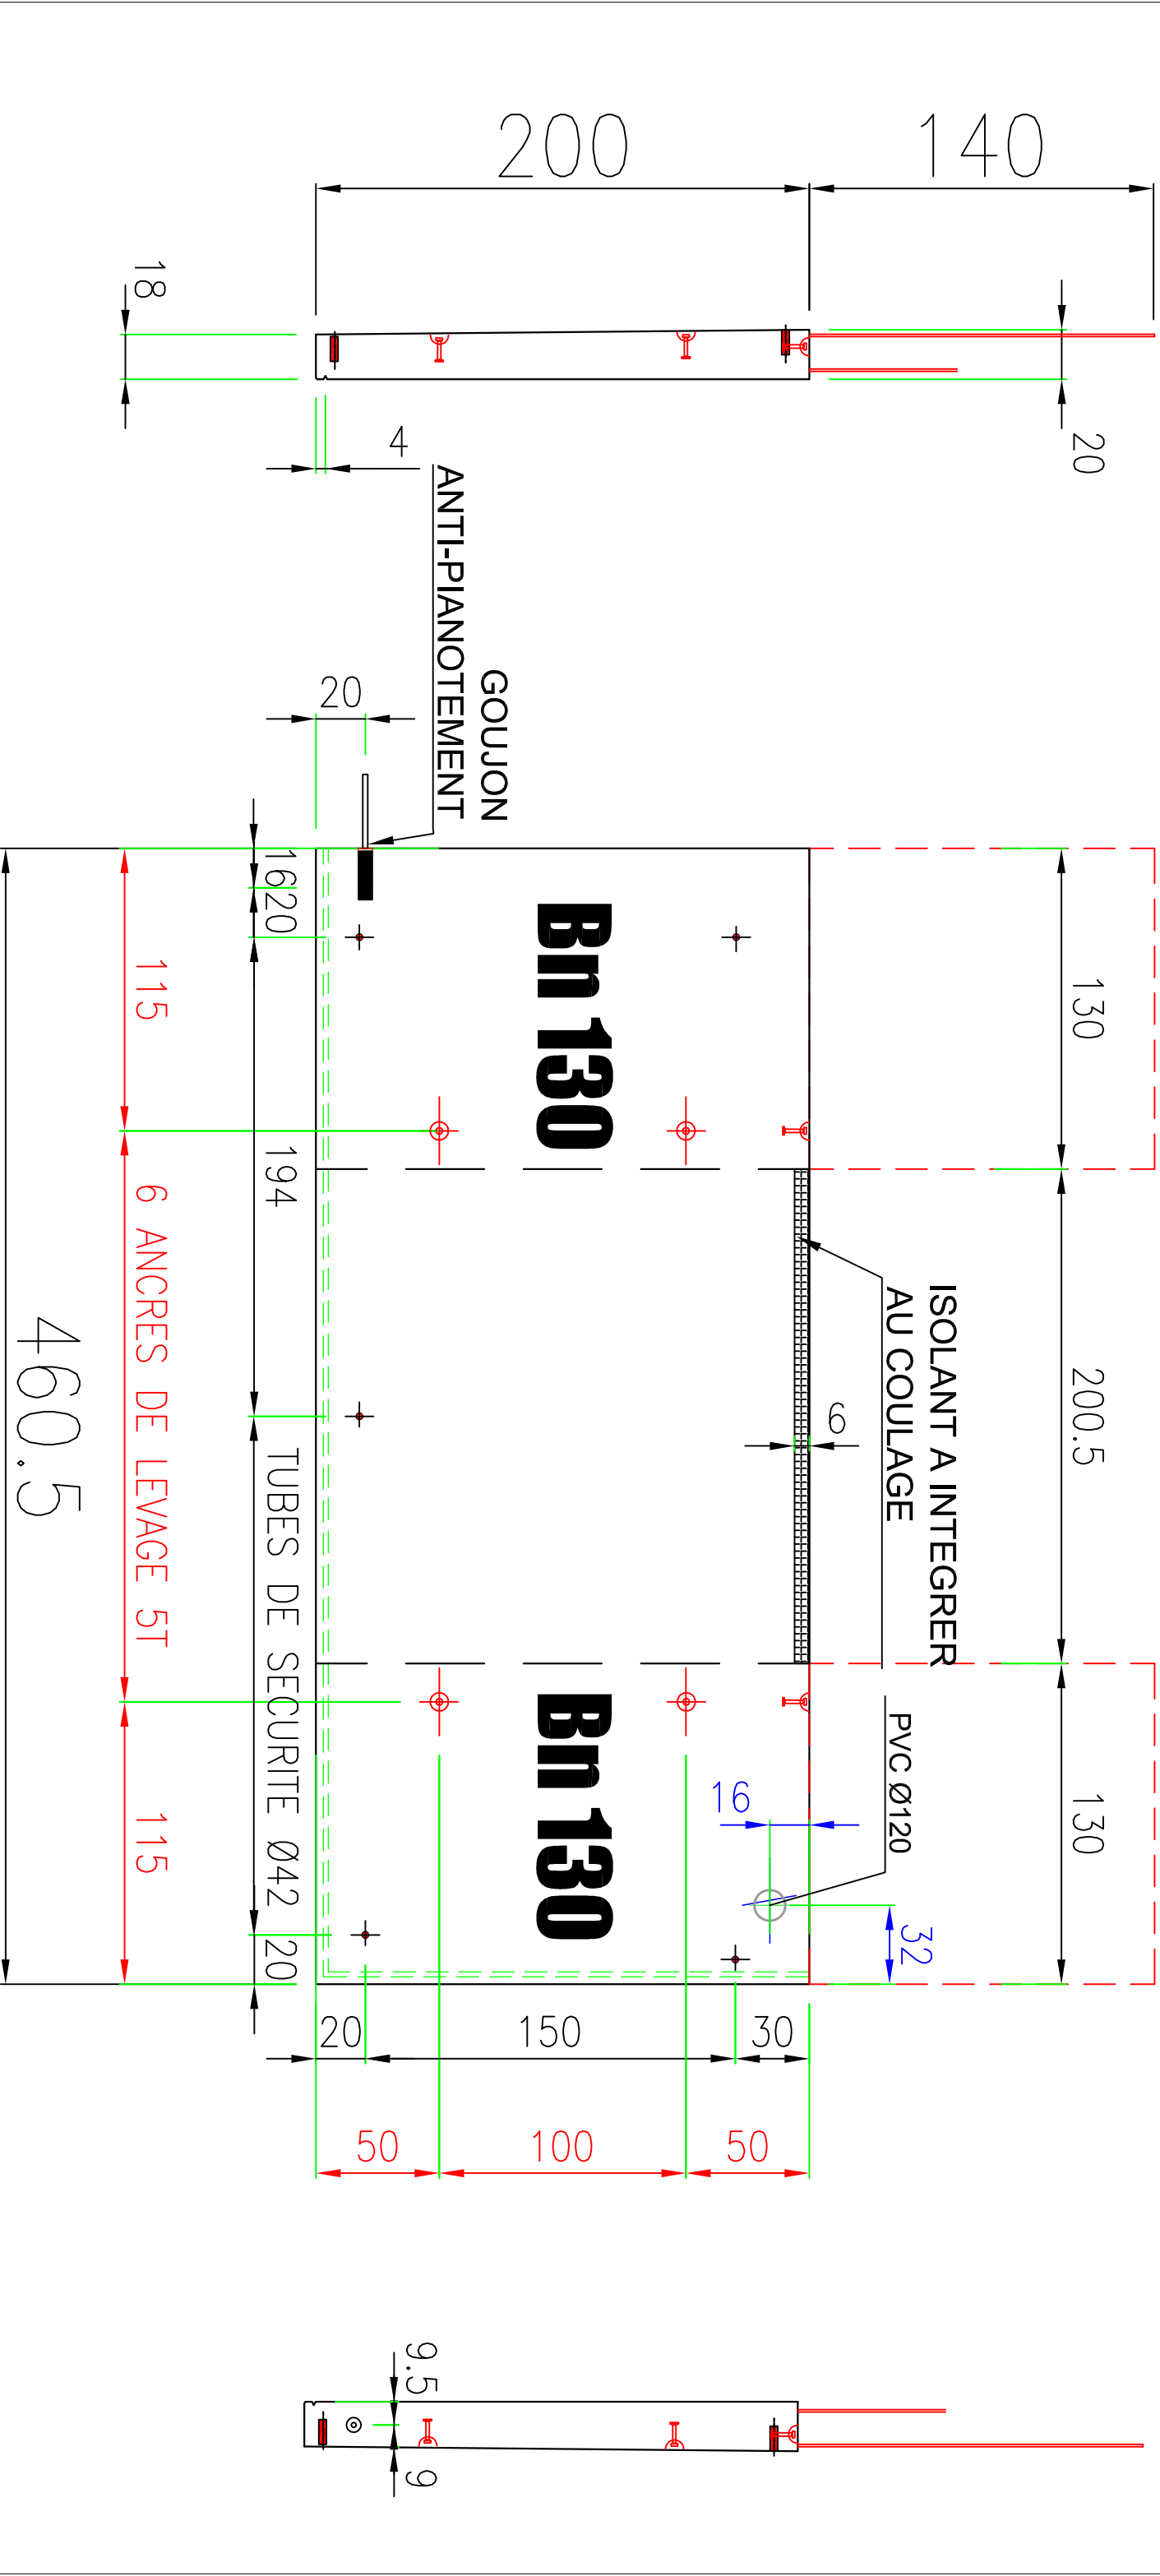

LEVAGE		INSERTS		INSERTS		INSERTS	
	Douille Ø		Ancre Frimeda T		EBA		TP - JV
	Douille Ø		Renfort Ø		Douille étalement		PVC Ø80
	Renfort Ø dx		Trifer		Ankrobox Ø50		Tube garde-corps
DATE: 11/12/2015		Plan N°		Indice		Page N°	

MOULE	N	NC	observations	CONTRÔLE	N	NC	observations	BETON	N	NC	observations	FICHE AUTO-CONTRÔLE
Conformité moule				Dimensions				Conformité béton				Opérateur :
Etat du moule				Armature				Mise en place				Responsable prod :
Propreté et huilage				Inserts				Aspect de surface				Date :


Ent. FONTANEL			Elément: BALCONS			PLAN DE FABRCATION			Surface: 9.21 m²	POIDS	REPERE	Nbr
LA MULATIERE			coffrage / ferrailage			Volume: 1.70 m3			4.10 T	B5b		
												1

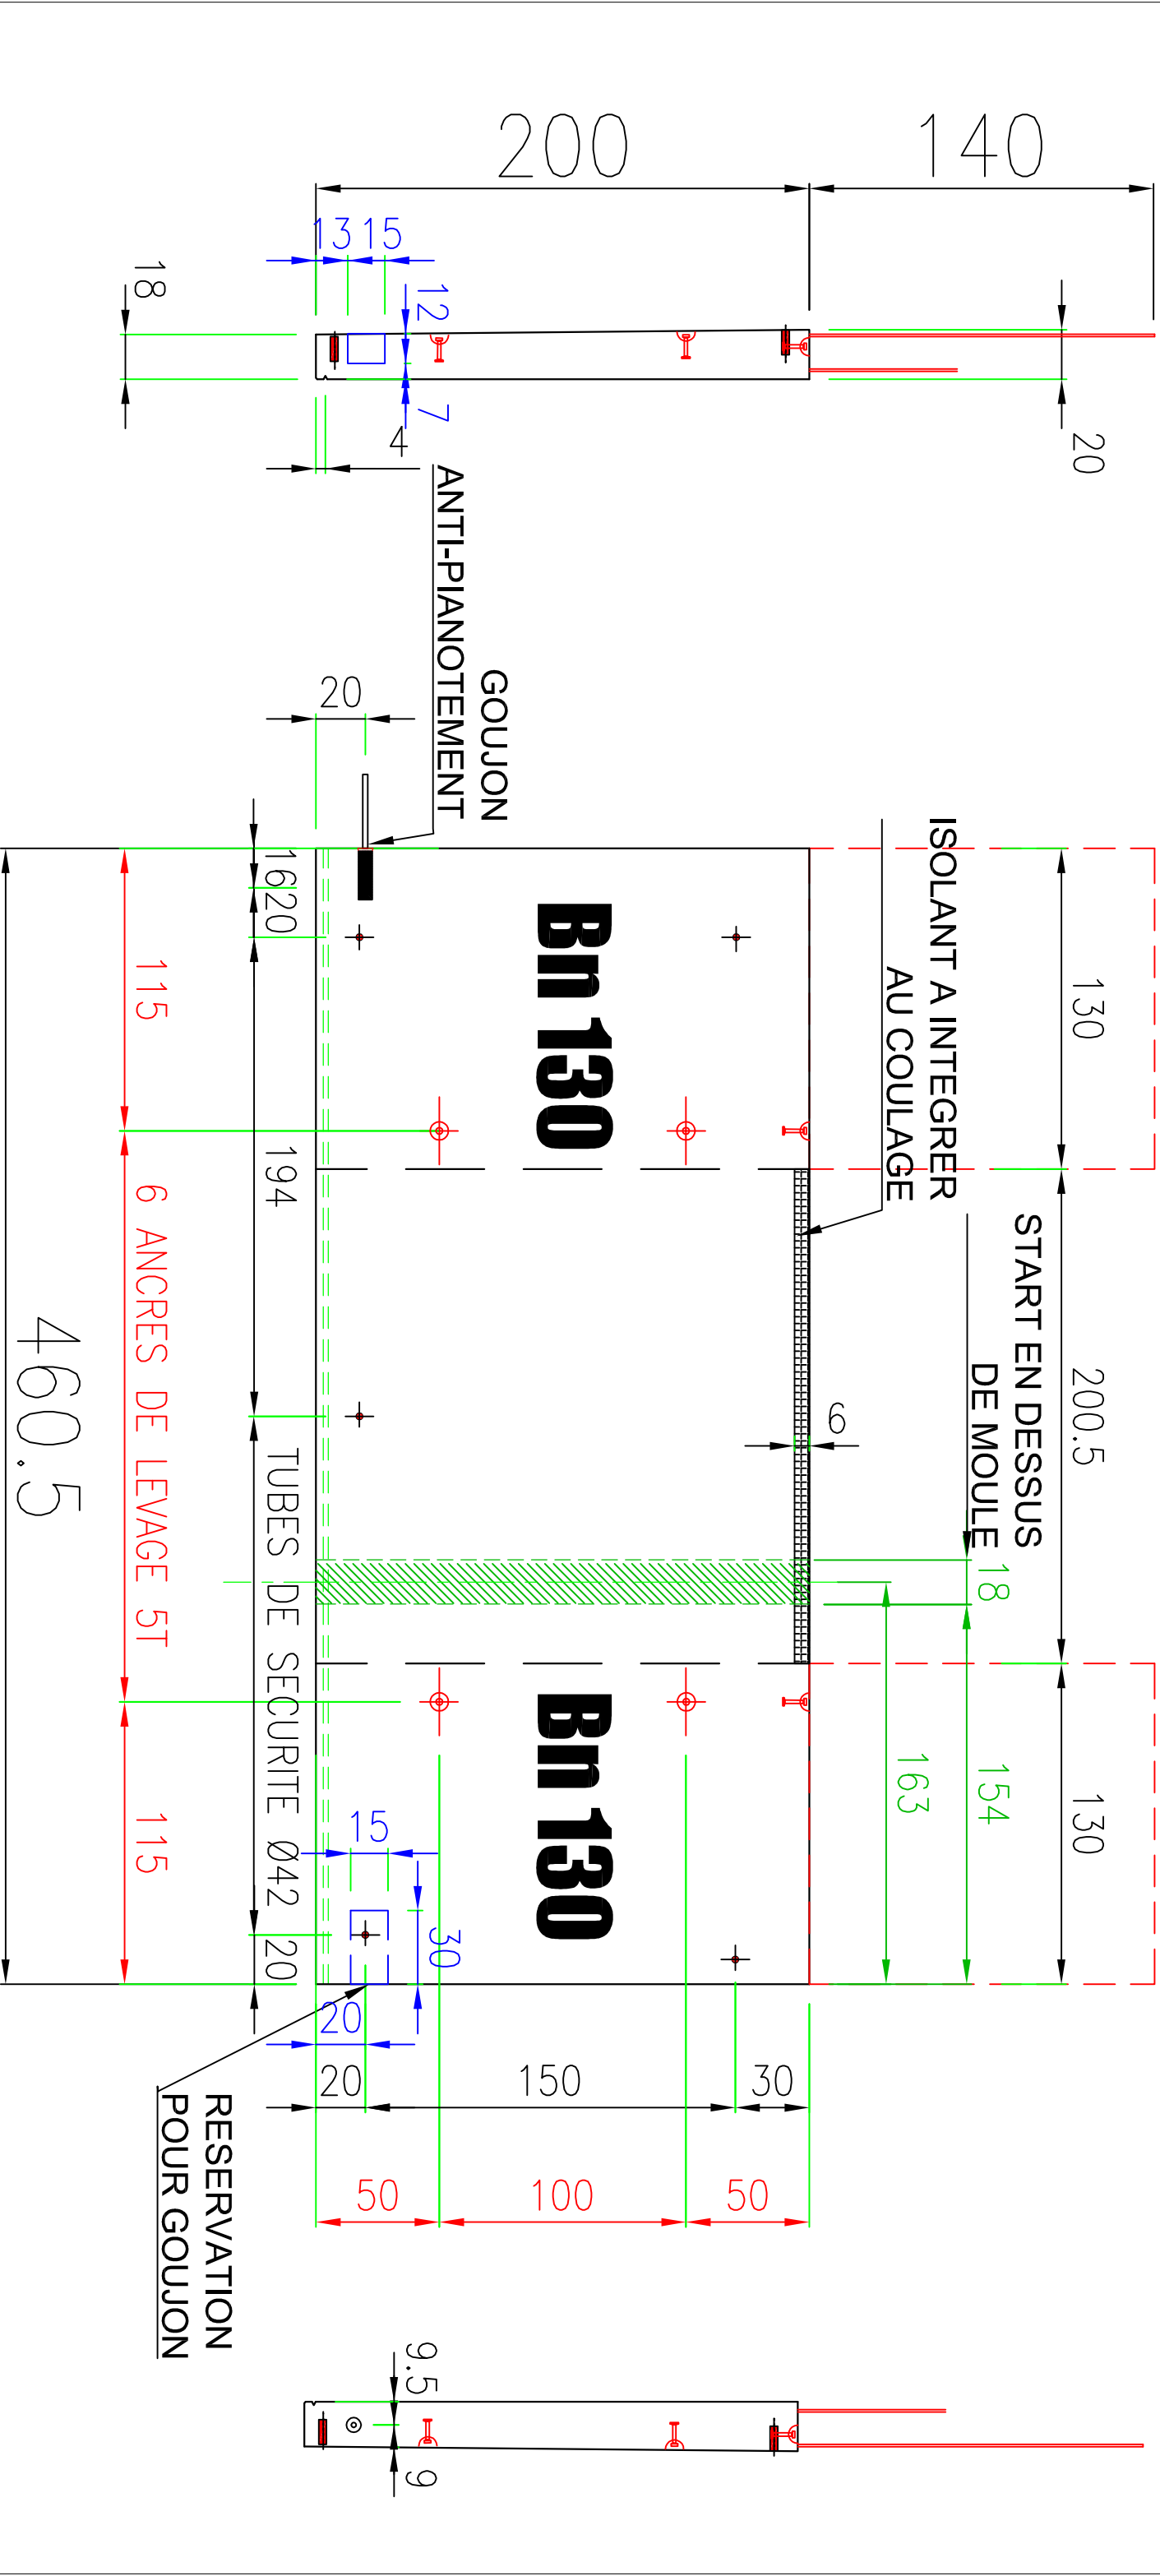

LEVAGE			INSERTS			INSERTS			INSERTS		
	Douille Ø			Ancre Frimeda T			EBA			TP - JV	DATE: 11/12/2015
	Douille Ø			Renfort Ø			Douille étalement			PVC Ø80	Plan N°
	Renfort Ø dx			Trifer			Ankrobox Ø50			Tube garde-corps	Indice
									Page N°		

MOULE	N	NC	observations	BETON	N	NC	observations	FICHE AUTO-CONTROLE
Conformité moule			Dimensions	Conformité béton				Opérateur :
Etat du moule			Armature	Mise en place				Responsable prod :
Propreté et huilage			Inserts	Aspect de surface				Date :

Ent. FONTANEL		Elément: BALCONS		PLAN DE FABRCATION		Surface: 9.21 m²	POIDS	REPERE	Nbr
LA MULATIERE		coffrage / ferrillage		PLATTARD S.A.S.		Volume: 1.70 m3	4.10 T	B5C	1

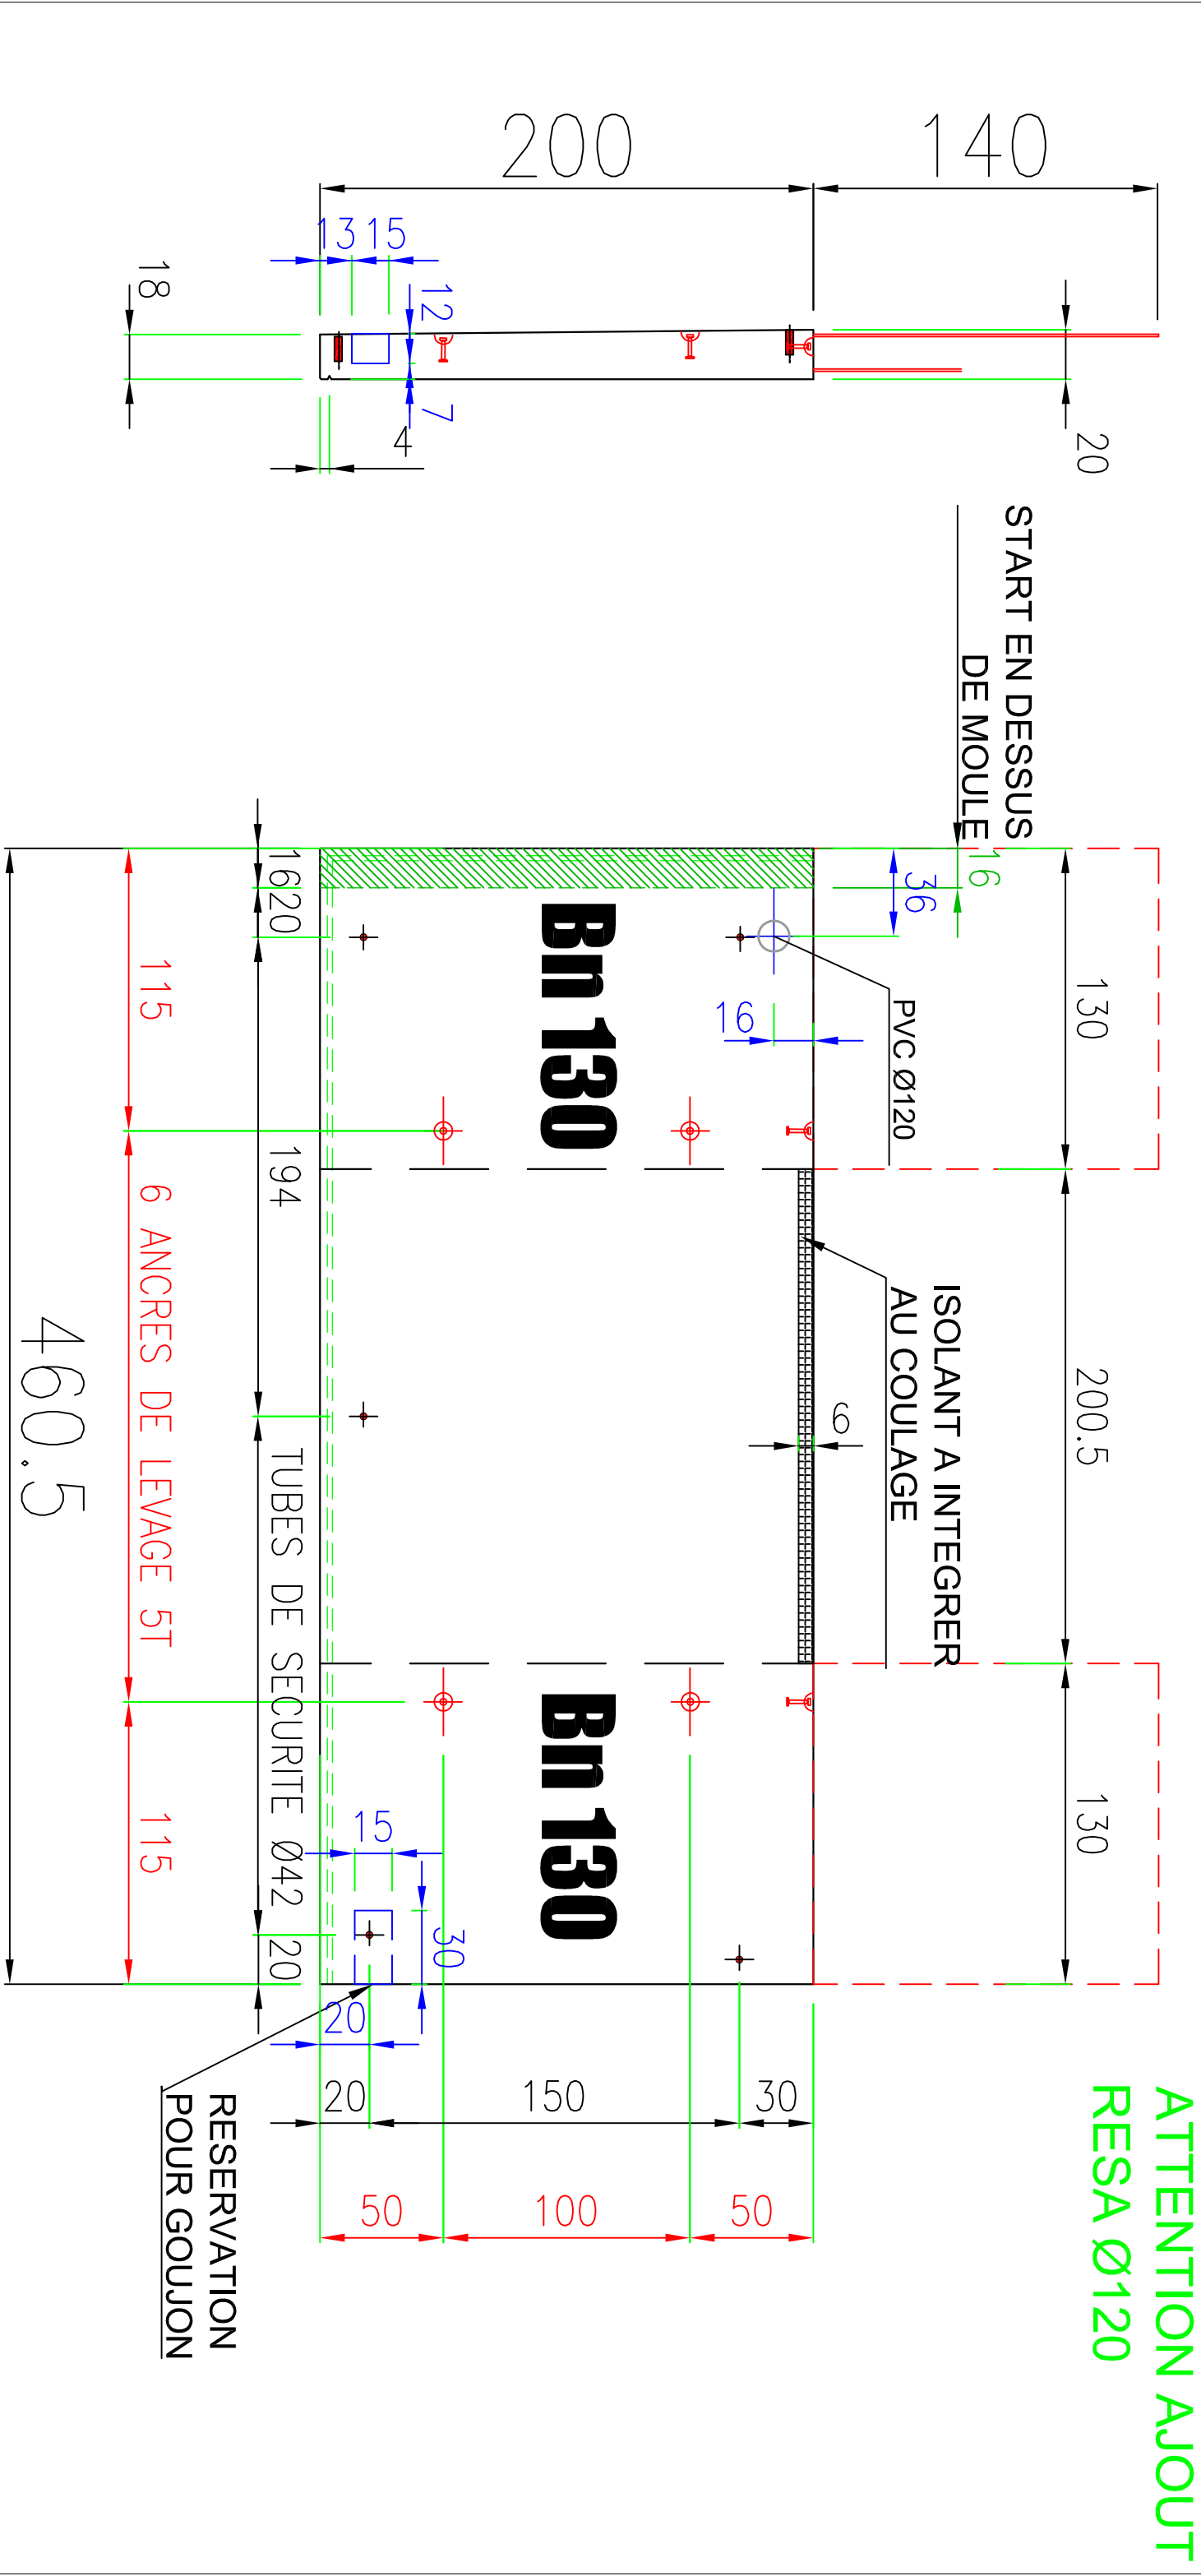

LEVAGE		INSERTS		INSERTS		INSERTS	
	Douille Ø		Ancre Frimeda T		EBA		TP - JV
	Douille Ø		Renfort Ø		Douille étalement		PVC Ø80
	Renfort Ø dx		Trifer		Ankrobox Ø50		Tube garde-corps
						DATE: 11/12/2015	
						Plan N°	
						Page N°	
						Indice	