

FONTANEL- LE 180°

69 LA MULATIERE

BALCONS DU NIVEAU N-1
BAT B

N°

EXE

Indice	Date	Designation des Modifications	Date :
A			01/02/2016
B			Affaire :
C			
D			Echelle :
E			
F			
G			
H			
I			

Type béton = B35 XF1
Aciers H.A et T.S = Fe E 500
Enrobage des armatures = ENR_{CA}ARMAT
Manutention = Tonnes



P L A T T A R D



BUREAU D'ETUDE
PLATTARD SAS
414 Avenue de la
plage
BP 119
69540
Villefrance-sur-Saône
Tél: 04 74 02 20 20
Fax: 04 74 62 26 62

Ce plan est la propriété intellectuelle de la PLATTARD SAS, il ne peut être reproduit sans son autorisation.

NOAHO

Chemin de Fontanière - 69350 La Mulatière

Création de logements

Les entreprises réalisant les travaux devront tenir compte des derniers plans architecte lors de la réalisation des travaux
Les plans du be MATTE ne doivent servir qu'au corps d'état concerné et doivent être des plans d'exécution.

ARCHITECTE(S): ATELIER DE LA PASSERELLE

MO DELEGUE:

BET STRUCTURE: MATTE SAS

MOE: PSO Ingénierie

BET FLUIDES: PRELEM

CSPS: SUD EST COORDINATION

ECONOMISTE: EXECO

OPC:

BUREAU DE CONTROLE: Bureau VERITAS

ENTREPRISE(S): Fontanel-pbc

Bât: B
PLANCHER sur -1
Coffrage

EXE

Contrainte de sol:

Aciers HA (T) FeE500
Aciers Doux (Ø) FeE 235
Aciers TS FeE 500
Béton fc28 >= 25MPa
Enrobage = 3 cm

PLAN N°
B34 0

DATE : 19/11/2015

MATTÉ
BUREAU D'ÉTUDES
STRUCTURES ET FLUIDES

119 BOULEVARD STALINGRAD 69100 VILLEURBANNE

Tél. 04 72 44 02 87 Fax 04 72 44 26 59


E-mail : bet@matte.fr


Dessiné par : J.BO

Contrôlé par : P.LIN

Echelle : 1/50°


Affaire N°
13.12.119

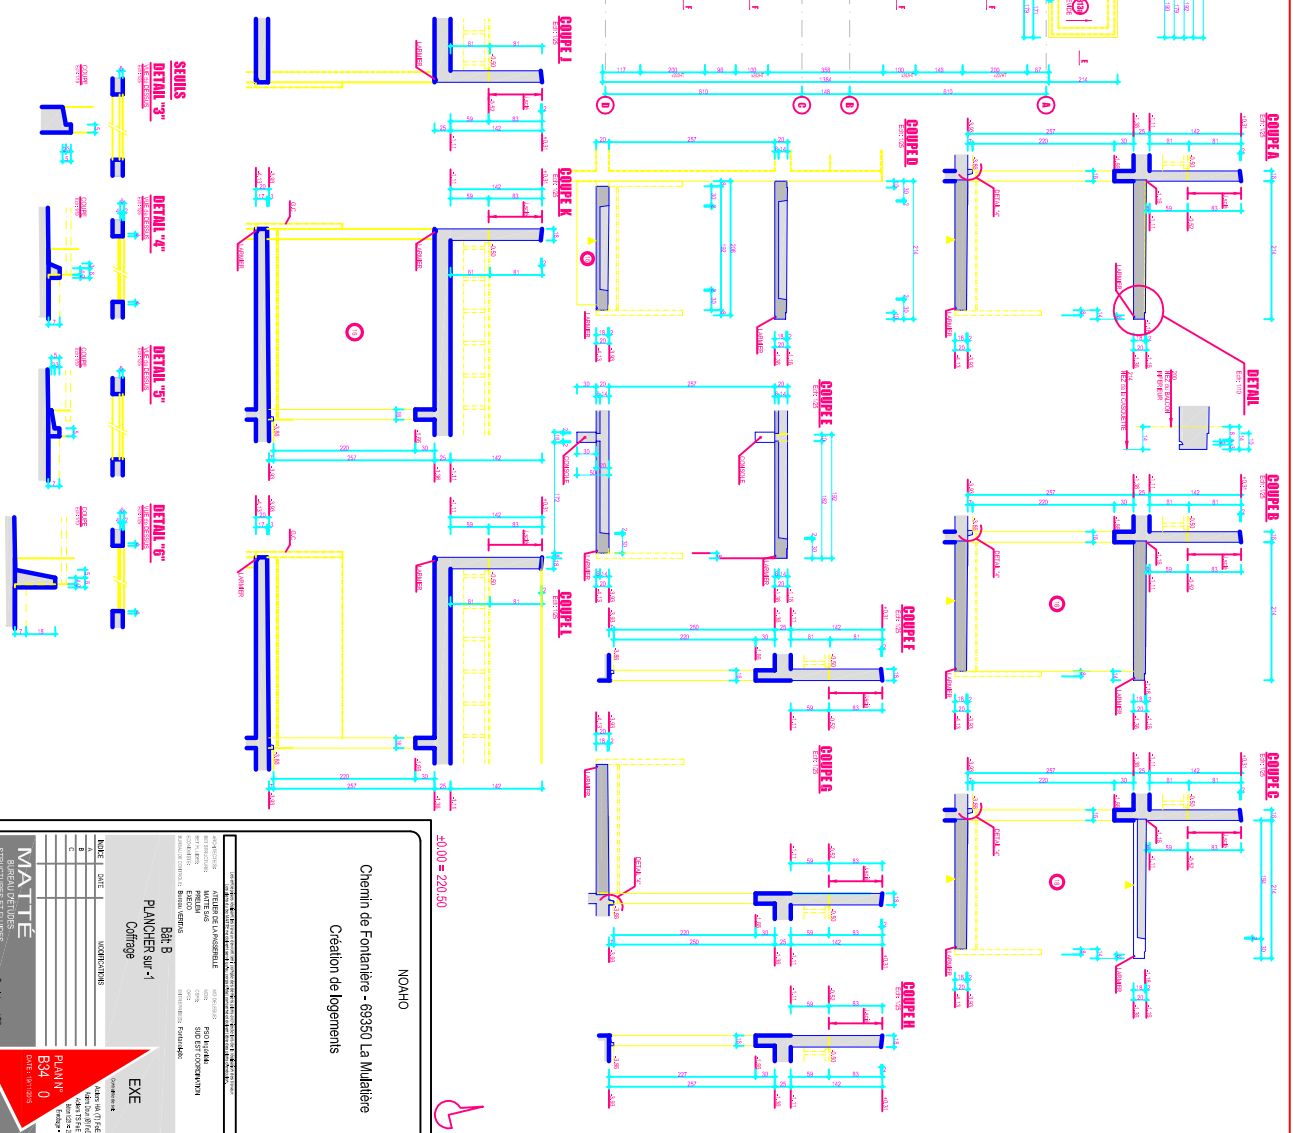

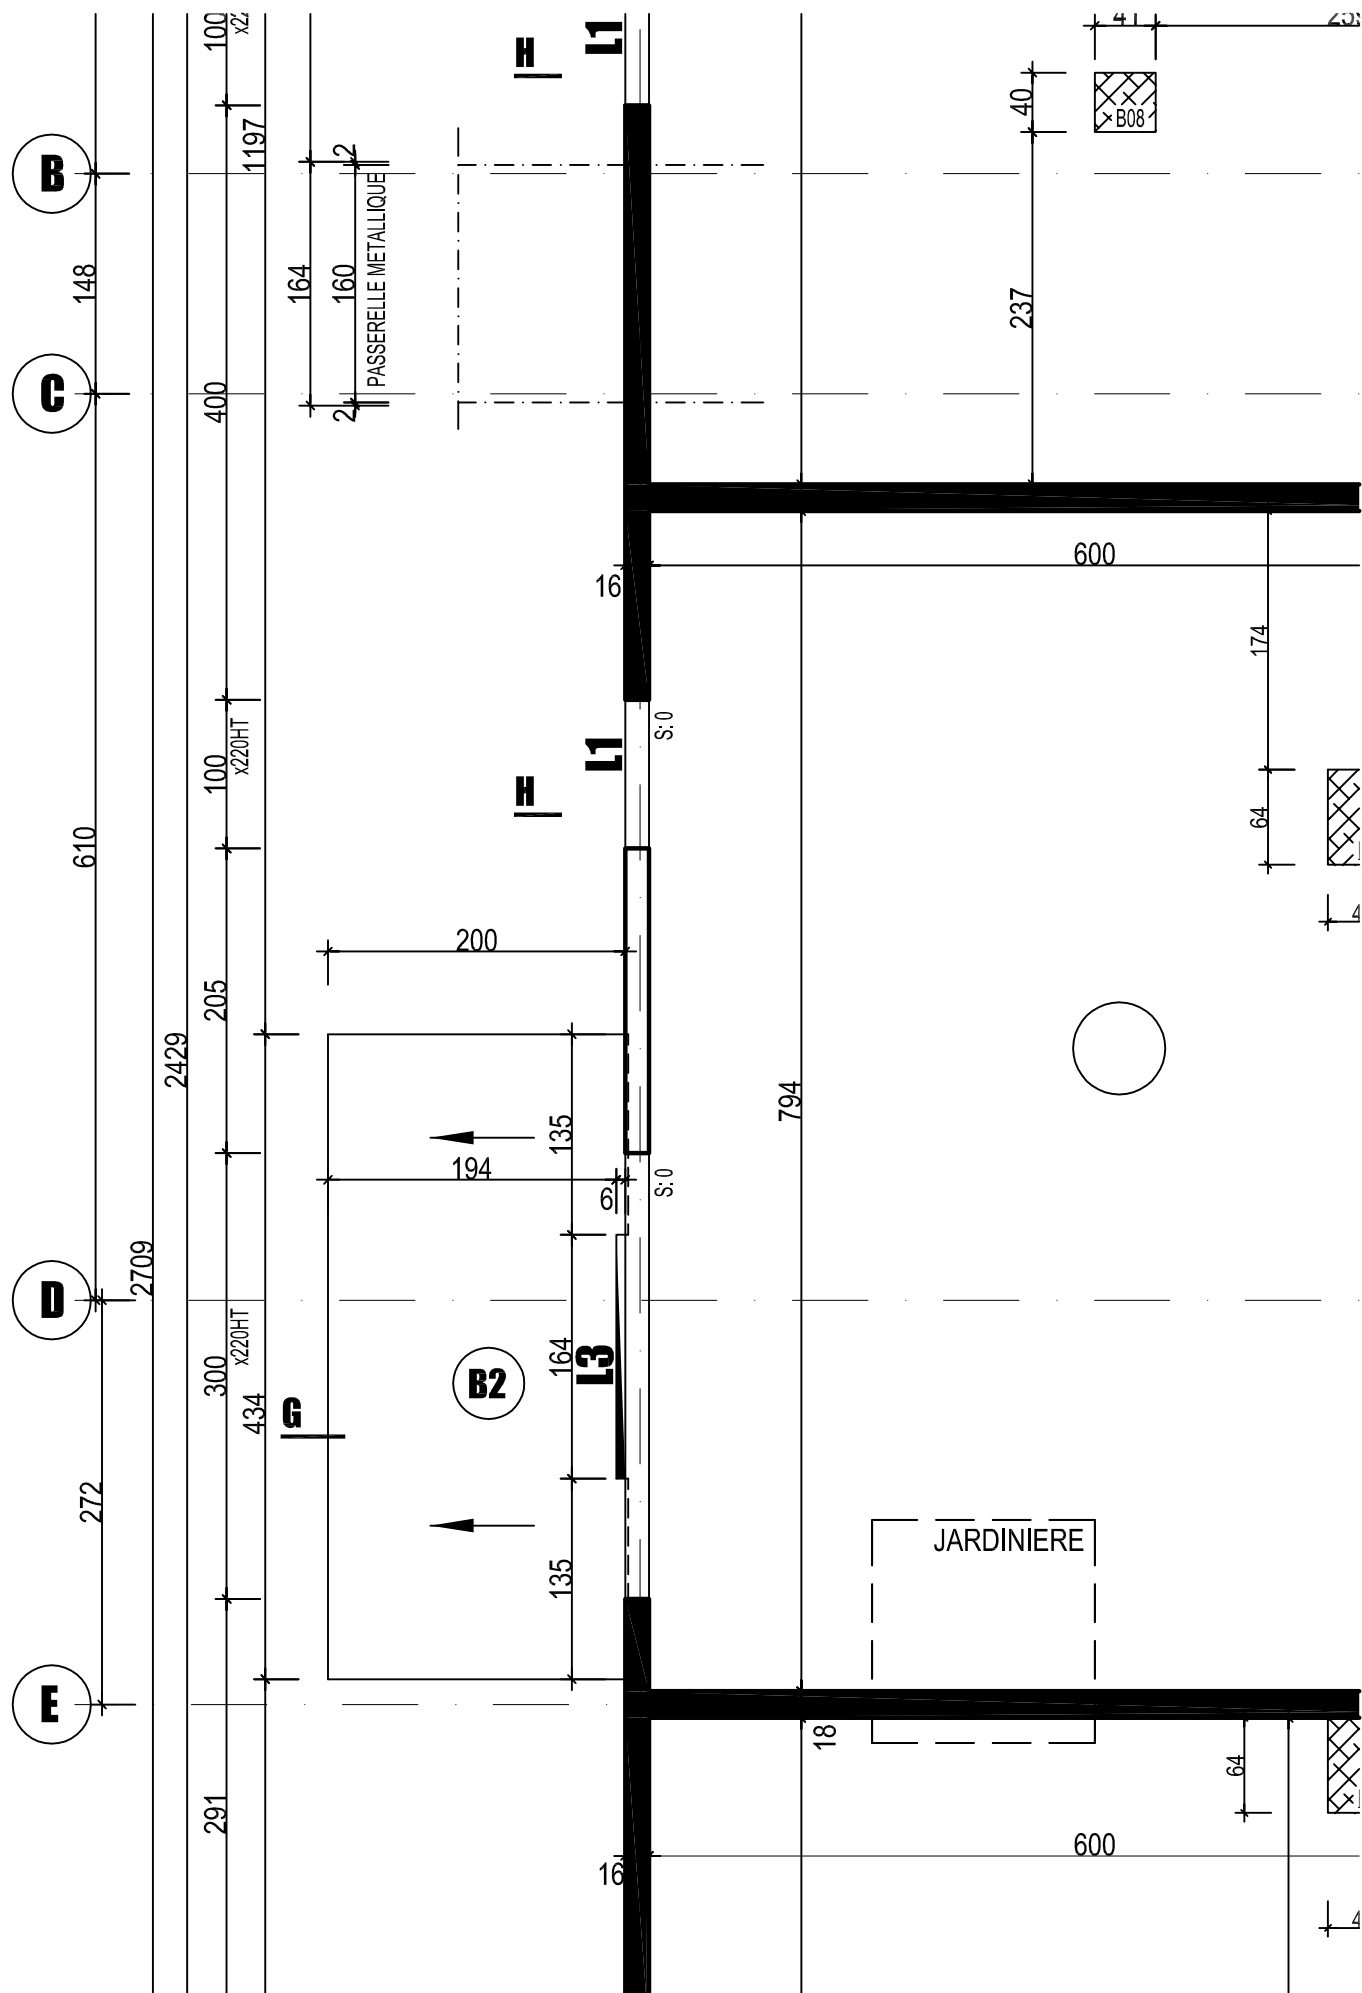


Plancher Niveau R-1

BAT. B

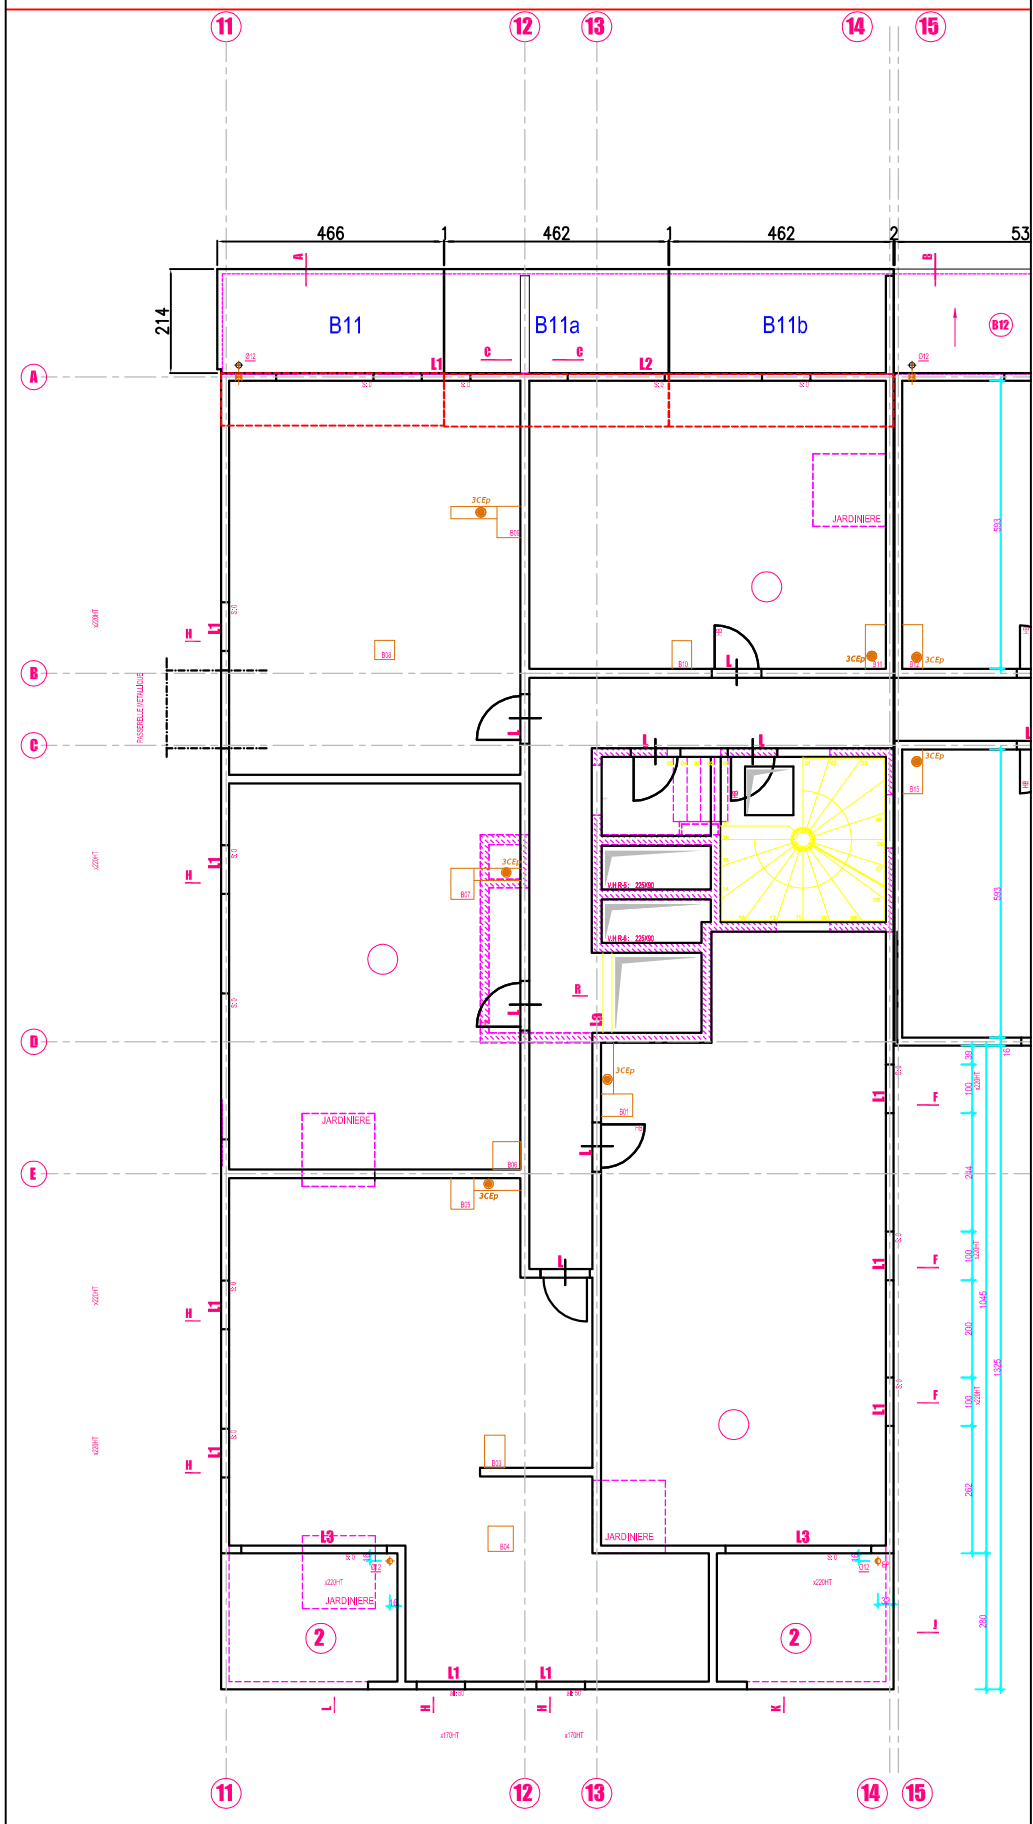

MOULE	N	NC	observations	CONTROLE	N	NC	observations	BETON	N	NC	observations	FICHE AUTO-CONTROLE
Conformité moule				Dimensions				Conformité béton				Opérateur :
Etat du moule				Armature				Mise en place				Responsable prod :
Propreté et huilage				Inserts				Aspect de surface				Date :


Ent. FONTANEL			Elément: BALCONS			PLAN DE FABRCATION			Surface:	9.97 m²	POIDS	REPERE	Nbr
LA MULATIERE			coffrage / ferrailage			PLATTARD S.A.S.			Volume:	1.90 m3	4.56 T	B11a	1

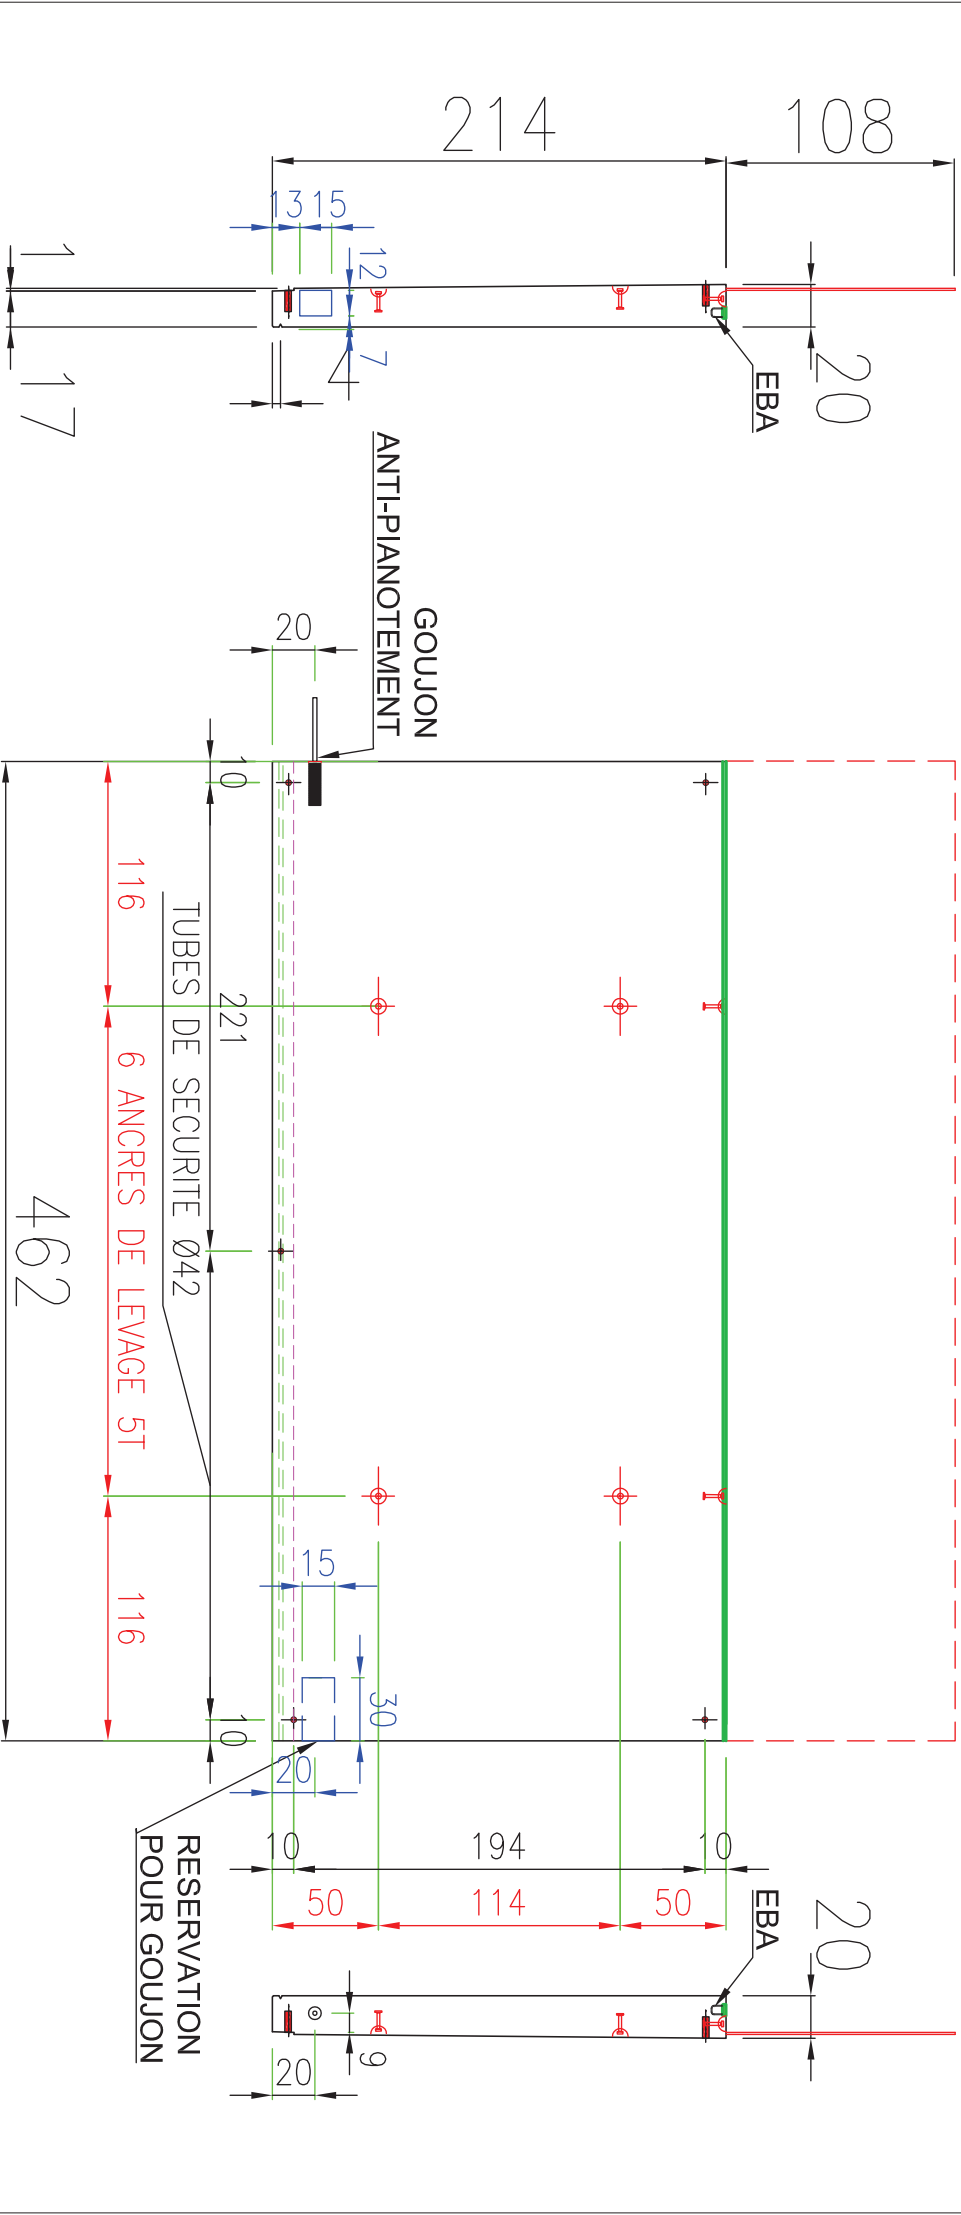

LEVAGE			INSERTS			INSERTS			INSERTS			INSERTS		
	Douille Ø			Ancre Frimeda T			EBA			TP - JV			DATE: 18/11/2015	
	Douille Ø			Reinfort Ø			Douille étalement			PVC Ø80			Plan N°	Page N°
	Reinfort Ø dx			Trifer			Ankrobox Ø50			Tube garde-corps			Indice	

MOULE	N	NC	observations	CONTRÔLE	N	NC	observations	BETON	N	NC	observations	FICHE AUTO-CONTROLE
Conformité moule				Dimensions				Conformité béton				Opérateur :
Etat du moule				Armature				Mise en place				Responsable prod :
Propreté et huilage				Inserts				Aspect de surface				Date :

Ent. FONTANEL			Elément: BALCONS			PLAN DE FABRCATION			Surface:	9.97 m²	POIDS	REPERE	Nbr
LA MULATIERE			coffrage / ferrailage			PLATTARD S.A.S.			Volume:	1.90 m3	4.56 T	B11b	1

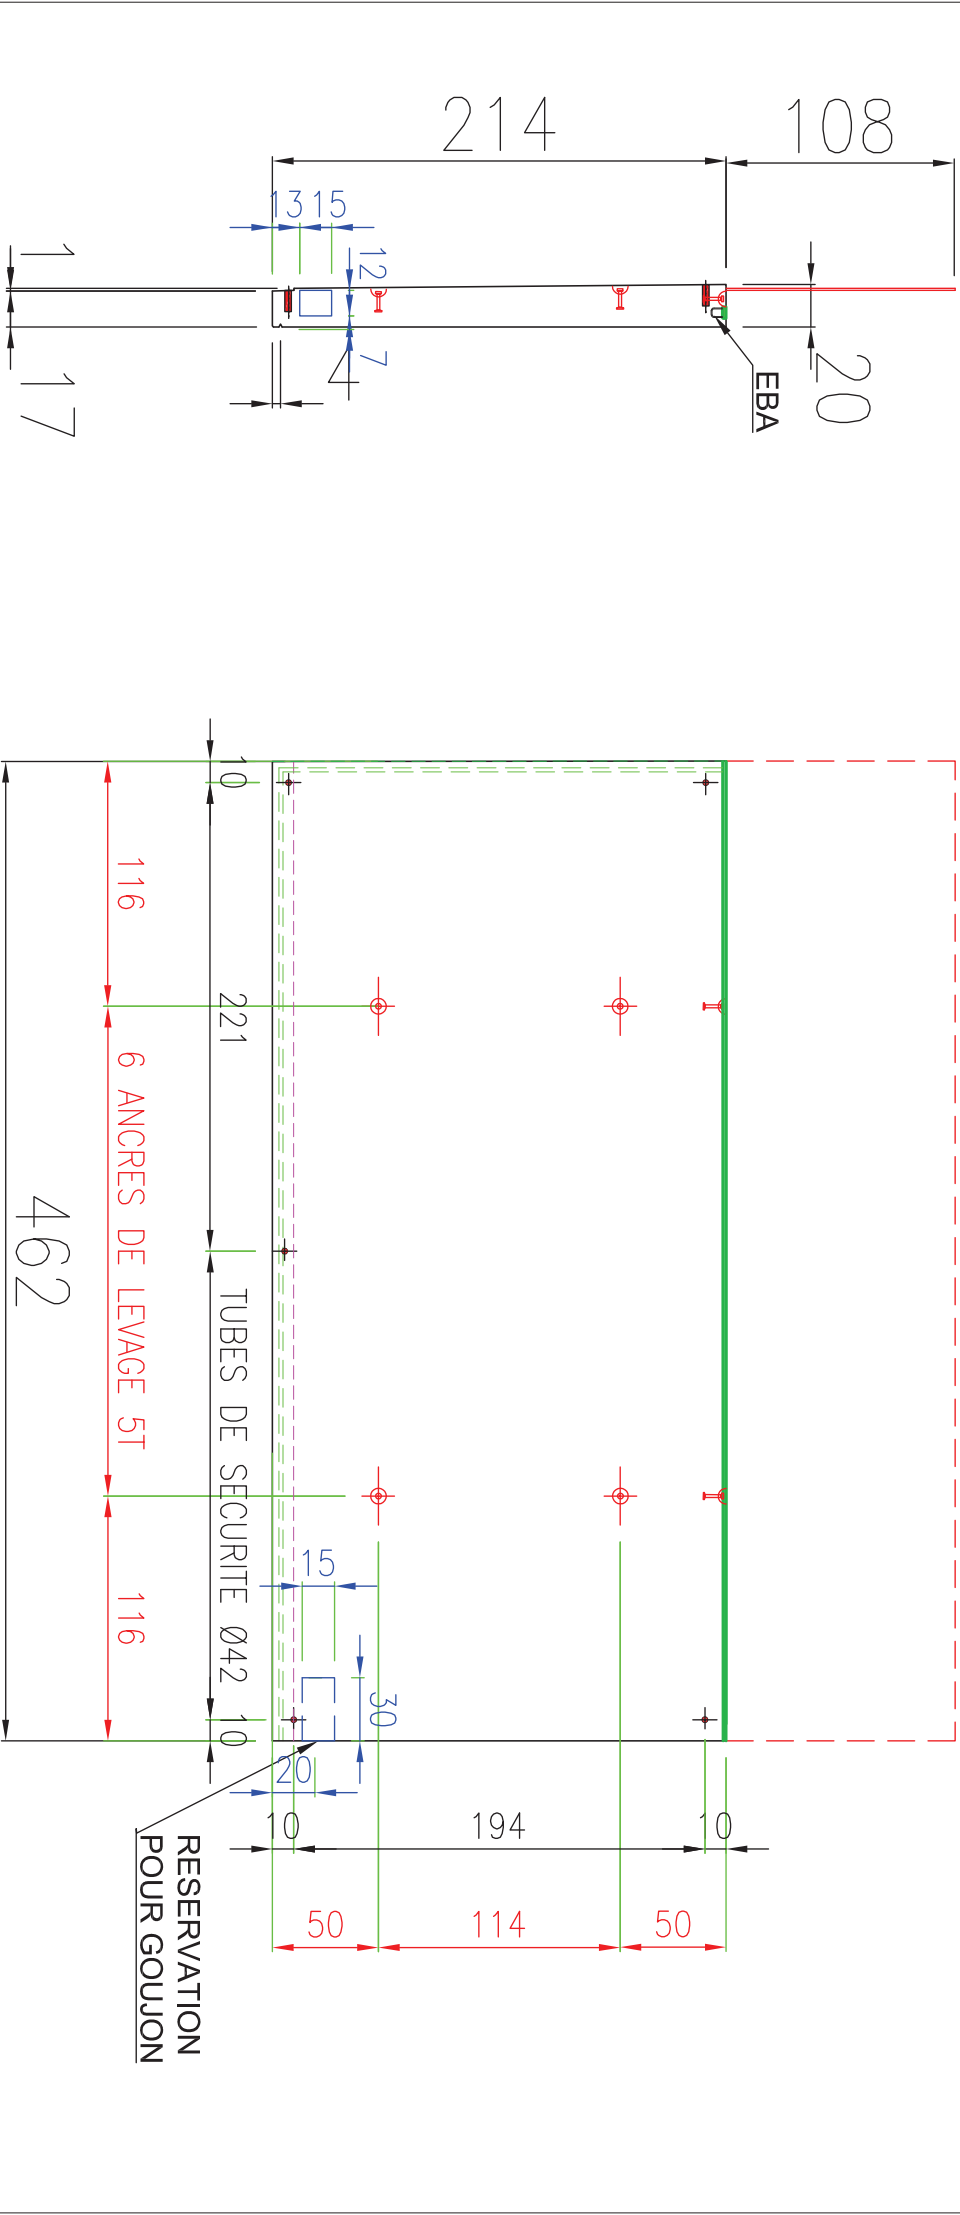

LEVAGE			INSERTS			INSERTS			INSERTS			INSERTS		
	Douille Ø			Ancre Frimeda T			EBA			TP - JV		DATE:	18/11/2015	
	Douille Ø			Renfort Ø			Douille étalement			PVC Ø80		Plan N°		Page N°
	Renfort Ø	dx		Trifer			Ankrobox Ø50			Tube garde-corps		Indice		