

NOAHO

Chemin de Fontanière - 69350 La Mulatière

Création de logements

Les entreprises réalisant les travaux devront tenir compte des derniers plans architecte lors de la réalisation des travaux
Les plans du be MATTE ne doivent servir qu'au corps d'état concerné et doivent être des plans d'exécution.

ARCHITECTE(S):
BET STRUCTURE:
BET FLUIDES:
ECONOMISTE:
BUREAU DE CONTROLE:

ATELIER DE LA PASSERELLE
MATTE SAS
PRELEM
EXECO
Bureau VERITAS

MO DELEGUE:
MOE:
CSPS:
OPC:
ENTREPRISE(S):

PSO Ingénierie
SUD EST COORDINATION

Fontanel-pbc

Bât: B

PLANCHER sur -2

Coffrage

EXE

Contrainte de sol:

INDICE	DATE	MODIFICATIONS
A	10/12/2015	AJOUTE DEFONCE DANS S.d.B suivant A
B		
C		

Aciers HA (T) FeE500
Aciers Doux (Ø) FeE 235
Aciers TS FeE 500
Béton fc28 >= 25MPa
Enrobage = 3 cm

PLAN N°
B28 A

DATE : 19/11/2015

MATTÉ

BUREAU D'ÉTUDES
STRUCTURES ET FLUIDES


119 BOULEVARD STALINGRAD 69100 VILLEURBANNE
Tél. 04 72 44 02 87 Fax 04 72 44 26 59
E-mail : bet@matte.fr

Dessiné par : J.BO
Contrôlé par : P.LIN
Echelle : 1/50°

Affaire N°
13.12.119


Plancher Niveau R-2

BAT. B

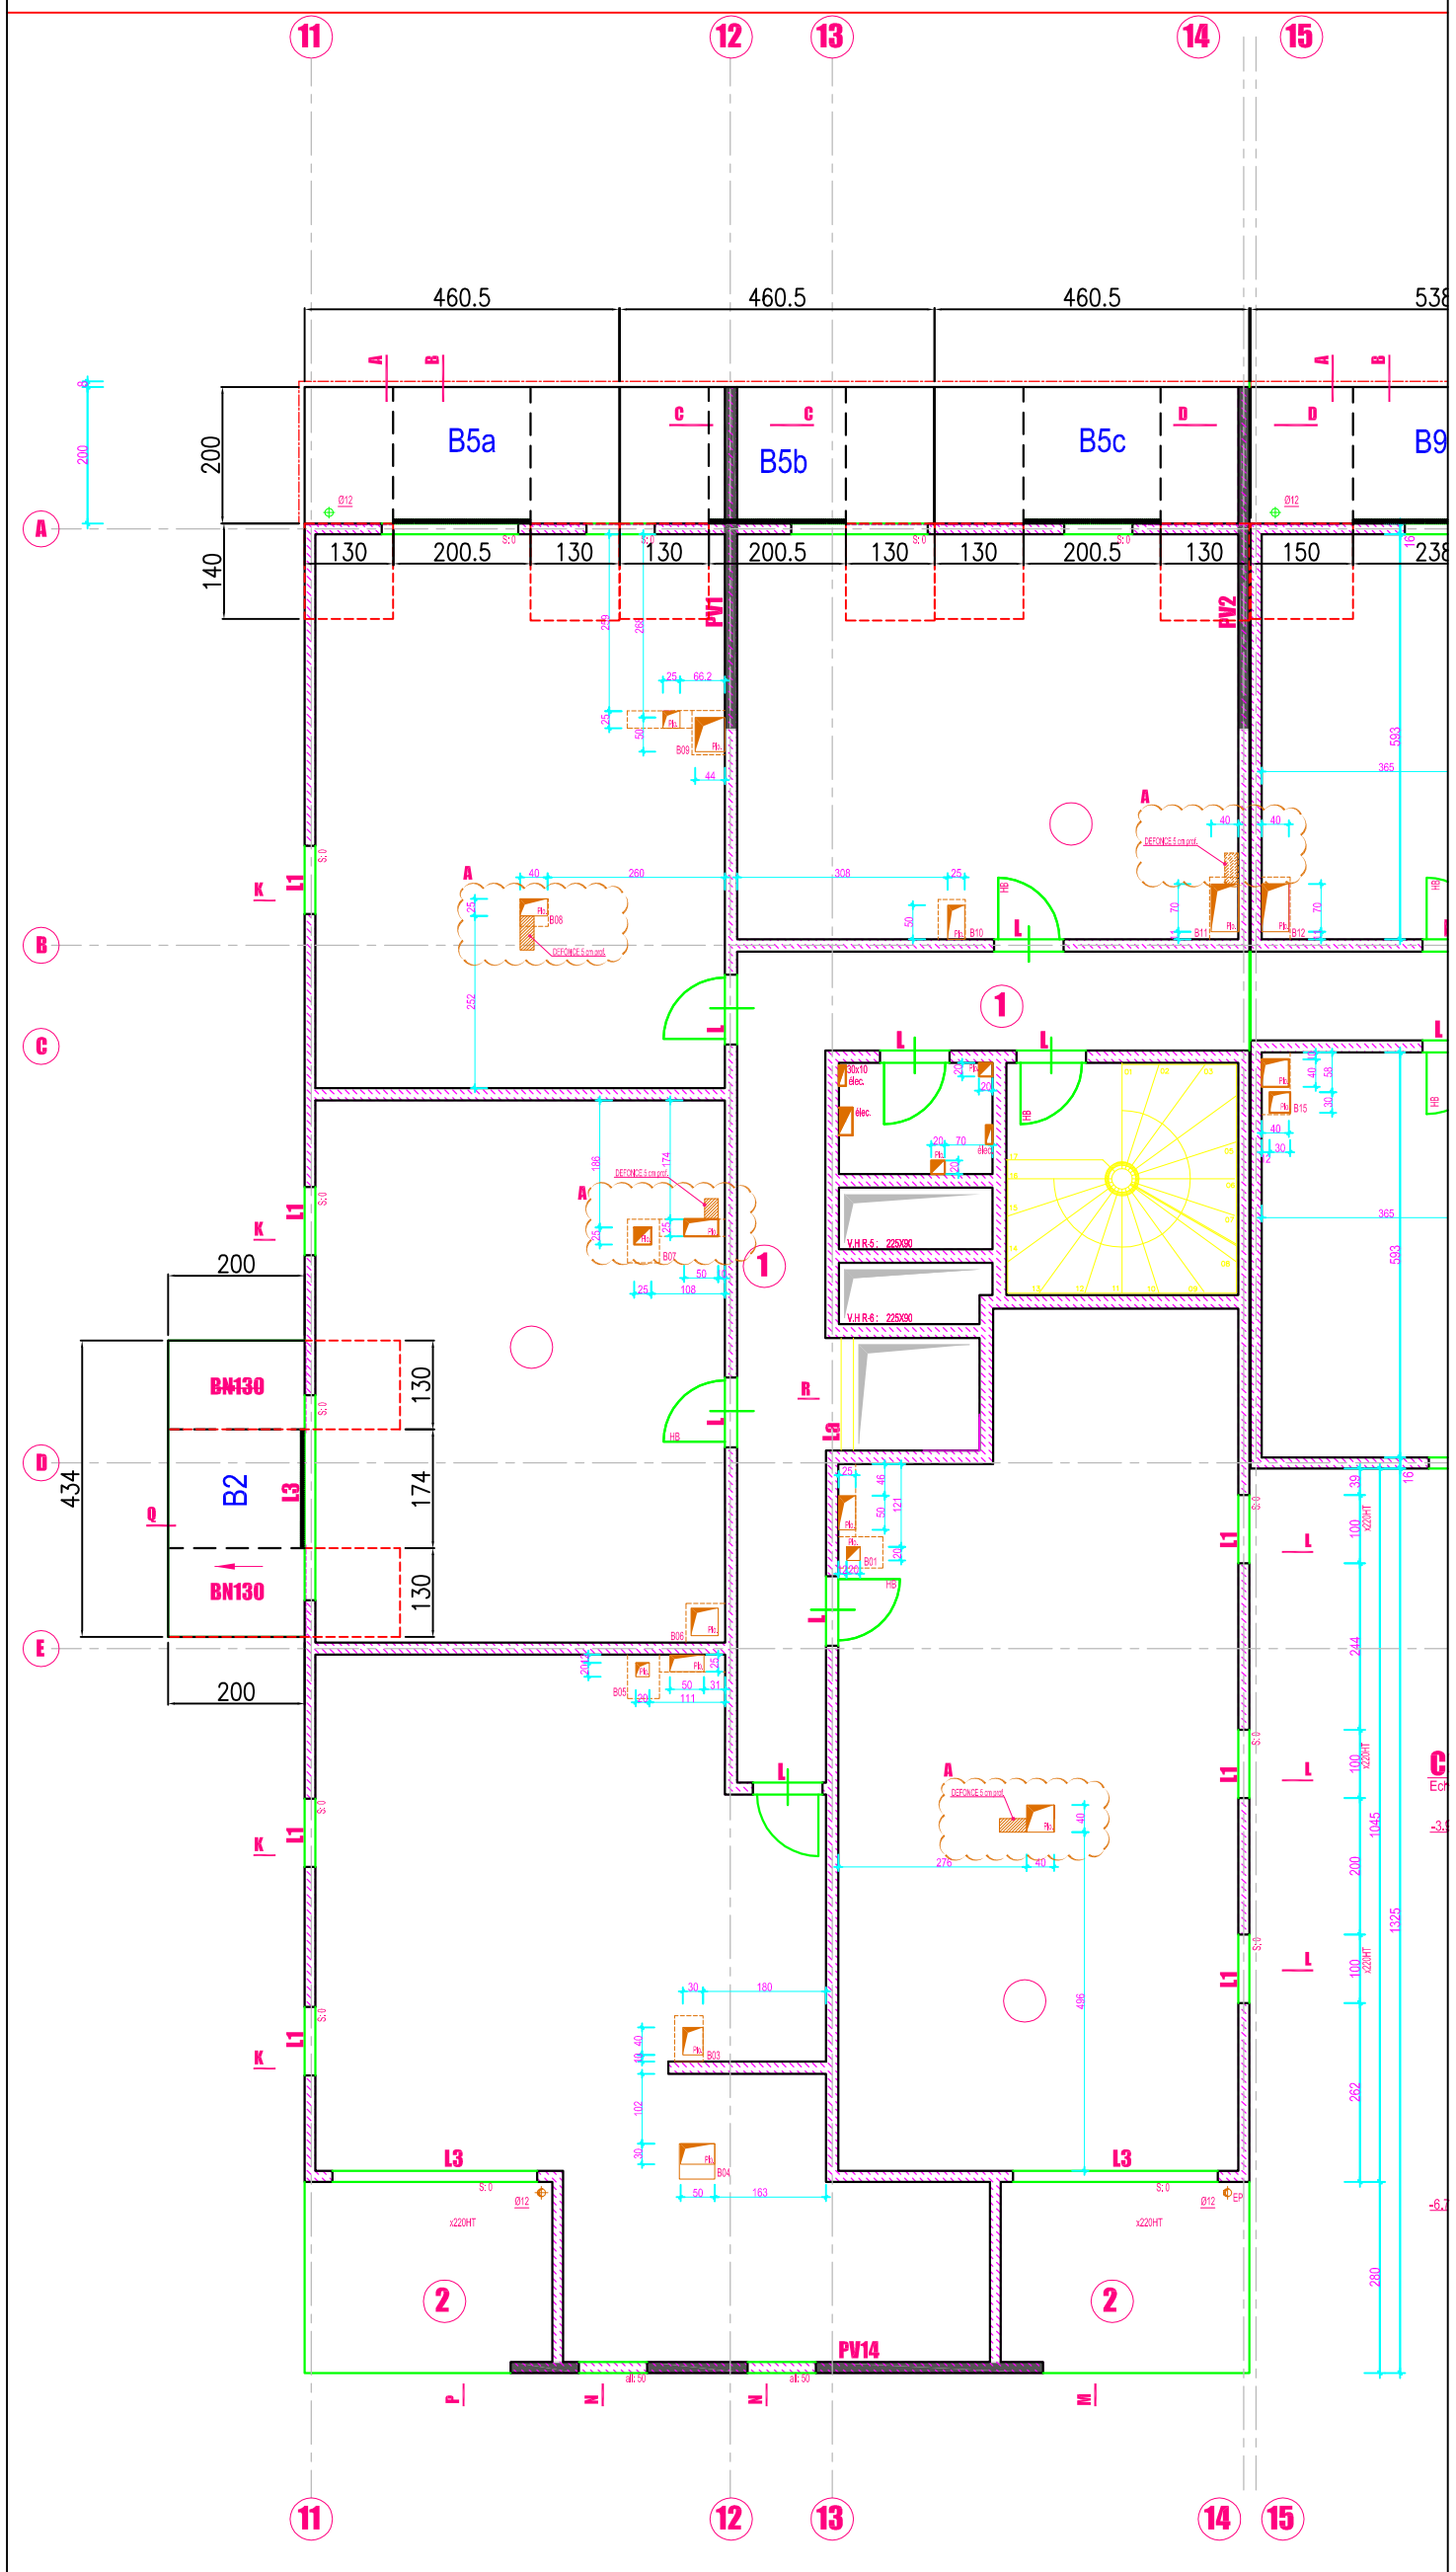

MOULE	N	NC	observations	BETON	N	NC	observations	FICHE AUTO-CONTROLE
Conformité moule			Dimensions	Conformité béton				Opérateur :
Etat du moule			Armature	Mise en place				Responsable prod :
Propreté et huilage			Inserts	Aspect de surface				Date :


Ent. FONTANEL				 PLATTARD S.A.S.		PLAN DE FABRCATION		Surface: 8.68 m²		POIDS		REPERE		Nbr	
LA MULATIERE		Elément: BALCONS				coffrage / ferrailage		Volume: 1.65 m3		3.95 T		B2		1	

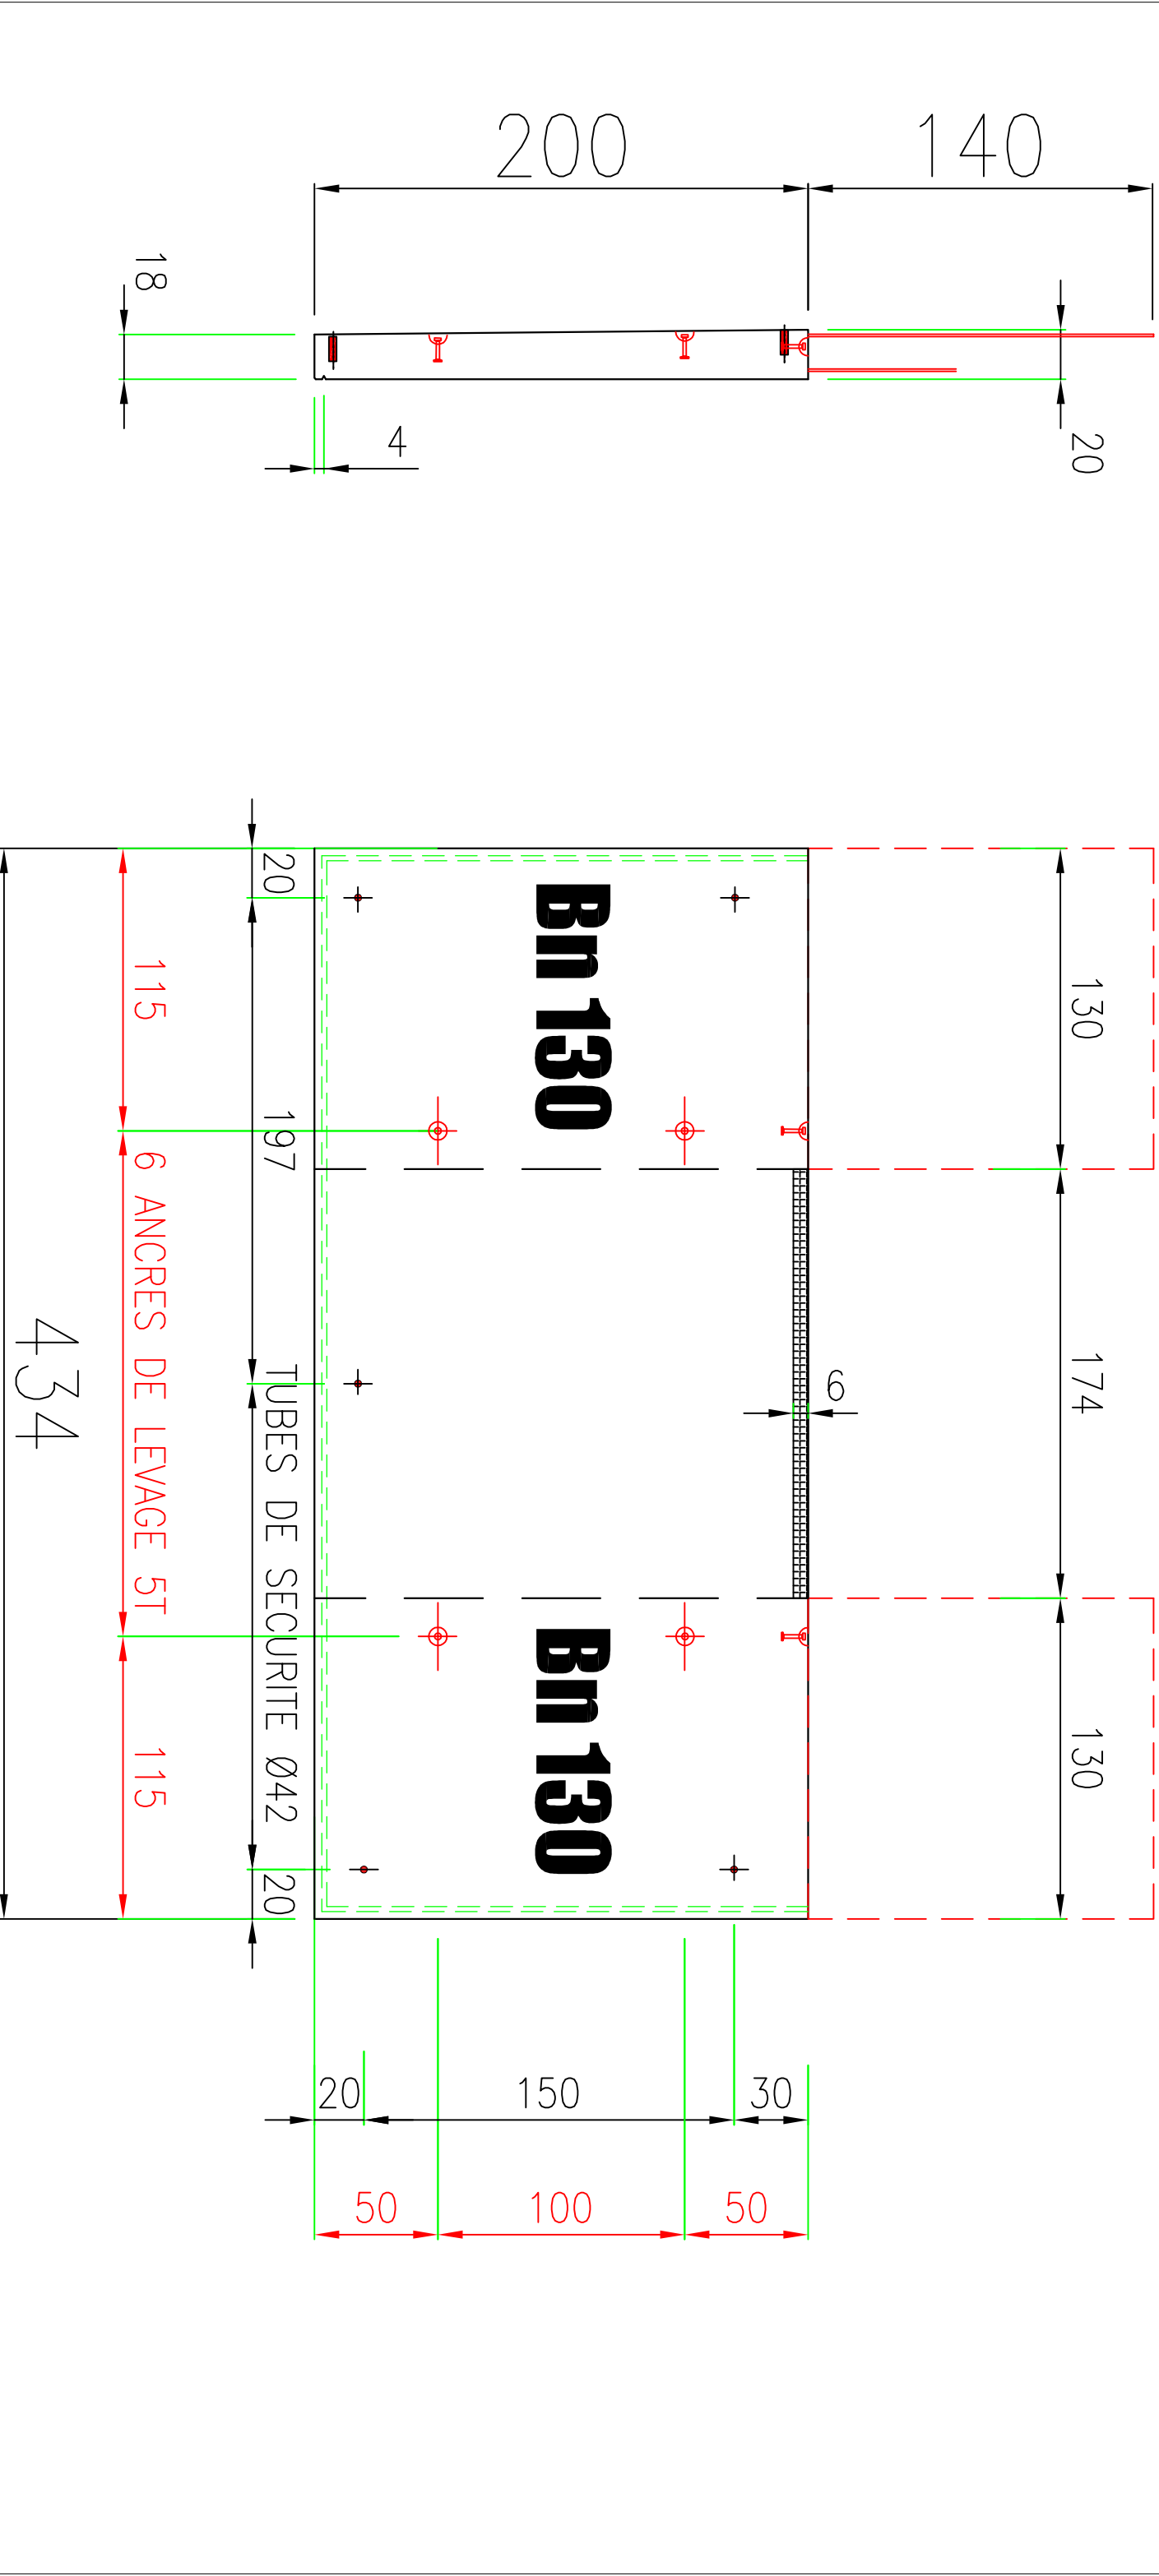

LEVAGE		INSERTS		INSERTS		INSERTS		INSERTS	
	Douille Ø		Ancre Frimeda T		EBA		TP - JV	DATE: 22/12/2015	
	Douille Ø		Renfort Ø		Douille étaielement		PVC Ø80	Plan N°	
	Renfort Ø dx		Trifer		Ankrobox Ø50		Tube garde-corps	Indice	Page N°

MOULE	N	NC	observations	CONTRÔLE	N	NC	observations	BETON	N	NC	observations	FICHE AUTO-CONTROLÉ
Conformité moule				Dimensions				Conformité béton				Opérateur :
Etat du moule				Armature				Mise en place				Responsable prod :
Propreté et huilage				Inserts				Aspect de surface				Date :


Ent. FONTANEL									
LA MULATIERE		Elément: BALCONS		coffrage / ferrailage		 PLATTARD S.A.S.		PLAN DE FABRCATION	
Surface:		9.21 m²		POIDS		REPERE		Nbr	
Volume:		1.70 m3		4.10 T		B5a		1	

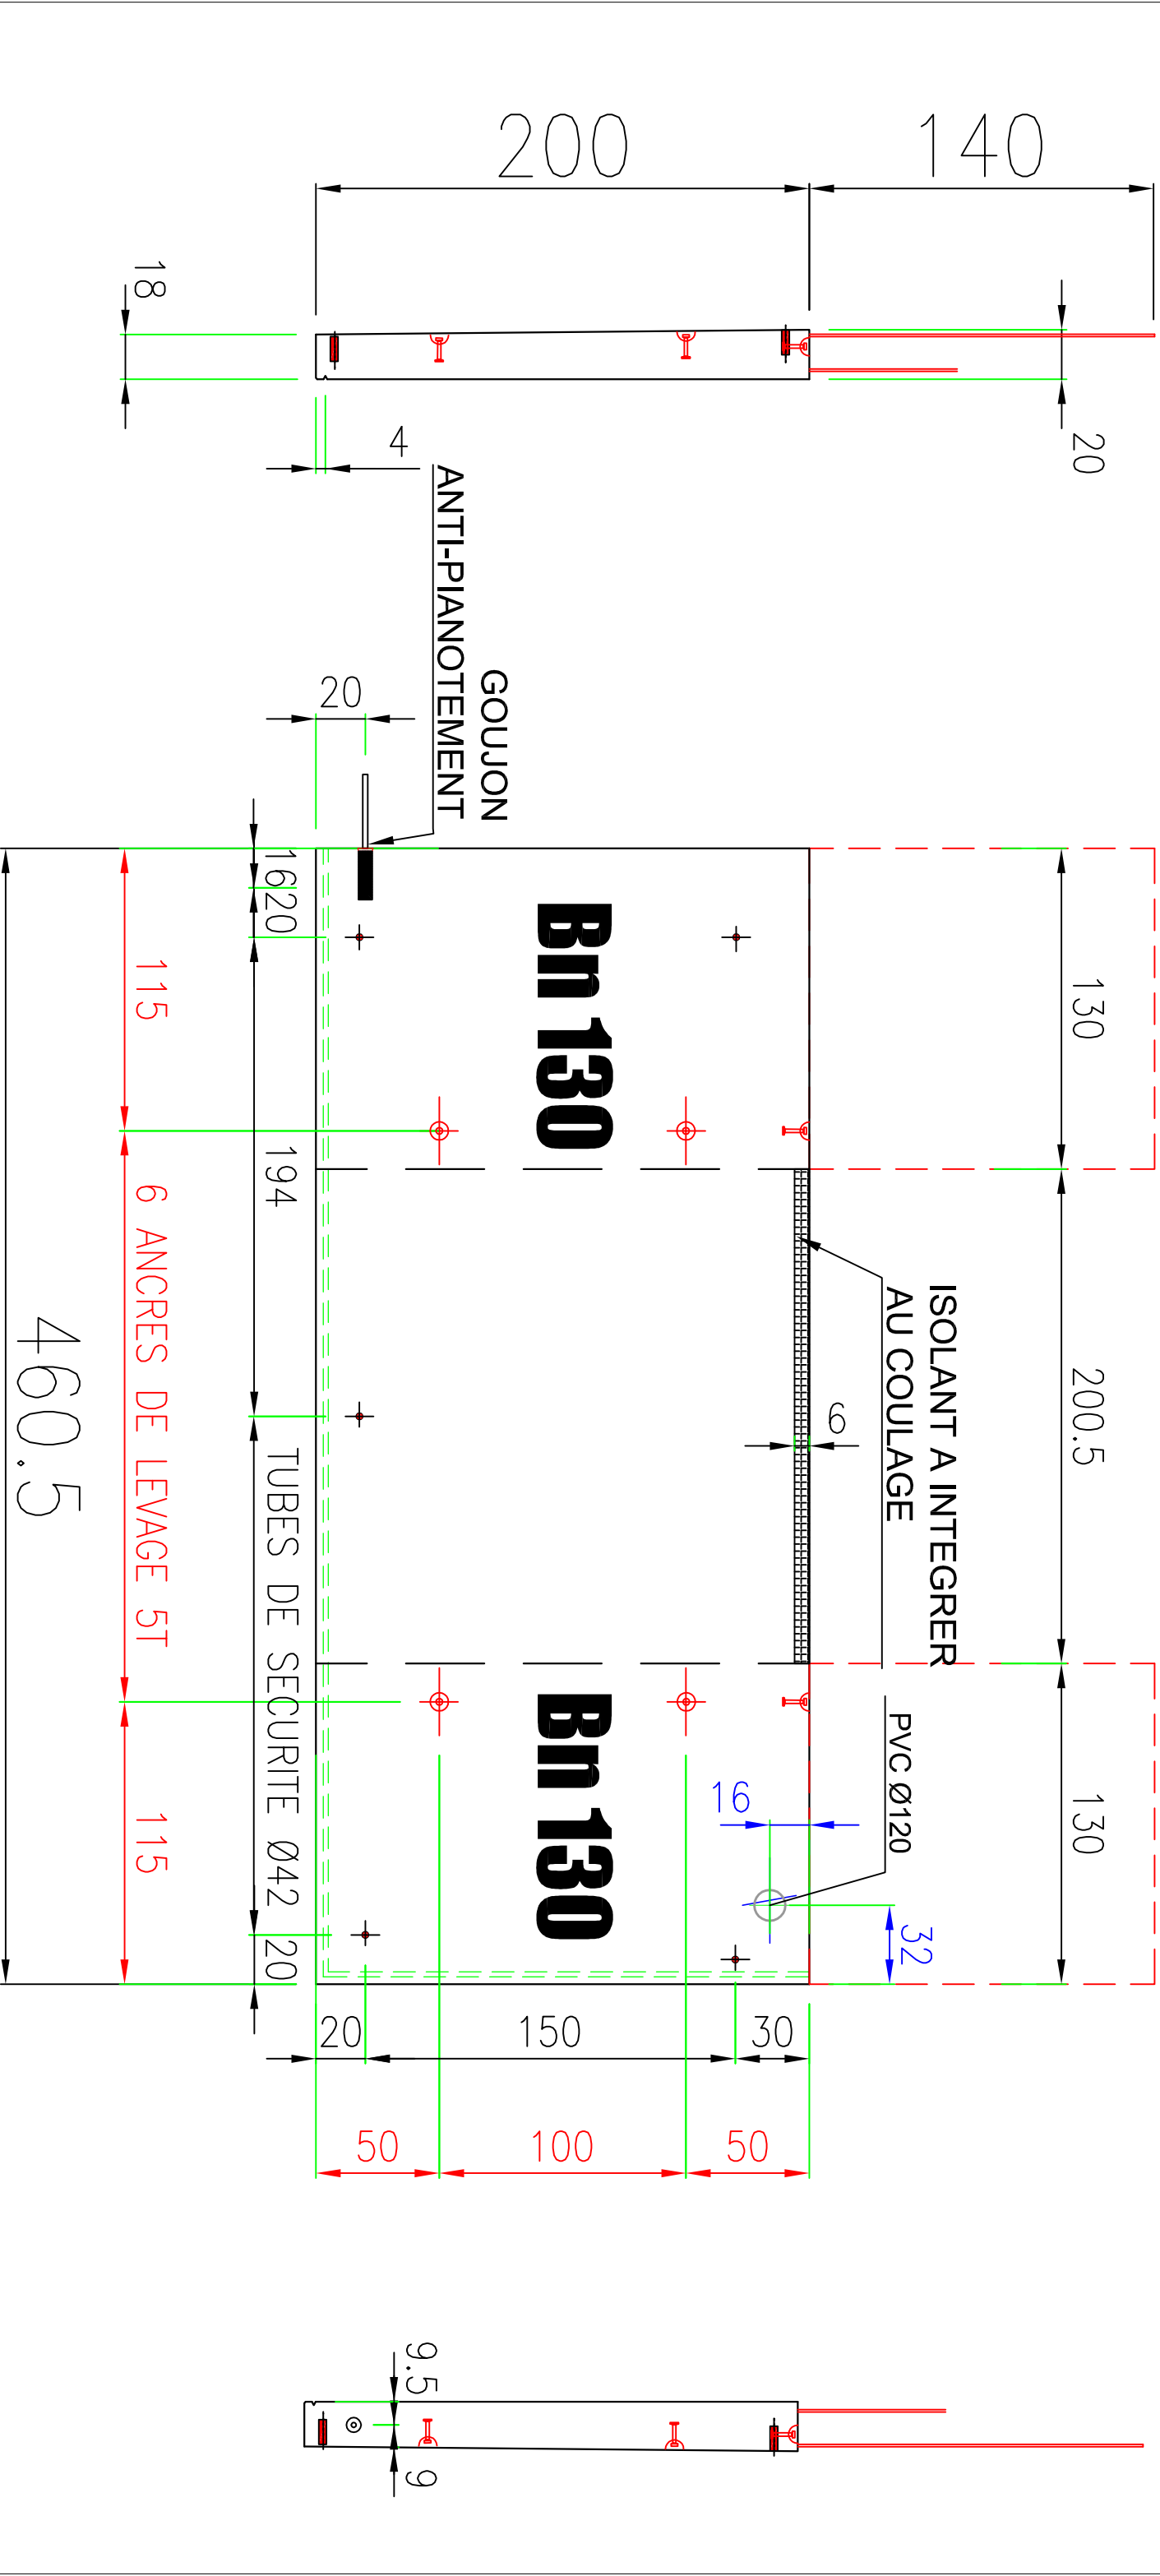

LEVAGE			INSERTS			INSERTS			INSERTS		
	Douille Ø			Ancre Frimeda T			EBA			TP - JV	DATE: 11/12/2015
	Douille Ø			Renfort Ø			Douille étalement			PVC Ø80	Plan N°
	Renfort Ø dx			Trifer			Ankrobox Ø50			Tube garde-corps	Indice
									Page N°		

FICHE AUTO-CONTROLE											
MOULE	N	NC	observations	CONTROLE	N	NC	observations	BETON	N	NC	observations
Conformité moule				Dimensions				Conformité béton			
Etat du moule				Armature				Mise en place			
Propreté et huilage				Inserts				Aspect de surface			
											Date :
											Responsable prod :
											Opérateur :

Ent. FONTANEL				 PLATTARD S.A.S.		PLAN DE FABRICATION	
LA MULATIERE		coffrage / ferrailage					
Elément: BALCONS		Surface: 9.21 m²		POIDS		REPERE	
		Volume: 1.70 m3		4.10 T		Nbr	
						B5c	
						1	

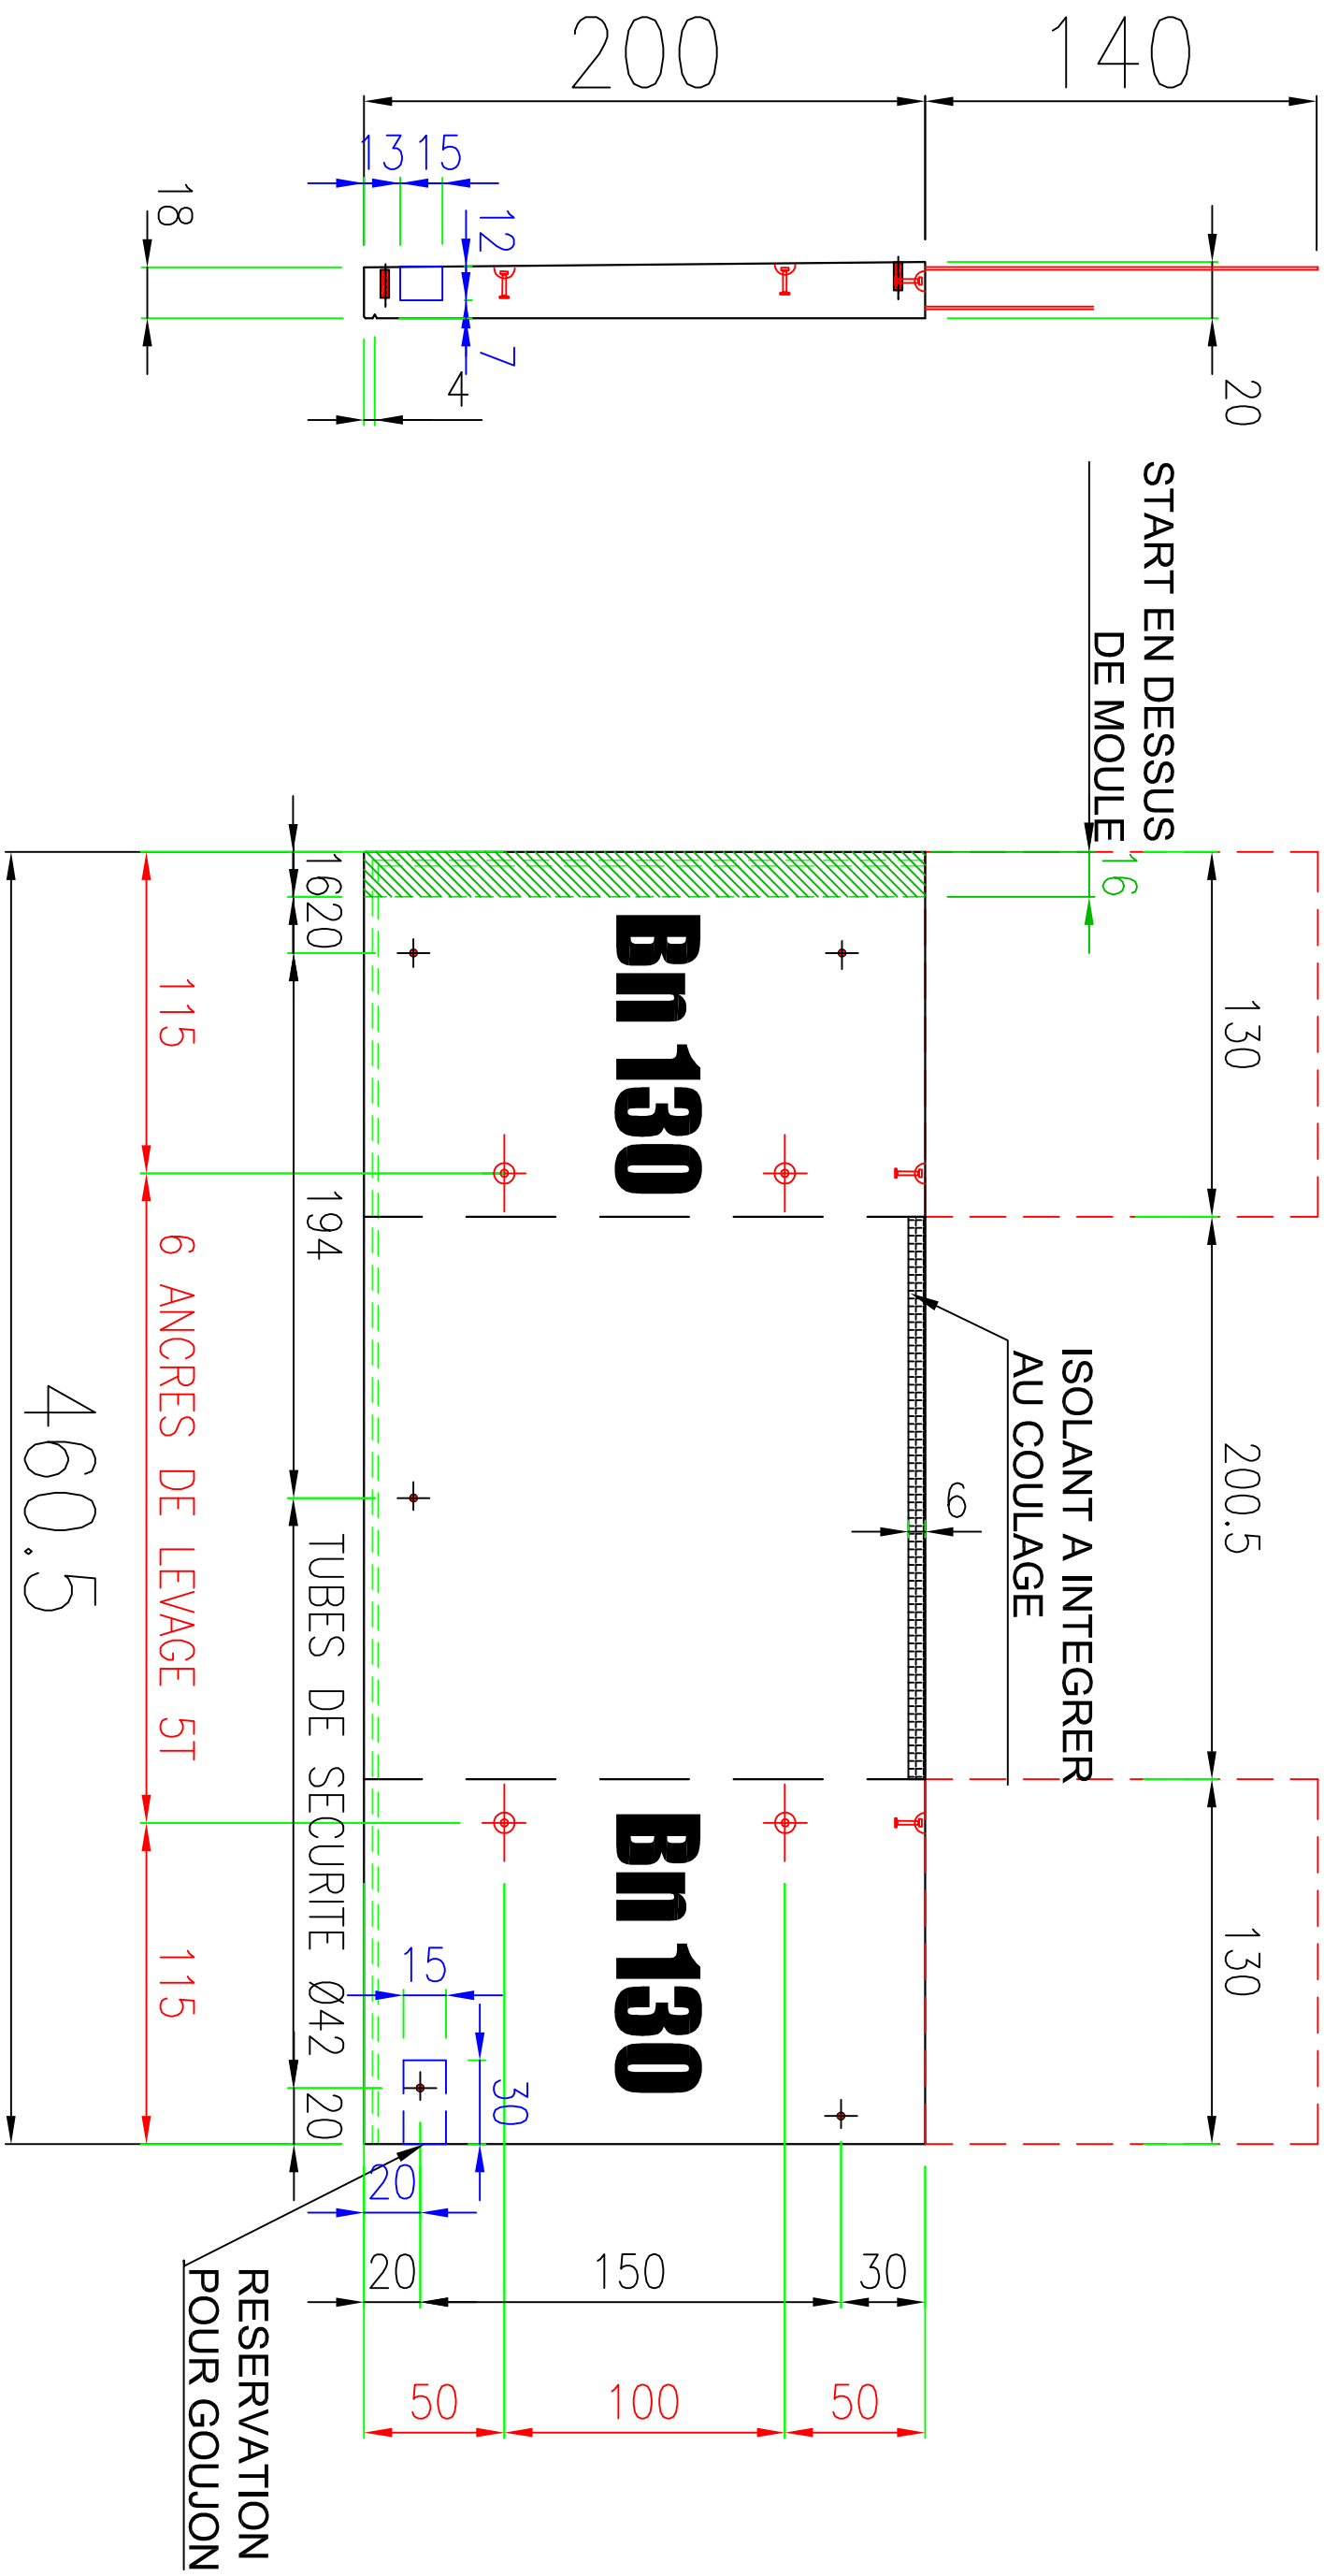

LEVERAGE									
	Douille Ø								
	Douille Ø								
	Renfort Ø dx								
INSERTS									
	Ancre Frimeda T								
	Renfort Ø								
	Trifer								
INSERTS									
	EBA								
	Douille étalement								
	Ankrobox Ø50								
INSERTS									
	TP - JV								
	PVC Ø80								
	Tube garde-corps								
DATE: 11/12/2015									
Plan N°			Page N°						
Indice									