

FONTANEL- LE 180°

69 LA MULATIERE

BALCONS DU NIVEAU N-3 suite
BAT B

N

EXE

Indice	Date	Designation des Modifications	Date :
A	07/04/2016	MODIFICATION BALCON B7	30/03/2016
B			Affaire :
C			
D			Echelle :
E			
F			
G			
H			
I			

Type béton = B35 XF1
Aciers H.A et T.S = Fe E 500
Enrobage des armatures = ENR_CARMAT
Manutention = Tonnes

BUREAU D'ETUDE
PLATTARD SAS
414 Avenue de la
plage
BP 119
69540
Villefrance-sur-Saône
Tél: 04 74 02 20 20
Fax: 04 74 62 26 62



Ce plan est la propriété intellectuelle de la PLATTARD SAS, il ne peut être reproduit sans son autorisation.

NOAHO

Chemin de Fontanière - 69350 La Mulatière

Création de logements

Les entreprises réalisant les travaux devront tenir compte des derniers plans architecte lors de la réalisation des travaux
Les plans du be MATTE ne doivent servir qu'au corps d'état concerné et doivent être des plans d'exécution.

ARCHITECTE(S): ATELIER DE LA PASSERELLE

BET STRUCTURE: MATTE SAS

BET FLUIDES: PRELEM

ECONOMISTE: EXECO

BUREAU DE CONTROLE: Bureau VERITAS

MO DELEGUE:

MOE: PSO Ingénierie

CSPS: SUD EST COORDINATION

OPC:

ENTREPRISE(S): Fontanel-pbc

Bât: B
PLANCHER sur -3
Coffrage

EXE

Contrainte de sol:

Aciers HA (T) FeE500

Aciers Doux (Ø) FeE 235

Aciers TS FeE 500

Béton fc28 >= 25MPa

Enrobage = 3 cm

PLAN N°
B22 0

DATE : 19/11/2015

MATTÉ
BUREAU D'ÉTUDES
STRUCTURES ET FLUIDES

119 BOULEVARD STALINGRAD 69100 VILLEURBANNE

Tél. 04 72 44 02 87 Fax 04 72 44 26 59

E-mail : bet@matte.fr

Dessiné par : J.BO


Contrôlé par : P.LIN

Echelle : 1/50°

Affaire N°
13.12.119


Plancher Niveau R-3

BAT. B suite

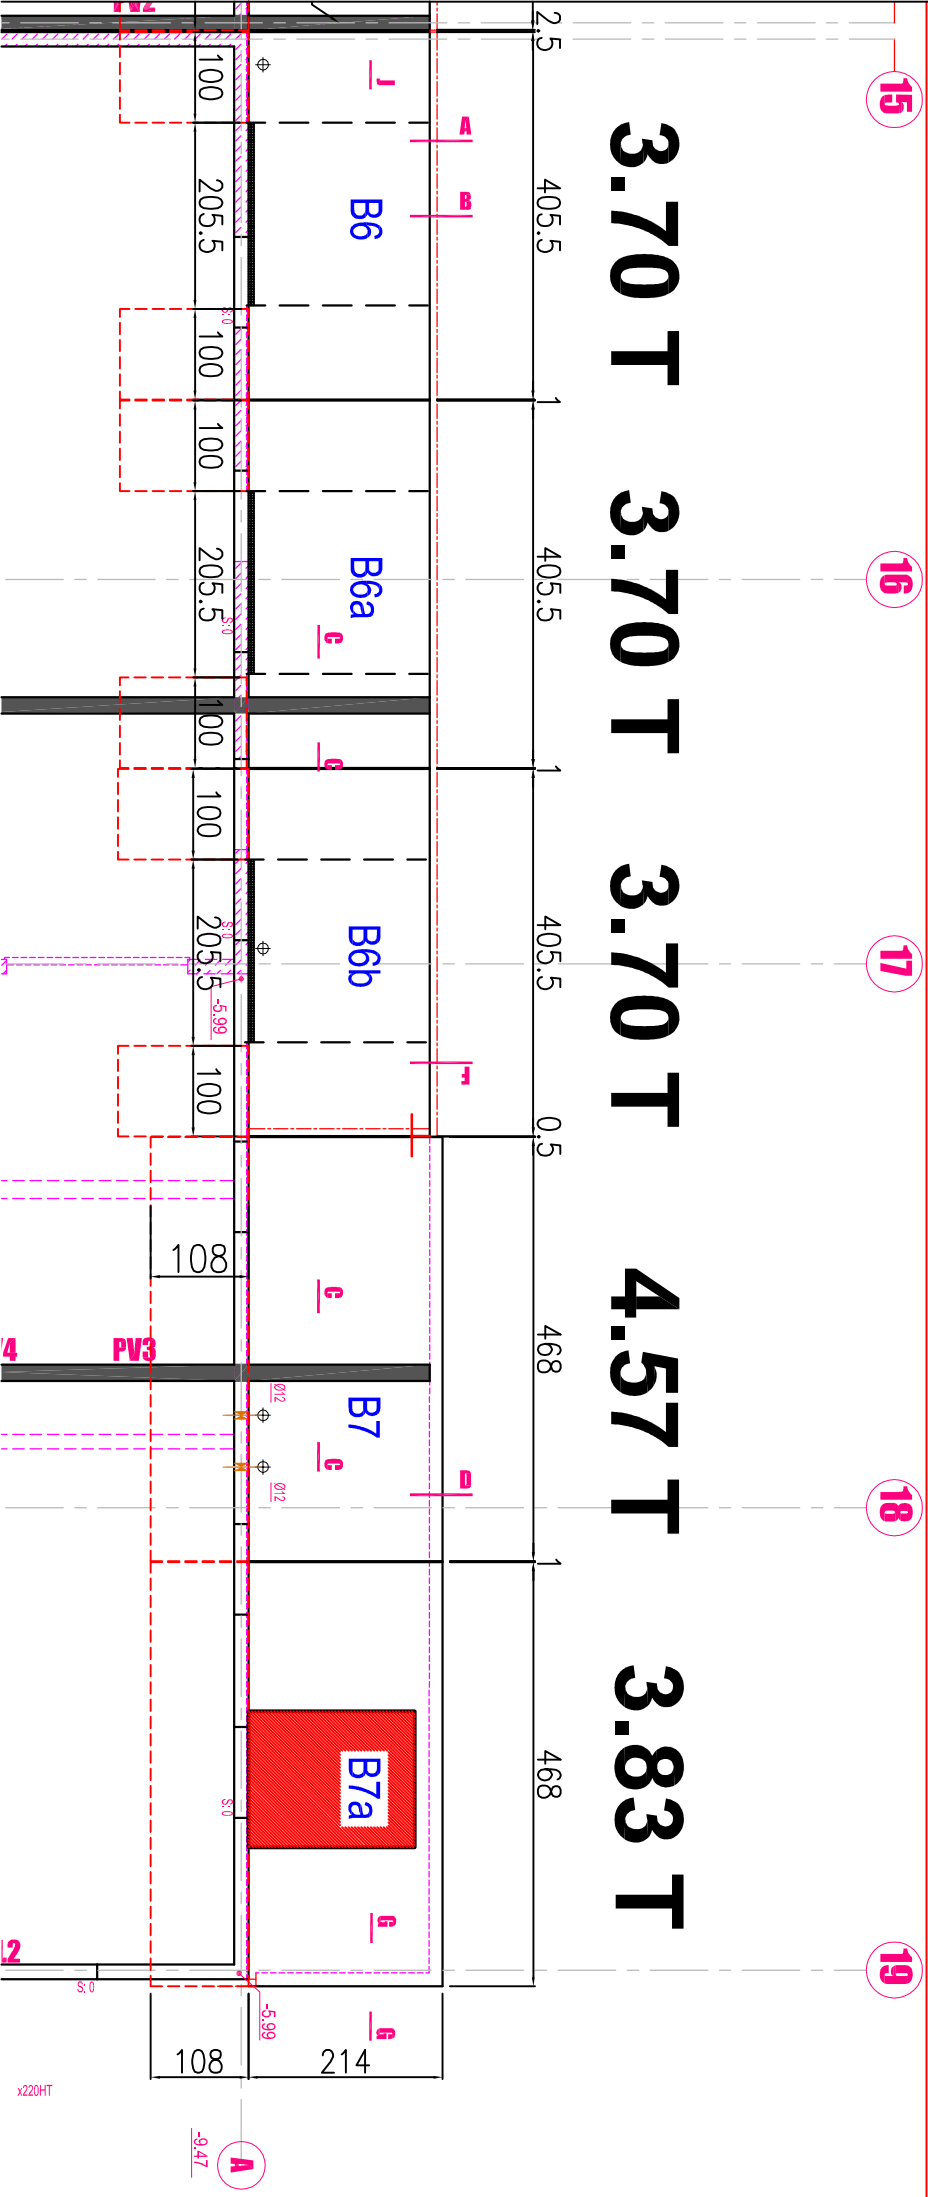

MOULE	N	NC	observations	CONTROLE	N	NC	observations	BETON	N	NC	observations	FICHE AUTO-CONTROLE
Conformité moule				Dimensions				Conformité béton				Opérateur :
Etat du moule				Armature				Mise en place				Responsable prod :
Propreté et huilage				Inserts				Aspect de surface				Date :


Ent. FONTANEL		Elément: BALCONS		 PLATTARD S.A.S.		PLAN DE FABRICATION		Surface: 8.11 m²		POIDS		REPERE		Nbr	
LA MULATIERE		coffrage / ferrillage				Volume: 1.54 m3		3.70 T		B6		1			

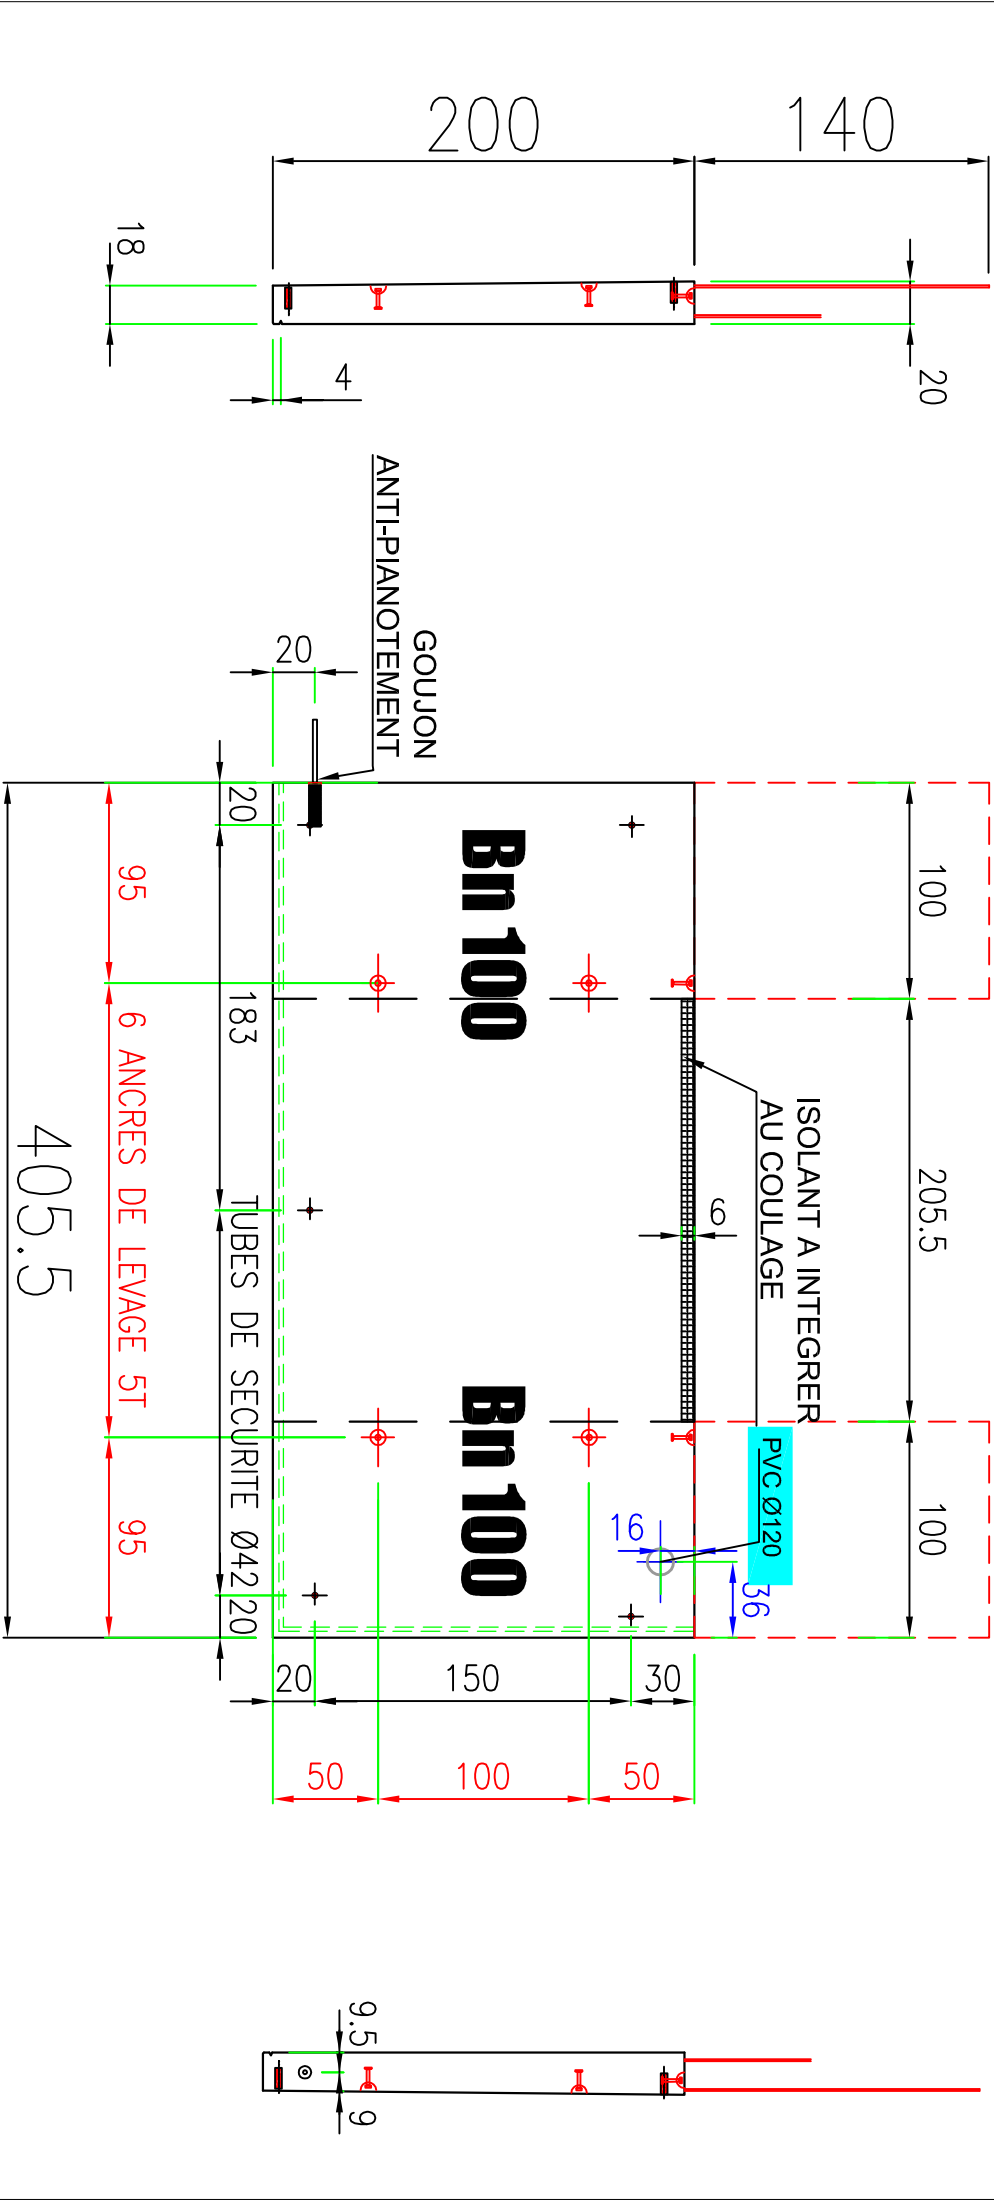

LEVAGE				INSERTS				INSERTS				INSERTS			
	Douille Ø		Renfort Ø dx		Ancre Frimeda T		Trifler		EBA		Douille étalement		TP - JV		DATE: 11/12/2015
	Douille Ø		Renfort Ø		Renfort Ø		Trifler		Ankrobox Ø50		Douille étalement		PVC Ø80		Plan N°
	Douille Ø		Renfort Ø		Trifler		Trifler		Ankrobox Ø50		Douille étalement		Tube garde-corps		Indice
	Douille Ø		Renfort Ø		Trifler		Trifler		Ankrobox Ø50		Douille étalement		Tube garde-corps		Indice

MOULE	N	NC	observations	CONTROLE	N	NC	observations	BETON	N	NC	observations	FICHE AUTO-CONTROLE
Conformité moule				Dimensions				Conformité béton				Opérateur :
Etat du moule				Armature				Mise en place				Responsable prod :
Propreté et huilage				Inserts				Aspect de surface				Date :


Ent. FONTANEL		Elément: BALCONS		 PLATTARD S.A.S.		PLAN DE FABRCATION		Surface: 8.11 m²		POIDS		REPERE		Nbr	
LA MULATIERE		coffrage / ferrillage				Volume: 1.54 m3		3.70 T		B6b		1			

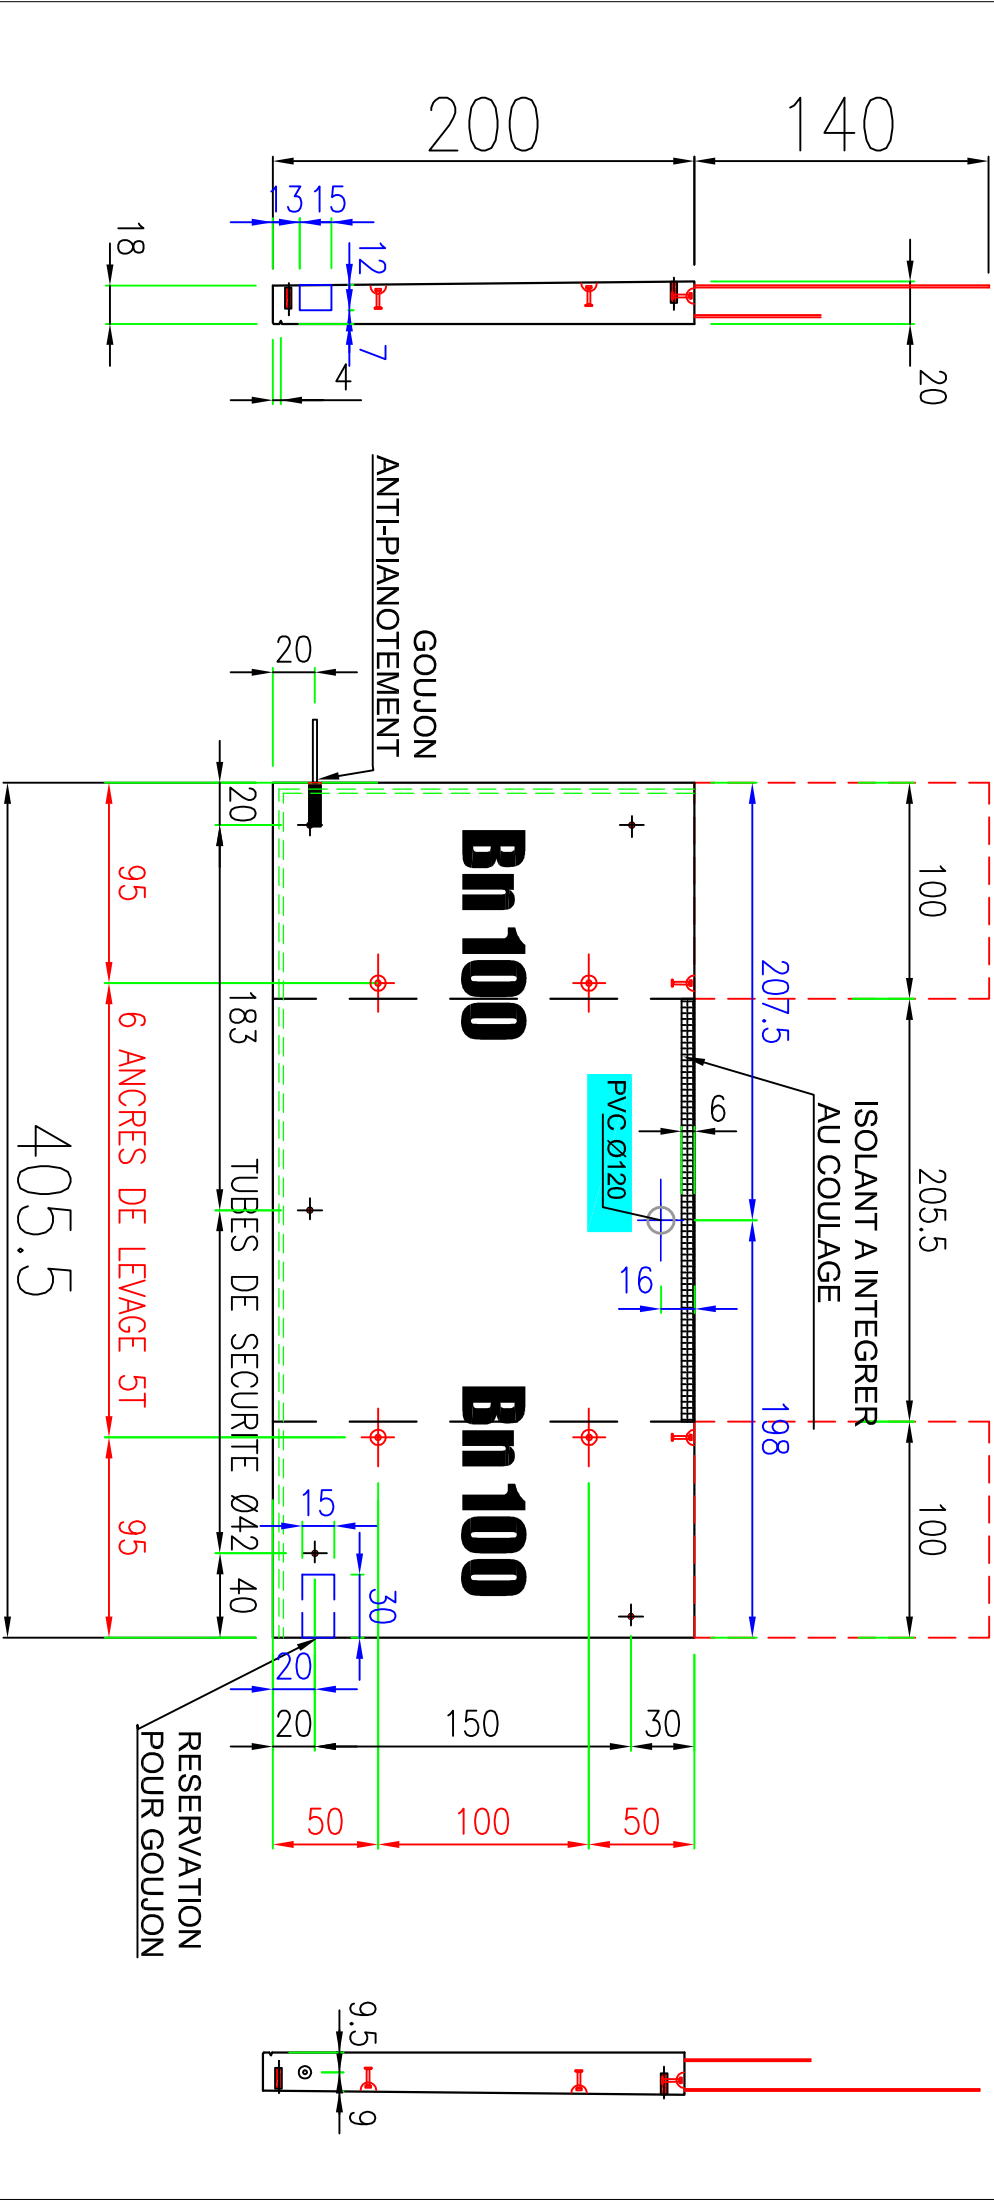

LEVAGE			INSERTS			INSERTS			INSERTS			INSERTS		
	Douille Ø			Ancre Frimeda T			EBA			TP - JV	DATE: 11/12/2015			
	Douille Ø			Renfort Ø			Douille étalement			PVC Ø80	Plan N°			
	Renfort Ø dx			Trifler			Ankrobox Ø50			Tube garde-corps	Indice			

MOULE	N	NC	observations	CONTROLE	N	NC	observations	BETON	N	NC	observations	FICHE AUTO-CONTROLE
Conformité moule				Dimensions				Conformité béton				Opérateur :
Etat du moule				Armature				Mise en place				Responsable prod :
Propreté et huilage				Inserts				Aspect de surface				Date :


Ent. FONTANEL		Elément: BALCONS		 PLATTARD S.A.S.		PLAN DE FABRCATION		Surface: 10 m²		POIDS		REPERE		Nbr	
LA MULATIERE		coffrage / ferrillage				Volume: 1.90 m3		4.57 T		B7		1			

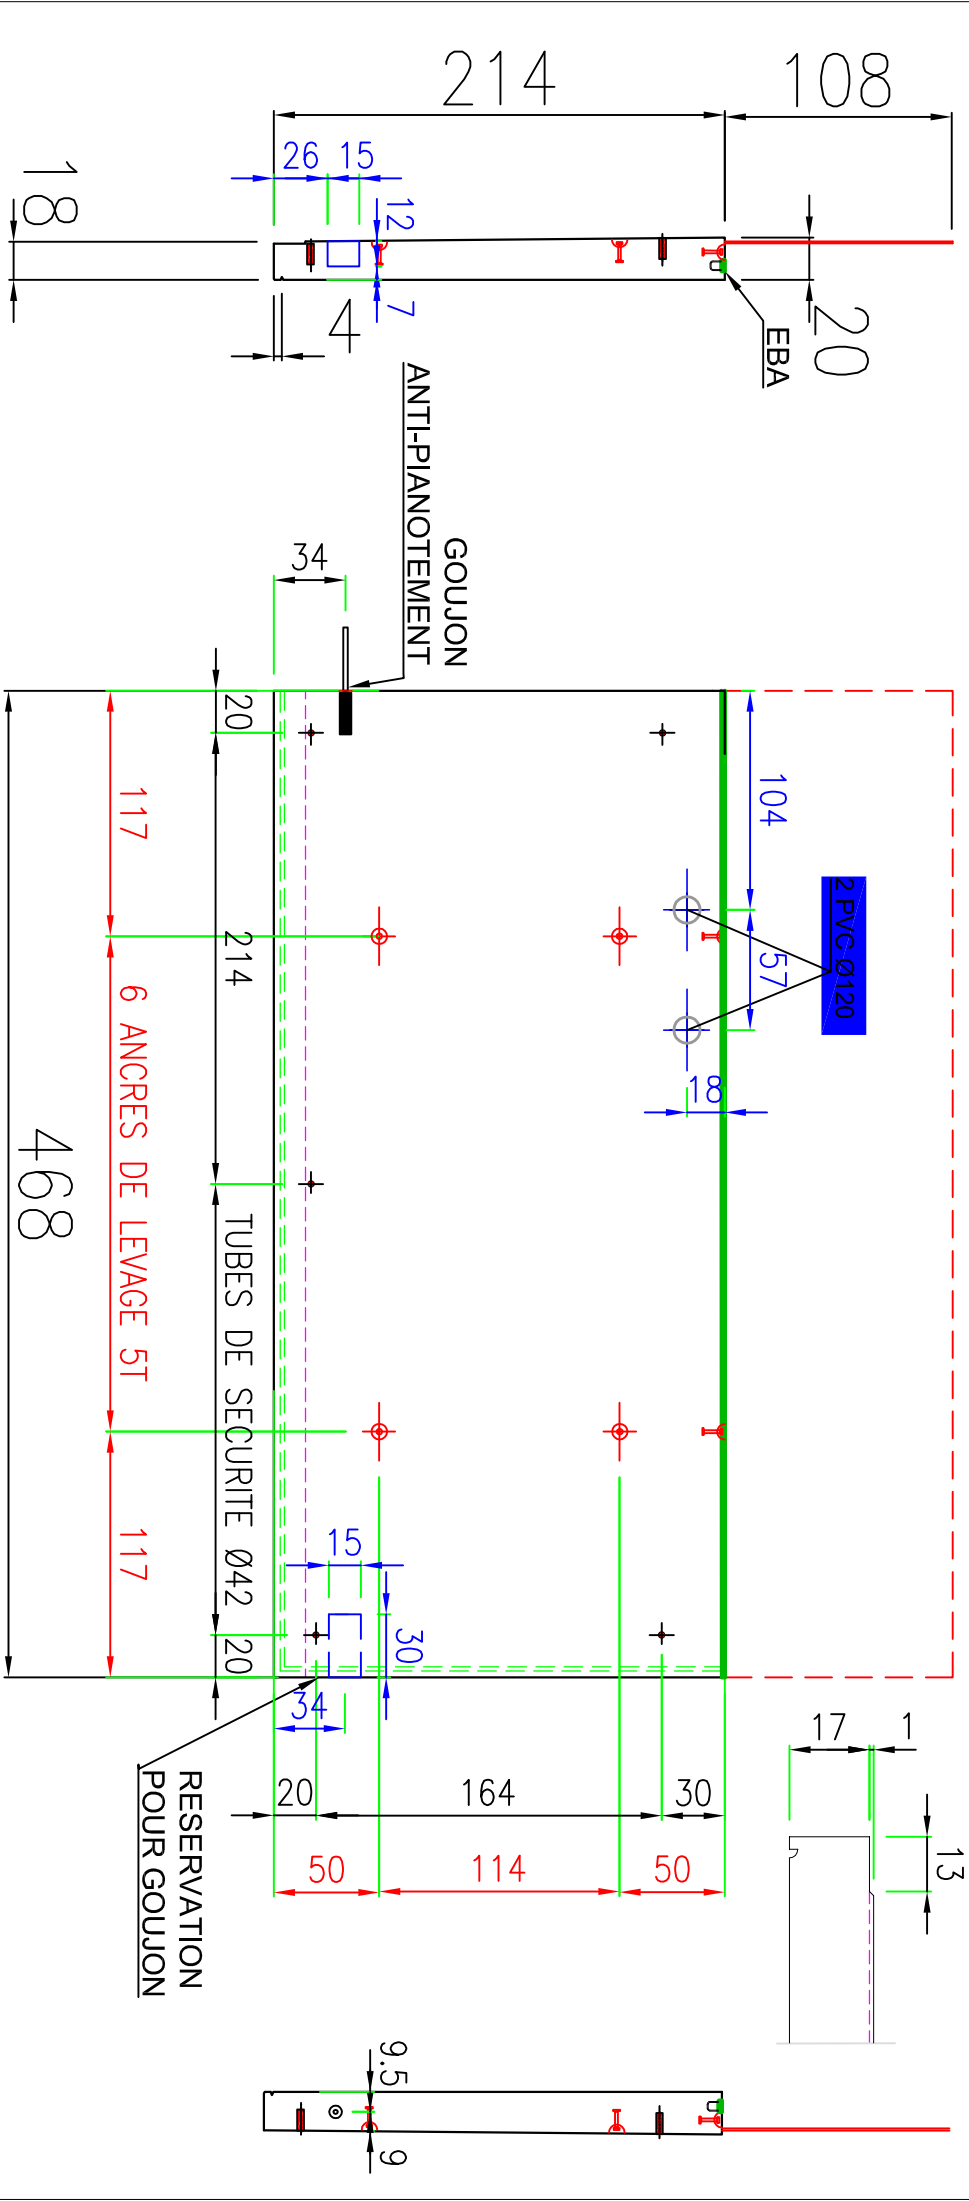

LEVAGE			INSERTS			INSERTS			INSERTS			INSERTS			DATE: 11/12/2015		
	Douille Ø			Ancre Frimeda T			EBA			TP - JV			PVC Ø80		Page N°		
	Douille Ø			Renfort Ø			Douille étalement										
	Renfort Ø dx			Trifier			Ankrobox Ø50			Tube garde-corps					Indice		

MOULE	N	NC	observations	CONTRÔLE	N	NC	observations	BETON	N	NC	observations	FICHE AUTO-CONTROLE
Conformité moule				Dimensions				Conformité béton				Opérateur :
Etat du moule				Armature				Mise en place				Responsable prod :
Propreté et huilage				Inserts				Aspect de surface				Date :

Ent. FONTANEL			Elément: BALCONS			PLATTARD S.A.S.			Surface: 10 m²		POIDS		REPÈRE	Nbr
LA MULATIERE			coffrage / ferrailage			PLAN DE FABRCATION			Volume: 1.60 m3		3.83 T		B7a	1

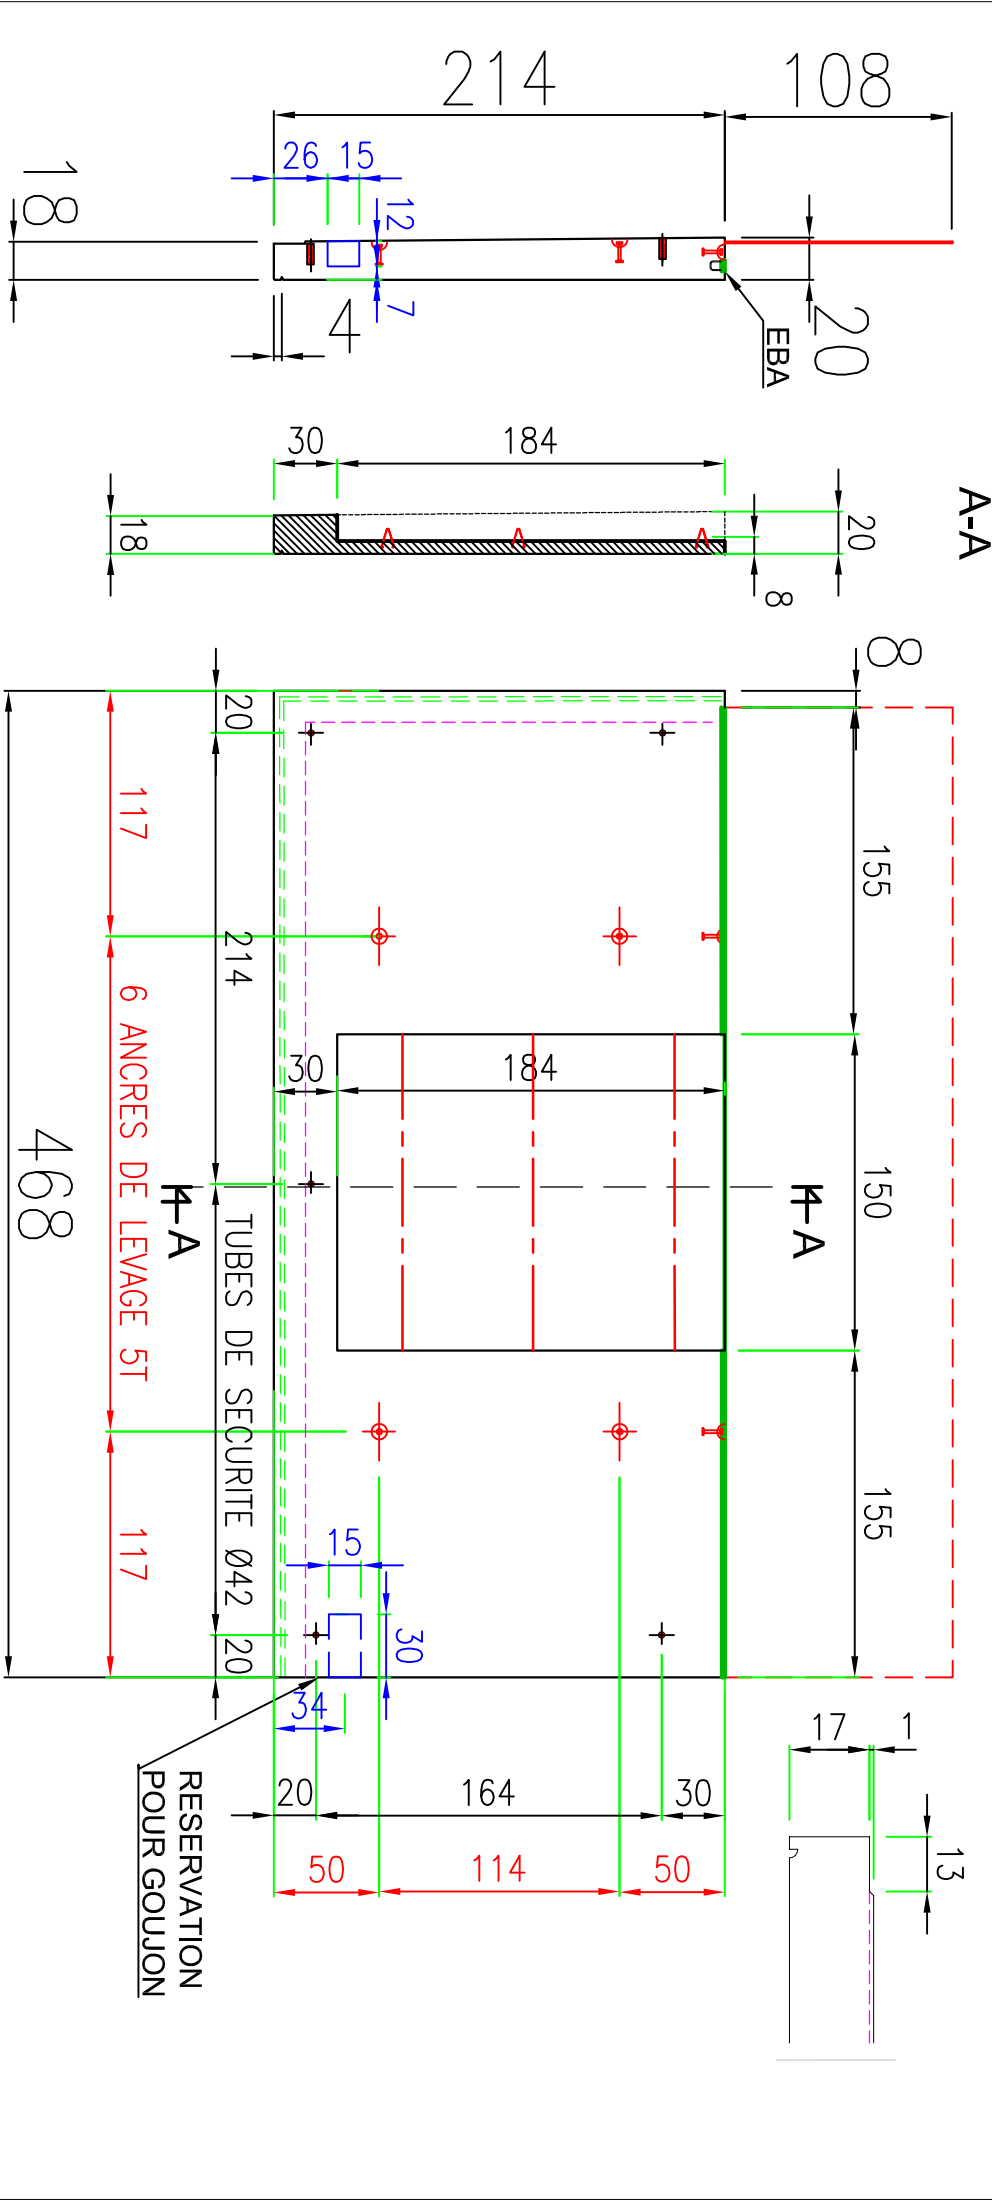

LEVAGE		INSERTS		INSERTS		INSERTS		INSERTS	
	Douille Ø		Ancre Frimeda T		EBA		TP - JV		DATE: 11/12/2015
	Douille Ø		Renfort Ø		Douille étalement		PVC Ø80		Plan N°
	Renfort Ø dx		Trifier		Ankrobox Ø50		Tube garde-corps		Indice
								Page N°	