




Plancher Niveau R-3

BAT. B

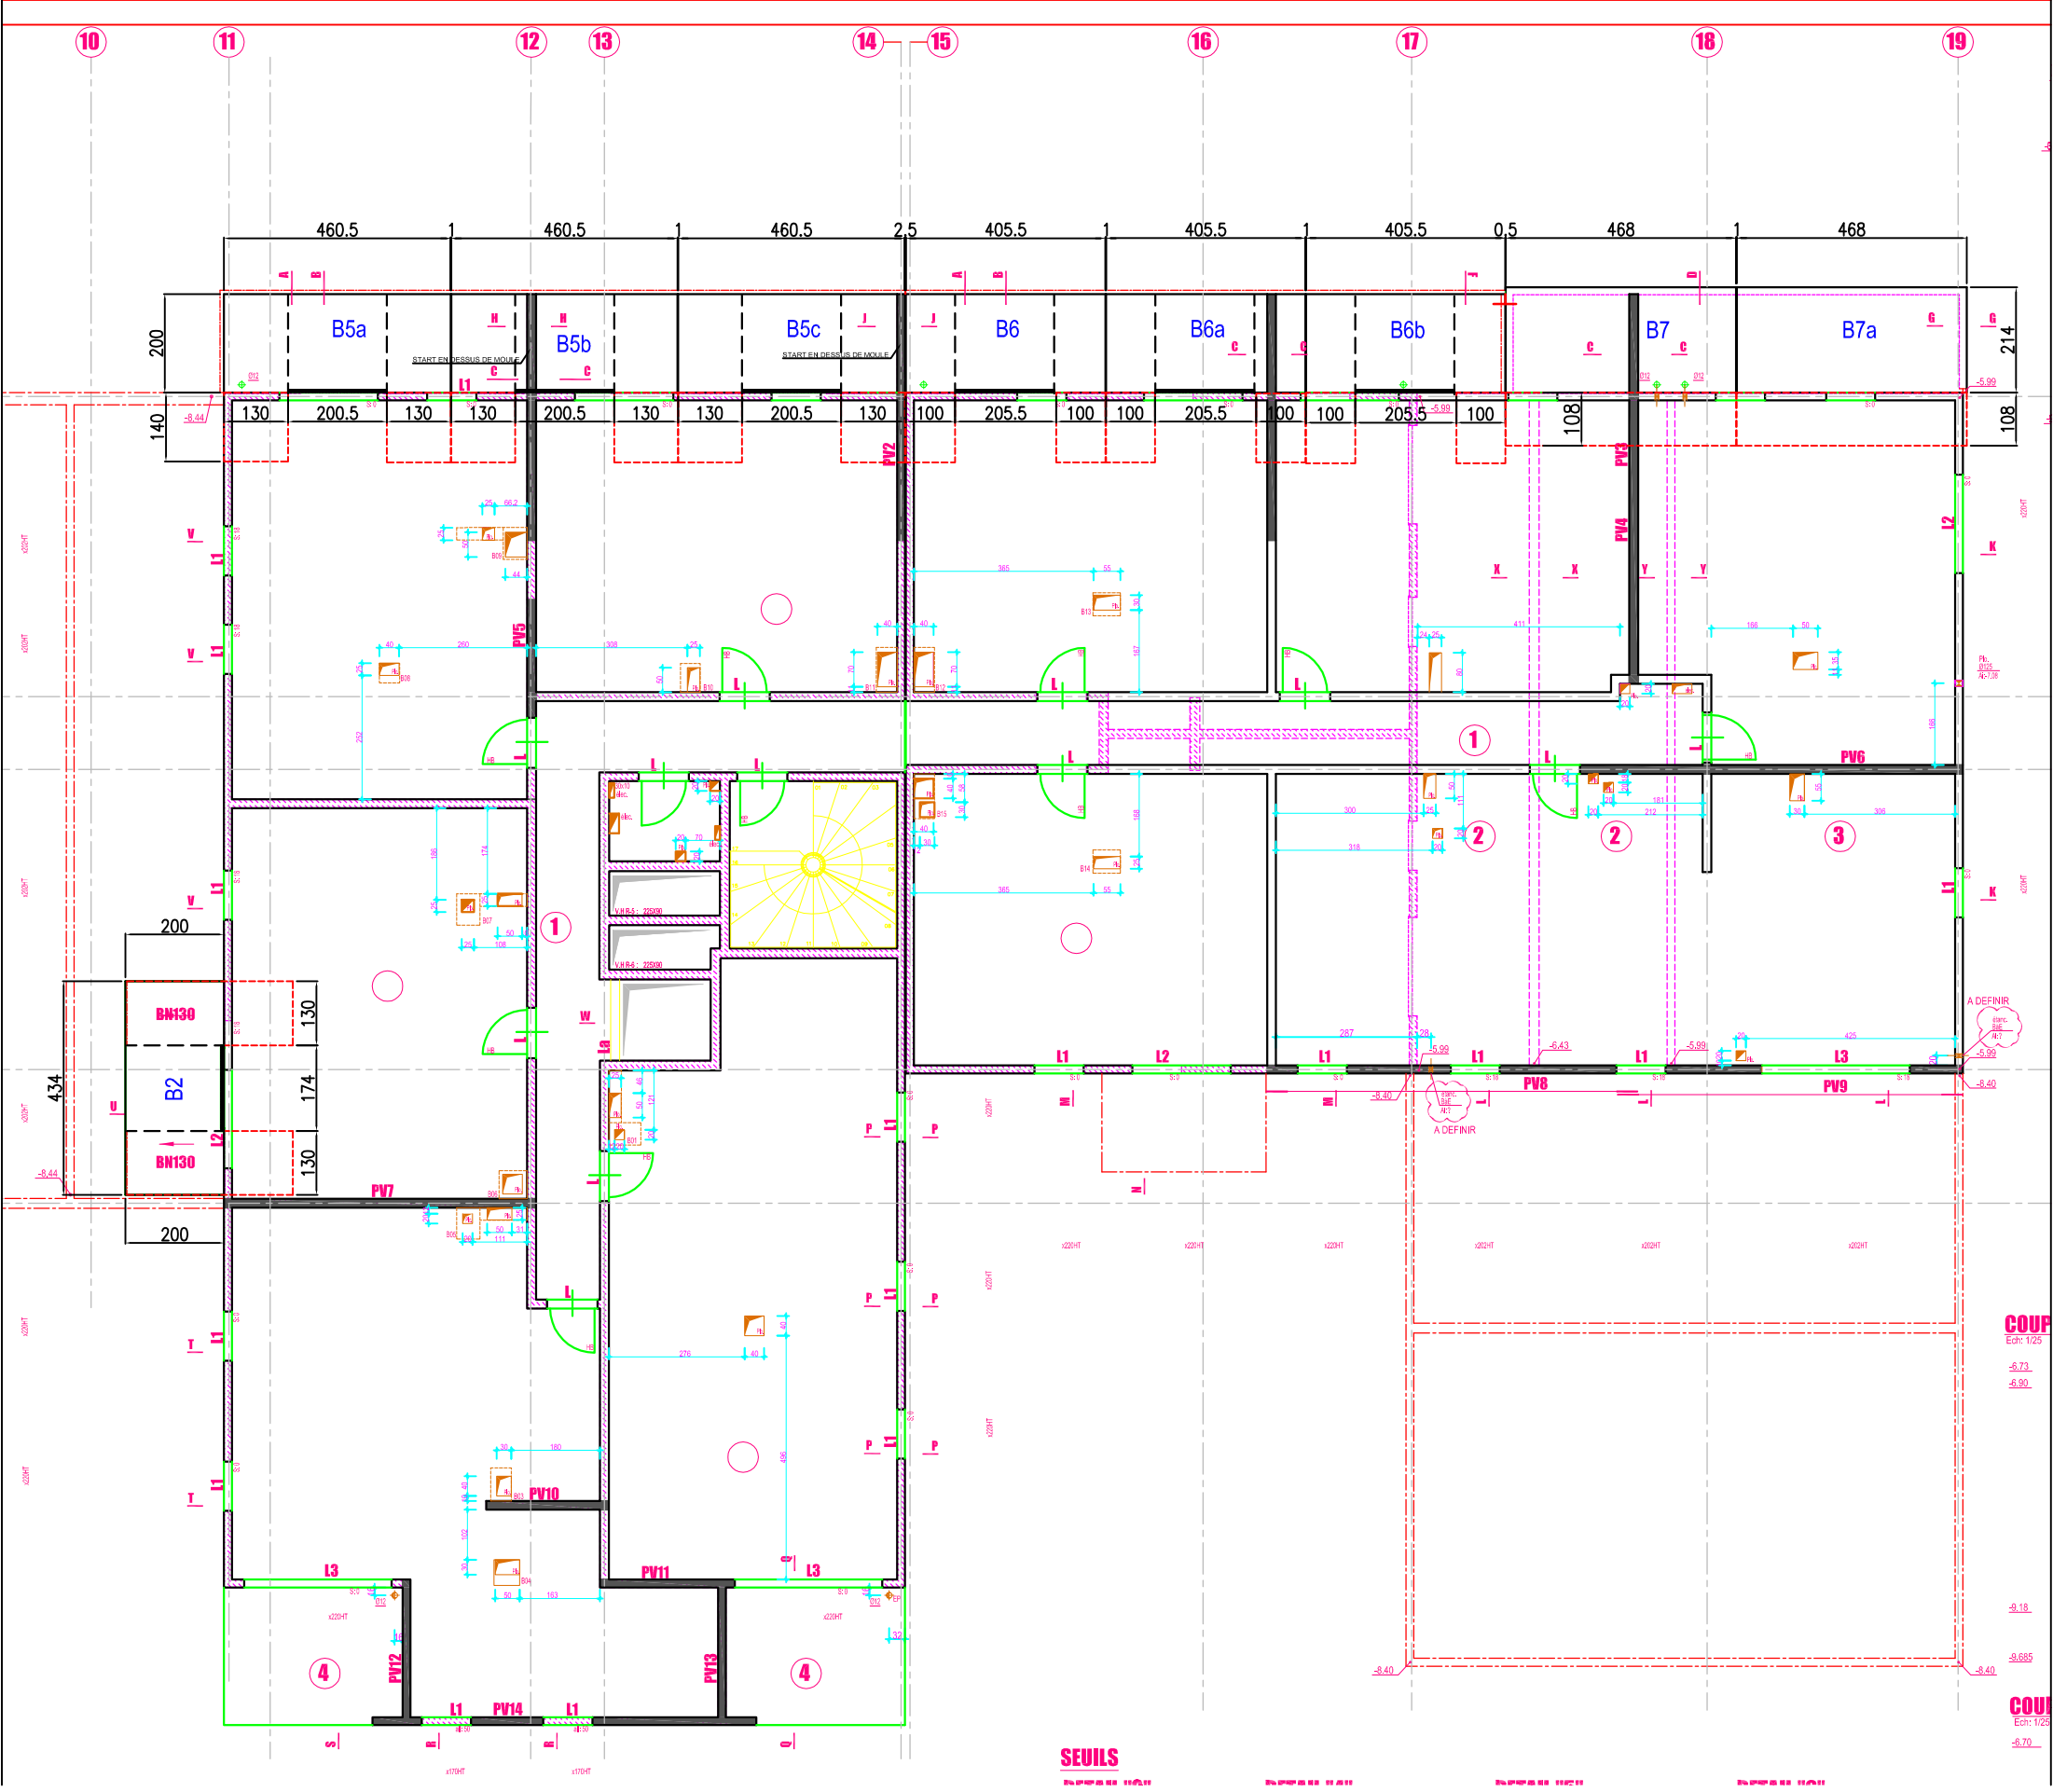

MOULE	N	NC	observations	BETON	N	NC	observations	FICHE AUTO-CONTROLE
Conformité moule			Dimensions	Conformité béton				Opérateur :
Etat du moule			Armature	Mise en place				Responsable prod :
Propreté et huilage			Inserts	Aspect de surface				Date :


Ent. FONTANEL		Elément: BALCONS		PLAN DE FABRCATION		Surface: 8.68 m²	POIDS	REPERE	Nbr
LA MULATIERE		coffrage / ferrailage				Volume: 1.65 m3	3.95 T	B2	1

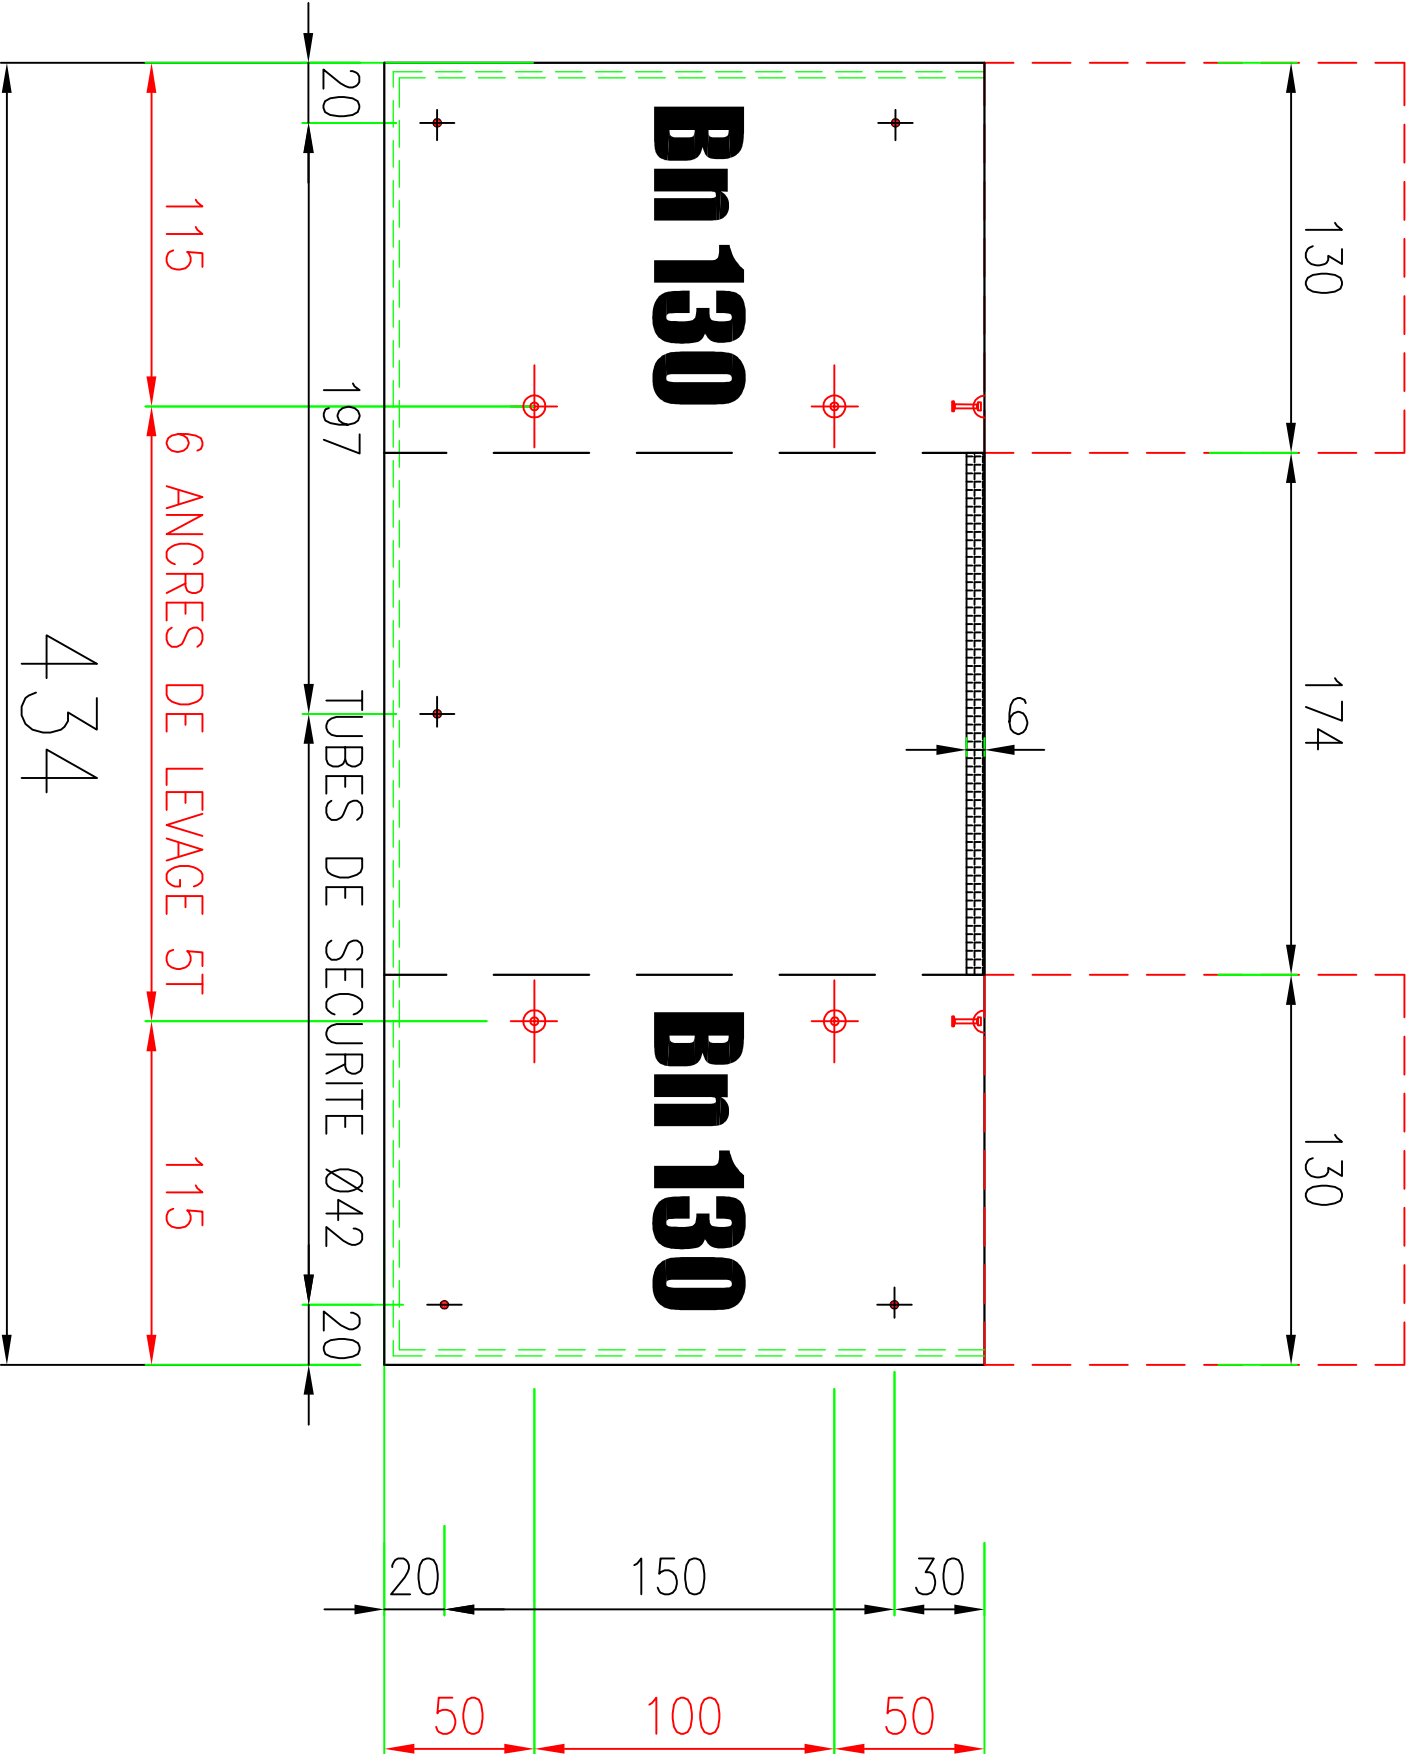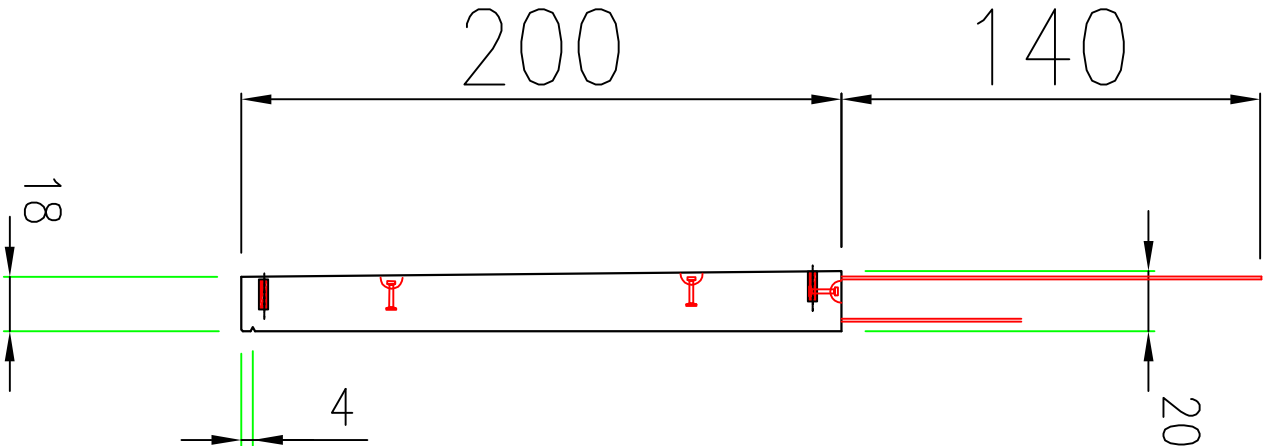

LEVAGE		INSERTS		INSERTS		INSERTS		INSERTS	
	Douille Ø		Ancre Frimeda T		EBA		TP - JV	DATE: 22/12/2015	
	Douille Ø		Renfort Ø		Douille étalement		PVC Ø80	Plan N°	
	Renfort Ø dx		Trifer		Ankrobox Ø50		Tube garde-corps	Indice	Page N°

MOULE	N	NC	observations	CONTROLE	N	NC	observations	BETON	N	NC	observations	FICHE AUTO-CONTROLE
Conformité moule				Dimensions				Conformité béton				Opérateur :
Etat du moule				Armature				Mise en place				Responsable prod :
Propreté et huilage				Inserts				Aspect de surface				Date :


Ent. FONTANEL		Elément: BALCONS		PLAN DE FABRCATION		Surface: 9.21 m²	POIDS	REPERE	Nbr
LA MULATIERE		coffrage / ferrailage		PLATTARD S.A.S.		Volume: 1.70 m3	4.10 T	B5a	1

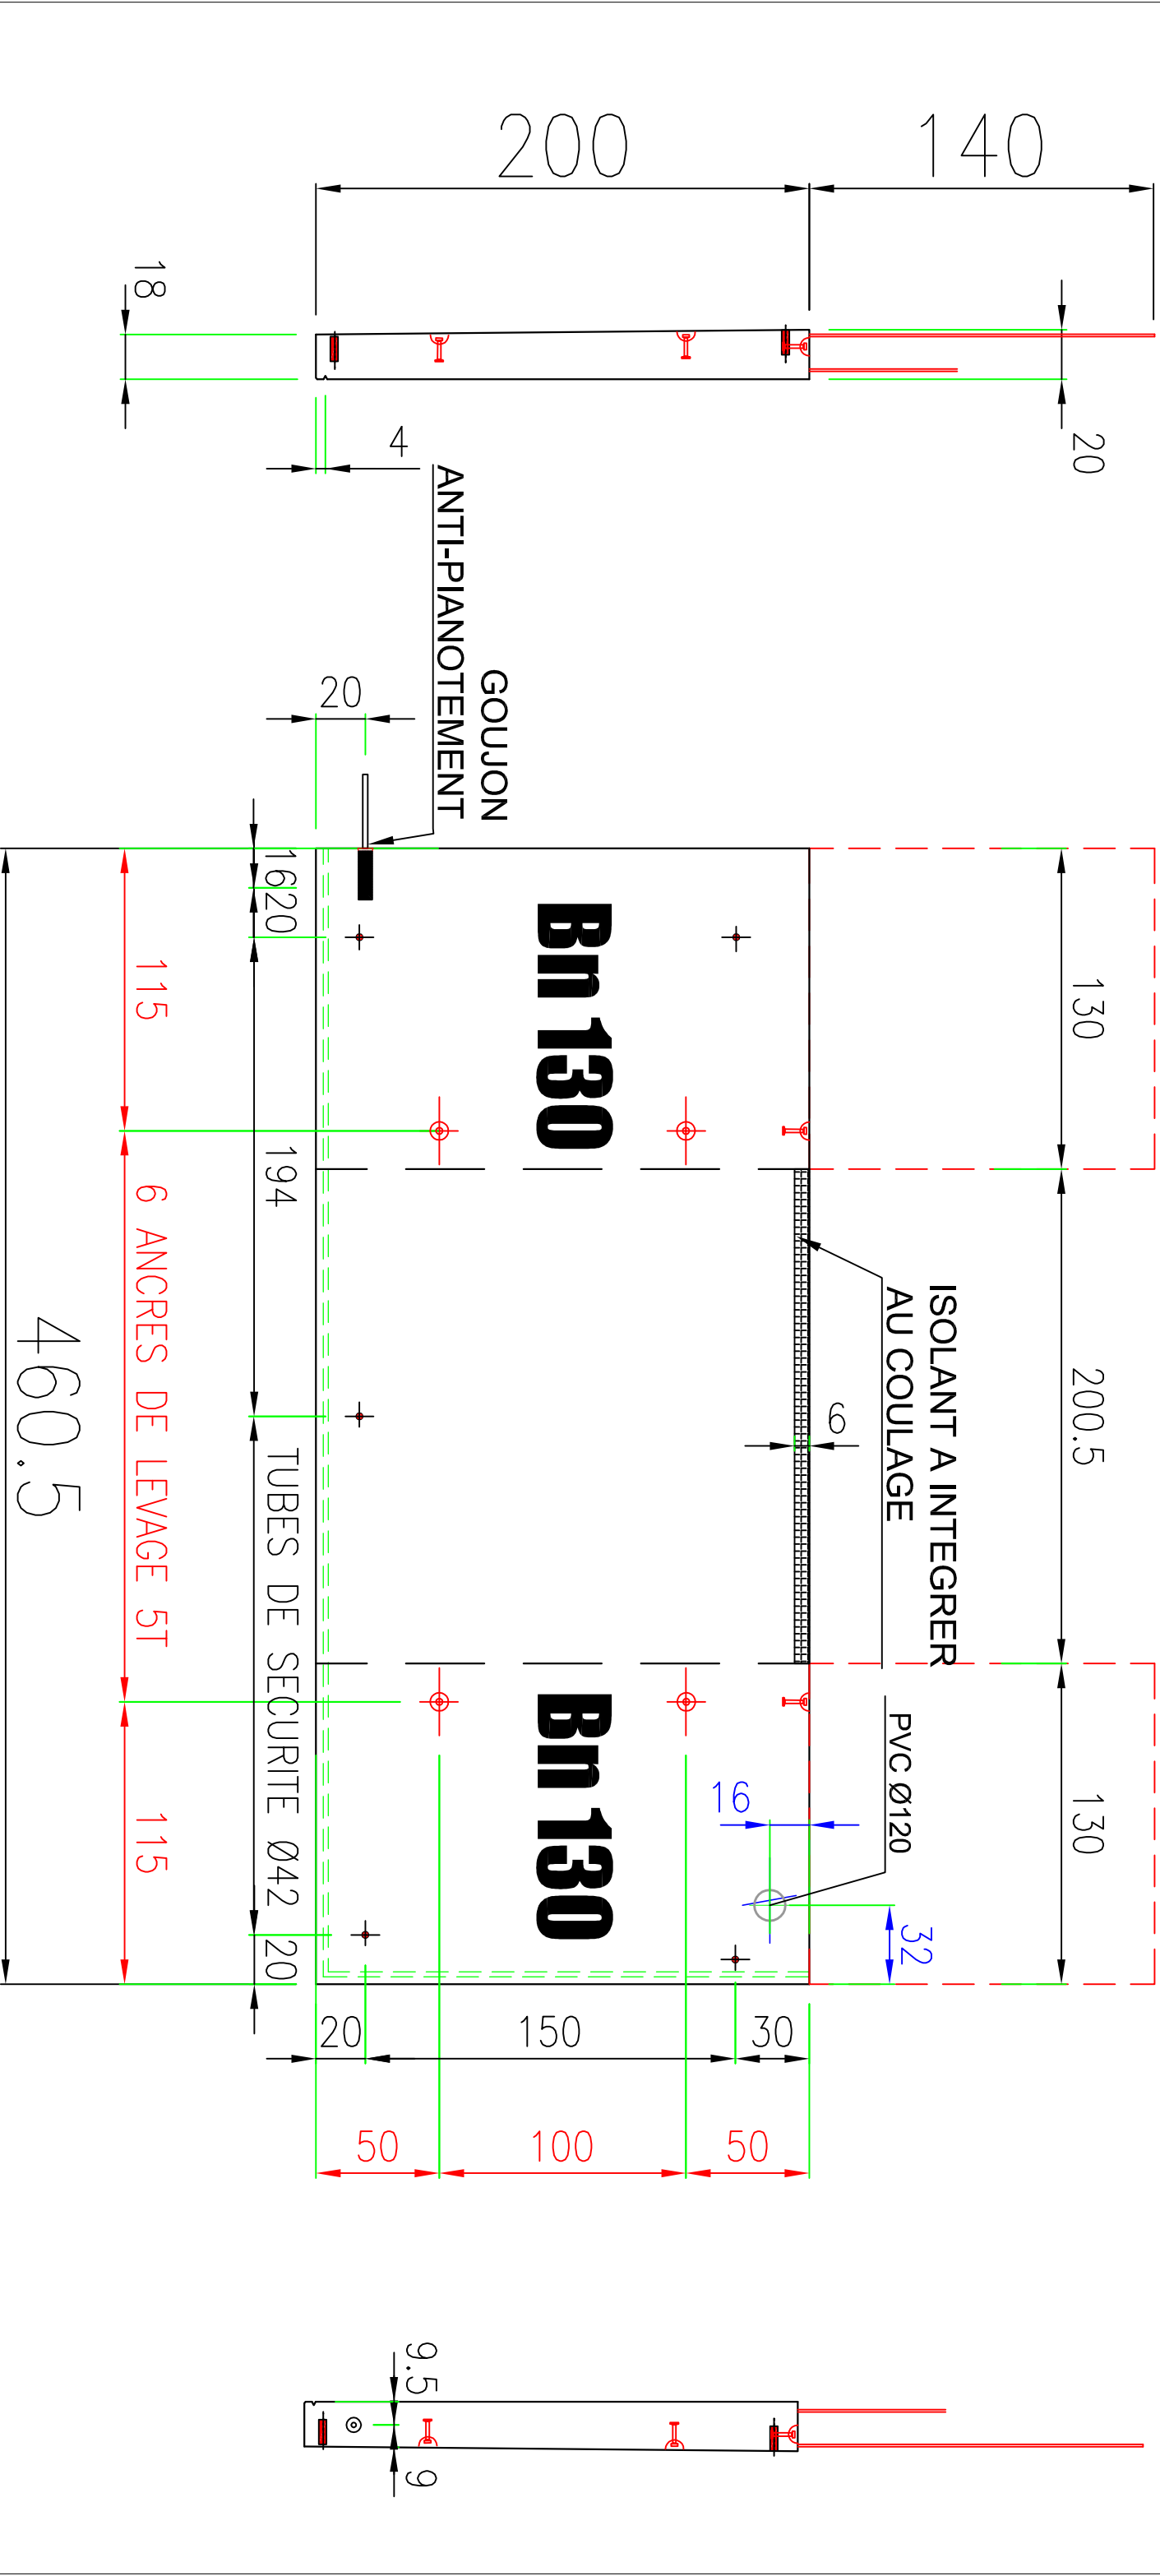

LEVAGE		INSERTS		INSERTS		INSERTS	
	Douille Ø		Ancre Frimeda T		EBA		TP - JV
	Douille Ø		Renfort Ø		Douille étalement		PVC Ø80
	Renfort Ø dx		Trifer		Ankrobox Ø50		Tube garde-corps
DATE: 11/12/2015		Plan N°		Indice		Page N°	

MOULE	N	NC	observations	CONTRÔLE	N	NC	observations	BETON	N	NC	observations	FICHE AUTO-CONTRÔLE
Conformité moule				Dimensions				Conformité béton				Opérateur :
Etat du moule				Armature				Mise en place				Responsable prod :
Propreté et huilage				Inserts				Aspect de surface				Date :


Ent. FONTANEL			Elément: BALCONS			PLAN DE FABRCATION			Surface:	9.21 m²	POIDS	REPERE	Nbr
LA MULATIERE			coffrage / ferrailage			PLATTARD S.A.S.			Volume:	1.70 m3	4.10 T	B5b 1	

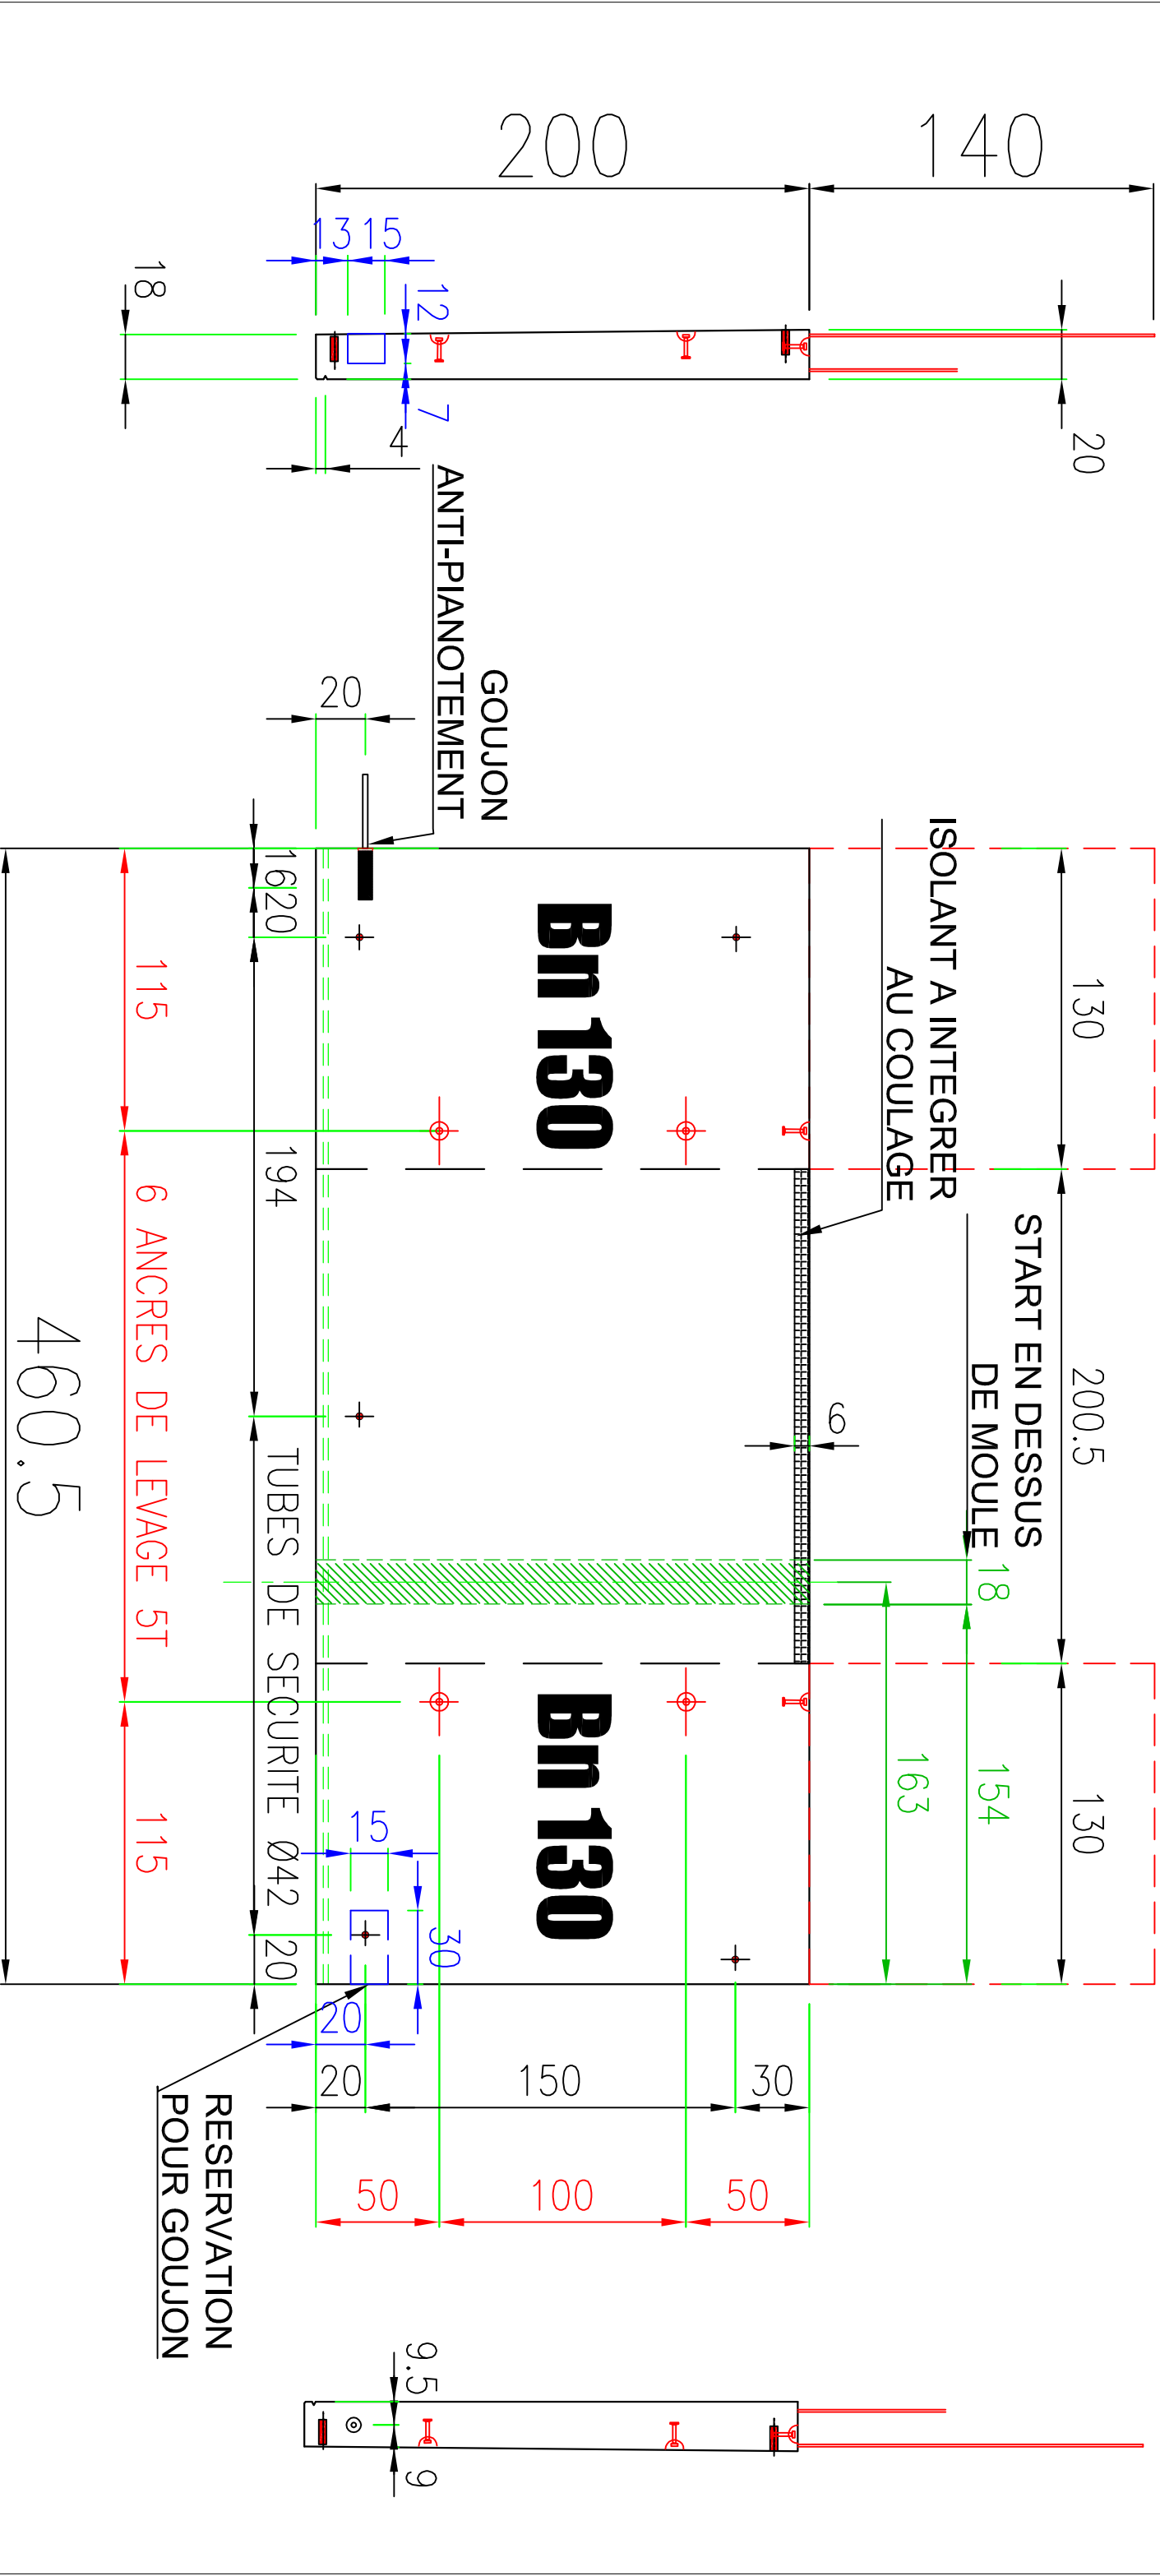

LEVAGE			INSERTS			INSERTS			INSERTS		
	Douille Ø			Ancre Frimeda T			EBA			TP - JV	DATE: 11/12/2015
	Douille Ø			Renfort Ø			Douille étalement			PVC Ø80	Plan N°
	Renfort Ø dx			Trifer			Ankrobox Ø50			Tube garde-corps	Indice

FICHE AUTO-CONTROLE												
MOULE	N	NC	observations	CONTROLE	N	NC	observations	BETON	N	NC	observations	Opérateur :
Conformité moule				Dimensions				Conformité béton				Responsable prod :
Etat du moule				Armature				Mise en place				Date :
Propreté et huilage				Inserts				Aspect de surface				

Ent. FONTANEL		Elément: BALCONS		 PLAN DE FABRICATION		Surface: 9.21 m²		POIDS 4.10 T		REPERE		Nbr	
LA MULATIERE		coffrage / ferrillage				Volume: 1.70 m3				B5c		1	

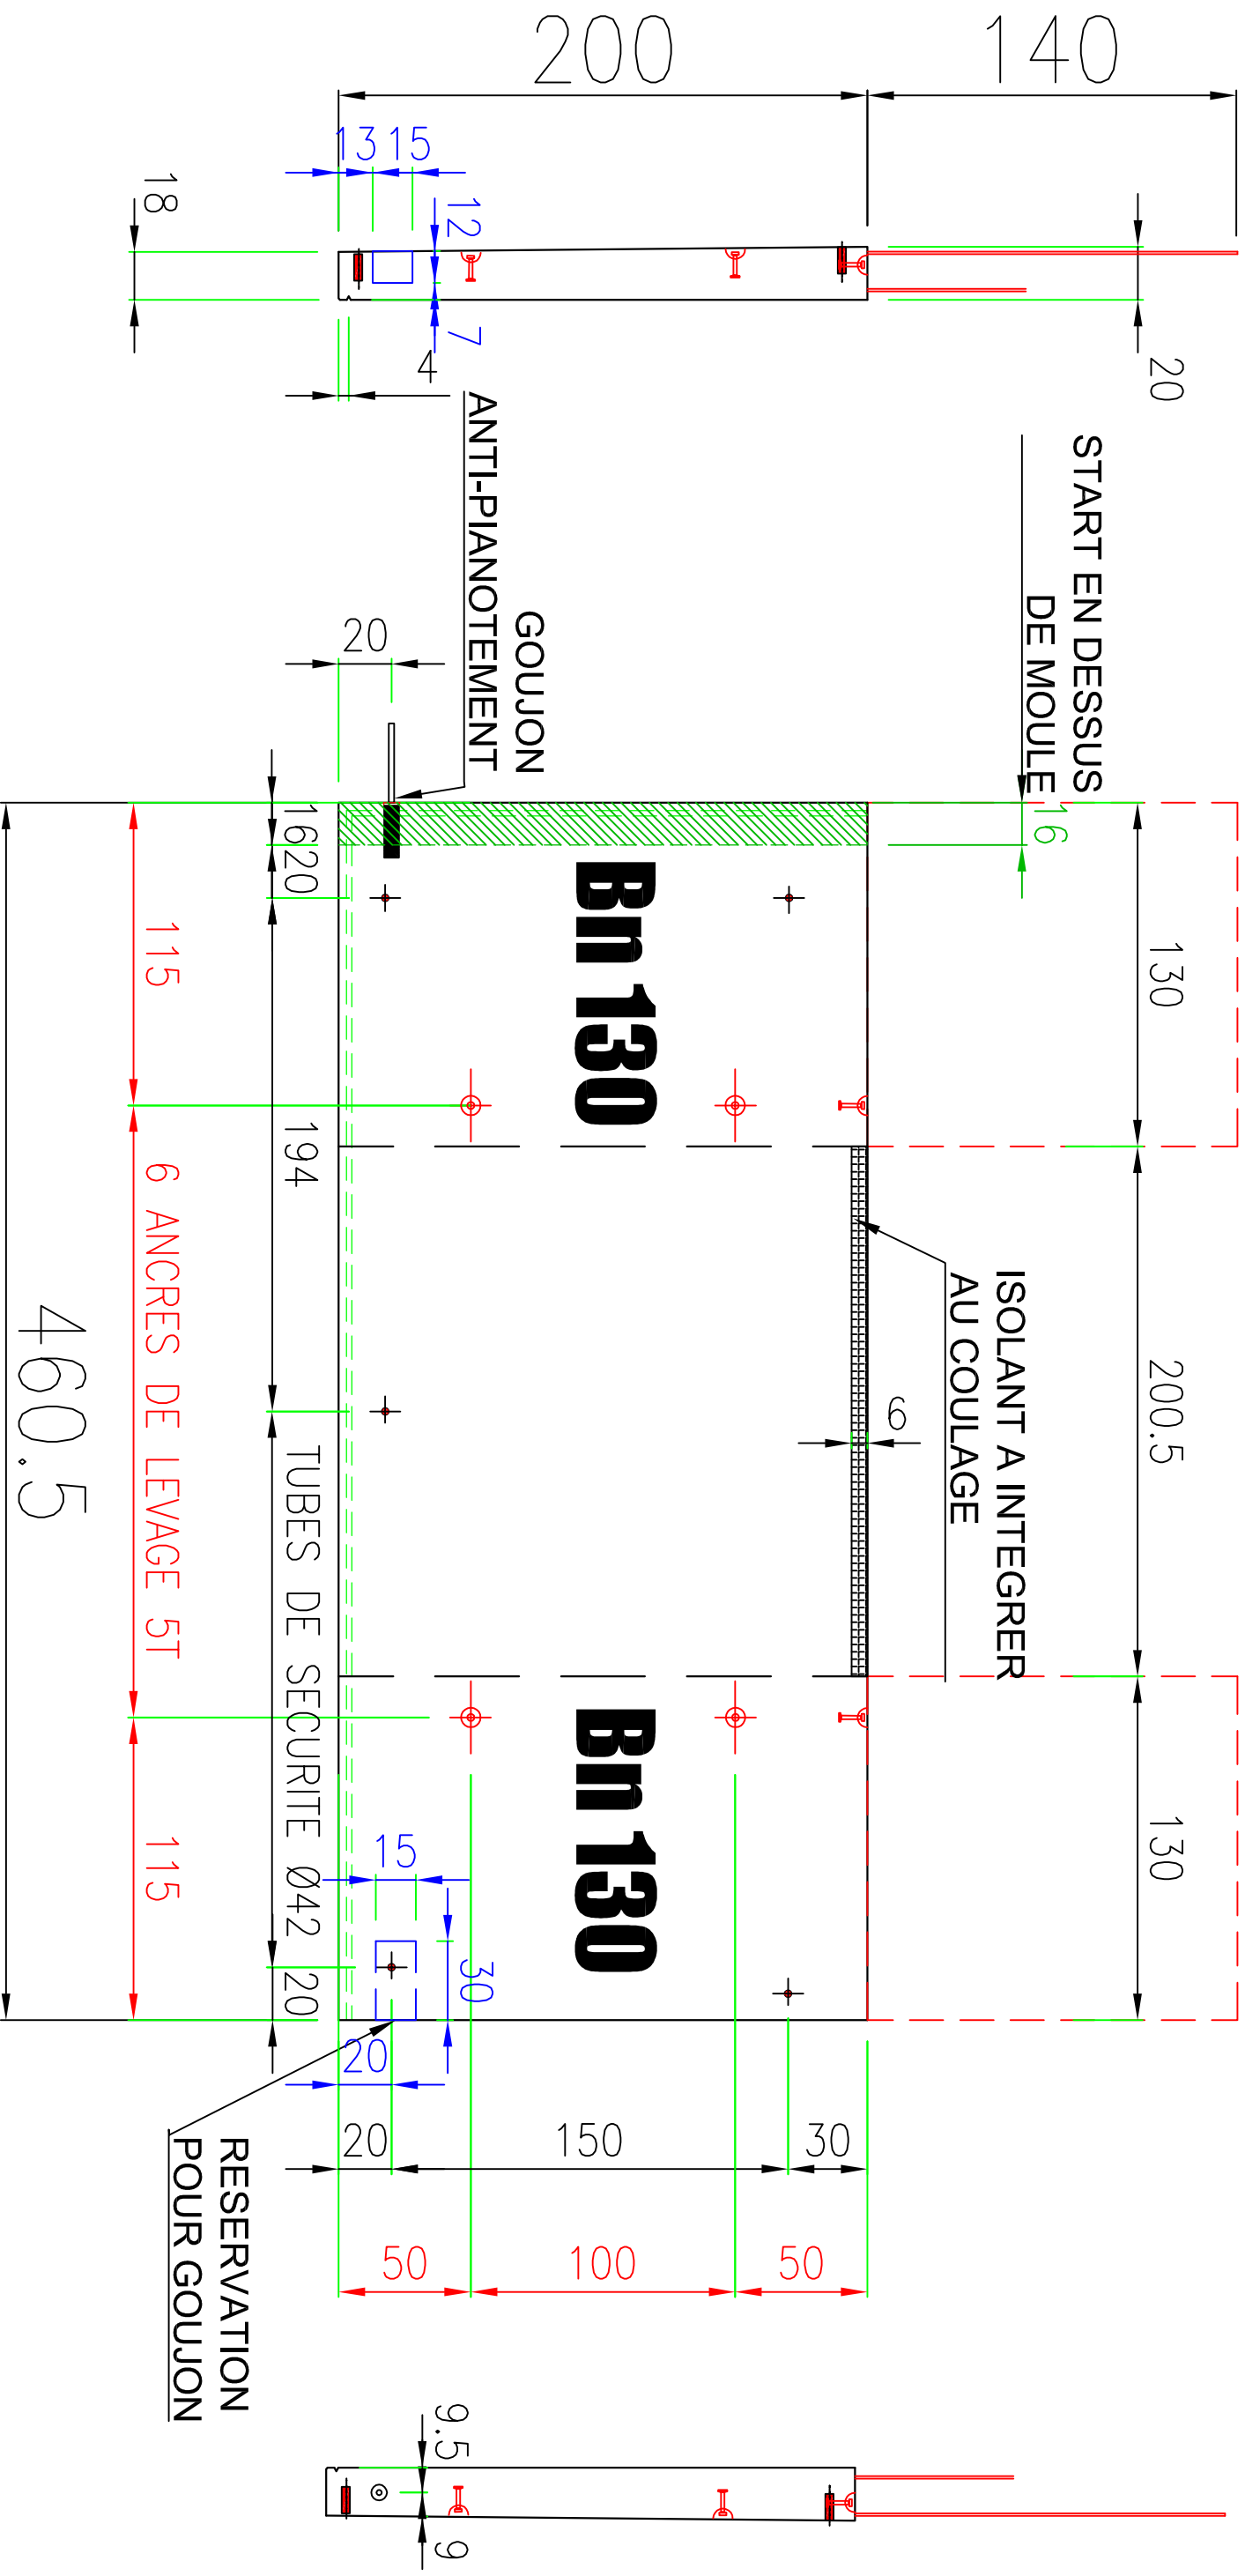

LEVAGE									
	Douille Ø								
	Douille Ø								
	Renfort Ø dx								
INSERTS									
	Ancre Frimeda T								
	Renfort Ø								
	Trifer								
INSERTS									
	EBA								
	Douille étalement								
	Ankrobox Ø50								
INSERTS									
	TP - JV								
	PVC Ø80								
	Tube garde-corps								
DATE: 11/12/2015									
Plan N°			Page N°						
Indice									