

FONTANEL- LE 180°

69 LA MULATIERE

BALCONS DU NIVEAU N-4 suite
BAT B

N

EXE

Indice	Date	Designation des Modifications	Date :
A	07/04/2016	EVIDEMENT BALCON B14c	30/03/2016
B			Affaire :
C			
D			Echelle :
E			
F			
G			
H			
I			

Type béton = B35 XF1
Aciers H.A et T.S = Fe E 500
Enrobage des armatures = ENR_CARMAT
Manutention = Tonnes

BUREAU D'ETUDE
PLATTARD SAS
414 Avenue de la
plage
BP 119
69540
Villefrance-sur-Saône
Tél: 04 74 02 20 20
Fax: 04 74 62 26 62



Ce plan est la propriété intellectuelle de la PLATTARD SAS, il ne peut être reproduit sans son autorisation.

NOAHO

Chemin de Fontanière - 69350 La Mulatière

Création de logements

Les entreprises réalisant les travaux devront tenir compte des derniers plans architecte lors de la réalisation des travaux
Les plans du be MATTE ne doivent servir qu'au corps d'état concerné et doivent être des plans d'exécution.

ARCHITECTE(S): ATELIER DE LA PASSERELLE

MO DELEGUE:

BET STRUCTURE: MATTE SAS

MOE: PSO Ingénierie

BET FLUIDES: PRELEM

CSPS: SUD EST COORDINATION

ECONOMISTE: EXECO

OPC:

BUREAU DE CONTROLE: Bureau VERITAS

ENTREPRISE(S): Fontanel-pbc

Bât: B
PLANCHER sur -4
Coffrage

EXE

Contrainte de sol: 8 bars ELS

INDICE	DATE	MODIFICATIONS
A	29/03/2016	COMPLETE

Aciers HA (T) FeE500

Aciers Doux (Ø) FeE 235

Aciers TS FeE 500

Béton fc28 >= 25MPa

Enrobage = 3 cm

PLAN N°
B26 A

DATE : 25/03/2016

MATTÉ
BUREAU D'ÉTUDES
STRUCTURES ET FLUIDES

119 BOULEVARD STALINGRAD 69100 VILLEURBANNE

Tél. 04 72 44 02 87 Fax 04 72 44 26 59


E-mail : bet@matte.fr

Dessiné par : J.BO

Contrôlé par : P.LIN


Echelle : 1/50°

Affaire N°
13.12.119

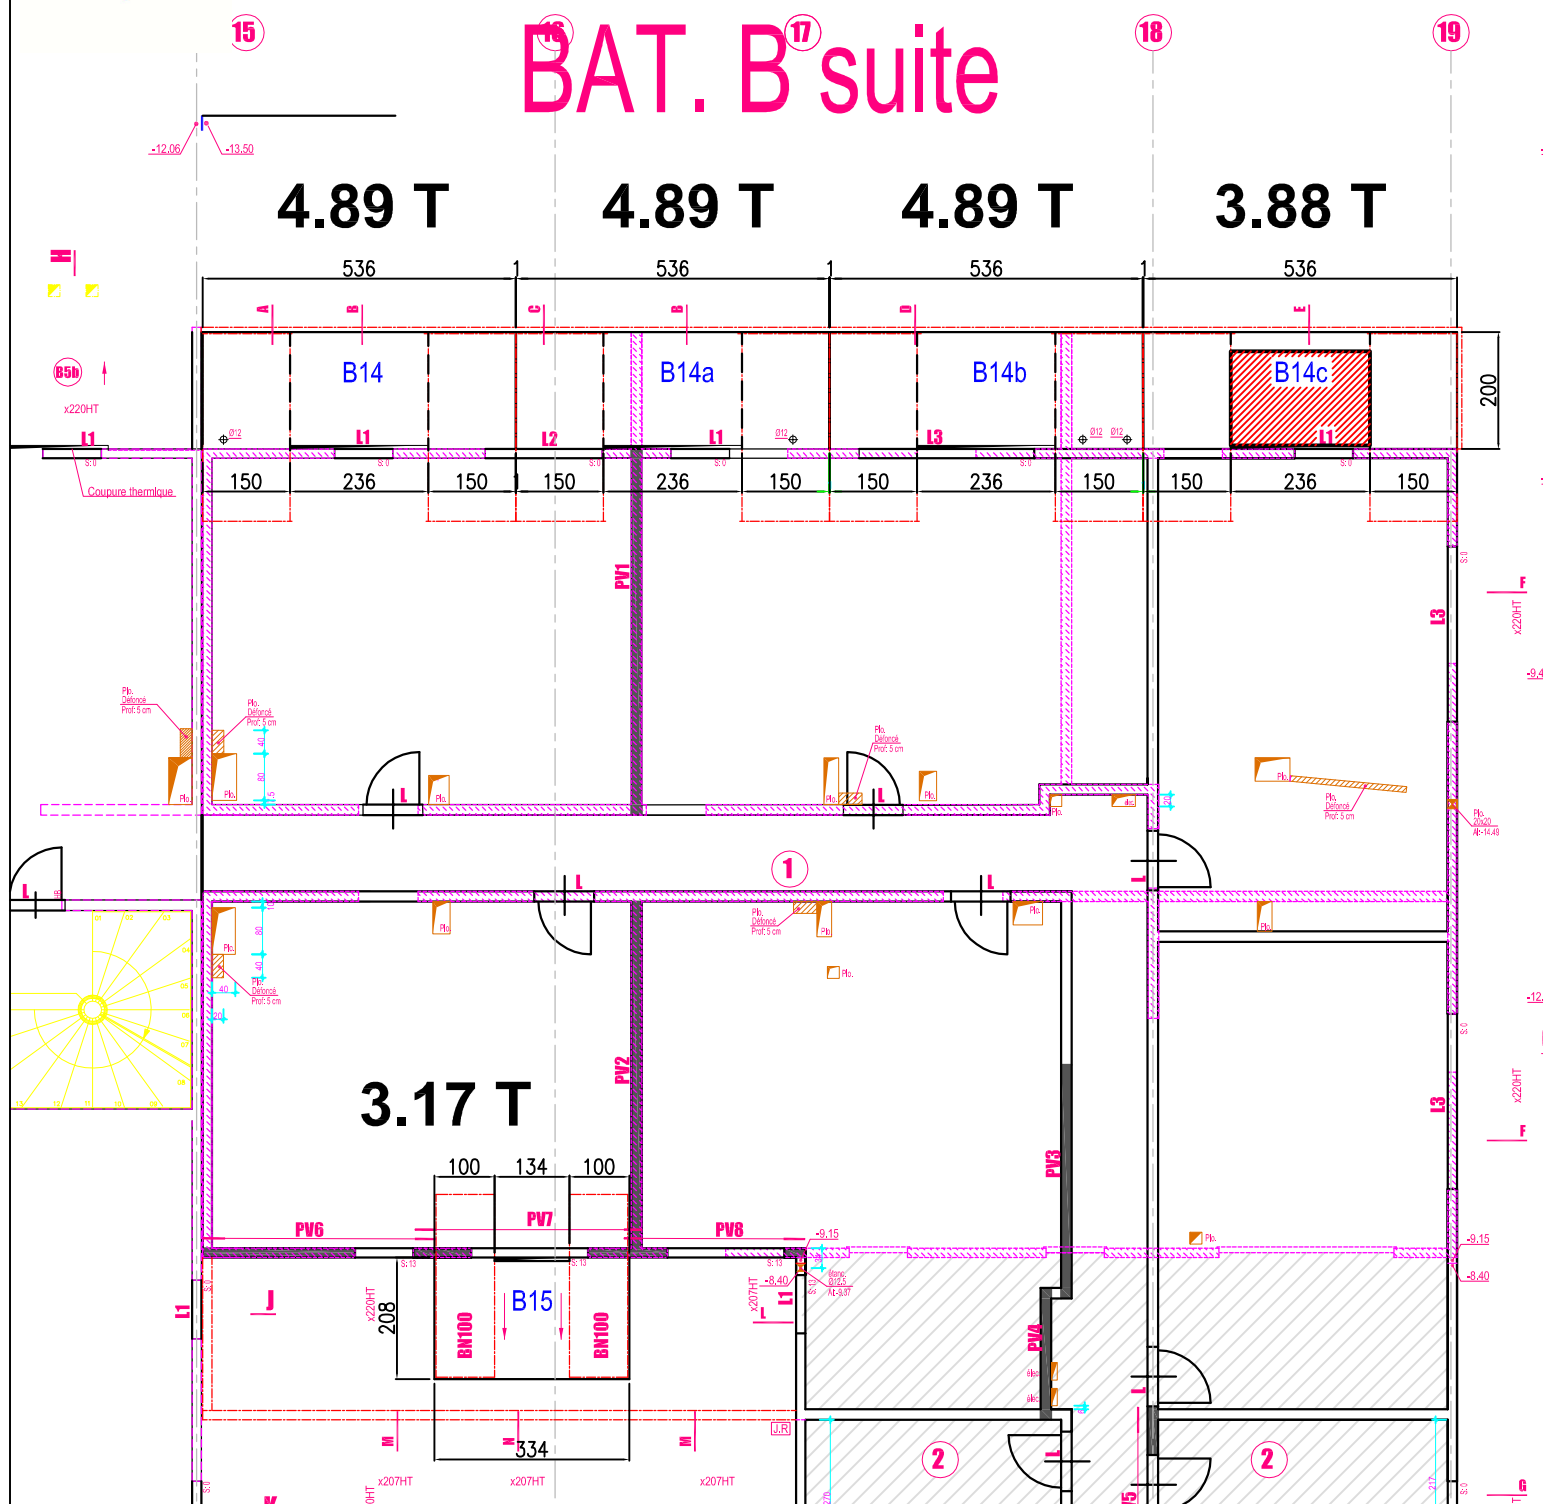

MOULE	N	NC	observations	CONTROLE	N	NC	observations	BETON	N	NC	observations	FICHE AUTO-CONTROLE
Conformité moule				Dimensions				Conformité béton				Opérateur :
Etat du moule				Armature				Mise en place				Responsable prod :
Propreté et huilage				Inserts				Aspect de surface				Date :


Ent. FONTANEL			Elément: BALCONS			Surface: 10.72 m²			POIDS			REPERE			Nbr		
LA MULATIERE			coffrage / ferrillage			PLATTARD S.A.S.			Volume: 2.04 m3			4.89 T			B14		
															1		

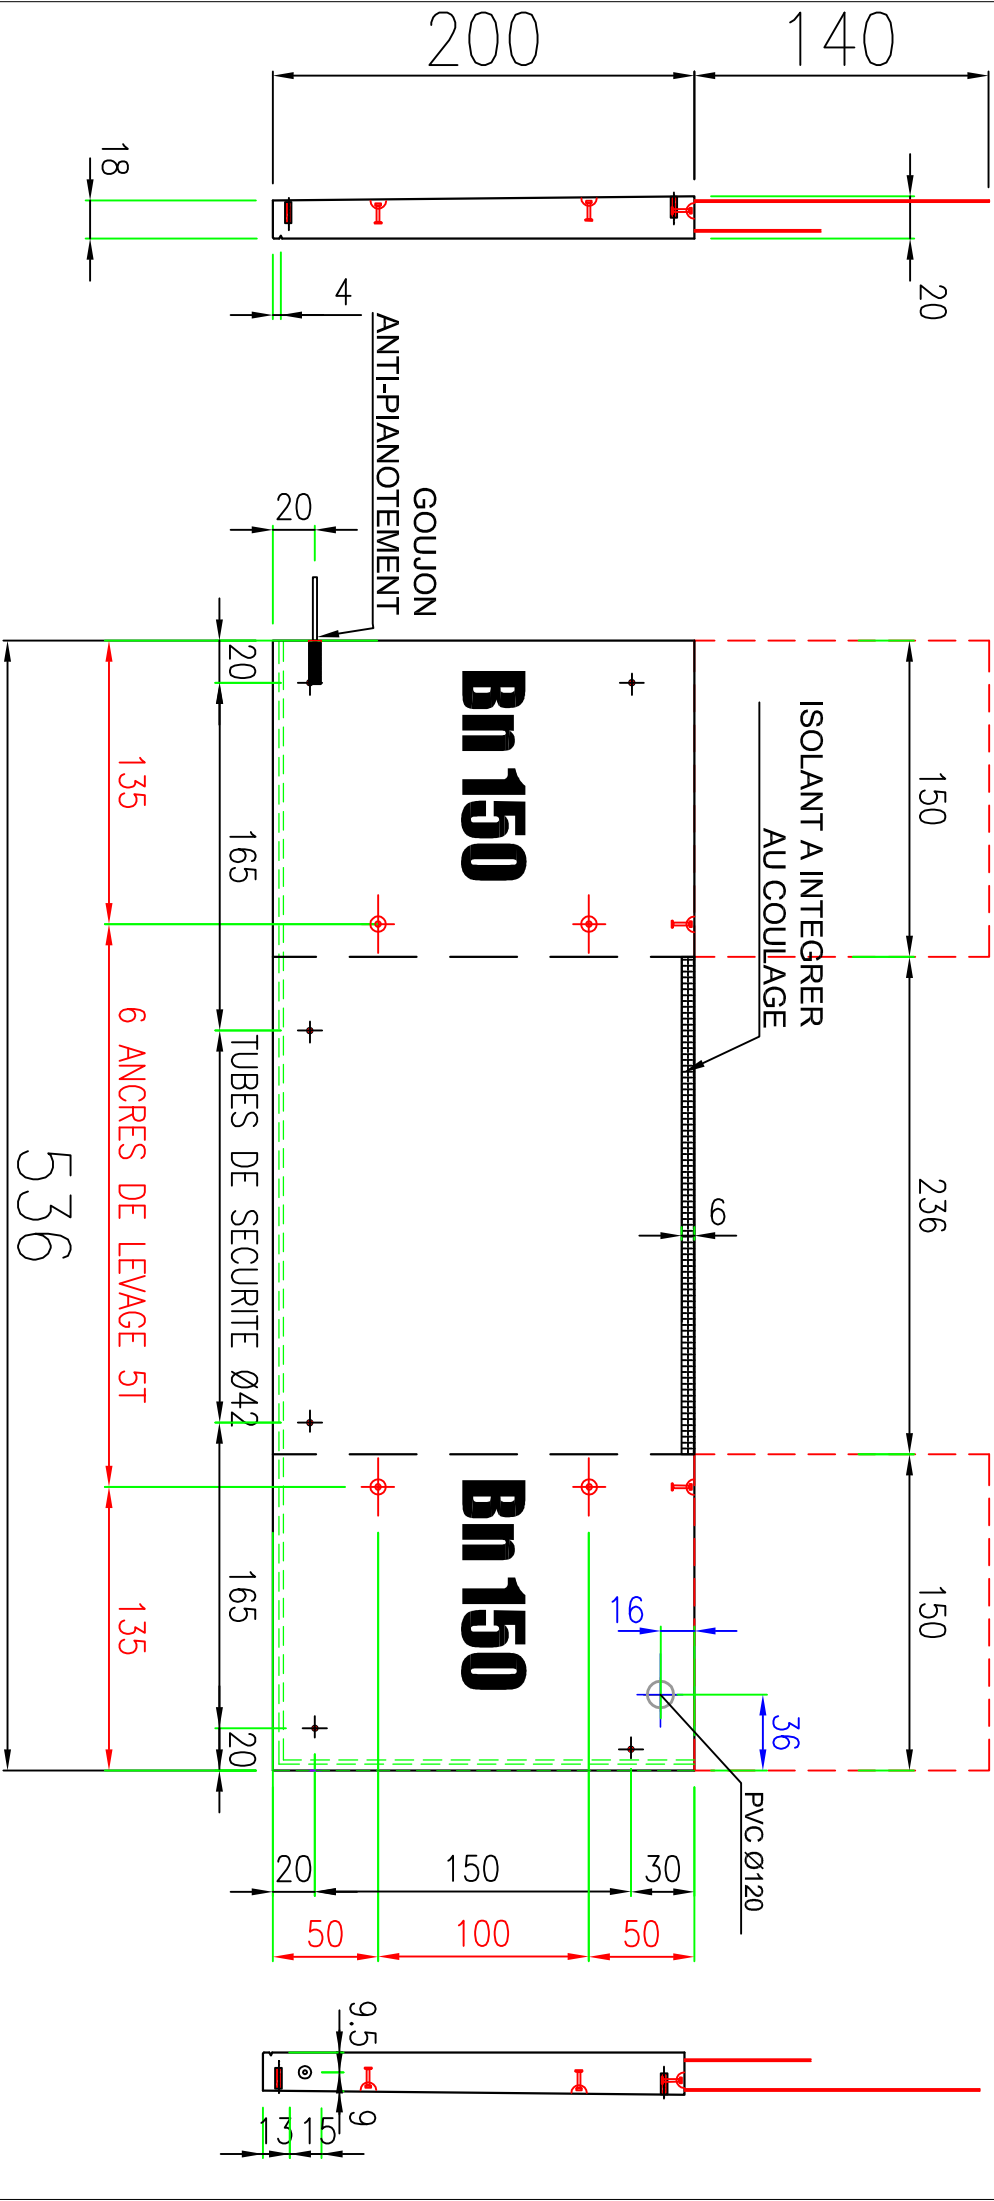

LEVAGE		INSERTS		INSERTS		INSERTS		DATE: 29/03/2016	
	Douille Ø		Ancre Frimeda T		EBA		TP - JV		
	Douille Ø		Renfort Ø		Douille étalement		PVC Ø80	Plan N°	Page N°
	Renfort Ø dx		Trifler		Ankrobox Ø50		Tube garde-corps	Indice	

MOULE	N	NC	observations	CONTROLE	N	NC	observations	BETON	N	NC	observations	FICHE AUTO-CONTROLE
Conformité moule				Dimensions				Conformité béton				Opérateur :
Etat du moule				Armature				Mise en place				Responsable prod :
Propreté et huilage				Inserts				Aspect de surface				Date :


Ent. FONTANEL		Elément: BALCONS		PLAN DE FABRCATION		Surface:	10.72 m²	POIDS	REPERE		Nbr
LA MULATIERE		coffrage / ferrailage		 PLATTARD S.A.S.		Volume:	2.04 m3	4.89 T	B14a		1

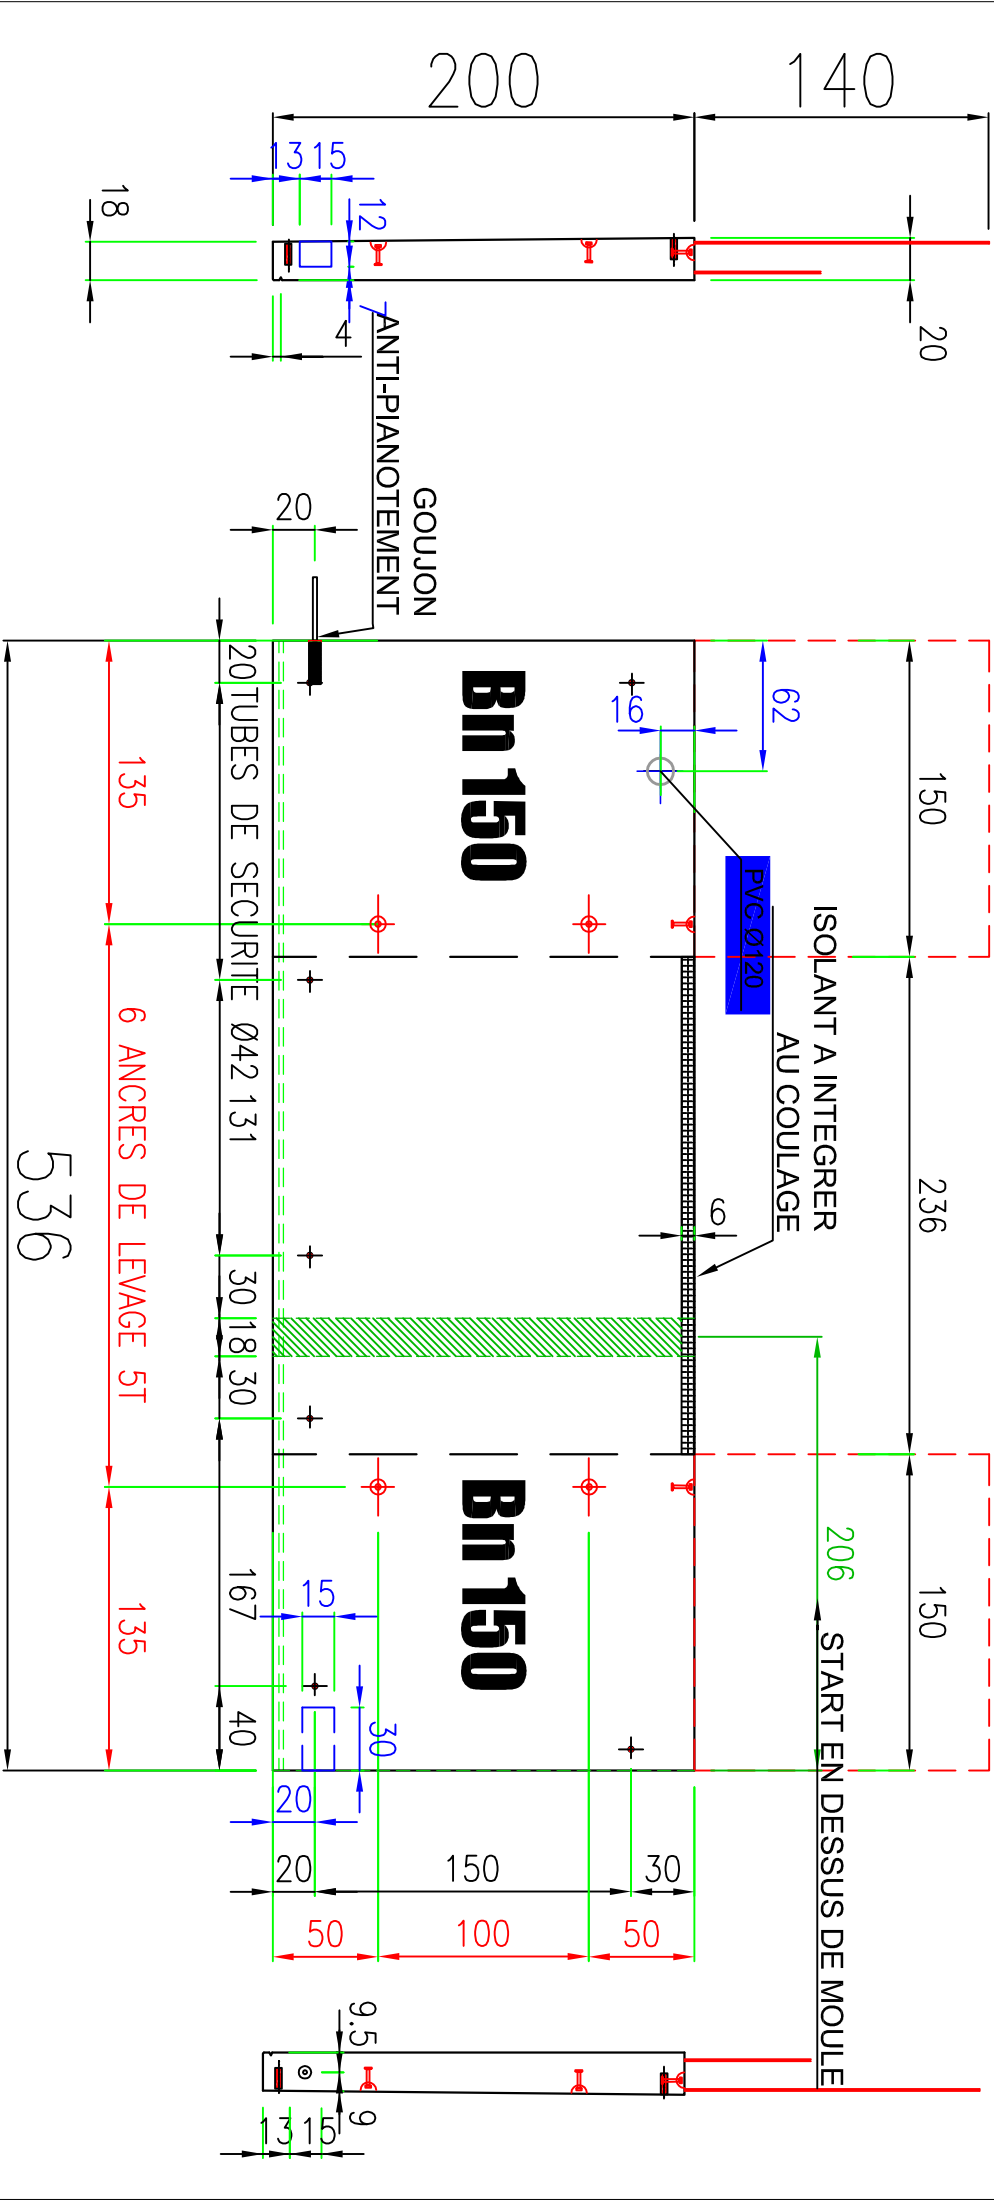

LEVAGE		INSERTS		INSERTS		INSERTS		INSERTS	
	Douille Ø		Ancre Frimeda T		EBA		TP - JV	DATE: 29/03/2016	
	Douille Ø		Renfort Ø		Douille étalement		PVC Ø80	Plan N°	
	Renfort Ø dx		Trifier		Ankrobox Ø50		Tube garde-corps	Indice	
								Page N°	

MOULE	N	NC	observations	CONTROLE	N	NC	observations	BETON	N	NC	observations	FICHE AUTO-CONTROLE
Conformité moule				Dimensions				Conformité béton				Opérateur :
Etat du moule				Armature				Mise en place				Responsable prod :
Propreté et huilage				Inserts				Aspect de surface				Date :


Ent. FONTANEL			Elément: BALCONS			PLAN DE FABRCATION			Surface:	10.72 m²	POIDS	REPERE	Nbr
LA MULATIERE			coffrage / ferrailage			PLATTARD S.A.S.			Volume:	2.04 m3	4.89 T	B14b	1

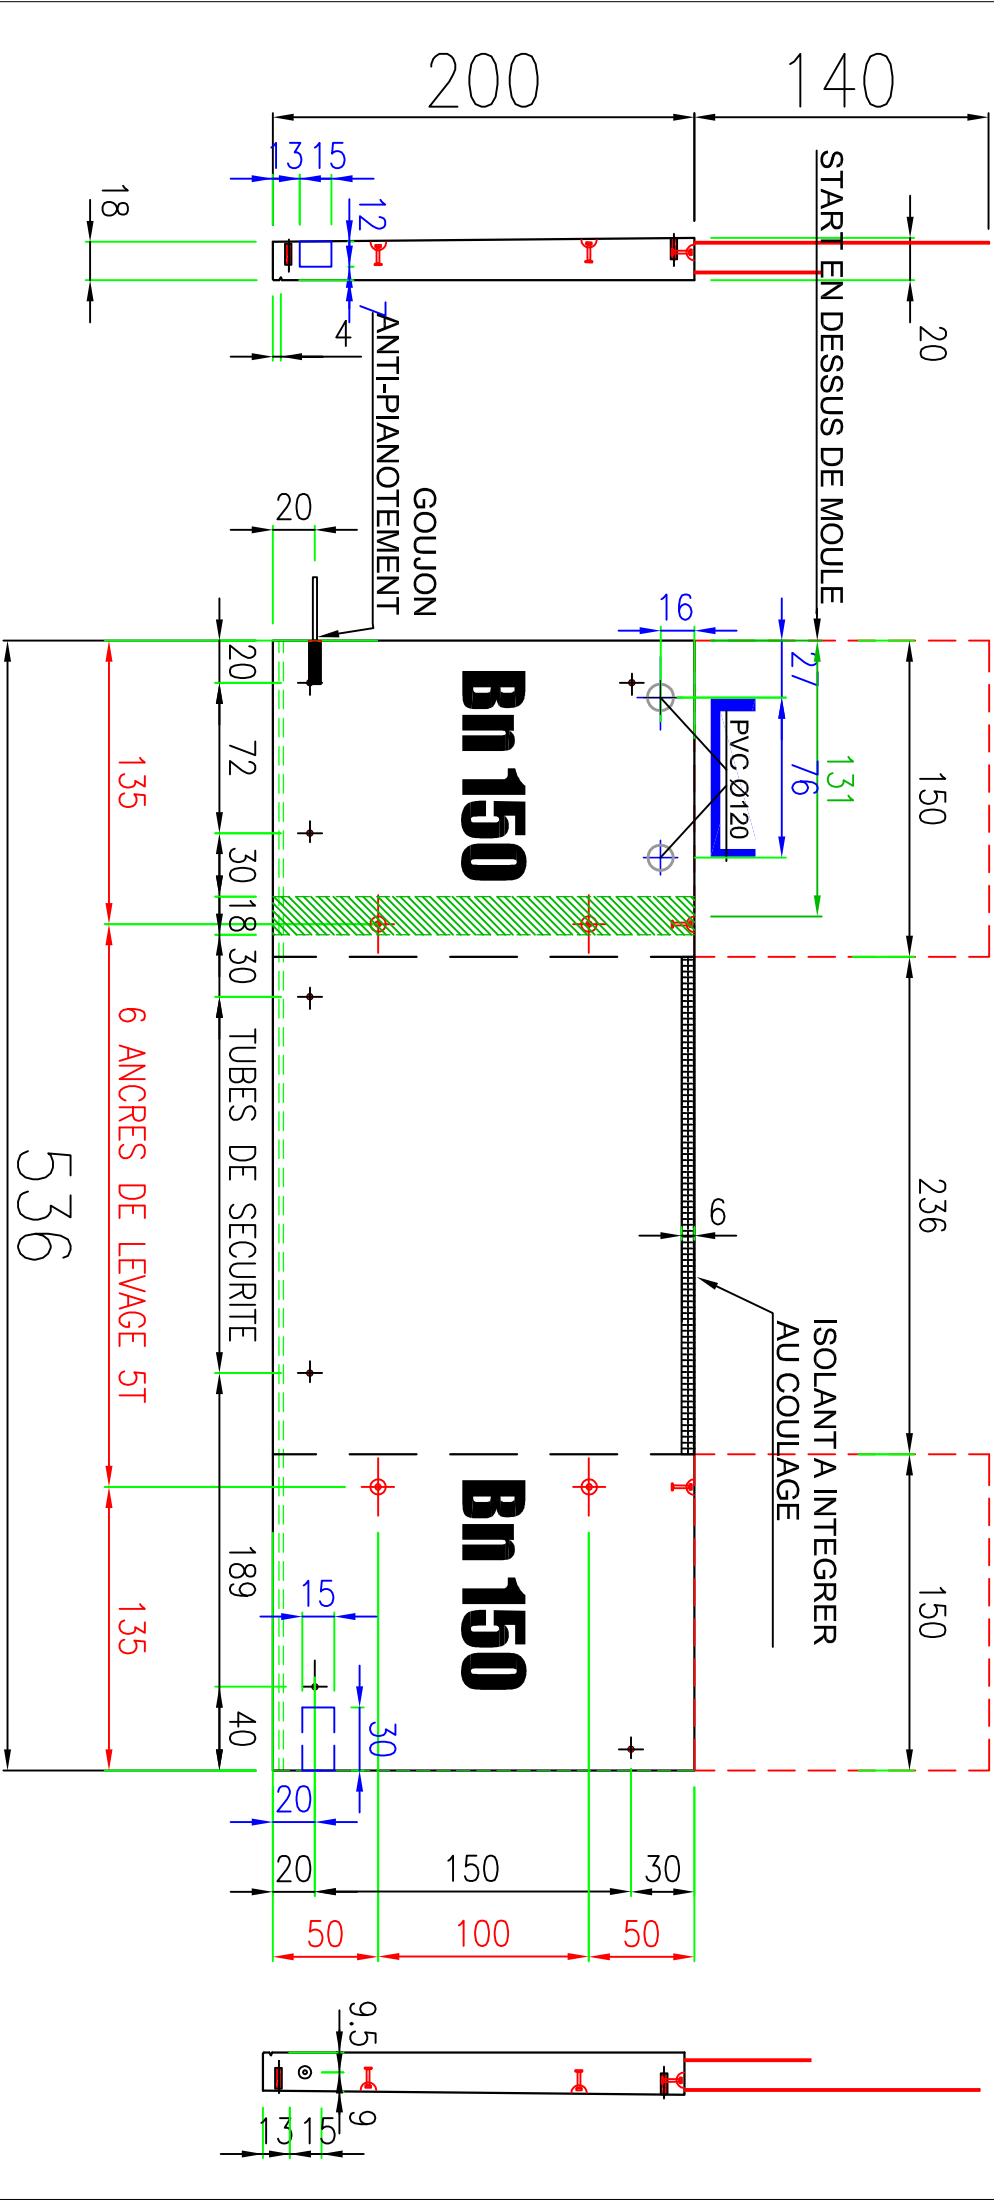

LEVAGE			INSERTS			INSERTS			INSERTS		
	Douille Ø	Renfort Ø dx		Ancre Frimeda T	Renfort Ø		EBA	Douille étalement		TP - JV	PVC Ø80
	Douille Ø	Renfort Ø dx		Renfort Ø	Trifler		Ankrobox Ø50			Tube garde-corps	Indice
DATE: 29/03/2016			Page N°			Page N°					

MOULE	N	NC	observations	CONTROLE	N	NC	observations	BETON	N	NC	observations	FICHE AUTO-CONTROLE
Conformité moule				Dimensions				Conformité béton				Opérateur :
Etat du moule				Armature				Mise en place				Responsable prod :
Propreté et huilage				Inserts				Aspect de surface				Date :

Ent. FONTANEL		Elément: BALCONS		 PLATTARD S.A.S. PLAN DE FABRCATION		Surface: 10.72 m²		POIDS		REPERE		Nbr	
LA MULATIERE		coffrage / ferrillage				Volume: 1.61 m3		3.88 T		B14c		1	

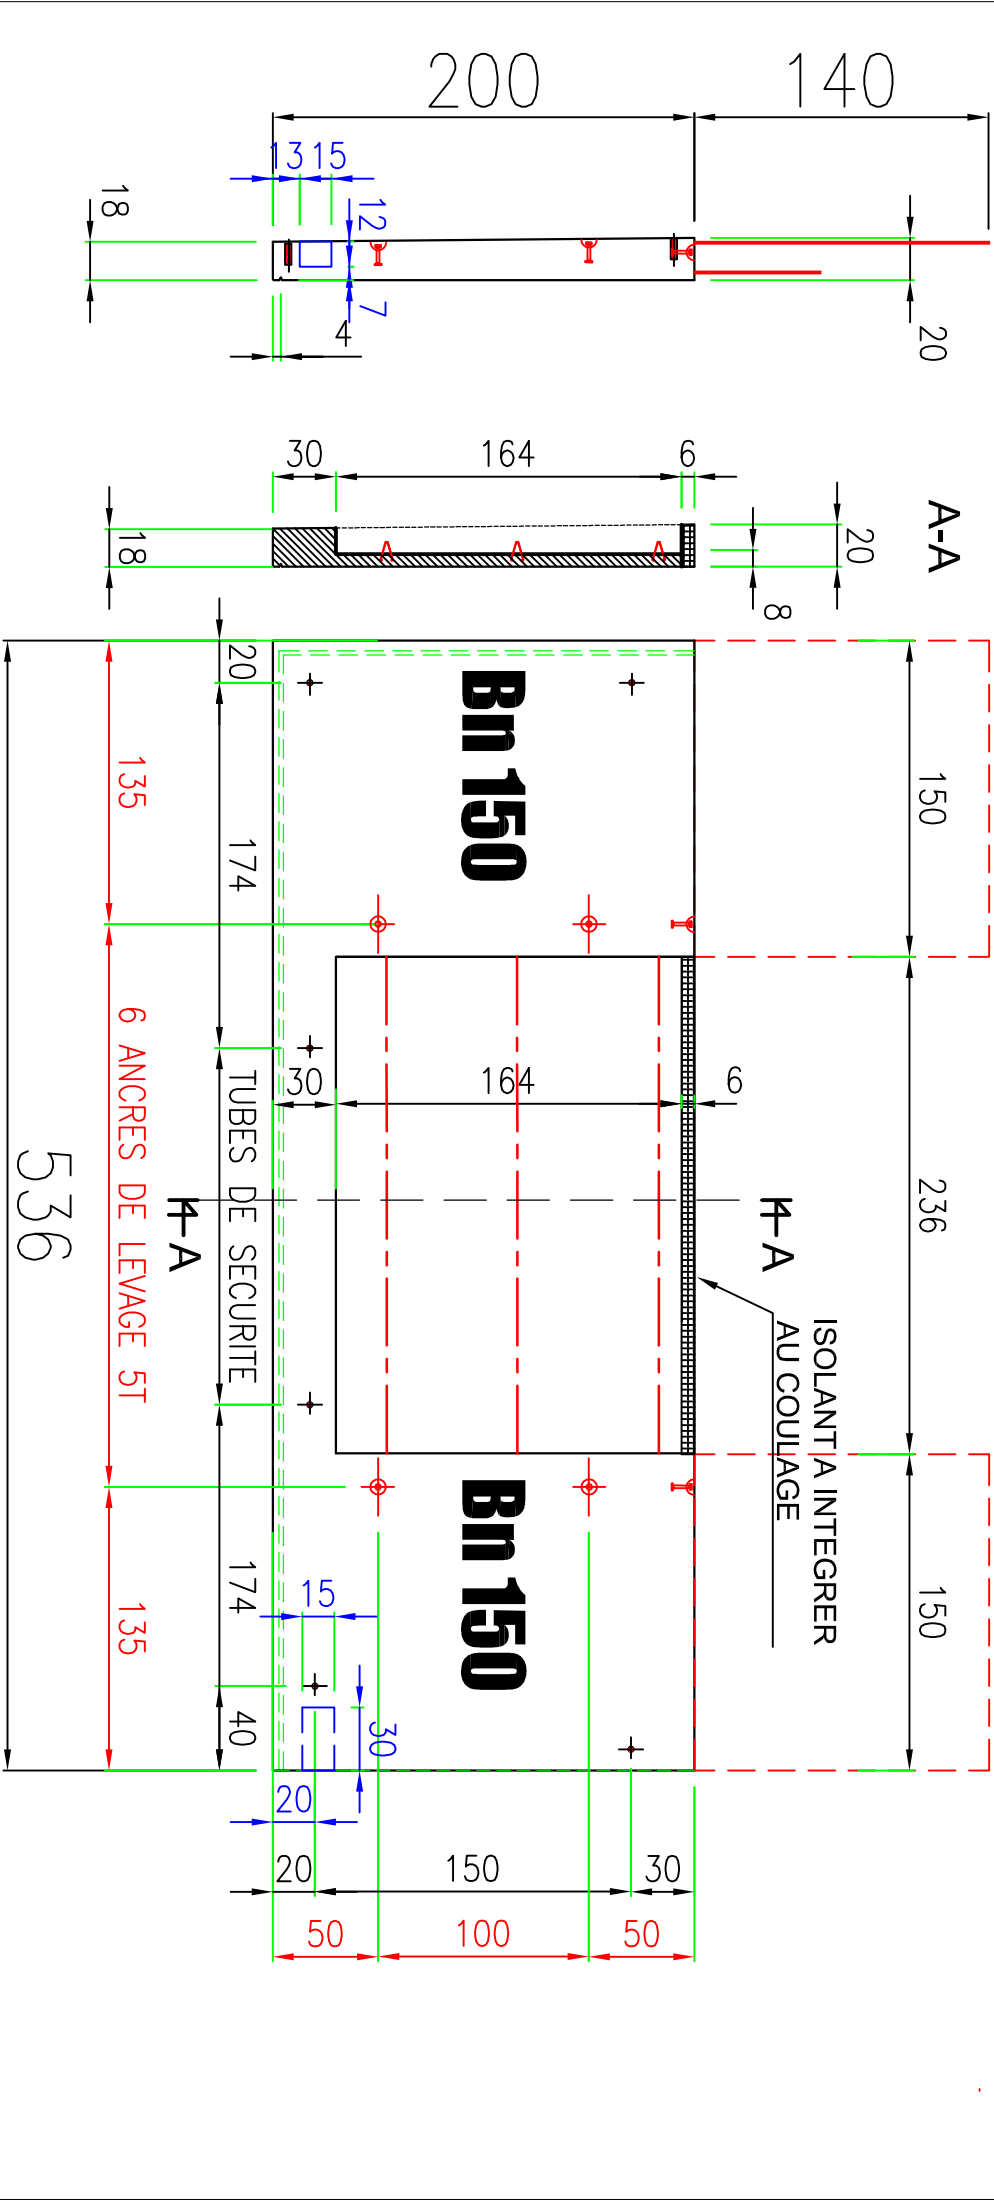

LEVAGE			INSERTS			INSERTS			INSERTS		
	Douille Ø	Renfort Ø dx		Ancre Frimeda T	Trifler		EBA	TP - JV		PVC Ø80	DATE: 29/03/2016
	Douille Ø	Renfort Ø		Renfort Ø			Douille étalement				Plan N°
							Ankrobox Ø50	Tube garde-corps		Indice	Page N°

