

FONTANEL- LE 180°

69 LA MULATIERE

BALCONS DU NIVEAU N-5
BAT B



EXE

Indice	Date	Designation des Modifications	Date :
A			01/02/2016
B			Affaire :
C			
D			Echelle :
E			
F			
G			
H			
I			

Type béton = B35 XF1
Aciers H.A et T.S = Fe E 500
Enrobage des armatures = ENR_CARMAT
Manutention = Tonnes


BUREAU D'ETUDE
PLATTARD SAS
414 Avenue de la
plage
BP 119
69540
Villefrance-sur-Saône
Tél: 04 74 02 20 20
Fax: 04 74 62 26 62



Ce plan est la propriété intellectuelle de la PLATTARD SAS, il ne peut être reproduit sans son autorisation.

Plancher Niveau R-5

Batiment B

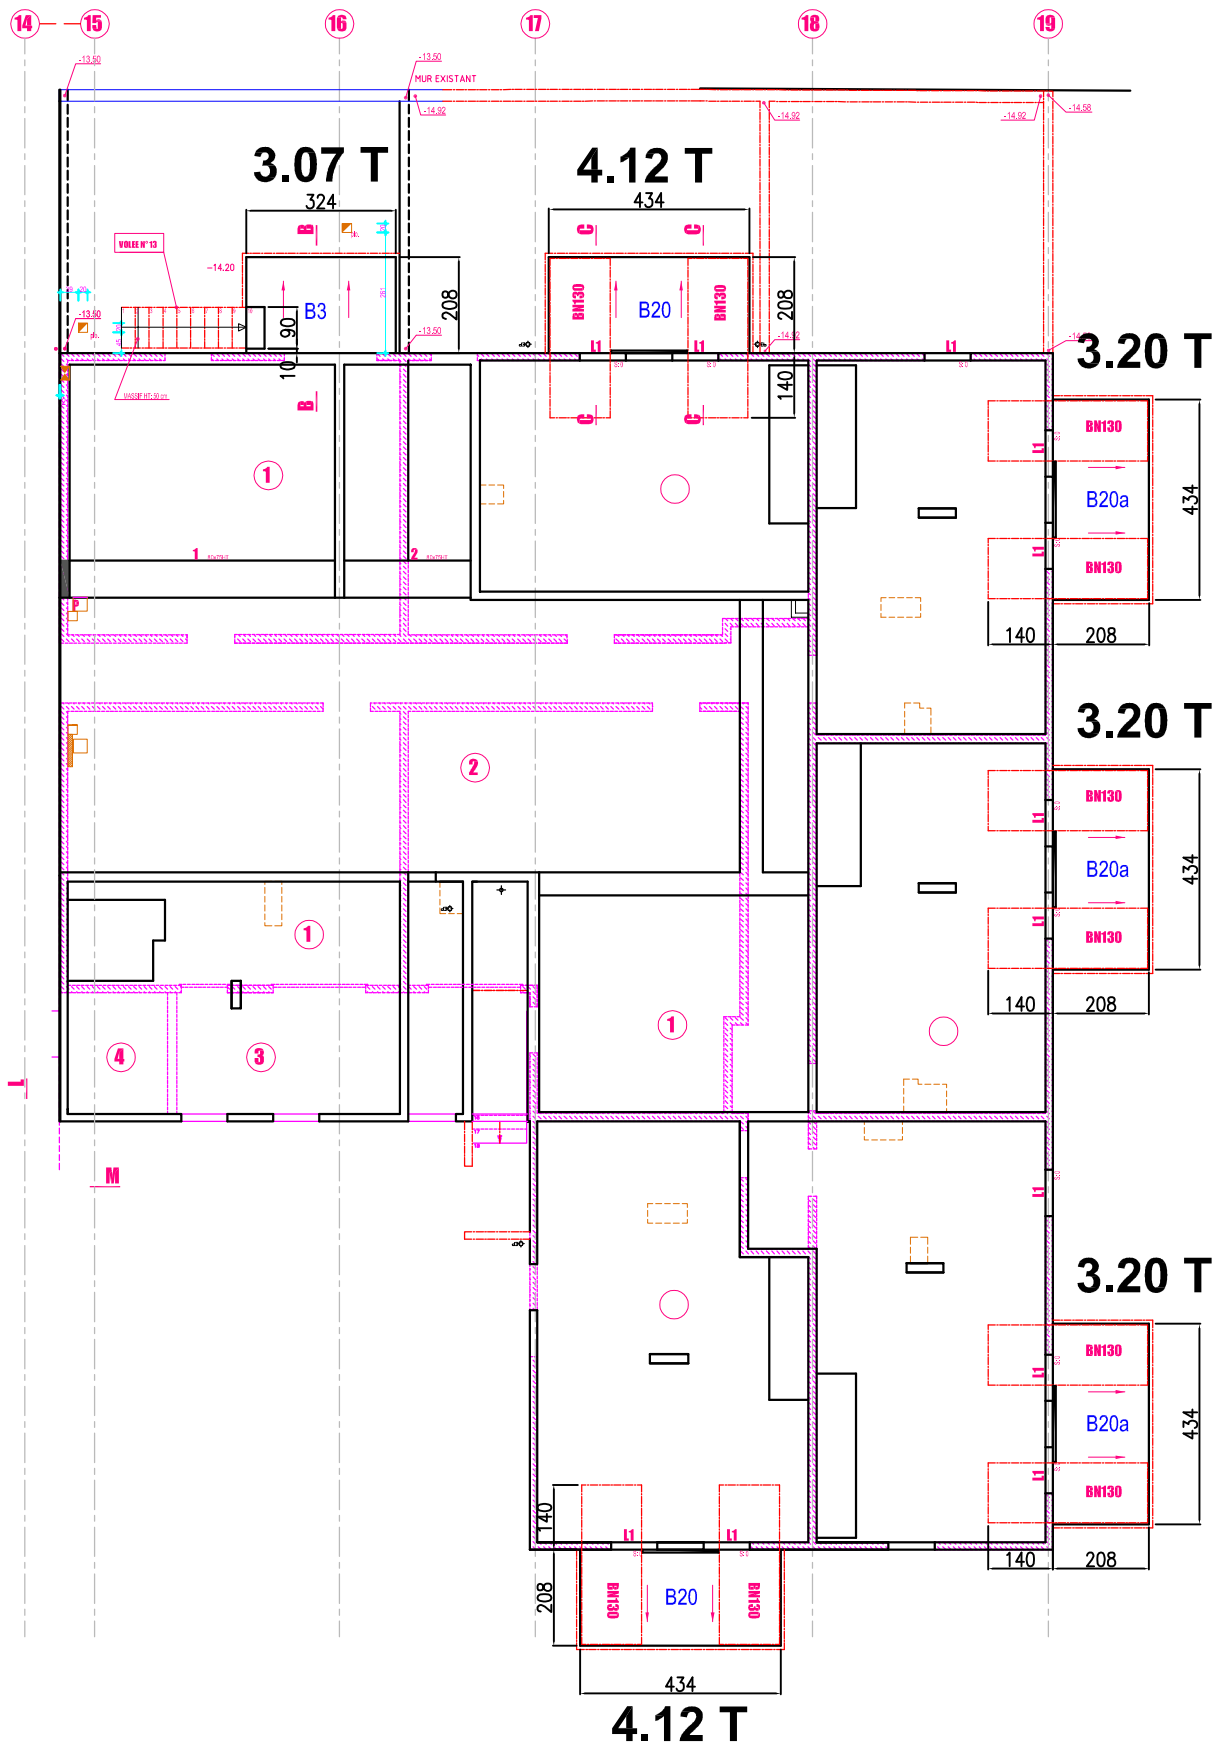

NOAHO

Chemin de Fontanière - 69350 La Mulatière

Création de logements

Les entreprises réalisant les travaux devront tenir compte des derniers plans architecte lors de la réalisation des travaux
Les plans du be MATTE ne doivent servir qu'au corps d'état concerné et doivent être des plans d'exécution.

ARCHITECTE(S): ATELIER DE LA PASSERELLE

MO DELEGUE:

BET STRUCTURE: MATTE SAS

MOE: PSO Ingénierie

BET FLUIDES: PRELEM

CSPS: SUD EST COORDINATION

ECONOMISTE: EXECO

OPC:

BUREAU DE CONTROLE: Bureau VERITAS

ENTREPRISE(S): Fontanel-pbc

Bât: B
PLANCHER sur -5
Coffrage

EXE

Contrainte de sol: 8 bars ELS

INDICE	DATE	MODIFICATIONS

Aciers HA (T) FeE500

Aciers Doux (Ø) FeE 235

Aciers TS FeE 500

Béton fc28 >= 25MPa

Enrobage = 3 cm

PLAN N°
B20 0

DATE : 06/03/2016

MATTÉ
BUREAU D'ÉTUDES
STRUCTURES ET FLUIDES

119 BOULEVARD STALINGRAD 69100 VILLEURBANNE

Tél. 04 72 44 02 87 Fax 04 72 44 26 59

E-mail : bet@matte.fr

Dessiné par : J.BO

Contrôlé par : P.LIN

Echelle : 1/50°


Affaire N°
13.12.119

MOULE	N	NC	observations	CONTROLE	N	NC	observations	BETON	N	NC	observations	FICHE AUTO-CONTROLE
Conformité moule				Dimensions				Conformité béton				Opérateur :
Etat du moule				Armature				Mise en place				Responsable prod :
Propreté et huilage				Inserts				Aspect de surface				Date :

Ent. FONTANEL			Elément: BALCONS			Surface: 6.74 m²			POIDS			REPERE			Nbr		
LA MULATIERE			coffrage / ferrillage			Volume: 1.28 m3			3.07 T			B3			1		





PLAN DE FABRCATION

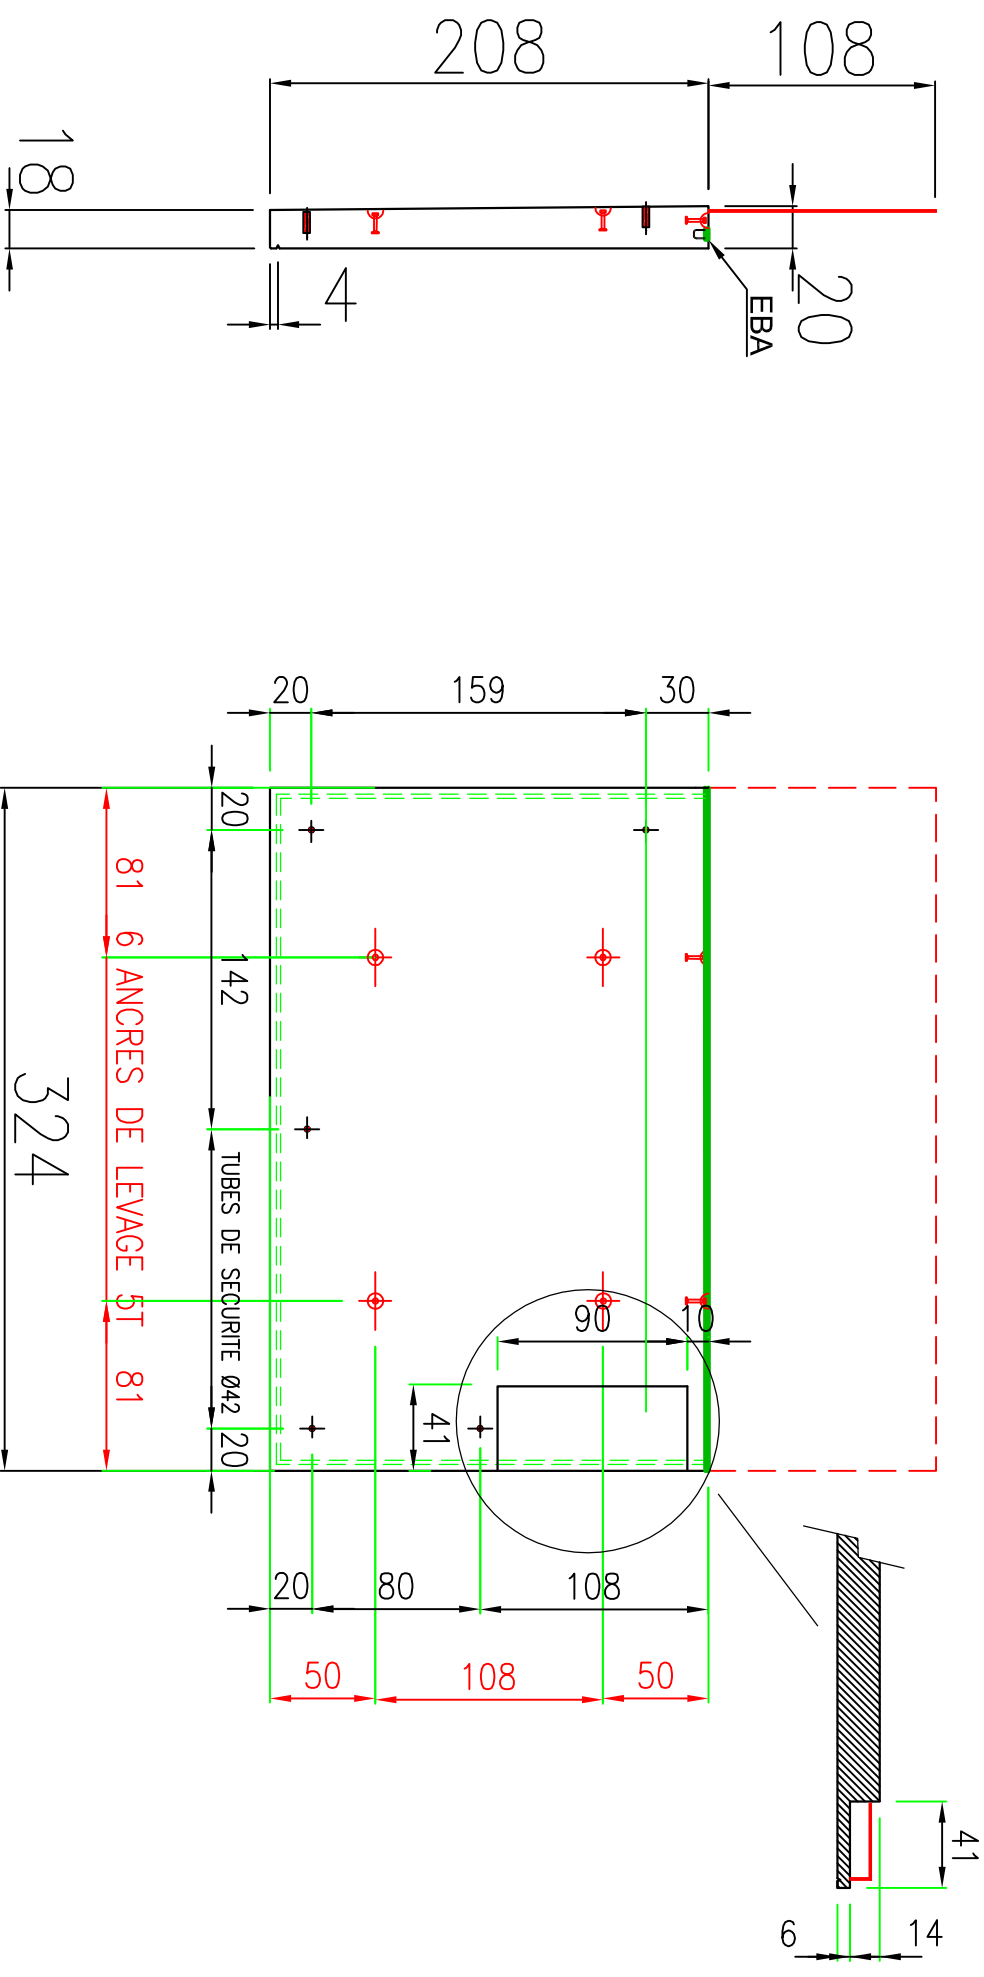

LEVAGE				INSERTS				INSERTS				INSERTS			
Douille Ø	Douille Ø	Douille Ø	Douille Ø	Ancre Frimeda T	Ancre Frimeda T	Ancre Frimeda T	Ancre Frimeda T	EBA	EBA	EBA	EBA	TP - JV	TP - JV	TP - JV	TP - JV
Renfort Ø	Renfort Ø	Renfort Ø	Renfort Ø	Renfort Ø	Renfort Ø	Renfort Ø	Renfort Ø	Douille étalement	Douille étalement	Douille étalement	Douille étalement	PVC Ø80	PVC Ø80	PVC Ø80	PVC Ø80
Renfort Ø	Renfort Ø	Renfort Ø	Renfort Ø	Trifier	Trifier	Trifier	Trifier	Ankrobox Ø50	Ankrobox Ø50	Ankrobox Ø50	Ankrobox Ø50	Tube garde-corps	Tube garde-corps	Tube garde-corps	Tube garde-corps
DATE: 07/01/2016				Plan N°				Indice				Page N°			

MOULE	N	NC	observations	CONTROLE	N	NC	observations	BETON	N	NC	observations	FICHE AUTO-CONTROLE
Conformité moule				Dimensions				Conformité béton				Opérateur :
Etat du moule				Armature				Mise en place				Responsable prod :
Propreté et huilage				Inserts				Aspect de surface				Date :

Ent. FONTANEL		Elément: BALCONS		 PLATTARD S.A.S.		PLAN DE FABRCATION		Surface: 9.05 m²		POIDS		REPERE		Nbr	
LA MULATIERE		coffrage / ferrillage				Volume: 1.33 m3		3.20 T		B20a		3			

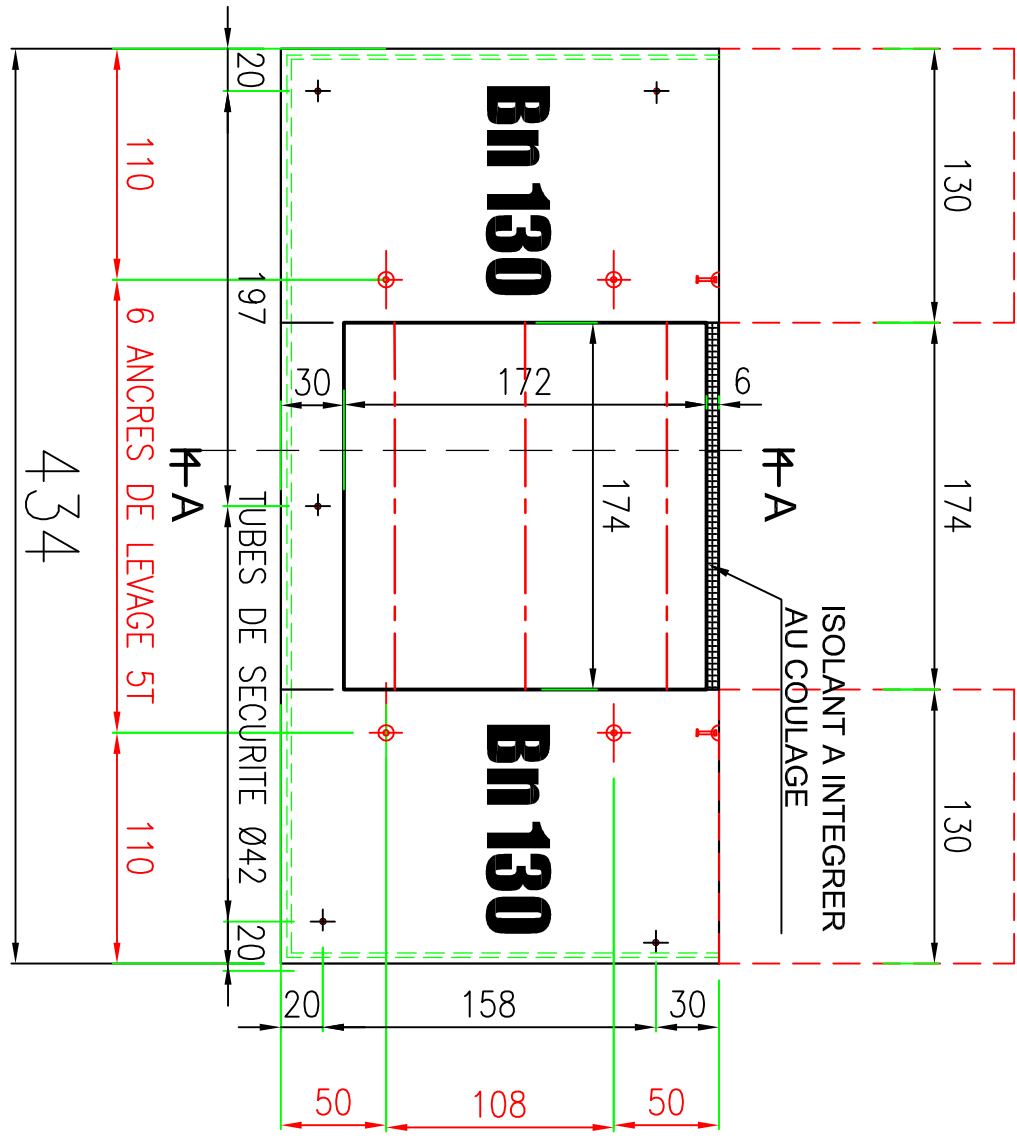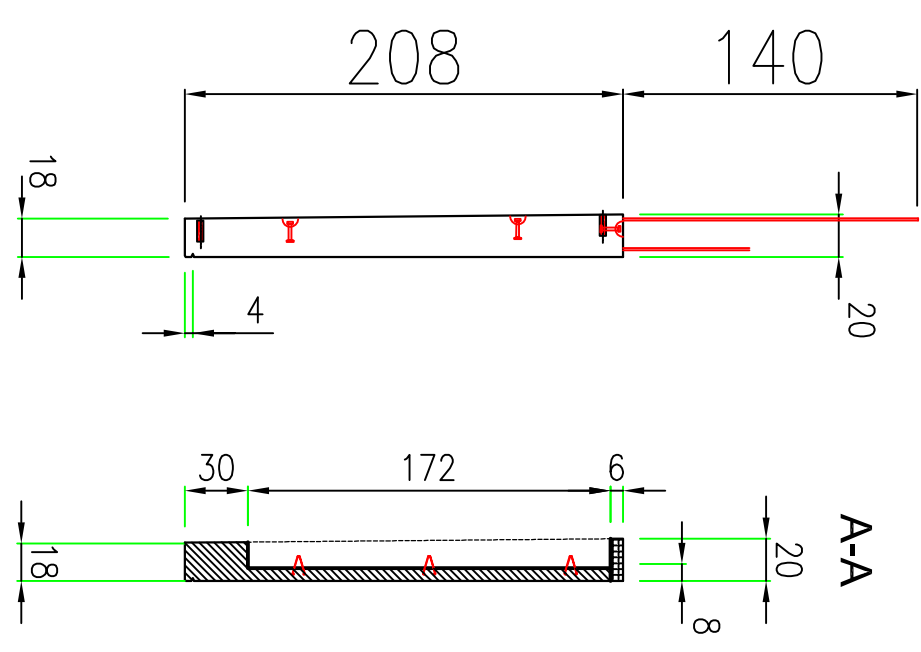

LEVAGE				INSERTS				INSERTS				INSERTS			
	Douille Ø		Ancre Frimeda T		Douille Ø		EBA		Douille étalement		TP - JV		PVC Ø80		DATE: 16/11/2015
	Douille Ø		Renfort Ø dx		Renfort Ø		Ankrobox Ø50		Tubes de securite Ø42		Indice		Plan N°		Page N°