

17/11/2015



GROUPE PLATTARD

CHANTIER

LA MULATIERE LE 180°



ENTREPRISE




BALCONS PRINCIPE ARMATURE

INDICE

B

mis à jour Plan B.E BN
3/12/15 - mis à jour ATTENTES VOÏE

CARNET DE DETAIL PREFAB

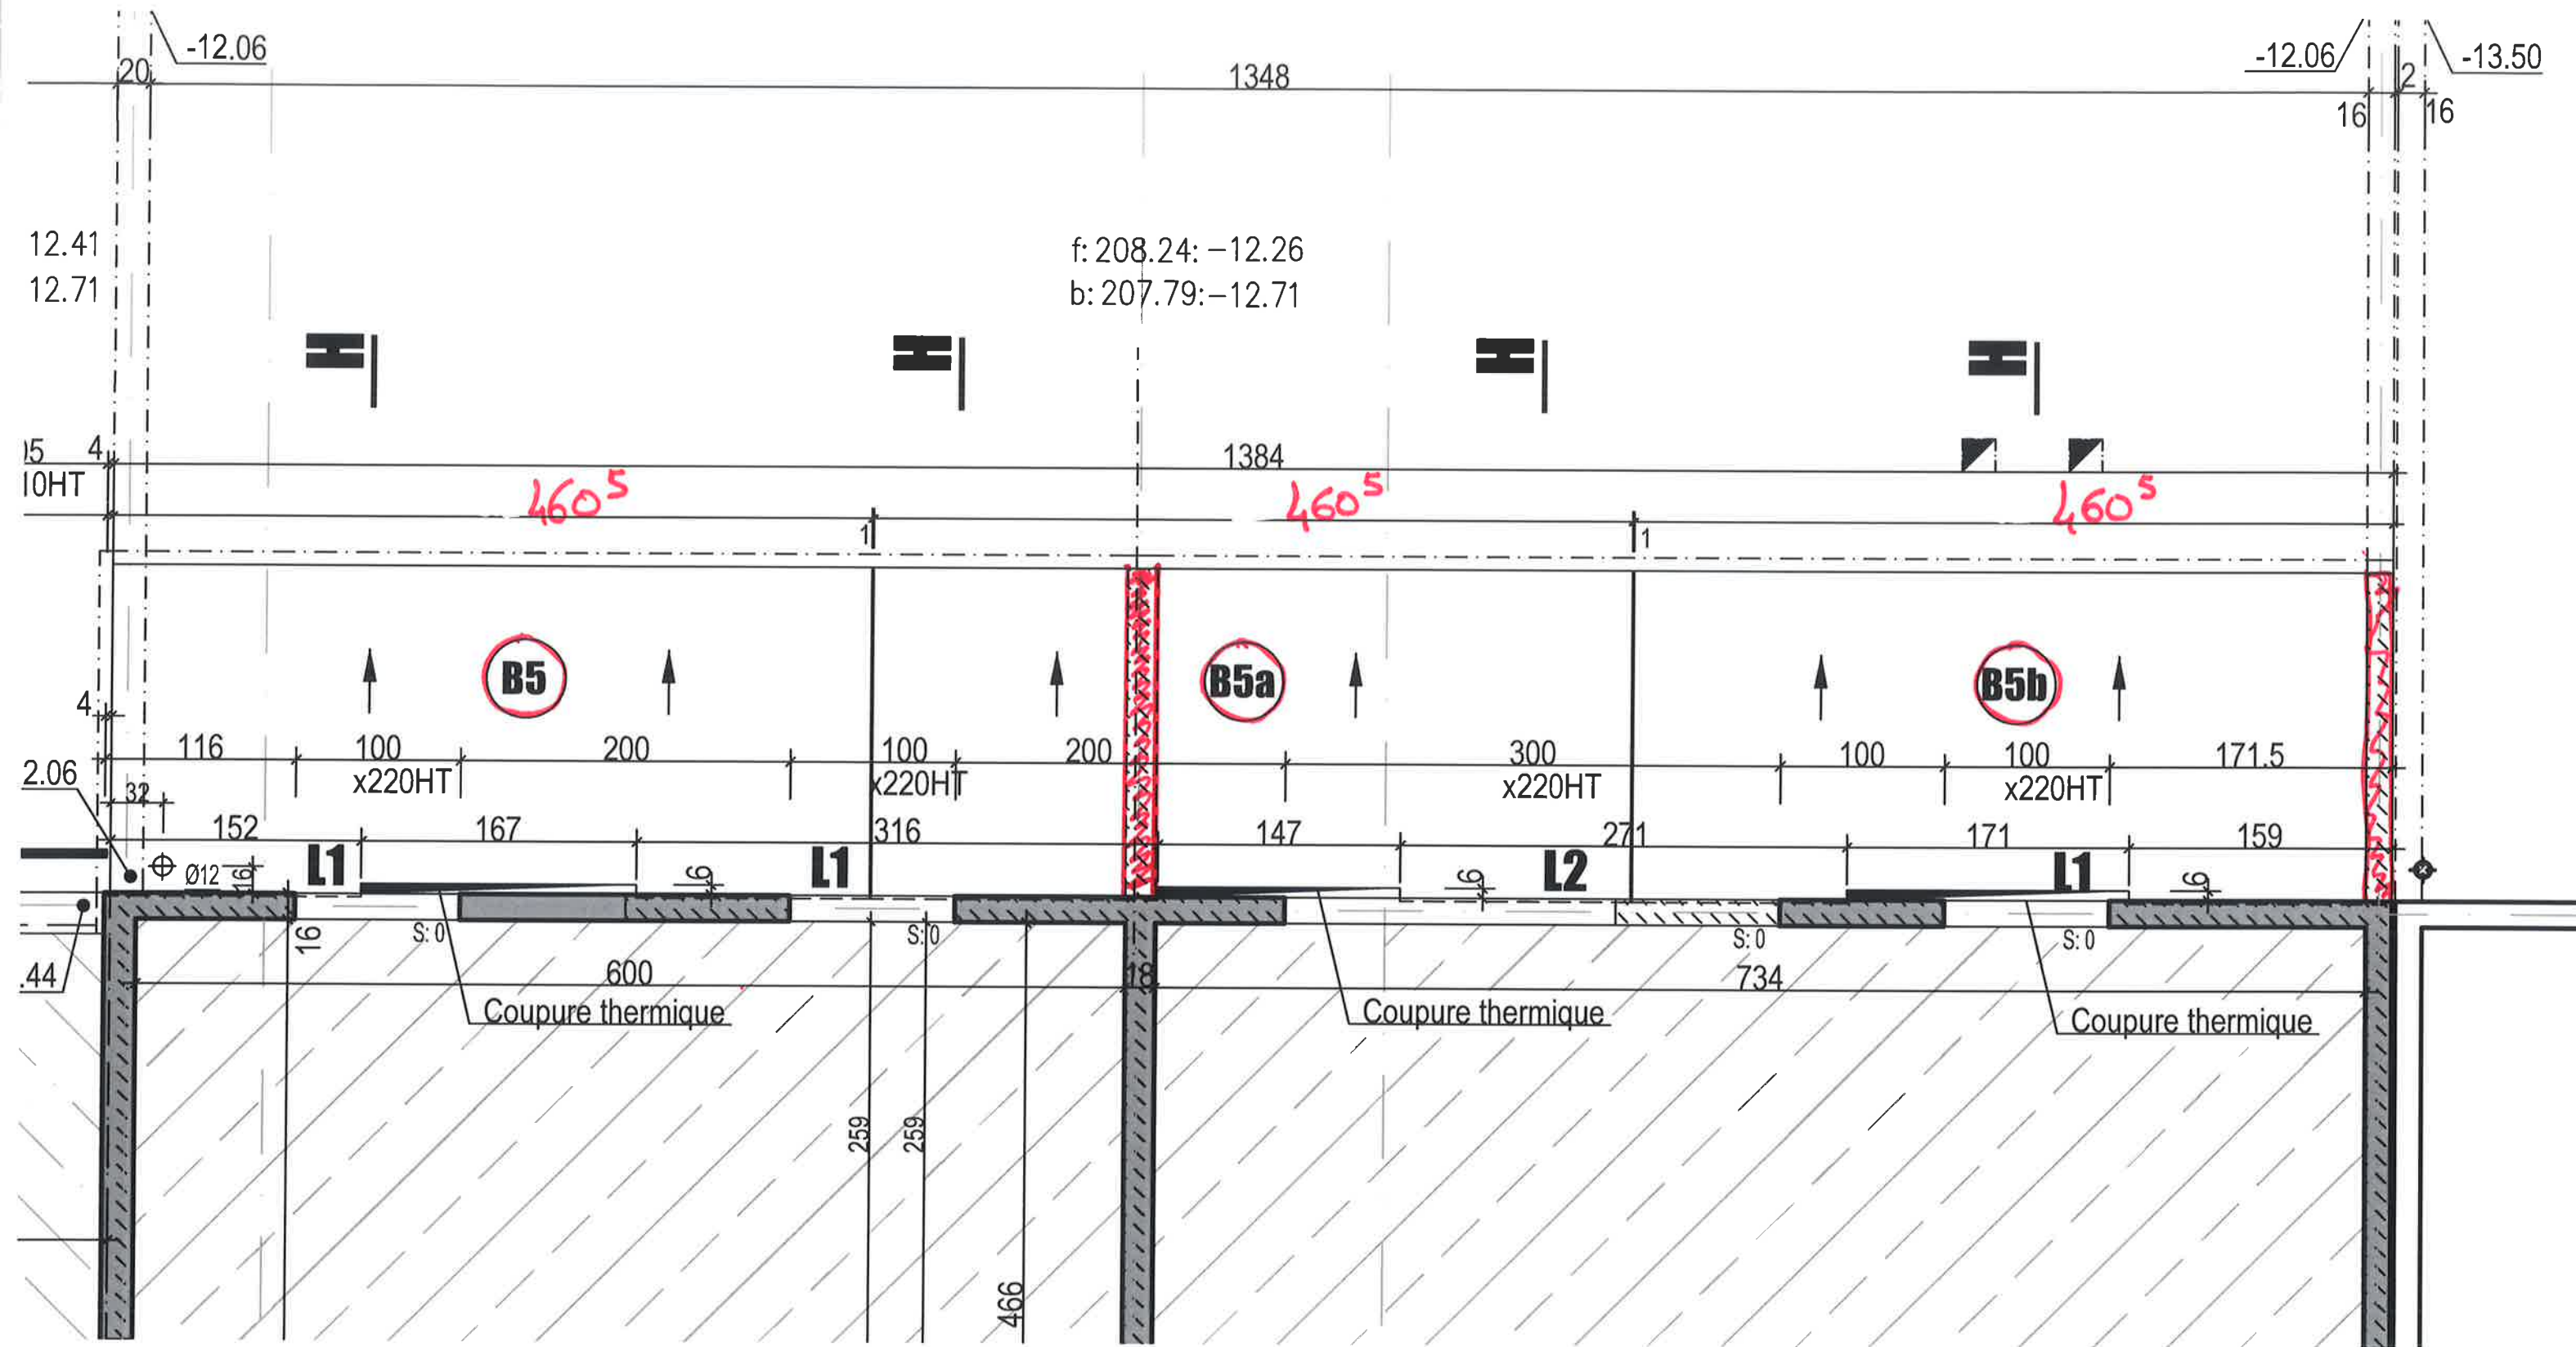

18

B.N

Enrobage

3

$\phi 8^r$

cadre $\phi 8^r$

2

Enrobage

$\phi 14^r$

le 2 dec ②

4

7


105

2 25


20

Armature entre BN

6 laine de roche


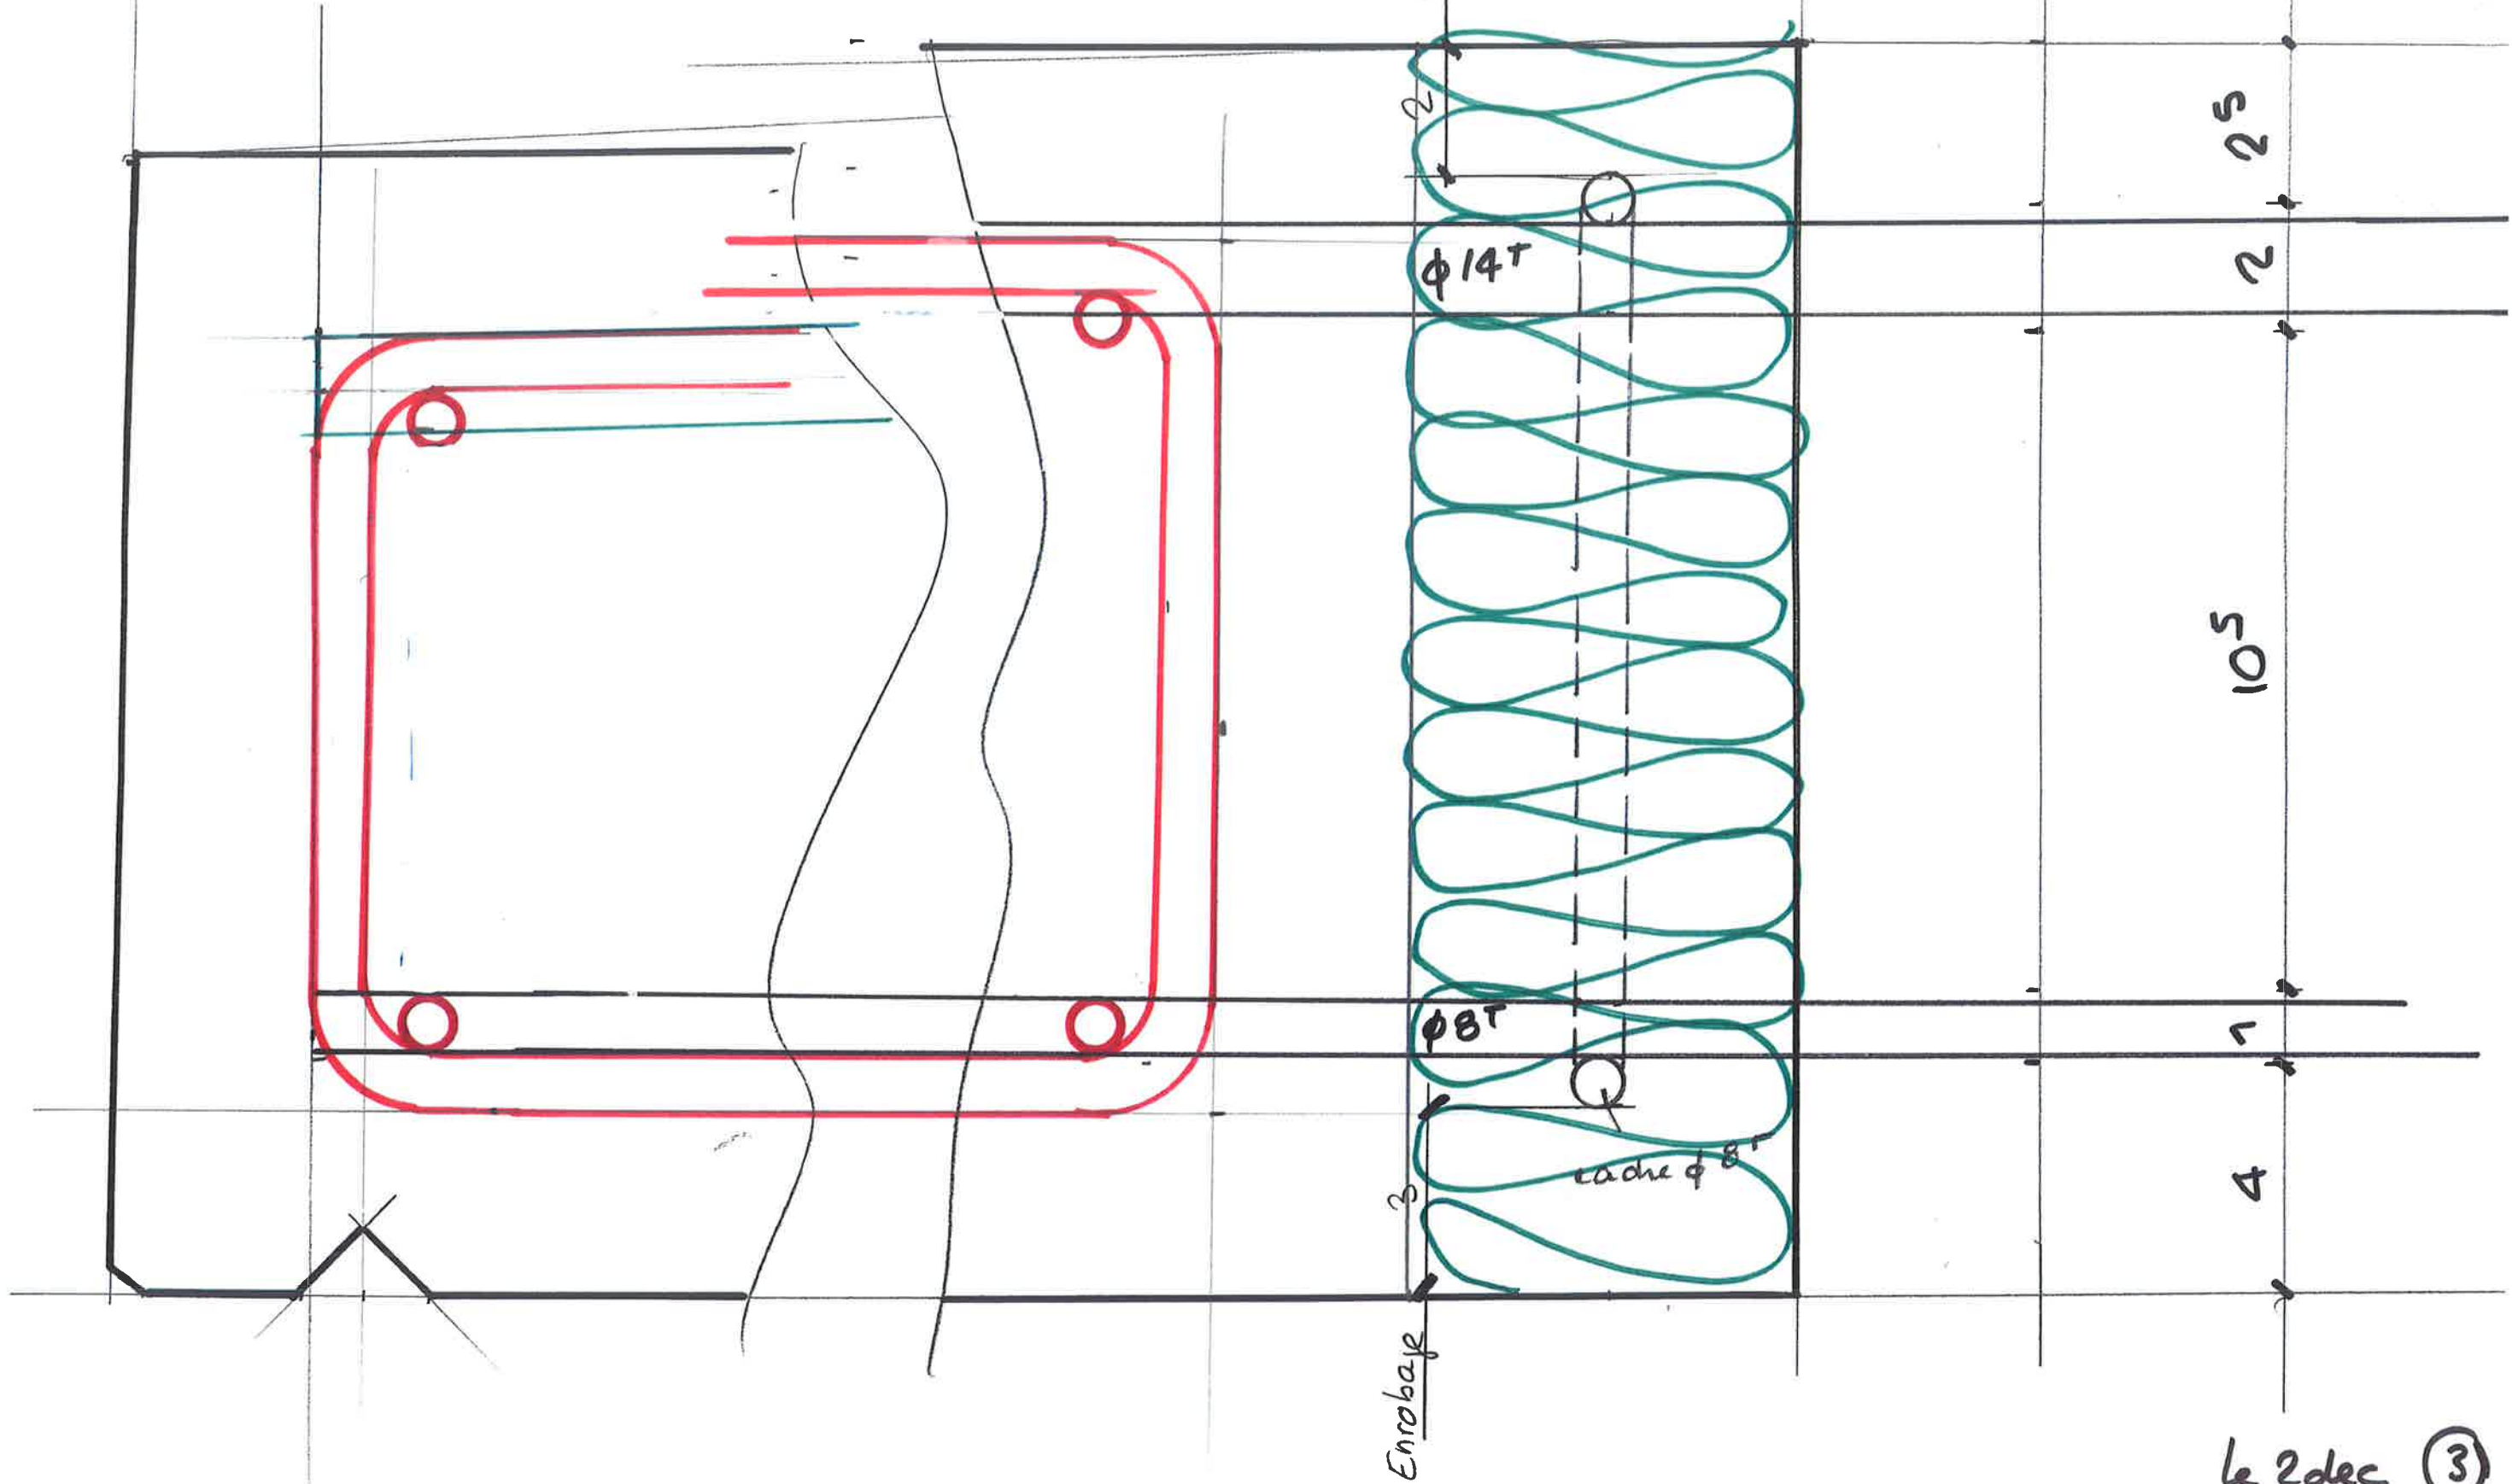


le 2 dec (3)

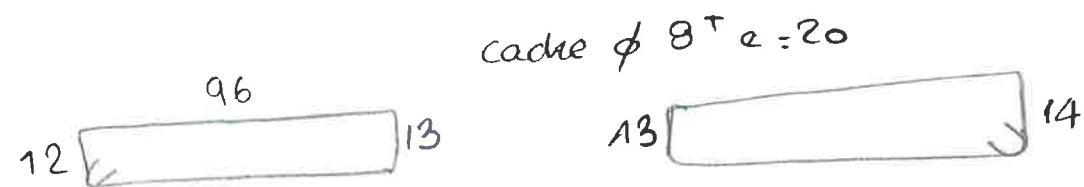


Armature entre B.N

22 points $\phi 8^T a=20$

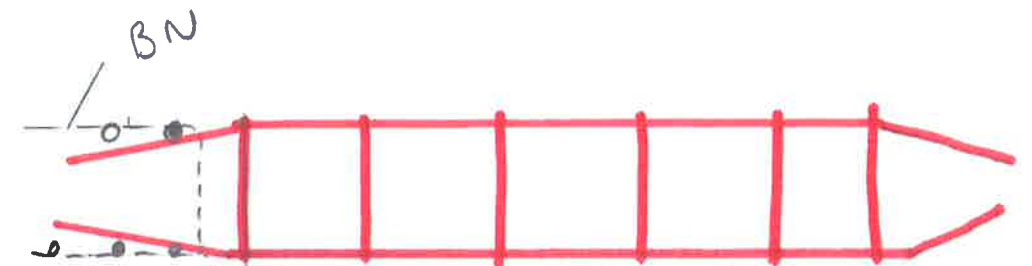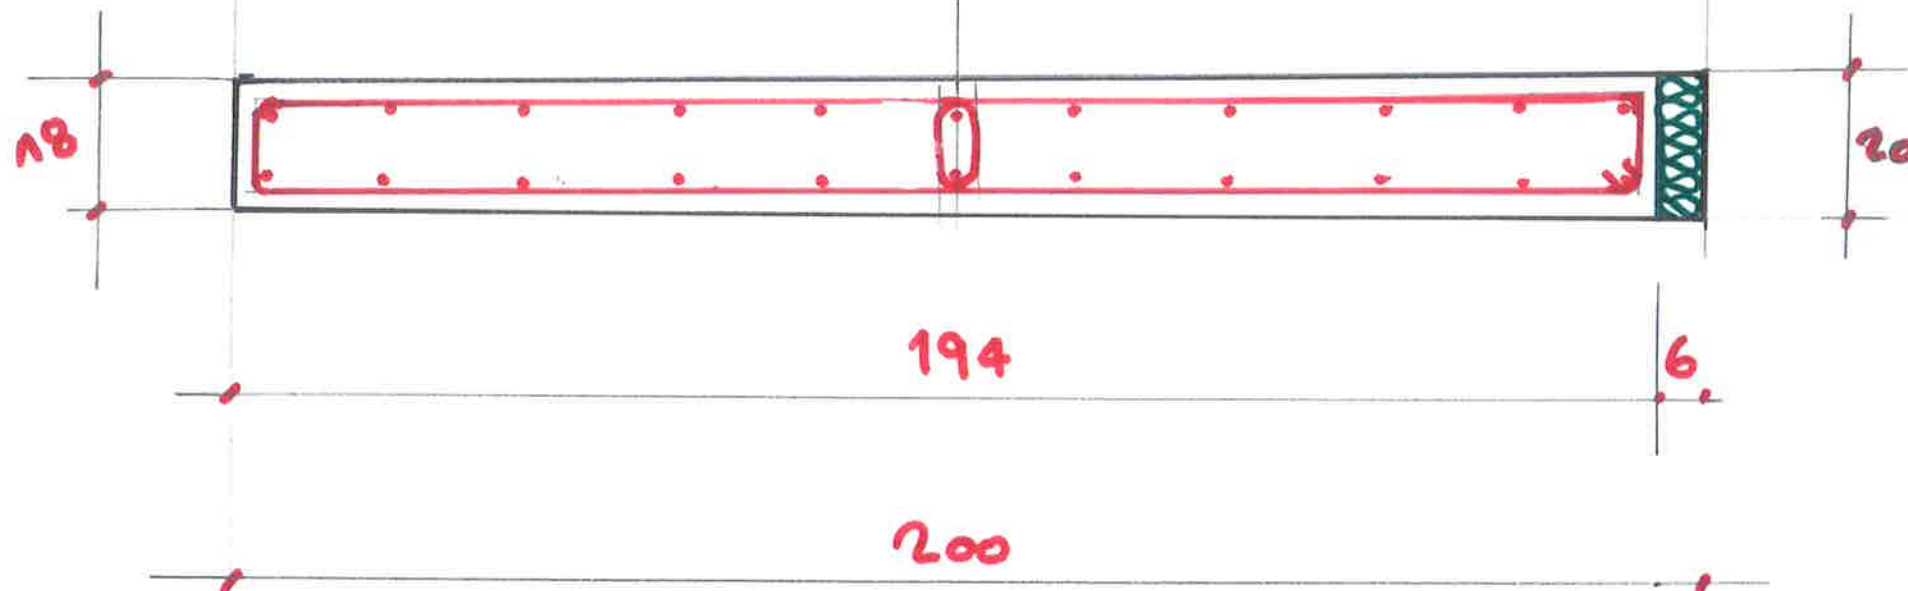

BN

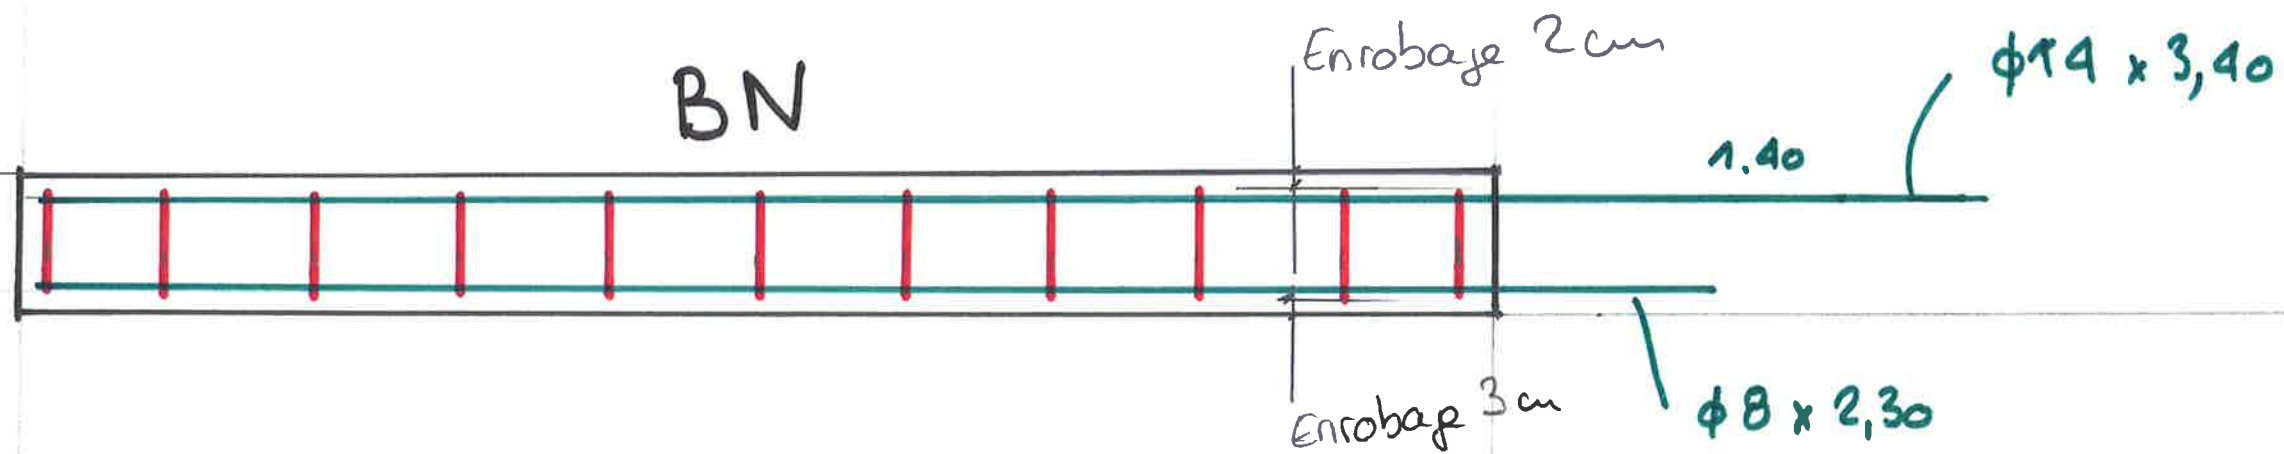


PLAN BE le 2. déc




FERRAILLAGE BN POUR BALCONS ISOLES

Armature à poser
dans le m^e plan

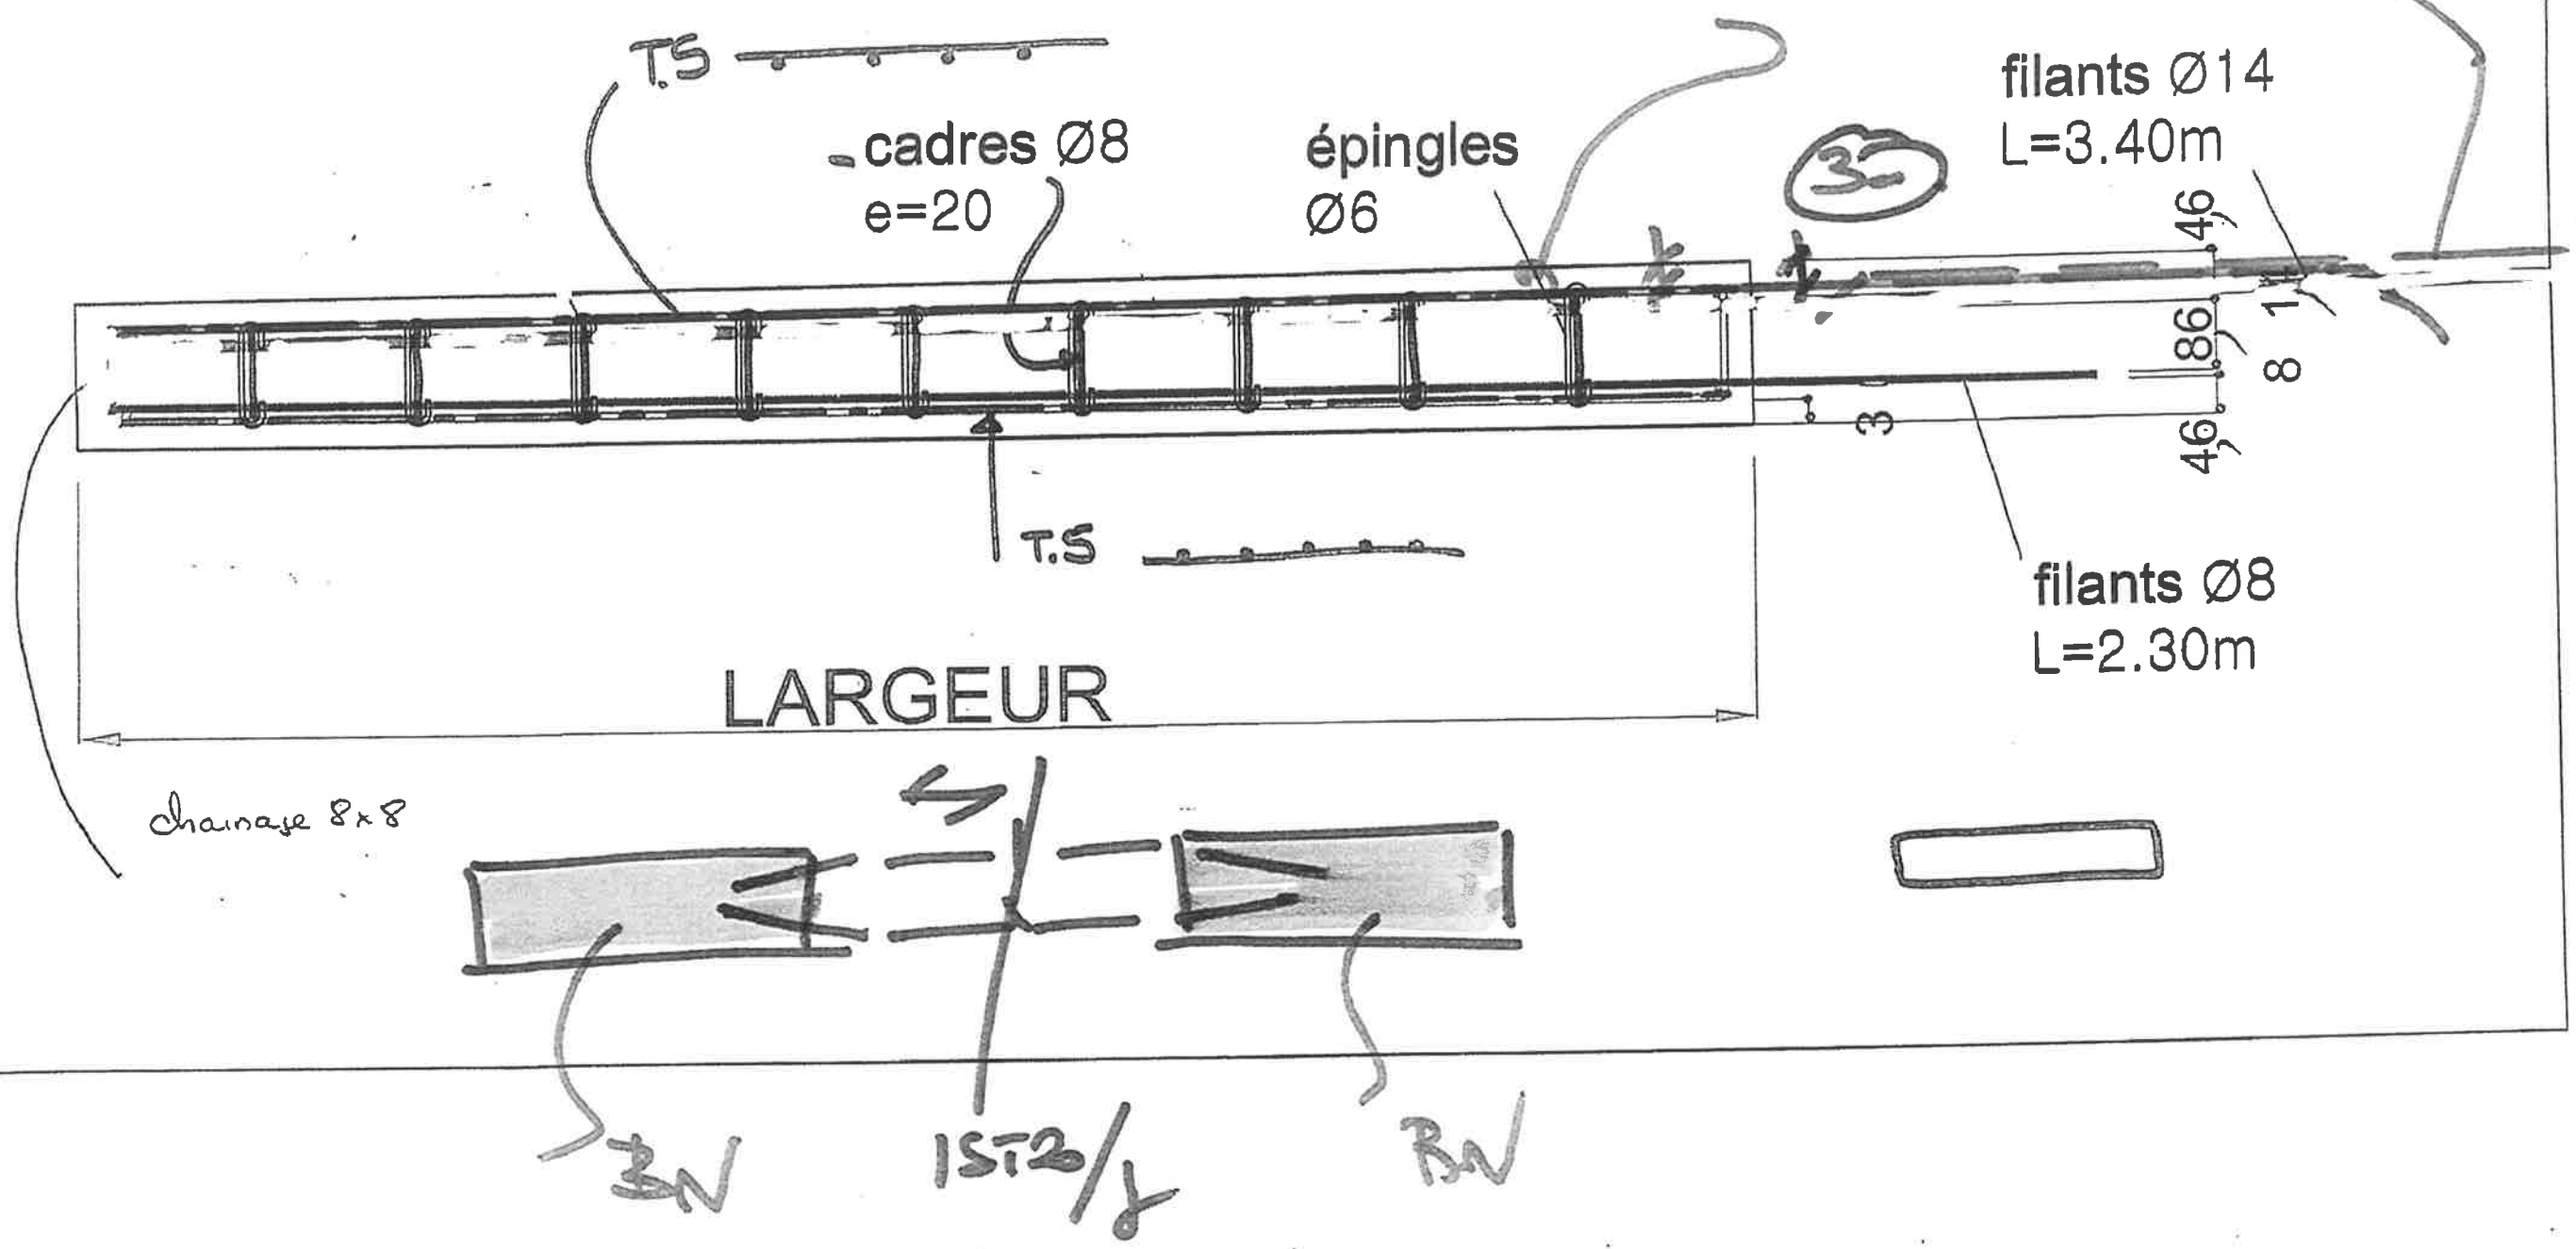


MOULE	N NC	observations	CONTROLE	N NC	observations	BETON	N NC	observations	FICHE AUTO-CONTROLE
Conformité moule			Dimensions			Conformité béton			Opérateur :
Etat du moule			Armature			Mise en place			Responsable prod :
Propreté et huilage			Inserts			Aspect de surface			Date :

Ent. FONTANEL			PLAN DE FABRCATION	Surface: 9.21 m²	POIDS	REPERE	Nbr		
LA MULATIERE	Elément: BALCONS			Volume: 1.70 m3	4.10 T			B5	1
	coffrage / ferrailage								

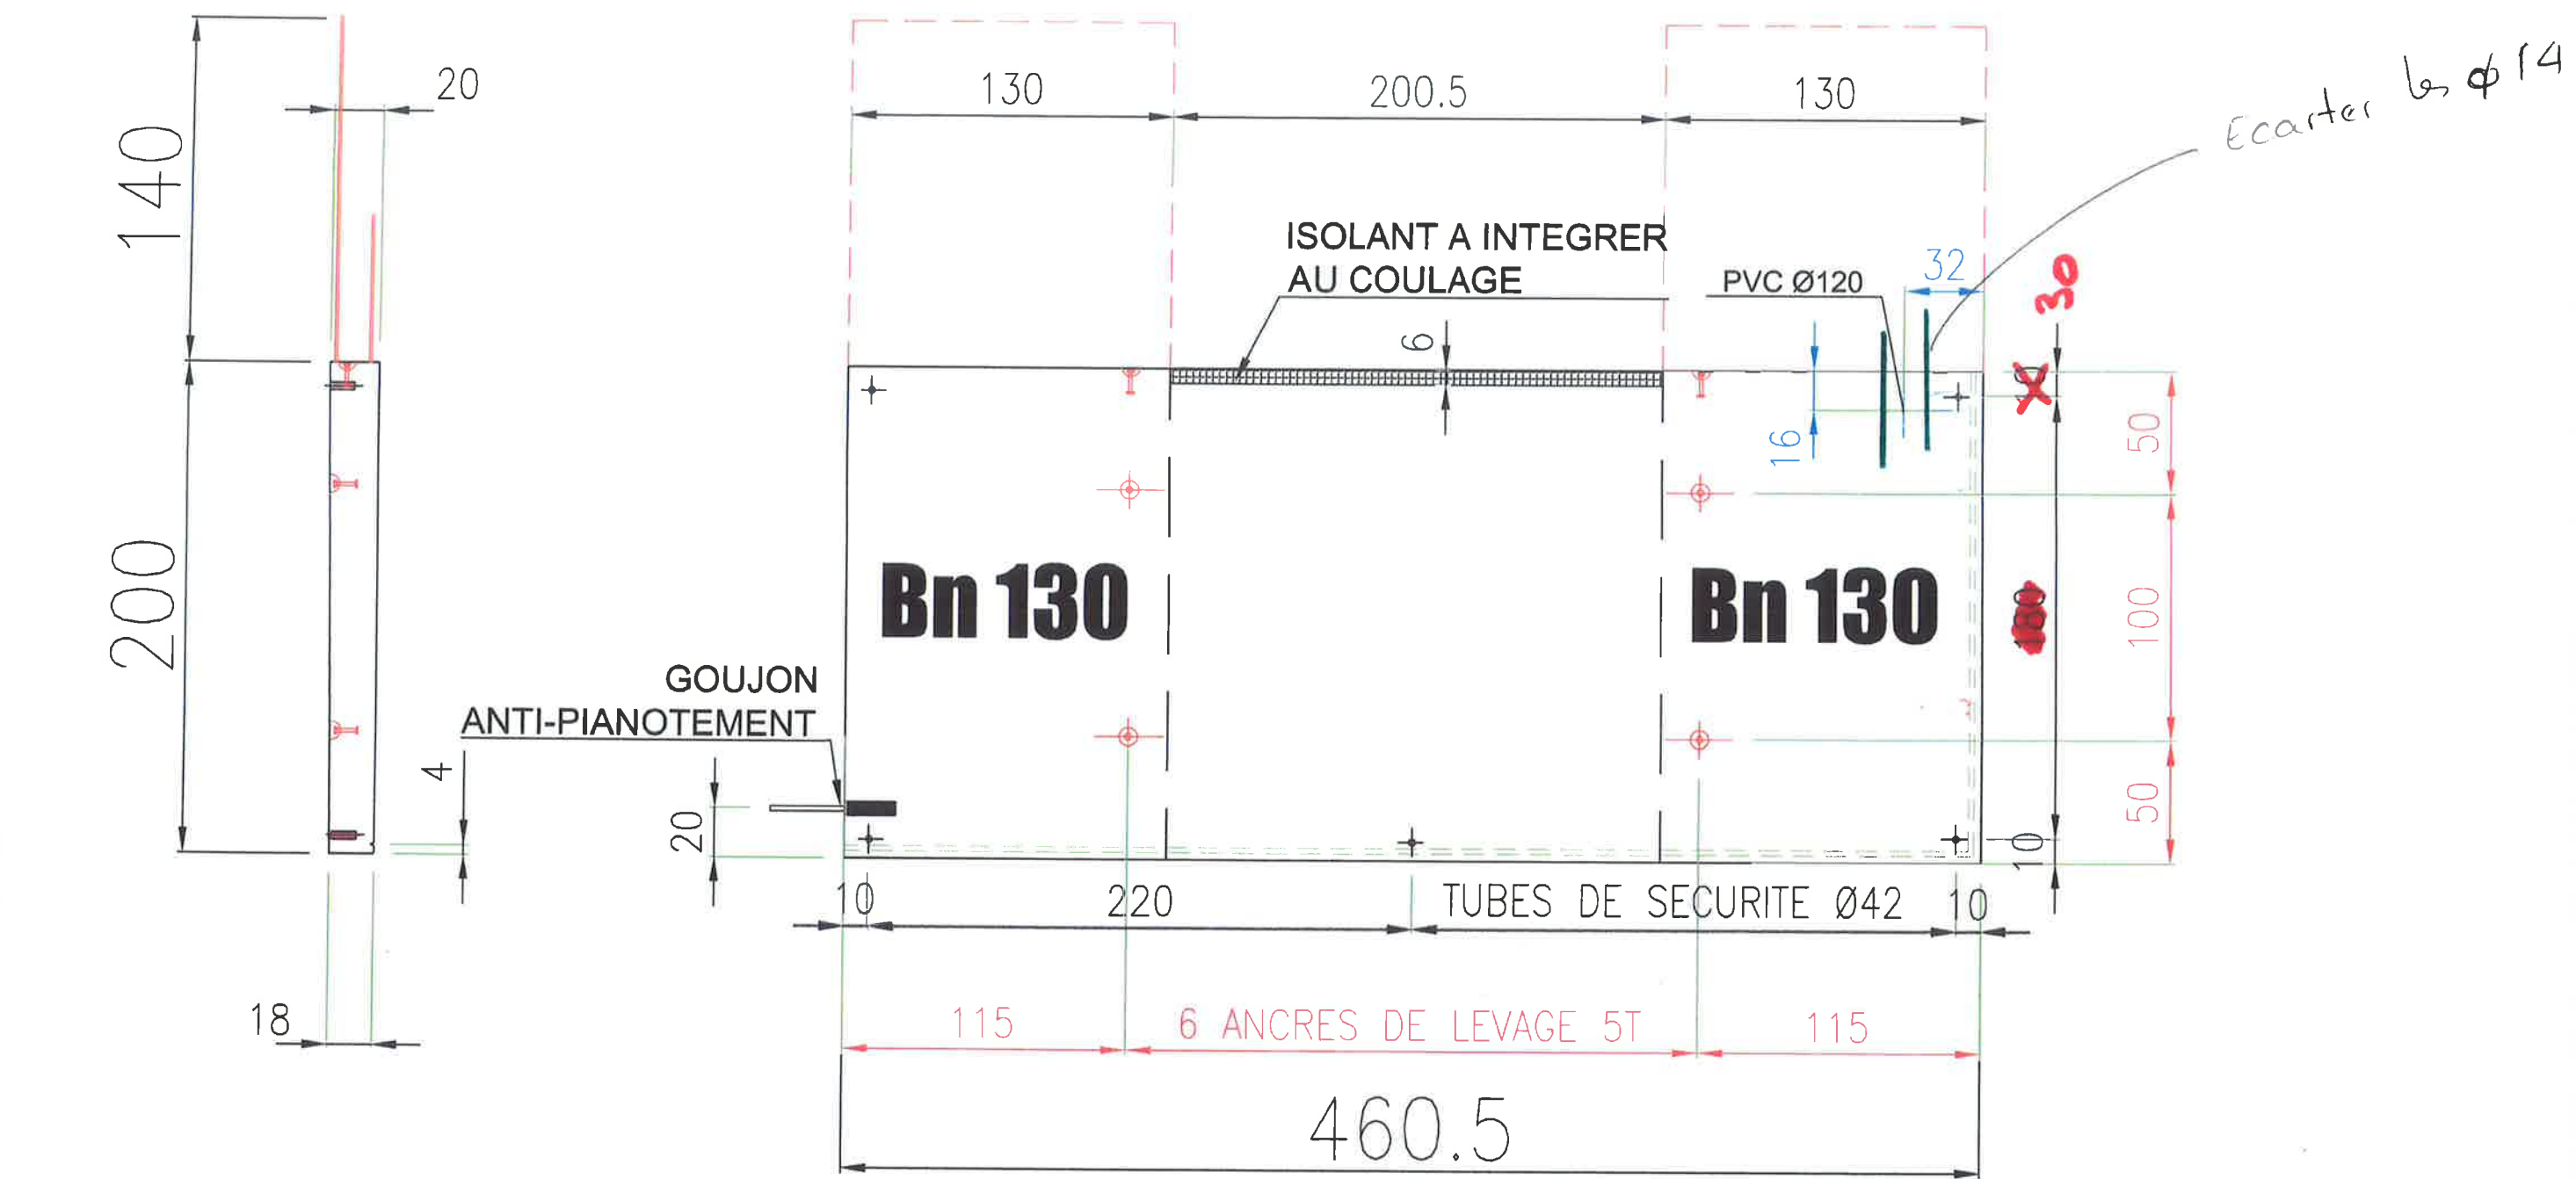


LEVAGE		Douille Ø	INSERTS		Ancre Frimeda T	INSERTS		EBA	INSERTS		TP - JV	DATE: 16/11/2015									
		Douille Ø			Renfort Ø			Douille étalement			PVC Ø80	Plan N°					Page N°				
		Renfort Ø dx			Trifer			Ankrobox Ø50			Tube garde-corps	Indice									

MOULE		N	NC	observations	CONTROLE		N	NC	observations	BETON		N	NC	observations	FICHE AUTO-CONTROLE	
Conformité moule					Dimensions					Conformité béton					Opérateur :	
Etat du moule					Armature					Mise en place					Responsable prod :	
Propreté et huilage					Inserts					Aspect de surface					Date :	
Ent. FONTANEL LA MULATIERE		Elément: BALCONS coffrage / ferraillage					PLAN DE FABRCATION		Surface:		9.21 m²	POIDS		REPERE		Nbr
												4.10 T		B5a		1
									Volume:		1.70 m3					

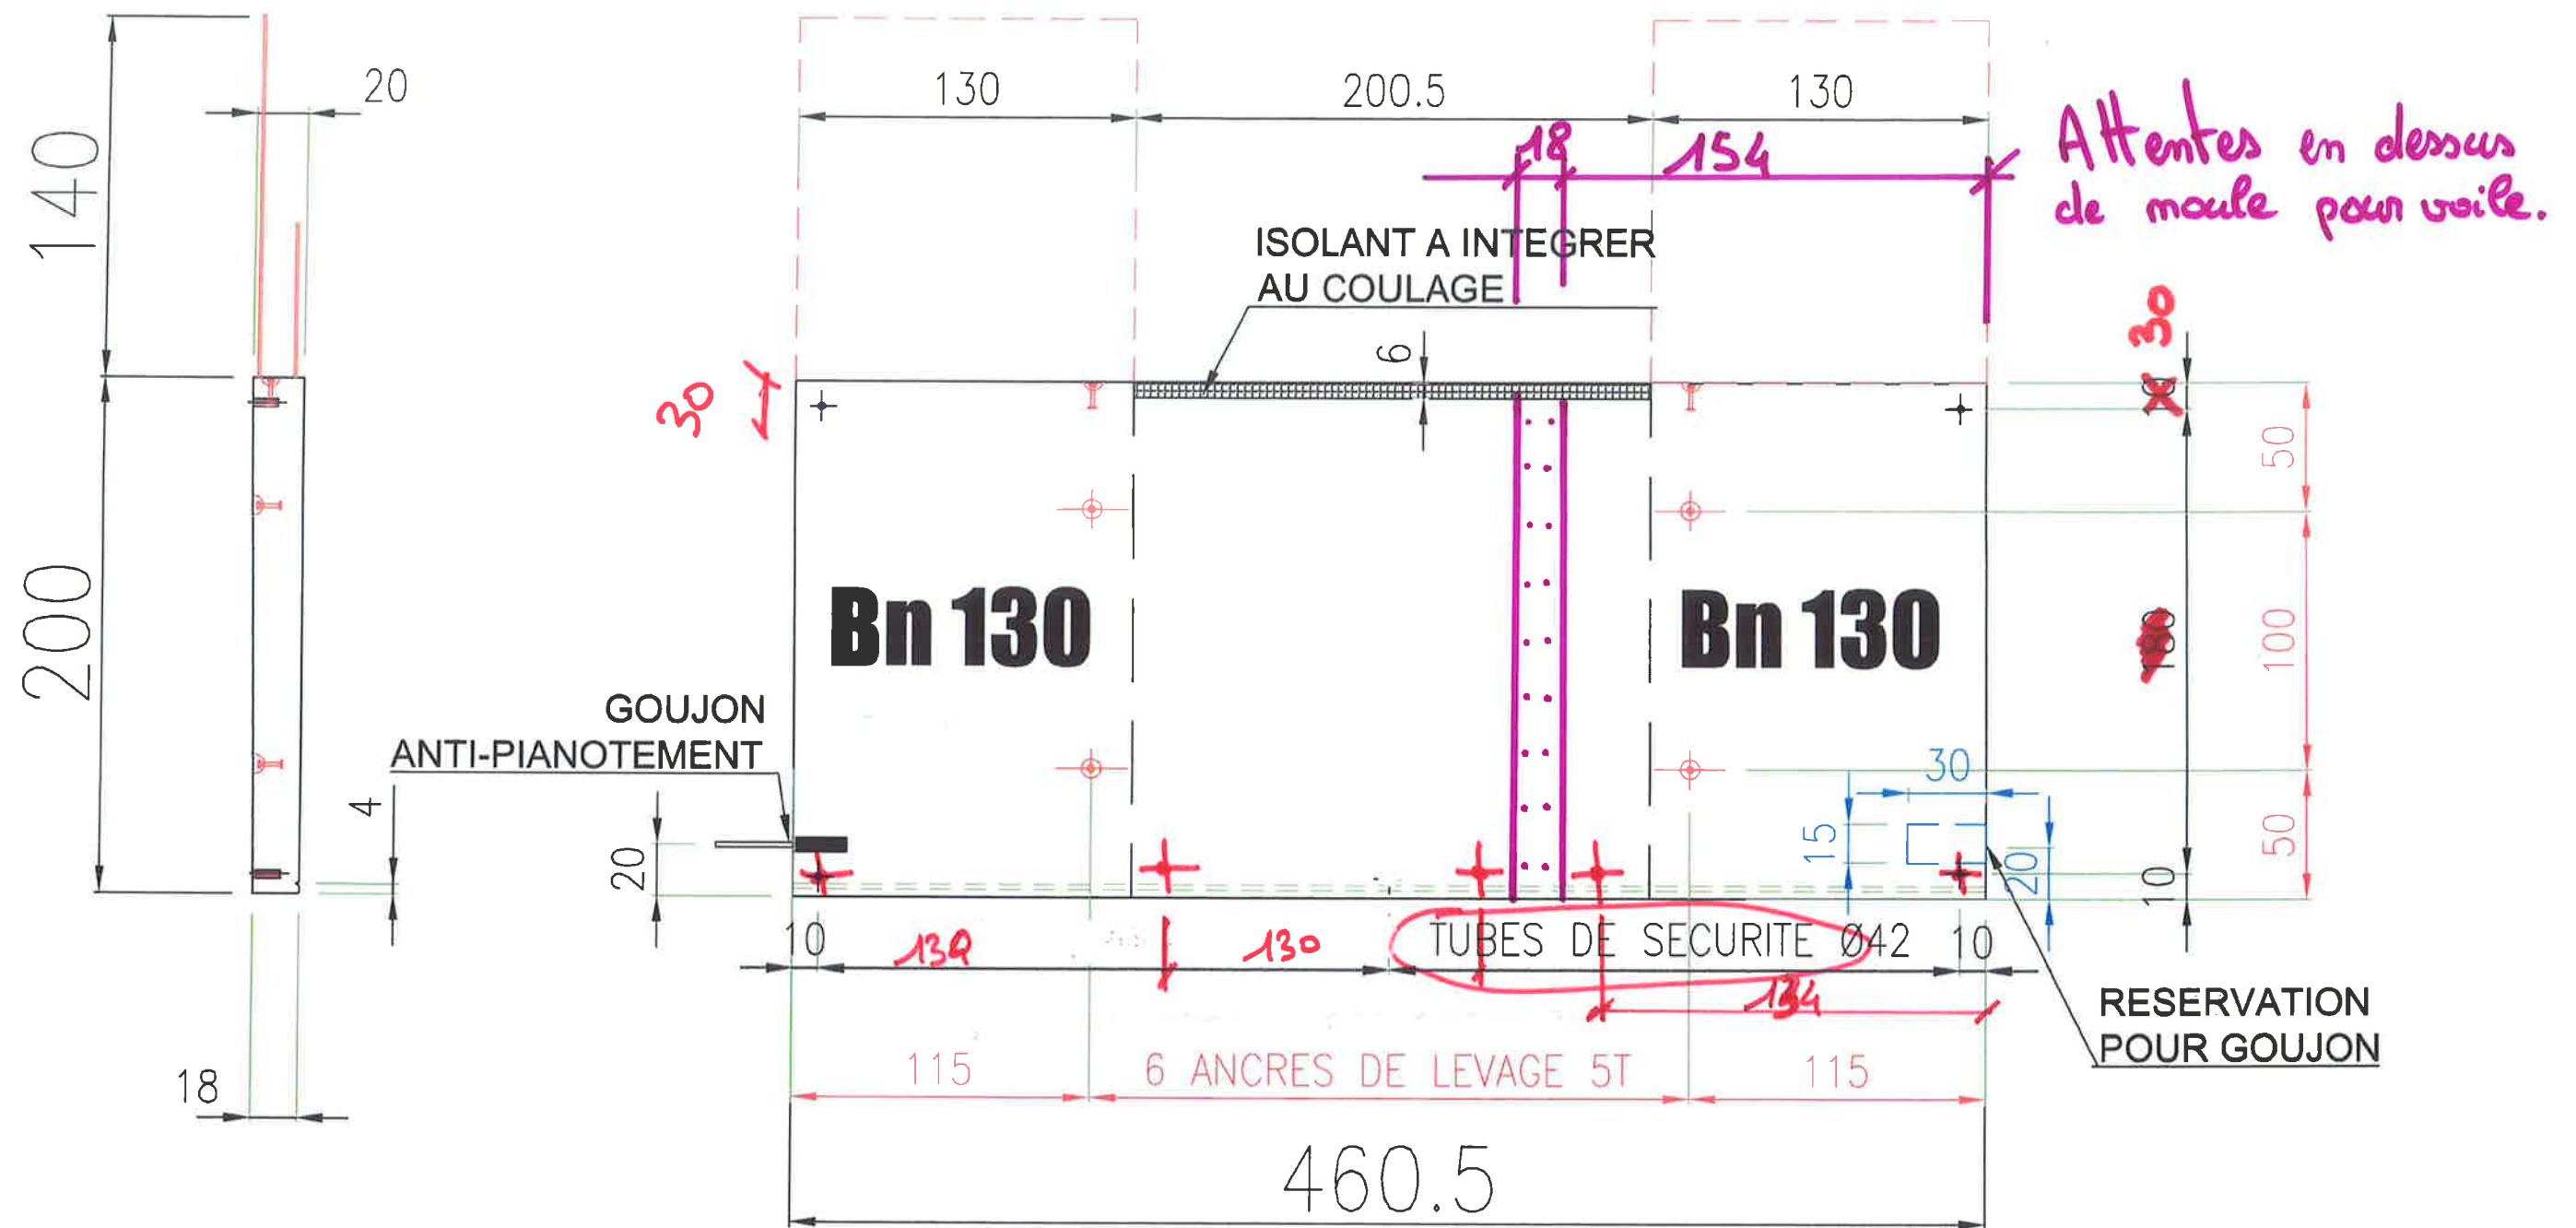



LEVAGE		Douille Ø	INSERTS		Ancre Frimeda T	INSERTS		EBA	INSERTS		TP - JV	DATE: 16/11/2015									
		Douille Ø			Renfort Ø			Douille étalement			PVC Ø80	Plan N°					Page N°				
		Renfort Ø dx			Trifer			Ankrobox Ø50			Tube garde-corps	Indice									

MOULE		N	NC	observations	CONTROLE		N	NC	observations	BETON		N	NC	observations	FICHE AUTO-CONTROLE						
Conformité moule					Dimensions					Conformité béton					Opérateur :						
Etat du moule					Armature					Mise en place					Responsable prod :						
Propreté et huilage					Inserts					Aspect de surface					Date :						
Ent. FONTANEL				Elément: BALCONS				 PLAN DE FABRICATION				Surface:		9.21 m²	POIDS		REPERE		Nbr		
												Volume:		1.70 m3		4.10 T		B5b		1	
LA MULATIERE				coffrage / ferrailage																	

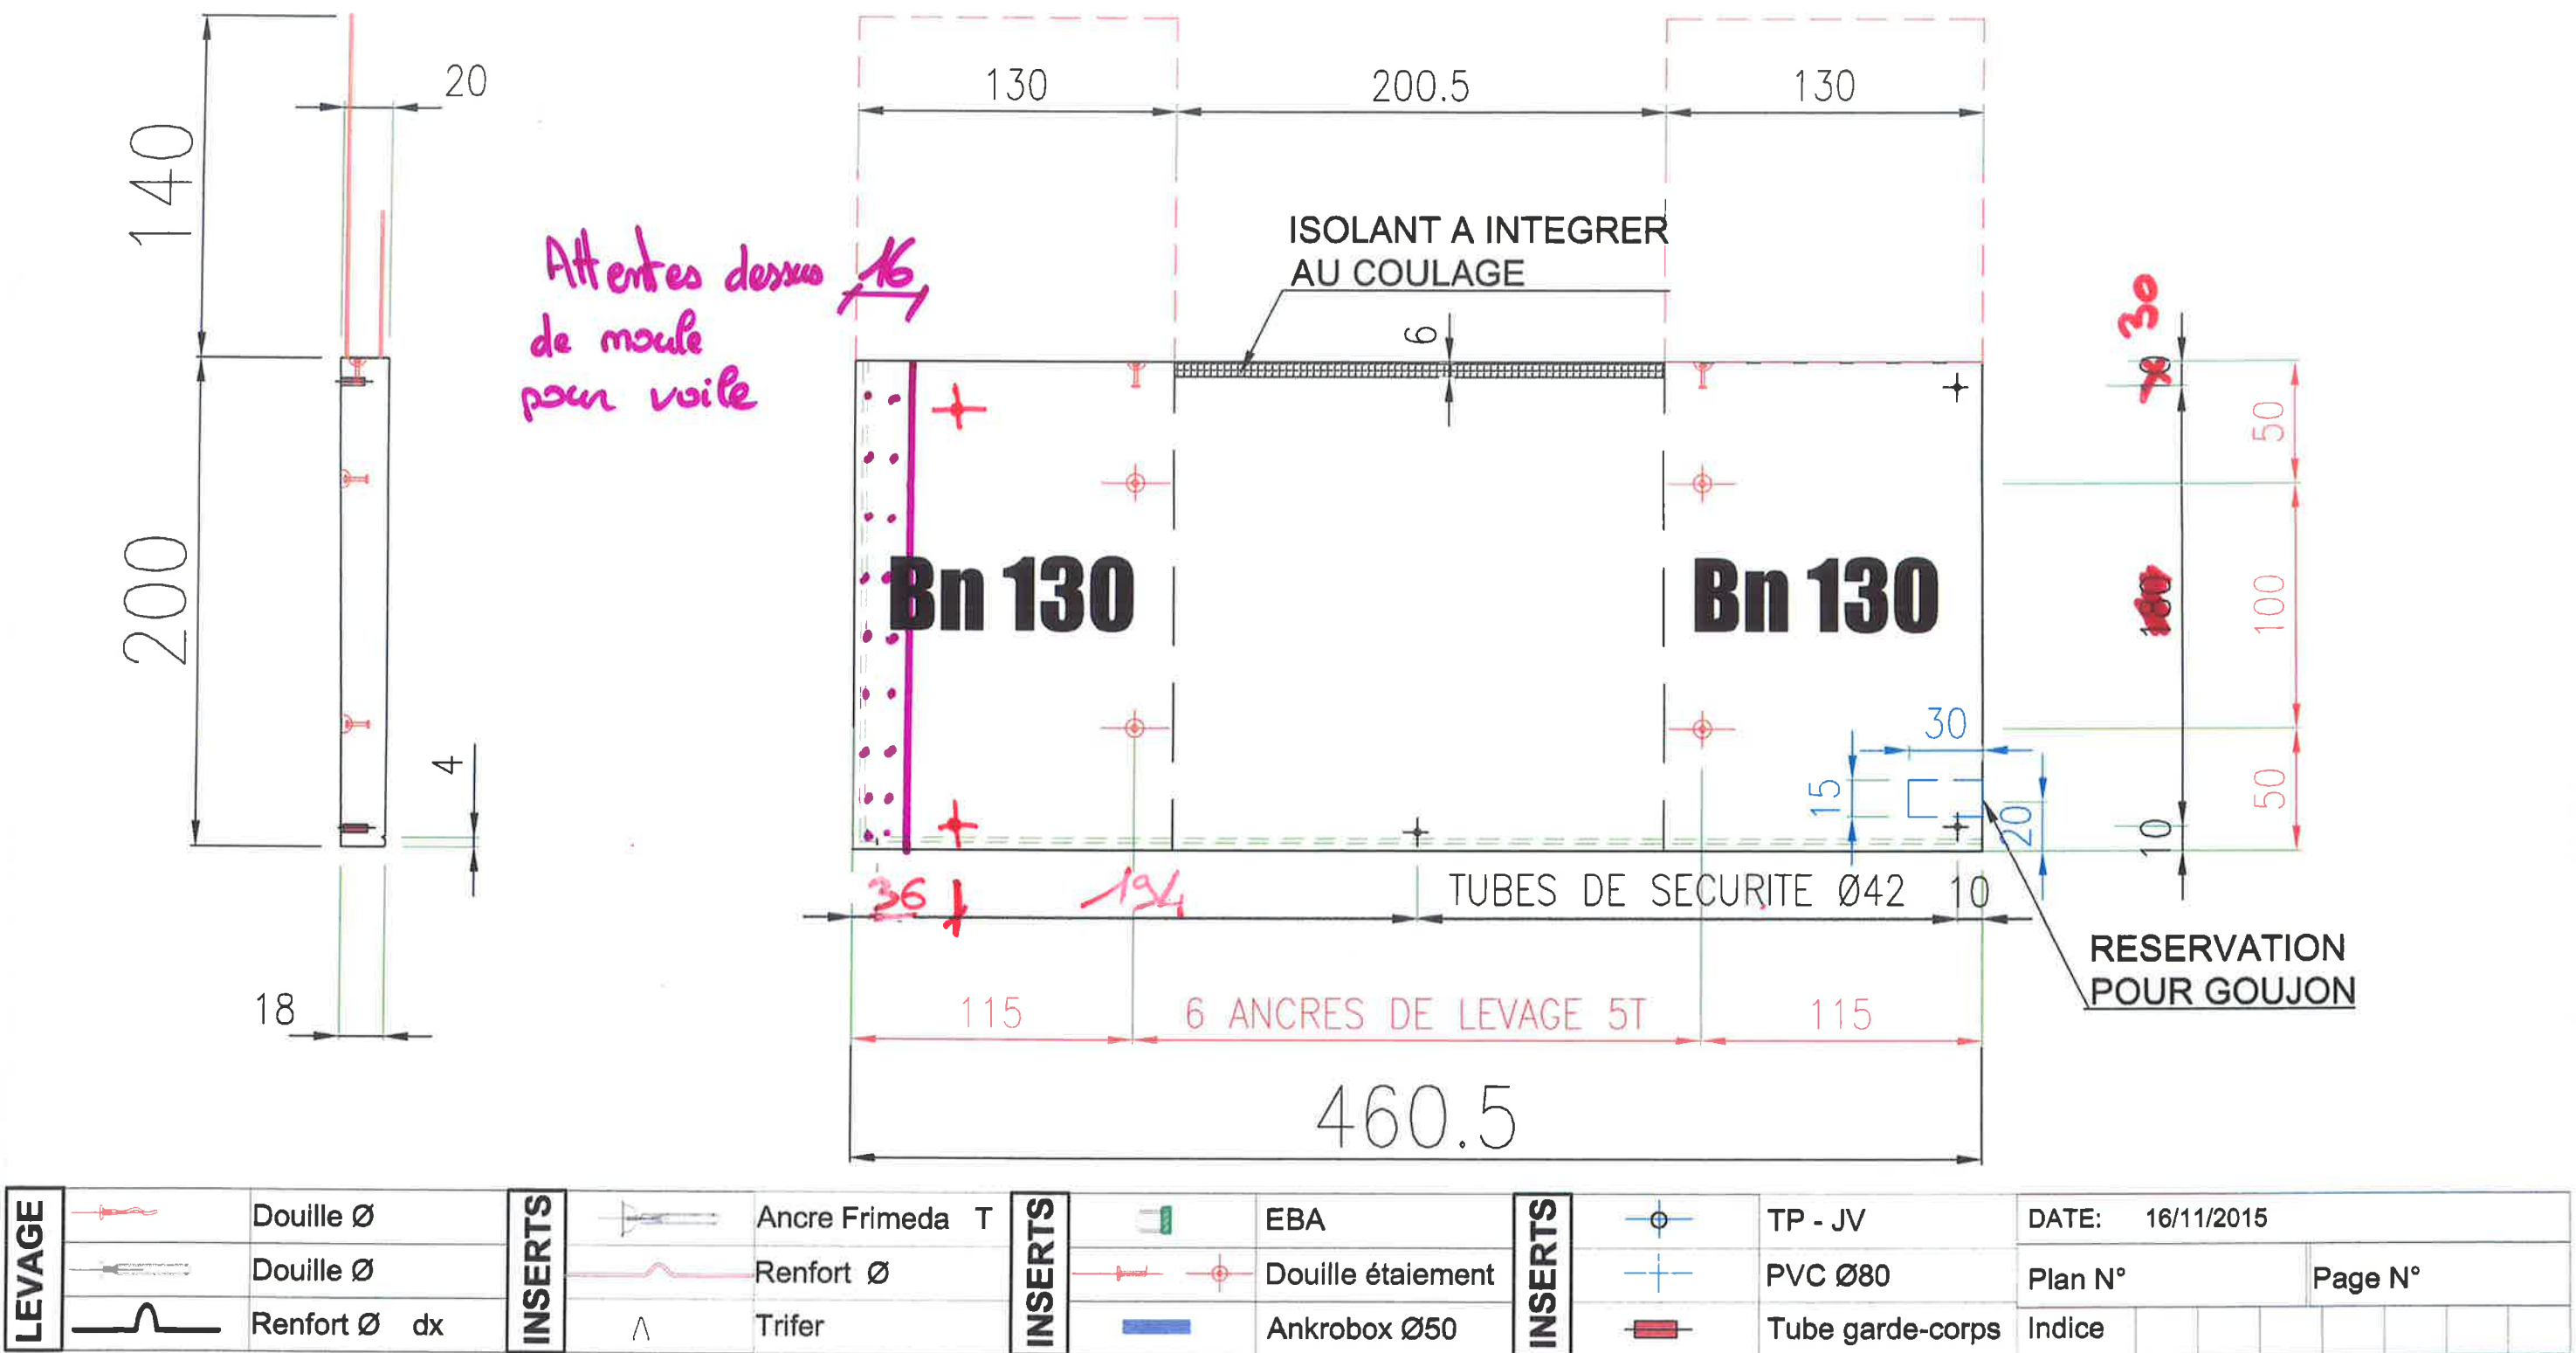


FERRAILLAGE BN POUR BALCONS ISOLES

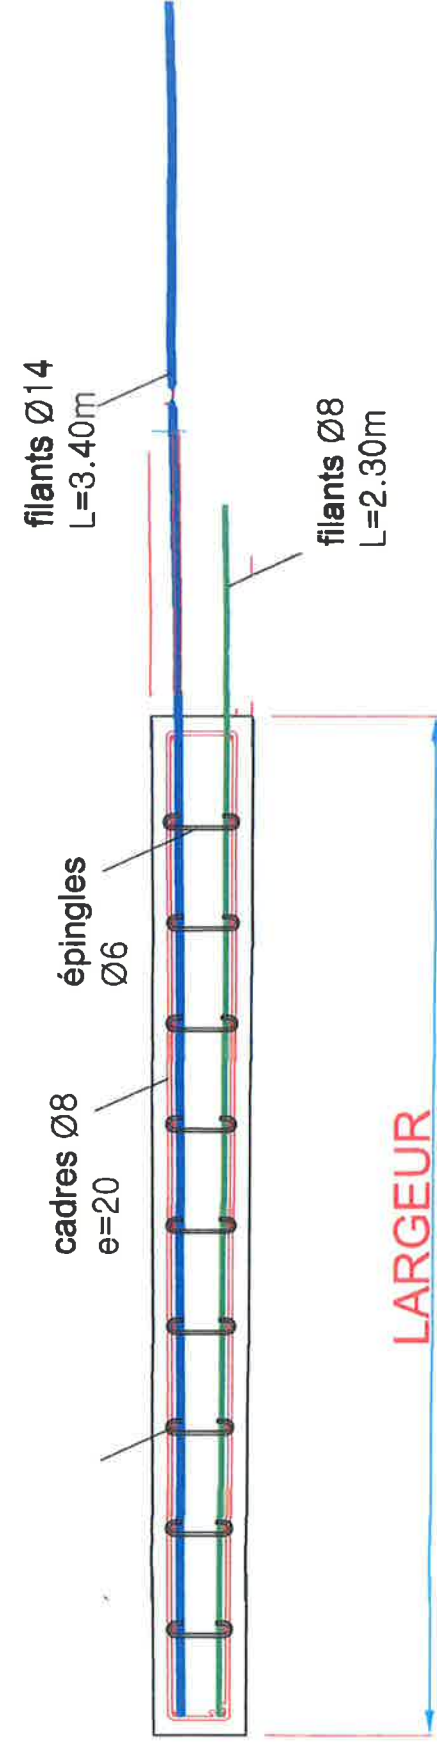


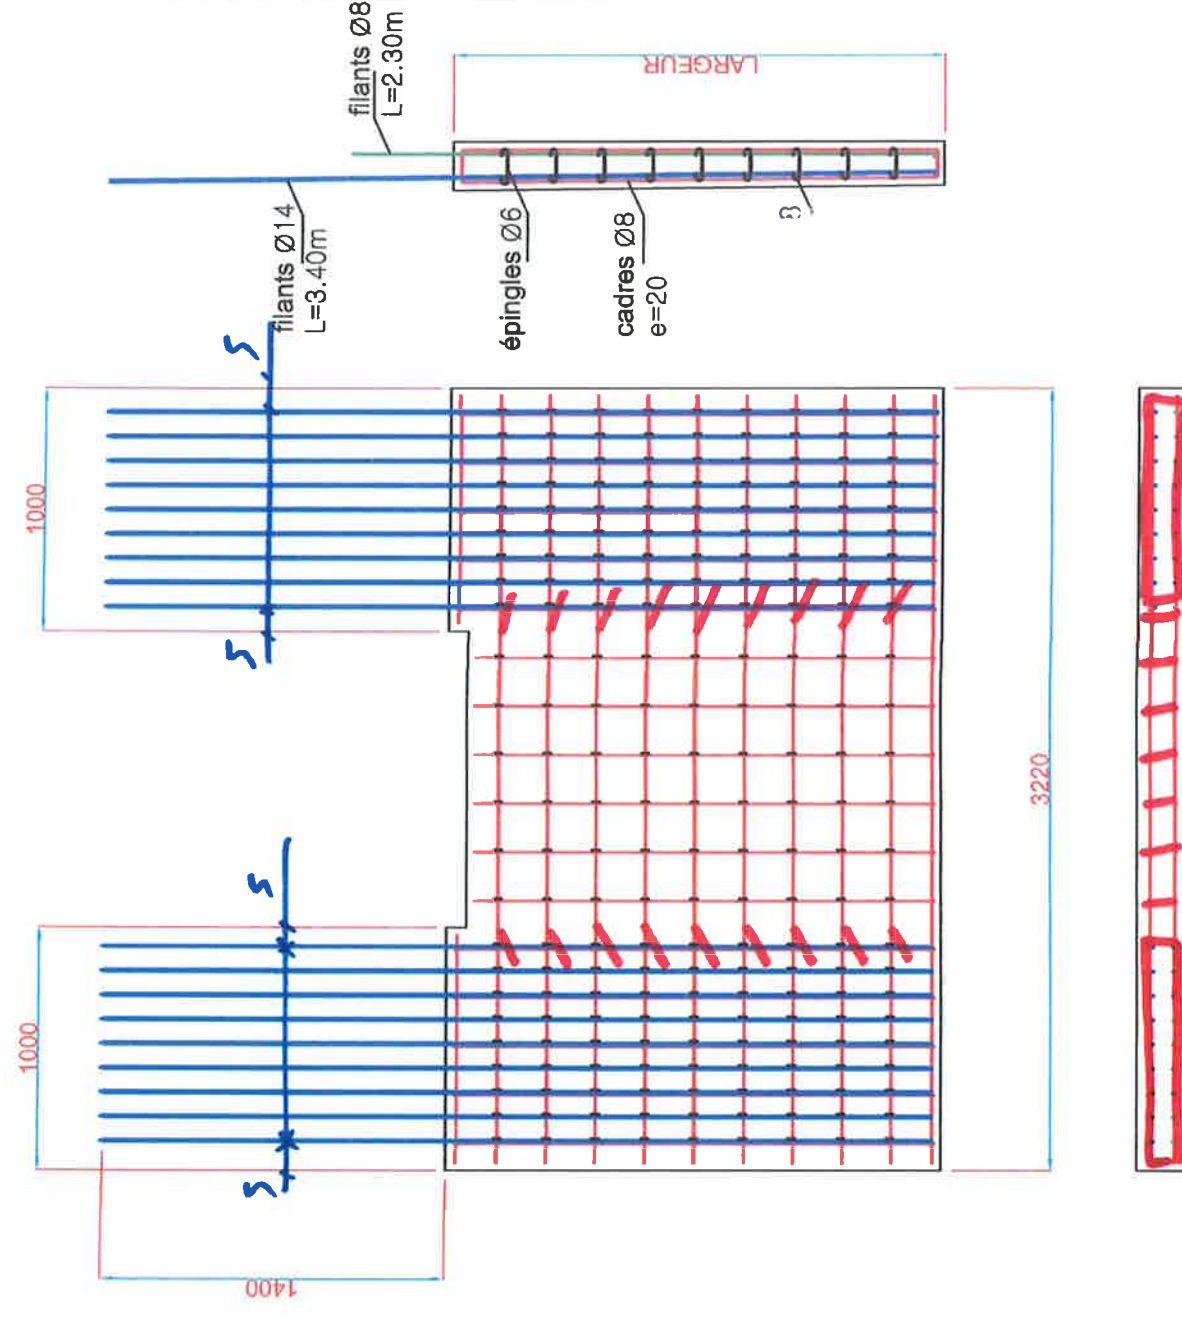

BALCON PORTEUR
AVEC BN Larg.1.30 m

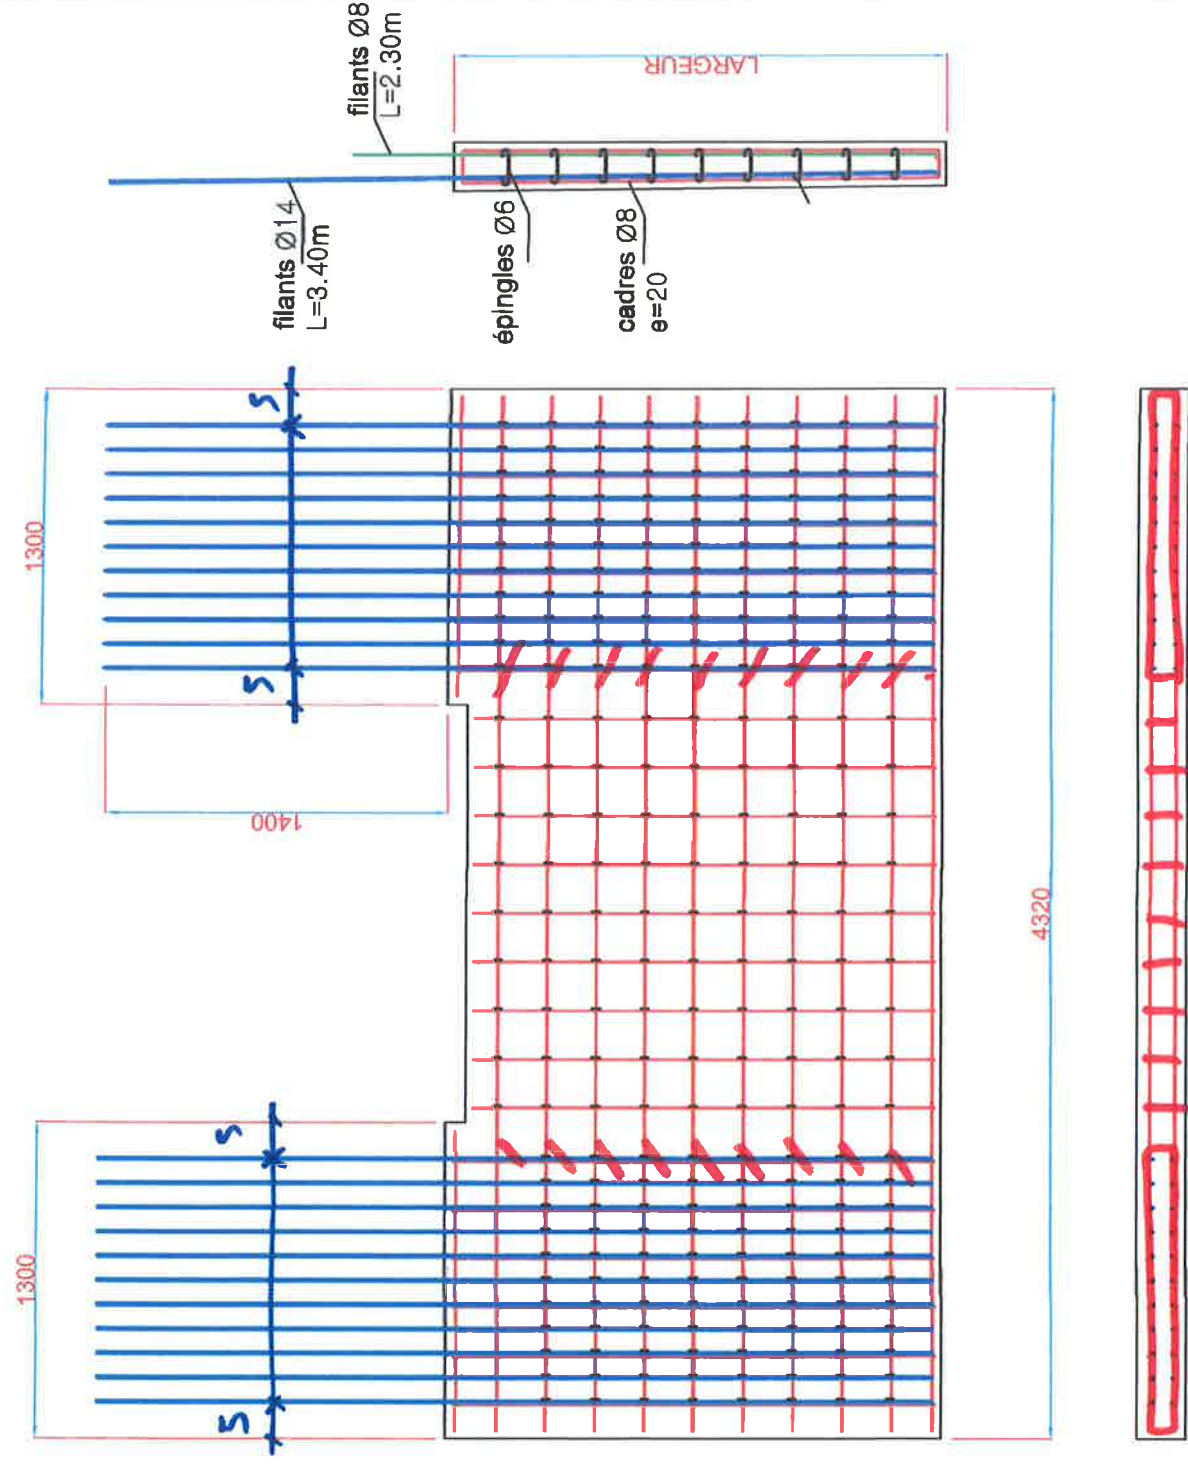

BALCON PORTEUR AVEC BN Larg.1.50 m

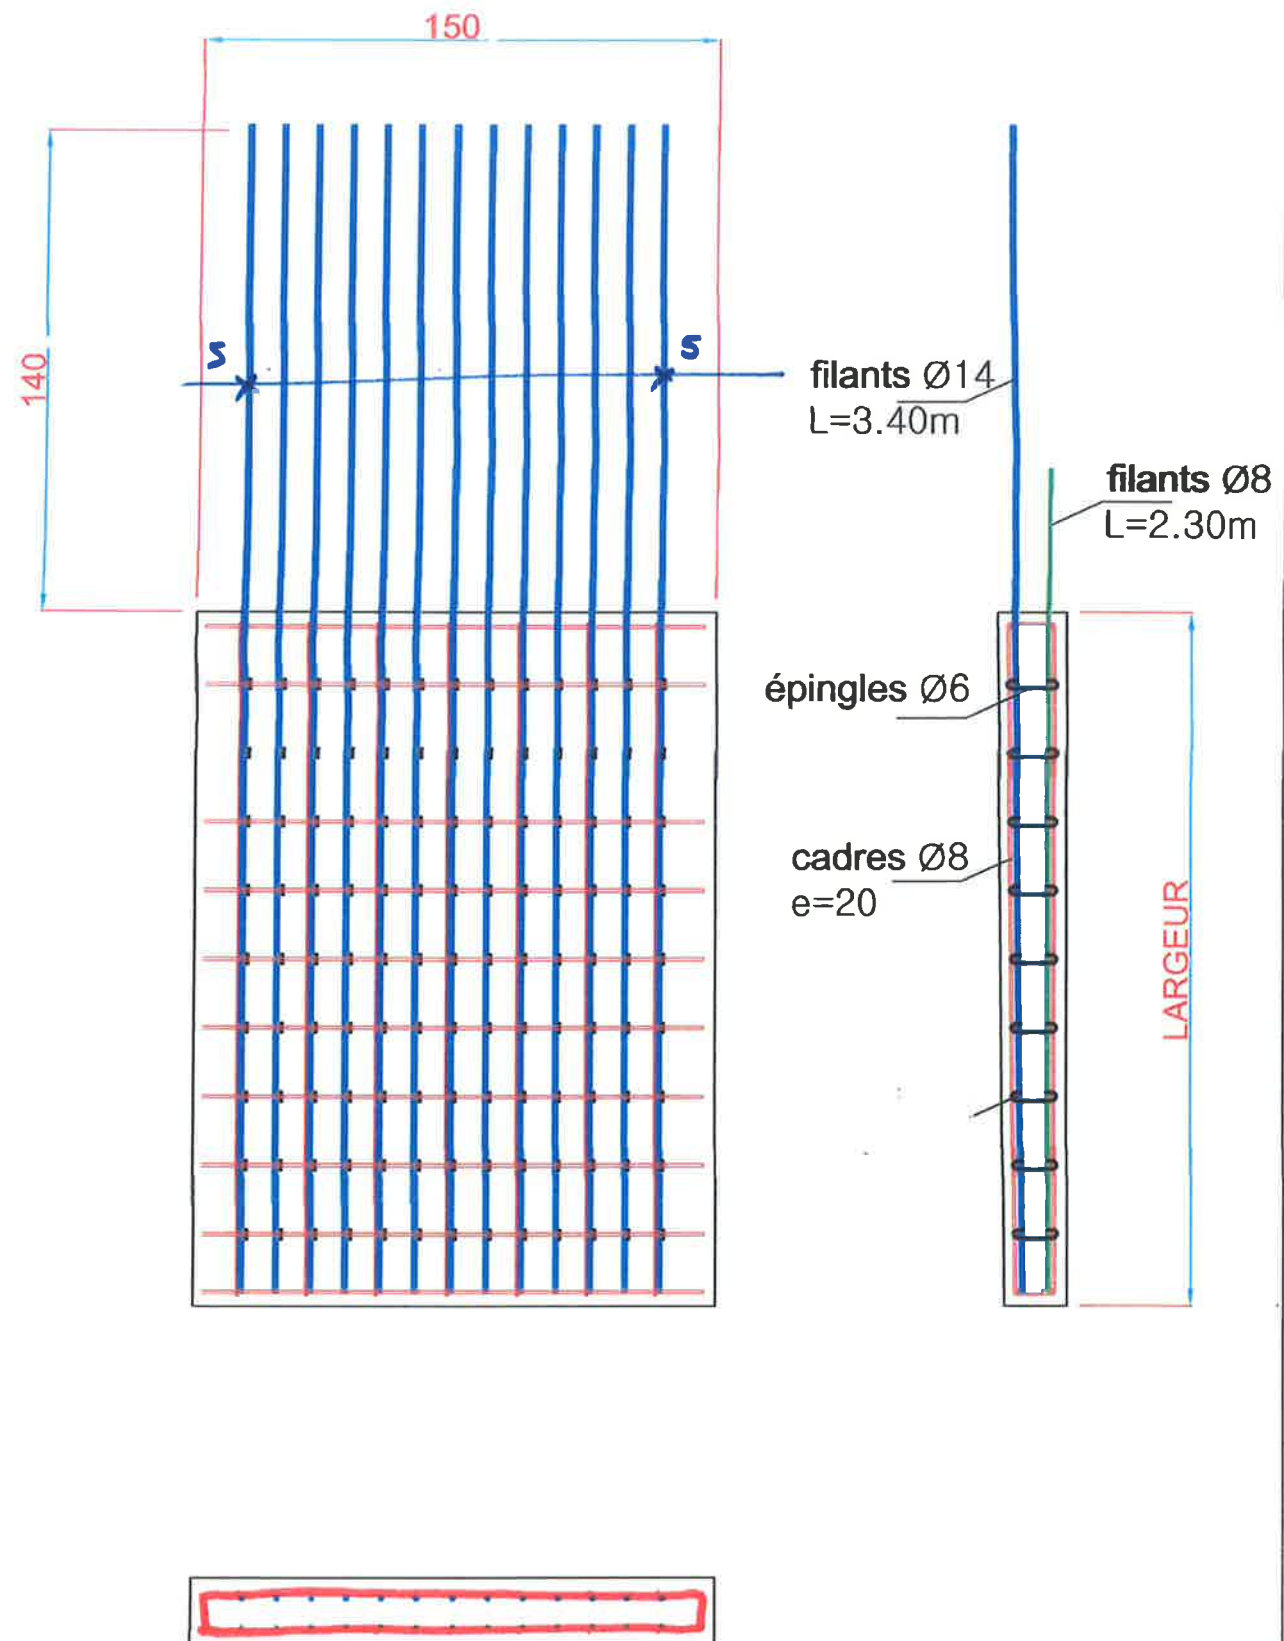

BALCON PORTEUR AVEC BN Larg. 2.00 m

