



±0.00 = 220.50

NOAHO
LE 180°
Chemin de Fontanière - 69350 La Mulatière
Création de logements

PLAN D'EXECUTION

Les entreprises réalisant les travaux devront tenir compte des derniers plans architecte lors de la réalisation des travaux
Les plans du be MATTE ne doivent servir qu'au corps d'état concerné et doivent être des plans d'exécution.

ARCHITECTE(S): ATELIER DE LA PASSERELLE
BET STRUCTURE: MATTE SAS
BET FLUIDES: PRELEM
ECONOMISTE: EXECO
BUREAU DE CONTROLE: Bureau VERITAS
MO DELEGUE: MOE: PSO Ingénierie
CSPTS: SUD EST COORDINATION
OPC: ENTREPRISE(S): Fontanel

Bât:A
PLANCHER SUR -1
Coffrage

MURS ARRONDIS. DALLES

INDICE	DATE	MODIFICATIONS
	15 février - Yes	

EXE

Contrainte de sol: 8 bars ELS

Aciers HA (T) FeE500
Aciers Doux (Ø) FeE 235
Aciers TS FeE 500
Béton fc28 >= 25MPa
Enrobage = 3 cm

PLAN N°
A35 0


DATE : 26/01/2016


Affaire N°
13.12.118

MATTÉ
BUREAU D'ÉTUDES
STRUCTURES ET FLUIDES

119 BOULEVARD STALINGRAD 69100 VILLEURBANNE
Tél. 04 72 44 02 87 Fax 04 72 44 26 59
E-mail : bet@matte.fr

Dessiné par : J.BO
Contrôlé par : P.LIN
Echelle : 1/50°

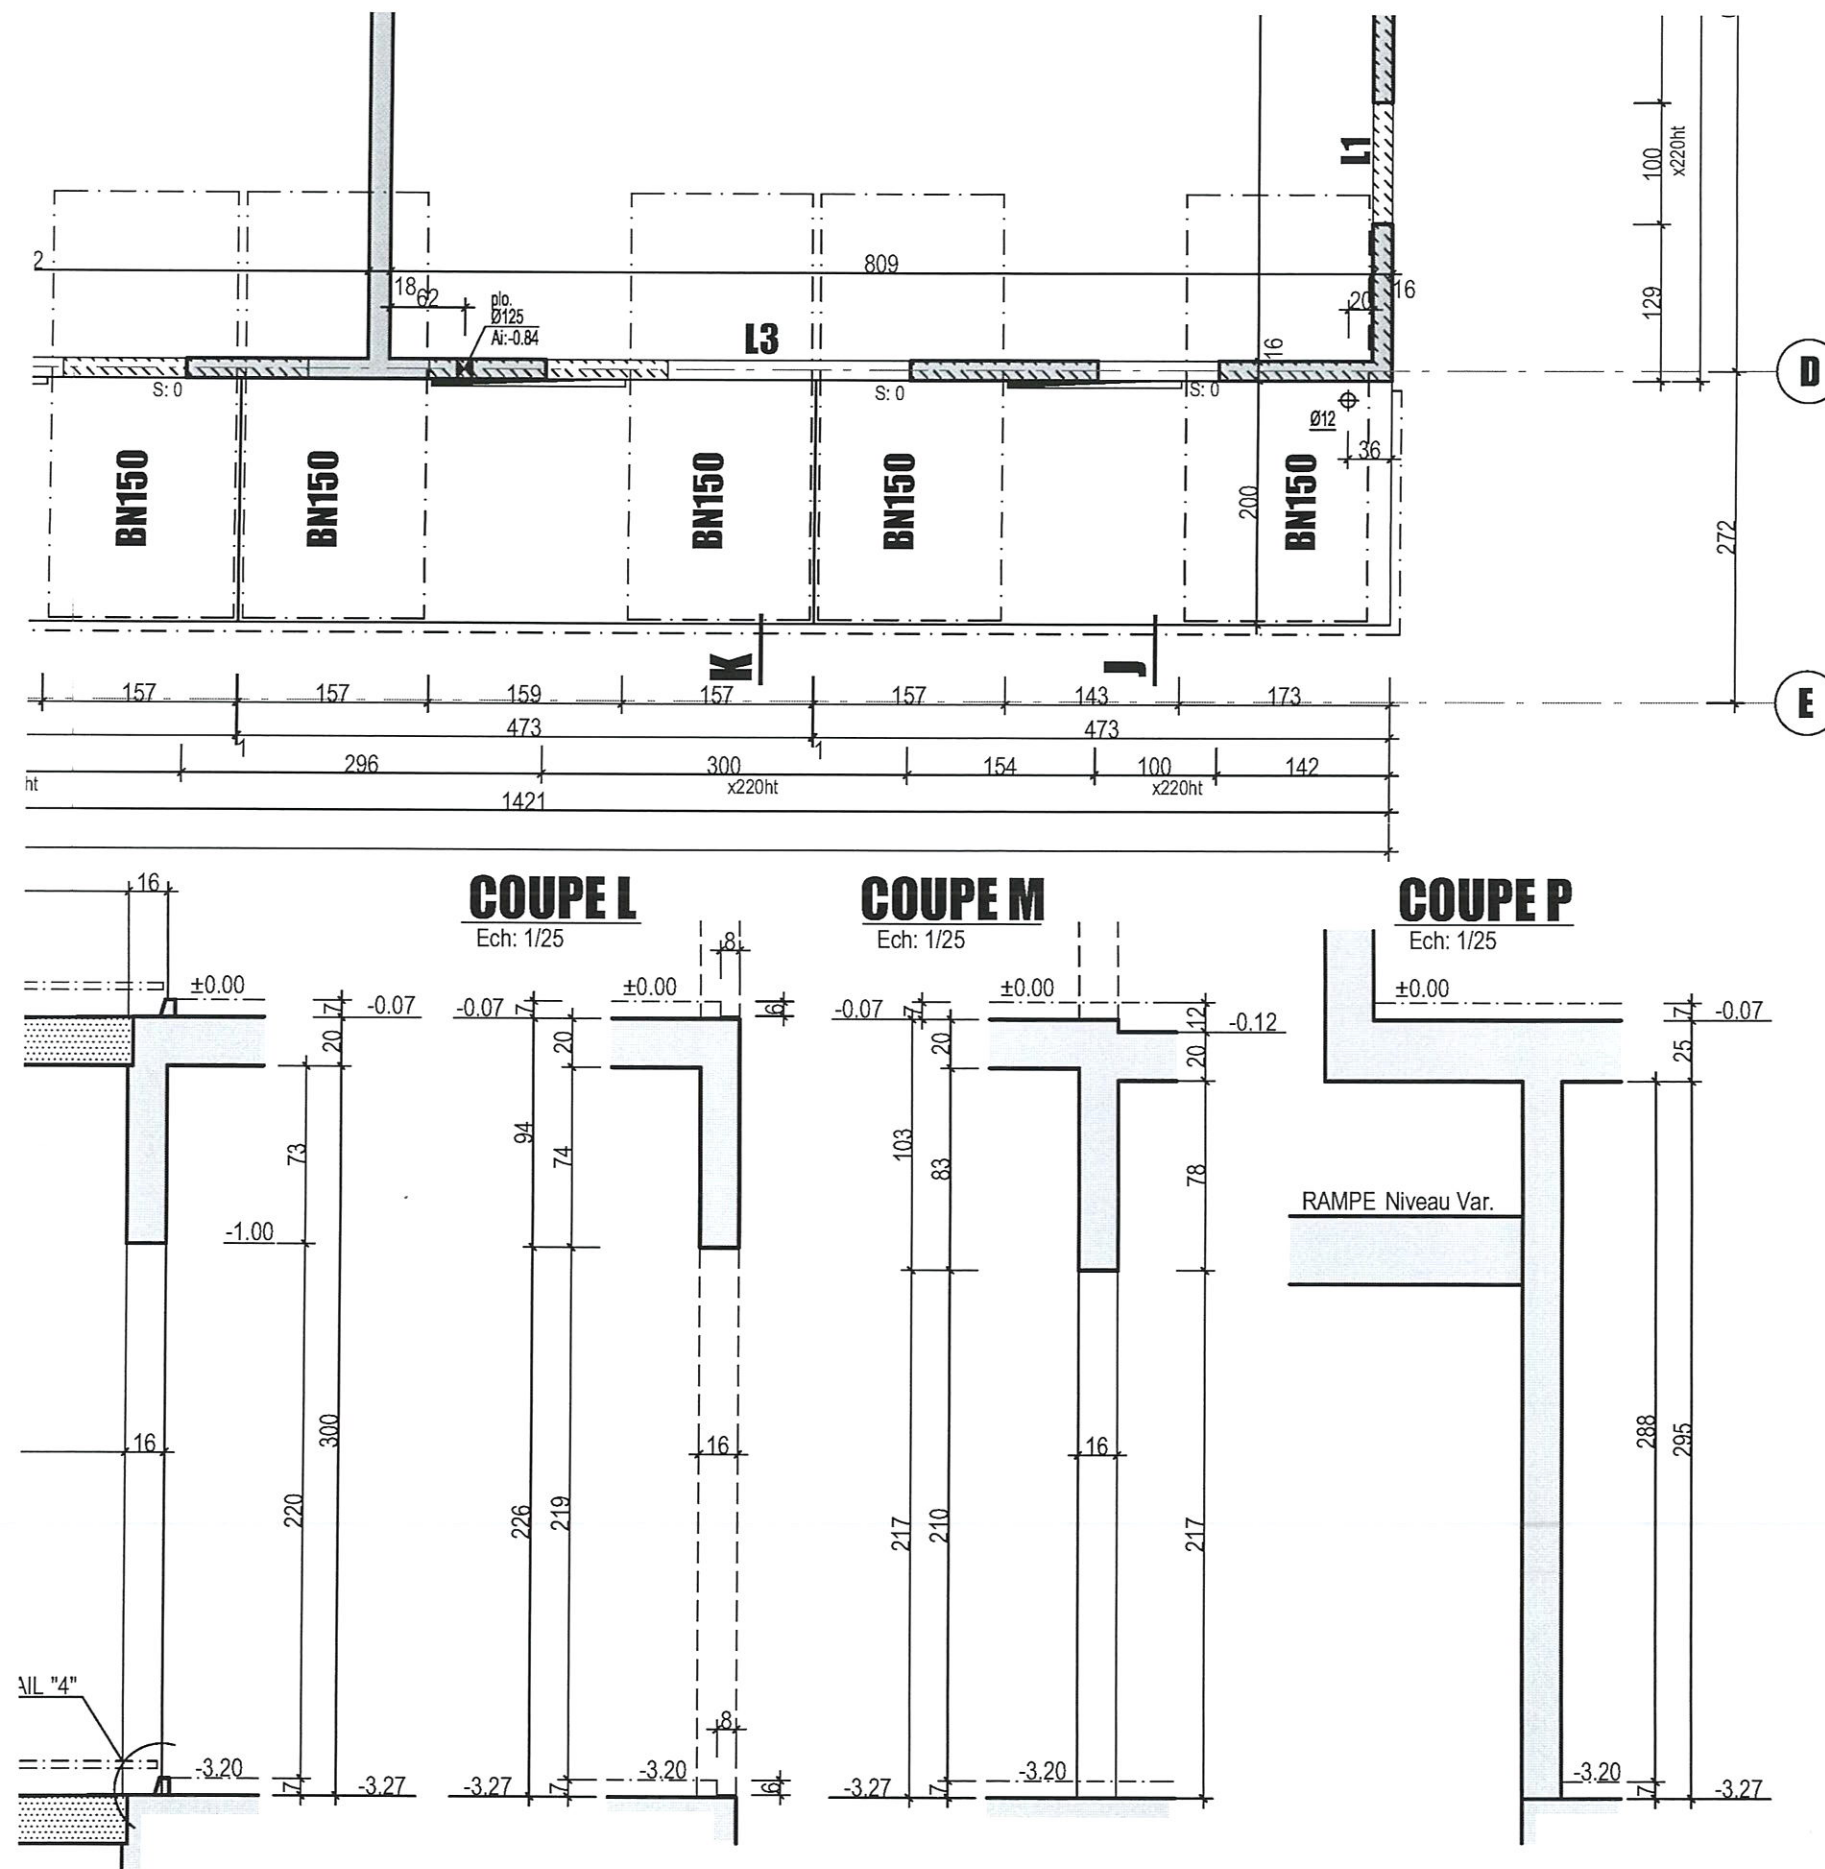

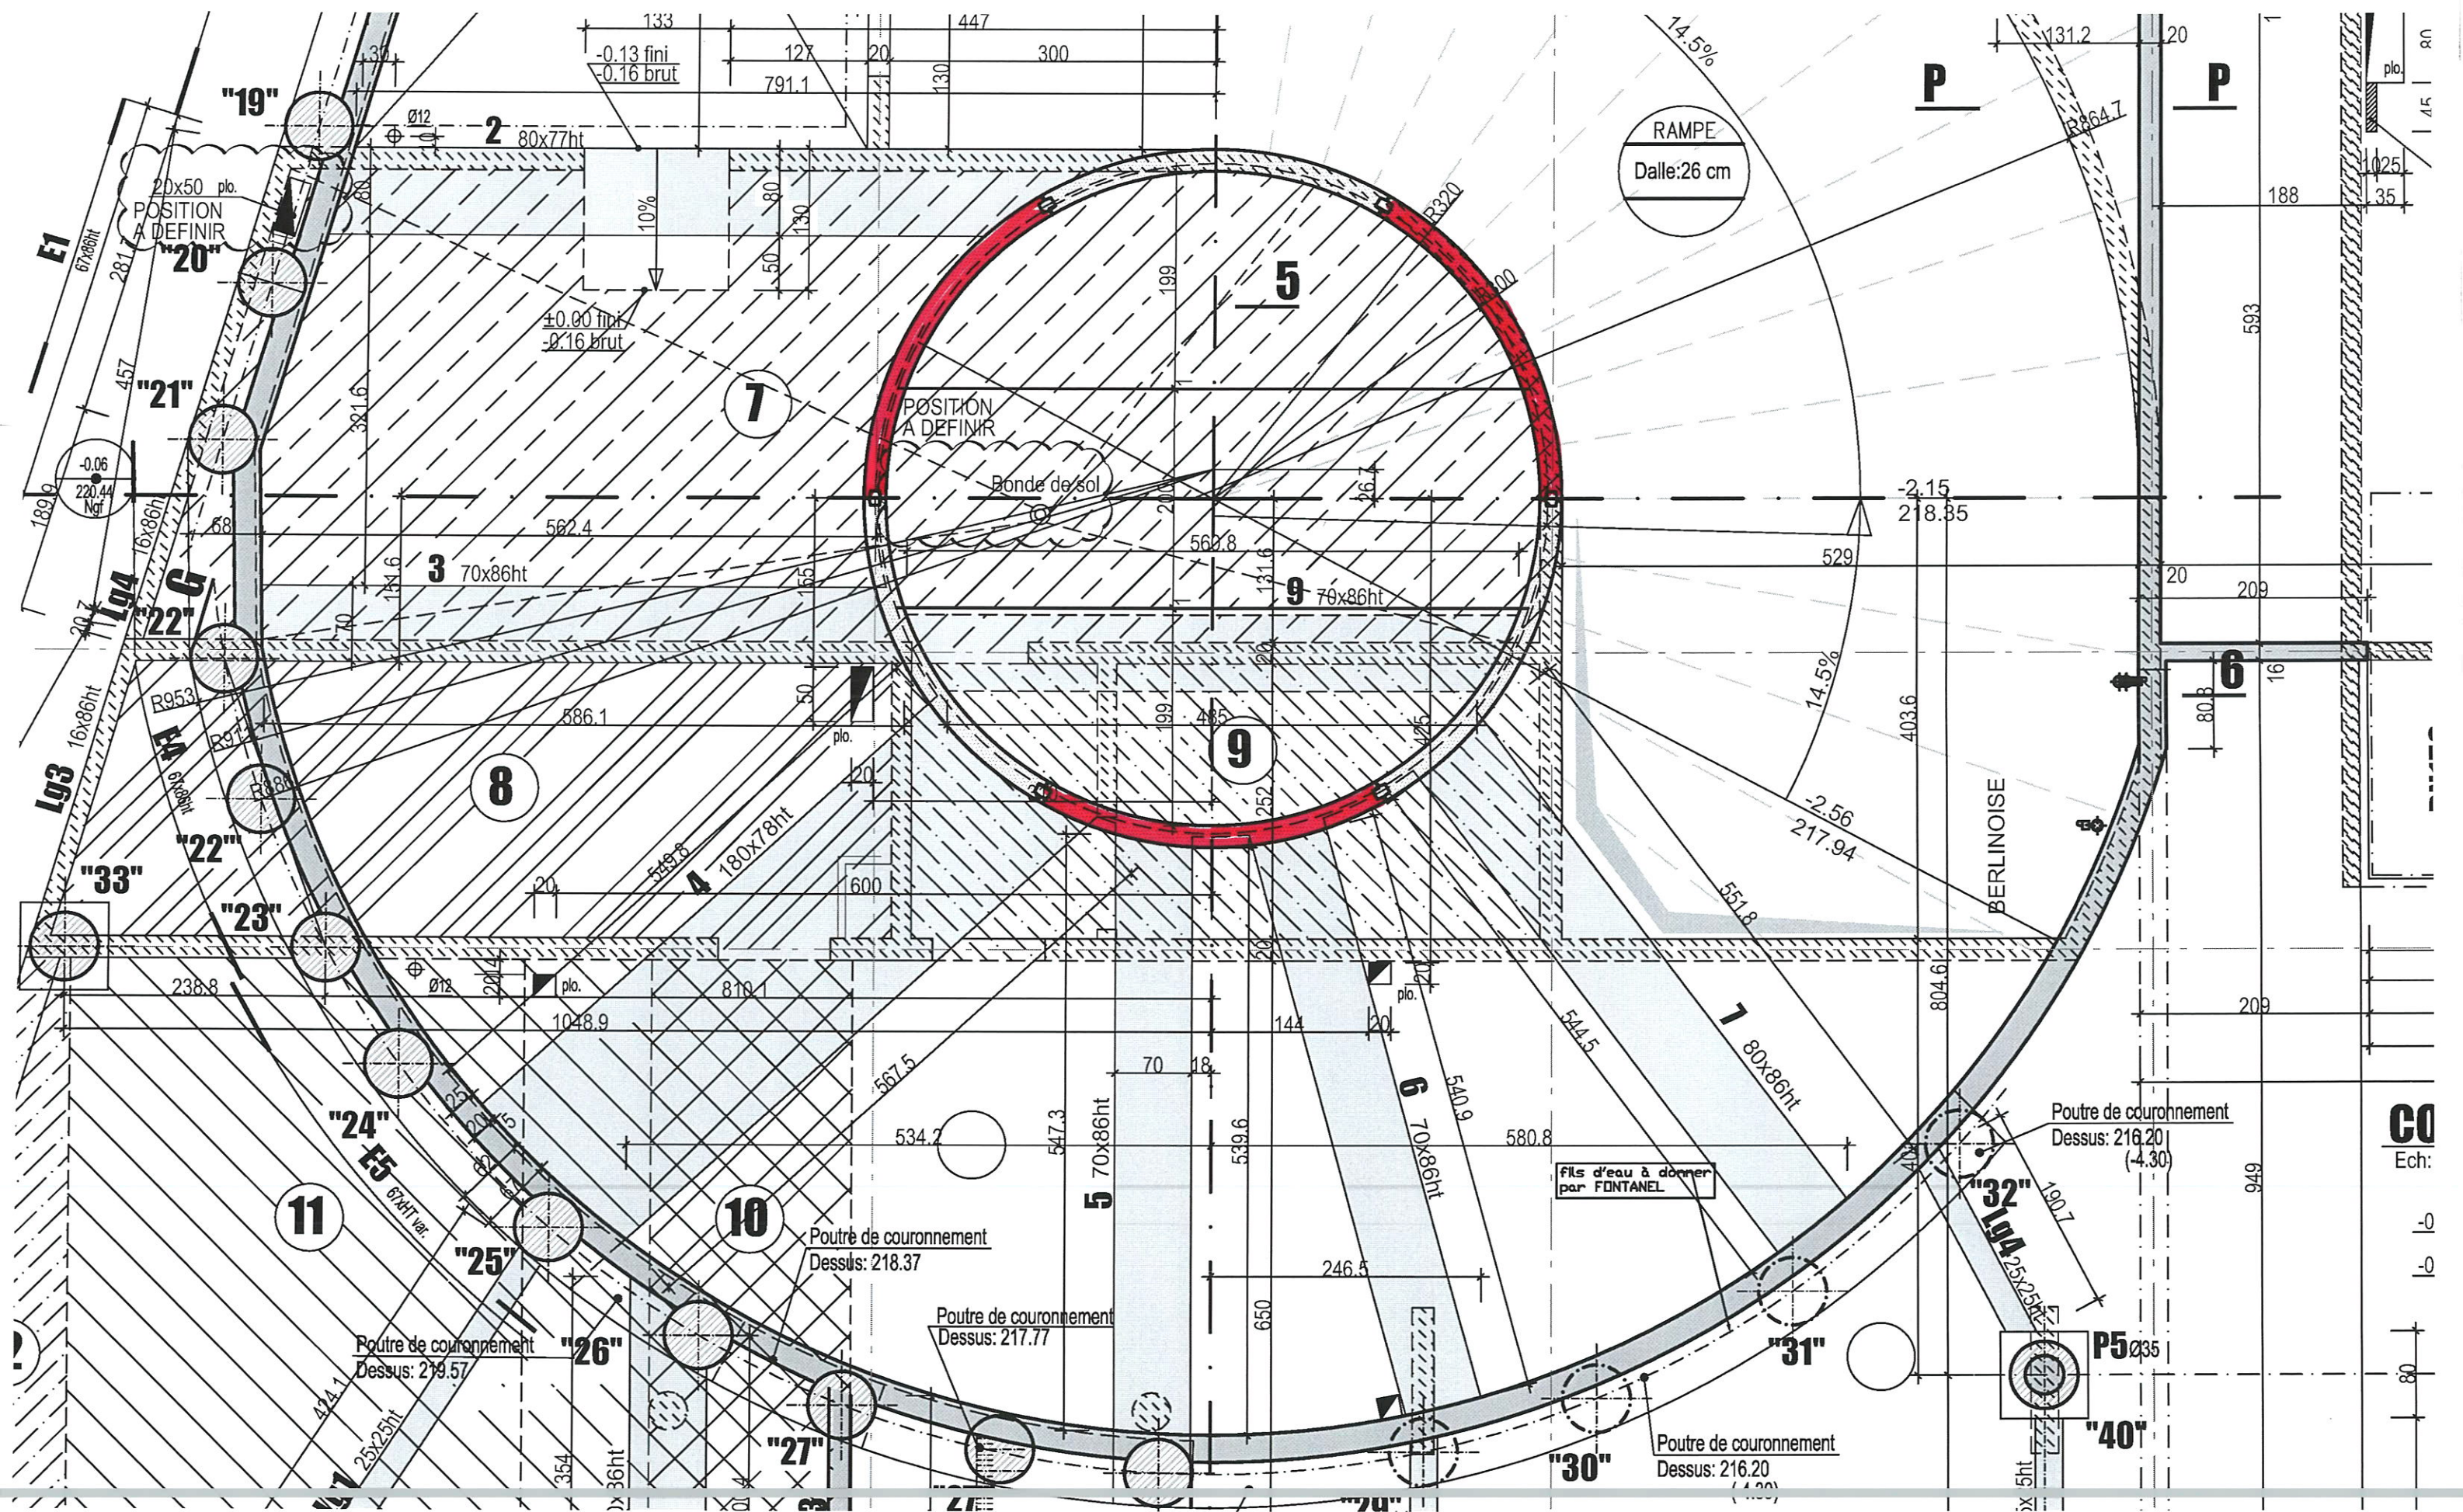

FONTANEL - LE 180°

69 LA MULATIERE

ARRONDIS DU NIVEAU
+ DALLE POSE SANS ETAIES

N

EXE

Indice	Date	Designation des Modifications	Date :
A	4.02	mise à jour pour approbation Fontanel	/ /
B	8.02	mise à jour remarque Fontanel.	
C			Affaire :
D			
E			Echelle :
F			
G			
H			
I			

Type béton = B35 XF1
Aciers H.A et T.S = Fe E 500
Enrobage des armatures = ENR ~~C~~ARMAT
Manutention = Tonnes

le Jeudi 4 Février 2016

BUREAU D'ETUDE
PLATTARD SAS
414 Avenue de la
plage
BP 119
69540
Villefrance-sur-Saône
Tél: 04 74 02 20 20
Fax: 04 74 62 26 62




P L A T T A R D

Valider :
- Paulo
- Sullivan
le 4 Février 2016

Ce plan est la propriété intellectuelle de la PLATTARD SAS, il ne peut être reproduit sans son autorisation.

Mis à jour le 12 Février 2016

LE 180° - LA MULATIERE

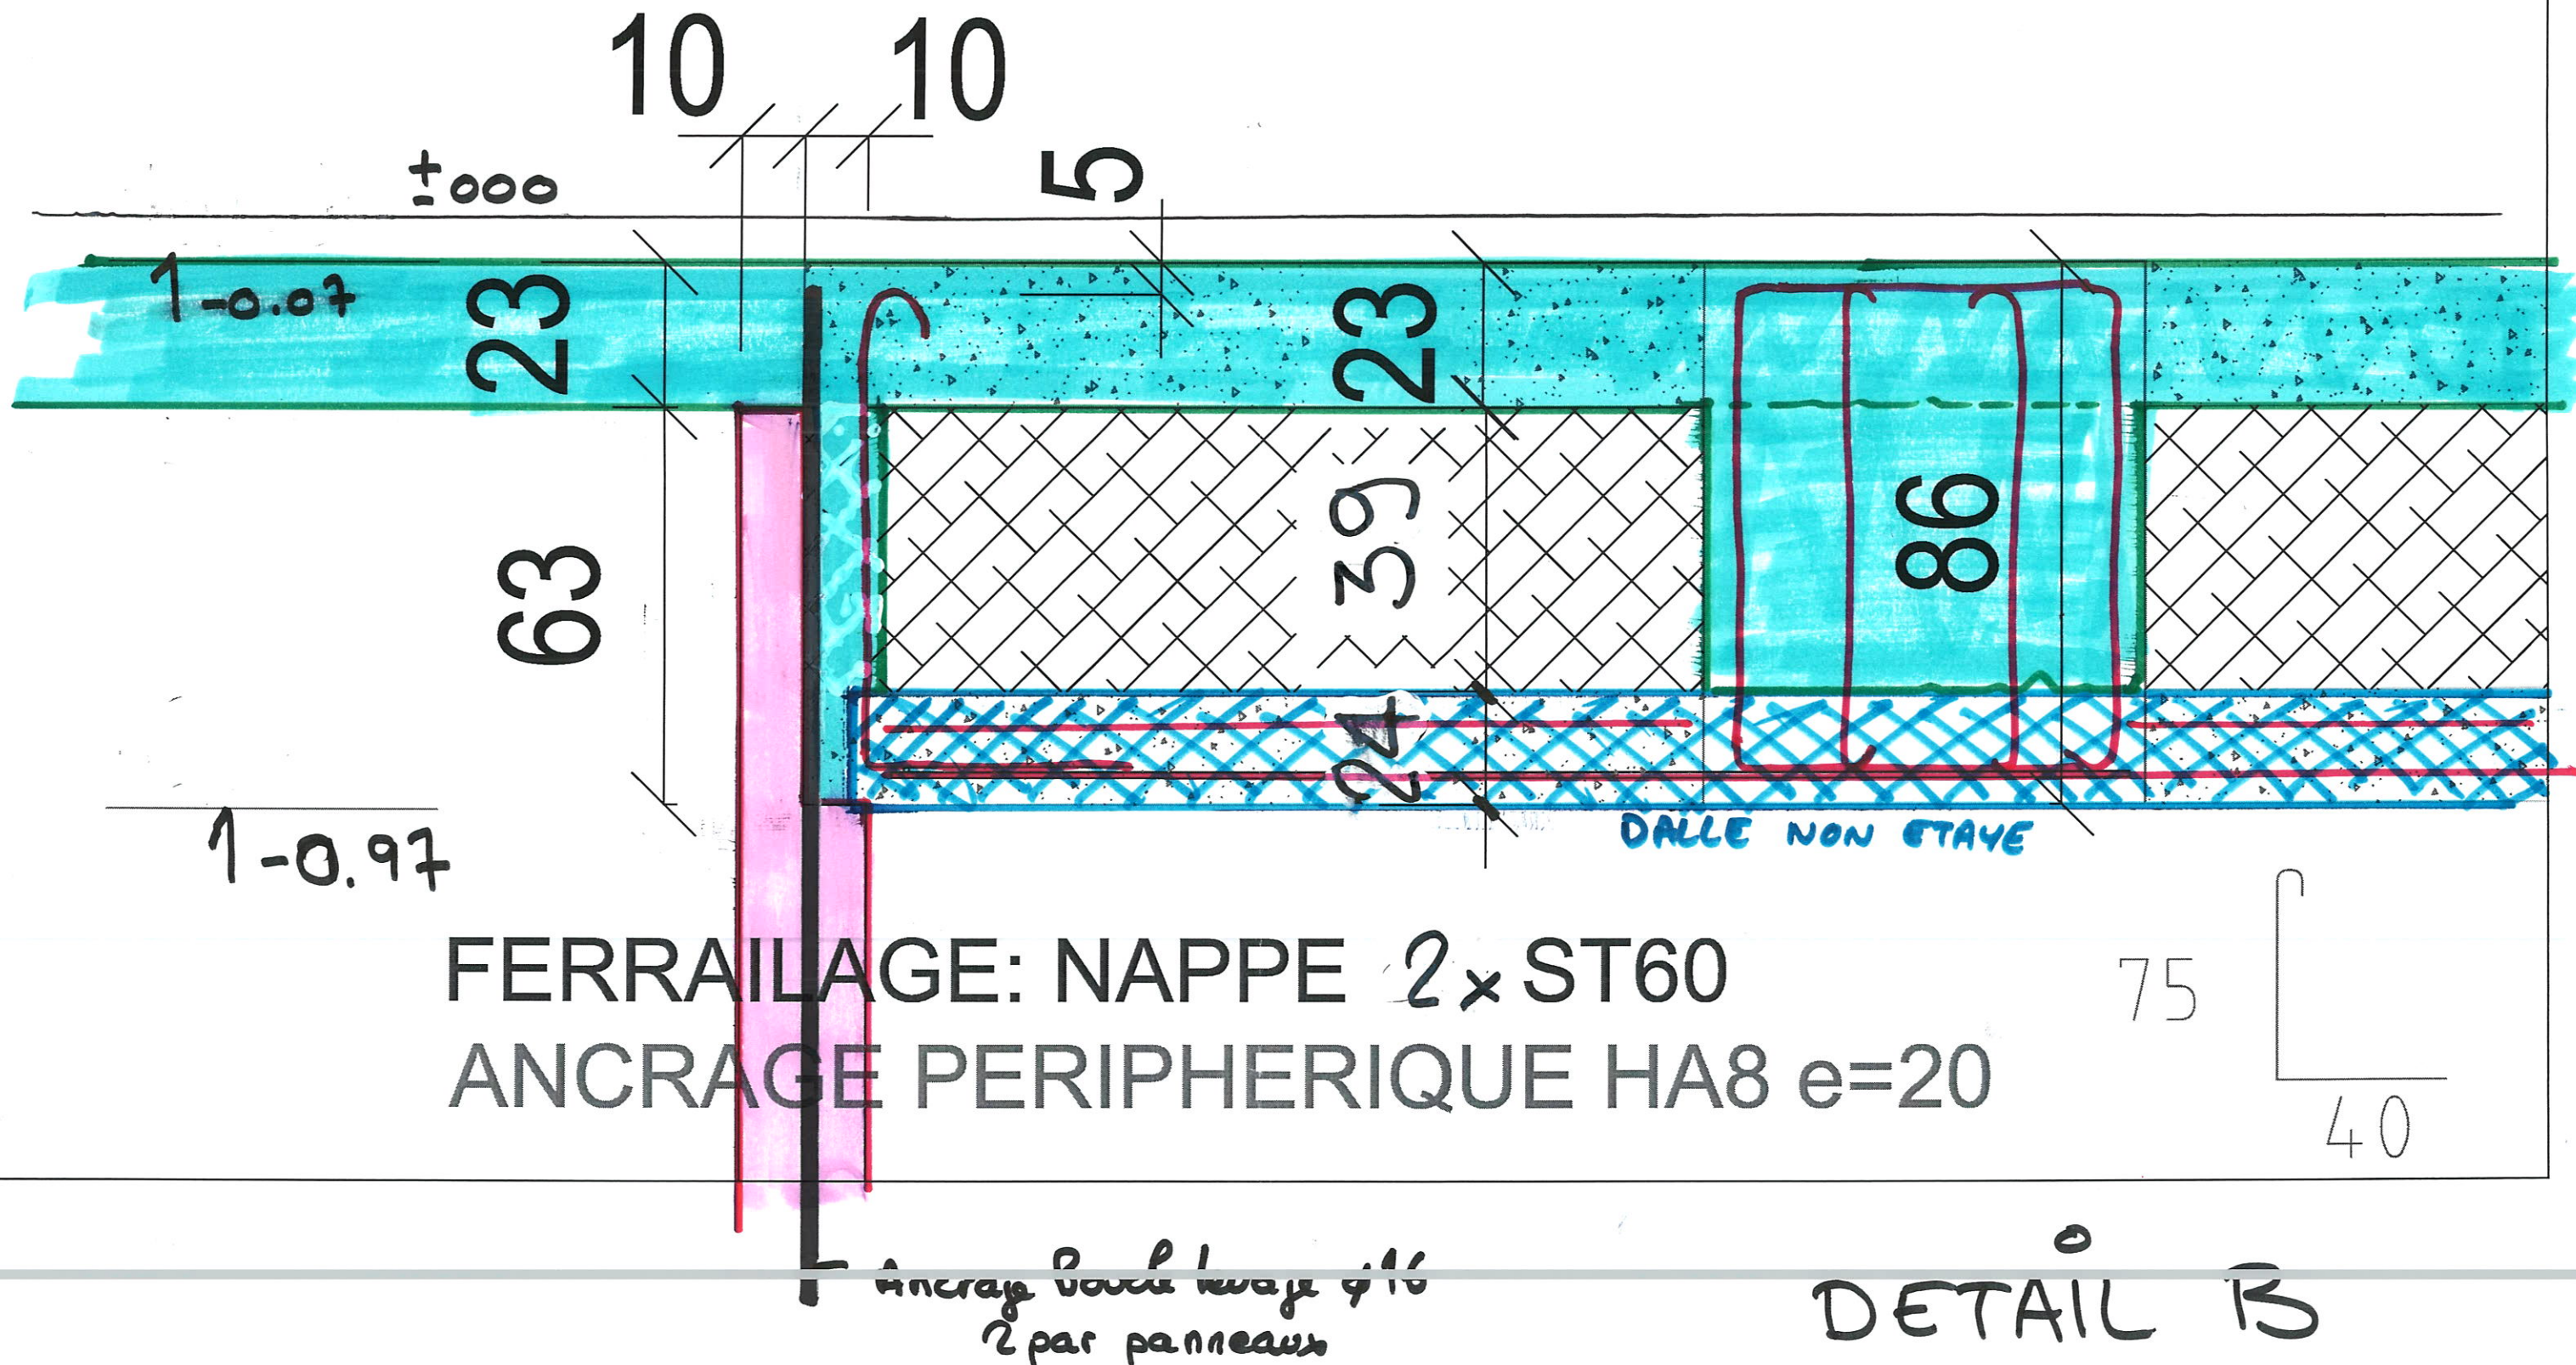

LE 180° - LA MULATIERE
COUPE MUR ARRONDI



1

2

620

310

DETAIL B

DETAIL A

PARTIE A COULER EN PLACE

retombe porte 63

302.6

0.8

302.5

0.8

302.5

0.8

882

NIVEAU

Dalle Pose Sans Etais

910

HAUTEUR
TOTALE

NIVEAU

NIVEAU

93.3


209.2


0.8

302.6


HAUTEUR
PANNEAU

LE 180° - LA MULATIERE
DECOUPAGE
NIVEAU 2

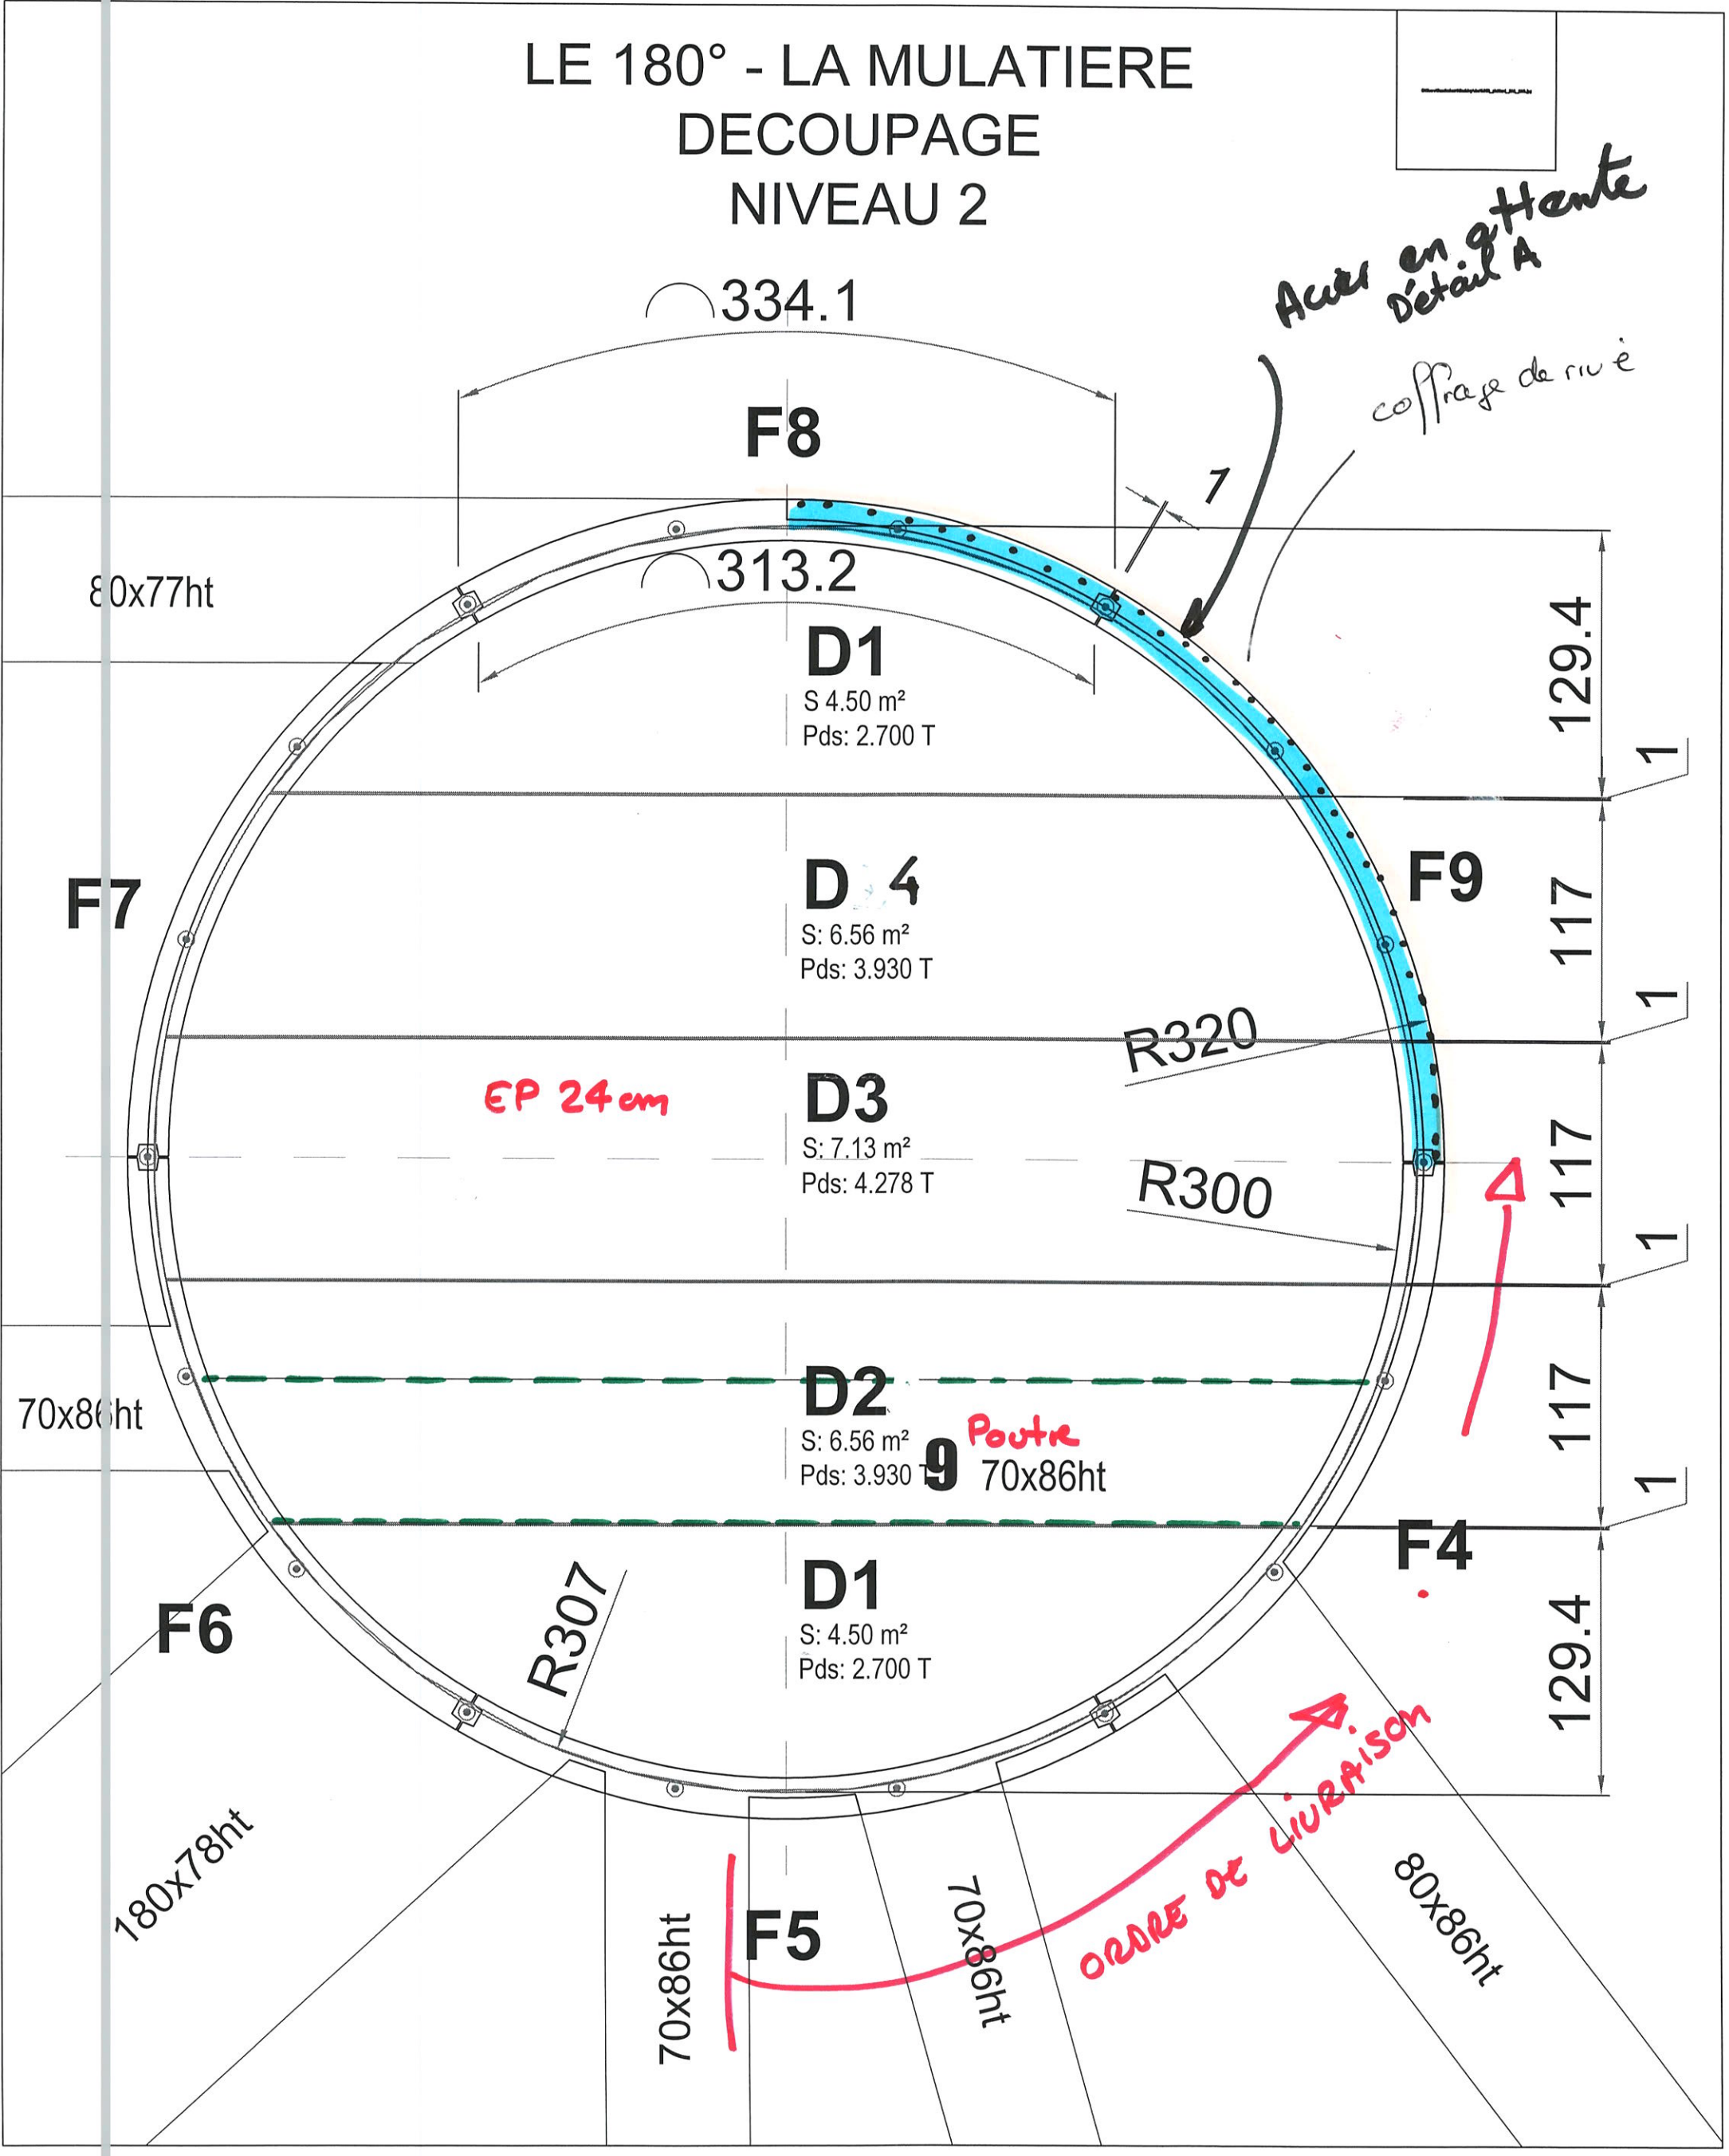


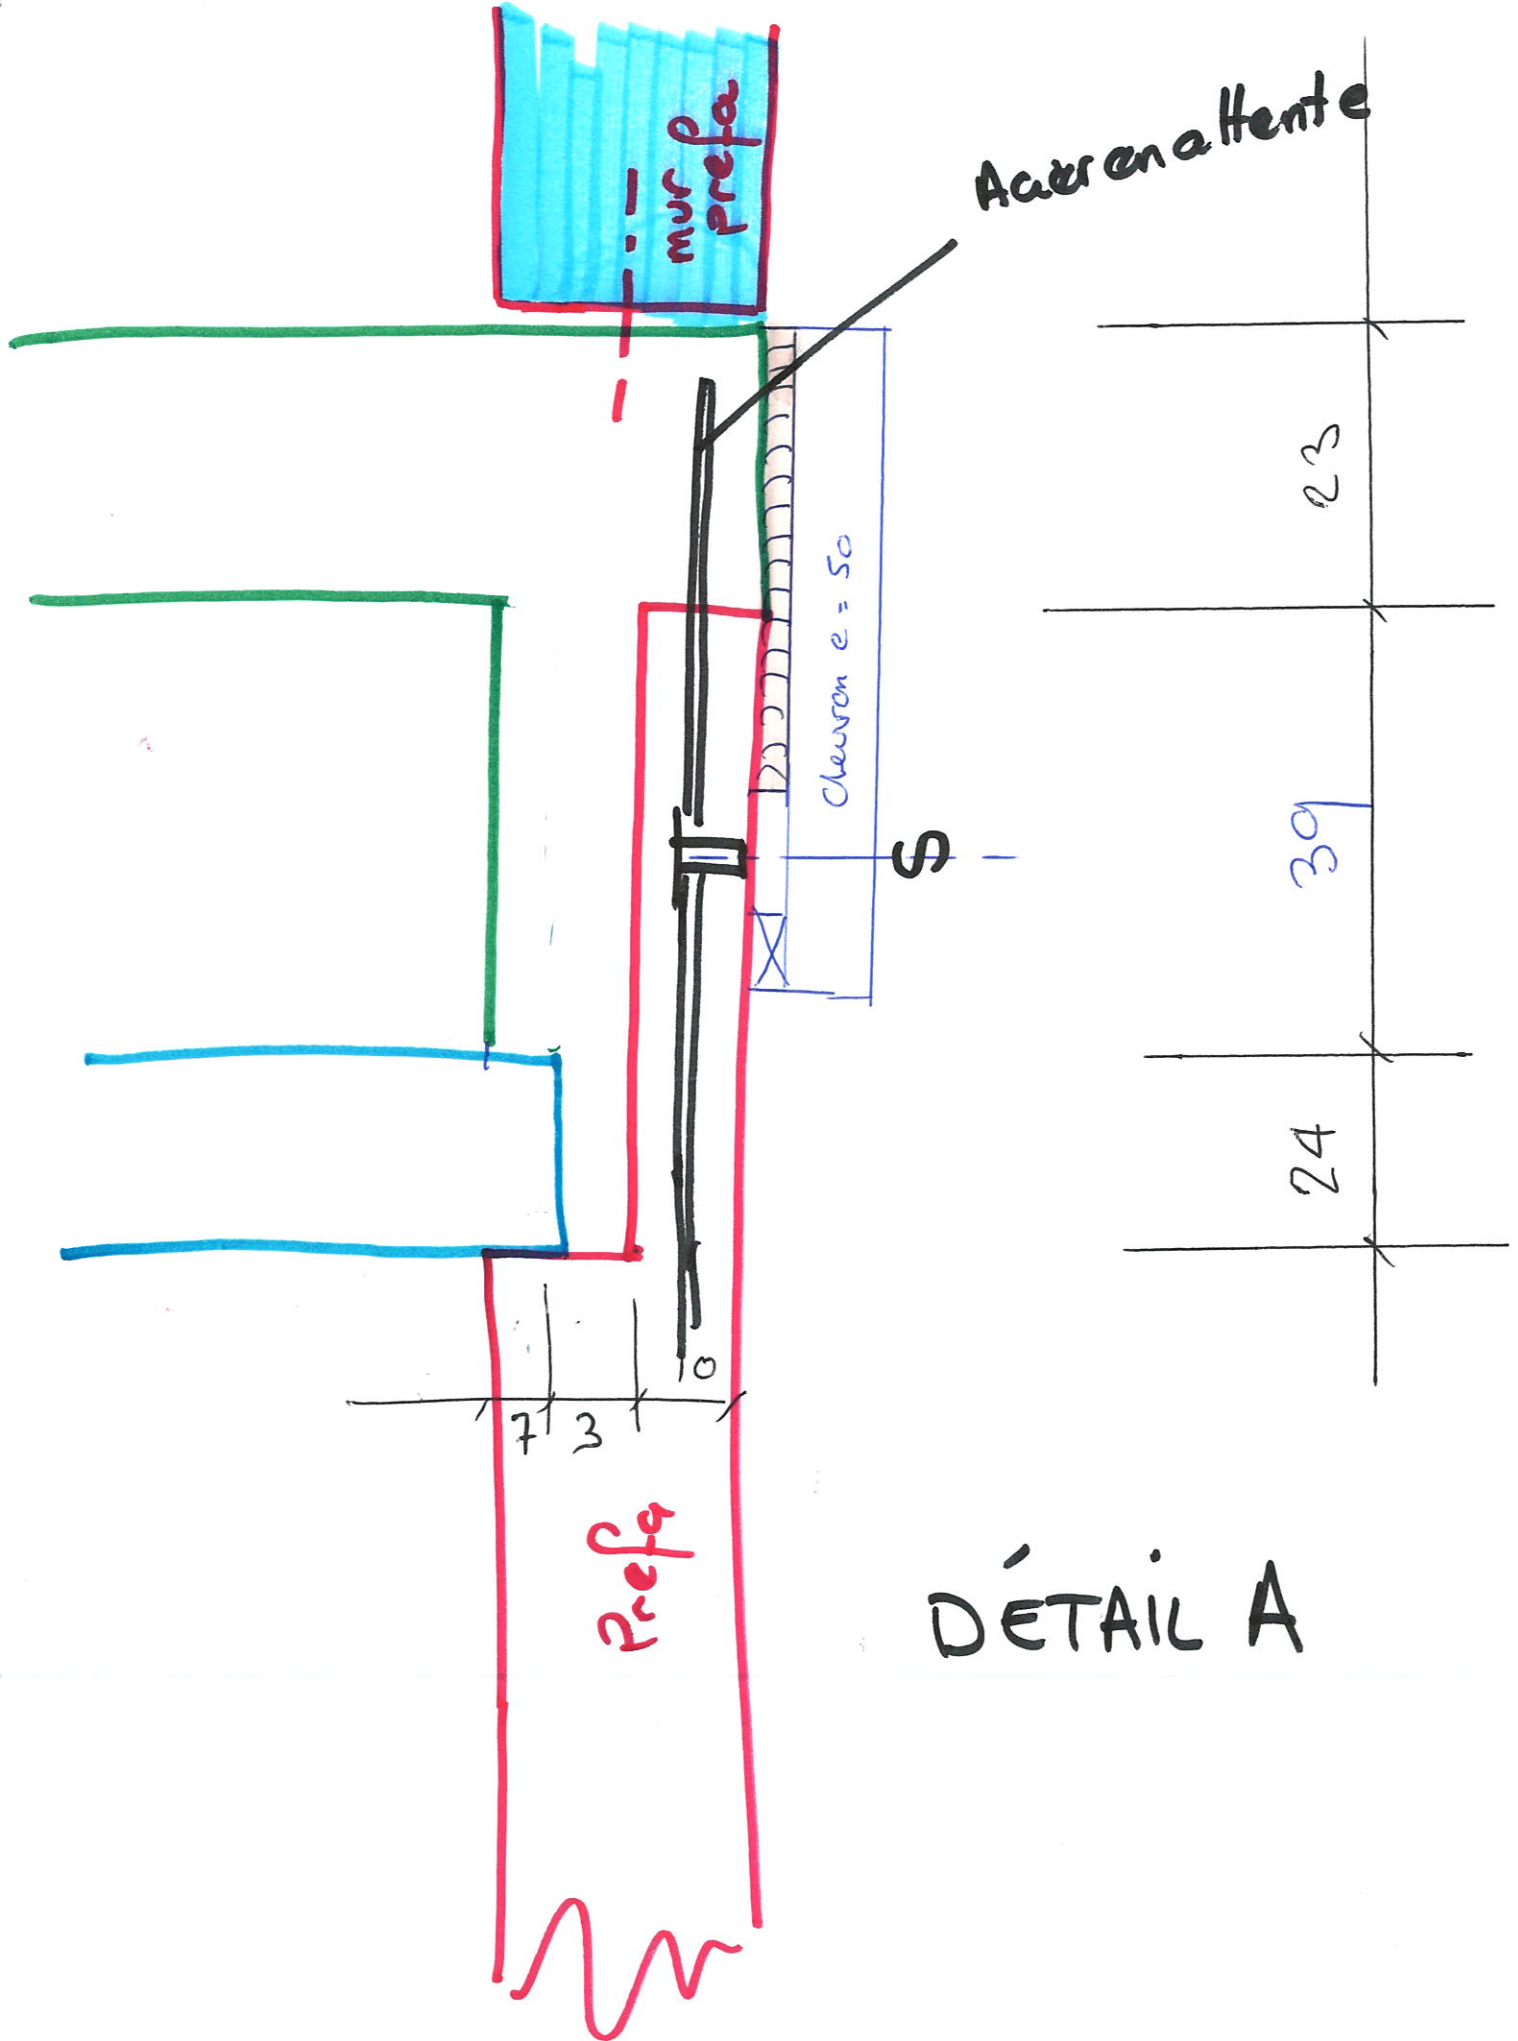

MOULE	N	NC	observations	CONTROLE	N	NC	observations	BETON	N	NC	observations	FICHE AUTO-CONTROLE			
Conformité moule				Dimensions				Conformité béton				Opérateur :			
Etat du moule				Armature				Mise en place				Responsable prod :			
Propreté et huilage				Inserts				Aspect de surface				Date :			
Ent. FONTANEL			Elément: PANNEAUX		 FICHE DE FABRICATION			Surface: 4.53 m²		POIDS		REPERE		Nbr	
180°- LA MULATIERE			ARRONDIS							2.70 T		D1		2	
			coffrage					Volume: 1.12 m3							

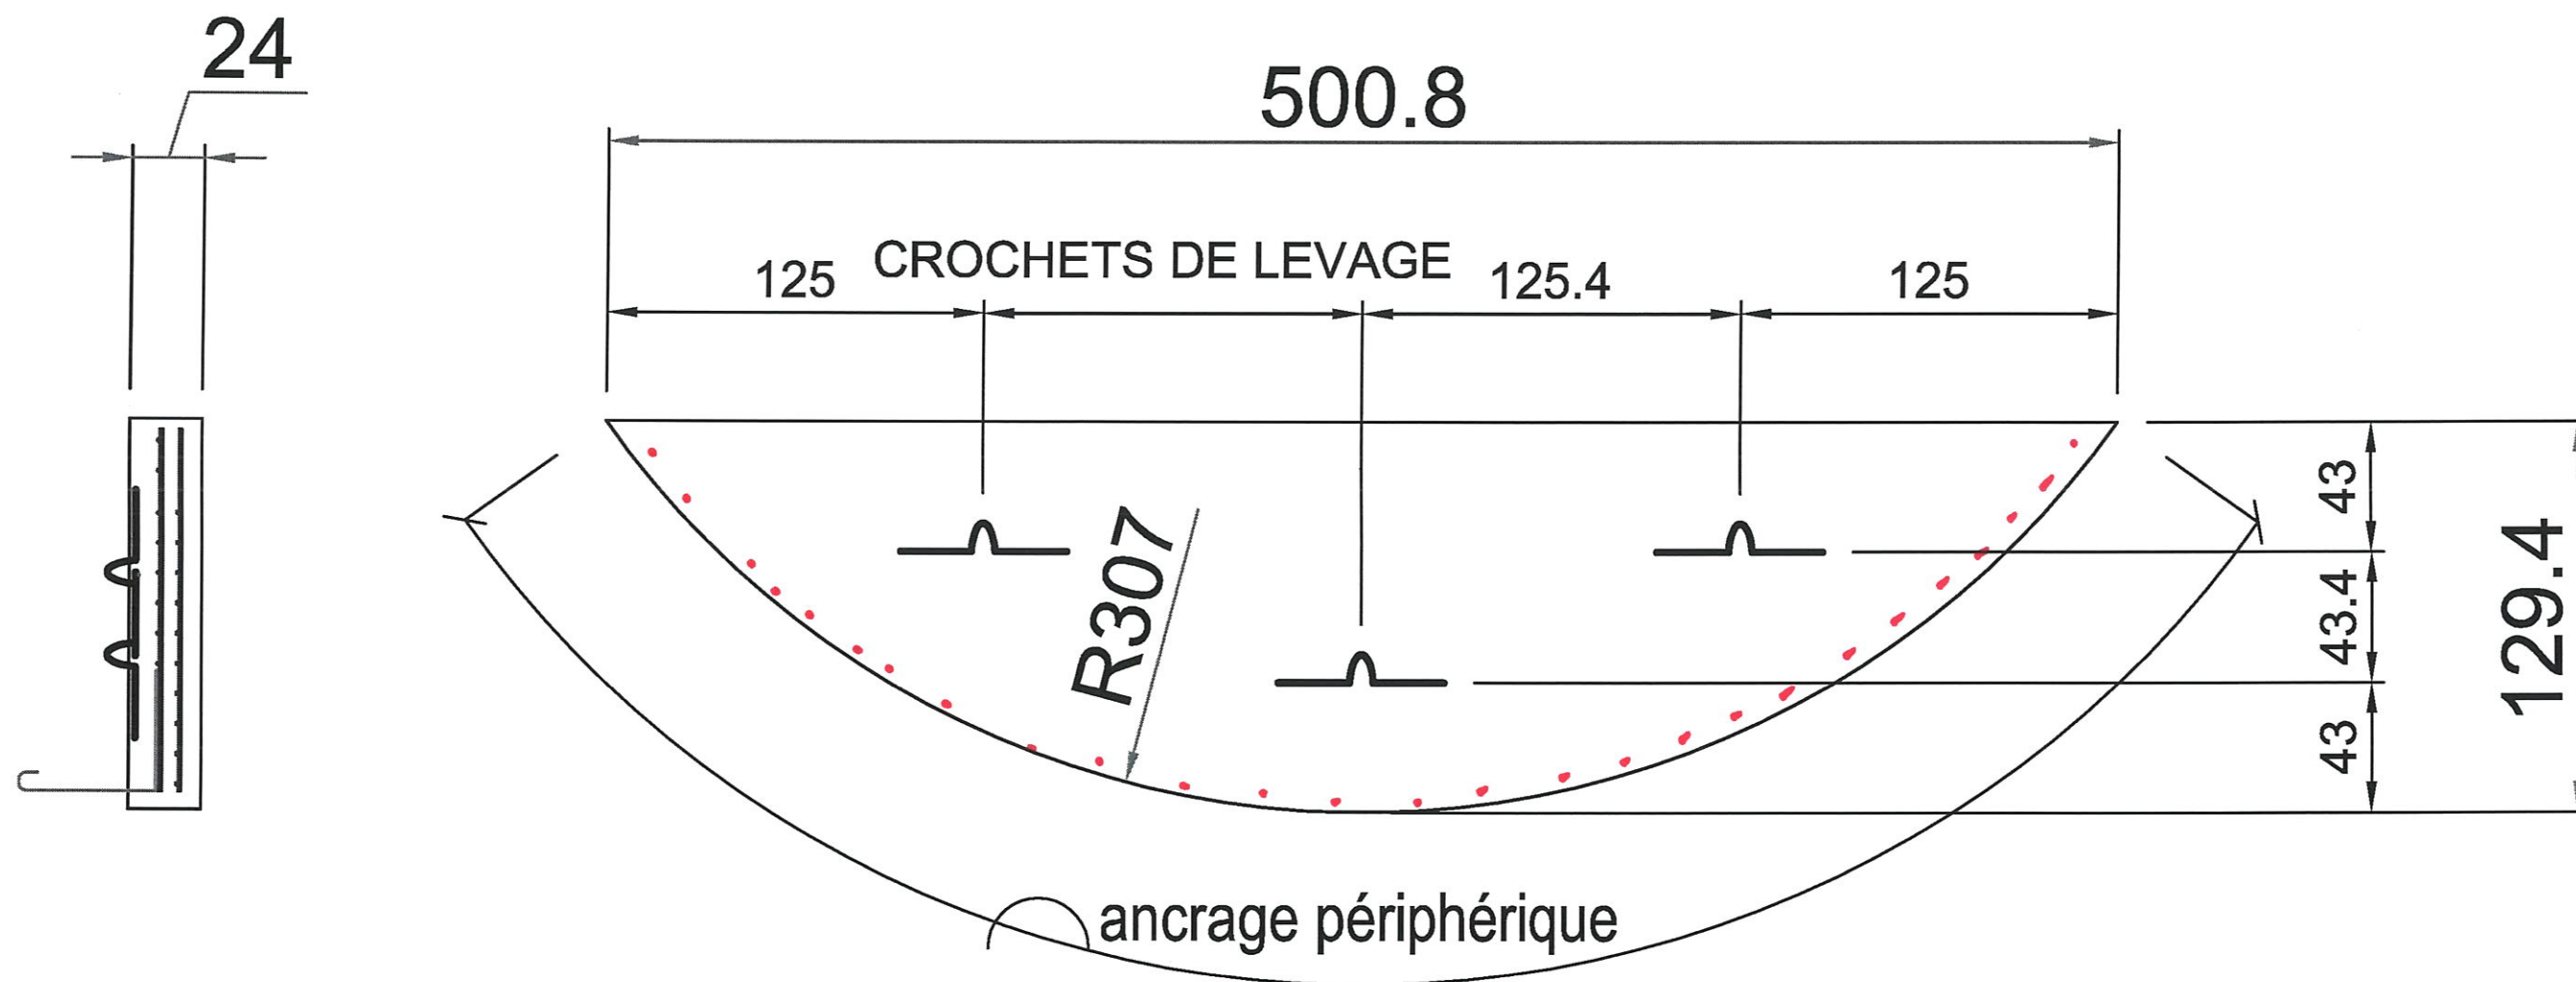


FERRAILAGE: 2 NAPPE DE ST60
ANCRAGE PERIPHERIQUE HA8 e=20

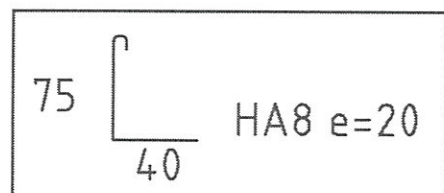

LEVAGE		Douille Ø	INSERTS		Ancre Frimeda T	INSERTS		EBA	INSERTS		TP - JV	DATE: 02 / 12 / 2015	
		Douille Ø			Renfort Ø			Douille étaie			PVC Ø80	Plan N°	Page N°
		Renfort Ø dx			Trifer			Ankrobox Ø50			Tube garde-corps	Indice	


Ent. FONTANEL	Elément: PANNEAUX	 PLATTARD S.A.S. •	FICHE DE FABRICATION	Surface: m²	POIDS	REPERE	Nbr
180°- LA MULATIERE	ARRONDIS				2.70 T	D1	2
	coffrage			Volume: 1.12 m3			

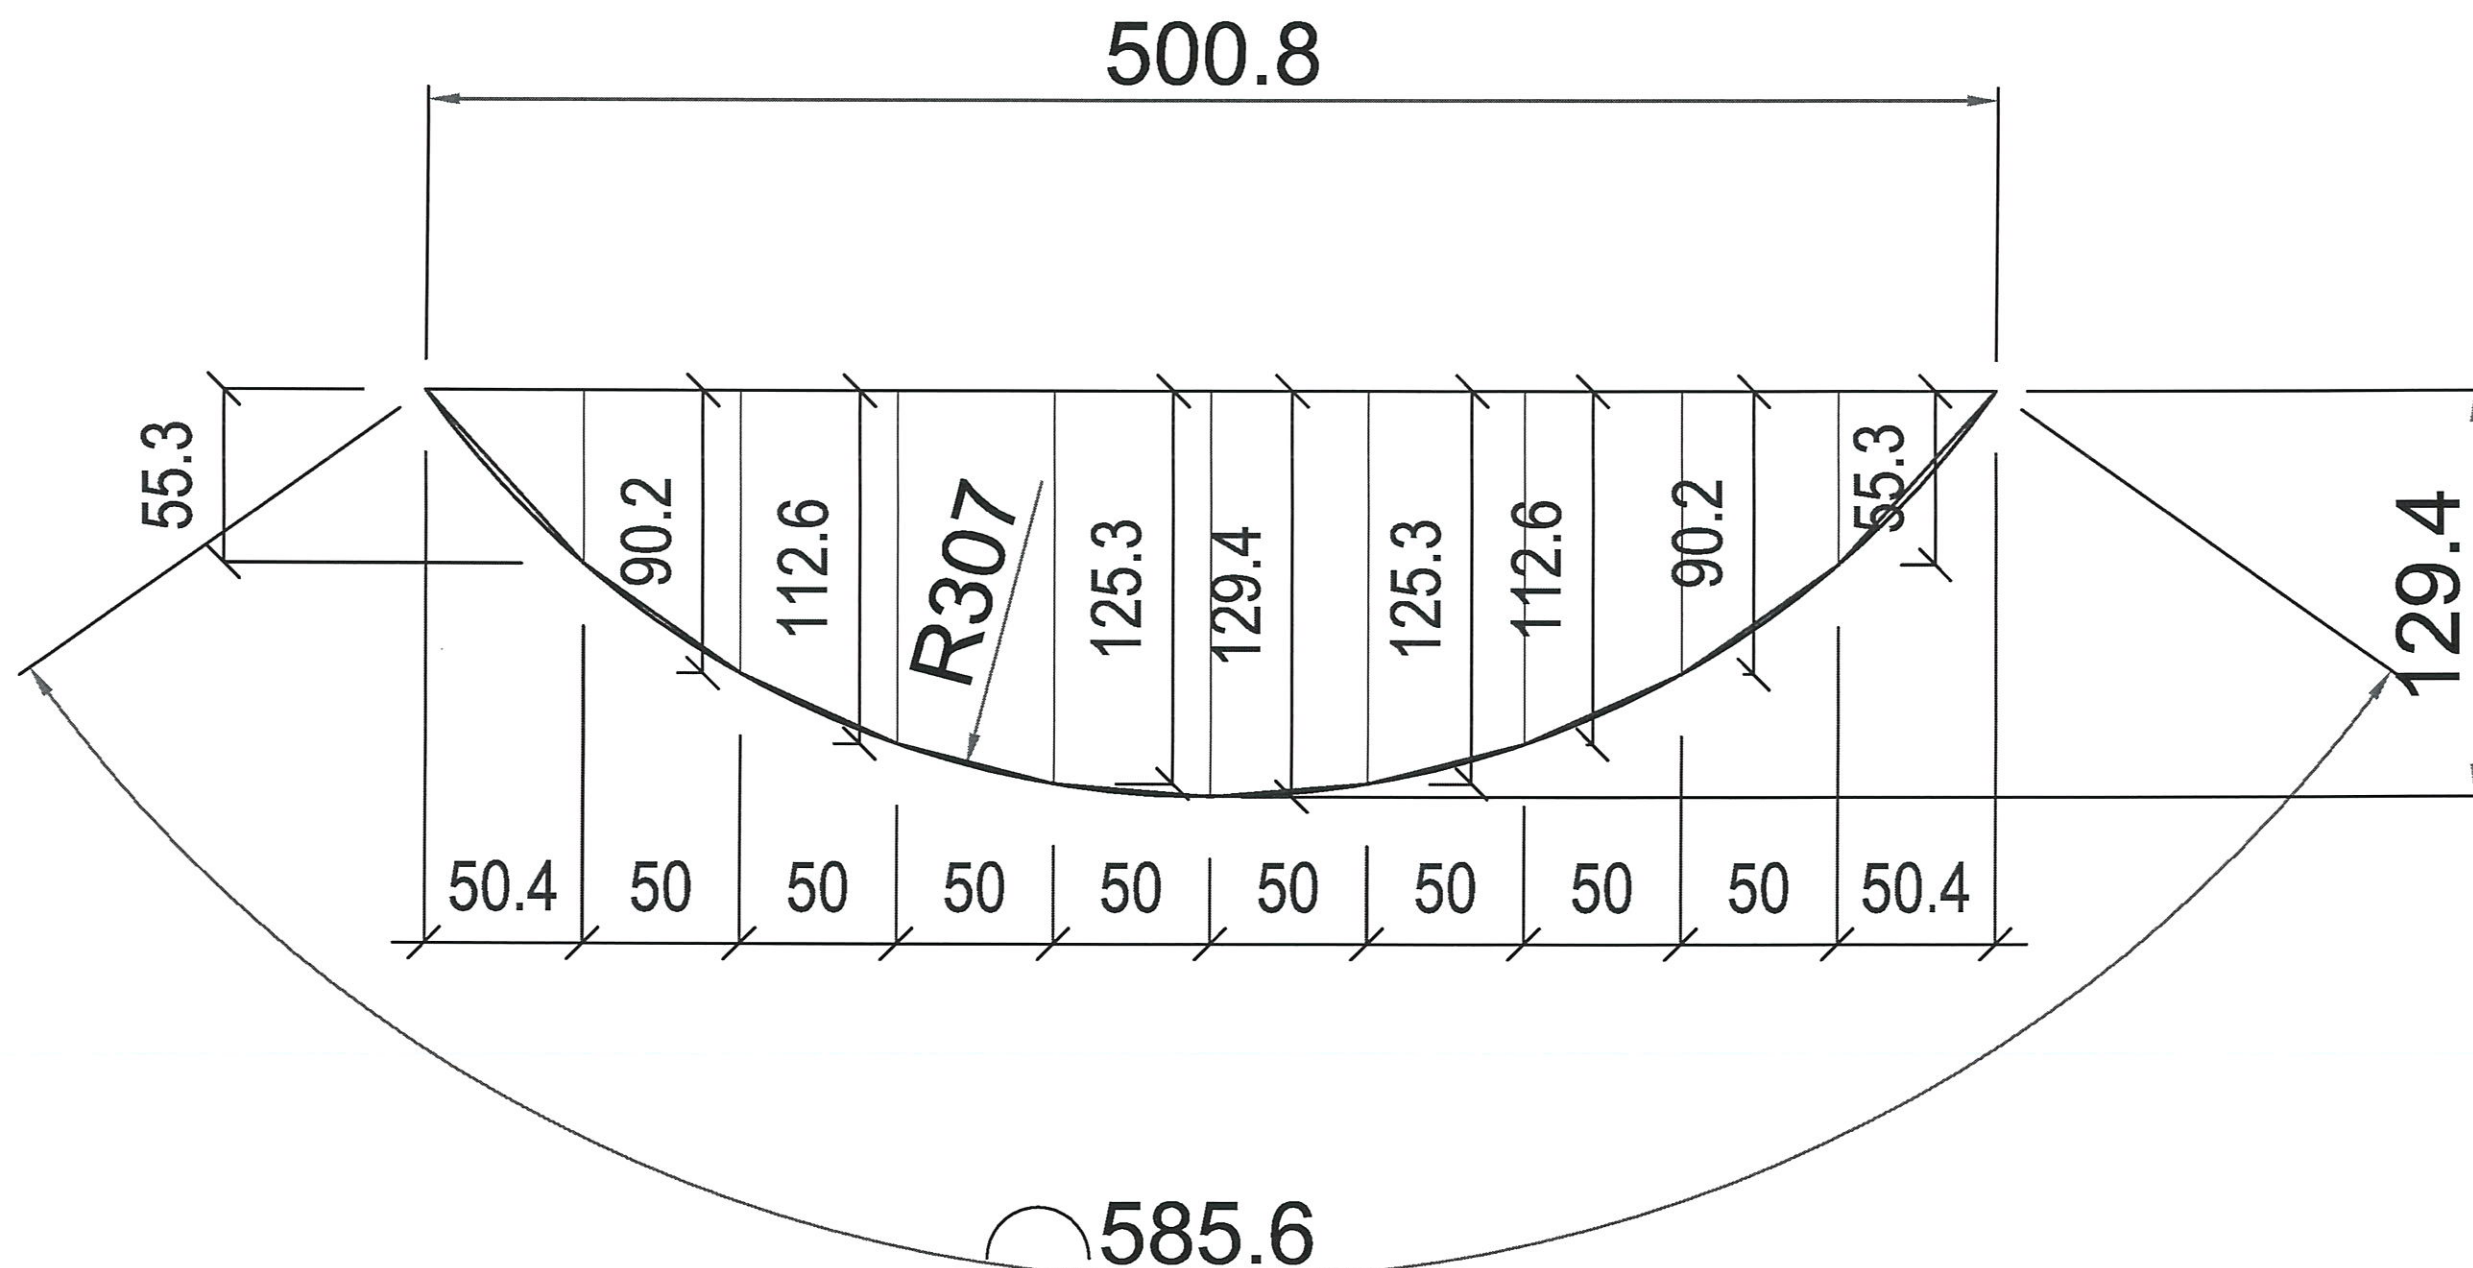



LEVAGE		Douille Ø	INSERTS		Ancre Frimeda T	INSERTS		EBA	INSERTS		TP - JV	DATE: 02 / 12 / 2015					
		Douille Ø			Renfort Ø			Douille étalement			PVC Ø80	Plan N°			Page N°		
		Renfort Ø dx			Trifer			Ankrobox Ø50			Tube garde-corps	Indice					


MOULE	N	NC	observations	CONTROLE	N	NC	observations	BETON	N	NC	observations	FICHE AUTO-CONTROLE
Conformité moule				Dimensions				Conformité béton				Opérateur :
Etat du moule				Armature				Mise en place				Responsable prod :
Propreté et huilage				Inserts				Aspect de surface				Date :

Ent. FONTANEL	Elément: PANNEAUX	 FICHE DE FABRICATION	Surface: 6,57 m ²	POIDS	REPERE	Nbr
180°- LA MULATIERE	ARRONDIS			2.70 T	D2	1
	coffrage		Volume: 1.12 m ³			

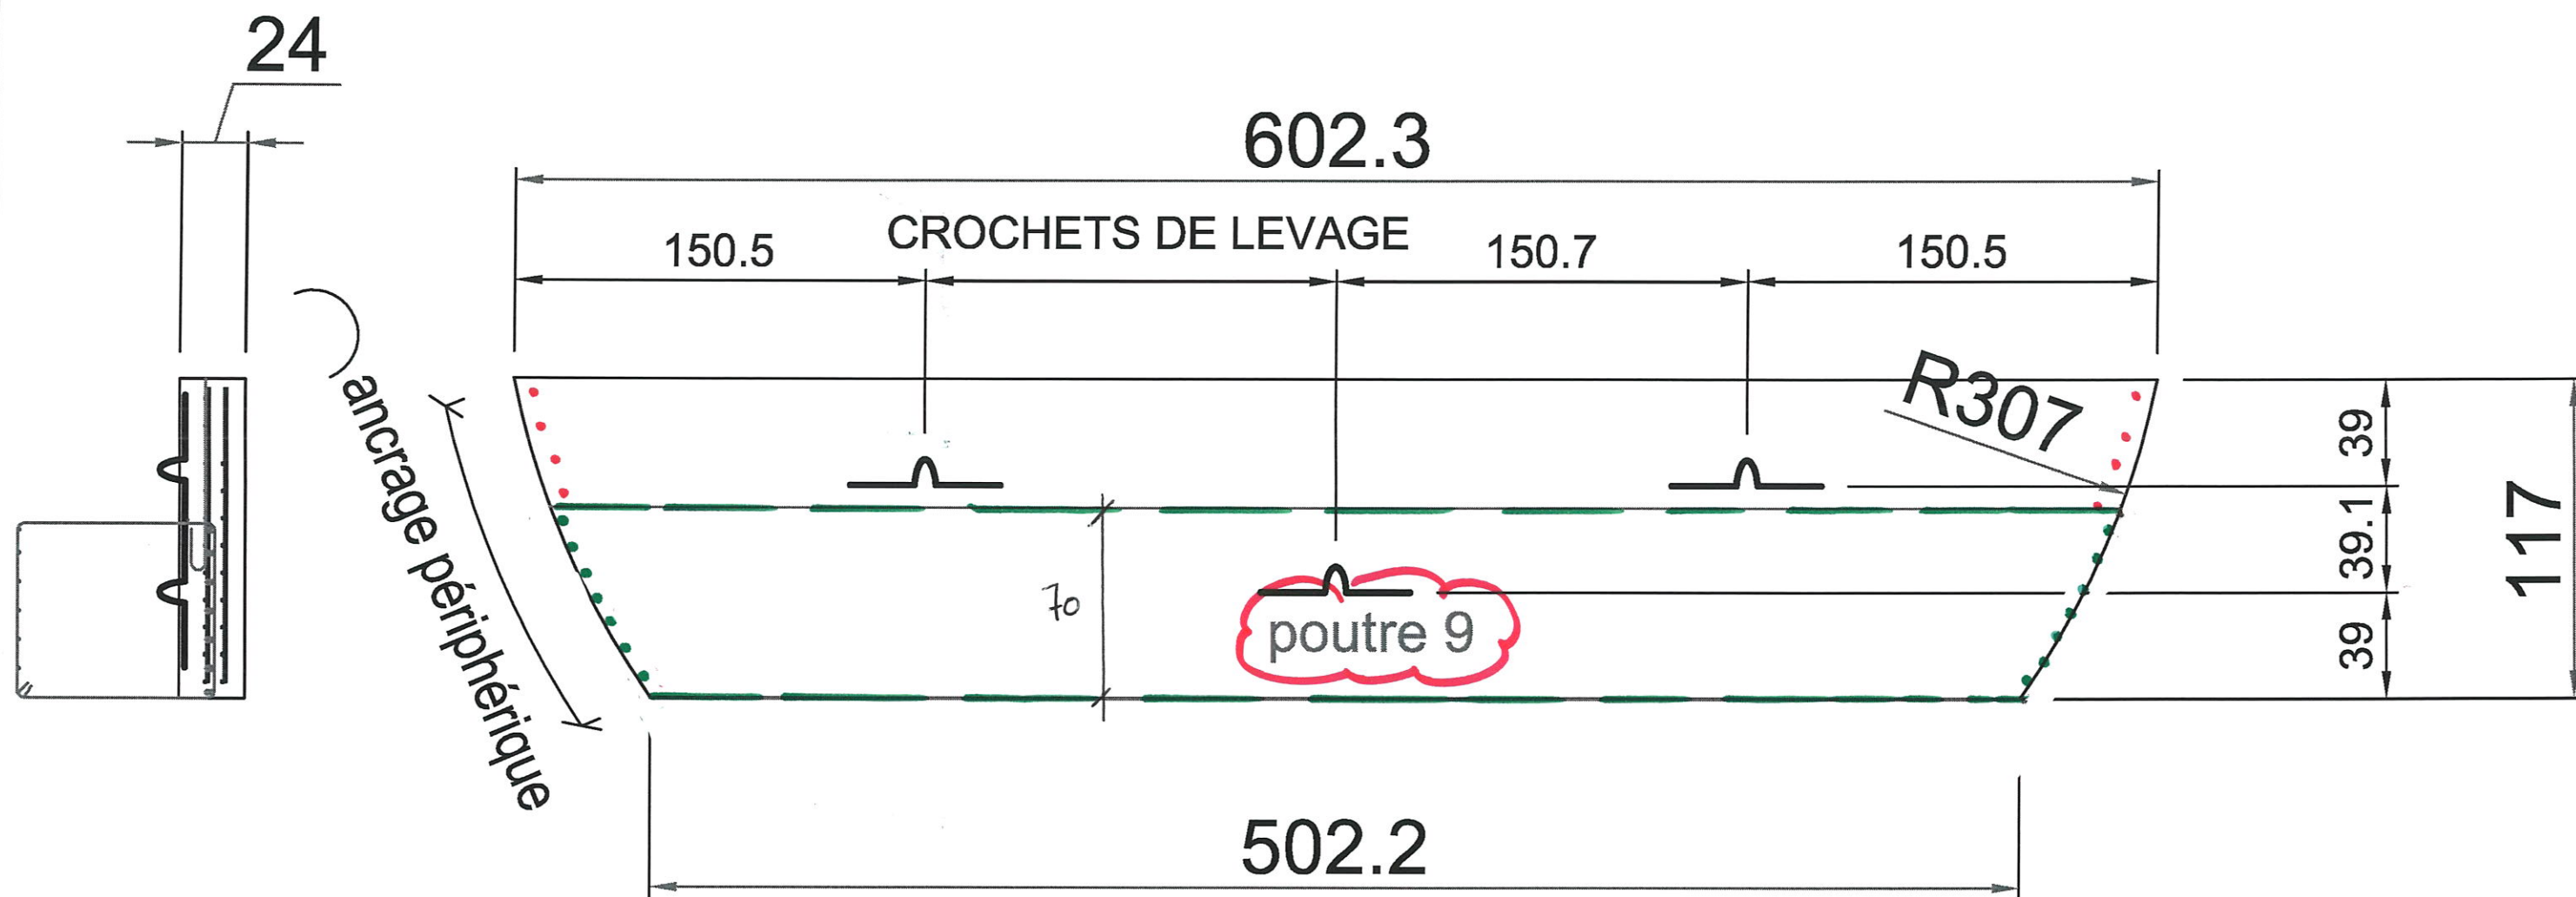


FERRAILLAGE: 2 NAPPE DE ST60
ANCRAGE PERIPHERIQUE HA8 e=20

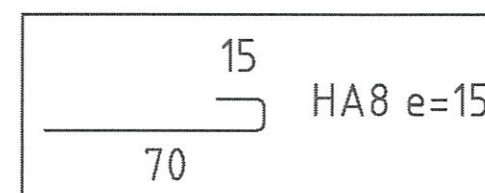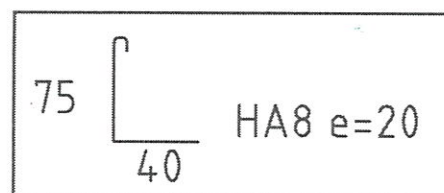

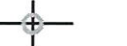
LEVAGE		Douille Ø	INSERTS		Ancre Frimeda T	INSERTS		EBA	INSERTS		TP - JV	DATE: 02 / 12 / 2015
		Douille Ø			Renfort Ø			Douille étalement			PVC Ø80	Plan N°
		Renfort Ø dx	INSERTS		Trifer	INSERTS		Ankrobox Ø50	INSERTS		Tube garde-corps	Indice

Section : 70 x 86ht
Fc28= 25 MPa Fe= 500 MPa Fissuration peu préjudiciable Coupe feu 1 H


Elévation
Echelle=1/33

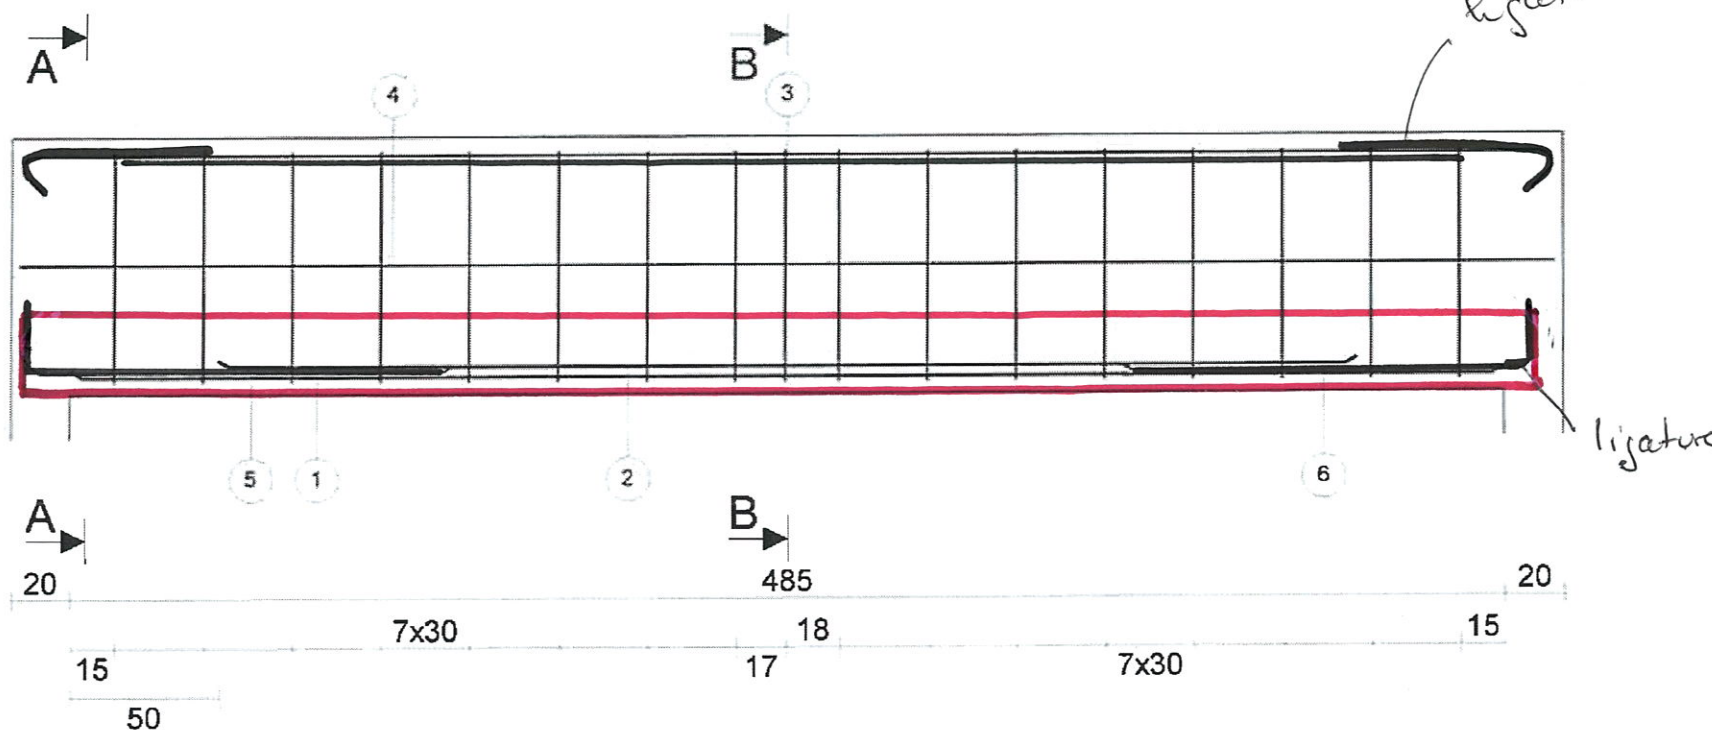

Coupe A-A
Echelle=1/20

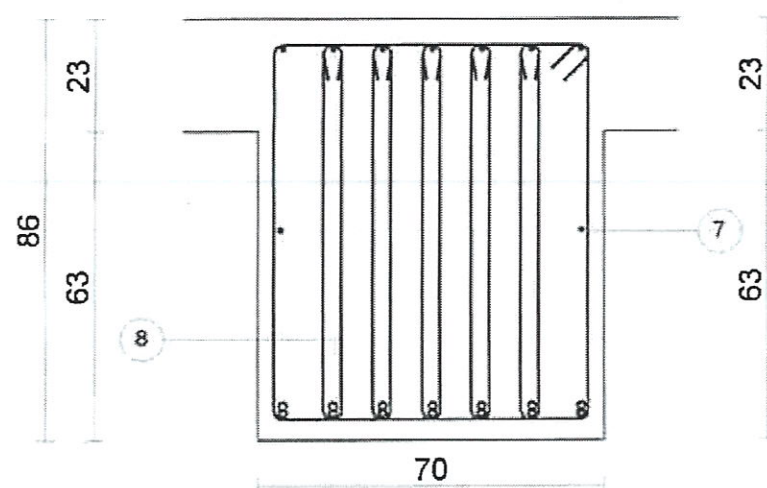

Coupe B-B
Echelle=1/20

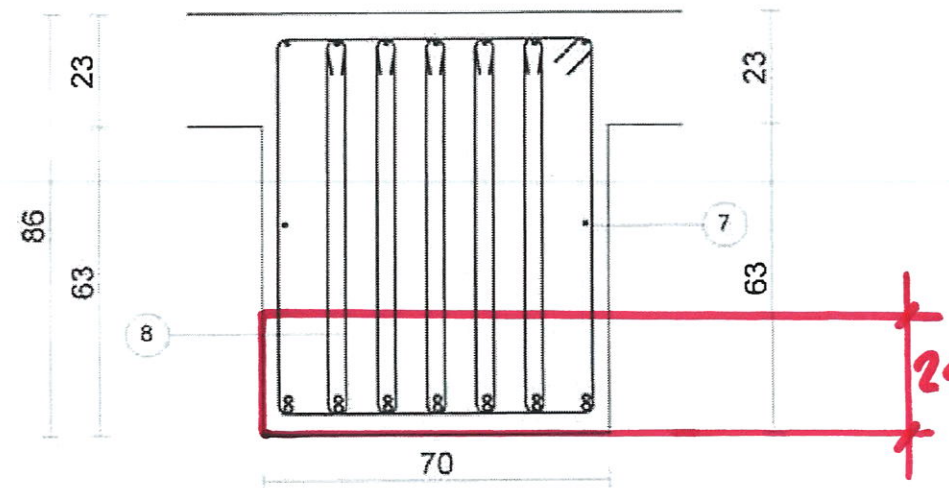


Barre	Lg	Forme
1	7HA16	485
2	7HA14	385
3	7HA8	544 135° 518 135°
4	2HA8	519
5	7HA16	171 135° 147
6	7HA16	171 147
7	17HA6	294 64 77
8	85HA6	173 77

Bureau d'Etudes MATTE

Structures et Fluides
119, bd Stalingrad - 69100 VILLEURBANNE
Tél. 04 72 44 02 87 - Fax 04 72 44 26 59
bet@matte.fr

Barre	Lg/Poids
HA6	197.2/43.8
HA8	48.4/19.1
HA14	27.0/32.6
HA16	58.0/91.5

Poutre 9 vue de dessus

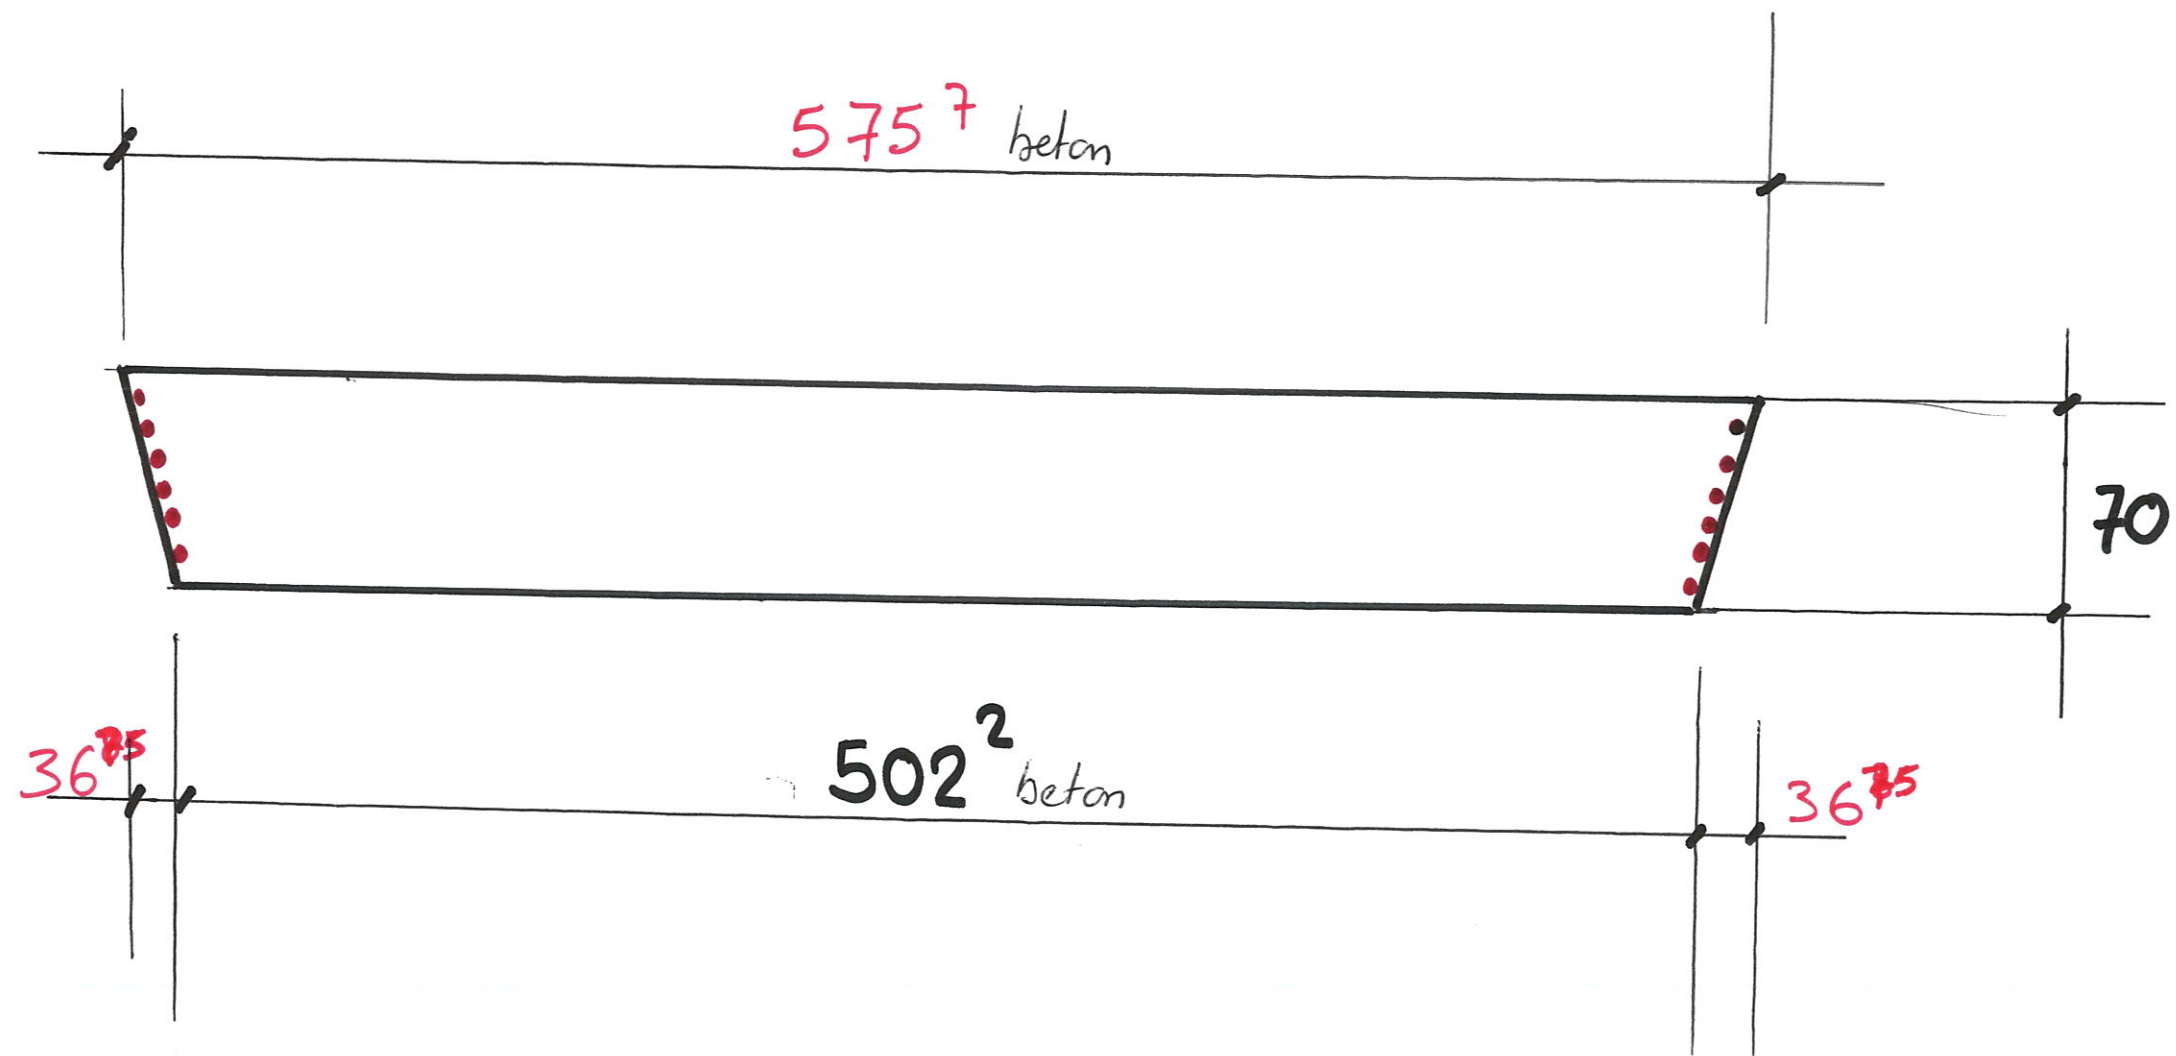


Loupe type Armatures

Ancrage Périphérique

HAB $e = 20$ 95 pièces

75
40

POUTRE 9

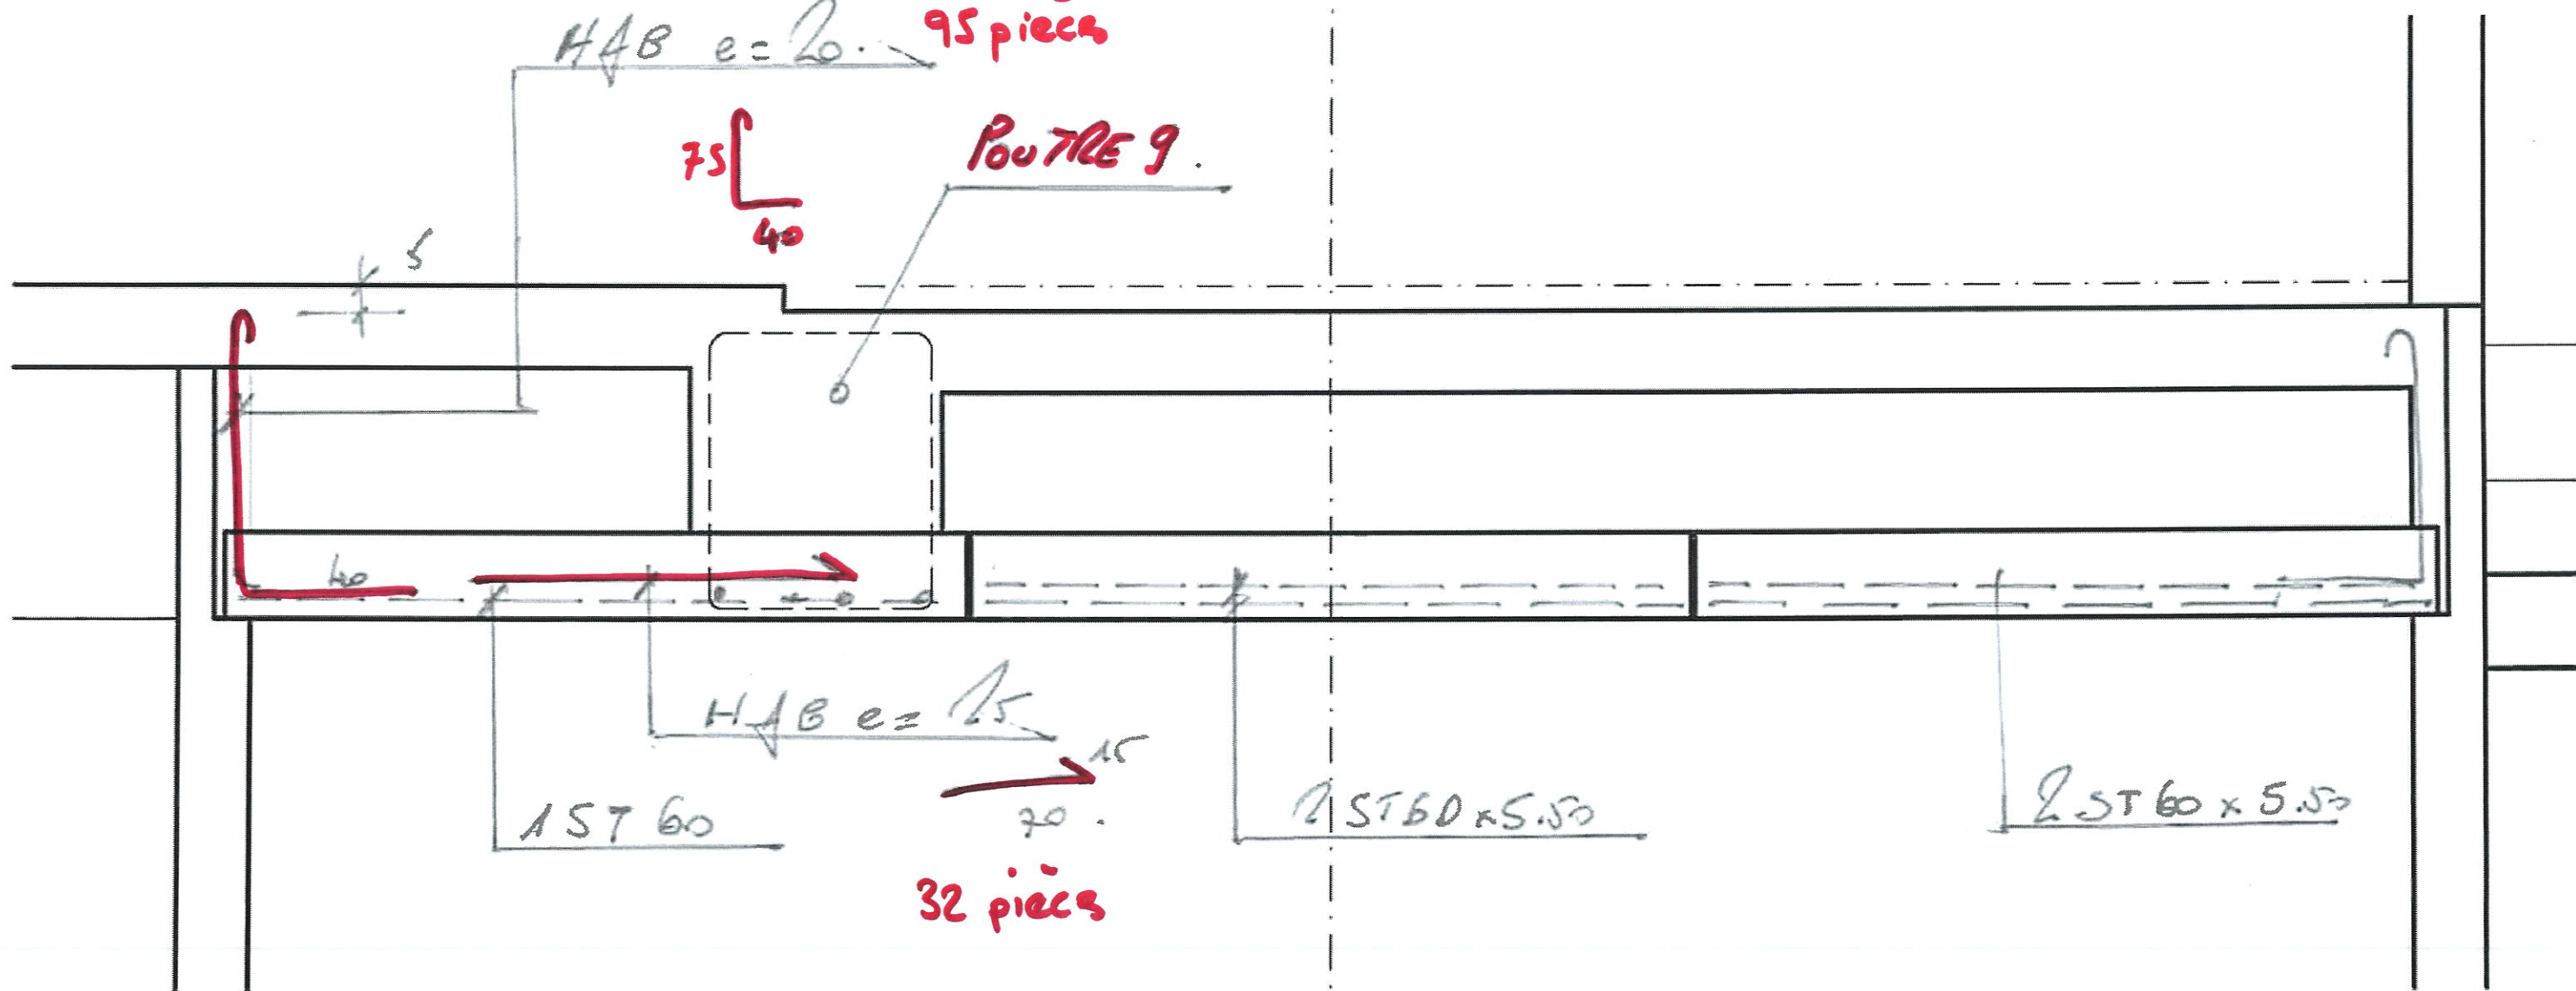

Bureau d'Etudes MATTE

Structures et Fluides

119, bd Stalingrad - 69100 VILLEURBANNE

Tél. 04 72 44 02 87 - Fax 04 72 44 26 59

bet@matte.fr


Technical drawing of a rectangular plate with the following dimensions and features:

- Overall width: 602.8
- Overall height: 117
- Top edge thickness: 24
- End flange thickness: 5.6
- Distance from end flange to first hook: 125
- Distance between hooks: 125
- Radius of the bottom-left corner: R307
- Label: CROCHETS DE LEVAGE (Hooks for lifting)
- Label: ancrage périphérique (Peripheral anchoring)
- Vertical dimensions on the right side: 39, 39.1, 39

75 $\int_{40}^{\quad}$ HA8 e=20

MOULE		N	NC	observations	CONTROLE		N	NC	observations	BETON		N	NC	observations	FICHE AUTO-CONTROLE			
Conformité moule							Dimensions						Conformité béton					Opérateur :
Etat du moule							Armature						Mise en place					Responsable prod :
Propreté et huilage							Inserts						Aspect de surface					Date :


Ent. FONTANEL		Elément: PANNEAUX			FICHE DE FABRICATION	Surface: m²		POIDS		REPERE		Nbr	
180°- LA MULATIERE		ARRONDIS						2.70 T		D3		1	
		coffrage				Volume: 1.12 m3							

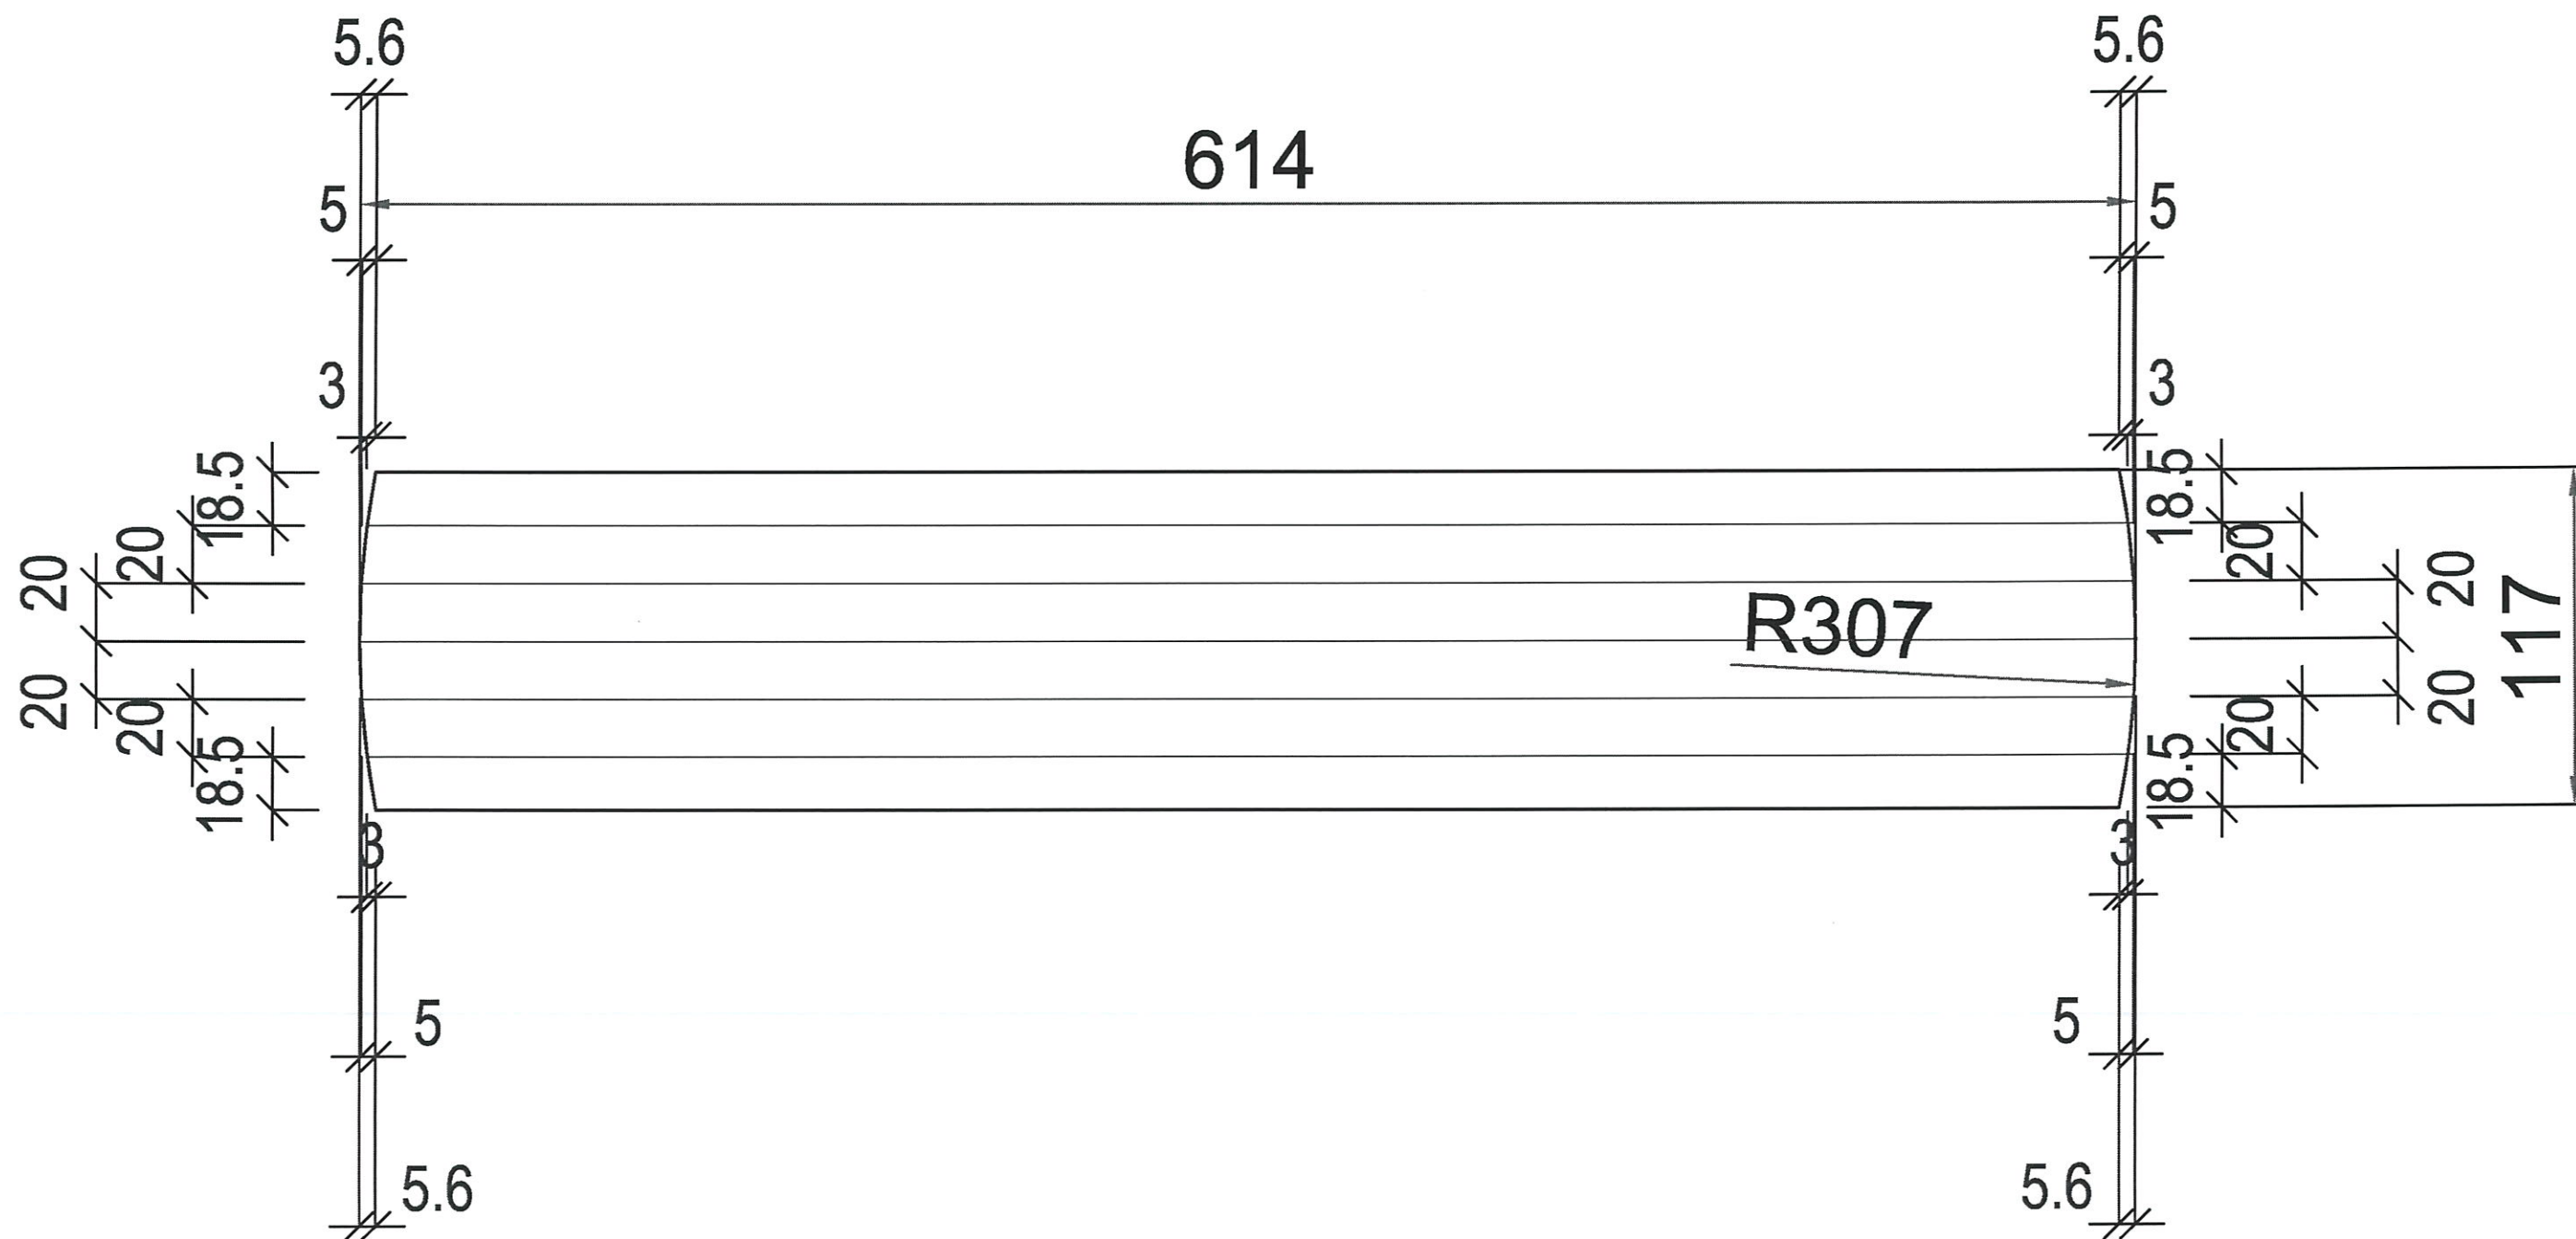


LEVAGE		Douille Ø	INSERTS		Ancre Frimeda T	INSERTS		EBA	INSERTS		TP - JV	DATE: 02 / 12 / 2015	
		Douille Ø			Renfort Ø			Douille étalement			PVC Ø80	Plan N°	Page N°
		Renfort Ø dx			Trifer			Ankrobox Ø50			Tube garde-corps	Indice	

MOULE		N	NC	observations	CONTROLE		N	NC	observations	BETON		N	NC	observations	FICHE AUTO-CONTROLE			
Conformité moule							Dimensions						Conformité béton					Opérateur :
Etat du moule							Armature						Mise en place					Responsable prod :
Propreté et huilage							Inserts						Aspect de surface					Date :

Ent. FONTANEL		Elément: PANNEAUX			FICHE DE FABRICATION	Surface: 6,57m²		POIDS		REPERE		Nbr	
180°- LA MULATIERE		ARRONDIS						2.70 T		D4		1	
		coffrage				Volume: 1.12 m3							

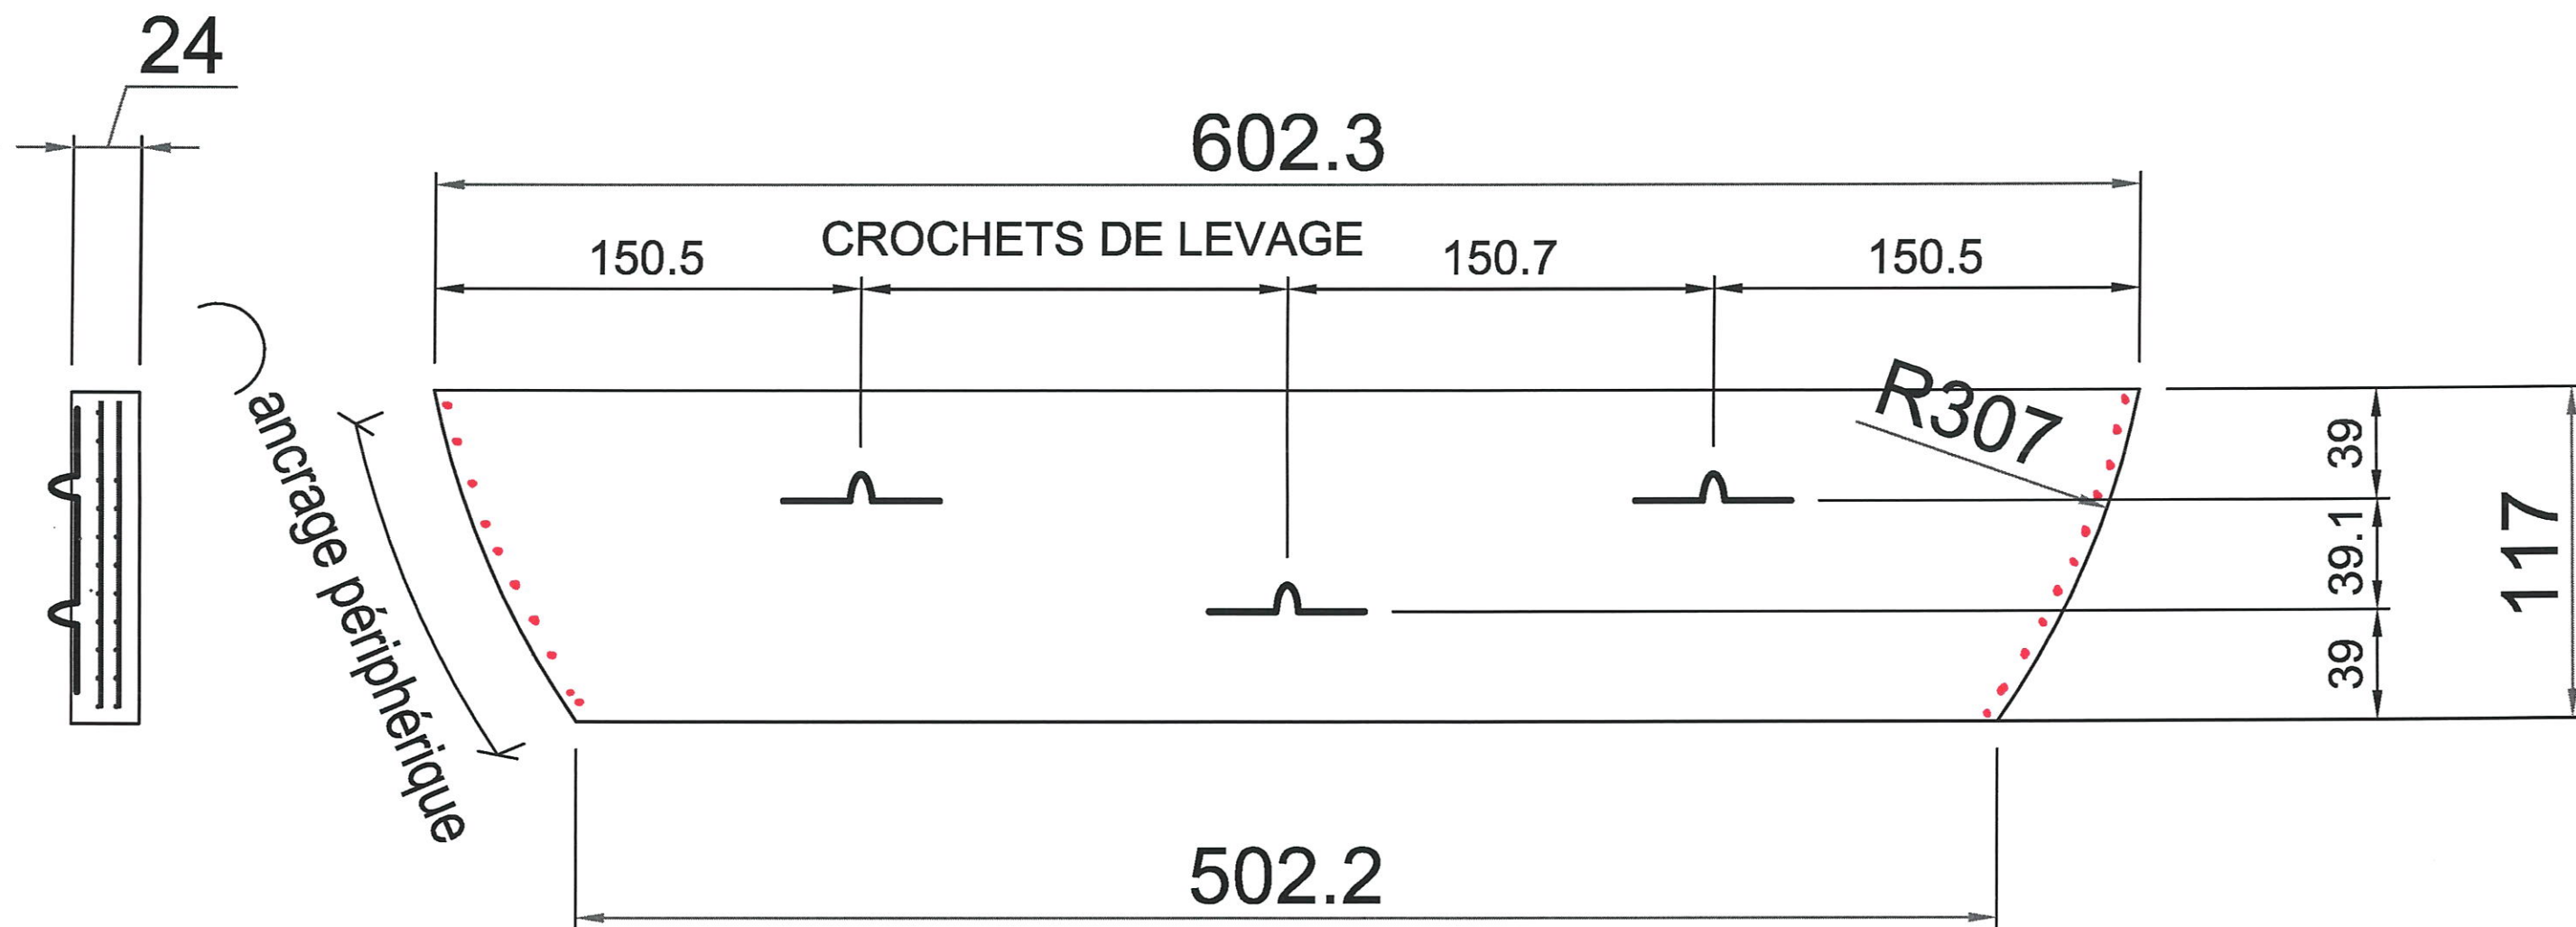


FERRAILLAGE: 2 NAPPE DE ST60
ANCRAGE PERIPHERIQUE HA8 e=20

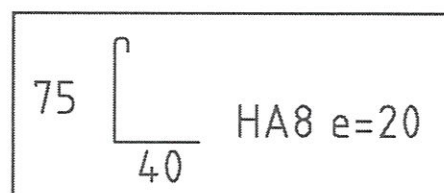

LEVAGE		Douille Ø	INSERTS		Ancre Frimeda T	INSERTS		EBA	INSERTS		TP - JV	DATE: 02 / 12 / 2015	
		Douille Ø			Renfort Ø			Douille étaiement			PVC Ø80	Plan N°	Page N°
		Renfort Ø dx			Trifer			Ankrbox Ø50			Tube garde-corps	Indice	

MOULE	N	NC	observations	CONTROLE	N	NC	observations	BETON	N	NC	observations	FICHE AUTO-CONTROLE
Conformité moule				Dimensions				Conformité béton				Opérateur :
Etat du moule				Armature				Mise en place				Responsable prod :
Propreté et huilage				Inserts				Aspect de surface				Date :

Ent. FONTANEL	Elément: PANNEAUX	 FICHE DE FABRICATION	Surface: m²	POIDS	REPERE	Nbr
180°- LA MULATIERE	ARRONDIS			2.70 T	D2	1
	coffrage		Volume: 1.12 m³			

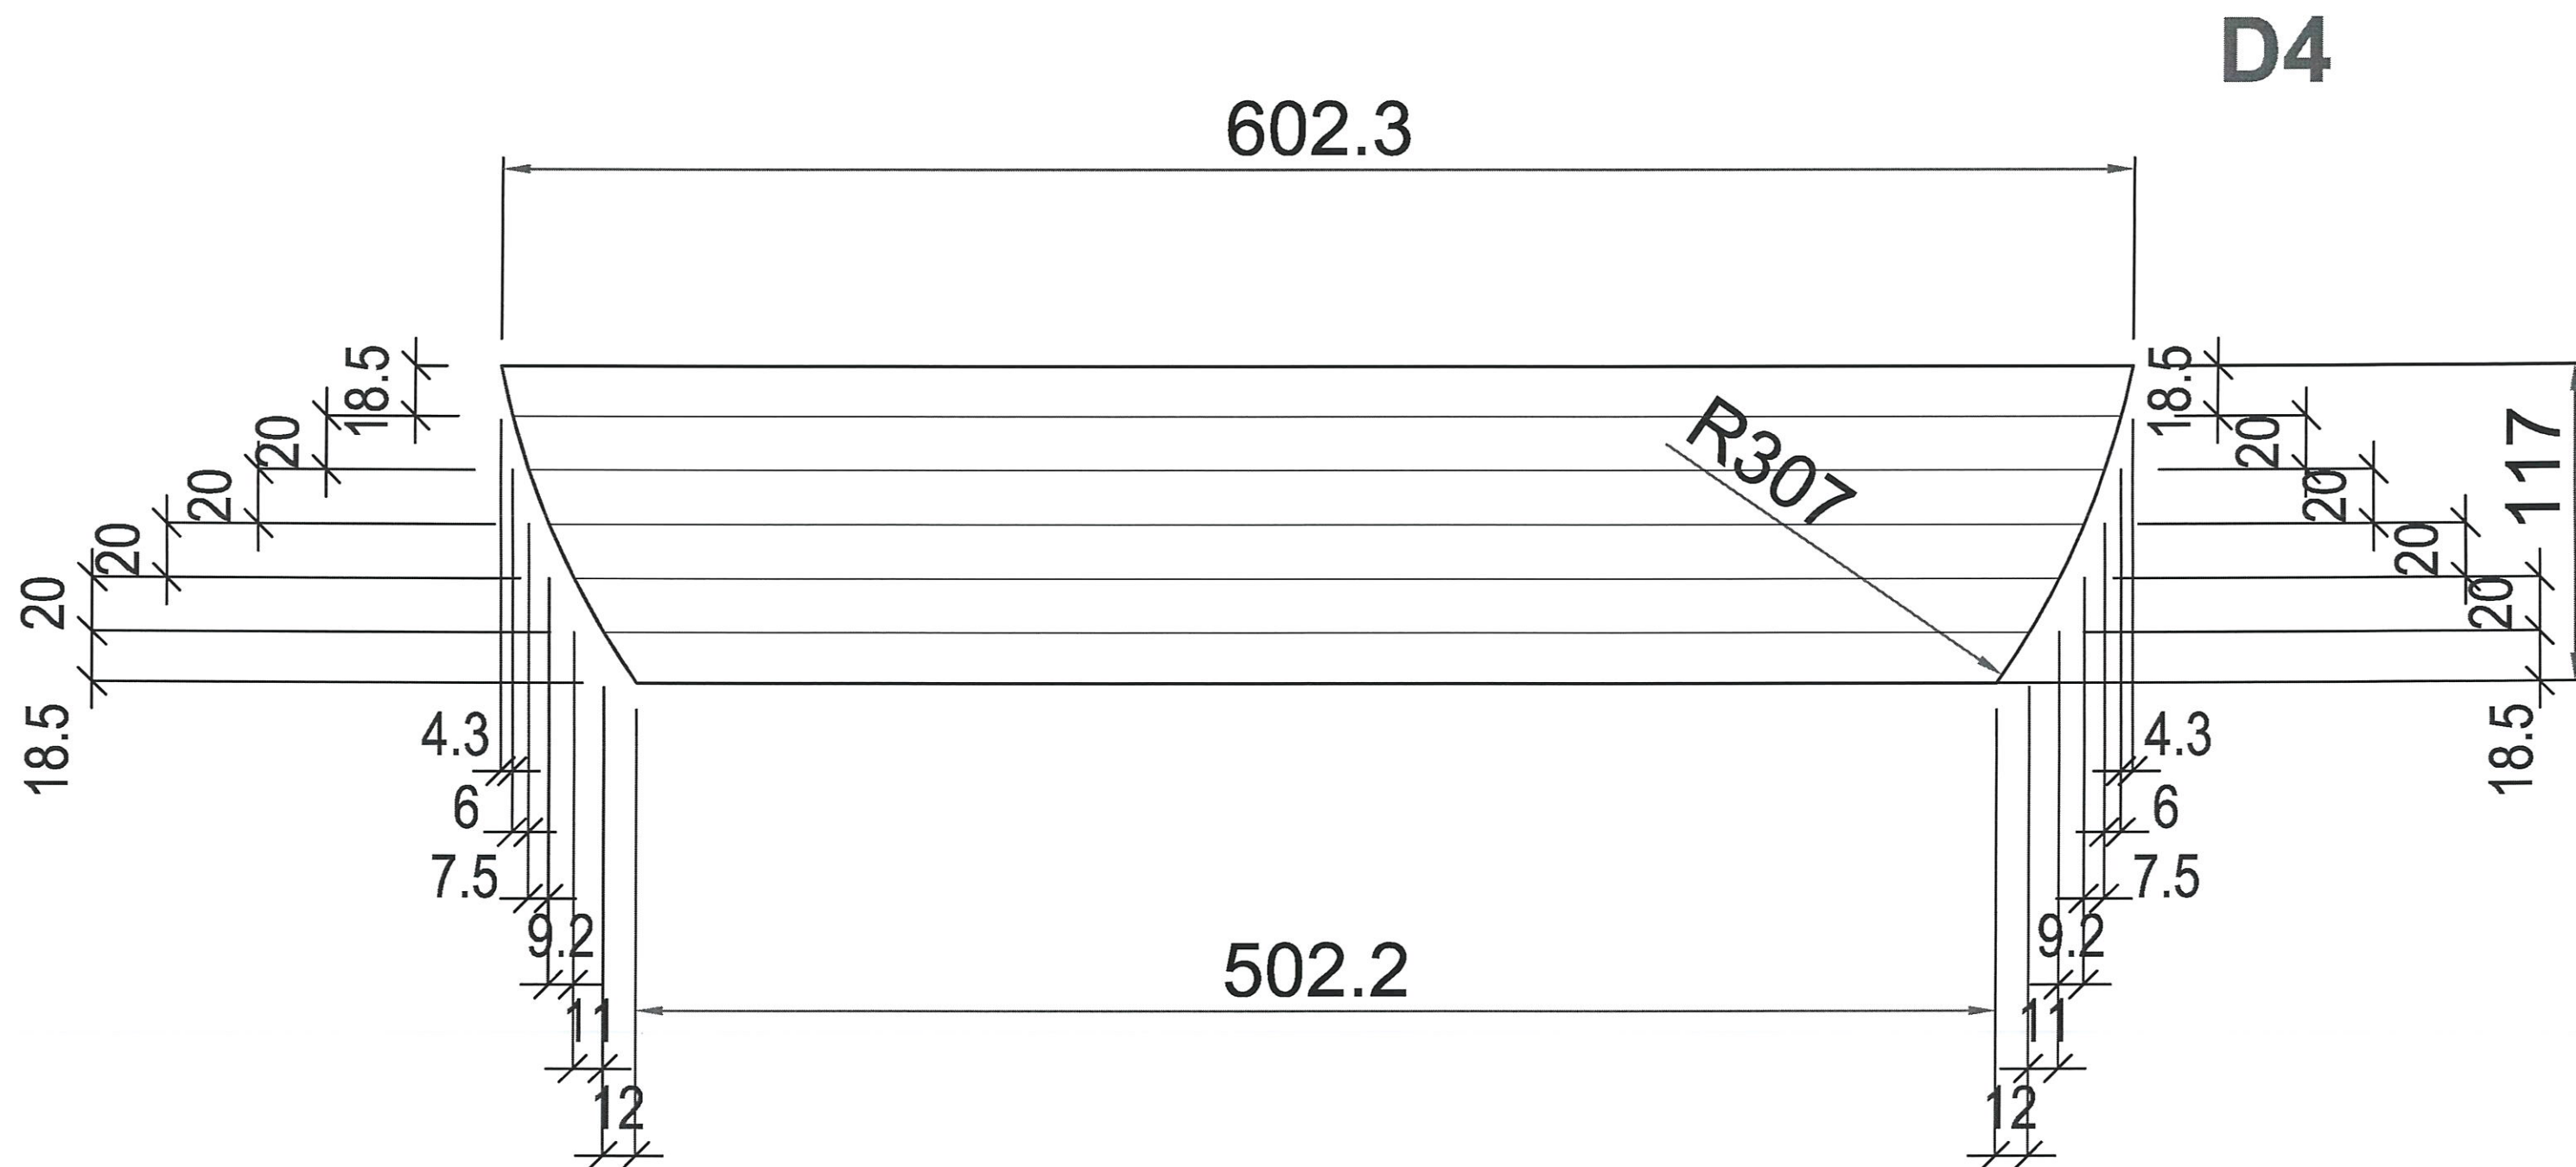

LEVAGE		Douille Ø	INSERTS		Ancre Frimeda T	INSERTS		EBA	INSERTS		TP - JV	DATE: 02 / 12 / 2015
		Douille Ø			Renfort Ø			Douille étaie			PVC Ø80	Plan N°
		Renfort Ø dx	INSERTS		Trifer	INSERTS		Ankrobox Ø50	INSERTS		Tube garde-corps	Indice